


建设项目用地预审与选址意见书附图

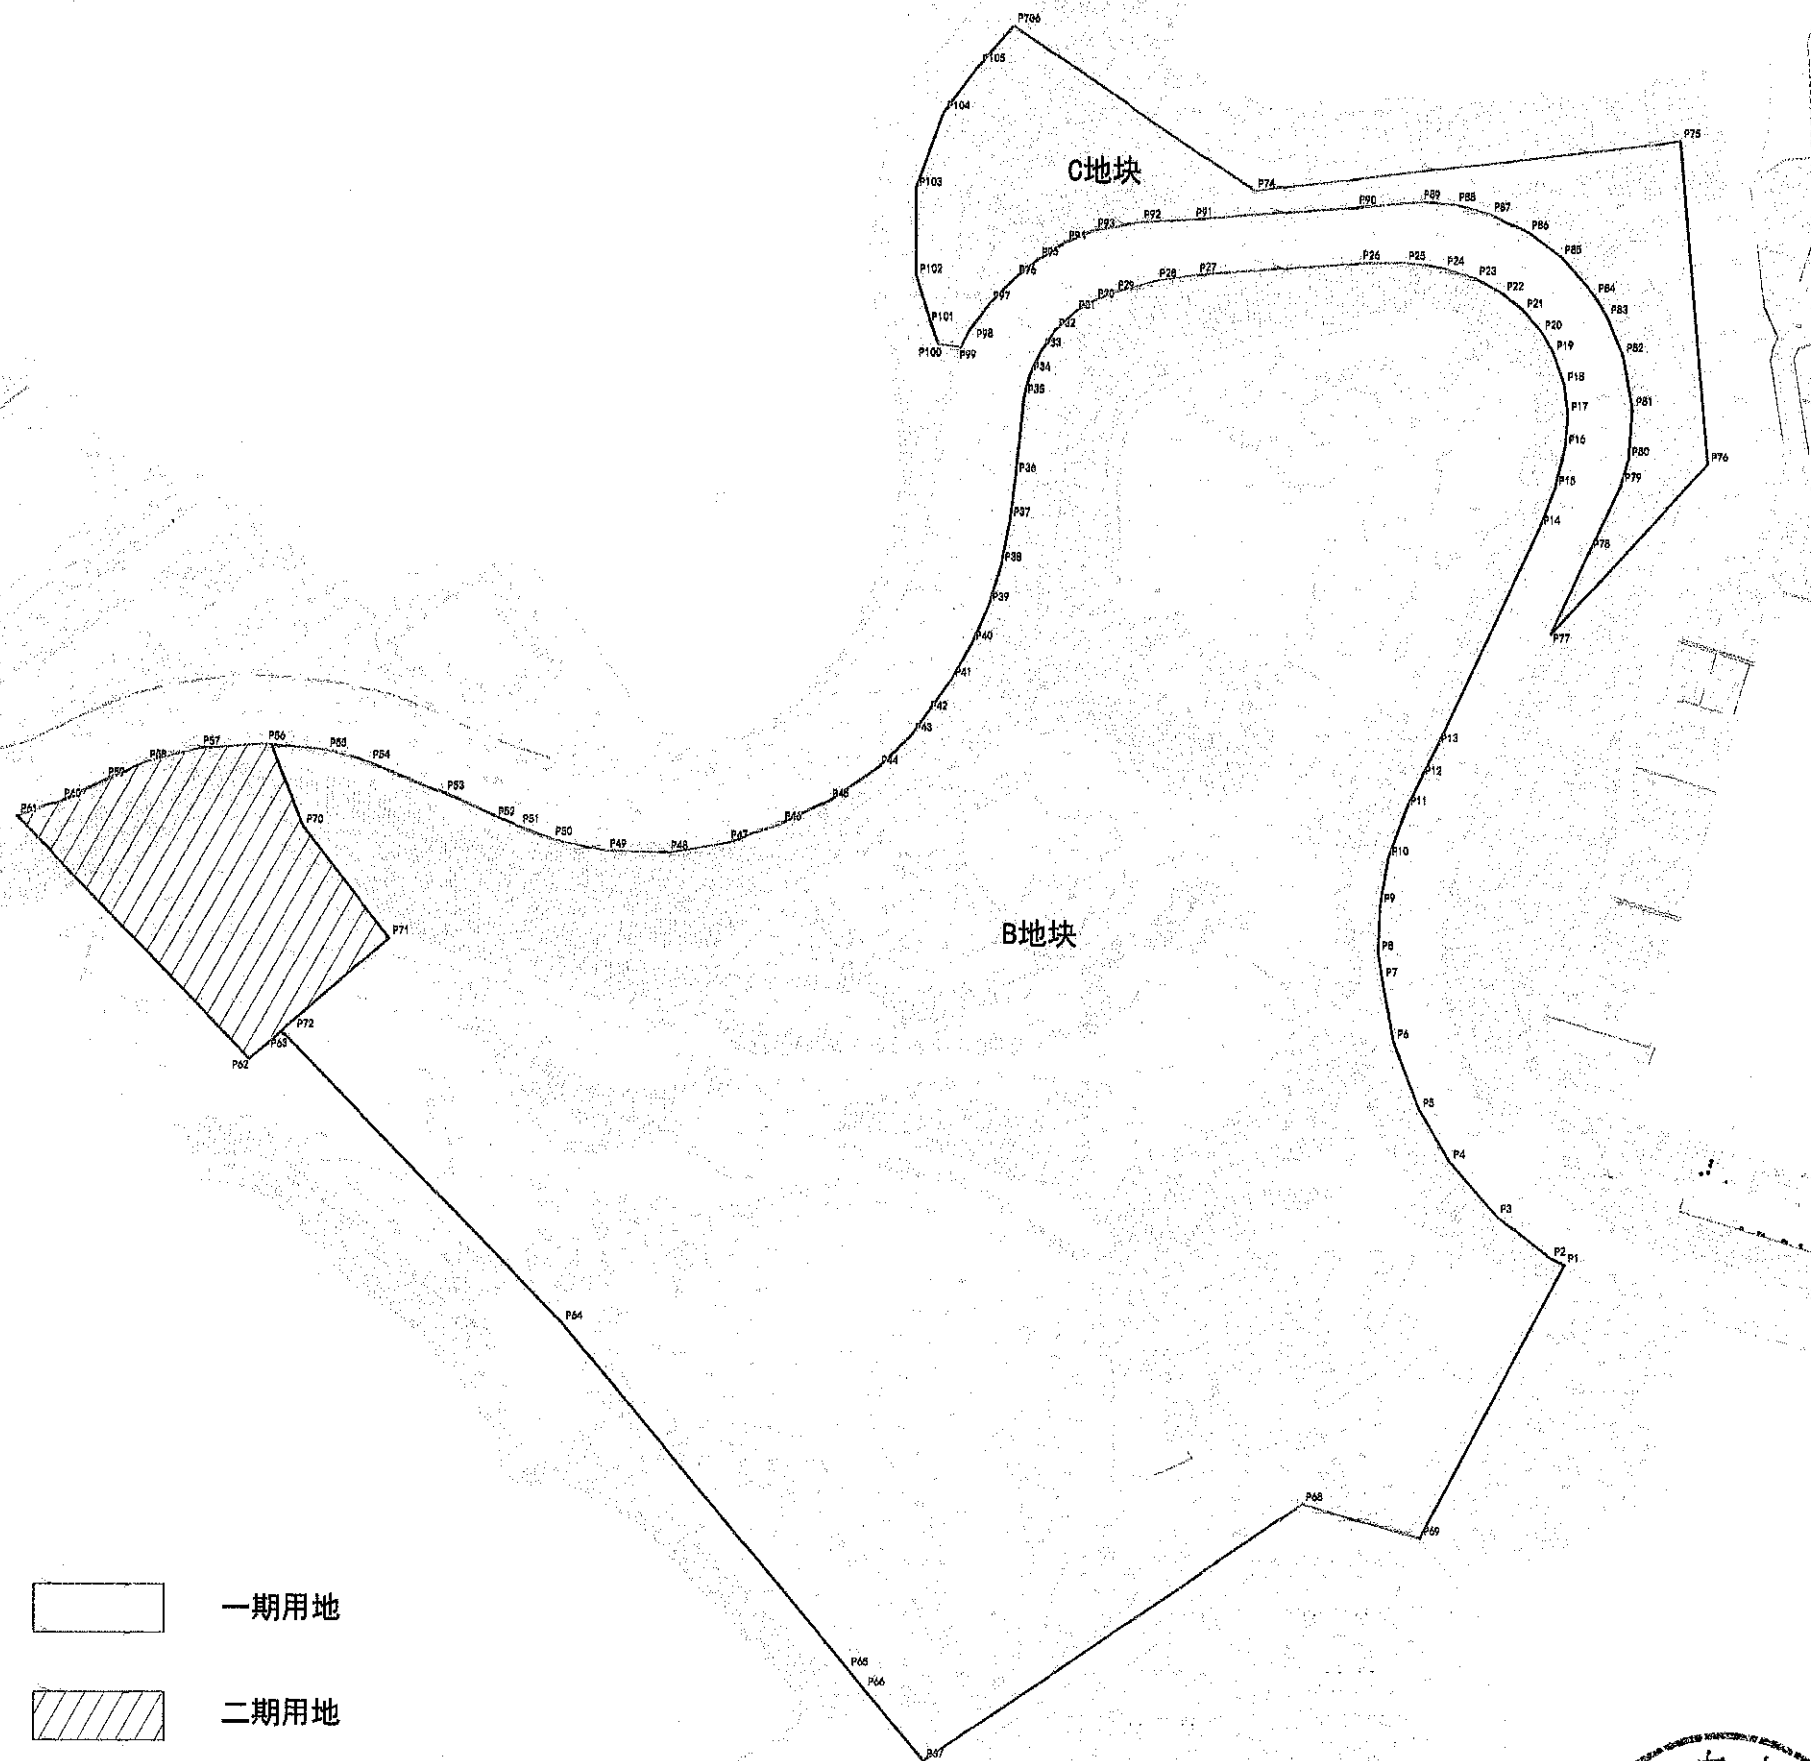

|    |      |   |             |   |            |
|----|------|---|-------------|---|------------|
| 点号 | P1   | X | 290748.773  | Y | 565323.205 |
| 点号 | P2   | X | 290748.333  | Y | 565318.165 |
| 点号 | P3   | X | 290748.311  | Y | 565297.505 |
| 点号 | P4   | X | 290748.017  | Y | 565279.422 |
| 点号 | P5   | X | 2908601.534 | Y | 565267.915 |
| 点号 | P6   | X | 2908627.674 | Y | 565253.053 |
| 点号 | P7   | X | 2908661.187 | Y | 565253.795 |
| 点号 | P8   | X | 2908661.842 | Y | 565252.205 |
| 点号 | P9   | X | 2908679.341 | Y | 565252.951 |
| 点号 | P10  | X | 2908677.082 | Y | 565252.953 |
| 点号 | P11  | X | 2908116.253 | Y | 565252.991 |
| 点号 | P12  | X | 2908187.665 | Y | 565248.522 |
| 点号 | P13  | X | 2908189.985 | Y | 565274.665 |
| 点号 | P14  | X | 2908182.914 | Y | 565313.384 |
| 点号 | P15  | X | 2908217.769 | Y | 565319.132 |
| 点号 | P16  | X | 2908233.376 | Y | 565322.913 |
| 点号 | P17  | X | 2908255.851 | Y | 565323.862 |
| 点号 | P18  | X | 2908277.201 | Y | 565322.424 |
| 点号 | P19  | X | 2908288.994 | Y | 565318.281 |
| 点号 | P20  | X | 2908296.849 | Y | 565313.760 |
| 点号 | P21  | X | 2908394.934 | Y | 565306.934 |
| 点号 | P22  | X | 2908311.409 | Y | 565299.301 |
| 点号 | P23  | X | 2908317.246 | Y | 565288.826 |
| 点号 | P24  | X | 2908320.931 | Y | 565276.450 |
| 点号 | P25  | X | 2908322.894 | Y | 565261.769 |
| 点号 | P26  | X | 2908322.964 | Y | 565244.482 |
| 点号 | P27  | X | 2908318.488 | Y | 565182.254 |
| 点号 | P28  | X | 2908311.388 | Y | 565164.973 |
| 点号 | P29  | X | 2908311.901 | Y | 565150.917 |
| 点号 | P30  | X | 2908308.647 | Y | 565143.115 |
| 点号 | P31  | X | 2908304.288 | Y | 565135.873 |
| 点号 | P32  | X | 2908277.315 | Y | 565128.184 |
| 点号 | P33  | X | 2908289.945 | Y | 565122.811 |
| 点号 | P34  | X | 2908280.846 | Y | 565118.615 |
| 点号 | P35  | X | 2908272.324 | Y | 565116.408 |
| 点号 | P36  | X | 2908252.511 | Y | 565113.277 |
| 点号 | P37  | X | 2908225.733 | Y | 565111.220 |
| 点号 | P38  | X | 2908275.683 | Y | 565107.928 |
| 点号 | P39  | X | 2908193.653 | Y | 565103.334 |
| 点号 | P40  | X | 2908178.912 | Y | 565096.922 |
| 点号 | P41  | X | 2908165.033 | Y | 565090.076 |
| 点号 | P42  | X | 2908152.241 | Y | 565079.811 |
| 点号 | P43  | X | 2908144.016 | Y | 565073.976 |
| 点号 | P44  | X | 2908131.623 | Y | 565068.882 |
| 点号 | P45  | X | 2908119.047 | Y | 565042.327 |
| 点号 | P46  | X | 2908110.300 | Y | 565024.162 |
| 点号 | P47  | X | 2908103.360 | Y | 565003.900 |
| 点号 | P48  | X | 2908099.368 | Y | 564981.022 |
| 点号 | P49  | X | 2908099.931 | Y | 564957.888 |
| 点号 | P50  | X | 2908104.521 | Y | 564937.082 |
| 点号 | P51  | X | 2908109.226 | Y | 564924.657 |
| 点号 | P52  | X | 2908111.437 | Y | 564918.831 |
| 点号 | P53  | X | 2908121.949 | Y | 564895.984 |
| 点号 | P54  | X | 2908135.750 | Y | 564867.669 |
| 点号 | P55  | X | 2908136.257 | Y | 564851.235 |
| 点号 | P56  | X | 2908140.872 | Y | 564827.841 |
| 点号 | P57  | X | 2908138.902 | Y | 564805.004 |
| 点号 | P58  | X | 2908133.597 | Y | 564782.815 |
| 点号 | P59  | X | 2908126.845 | Y | 564767.017 |
| 点号 | P60  | X | 2908118.611 | Y | 564750.334 |
| 点号 | P61  | X | 2908112.938 | Y | 564733.751 |
| 点号 | P62  | X | 2908121.245 | Y | 564822.211 |
| 点号 | P63  | X | 2908091.702 | Y | 564834.368 |
| 点号 | P64  | X | 2907920.657 | Y | 564941.523 |
| 点号 | P65  | X | 2907789.776 | Y | 565050.255 |
| 点号 | P66  | X | 2907782.213 | Y | 565056.537 |
| 点号 | P67  | X | 2907785.067 | Y | 565079.087 |
| 点号 | P68  | X | 2907852.237 | Y | 565223.676 |
| 点号 | P69  | X | 2907839.203 | Y | 565266.356 |
| 点号 | P70  | X | 2908189.256 | Y | 564842.428 |
| 点号 | P71  | X | 2908066.934 | Y | 564875.328 |
| 点号 | P72  | X | 2908031.711 | Y | 564834.394 |
| 点号 | P73  | X | 2908412.914 | Y | 565112.108 |
| 点号 | P74  | X | 2908300.183 | Y | 565204.485 |
| 点号 | P75  | X | 2908399.105 | Y | 565366.452 |
| 点号 | P76  | X | 2908346.413 | Y | 565377.153 |
| 点号 | P77  | X | 2908181.939 | Y | 565317.454 |
| 点号 | P78  | X | 2908213.919 | Y | 565332.408 |
| 点号 | P79  | X | 2908238.899 | Y | 565344.276 |
| 点号 | P80  | X | 2908248.813 | Y | 565347.053 |
| 点号 | P81  | X | 2908267.577 | Y | 565348.525 |
| 点号 | P82  | X | 2908238.135 | Y | 565344.862 |
| 点号 | P83  | X | 2908262.625 | Y | 565338.978 |
| 点号 | P84  | X | 2908310.792 | Y | 565334.027 |
| 点号 | P85  | X | 2908325.440 | Y | 565321.102 |
| 点号 | P86  | X | 2908334.685 | Y | 565308.599 |
| 点号 | P87  | X | 2908341.518 | Y | 565294.248 |
| 点号 | P88  | X | 2908345.142 | Y | 565280.810 |
| 点号 | P89  | X | 2908345.965 | Y | 565267.487 |
| 点号 | P90  | X | 2908343.910 | Y | 565242.975 |
| 点号 | P91  | X | 2908339.434 | Y | 565180.757 |
| 点号 | P92  | X | 2908338.527 | Y | 565160.934 |
| 点号 | P93  | X | 2908336.238 | Y | 565143.126 |
| 点号 | P94  | X | 2908330.597 | Y | 565132.008 |
| 点号 | P95  | X | 2908334.371 | Y | 565121.665 |
| 点号 | P96  | X | 2908317.528 | Y | 565112.963 |
| 点号 | P97  | X | 2908307.655 | Y | 565103.235 |
| 点号 | P98  | X | 2908277.121 | Y | 565095.419 |
| 点号 | P99  | X | 2908291.023 | Y | 565092.260 |
| 点号 | P100 | X | 2908292.128 | Y | 565083.581 |
| 点号 | P101 | X | 2908298.163 | Y | 565081.438 |
| 点号 | P102 | X | 2908317.906 | Y | 565075.182 |
| 点号 | P103 | X | 2908350.711 | Y | 565074.911 |
| 点号 | P104 | X | 2908377.716 | Y | 565085.408 |
| 点号 | P105 | X | 2908397.693 | Y | 565096.924 |
| 点号 | P106 | X | 2908412.914 | Y | 565112.108 |

三明市城乡改造有限公司“三明市徐碧‘城中村’改造安置房项目（三明市徐碧村甲头B、C地块）选址红线图，总用地面积17.5031公顷，其中B地块16.0304公顷，C地块1.4727公顷。一期用地面积16.6297公顷，二期用地面积0.8734公顷。

