


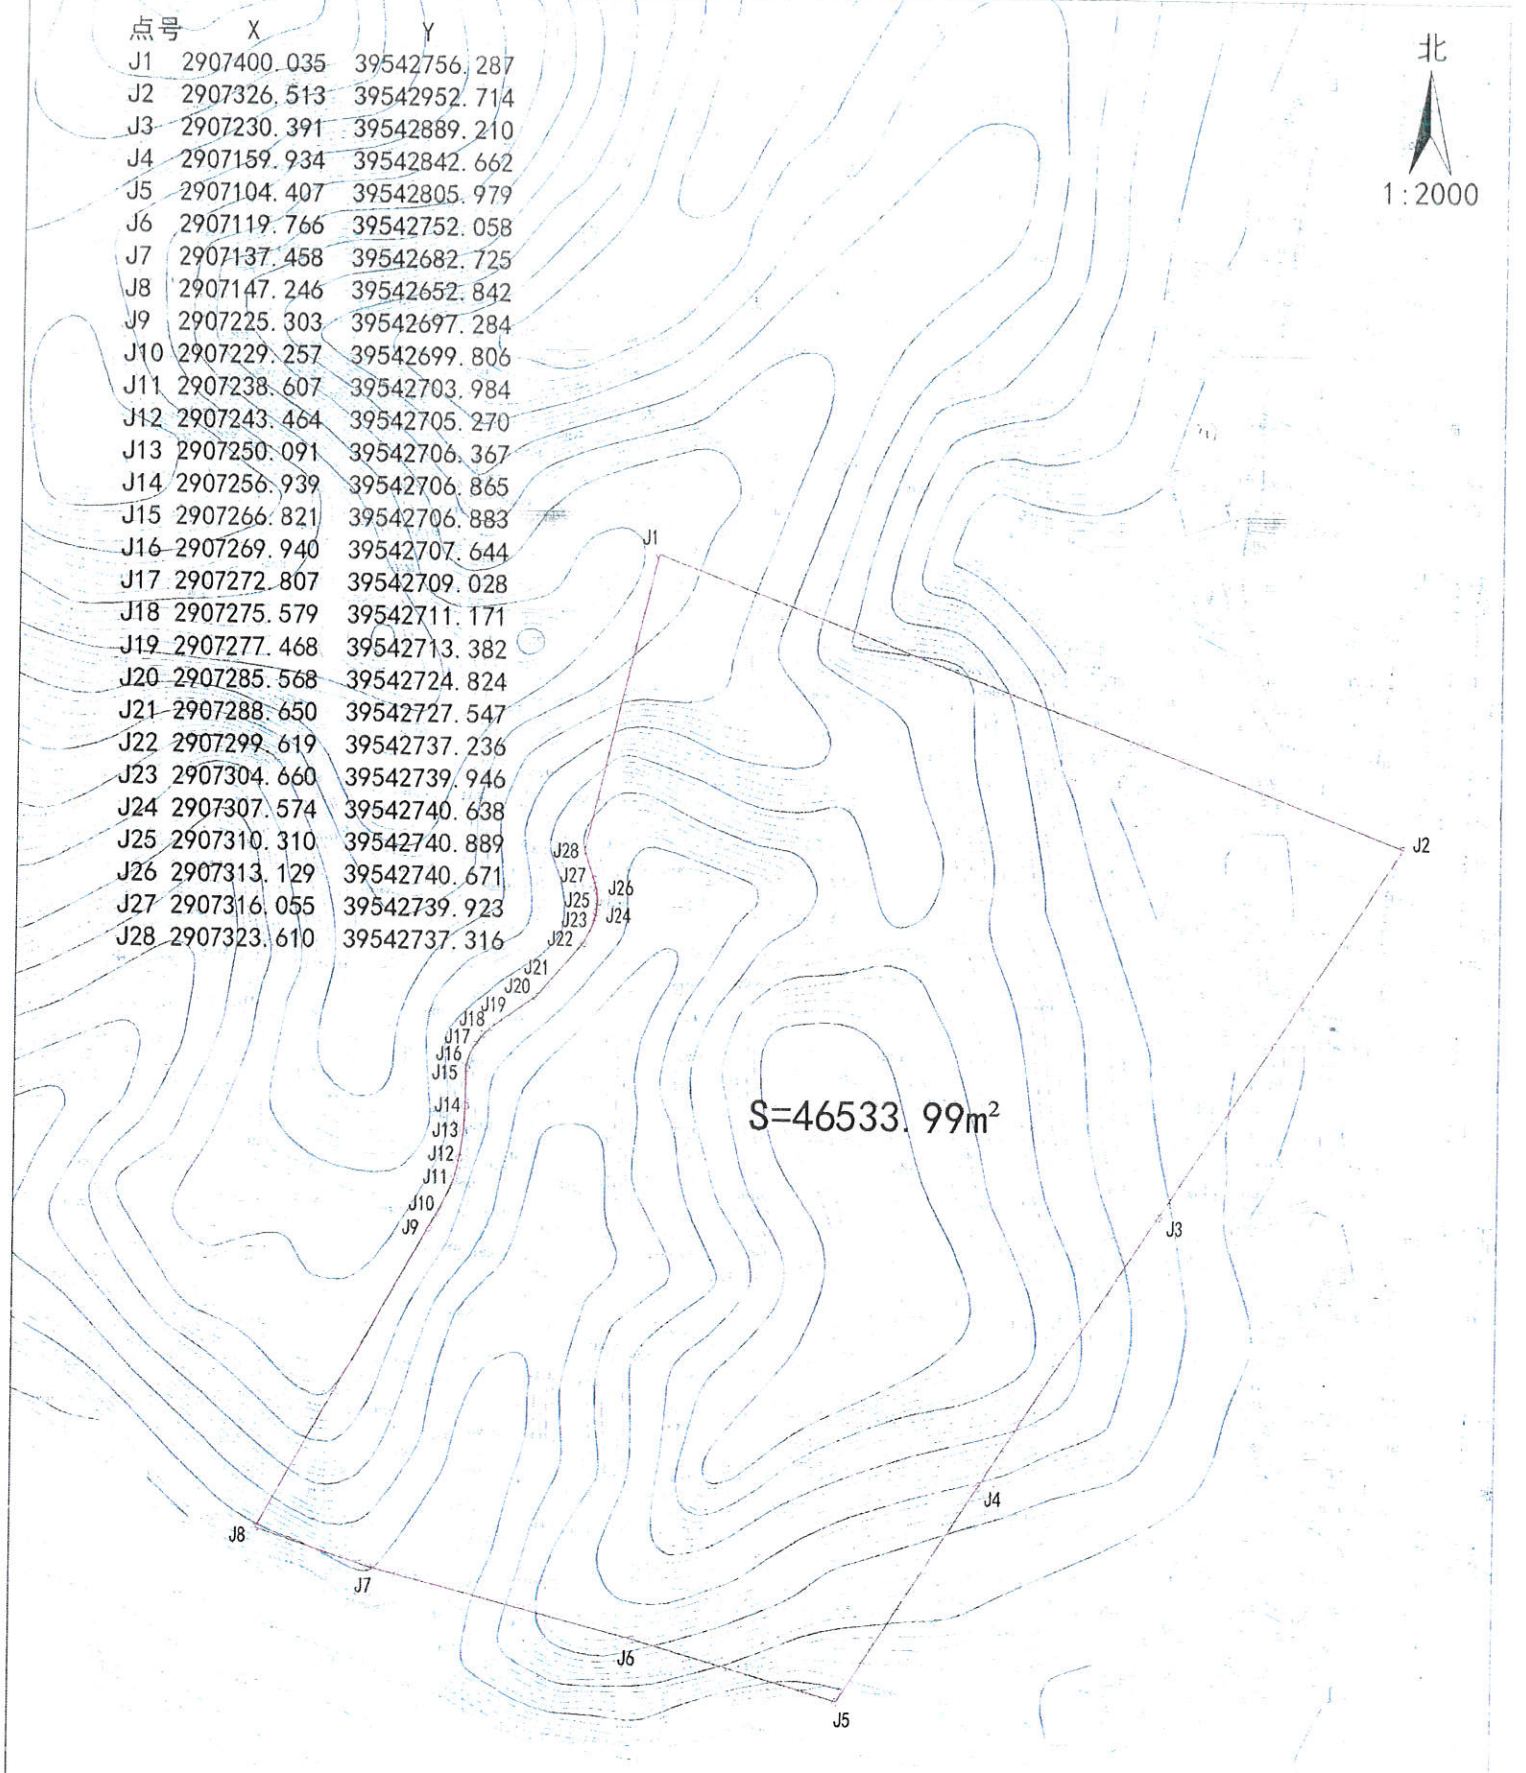

1:2000


点号	X	Y
J1	2907400.035	39542756.287
J2	2907326.513	39542952.714
J3	2907230.391	39542889.210
J4	2907159.934	39542842.662
J5	2907104.407	39542805.979
J6	2907119.766	39542752.058
J7	2907137.458	39542682.725
J8	2907147.246	39542652.842
J9	2907225.303	39542697.284
J10	2907229.257	39542699.806
J11	2907238.607	39542703.984
J12	2907243.464	39542705.270
J13	2907250.091	39542706.367
J14	2907256.939	39542706.865
J15	2907266.821	39542706.883
J16	2907269.940	39542707.644
J17	2907272.807	39542709.028
J18	2907275.579	39542711.171
J19	2907277.468	39542713.382
J20	2907285.568	39542724.824
J21	2907288.650	39542727.547
J22	2907299.619	39542737.236
J23	2907304.660	39542739.946
J24	2907307.574	39542740.638
J25	2907310.310	39542740.889
J26	2907313.129	39542740.671
J27	2907316.055	39542739.923
J28	2907323.610	39542737.316



S=46533.99m²

福建汇氟电子材料有限公司预申请工业用地红线图，用地面积46533.99平方米。

三明市三元区自然资源局
2021年6月3日

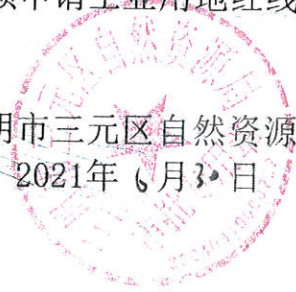

2000国家大地坐标系。
1985国家高程基准，等高距为1.0米。
1996年版图式。