


三明梅列碧湖220千伏输变电（搬迁）工程（站区）勘测定界图

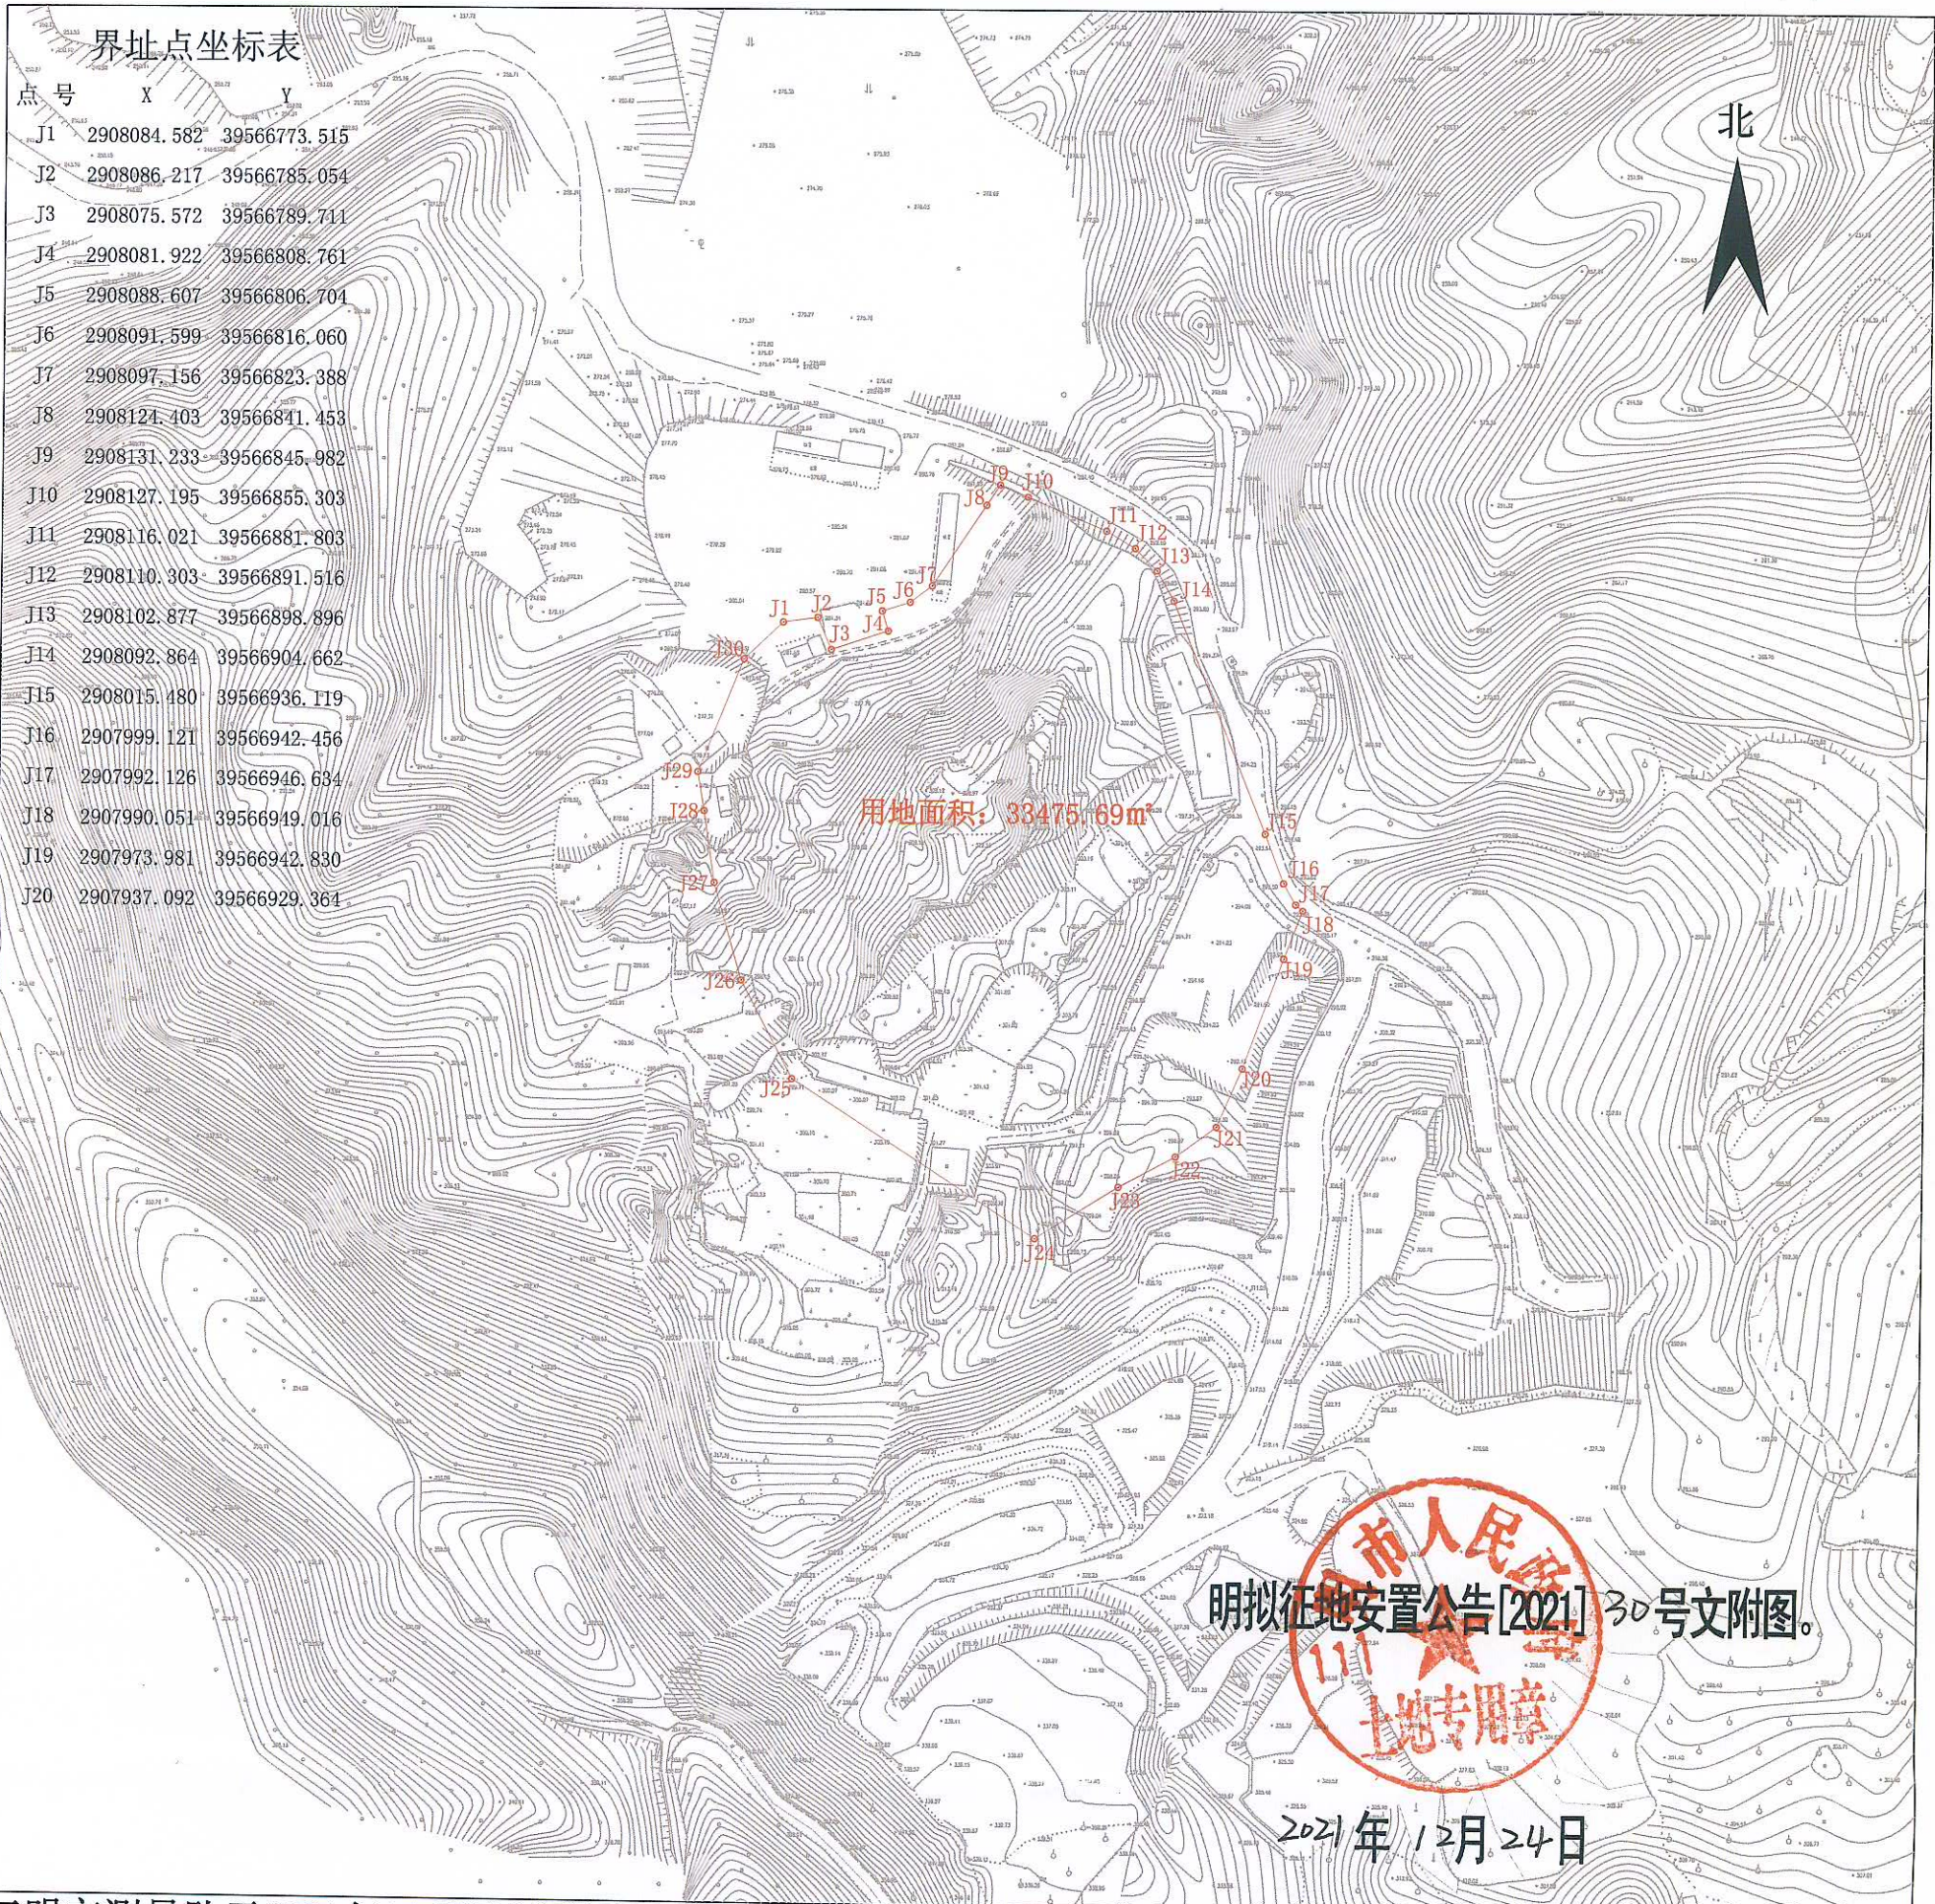

三明市测量队

三明市测量队于2021年11月测制成图。
2000国家大地坐标系，中央子午线117° 00'。
1985国家高程基准，等高距1.0米。
2017图式

1: 2500

测量员: 张祥宝 林小强
绘图员: 张祥宝
检查员: 曹俊彦