



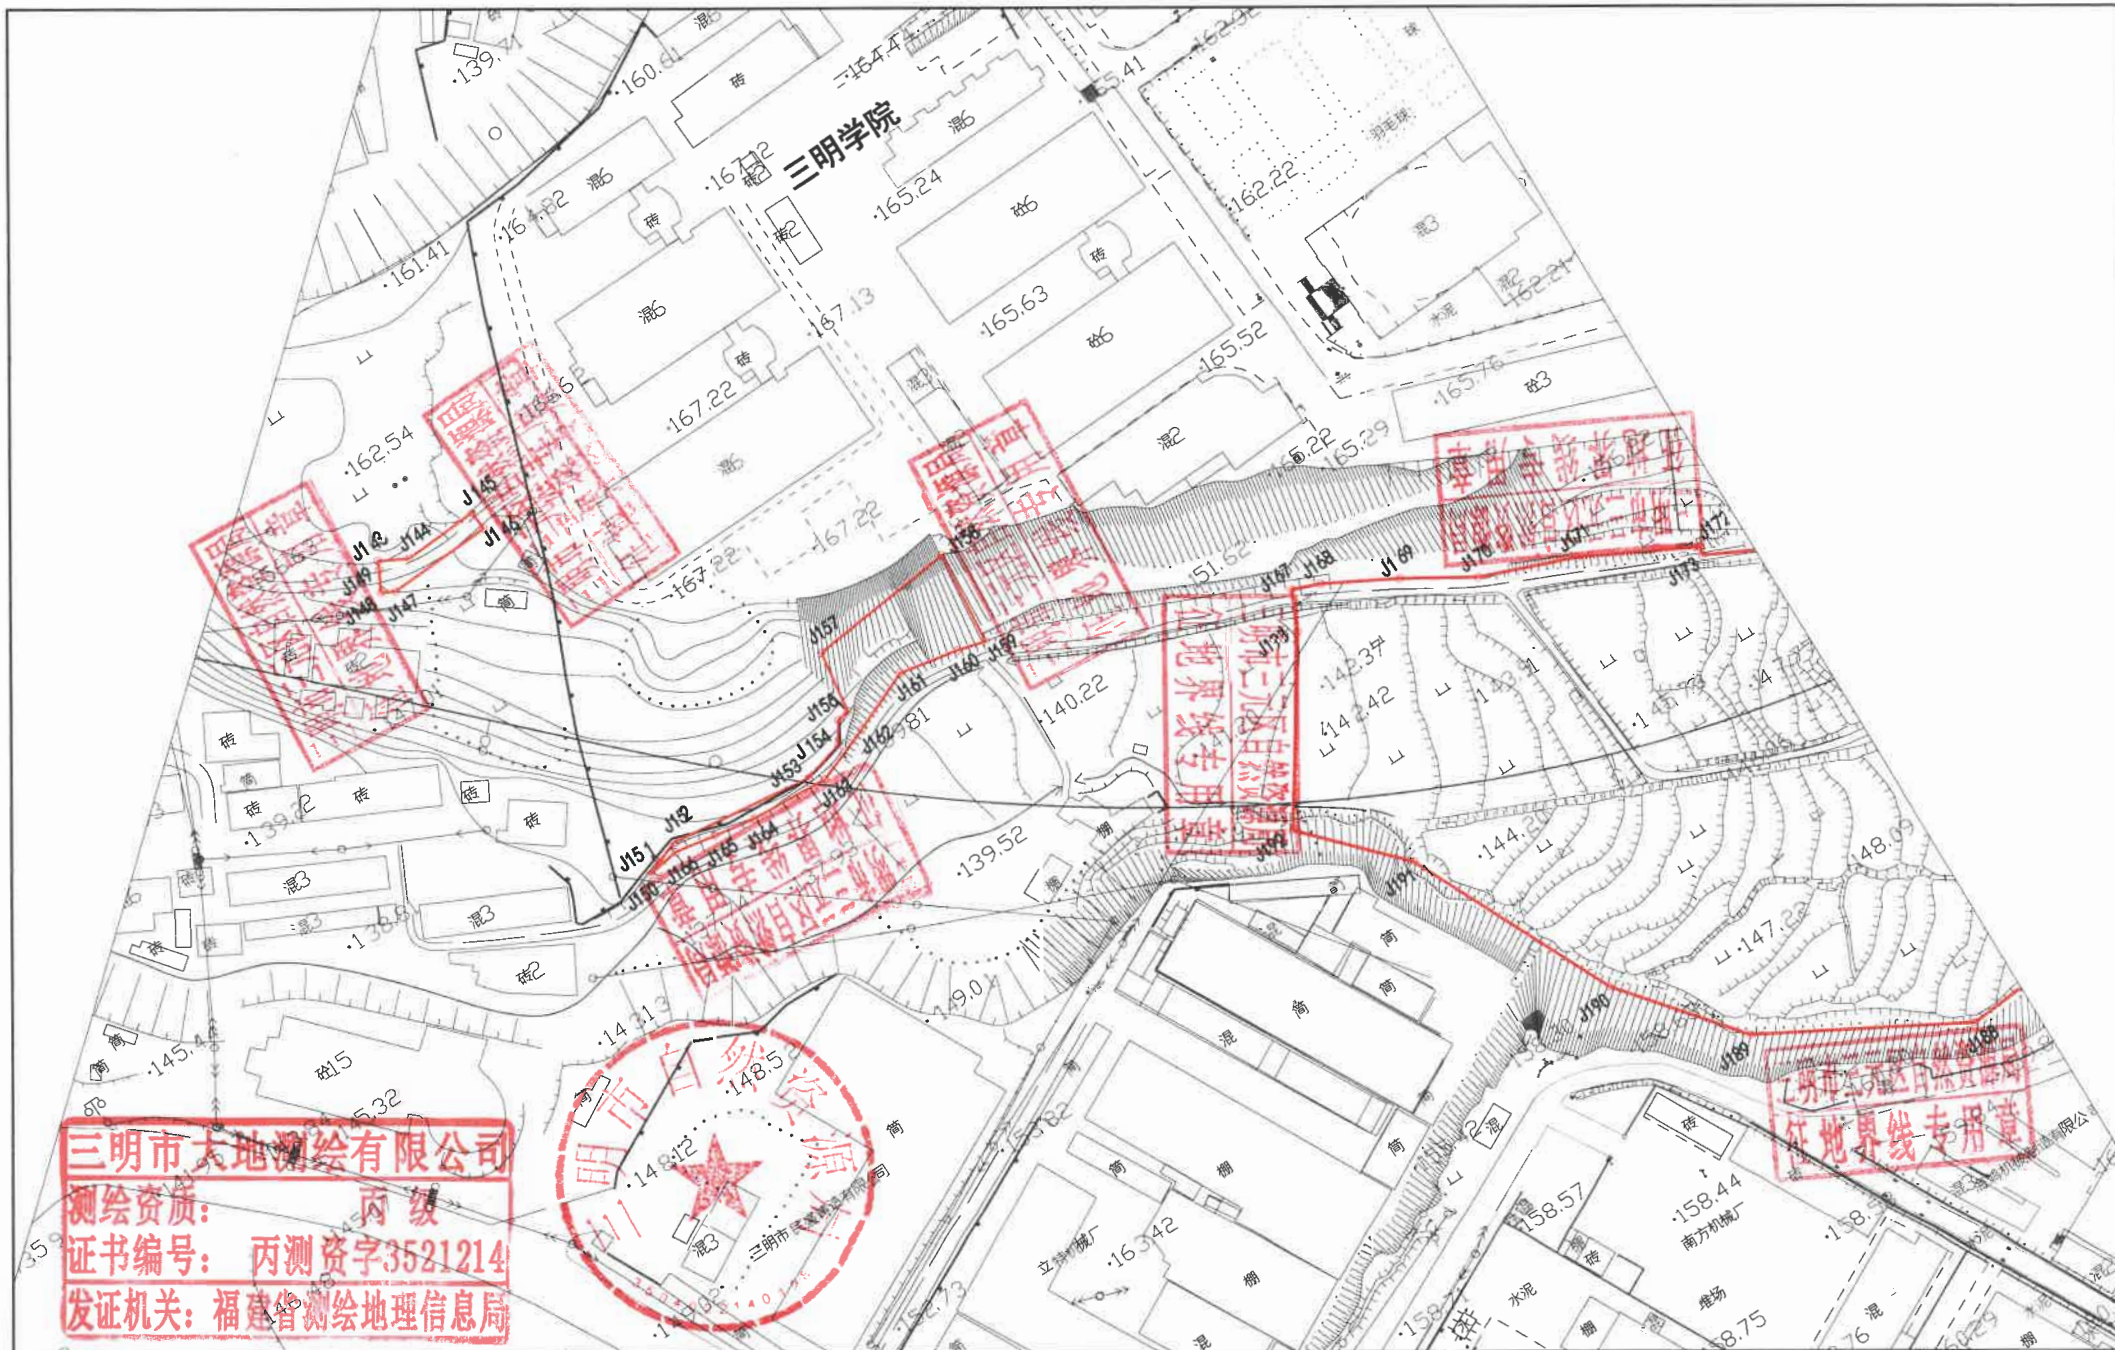

三明市大地测绘有限公司
测绘资质：丙级
证书编号：丙测资字3521214
发证机关：福建省测绘地理信息局






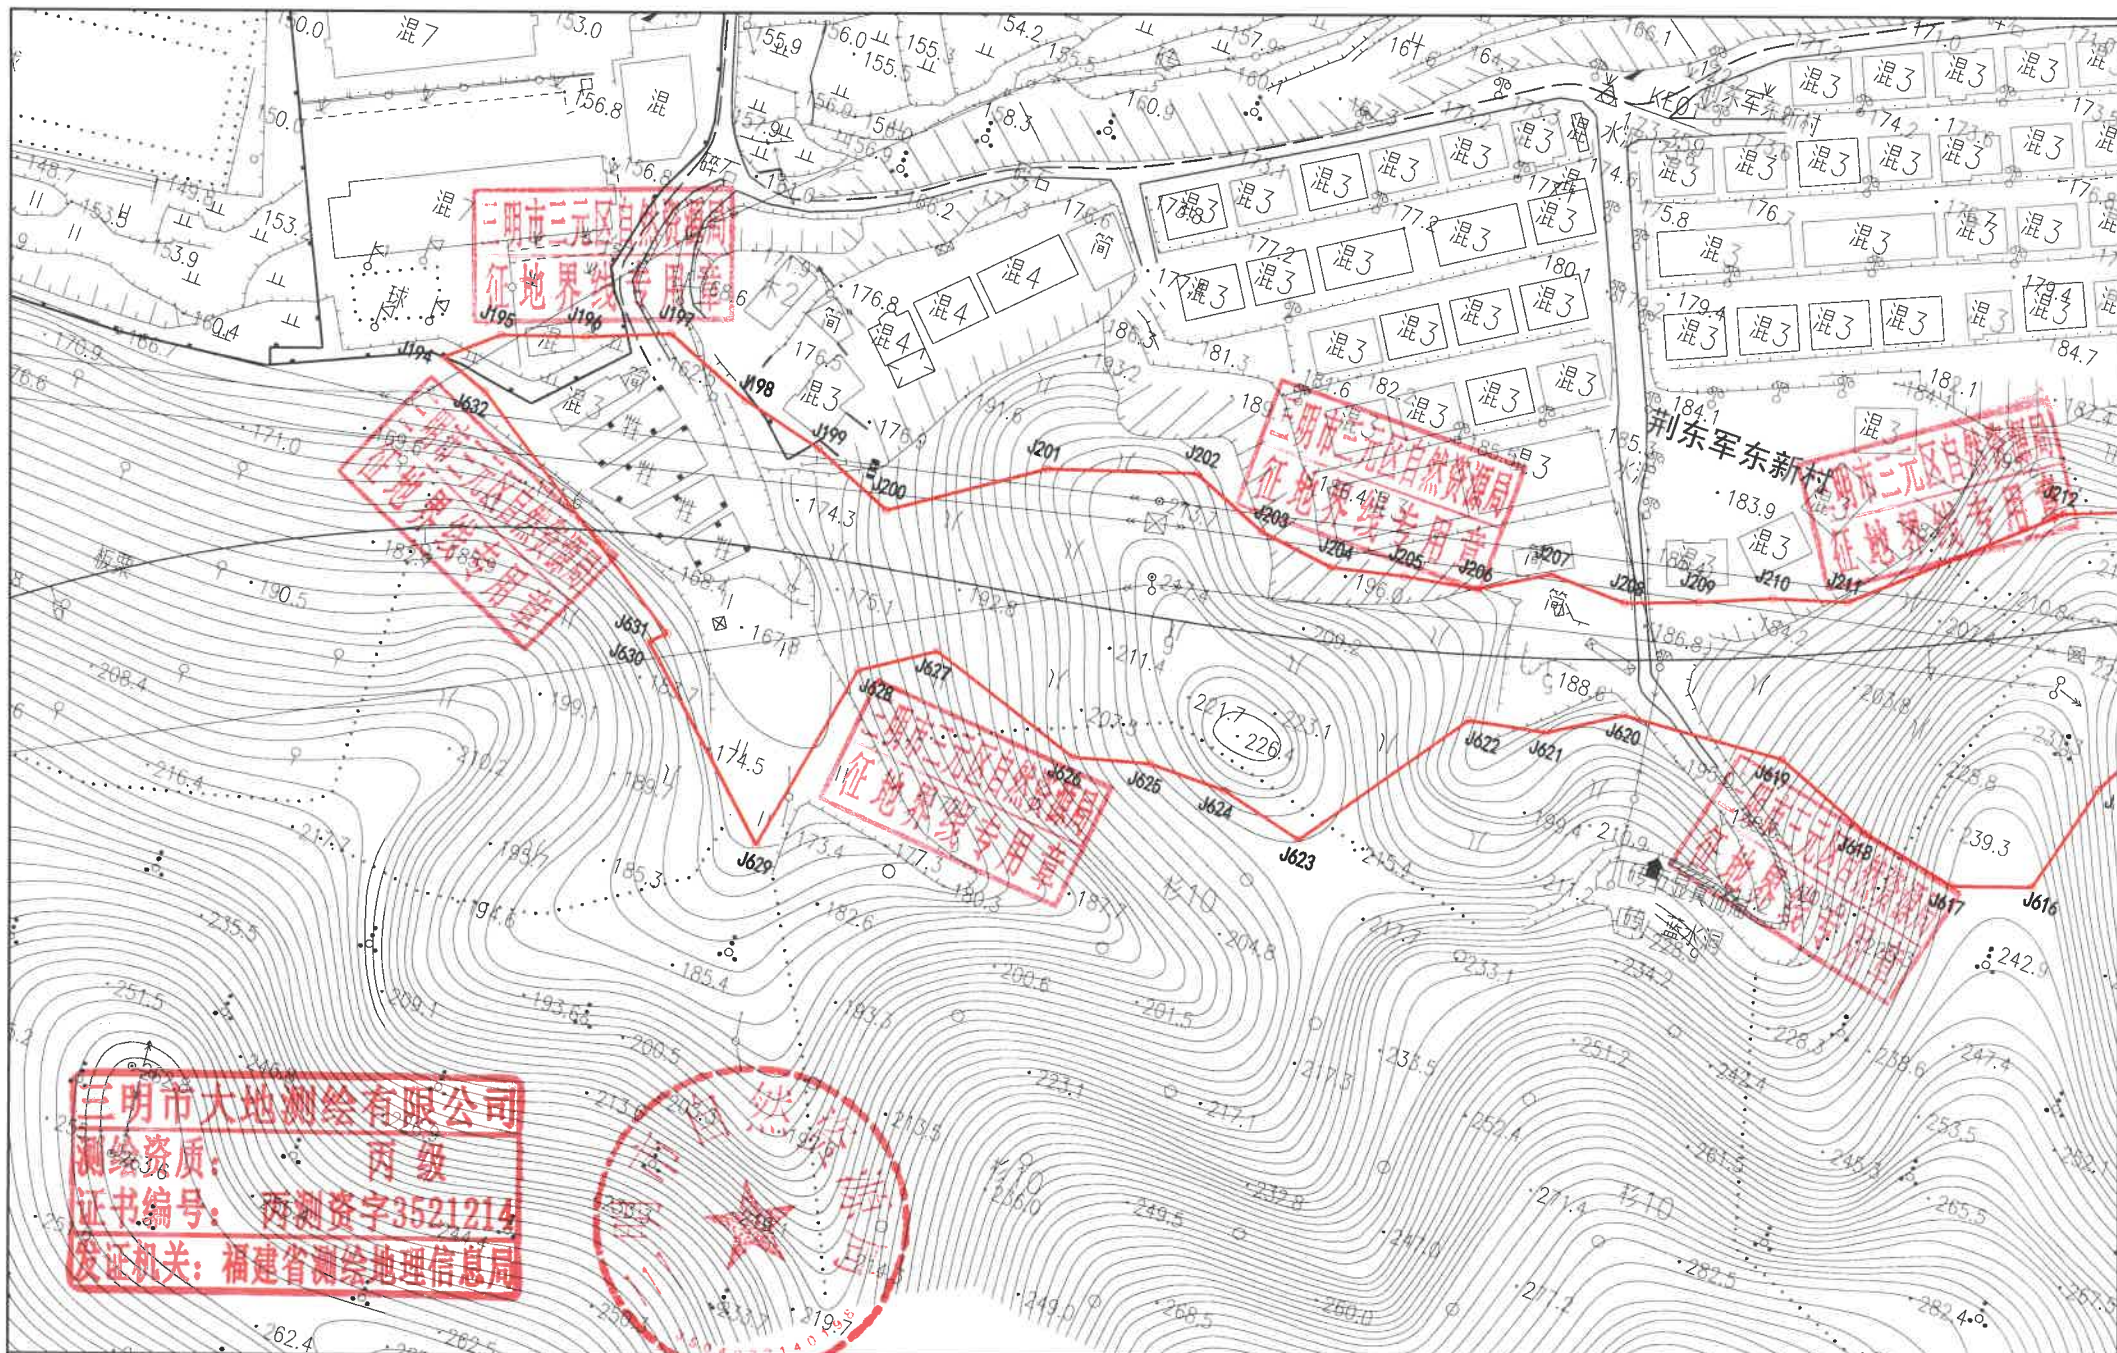

三明市大地测绘有限公司
 测绘资质: 丙级
 证书编号: 丙测资字3521214
 发证机关: 福建省测绘地理信息局

国道534(横六线)三元区村头至荆东二期工程勘测定界图

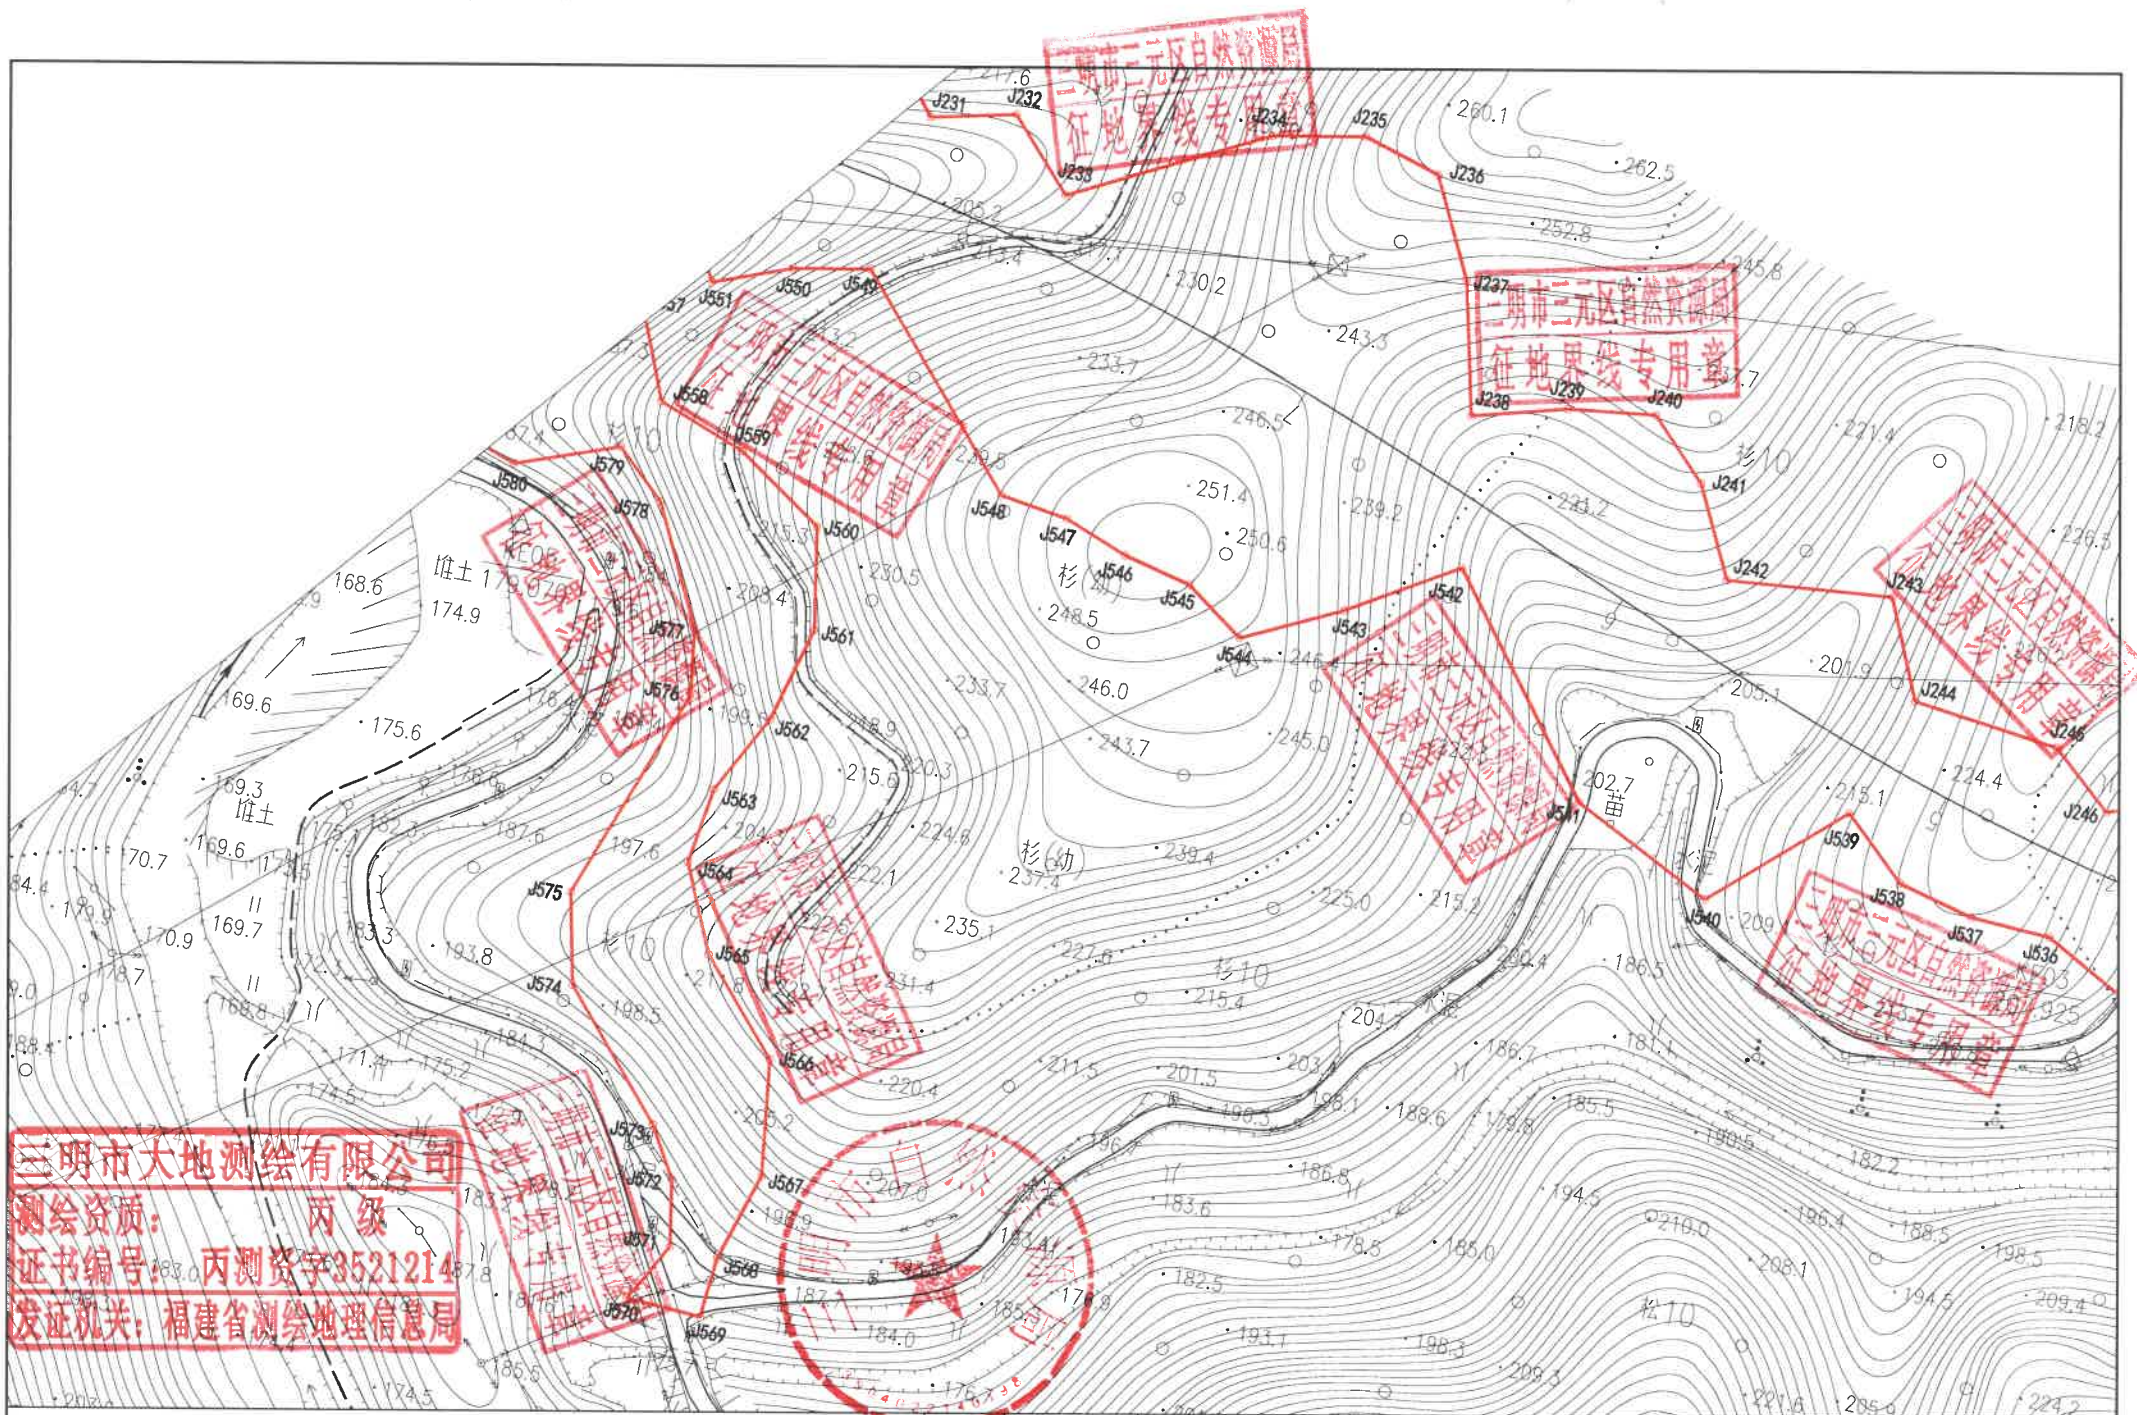

国道534（横六线）三元区村头至荆东二期工程勘测定界图

绘图

林向华

复核


蔡建平


日期

2020年9月

1、本图比例1:2000。
 2、2000国家大地坐标系，中央子午线为117°。

第 6 页,共13页

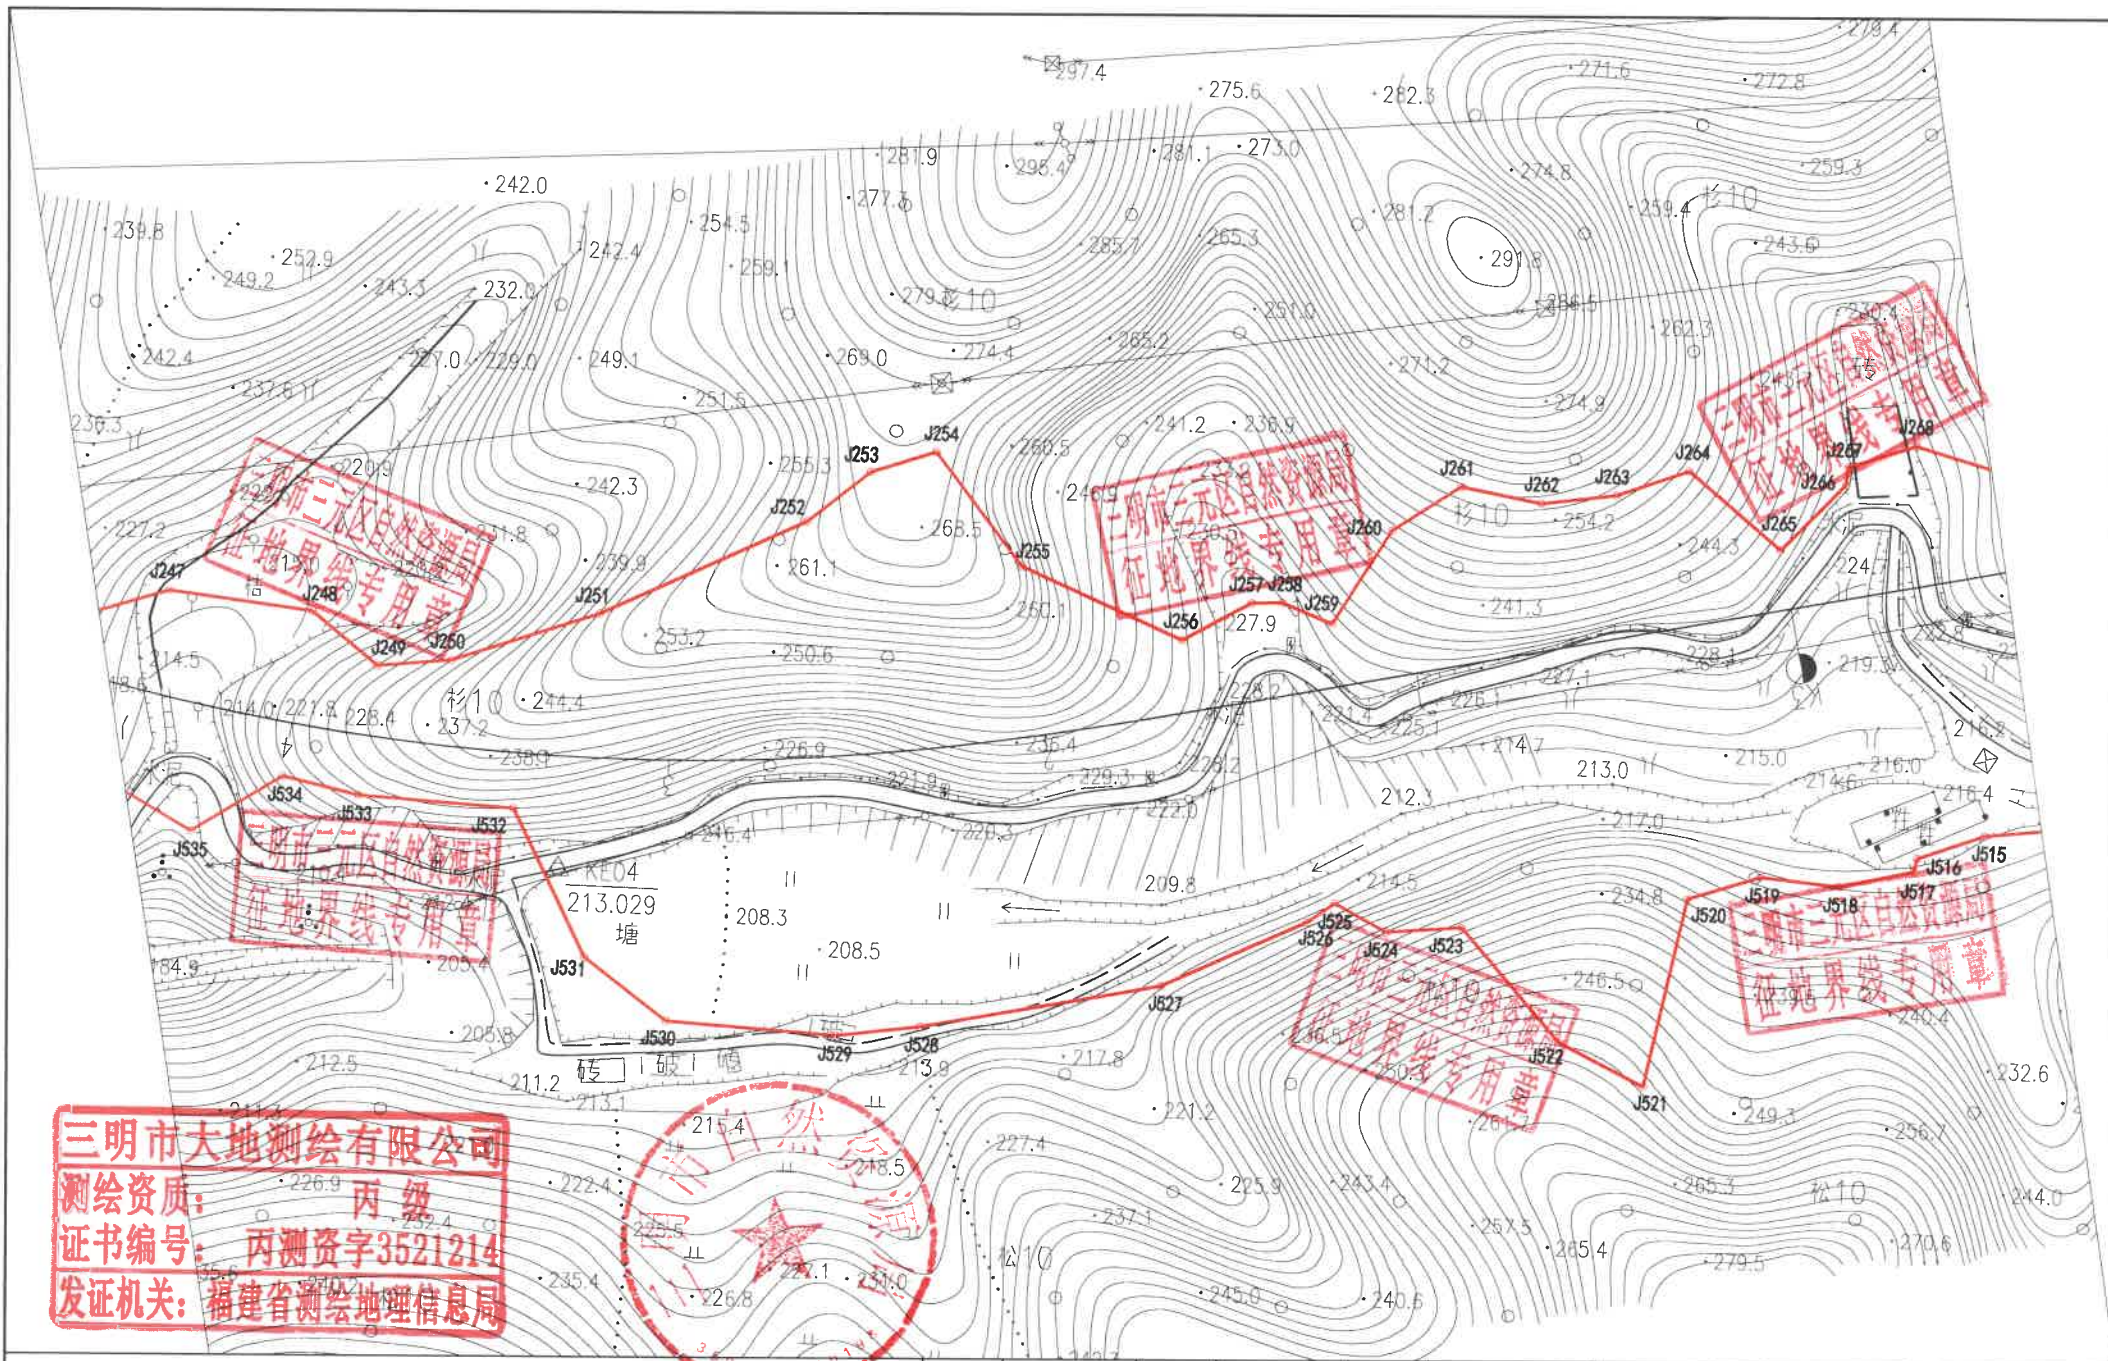

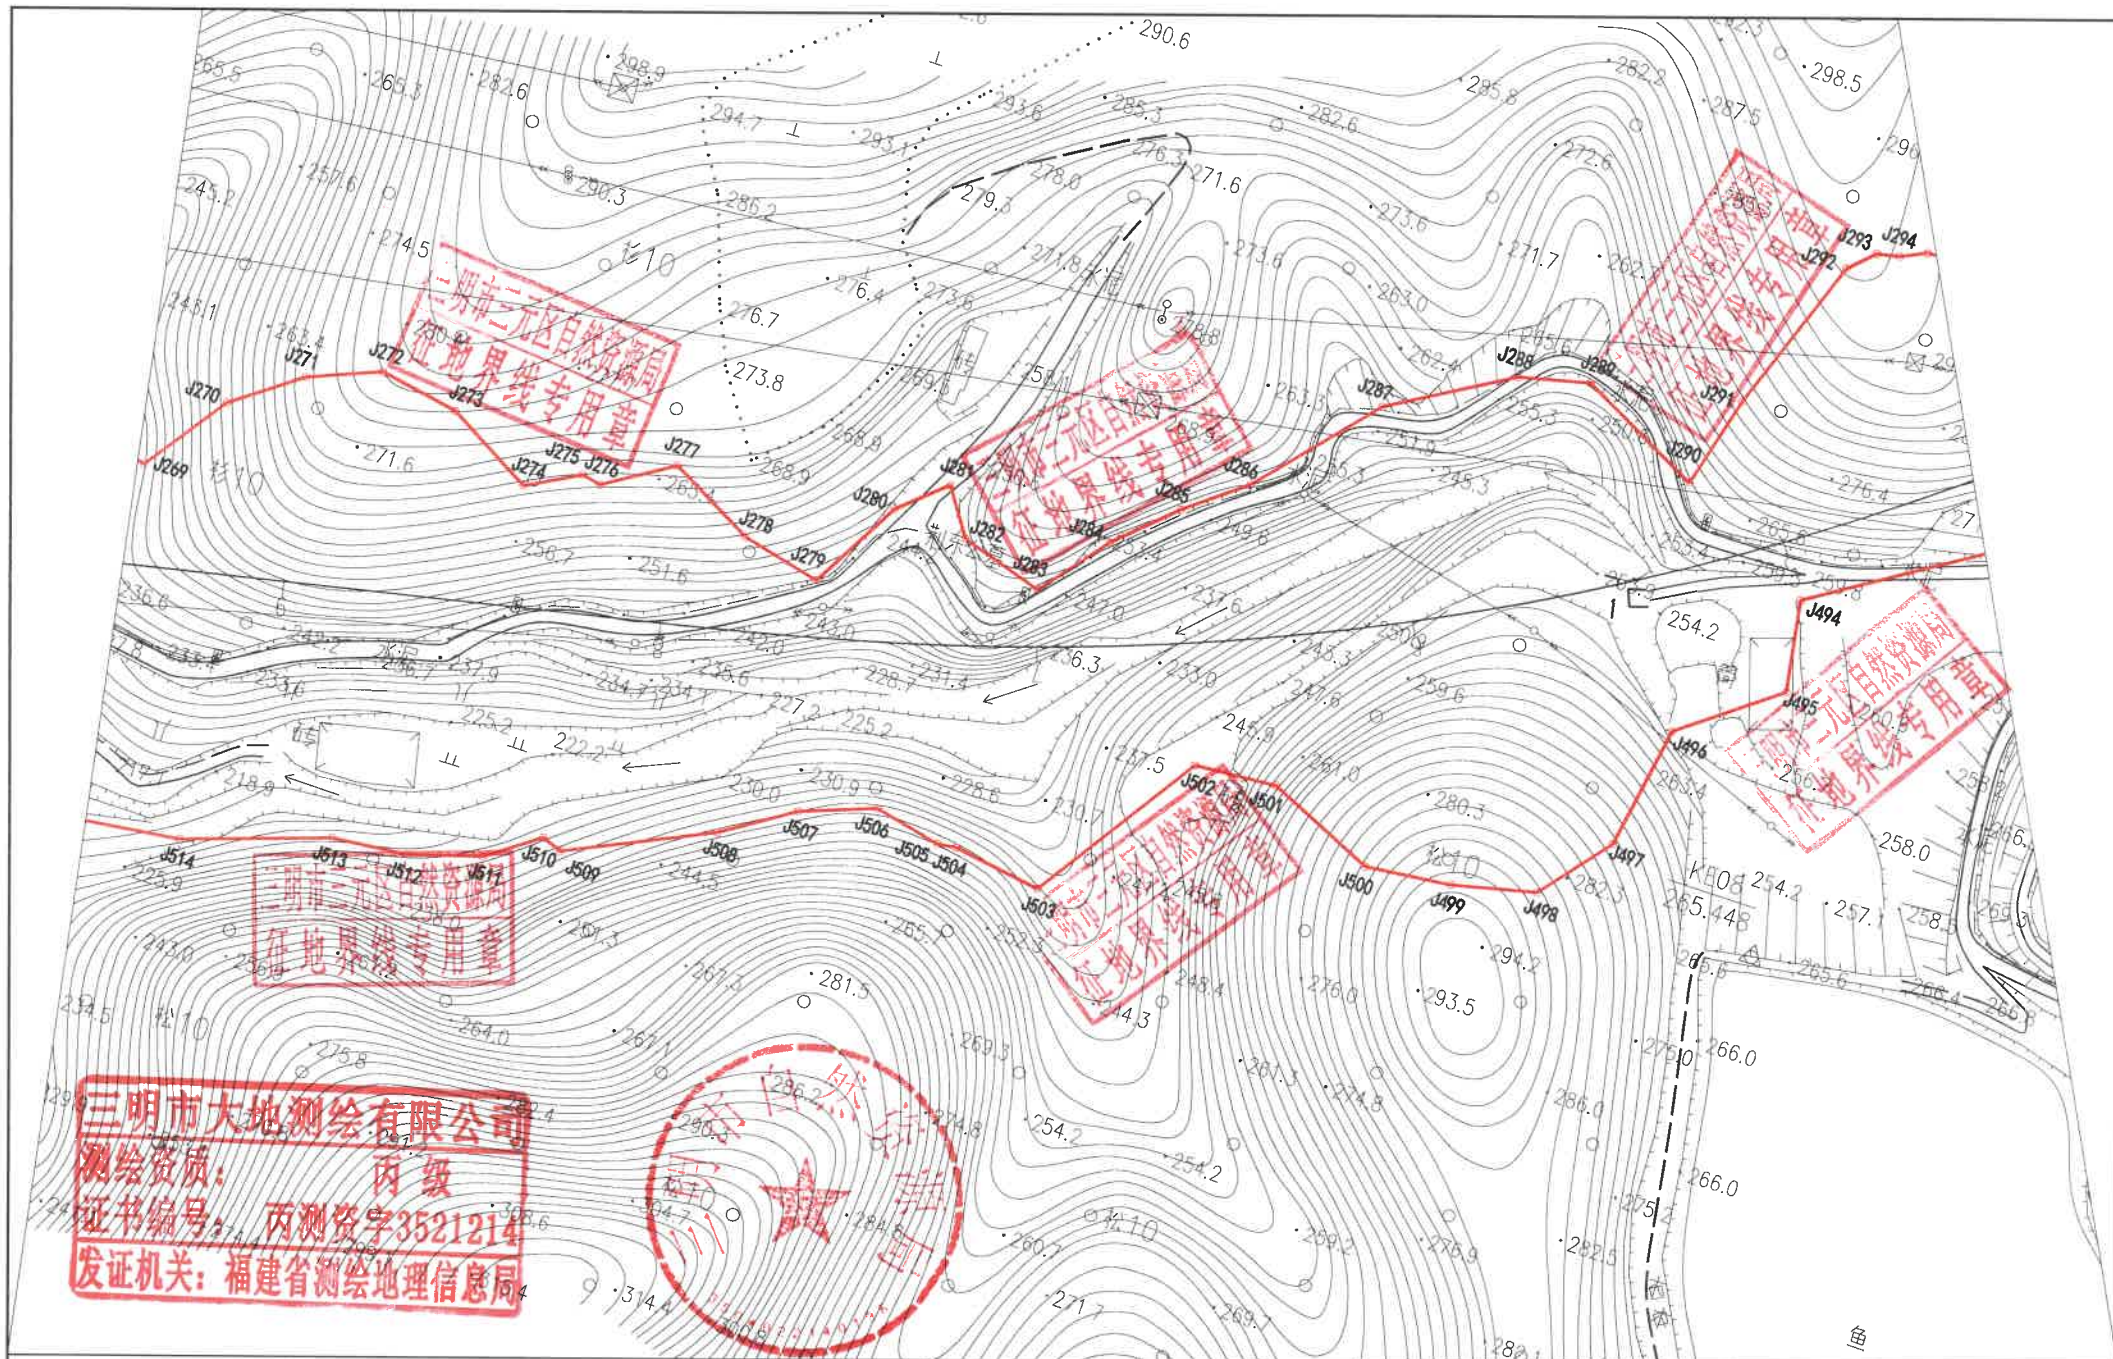

三明市大地测绘有限公司
 测绘资质：丙级
 证书编号：丙测资字3521214
 发证机关：福建省测绘地理信息局

国道534（横六线）三元区村头至荆东二期工程勘测定界图

绘图

林向华

复核


蔡建平

日期

2020年9月

1、本图比例1:2000。
 2、2000国家大地坐标系，中央子午线为117°。

第 8 页, 共13页

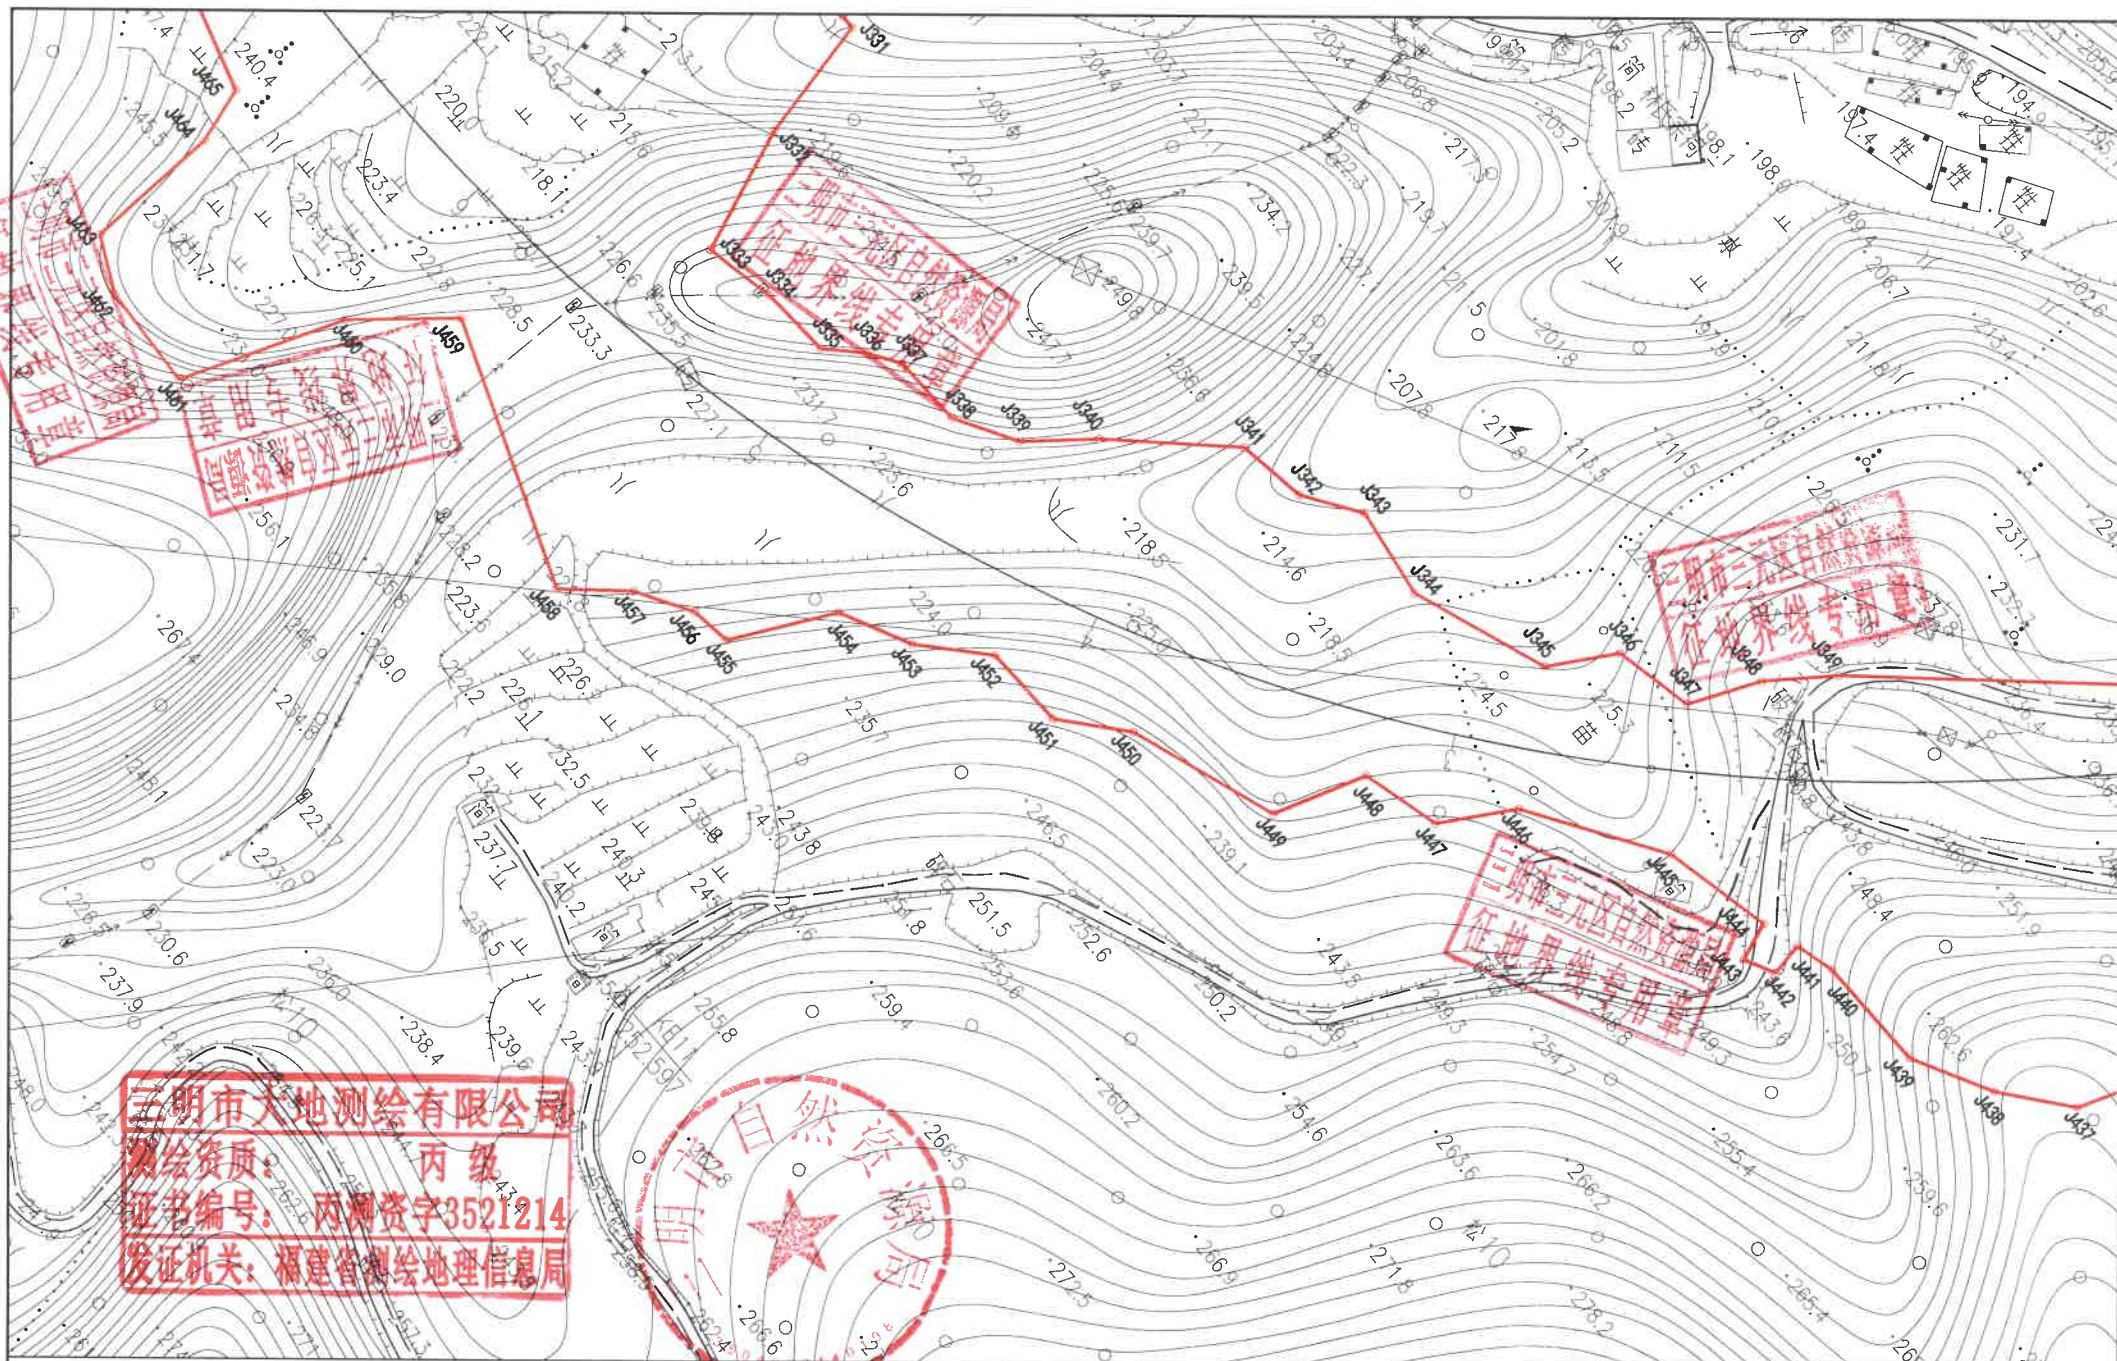

国道534（横六线）三元区村头至荆东二期工程勘测定界图

绘图

林向华

复核


蔡建平

日期

2020年9月

1、本图比例1:2000。
2、2000国家大地坐标系，中央子午线为117°。

第11页,共13页

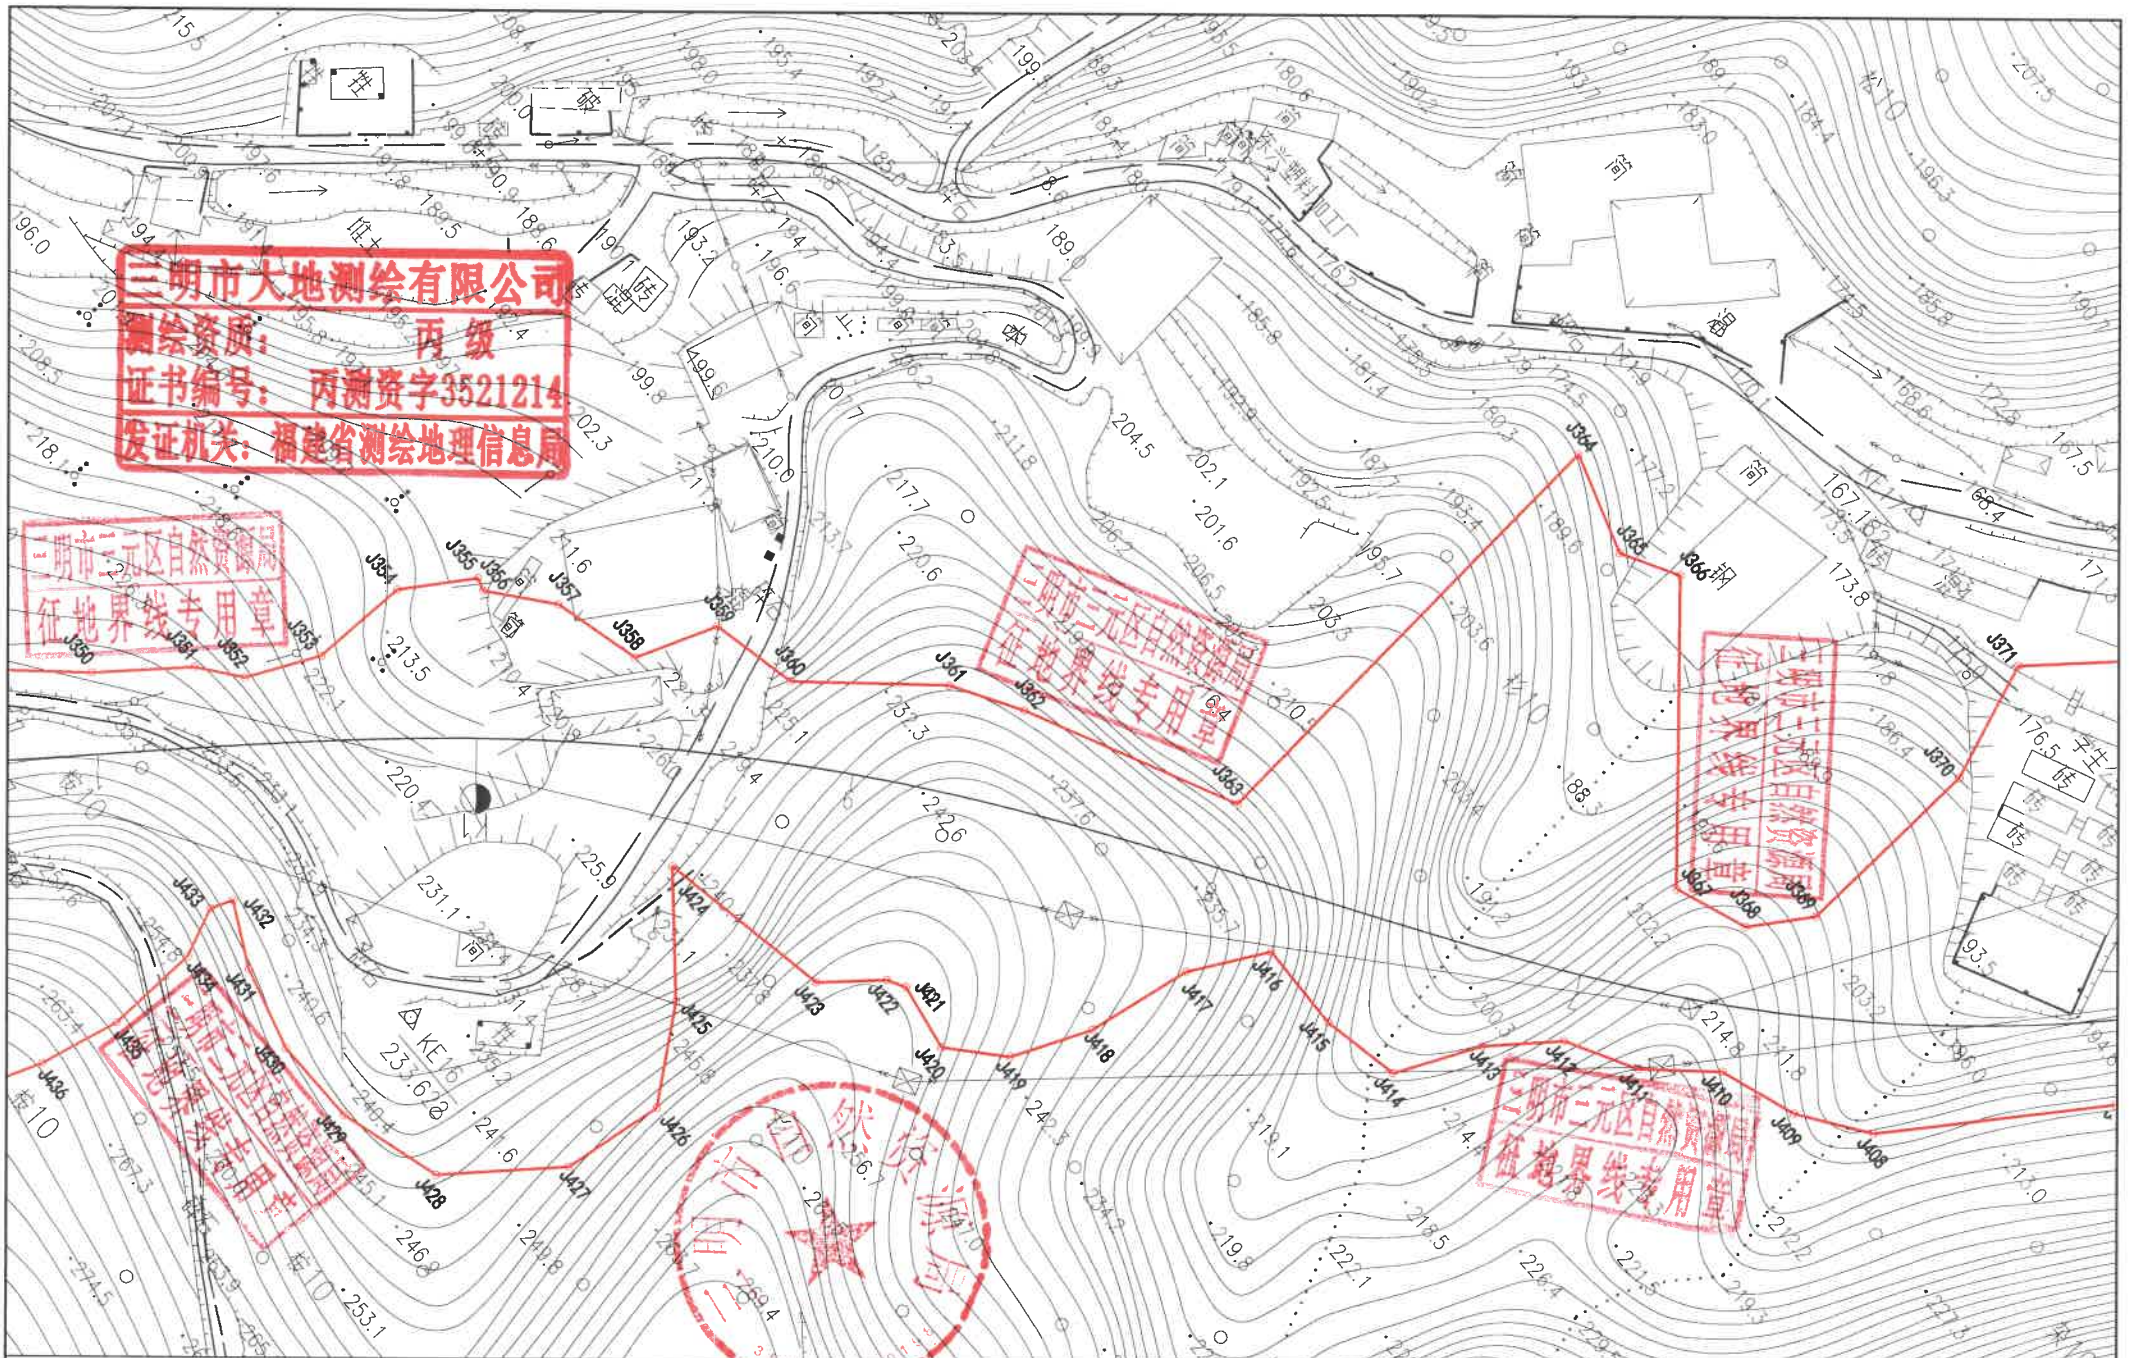

国道534（横六线）三元区村头至荆东二期工程勘测定界图

绘图

林向华

复核


蔡建平

日期

2020年9月

1、本图比例1:2000。
2、2000国家大地坐标系，中央子午线为117°。

第12页,共13页

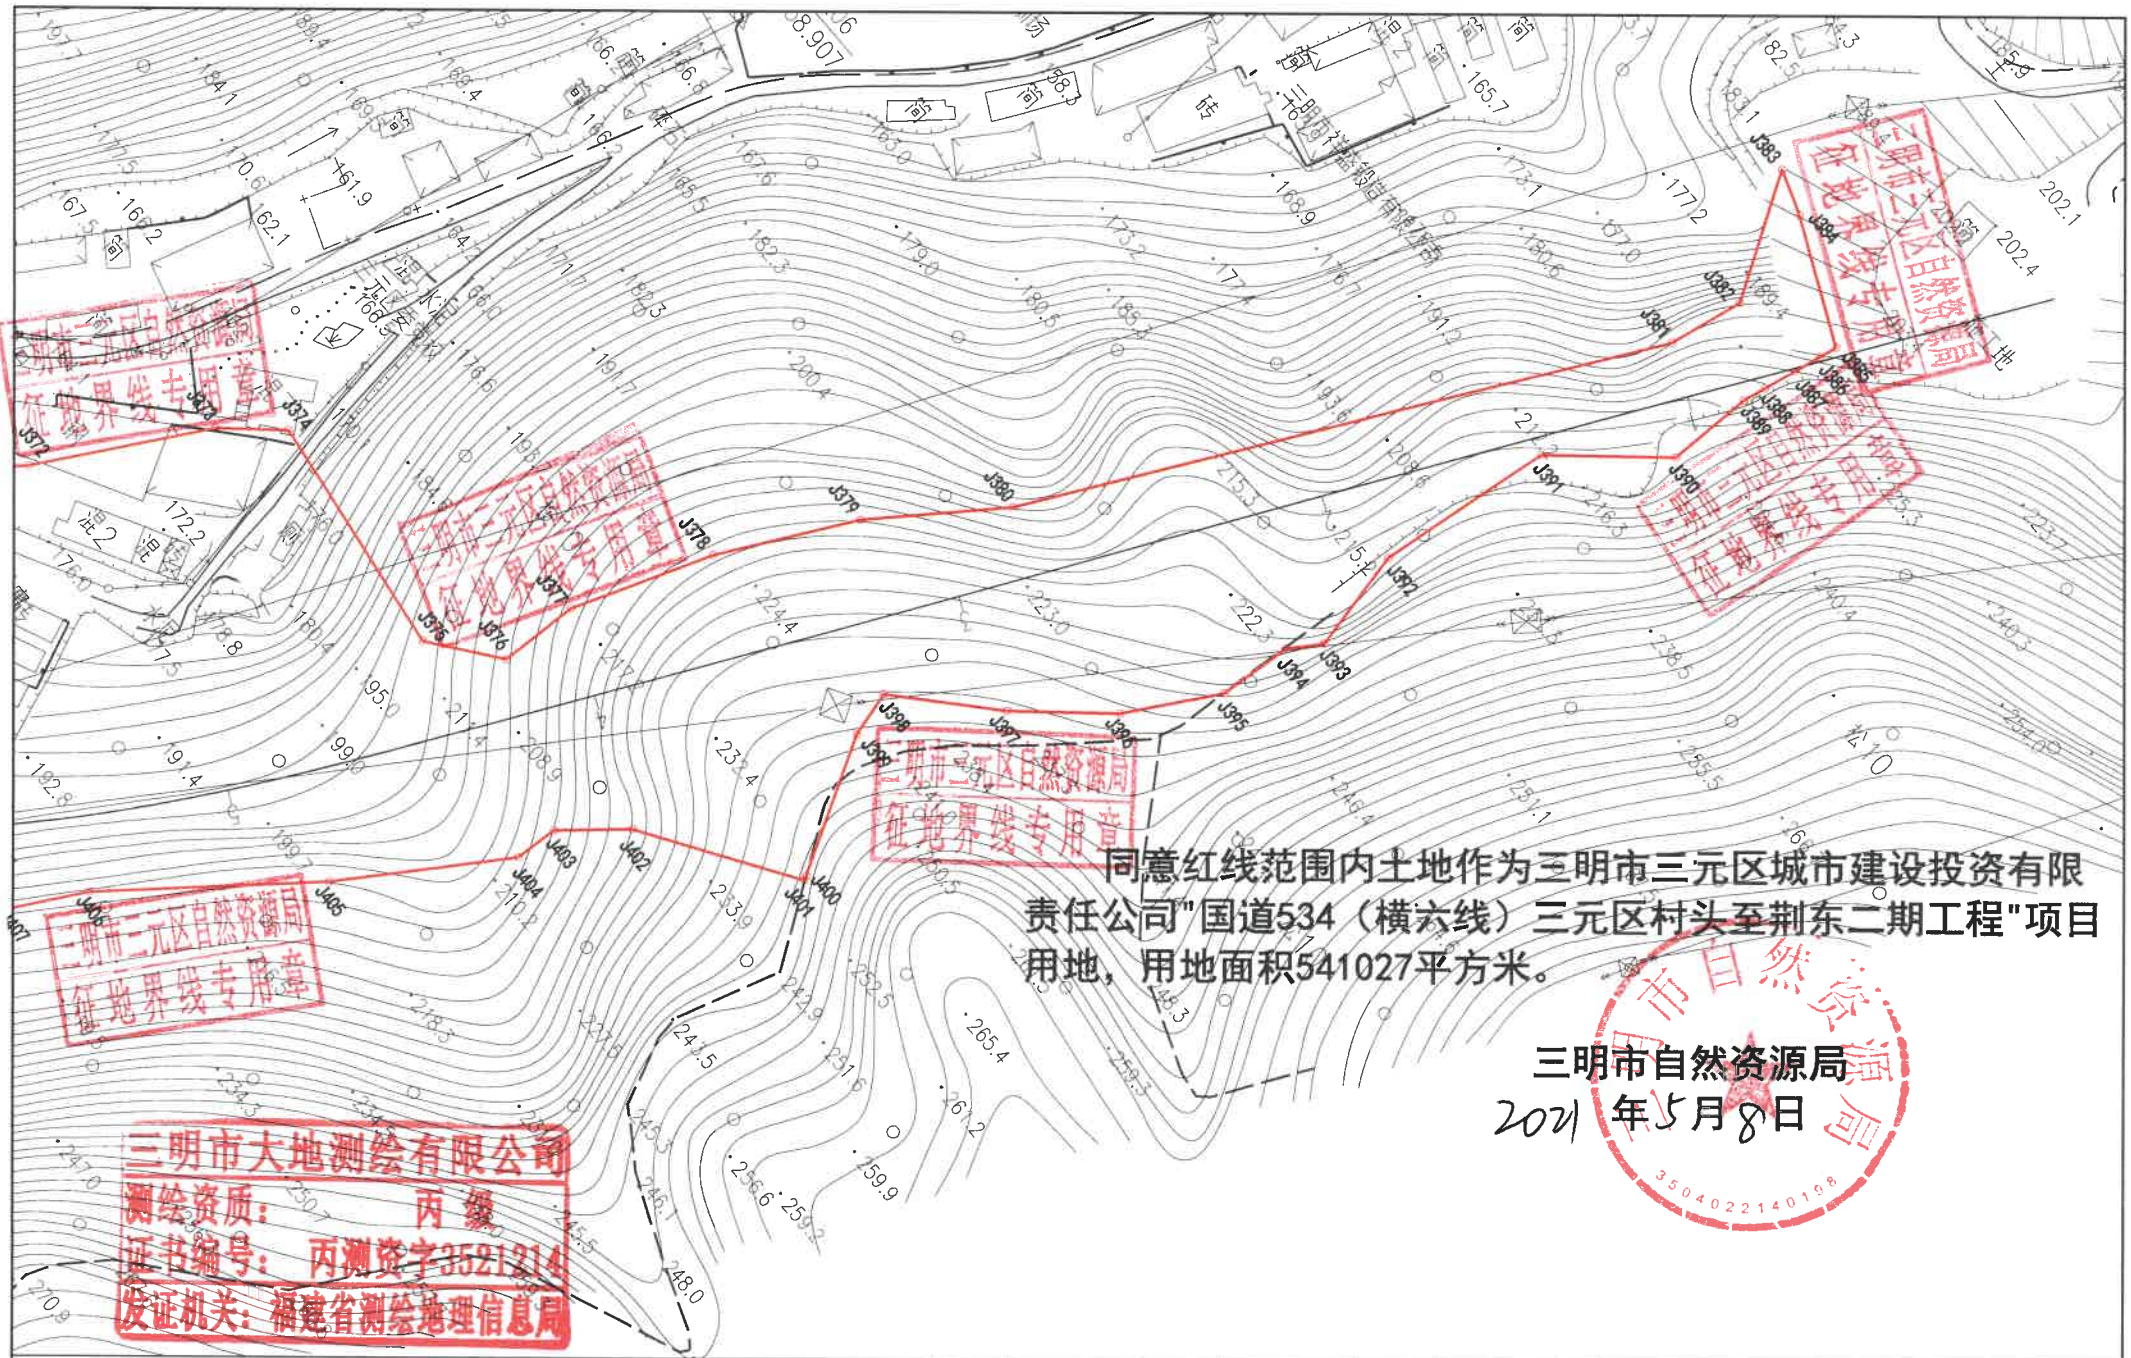

同意红线范围内土地作为三明市三元区城市建设投资有限公司“国道534（横六线）三元区村头至荆东二期工程”项目用地，用地面积541027平方米。

三明市自然资源局
2021年5月8日

三明市大地测绘有限公司
测绘资质：丙级
证书编号：丙测资字3521214
发证机关：福建省测绘地理信息局

国道534（横六线）三元区村头至荆东二期工程勘测定界图