


福建天尊新材料制造有限公司“350402-05-I-06A地块铸造用生铁高炉改建项目”勘测定界图

北
1:1600

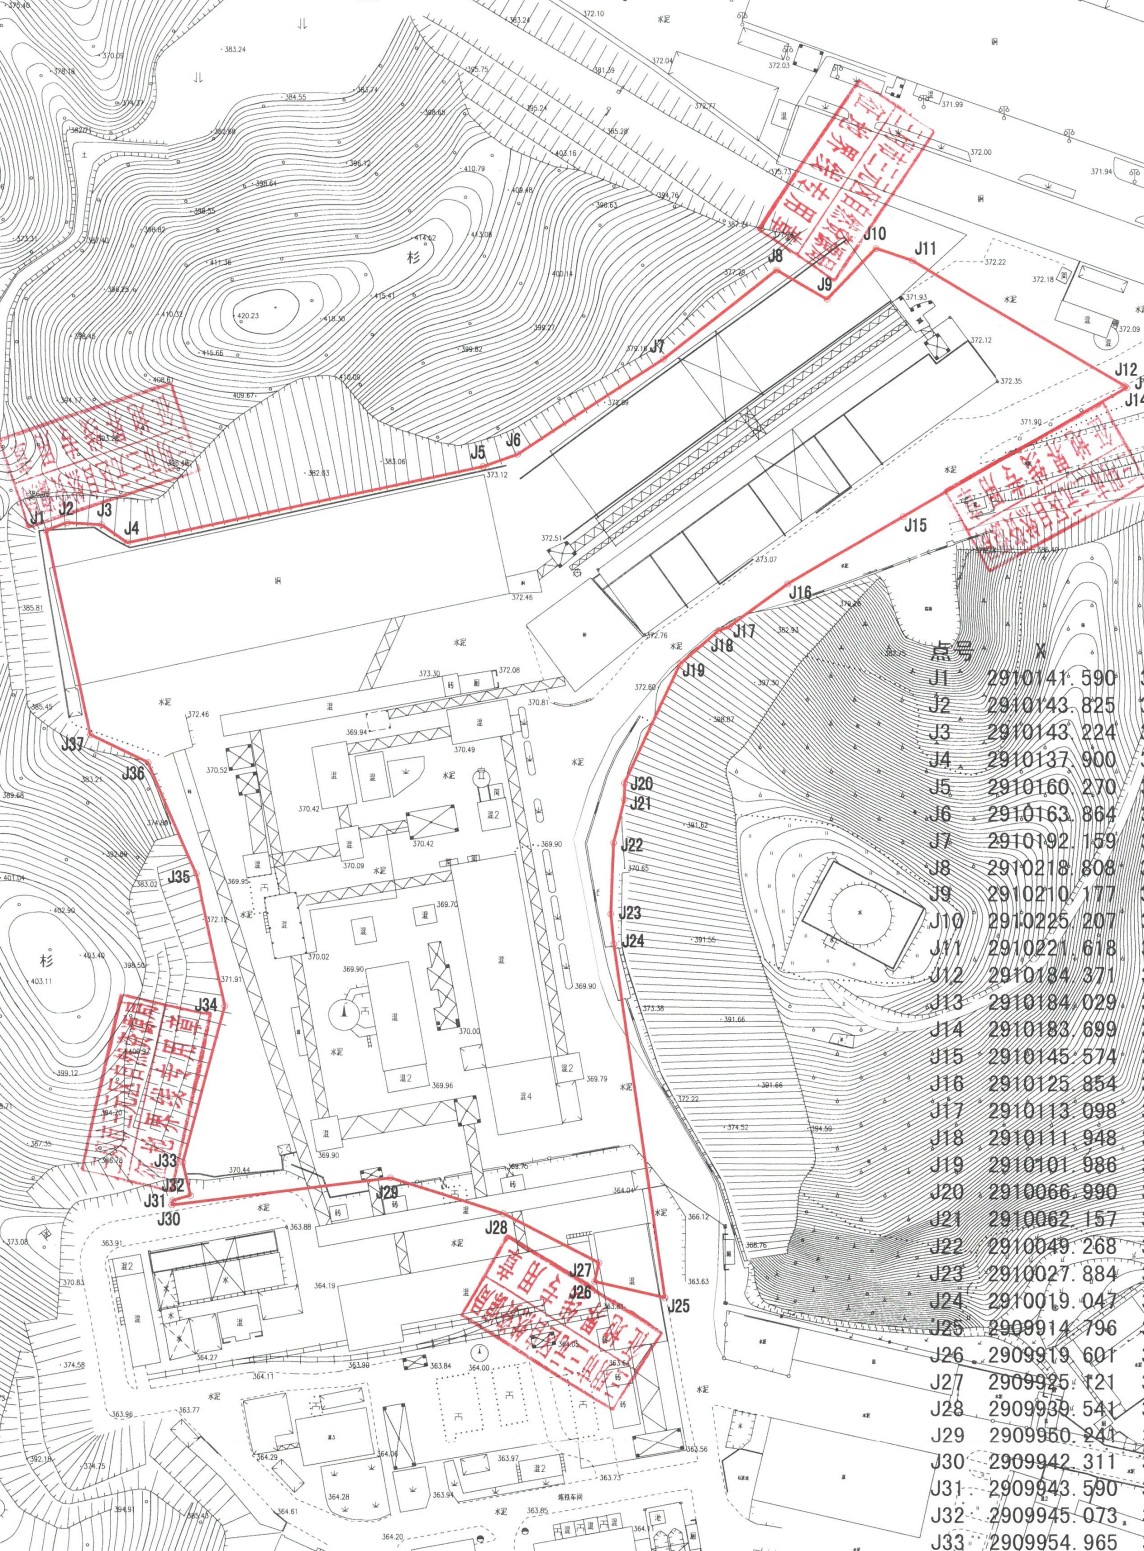

点号	X	Y
J1	2910141.590	39555292.247
J2	2910143.825	39555298.482
J3	2910143.224	39555308.570
J4	2910137.900	39555316.197
J5	2910160.270	39555421.218
J6	2910163.864	39555431.462
J7	2910192.159	39555474.925
J8	2910218.808	39555508.539
J9	2910210.177	39555523.434
J10	2910225.207	39555537.902
J11	2910221.618	39555548.581
J12	2910184.371	39555610.724
J13	2910184.029	39555611.181
J14	2910183.699	39555611.621
J15	2910145.574	39555645.679
J16	2910125.854	39555611.571
J17	2910113.098	39555494.202
J18	2910111.948	39555491.056
J19	2910101.986	39555479.628
J20	2910066.990	39555463.021
J21	2910062.157	39555462.932
J22	2910049.268	39555459.720
J23	2910027.884	39555458.809
J24	2910019.047	39555459.700
J25	2909914.796	39555474.644
J26	2909919.601	39555453.720
J27	2909925.121	39555455.030
J28	2909939.541	39555426.830
J29	2909950.241	39555398.030
J30	2909942.311	39555328.460
J31	2909943.590	39555328.808
J32	2909945.073	39555334.060
J33	2909954.965	39555331.899
J34	2910000.965	39555344.399
J35	2910040.235	39555336.029
J36	2910073.085	39555322.031
J37	2910081.184	39555305.082

同意红线范围内土地作为福建天尊新材料制造有限公司“350402-05-I-06A地块铸造用生铁高炉改建项目”预申请用地，用地面积40340.37m²。

三明市自然资源局

2021年11月24日

三明市大地测绘有限公司
测绘资质 丙级
证书编号：闽测资字3521214
发证机关：福建省测绘地理信息局