


陈景润实验小学富兴校区市政道路工程勘测定界图

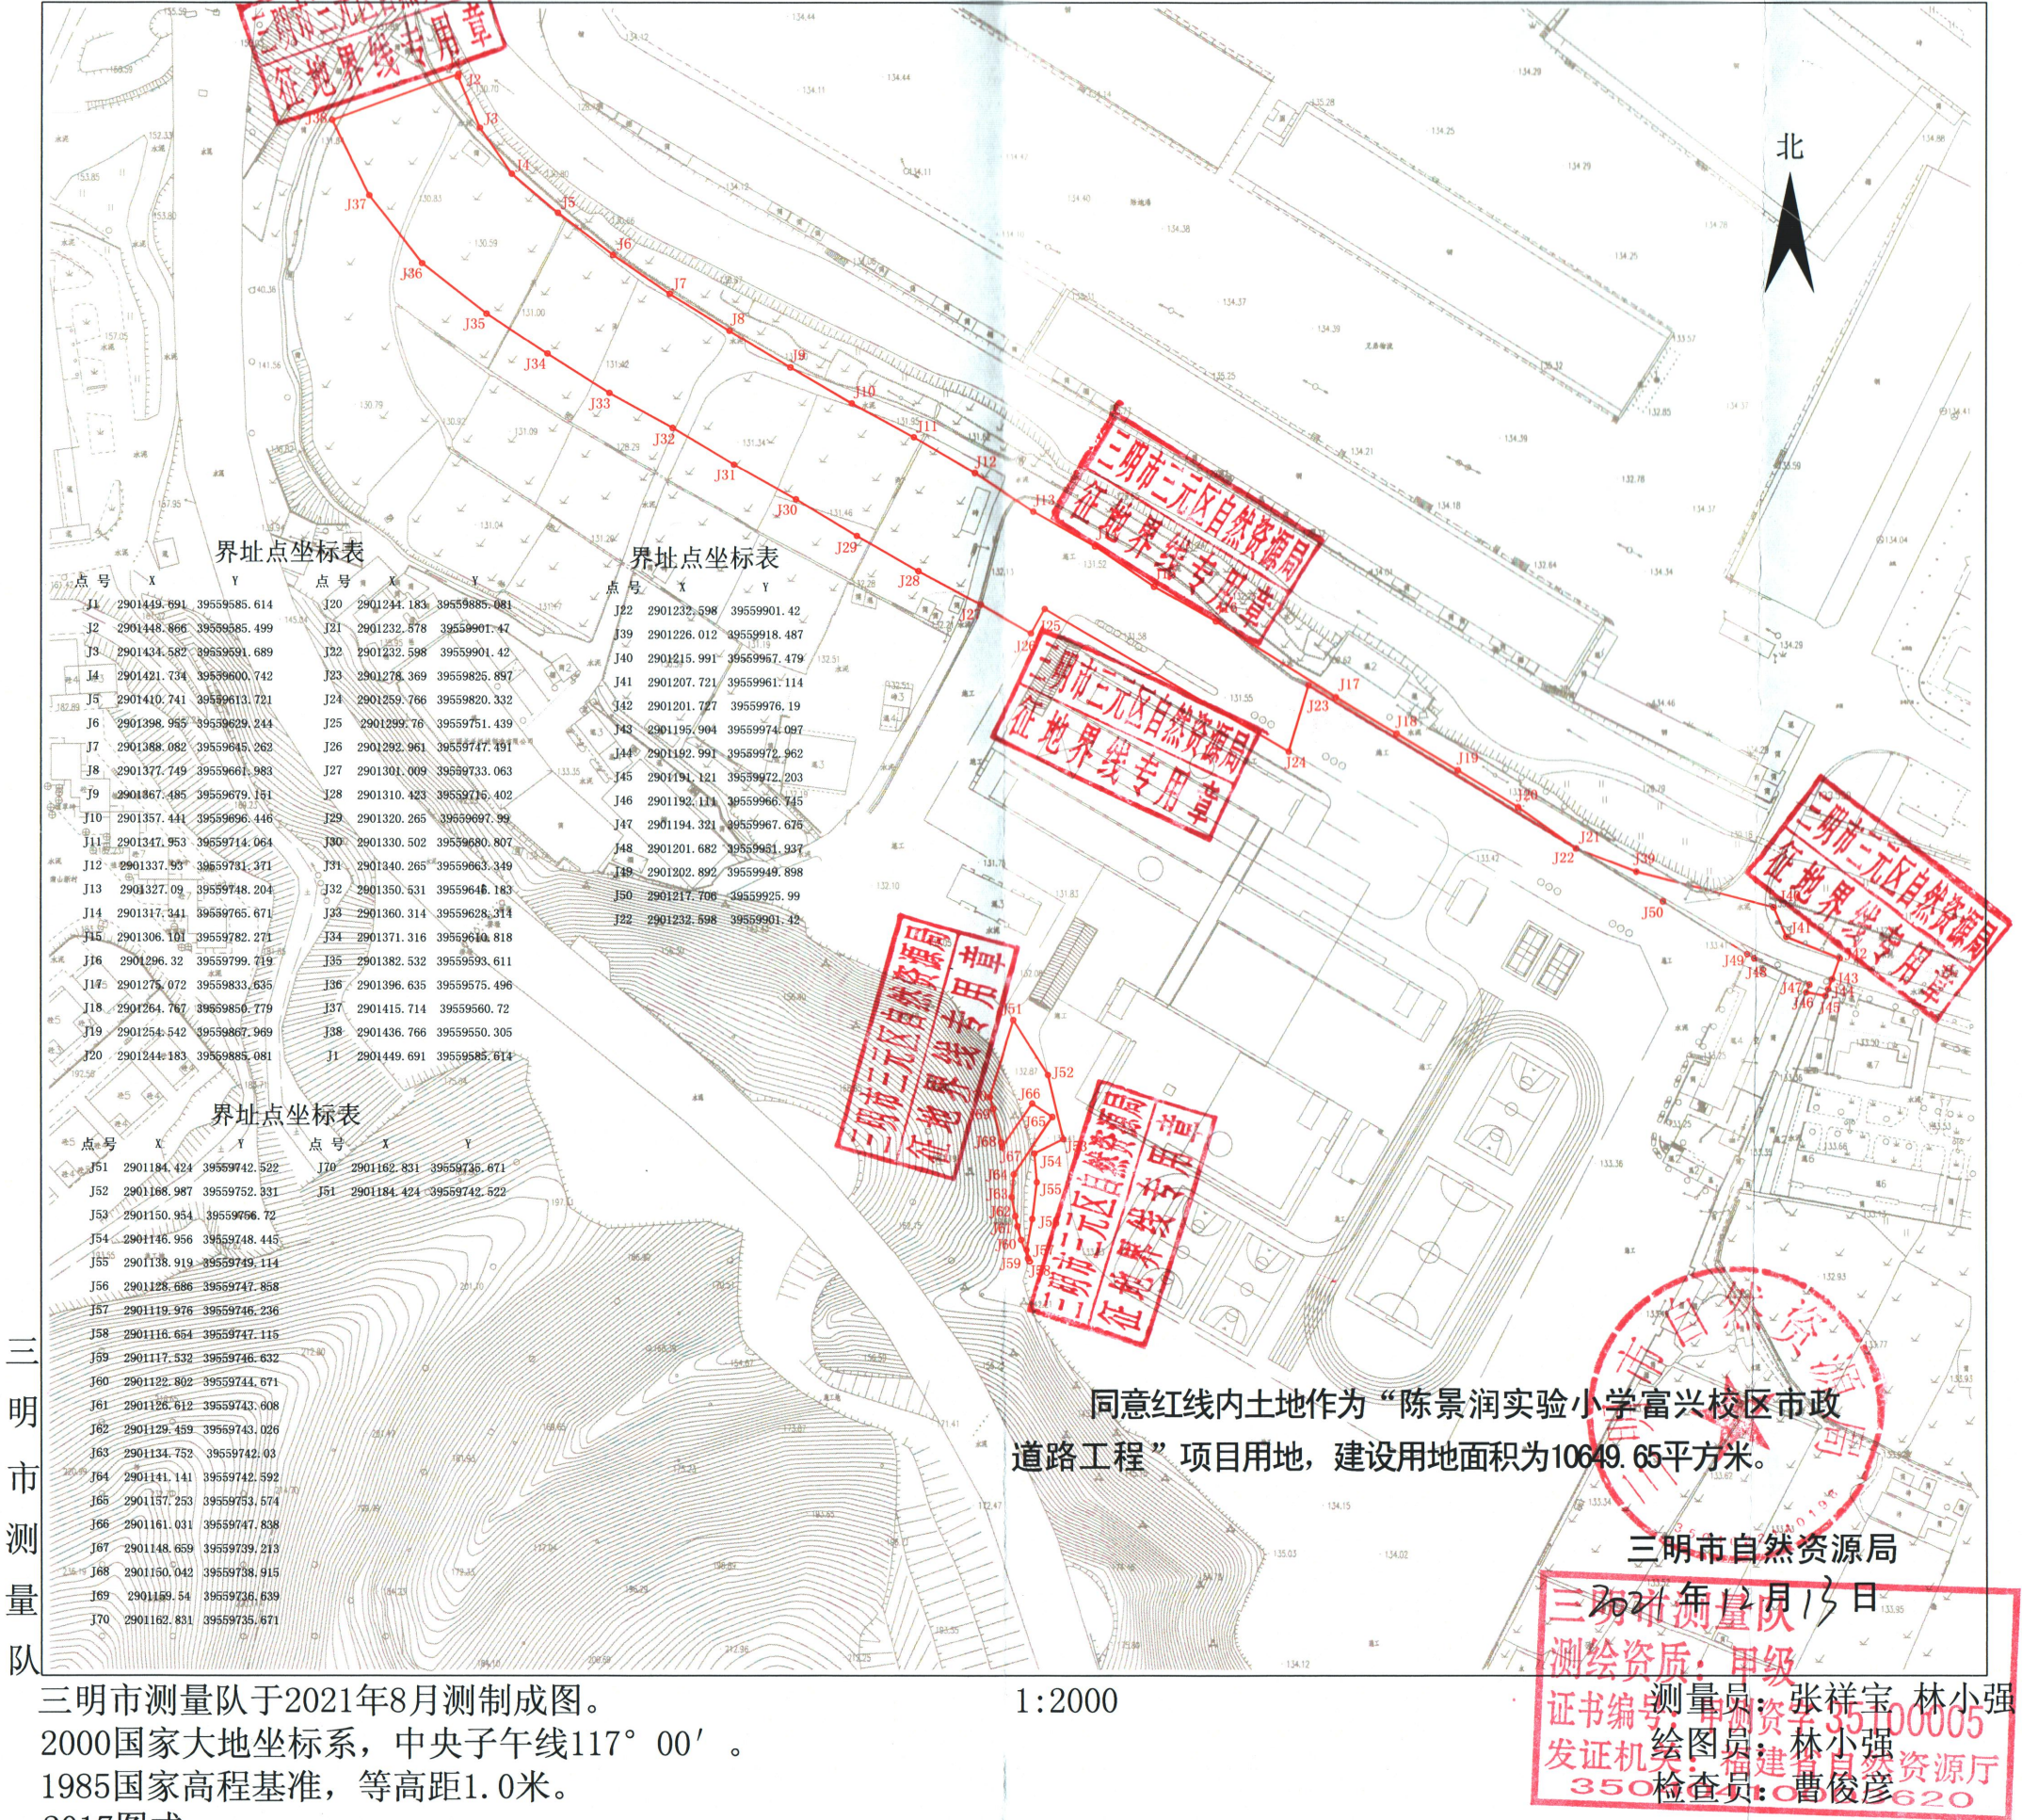

界址点坐标表

点号	X	Y
J1	2901449.891	3955985.614
J2	2901448.866	3955985.499
J3	2901434.582	3955989.689
J4	2901421.734	3955980.742
J5	2901410.741	39559613.721
J6	2901398.955	39559829.244
J7	2901388.082	39559645.262
J8	2901377.749	39559661.983
J9	2901367.485	39559679.151
J10	2901357.441	39559696.446
J11	2901347.953	39559714.064
J12	2901337.957	39559731.371
J13	2901327.09	39559748.204
J14	2901317.341	39559765.671
J15	2901306.101	39559782.271
J16	2901296.32	39559799.719
J17	2901275.072	39559833.635
J18	2901264.767	39559850.779
J19	2901254.542	39559867.969
J20	2901244.183	39559885.081

界址点坐标表

点号	X	Y
J21	2901232.578	39559901.47
J22	2901232.598	39559901.42
J23	2901278.369	39559825.897
J24	2901259.766	39559820.332
J25	2901299.76	39559751.439
J26	2901282.961	39559747.491
J27	2901301.009	39559733.063
J28	2901310.423	39559716.402
J29	2901320.265	39559697.99
J30	2901330.502	39559680.807
J31	2901340.265	39559663.349
J32	2901350.531	39559646.183
J33	2901360.314	39559628.314
J34	2901371.316	39559610.818
J35	2901382.532	39559593.611
J36	2901396.635	39559575.496
J37	2901415.714	39559560.72
J38	2901436.766	39559550.305
J1	2901449.891	3955985.614

界址点坐标表

点号	X	Y
J39	2901226.012	39559918.487
J40	2901215.991	39559957.479
J41	2901207.721	39559961.114
J42	2901201.727	39559976.19
J43	2901195.904	39559974.087
J44	2901192.991	39559972.962
J45	2901191.121	39559972.203
J46	2901192.111	39559966.745
J47	2901194.321	39559967.675
J48	2901201.682	39559951.937
J49	2901202.892	39559949.898
J50	2901217.706	39559925.99
J22	2901232.598	39559901.42

界址点坐标表

点号	X	Y
J51	2901184.424	39559742.522
J52	2901168.987	39559752.331
J53	2901150.954	39559766.72
J54	2901146.956	39559748.445
J55	2901138.919	39559749.114
J56	2901128.686	39559747.858
J57	2901119.976	39559746.236
J58	2901116.654	39559747.115
J59	2901117.532	39559746.632
J60	2901122.802	39559744.671
J61	2901126.612	39559743.608
J62	2901129.459	39559743.026
J63	2901134.752	39559742.03
J64	2901141.141	39559742.592
J65	2901137.253	39559753.574
J66	2901161.031	39559747.838
J67	2901148.659	39559739.213
J68	2901150.042	39559738.915
J69	2901159.54	39559738.639
J70	2901162.831	39559735.671