


陈大片区B地块项目勘测定界图

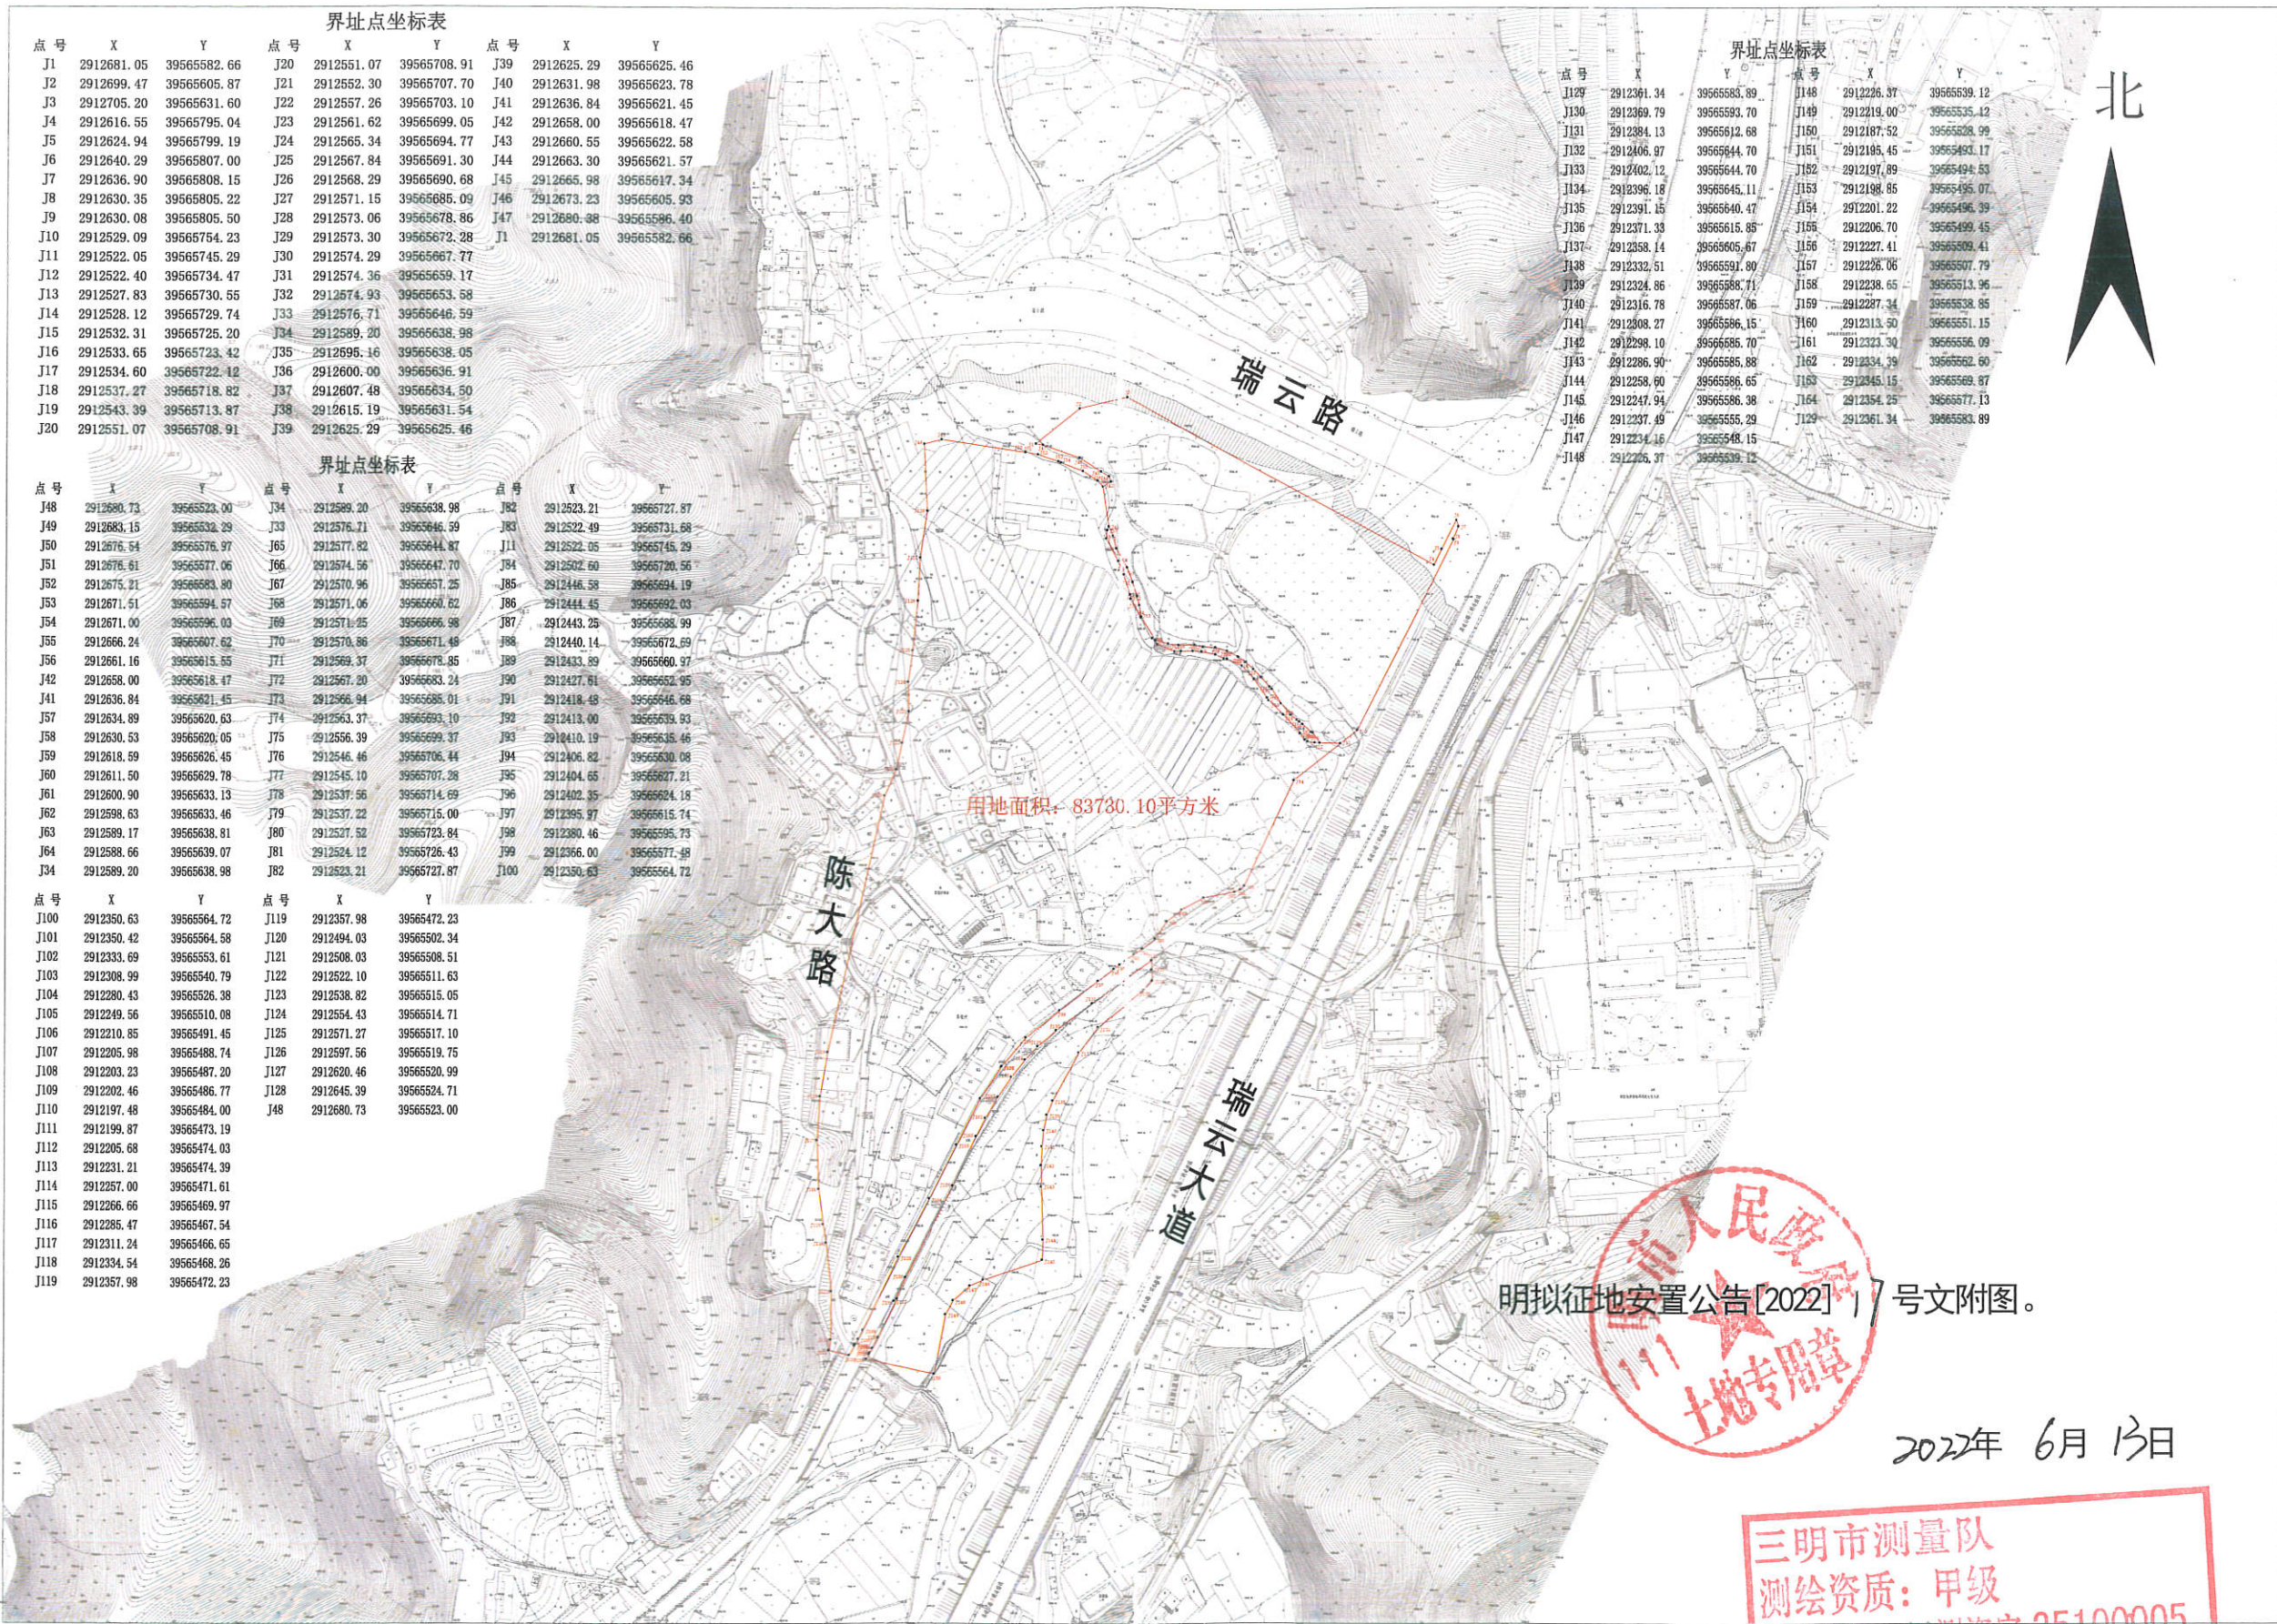

三明市测量队于2022年4月成图。
2000国家大地坐标系, 中央子午线117° 00' 。
1956高程系统, 等高距1.0米。
2017图式

明拟征地安置公告[2022] 111号文附图。

2022年 6月 13日

三明市测量队
测绘资质: 甲级
证书编号: 甲测资字 35100005
测量员: 张祥宝 林小强
绘图员: 张祥宝
检查员: 曹俊彦

三明市测量队