


福建莱得化工科技有限公司预申请工业用地项目勘测定界图

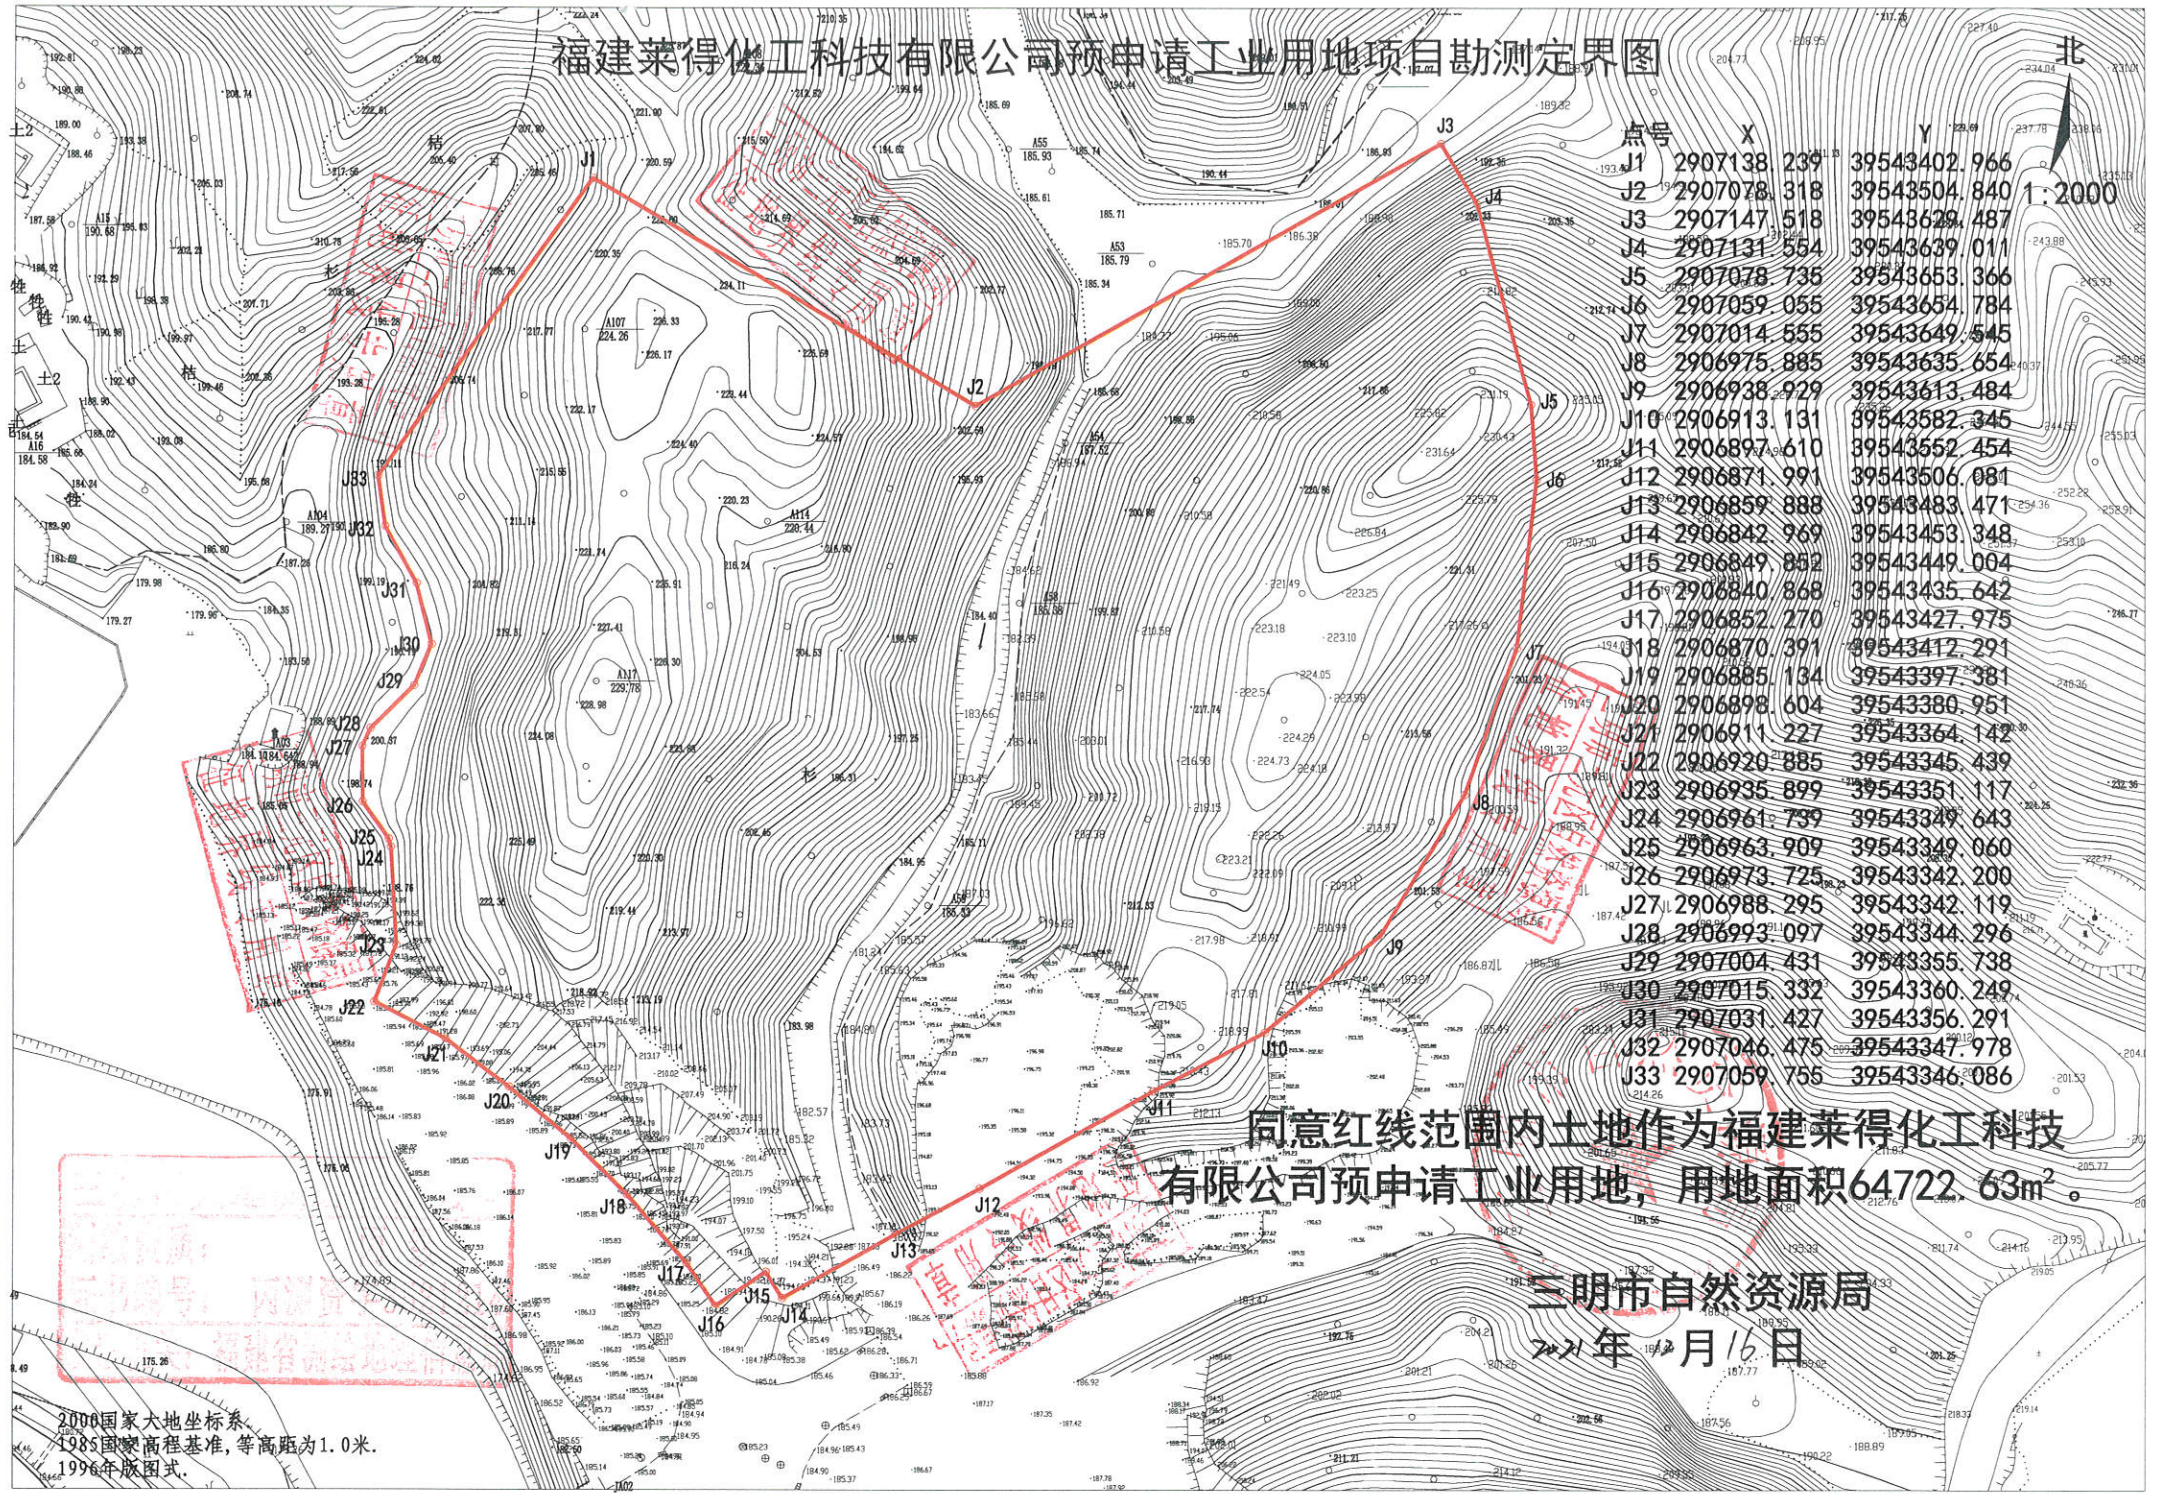

点号	X	Y
J1	2907138	239 39543402.966
J2	2907078	318 39543504.840
J3	2907147	518 39543629.487
J4	2907131	554 39543639.011
J5	2907078	736 39543653.366
J6	2907059	055 39543654.784
J7	2907014	555 39543649.545
J8	2906975	885 39543635.654
J9	2906938	929 39543613.484
J10	2906913	131 39543582.345
J11	2906897	610 39543552.454
J12	2906871	991 39543506.081
J13	2906859	888 39543483.471
J14	2906842	969 39543453.348
J15	2906849	852 39543449.004
J16	2906840	868 39543435.642
J17	2906852	270 39543427.975
J18	2906870	391 39543412.291
J19	2906885	134 39543397.381
J20	2906898	604 39543380.951
J21	2906911	227 39543364.142
J22	2906920	885 39543345.439
J23	2906935	899 39543351.117
J24	2906961	739 39543349.643
J25	2906963	909 39543349.060
J26	2906973	725 39543342.200
J27	2906988	295 39543342.119
J28	2906993	097 39543344.296
J29	2907004	431 39543355.738
J30	2907015	332 39543360.249
J31	2907031	427 39543356.291
J32	2907046	475 39543347.978
J33	2907059	755 39543346.086

同意红线范围内土地作为福建莱得化工科技有限公司预申请工业用地，用地面积64722.63m²。

三明市自然资源局
2021年12月16日

2000国家大地坐标系
1985国家高程基准，等高距为1.0米。
1996年版图式。