


三钢北通道防护绿地项目勘测定界图

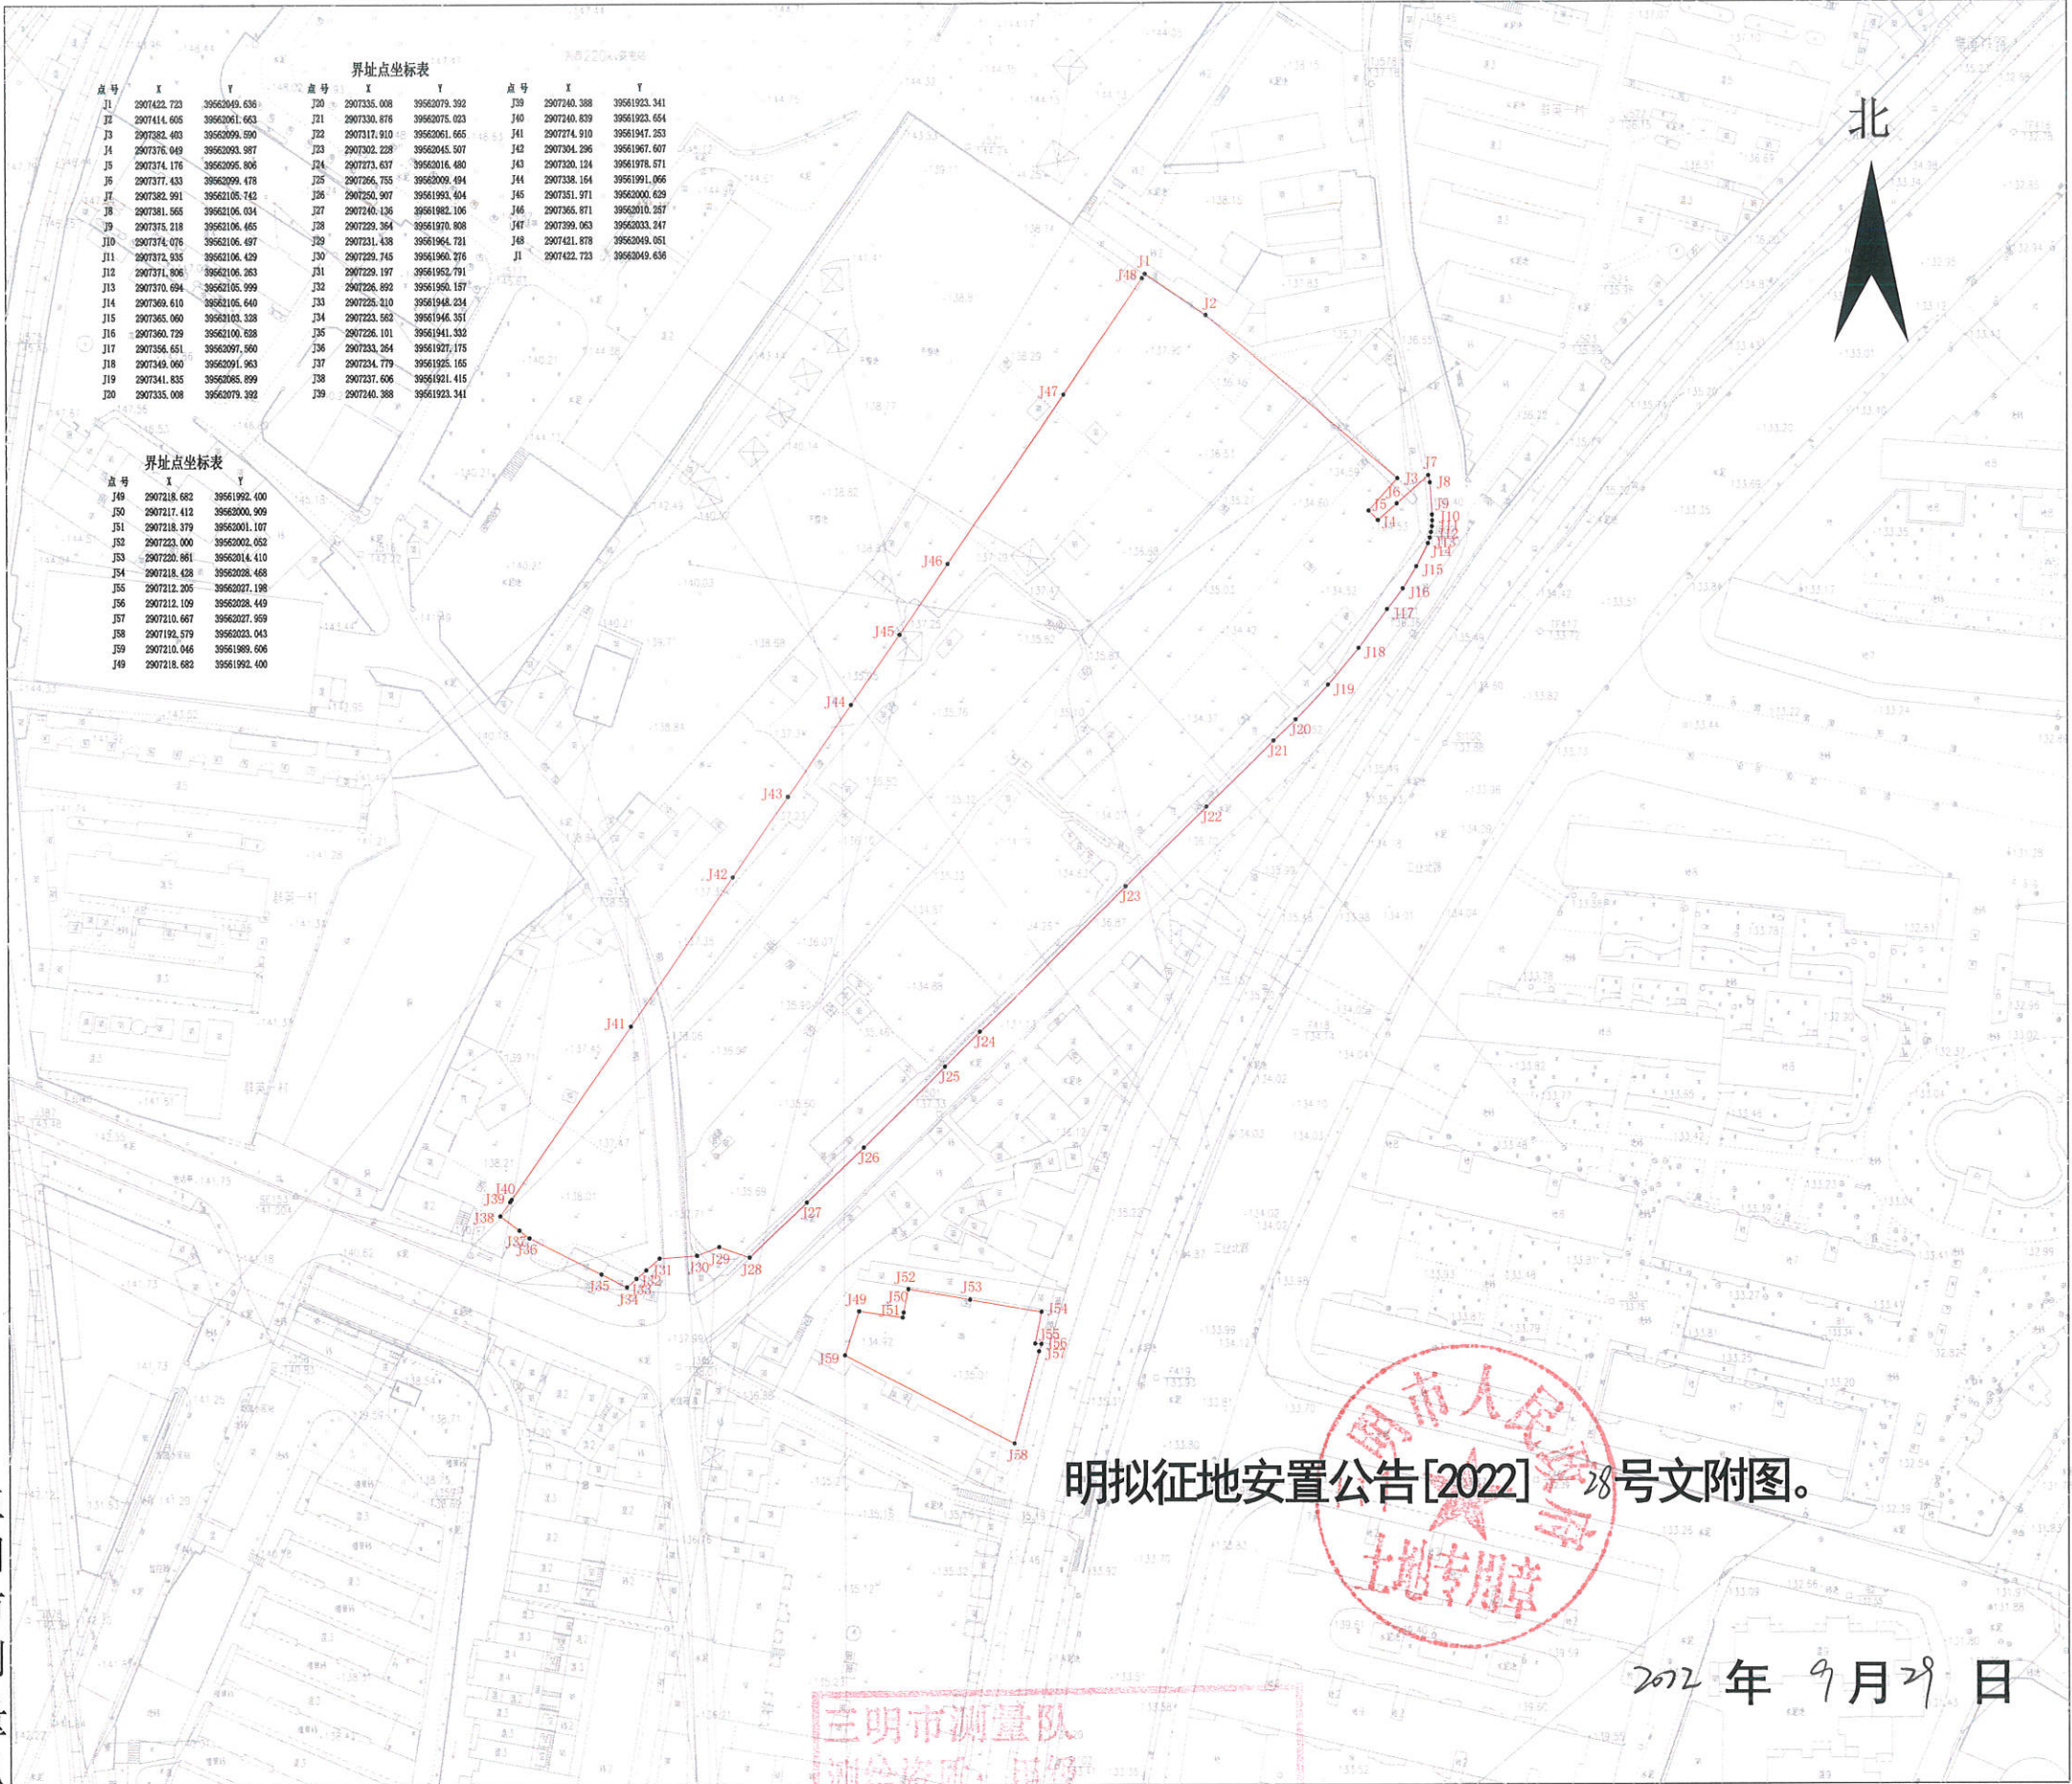

界址点坐标表			界址点坐标表			界址点坐标表		
点号	X	Y	点号	X	Y	点号	X	Y
J1	2907422.723	39562049.636	J20	2907235.008	39562079.392	J39	2907240.388	39561923.341
J2	2907414.605	39562061.663	J21	2907230.876	39562075.023	J40	2907240.839	39561923.664
J3	2907382.403	39562099.590	J22	2907317.910	39562061.665	J41	2907274.910	39561947.253
J4	2907376.049	39562093.987	J23	2907302.228	39562045.507	J42	2907304.296	39561967.607
J5	2907374.176	39562095.806	J24	2907273.637	39562016.480	J43	2907320.124	39561976.871
J6	2907377.433	39562099.478	J25	2907266.755	39562009.494	J44	2907338.164	39561991.096
J7	2907382.991	39562105.743	J26	2907250.907	39561991.494	J45	2907351.971	39562000.639
J8	2907381.565	39562106.034	J27	2907240.126	39561982.106	J46	2907365.871	39562010.287
J9	2907375.218	39562106.465	J28	2907229.364	39561970.808	J47	2907399.063	39562033.247
J10	2907374.076	39562106.497	J29	2907231.438	39561964.721	J48	2907421.878	39562049.651
J11	2907372.935	39562106.429	J30	2907229.745	39561960.276	J1	2907422.723	39562049.636
J12	2907371.806	39562106.263	J31	2907229.197	39561952.791			
J13	2907370.694	39562105.999	J32	2907226.892	39561950.157			
J14	2907369.610	39562105.640	J33	2907225.410	39561948.234			
J15	2907365.060	39562103.328	J34	2907223.562	39561946.351			
J16	2907360.729	39562100.888	J35	2907226.101	39561941.332			
J17	2907356.651	39562097.560	J36	2907233.264	39561927.175			
J18	2907349.060	39562091.963	J37	2907234.779	39561925.165			
J19	2907341.835	39562085.899	J38	2907237.606	39561921.415			
J20	2907335.008	39562079.392	J39	2907240.388	39561923.341			

界址点坐标表		
点号	X	Y
J49	2907218.682	39561992.400
J50	2907217.412	39562000.909
J51	2907218.379	39562001.107
J52	2907223.000	39562002.053
J53	2907220.661	39562016.410
J54	2907218.428	39562028.468
J55	2907212.205	39562027.198
J56	2907212.109	39562028.449
J57	2907210.667	39562027.959
J58	2907198.579	39562023.043
J59	2907210.046	39561989.606
J49	2907218.682	39561992.400

明拟征地安置公告[2022] 28号文附图。

2022年9月29日

三明市测量队

三明市测量队于2022年8月测制成图。
2000国家大地坐标系，中央子午线117° 00'。
1985国家高程基准，等高距1.0米。
2017图式

三明市测量队
测绘资质：甲级
证书编号：甲测资字 35100005
发证机关：福建省自然资源厅

测量员：许子涵 林小强
绘图员：张祥宝
检查员：肖丽文