



福建凯筑工程设计集团有限公司
(原名称:福建浚澄集团设计院有限公司)

设计修改(补充)通知单

建设单位: 三明市亚通物资有限公司

设计号: 2020-LC-0643

第 号

项 目: 三明市亚通物资有限公司金属仓库建设项目

专 业: 建筑

日 期:

审定人	张华	专业负责人	杨松华	校对	张华	修改人	张华
-----	----	-------	-----	----	----	-----	----

修改原因及内容:

根据工艺使用功能及采光通风要求, 原有建筑外墙和门窗, 现取消建筑外墙及门窗。
变更部分的内容已用云线圈出, 具体详图纸。


会签	建 筑	结 构	给排水	暖 通	电 气	电 讯	动 力
	张华						
设计总负责人: 杨松华				2022年1月20日			


注: 本目录所列图纸中加盖的单位资质章(出图章)与单位公章具有等同效力。

变更前效果图




变更后效果图

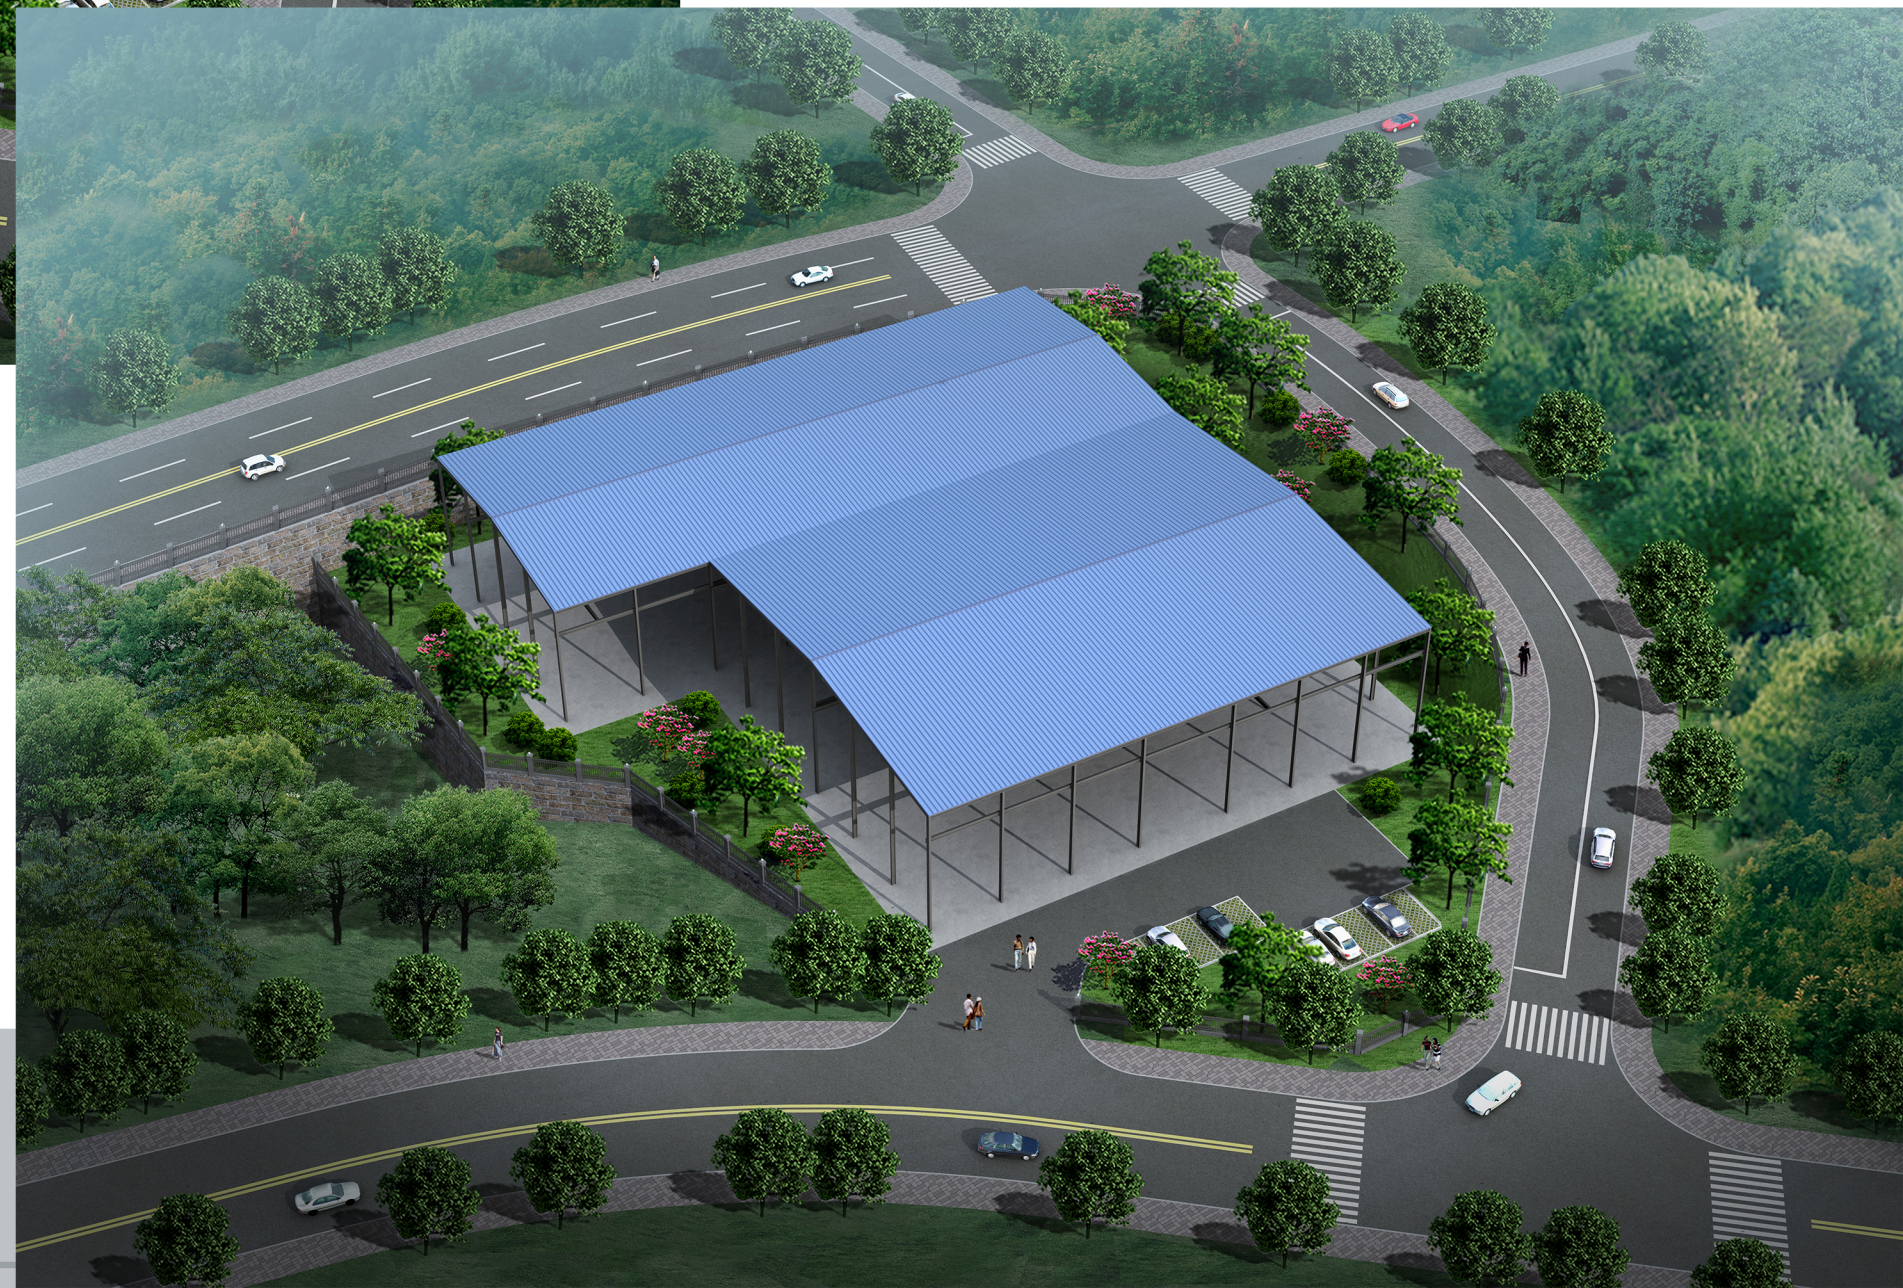


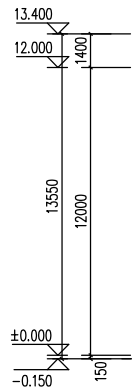

变更前①-②轴立面图 1:100

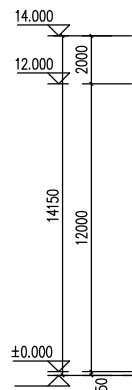

变更前①-⑬轴立面图 1:100

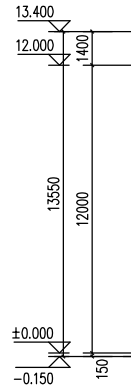

变更前1-1剖面图 1:100

STATUS 状态	DRAWING 图样
比例	日期

DRAWING No.	
目次	

注：1、建筑面积：3833.00m²；
2、建筑计容面积：7666.00m²；

 宁波中远工程设计集团有限公司 (原名: 宁波中远建筑设计有限公司) 建筑设计研究院 注册证书: A230000004 地址: 宁波市鄞州区中河街道12号锦泰207 电话: 0584-6535000 传真: 0584-6532320 邮箱: nzyd@126.com	
合同设计号: CONTRACT DESIGN WITH	
专业注册建筑师章: PROFESSIONAL REGISTERED SEAL	
注册建筑师章: REGISTERED ARCHITECT'S SEAL	
制图章: DRAWING PROJECT SEAL	
施工图审查章: 施工图审查合格专用章:	
设计人: 柳松华 校对人: 柳松华 审核人: 柳松华 审定人: 柳松华 日期: 2020.01	

