



三明梅园国际大酒店二期工程规划设计方案变更

福州精业建筑工程设计咨询有限公司 2022.04

法定代表人：

工程负责人：

建筑专业负责人：

结构专业负责人：

电气专业负责人：

给排水专业负责人：

暖通专业负责人：

主要设计人：

缪弘

陈泉金

陈泉金


吴建明

杨华兰

贺安龙

林智捷

陈泉金 胡宏宇 彭仙沾

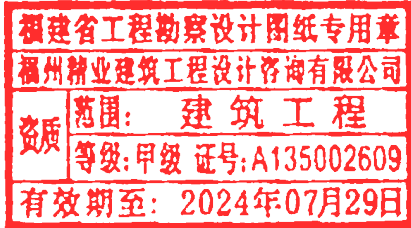

福州精业建筑工程设计咨询有限公司
King · Yea (CHINA FU ZHOU) Engineer Design Consultants, Ltd.
(甲级设计证书编号A135002609)
2022年04月



建设单位 三明梅园国际大酒店有限公司

施工单位

工程名称 三明梅园国际大酒店二期项目

监理单位

工程编号 1908-DXS

日期

2022年04月26日

更改理由 优化设计

文件编号

设变字第

号

变更内容：

- 1、地下一层D11~D13轴交DH~DN轴处的三个停车位从新布置；
- 2、地下二层D2~D3轴交DJ~DP轴处、ADC~ADF交AD3轴处和AD3~AD4轴交轴ADC处分别增加一个机动车停车位，总计增加三个机动车停车位；
- 3、取消一层C~E轴交11~15轴处的值班管理室和卫生间。
- 4、屋面层D~G轴交9~14轴处的电梯井出屋面，电梯机房标高更改为96.60，电梯机房标高位99.30米处。

福建省工程勘察设计图纸专用章
福州精业建筑工程设计咨询有限公司
范围：建筑工程
资质等级：甲级 证号：A135002609
有效期至：2024年07月29日

中华人民共和国一级注册建筑师

姓名：陈泉金

注册号：3500260-003

有效期：至2023年6月



福州精业建筑工程设计咨询有限公司

原设计人

陈泉金

校核人

胡宏宇

审核人

陈泉金

变更人


陈泉金

项目负责人

陈泉金

相关专业会签

地下室一层 变更前

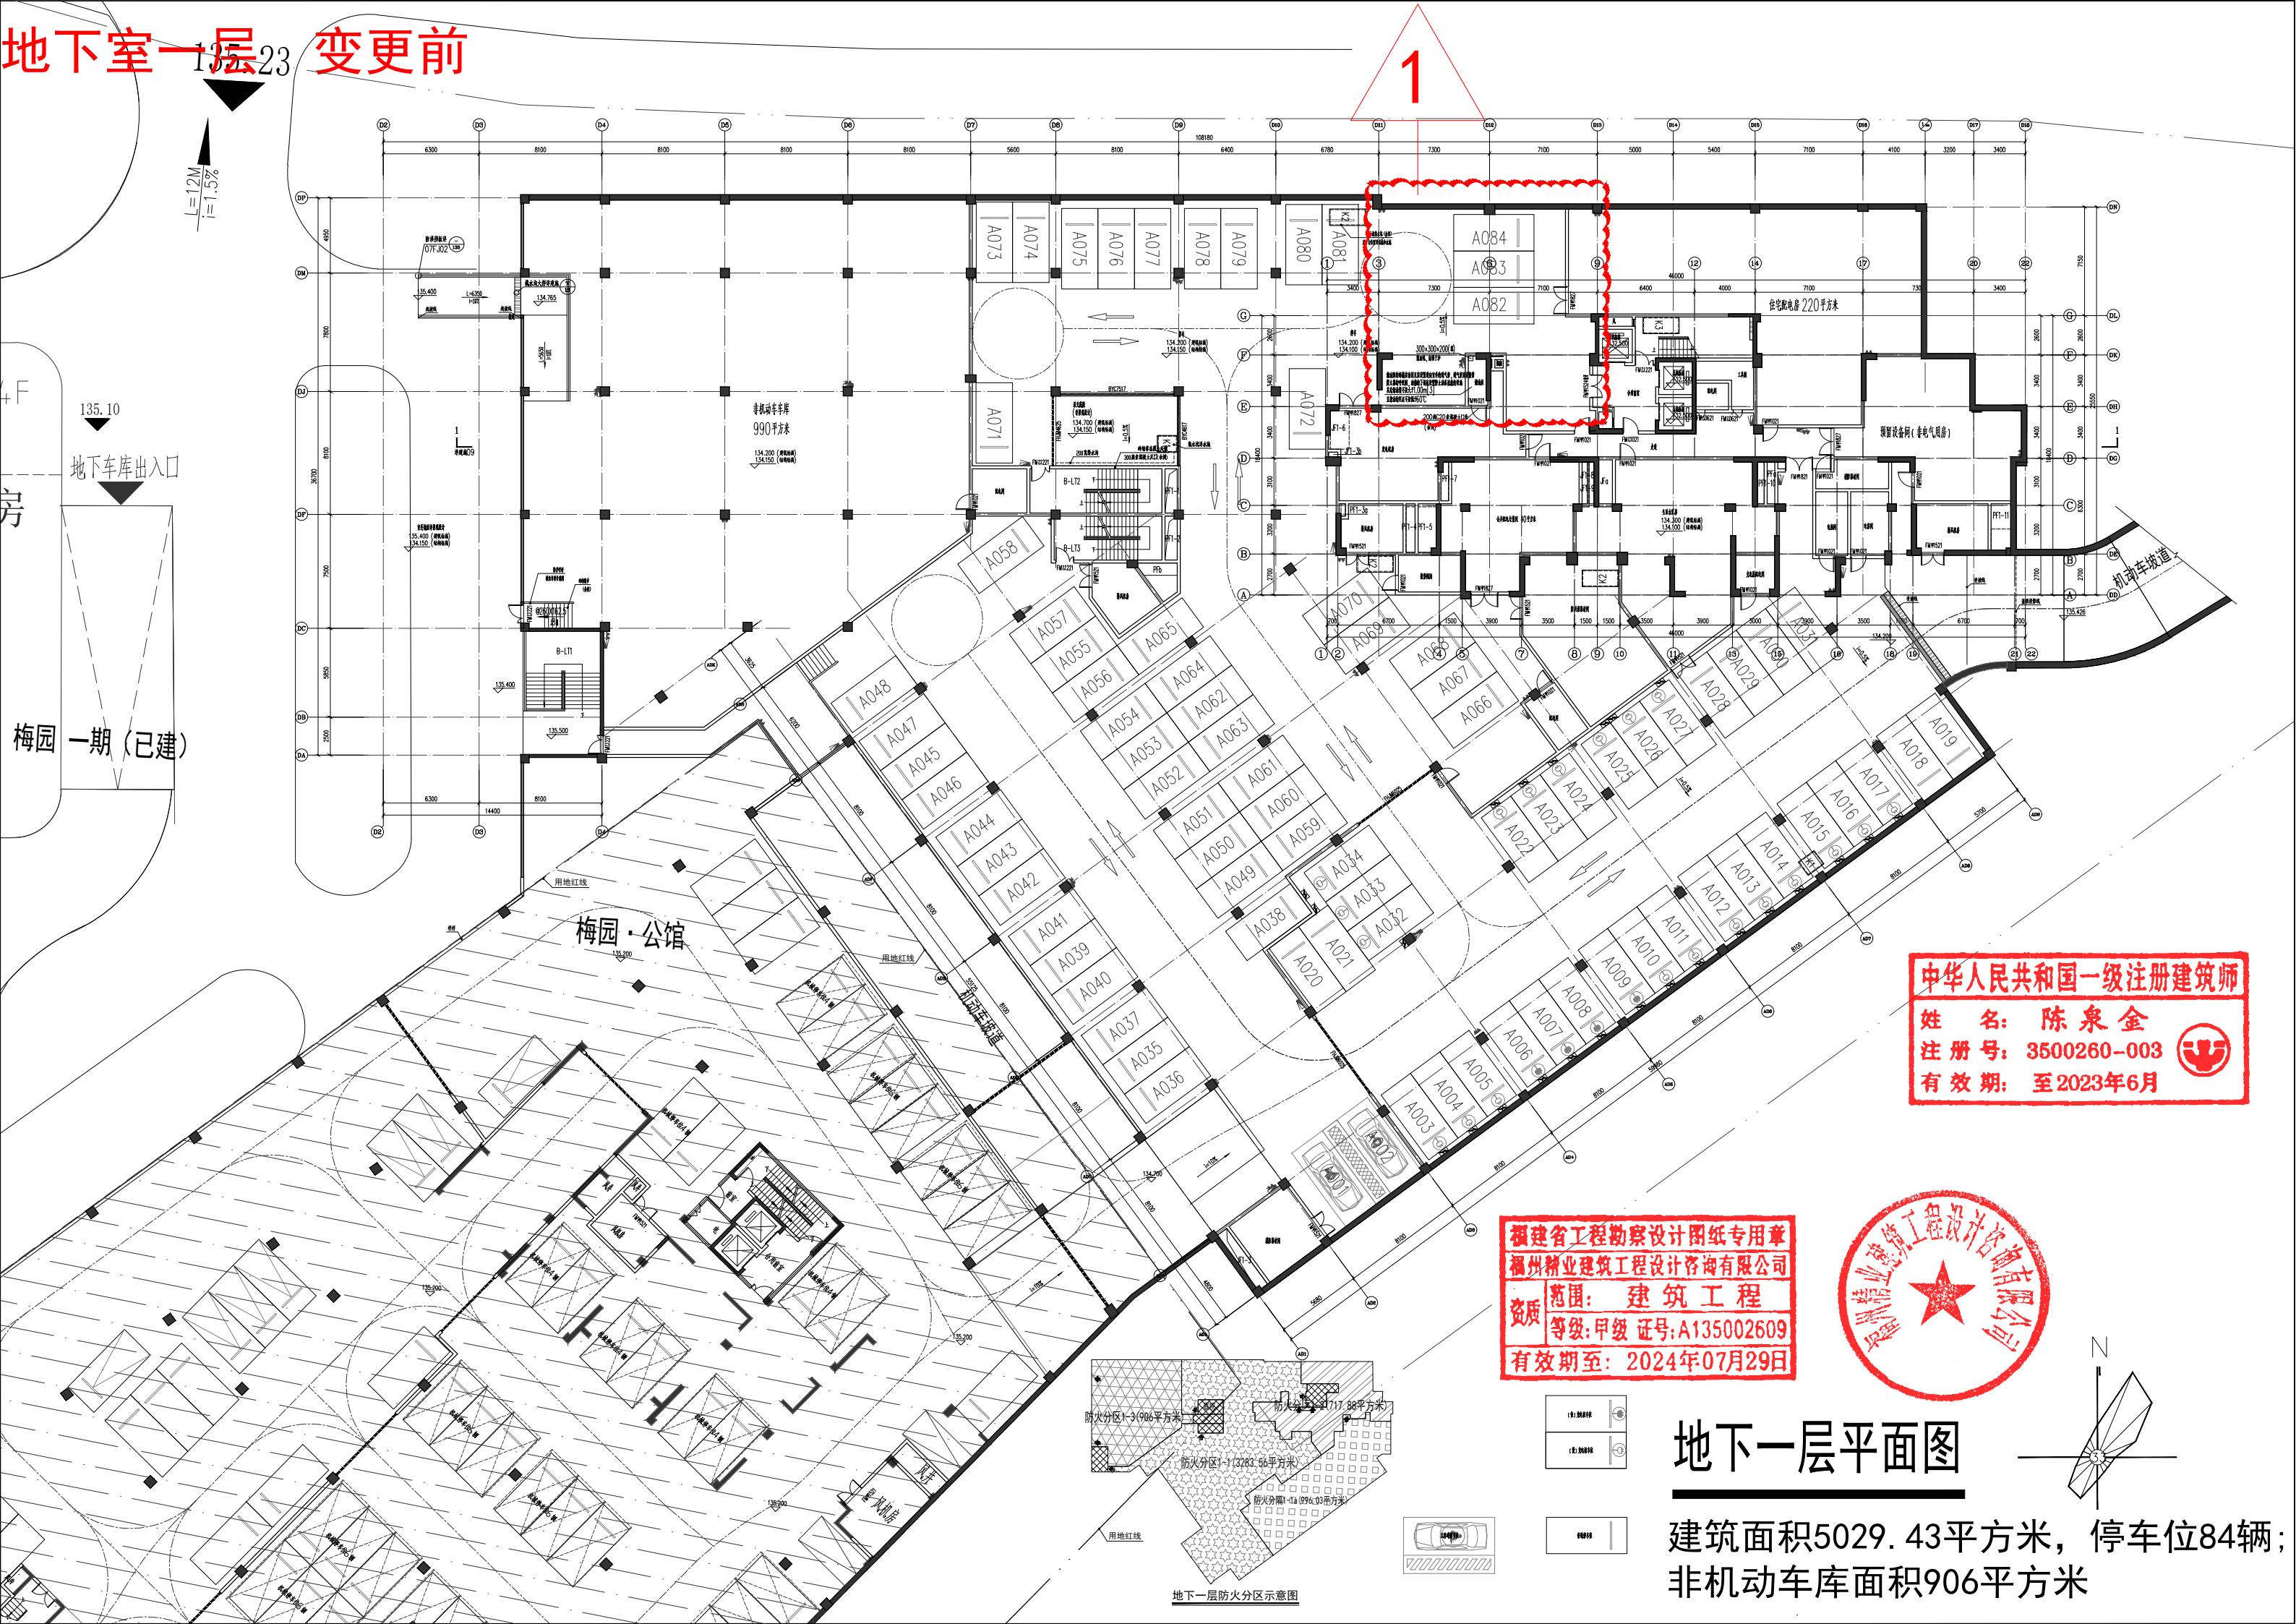


中华人民共和国一级注册建筑师
姓名: 陈泉金
注册号: 3500260-003
有效期: 至2023年6月

福建省工程勘察设计图纸专用章
福州精业建筑工程设计咨询有限公司
范围: 建筑工程
资质等级: 甲级 证号: A135002609
有效期至: 2024年07月29日




地下一层平面图

建筑面积5029.43平方米, 停车位84辆;
非机动车库面积906平方米

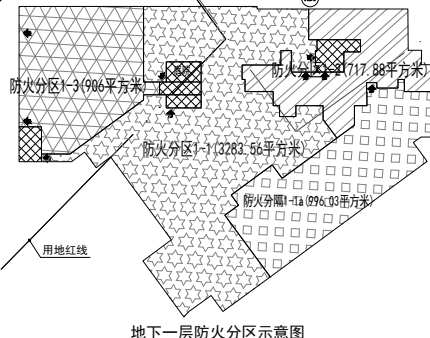

地下一层防火分区示意图

地下室1层 变更后

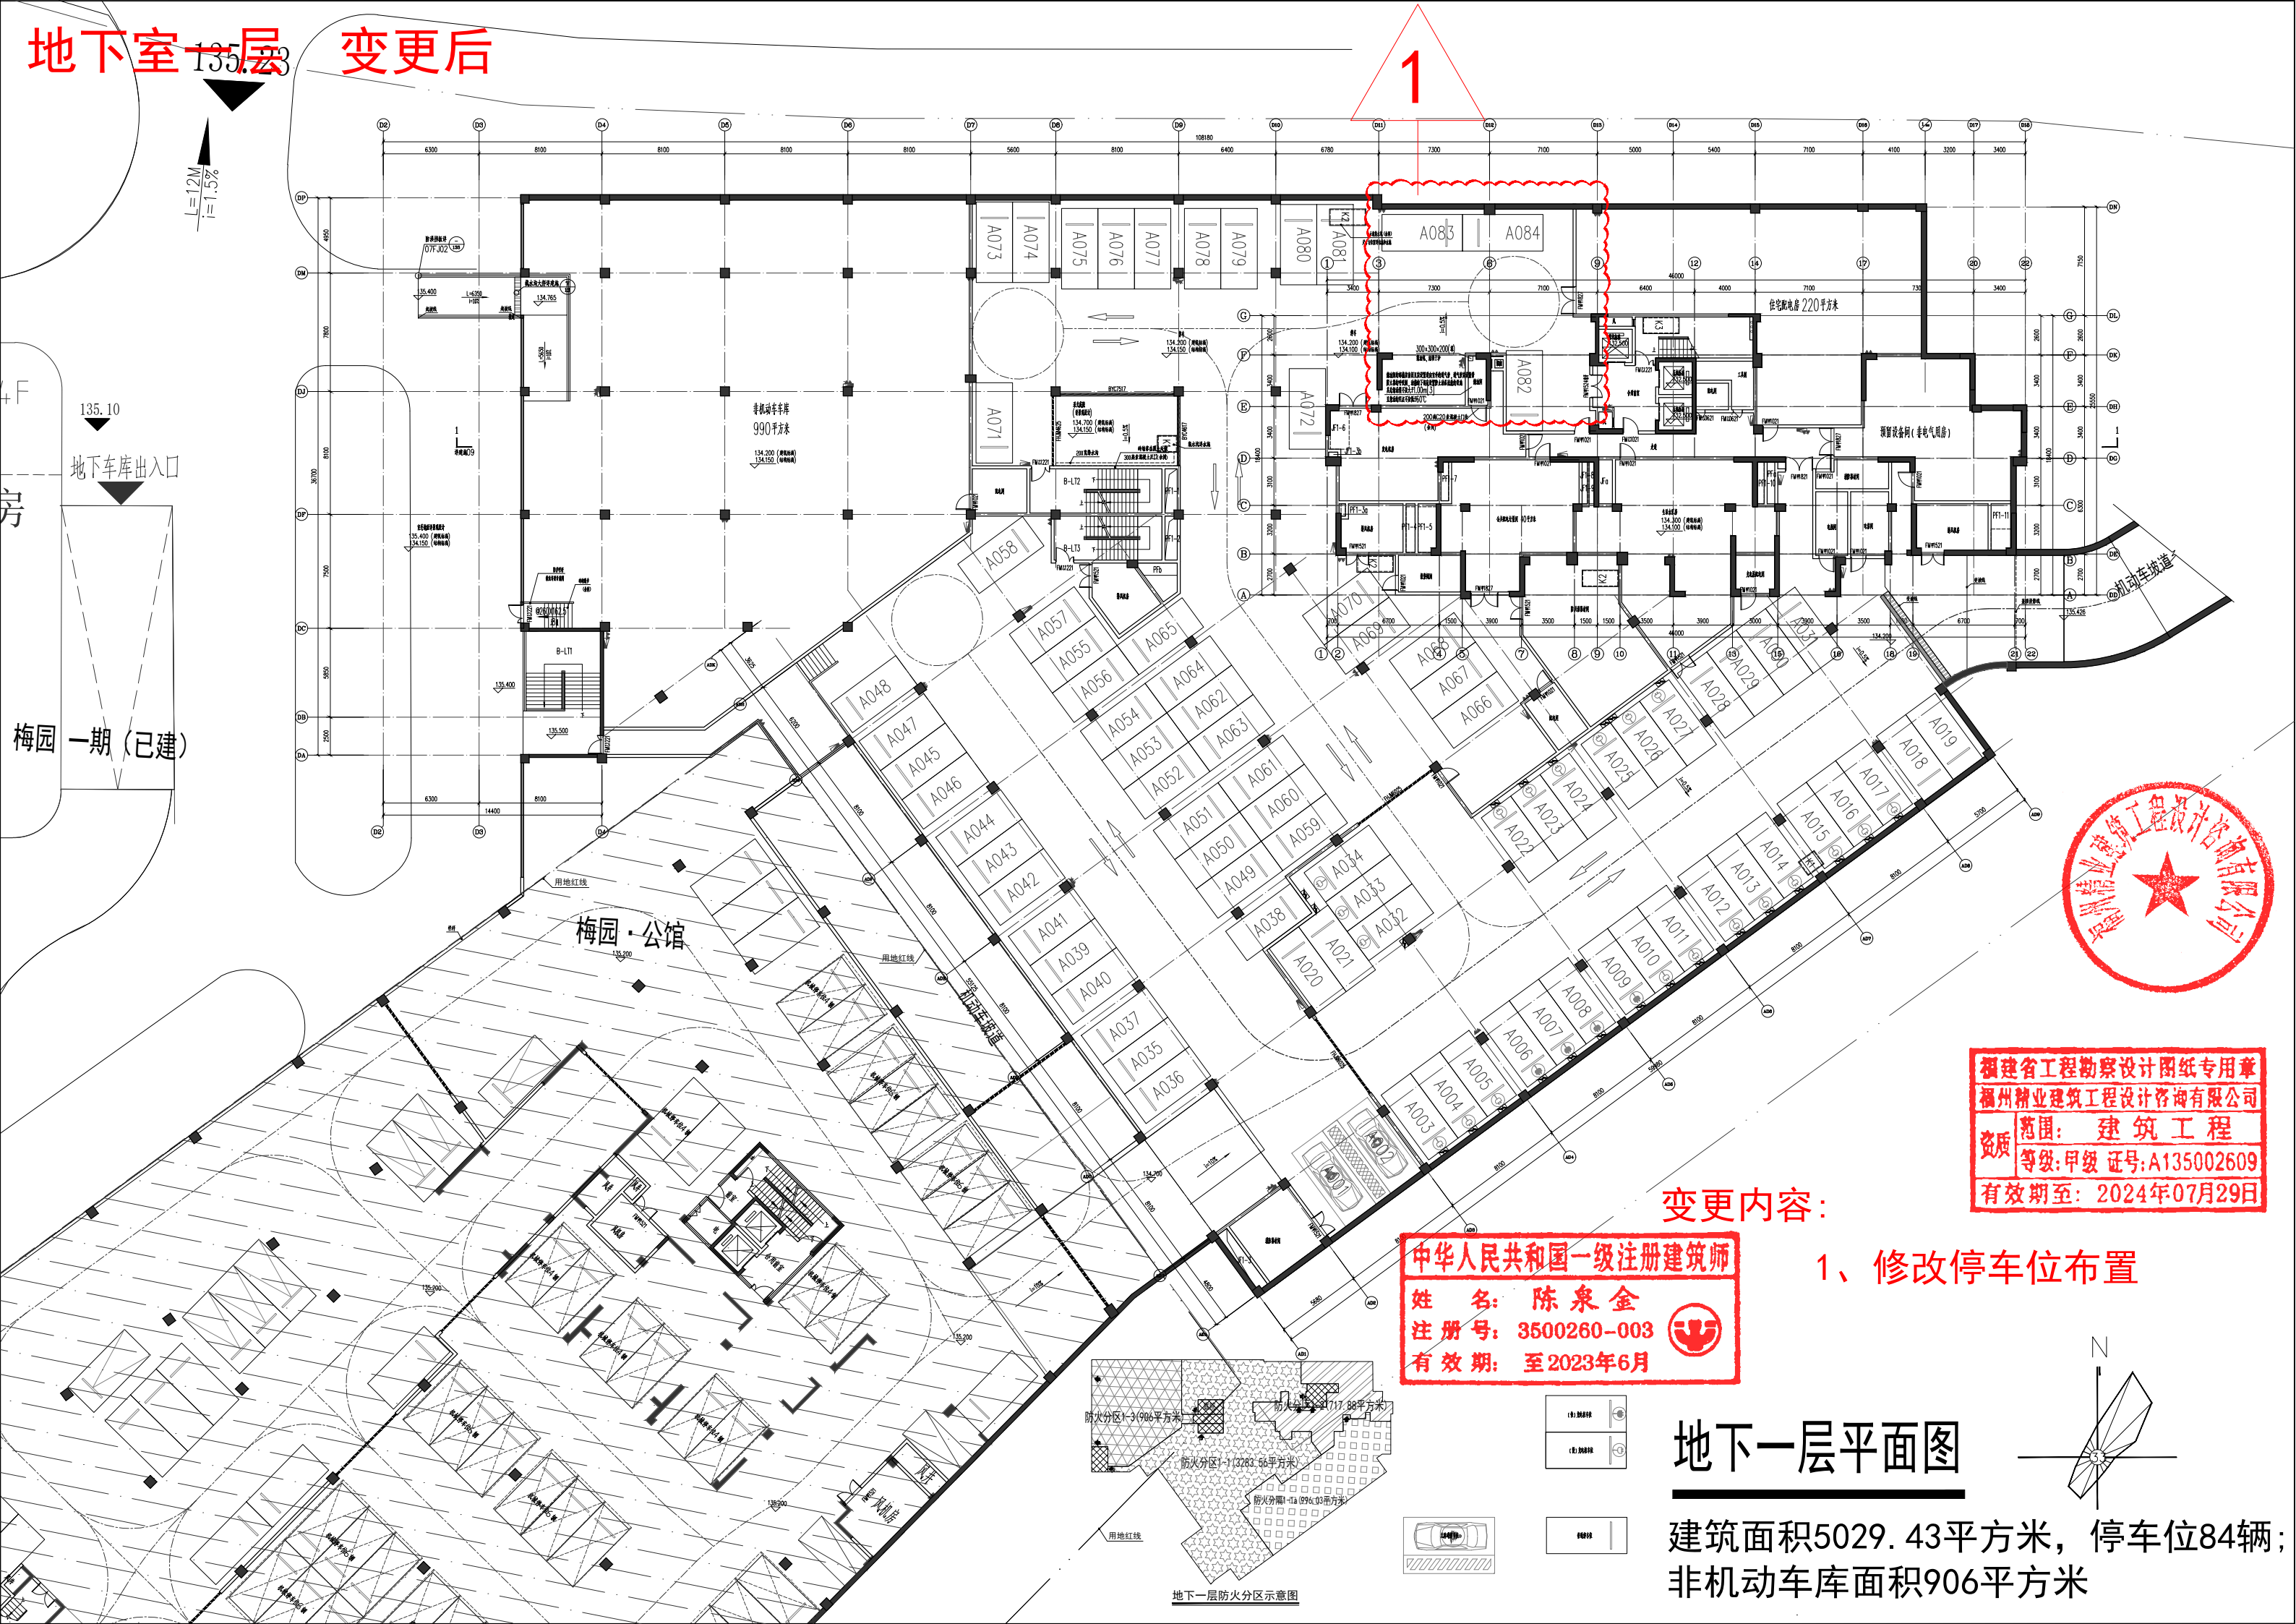





福建省工程勘察设计图纸专用章
福州精业建筑工程设计咨询有限公司
范围: 建筑工程
资质等级: 甲级 证号: A135002609
有效期至: 2024年07月29日

变更内容:
1、修改停车位布置


中华人民共和国一级注册建筑师
姓名: 陈泉金
注册号: 3500260-003
有效期: 至2023年6月

地下一层平面图

建筑面积5029.43平方米, 停车位84辆;
非机动车库面积906平方米

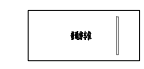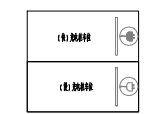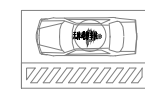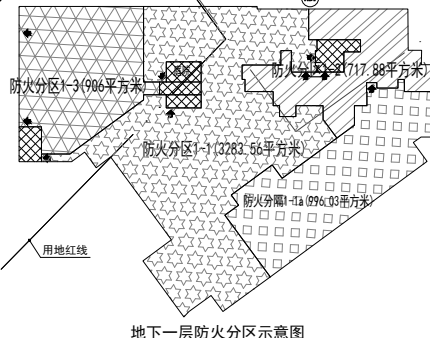

地下室二层 变更前

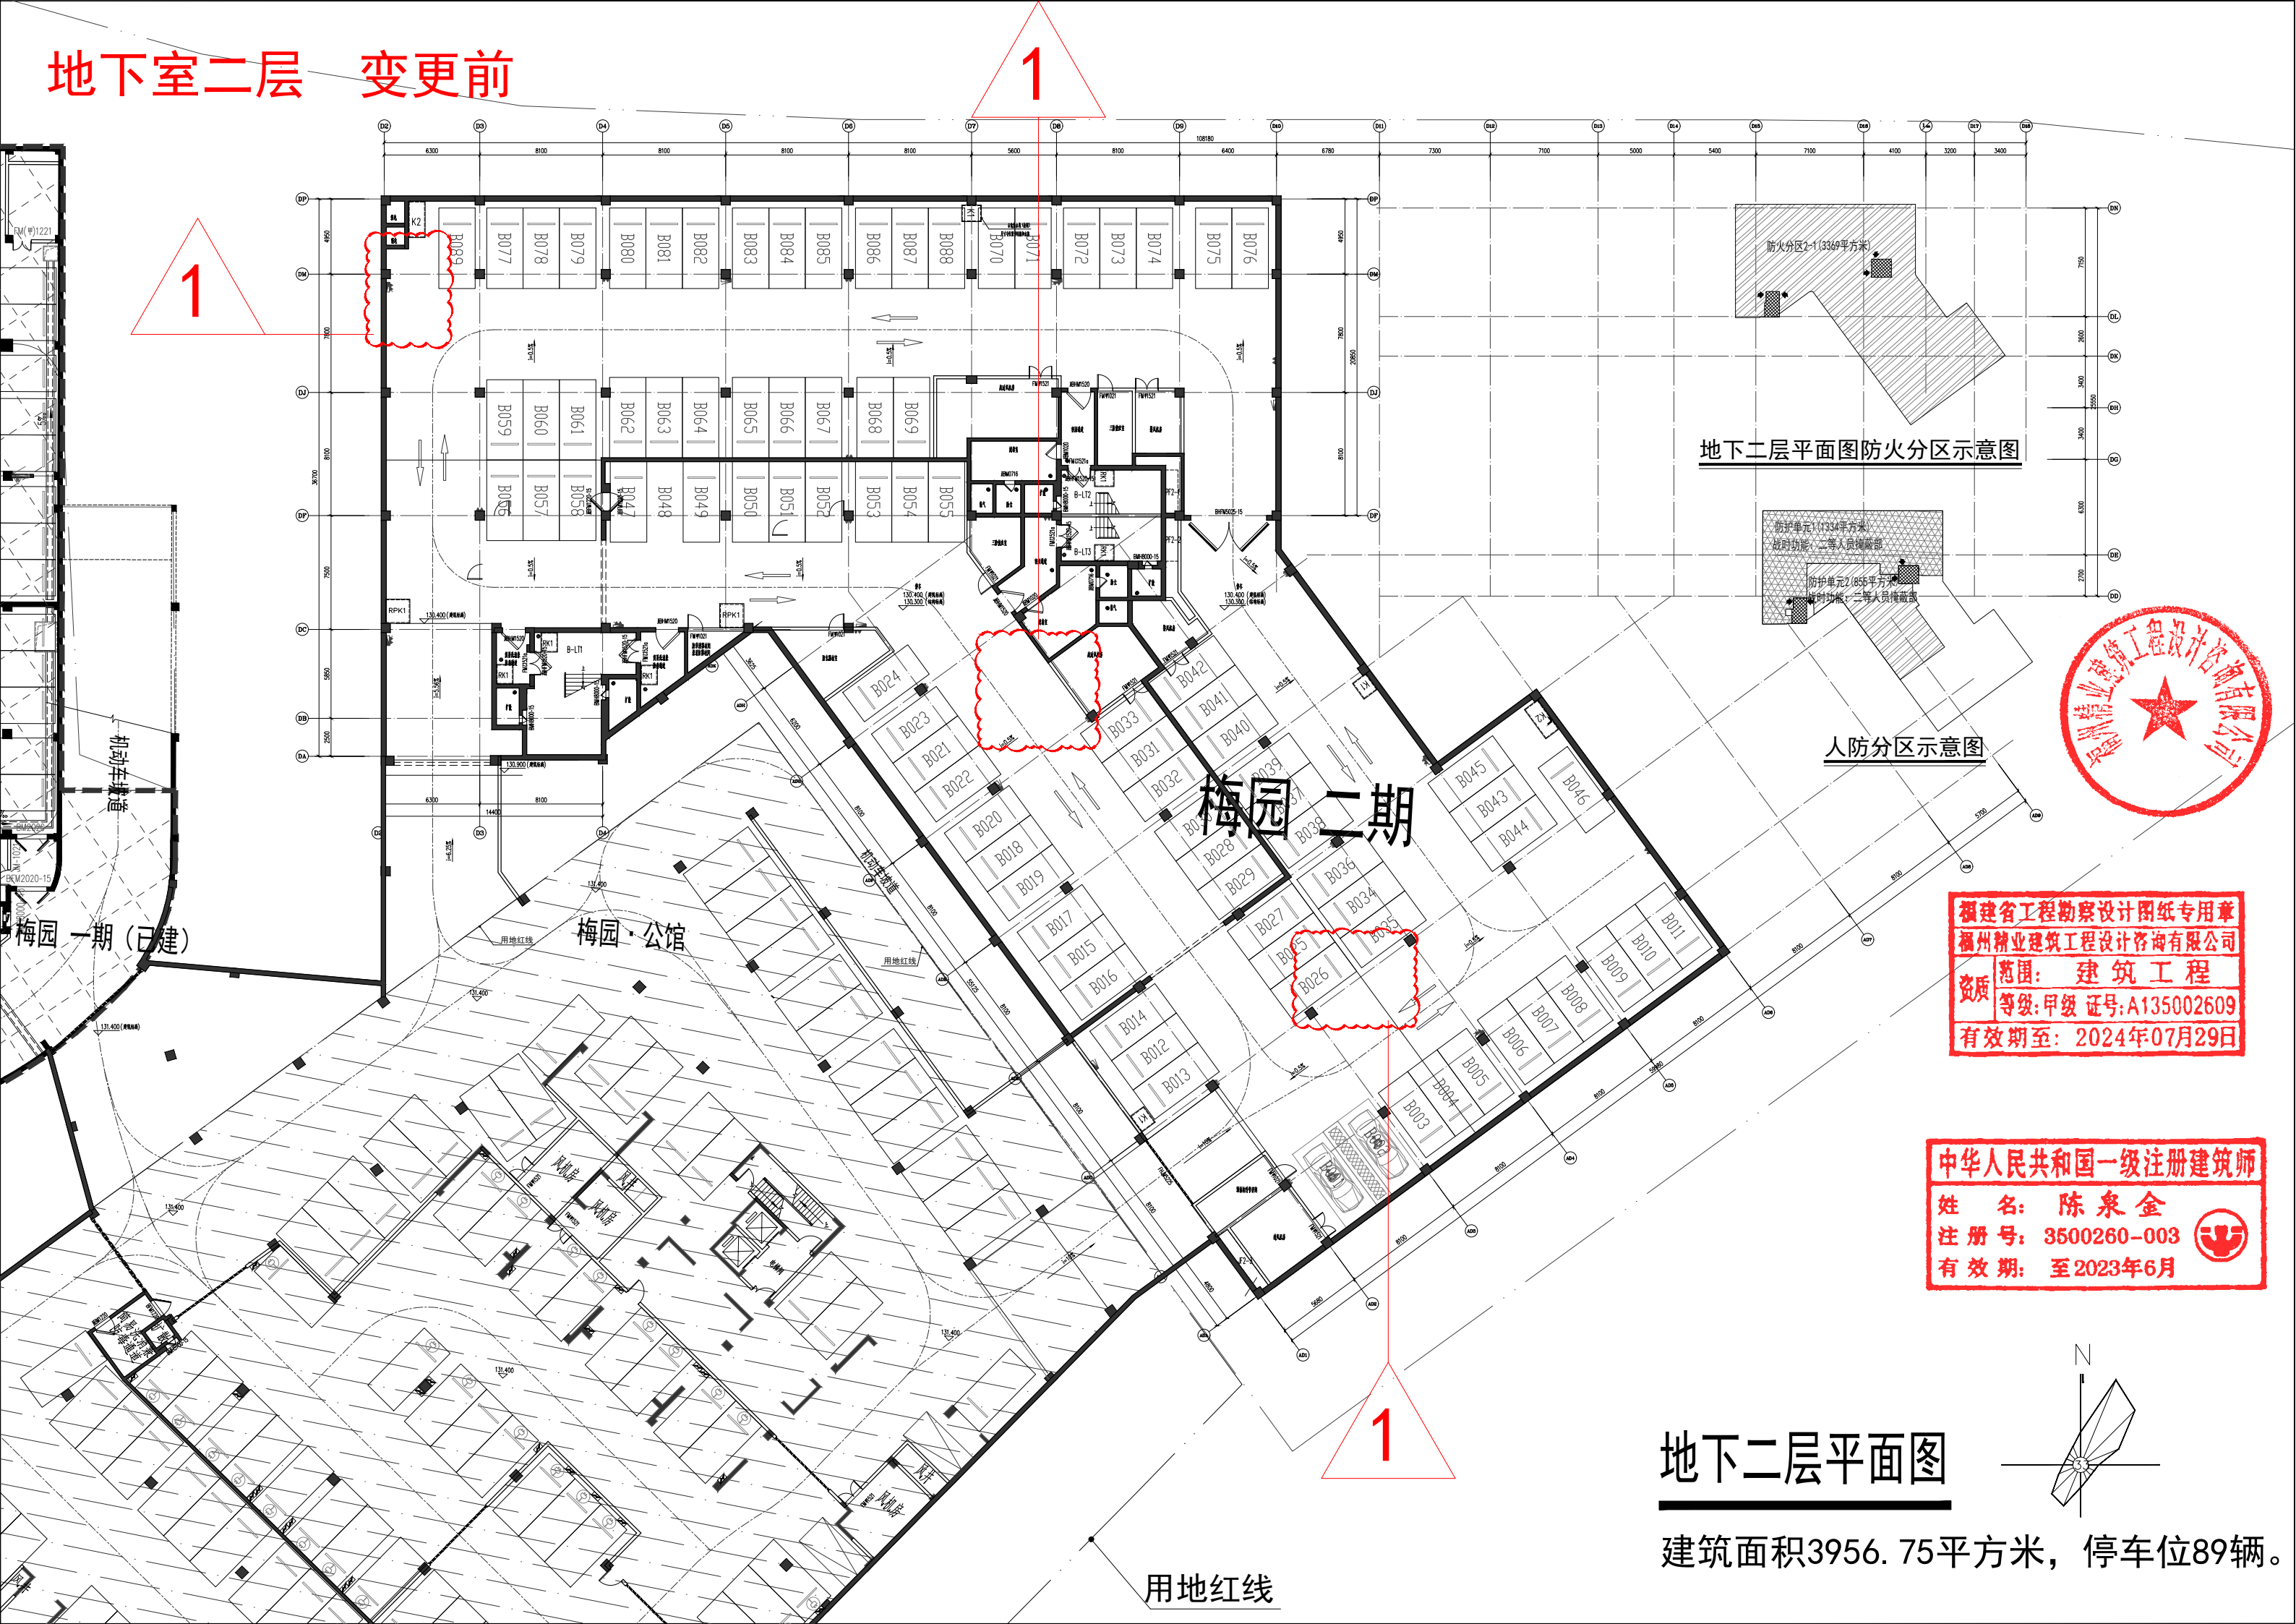

地下二层平面图防火分区示意图

人防分区示意图



福建省工程勘察设计图纸专用章
福州精业建筑工程设计咨询有限公司
范围： 建筑工程
资质等级：甲级 证号：A135002609
有效期至：2024年07月29日


中华人民共和国一级注册建筑师
姓名：陈泉金
注册号：3500260-003
有效期：至2023年6月

地下二层平面图

建筑面积3956.75平方米，停车位89辆。

用地红线

地下室二层 变更后

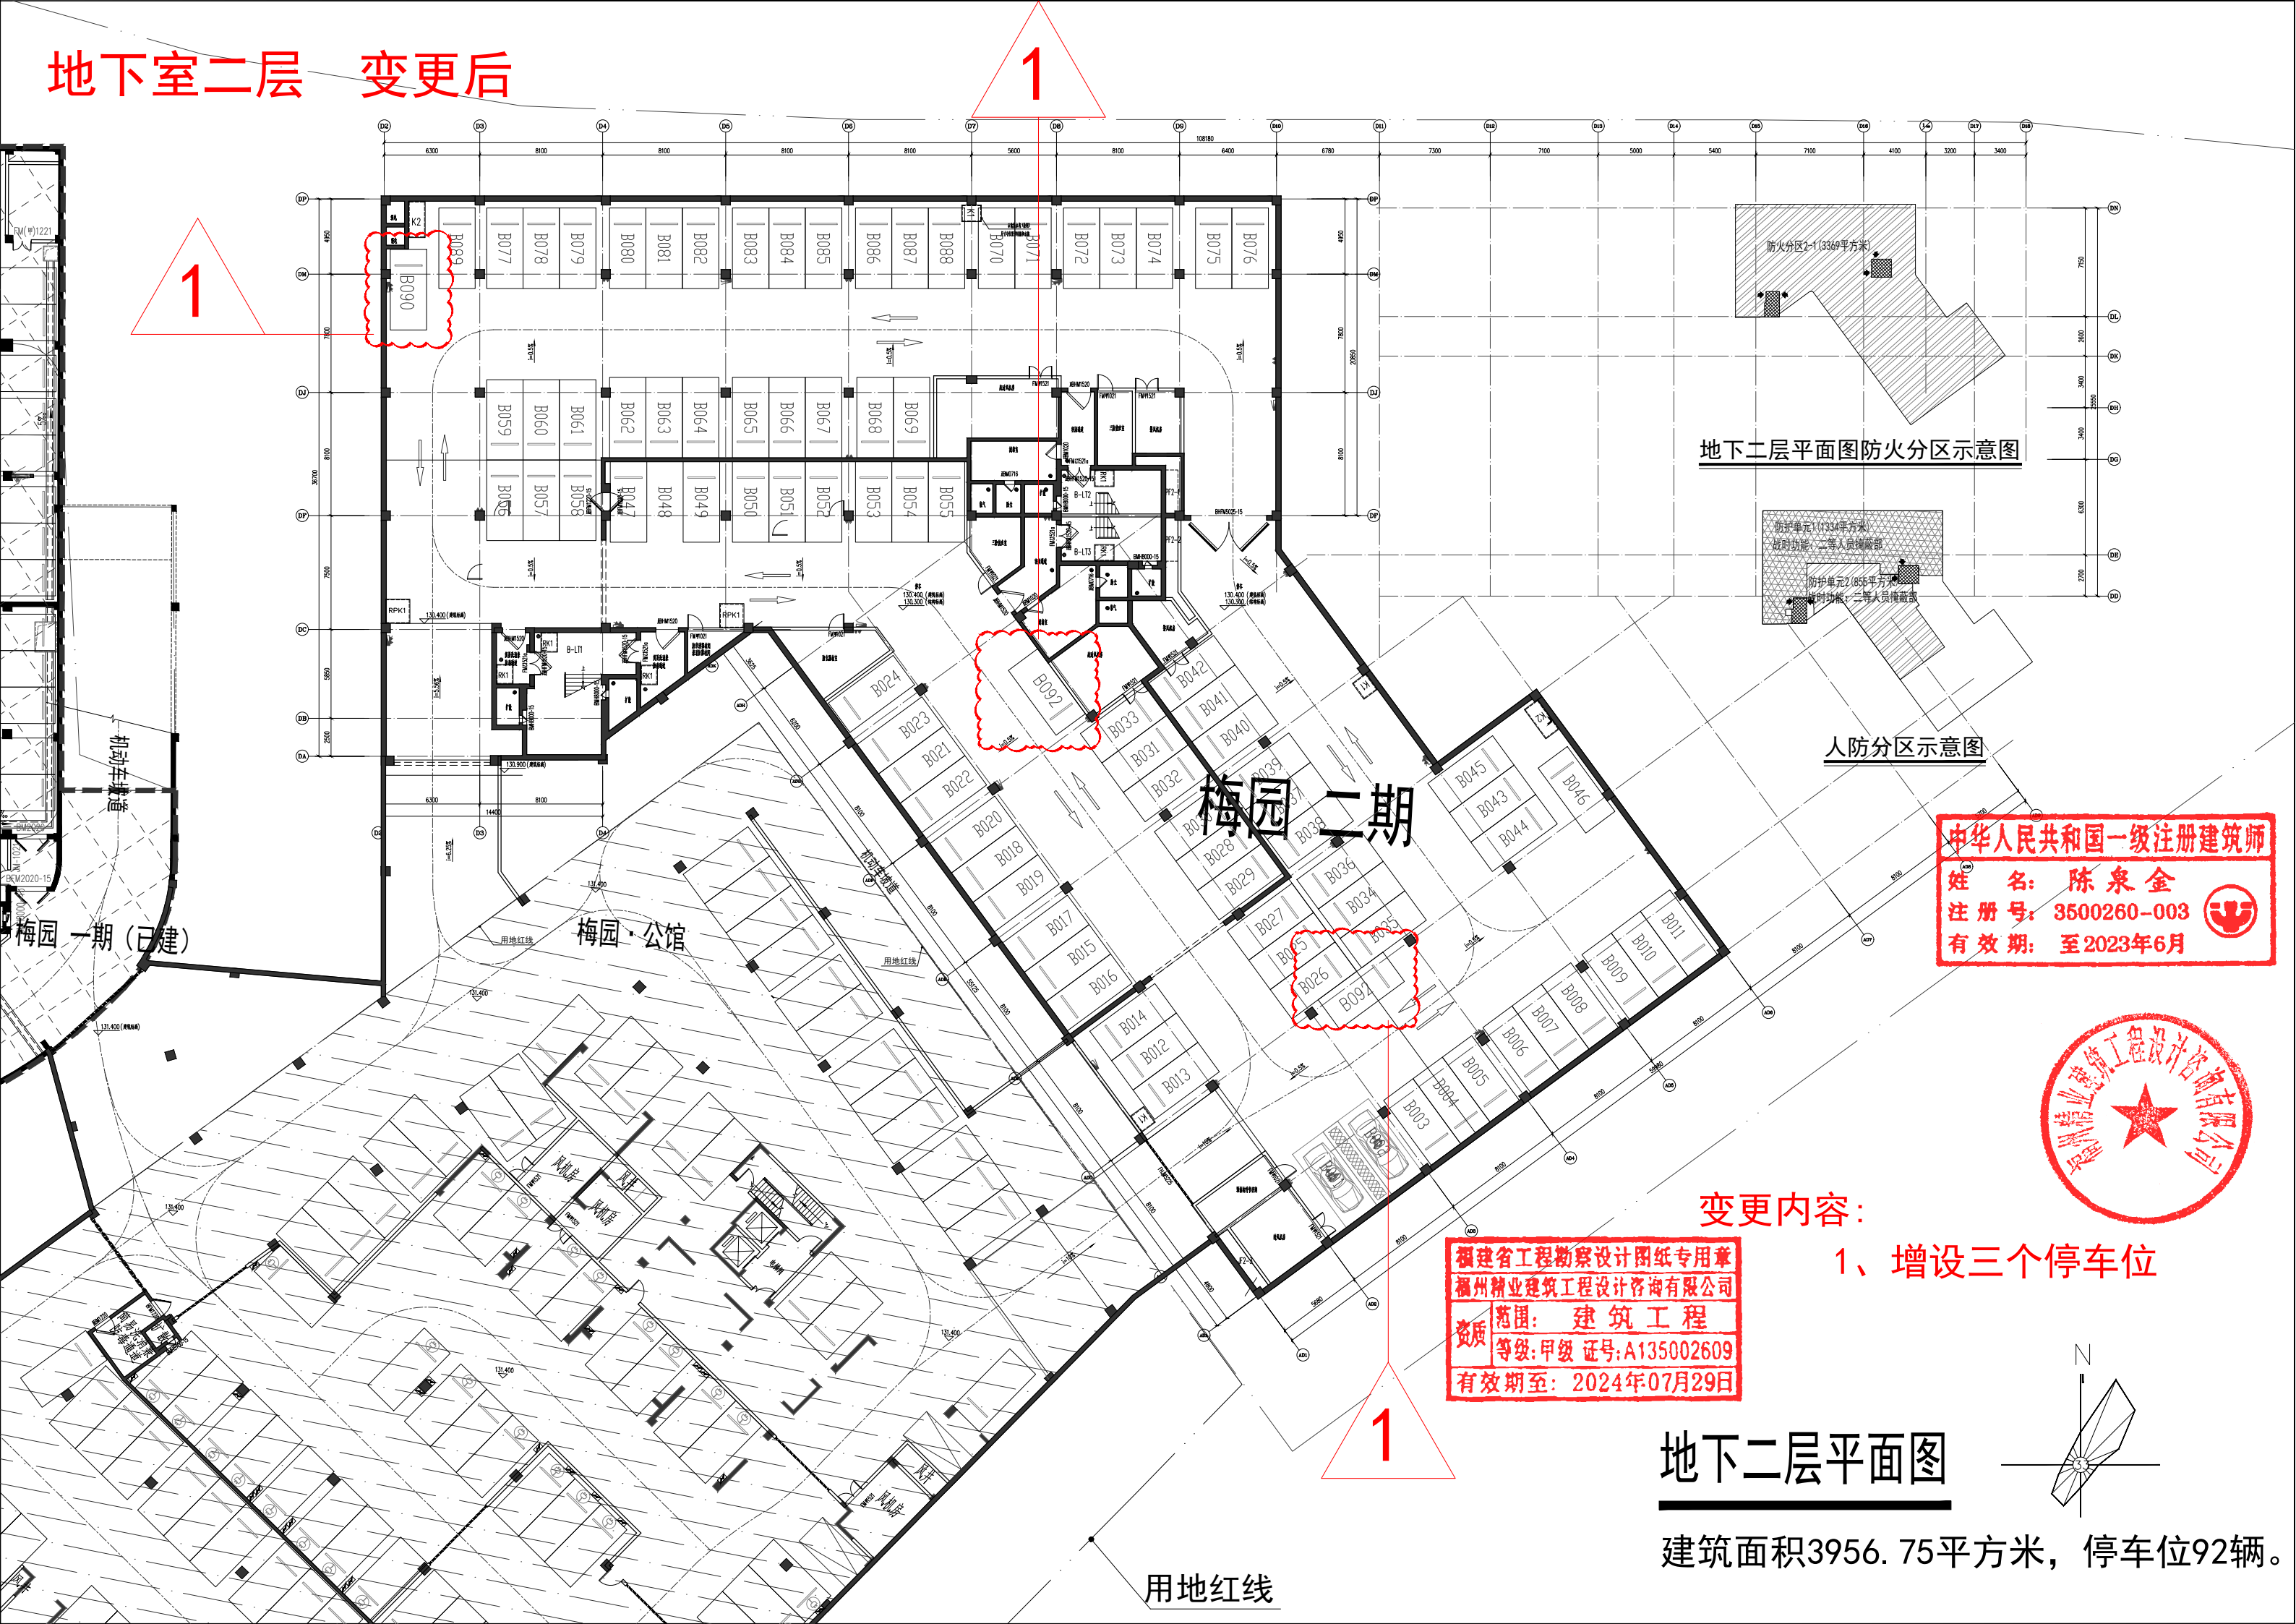

地下二层平面图防火分区示意图

人防分区示意图

中华人民共和国一级注册建筑师
姓名: 陈泉金
注册号: 3500260-003
有效期: 至2023年6月



变更内容:

1、增设三个停车位

福建省工程勘察设计图纸专用章
福州精业建筑工程设计咨询有限公司
资质范围: 建筑工程
等级: 甲级 证号: A135002609
有效期至: 2024年07月29日

地下二层平面图


建筑面积3956.75平方米, 停车位92辆。

用地红线

福建省工程勘察设计图纸专用章
福州精业建筑工程设计咨询有限公司
范围: 建筑工程
资质等级: 甲级 证号: A135002609
有效期至: 2024年07月29日



中华人民共和国一级注册建筑师
姓名: 陈泉金
注册号: 3500260-003
有效期: 至2023年6月

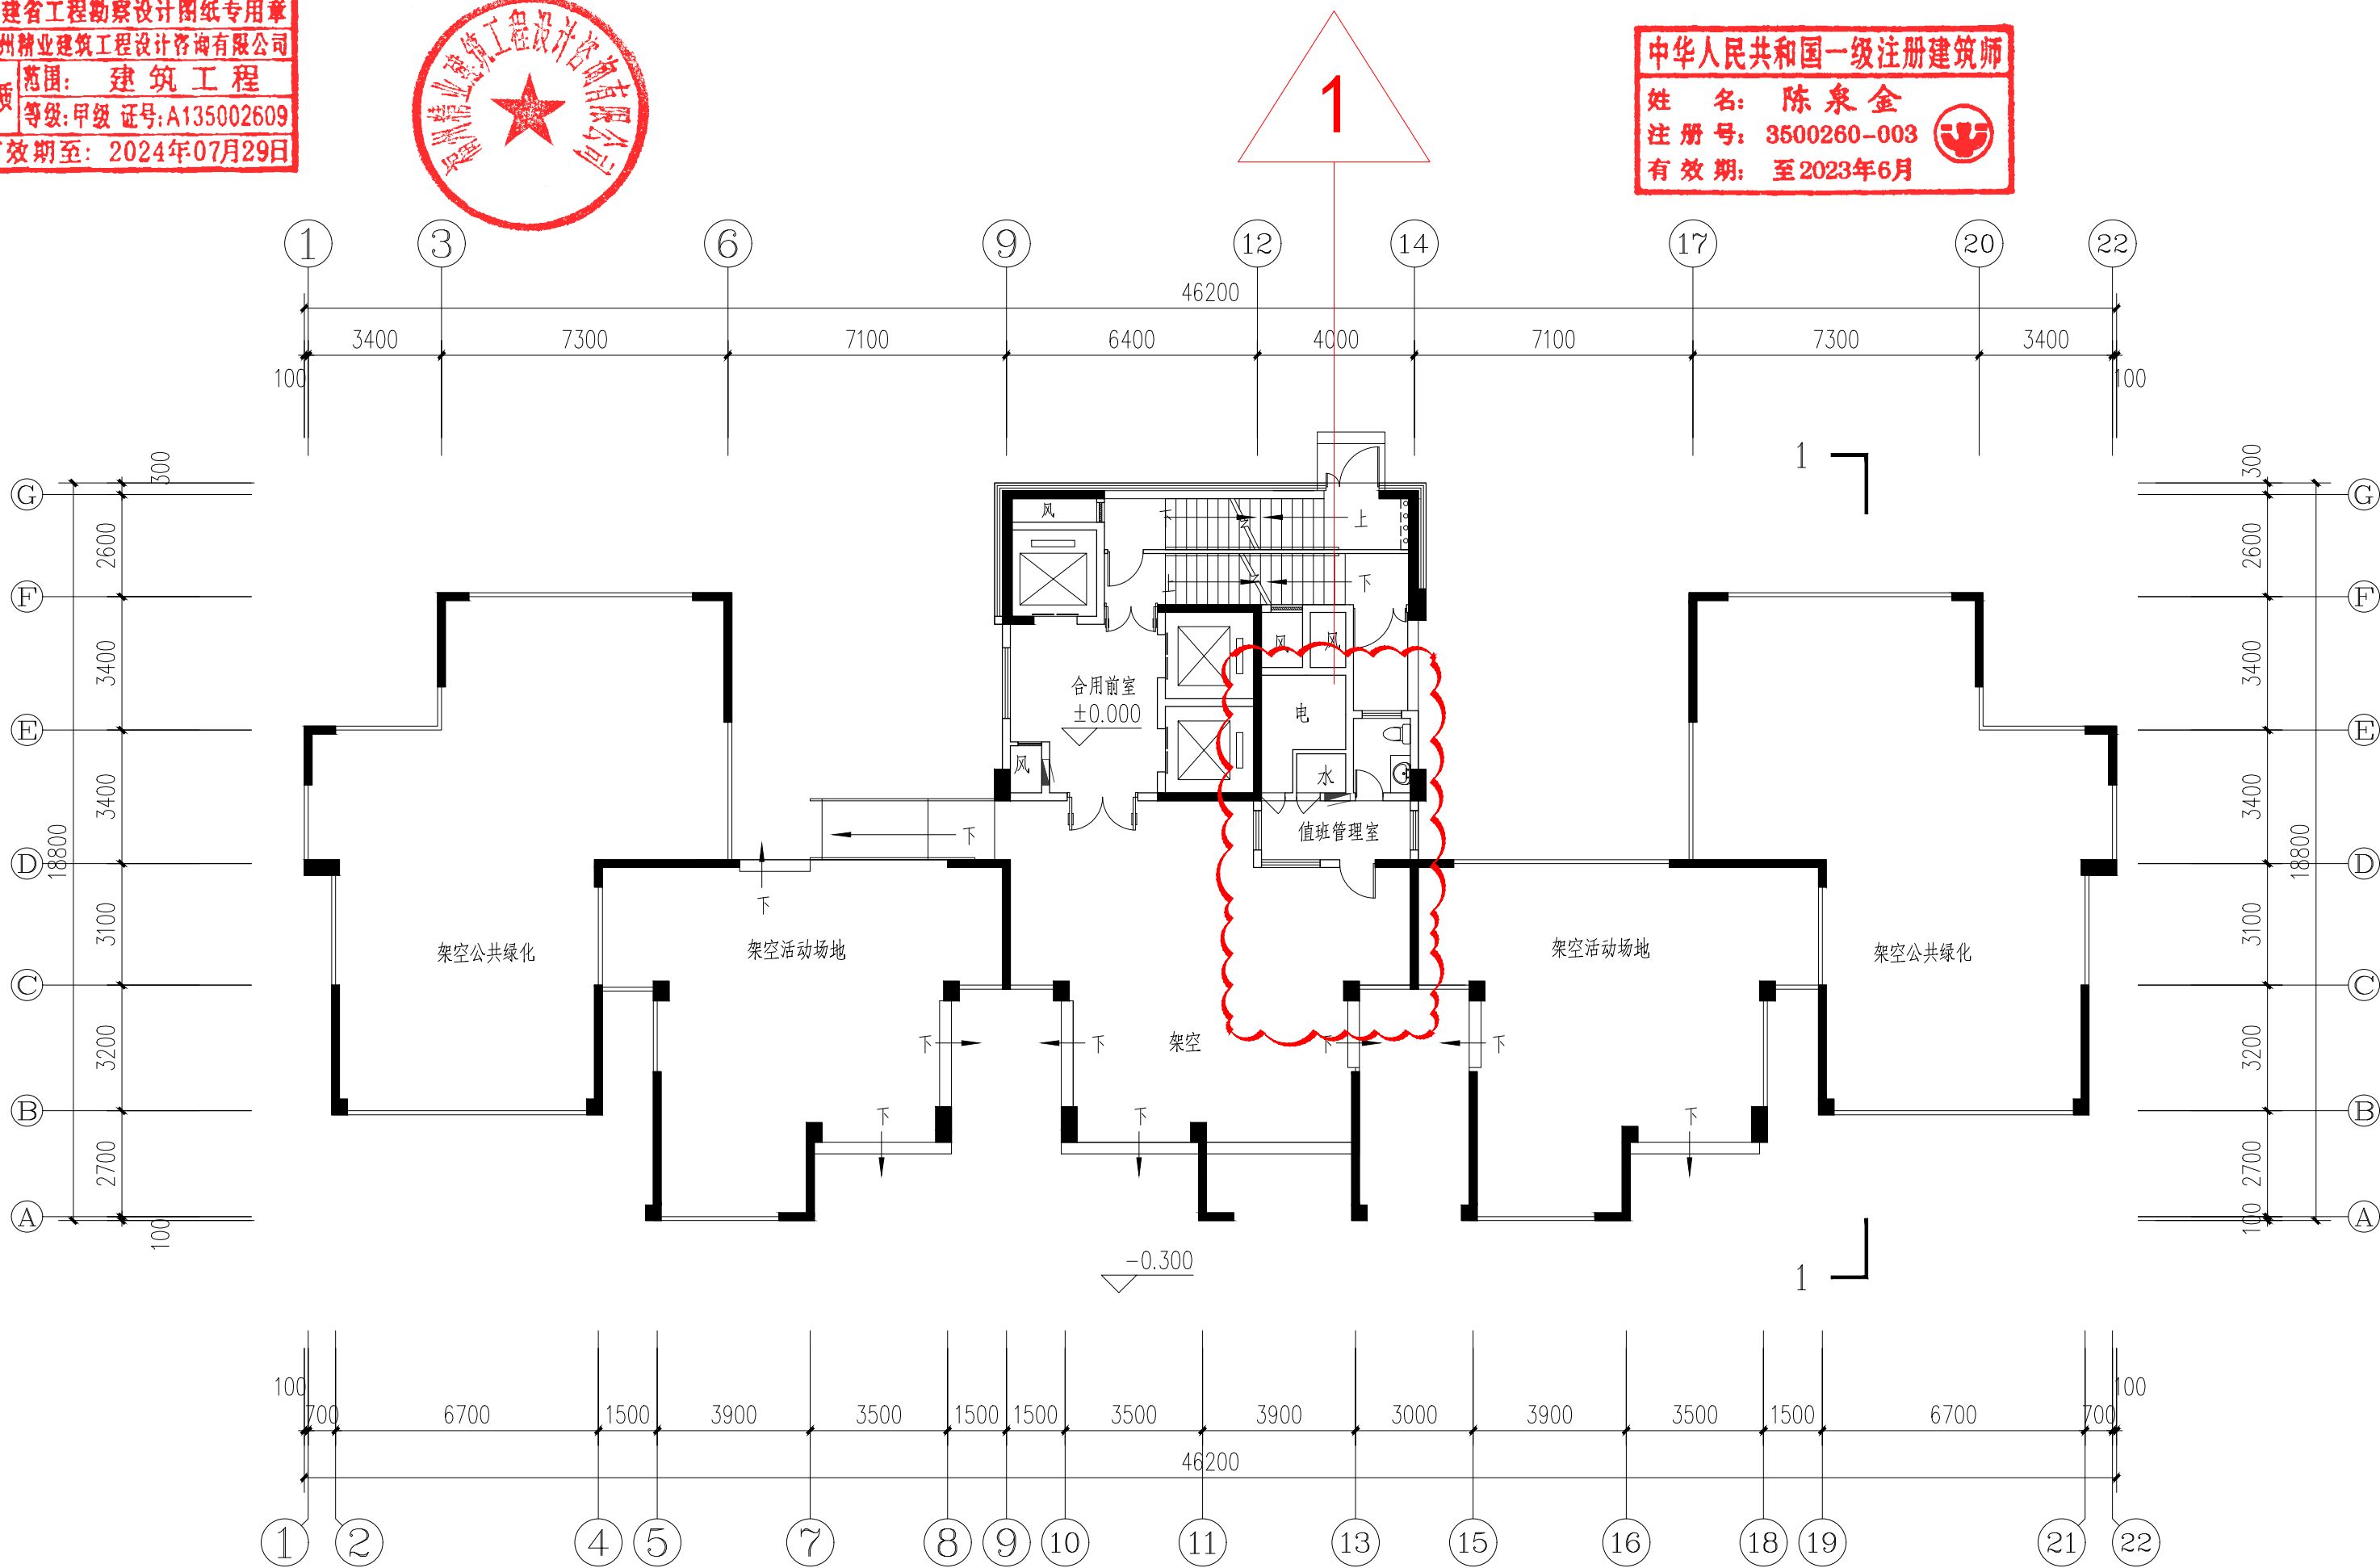



一层平面图

一层平面图变更前



福建省工程勘察设计图纸专用章
福州精业建筑工程设计咨询有限公司
资质 范围: 建筑工程
等级: 甲级 证号: A135002609
有效期至: 2024年07月29日

中华人民共和国一级注册建筑师
姓名: 陈泉金
注册号: 3500260-003
有效期: 至2023年6月

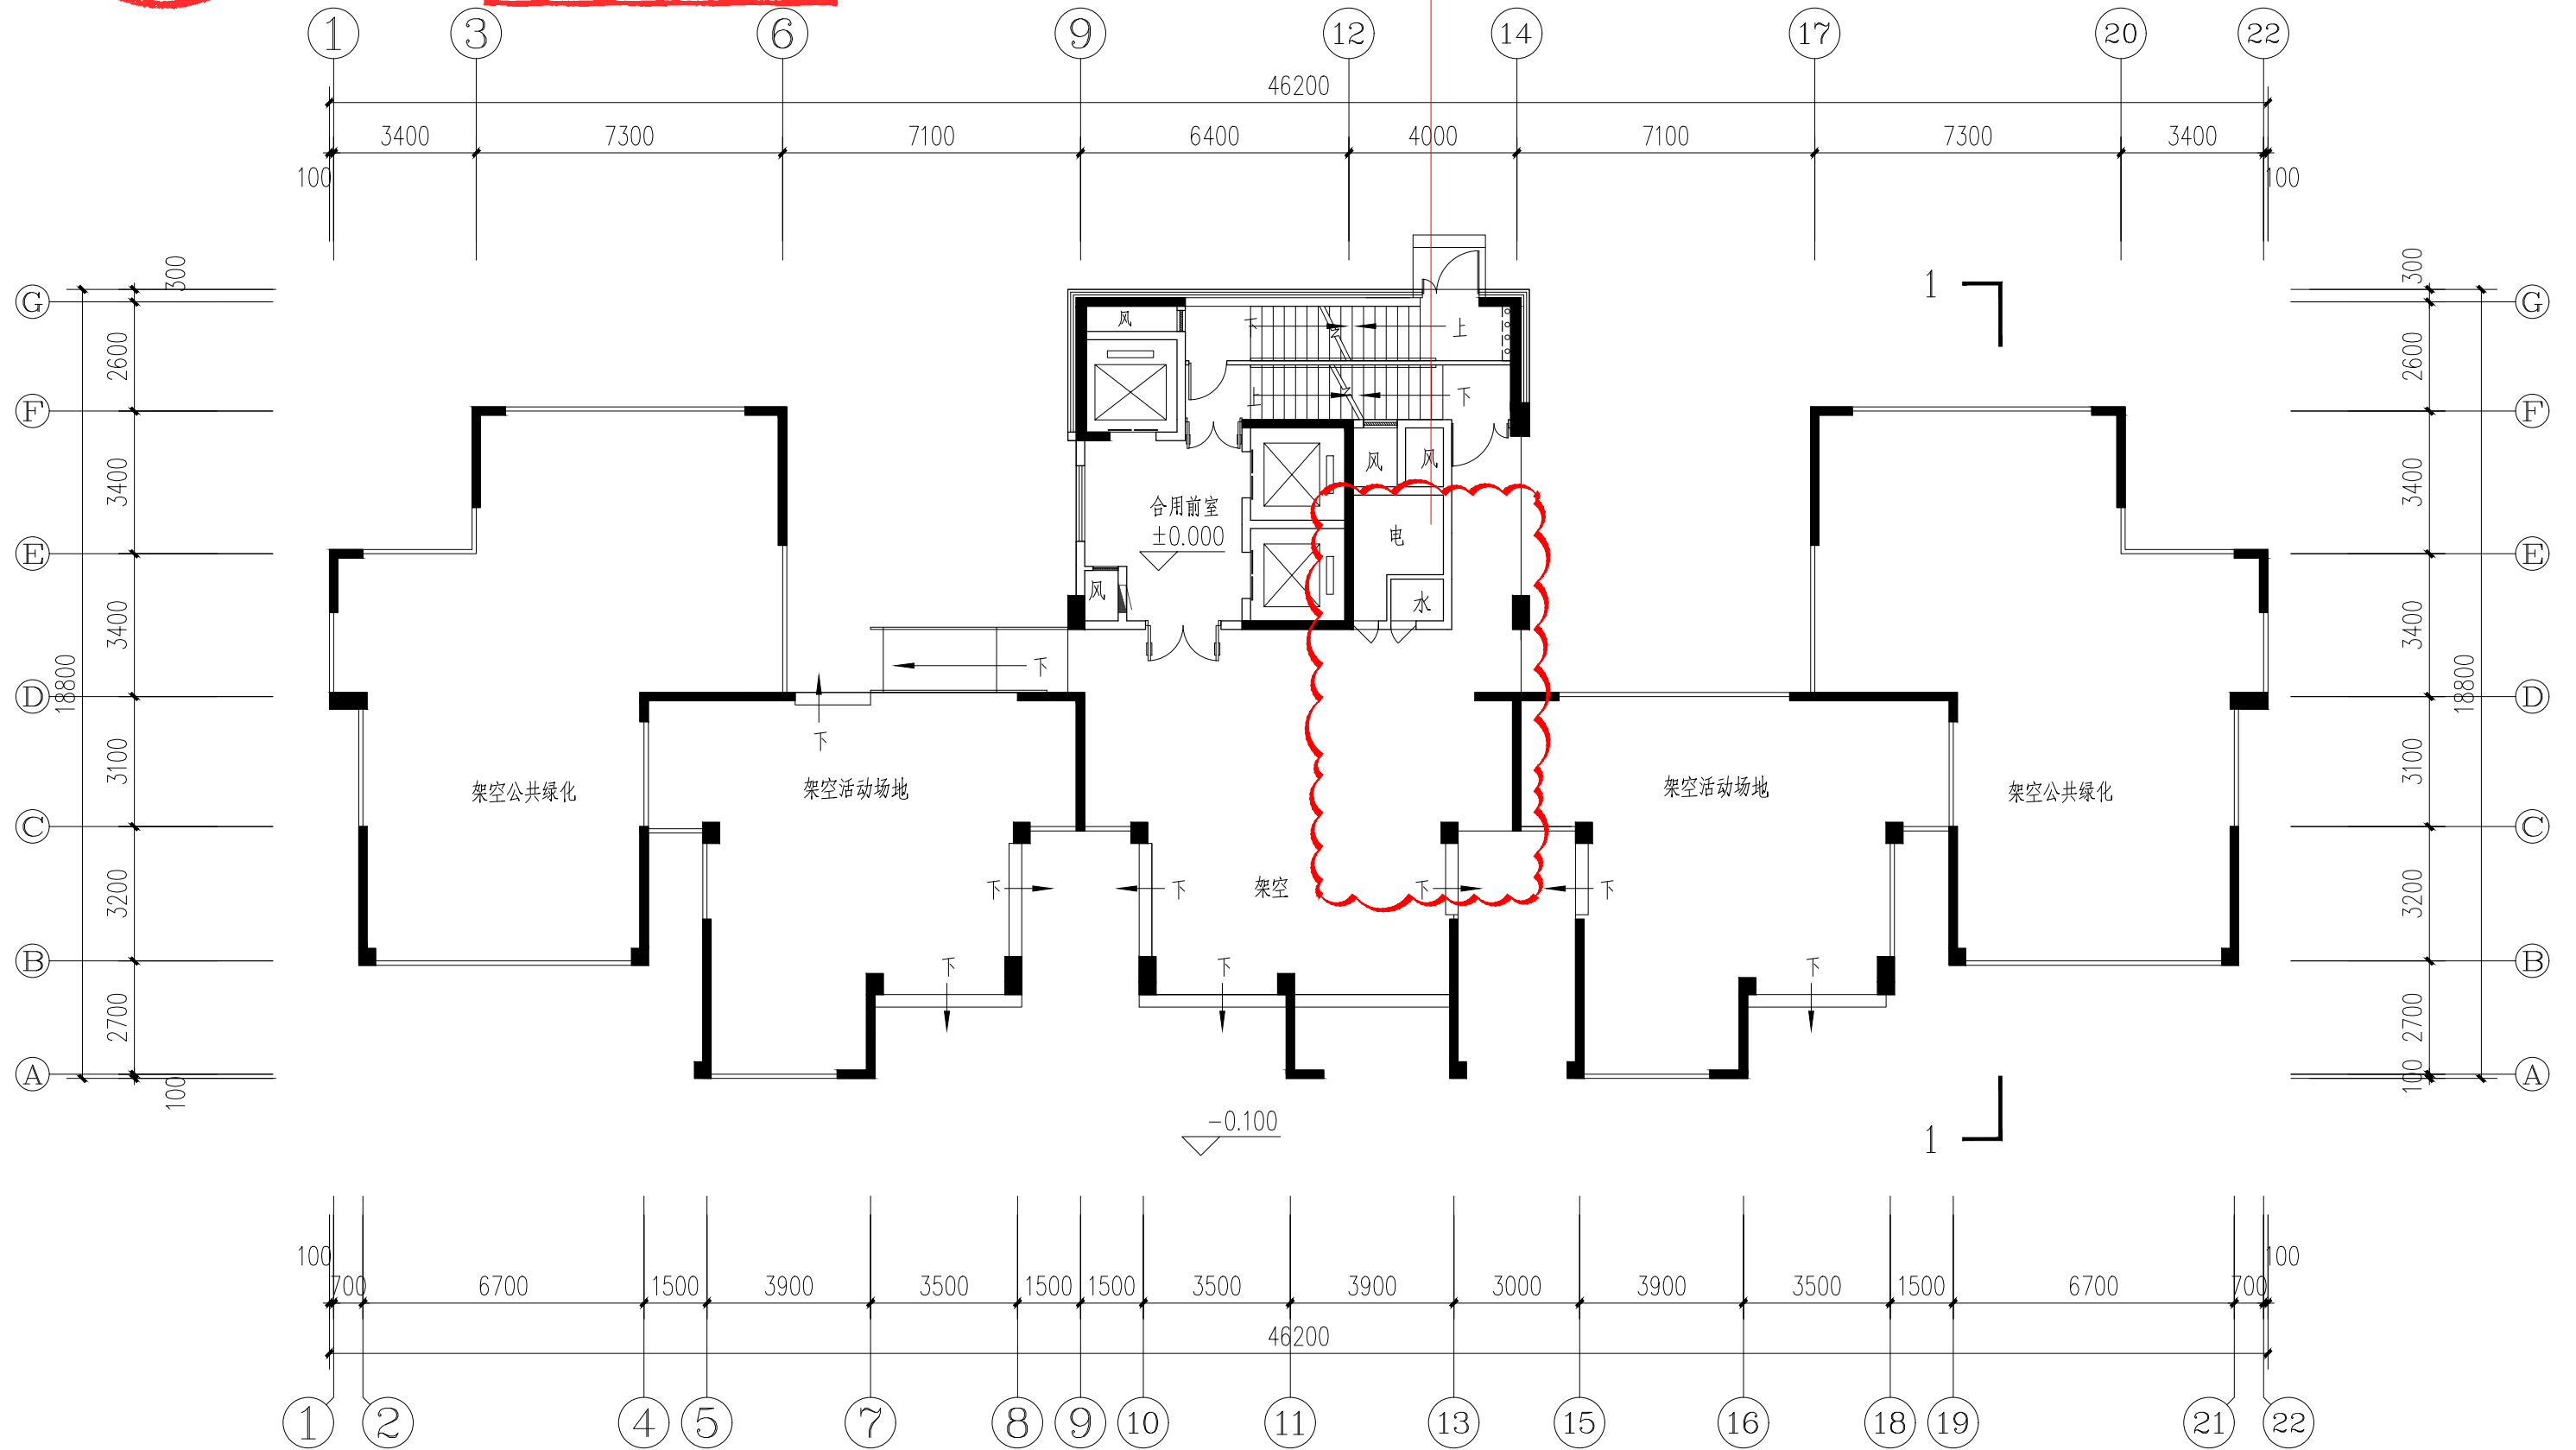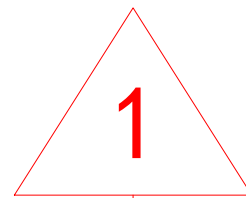


变更内容:

1、取消卫生间、值班管理室。


一层平面图

一层平面图变更后

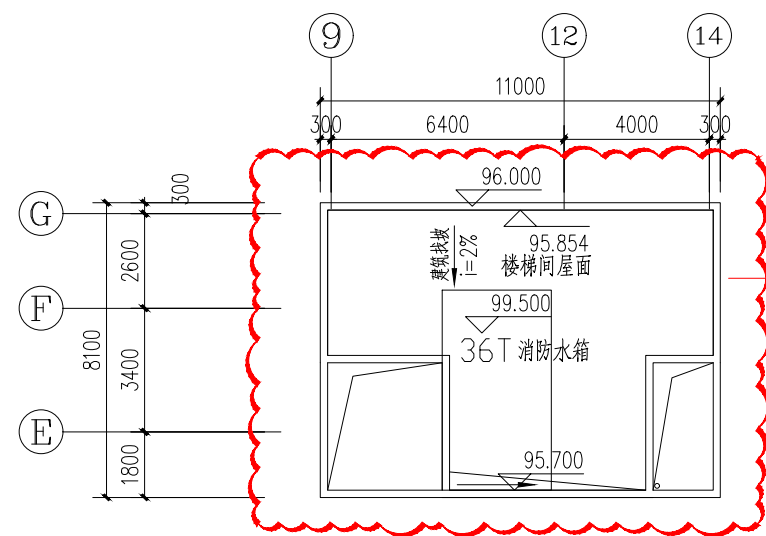


中华人民共和国一级注册建筑师
姓名: 陈泉金
注册号: 3500260-003
有效期: 至2023年6月

福建省工程勘察设计图纸专用章
福州精业建筑工程设计咨询有限公司
范围: 建筑工程
资质等级: 甲级 证号: A135002609
有效期至: 2024年07月29日

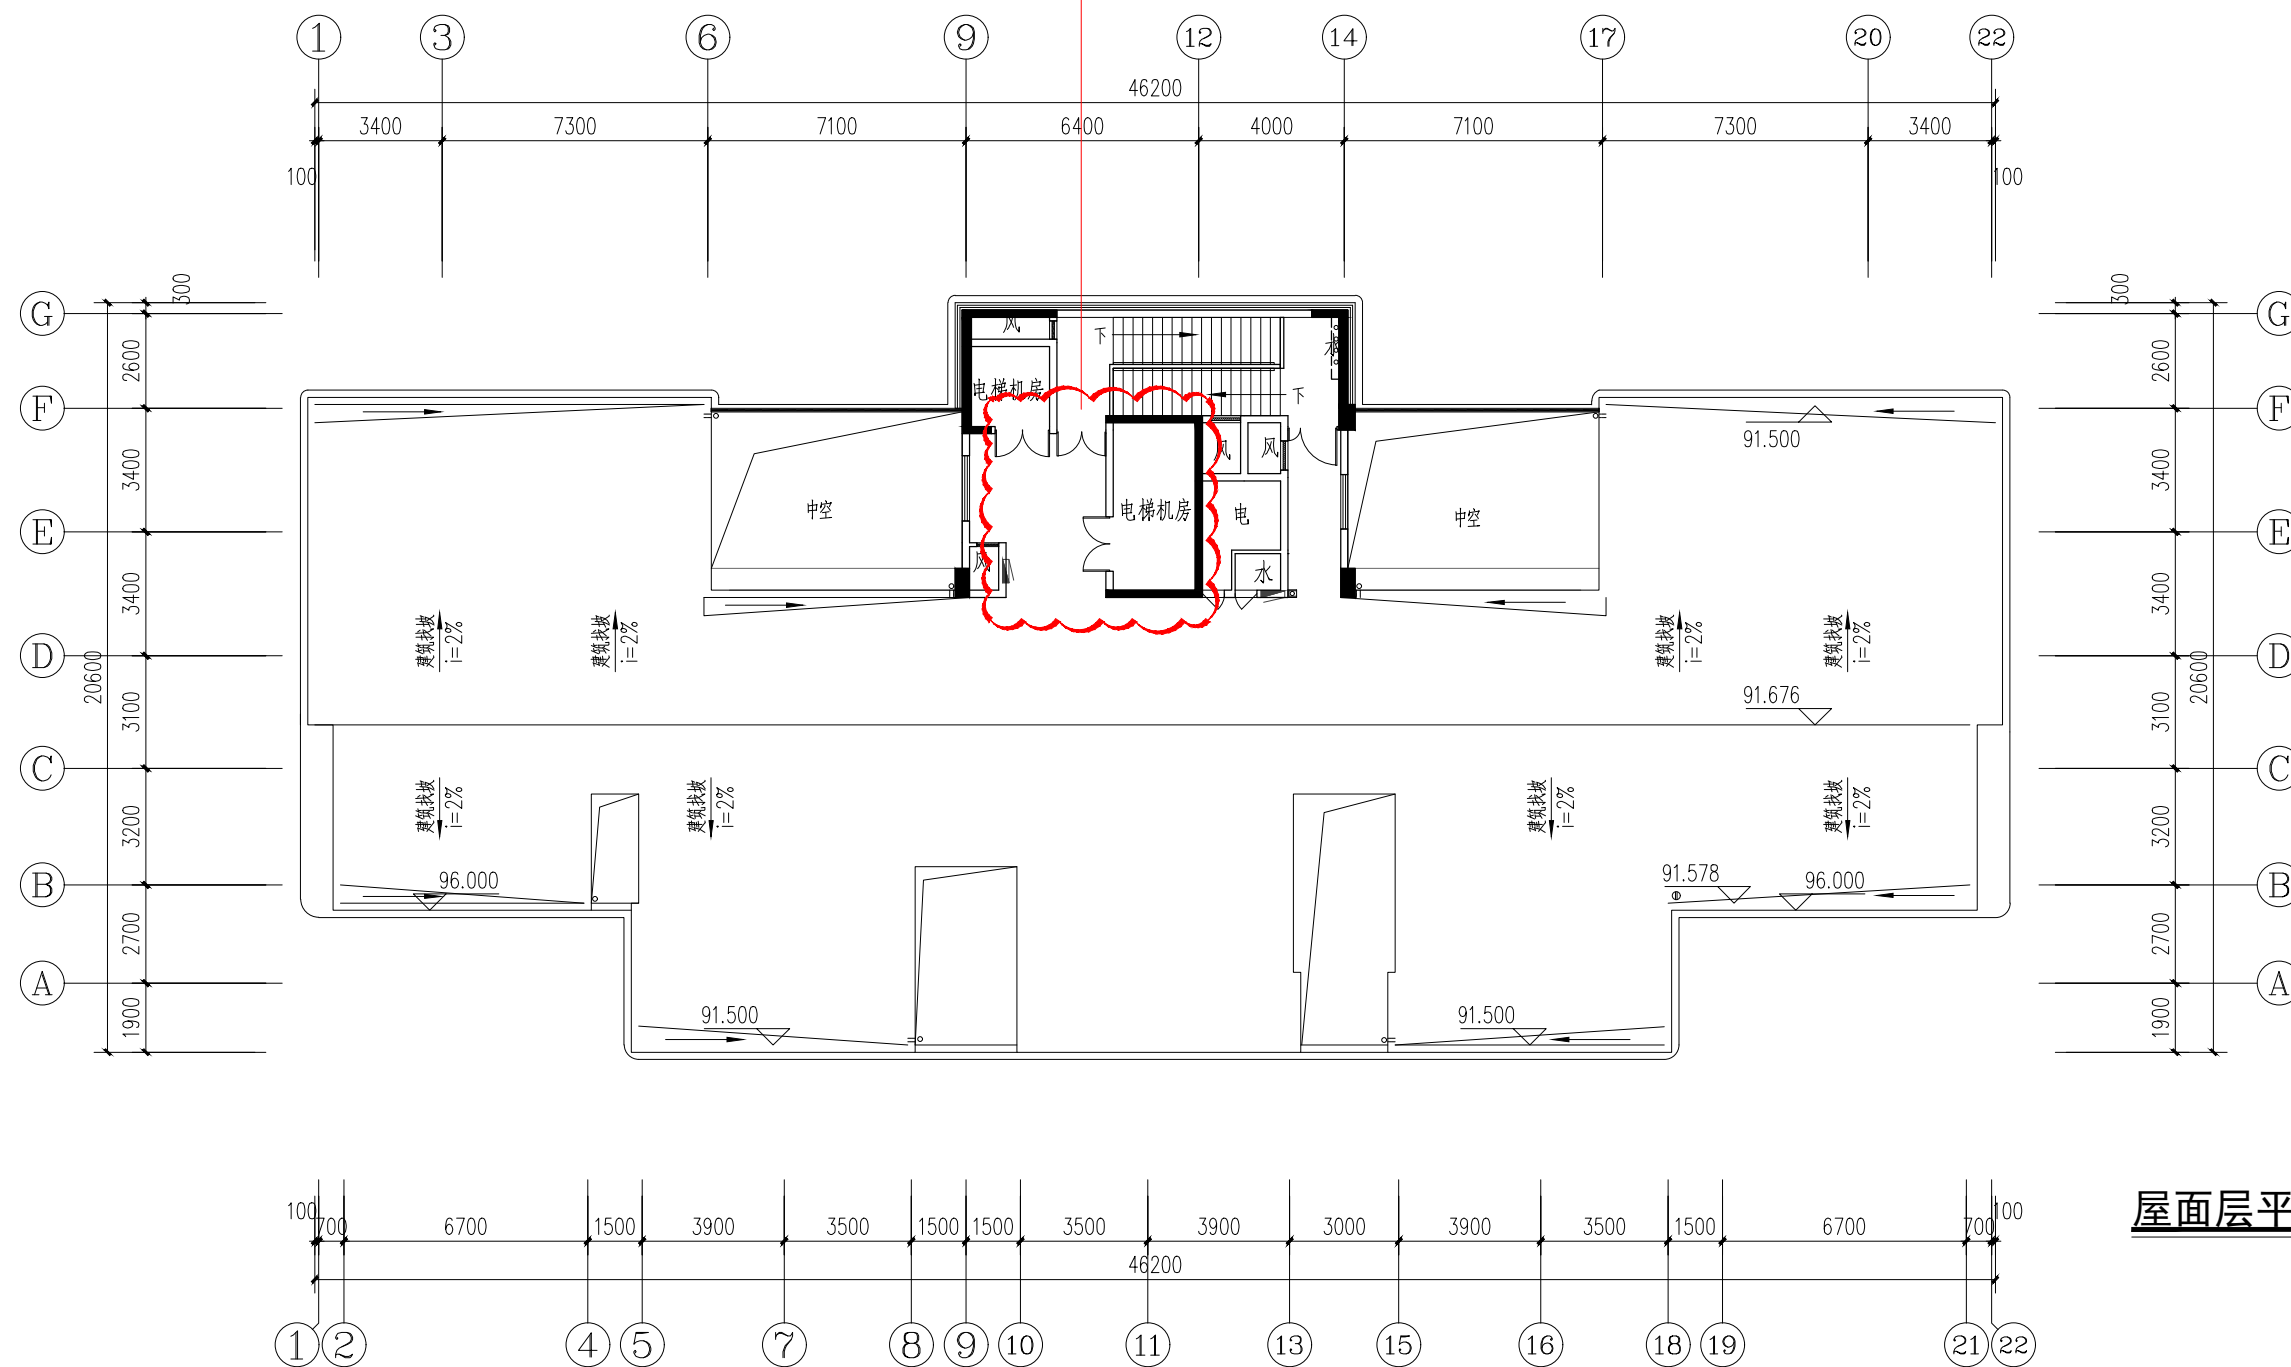


屋面层平面图

屋面层平面图变更前

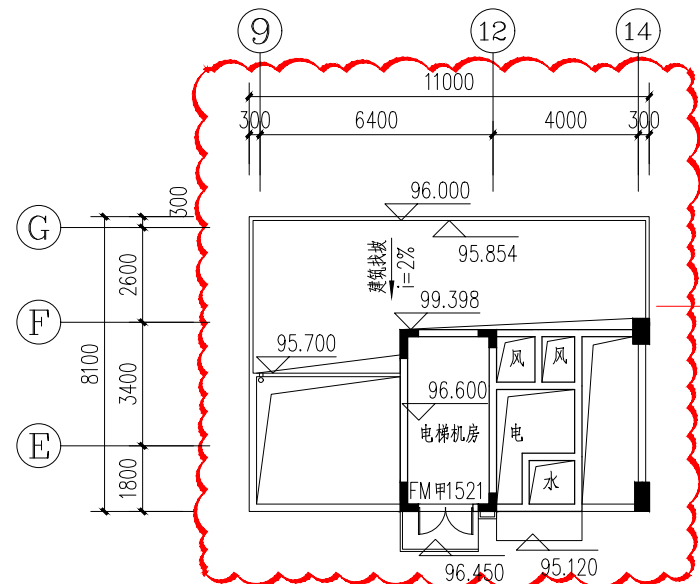

楼梯间屋面平面图

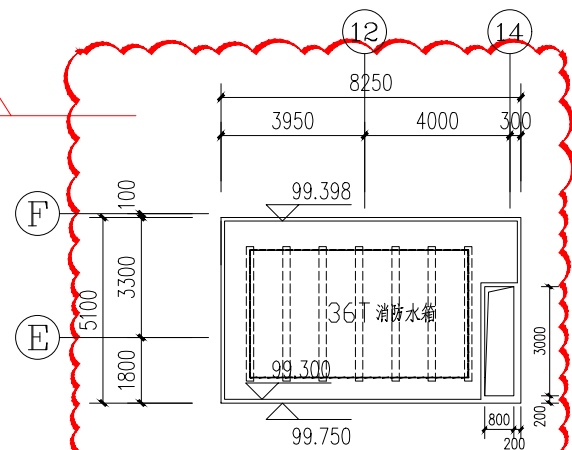

电梯机房屋面平面图


变更内容:

- 1、电梯上屋面层。
- 2、调整电梯机房标高及机电梯房屋面标高。

福建省工程勘察设计图纸专用章
福州精业建筑工程设计咨询有限公司
范围: 建筑工程
资质等级: 甲级 证号: A135002609
有效期至: 2024年07月29日



中华人民共和国一级注册建筑师
姓名: 陈泉金
注册号: 3500260-003
有效期: 至2023年6月

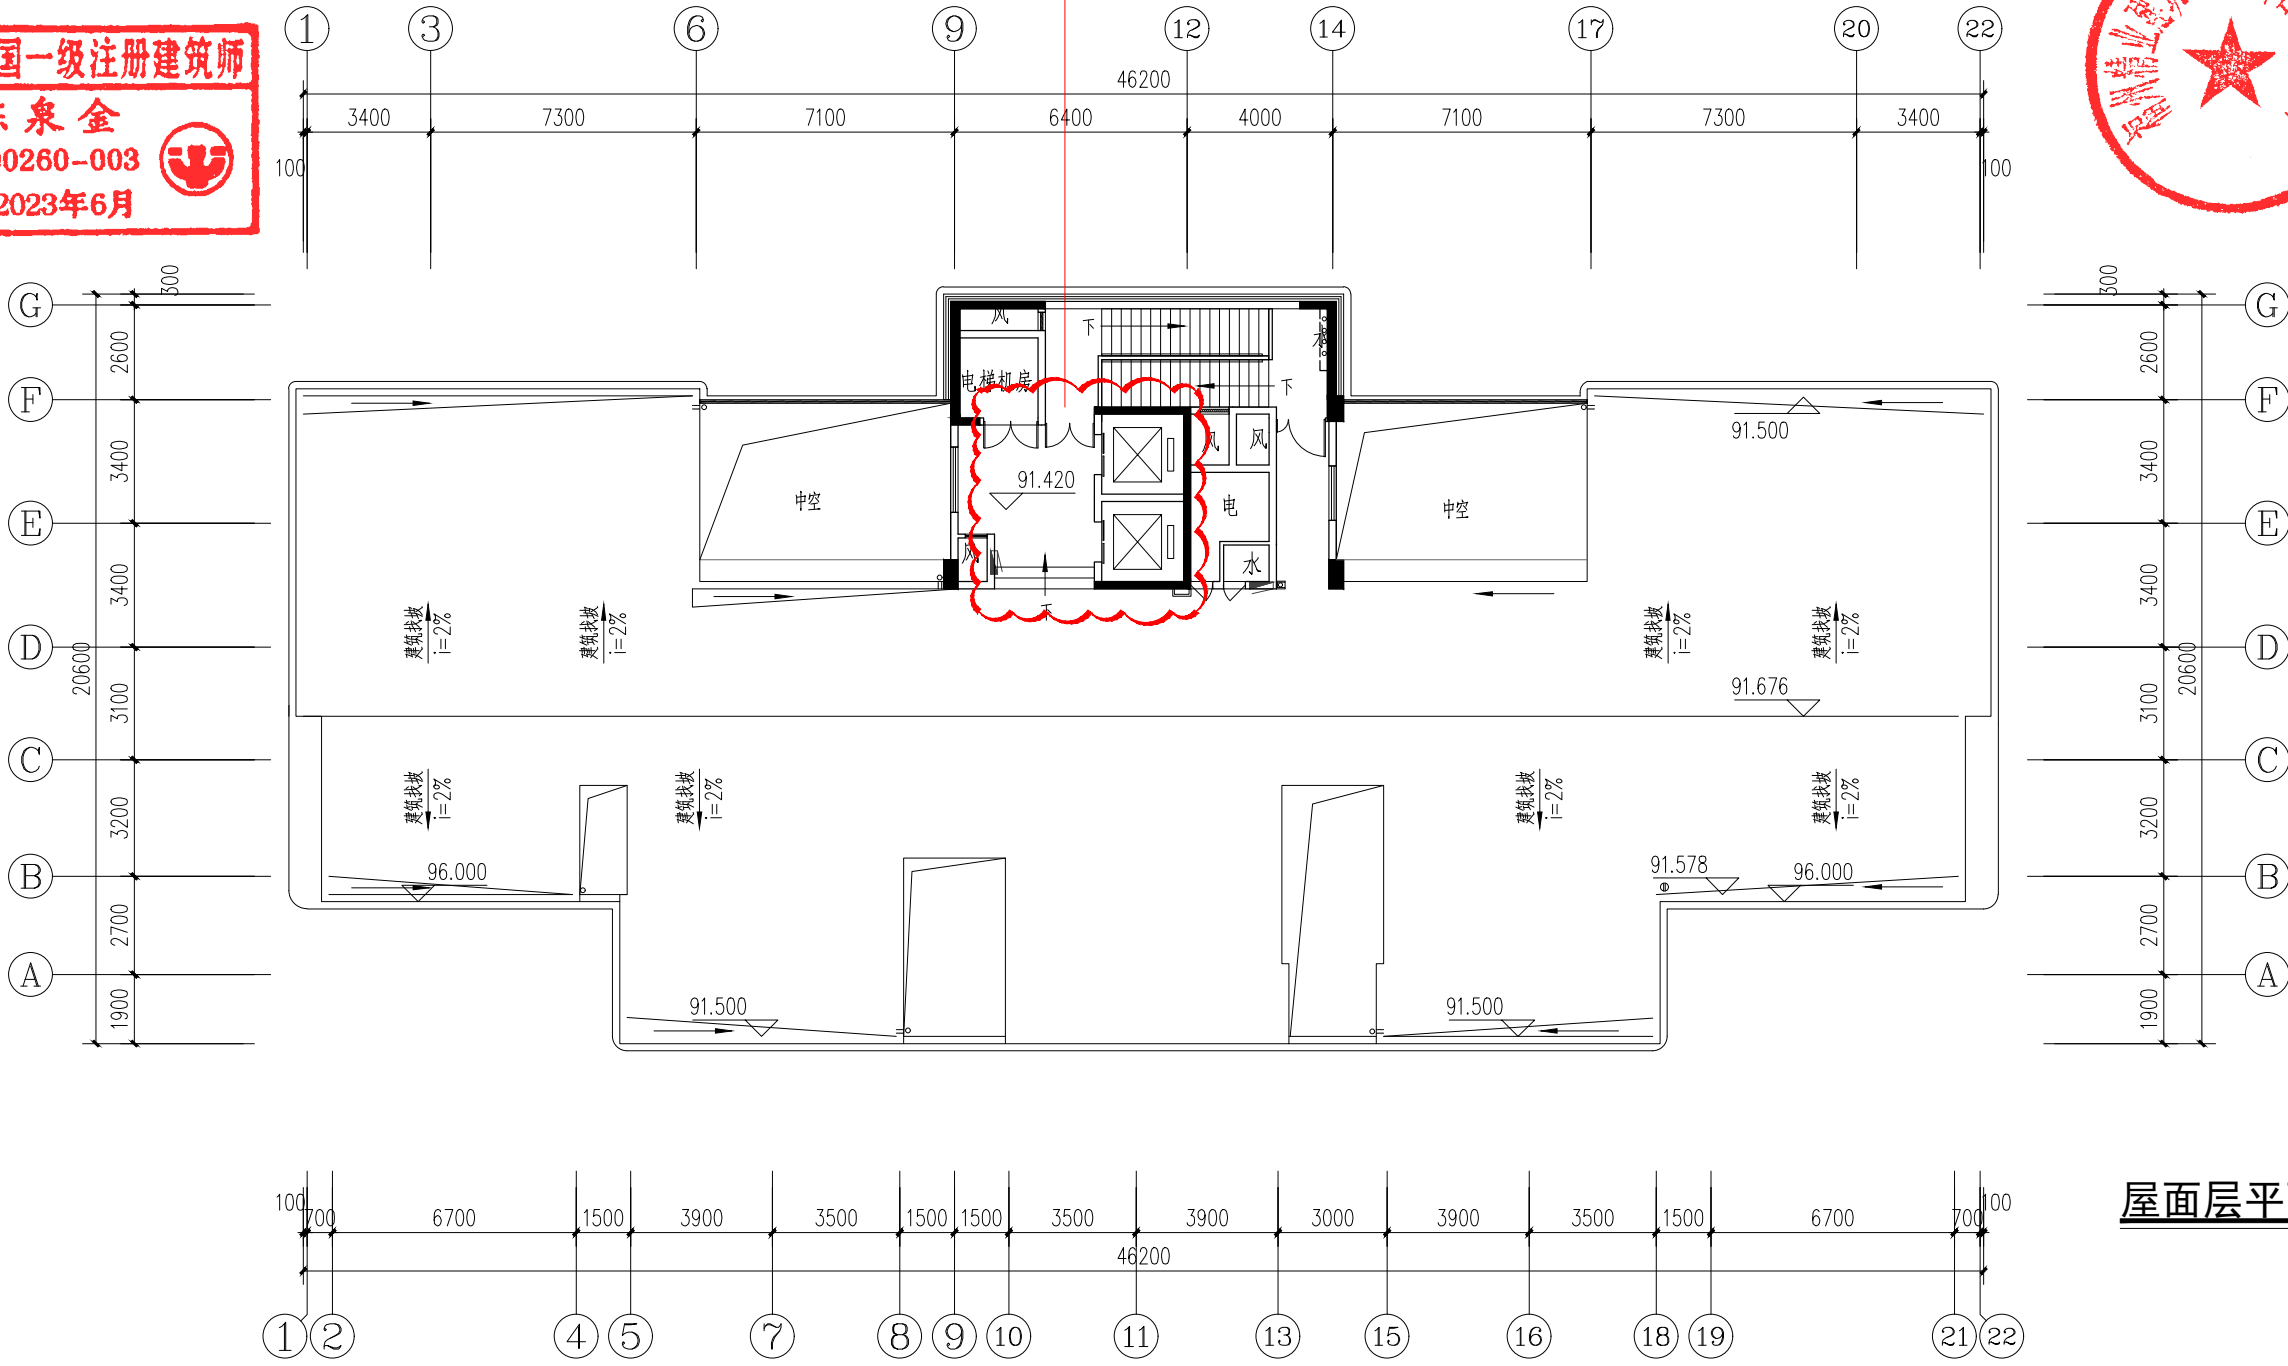

屋面层平面图

屋面层平面图变更后