

勘察设计一般变更记录单


项目名称	三明融侨观邸					
建设单位	三明融侨置业有限公司					
勘察或设计单位	厦门上城建筑设计有限公司					
变更原因及依据	根据现场实际测量发现，部分位置存在施工的误差、根据现场实际情况所做的过程变更等原因需对原住宅、商业、地下室局部做设计调整以满足要求。					
变更内容说明	1#楼：1、玻璃门 MLC3326b 所在的墙体向 1-C 轴移动 0.85m，大堂侧边局部墙体往内移 0.10m，1-11 轴处消火栓所在的墙体向外加厚 0.10m。 2#楼：大堂侧边墙体向 2-7 轴移动 0.10m，2-10 轴处消火栓所在的墙体加厚 0.10m。 3#楼：3-10 轴处消火栓所在的墙体向外加厚 0.10m。 5#楼：5-11 轴处消火栓所在的墙体向外加厚 0.10m。 1#、2#、3#、5#、7#楼屋面：电梯机房的防火门和室外钢梯调整至右侧。 8#楼：8-B~8-D 轴交 8-1~8-3 周处补充人防出地面楼梯，平时预制盖板封堵；柴油发电机房排风井墙体及百叶位置调整；开闭所局部增加砖墙（原开闭所空间变化为覆土空间）。 9#楼：首层 9-C 轴处砖墙往 9-B 轴平移 2.40m；9a-1 轴处局部砖墙地下室非机动车位出入口移动 0.10m 11#楼：一层 11-D 轴处玻璃门 MQ3834b 往外平移 0.10m，玻璃门 MQ5434b 往外平移 0.20m；二层 11-D 轴处玻璃窗 MQ3837 往外平移 0.10m，玻璃窗 MQ5416b 往外平移 0.20m；三层 11-B 轴处玻璃门 MQ5430b 往下平移 0.10m，扶梯南侧的上空区域封板，物业用房功能标注有误，实际为小区公共电梯厅。 12#楼：12A-1 轴处局部墙体及玻璃门窗往外移 0.13m；2B-1 轴处局部墙体及玻璃门窗往外移 0.10m。					
更改专业 (在□打√)	建筑专业 是□ 否□	结构专业 是□ 否□	给排水专业 是□ 否□	电气专业 是□ 否□	暖通专业 是□ 否□	勘察专业 是□ 否□
专业负责人 签字						

勘察或设计 单位声明	1.以上变更内容不属重大变更范围，属一般变更； 2.除上述变更内容外，本次送审的图纸与原审查通过的图纸内容一致。	
提示	此次变更涉及工程造价（ ☐ 变化较大， ☐ 变化不大），请建设单位进一步确认。	
建设单位公章 年月日	勘察或设计单位公章 年月日	项目负责人签字： 注册章：


注：1.本表由勘察设计单位填写，一式二份，建设单位、勘察设计单位各一份；
2.对变更类别存有疑问或难以判定的，勘察设计单位应与建设单位一并征求原审查机构意见；
3.变更内容说明栏应按条目说明变更内容、部位、所涉专业及图号，页面不够可另附页。

工程名称	三明融侨观邸				子项名称	1#、2#、3#、5#楼	专业	建施	审定	审核	工程负责人	专业负责人	专业负责人助理
更改原因	根据实测和建设单位要求修改				校对	李永成	更改人	李永成	设计变更	发起专业	备注		

1、1#楼一层平面图中，玻璃门MLC3326b所在的墙体向1-C轴移动0.85m，大堂侧边局部墙体往内移0.10m，1-11轴处消火栓所在的墙体向外加厚0.10m。详下图云线圈注所示。

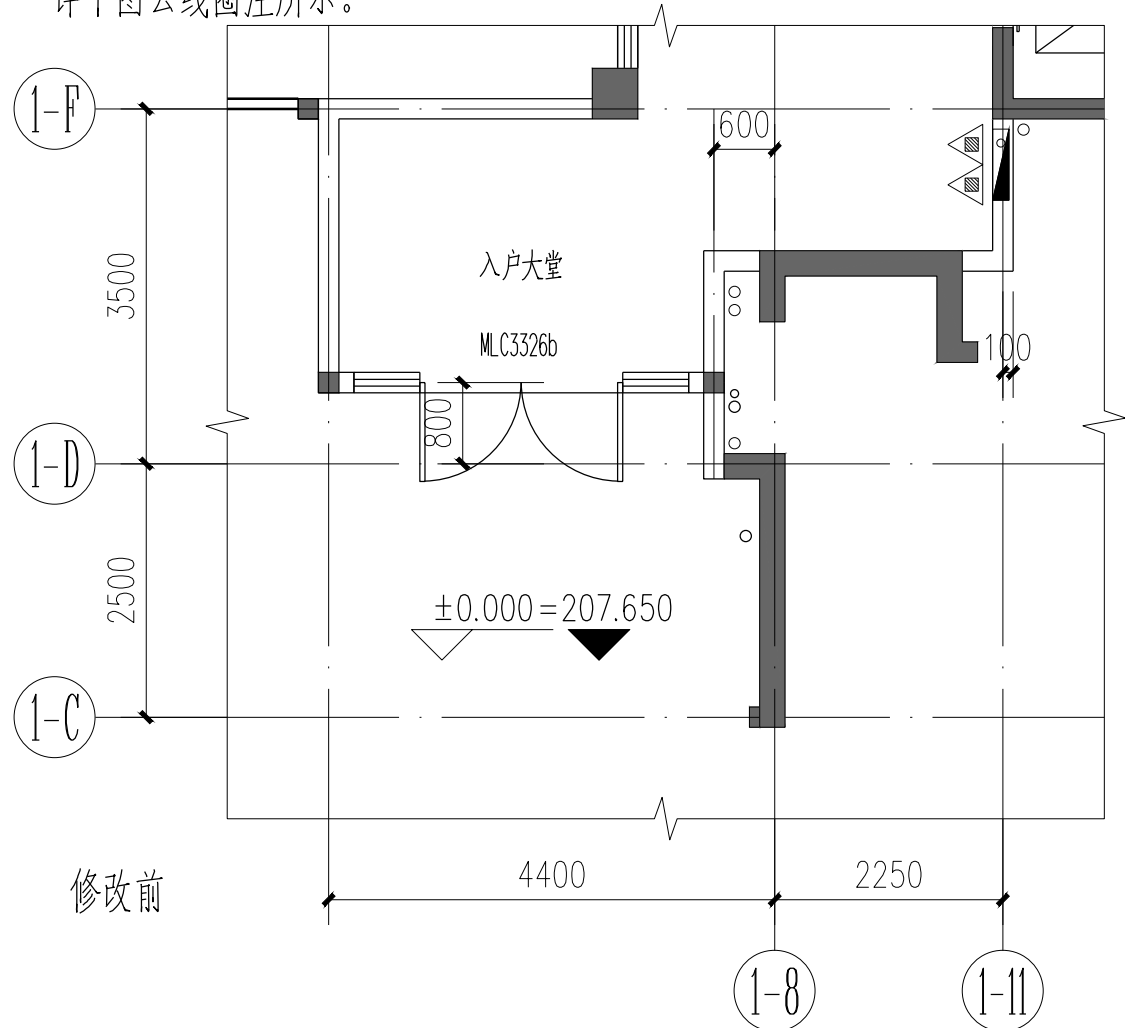


1#楼 一层局部平面图 1:100

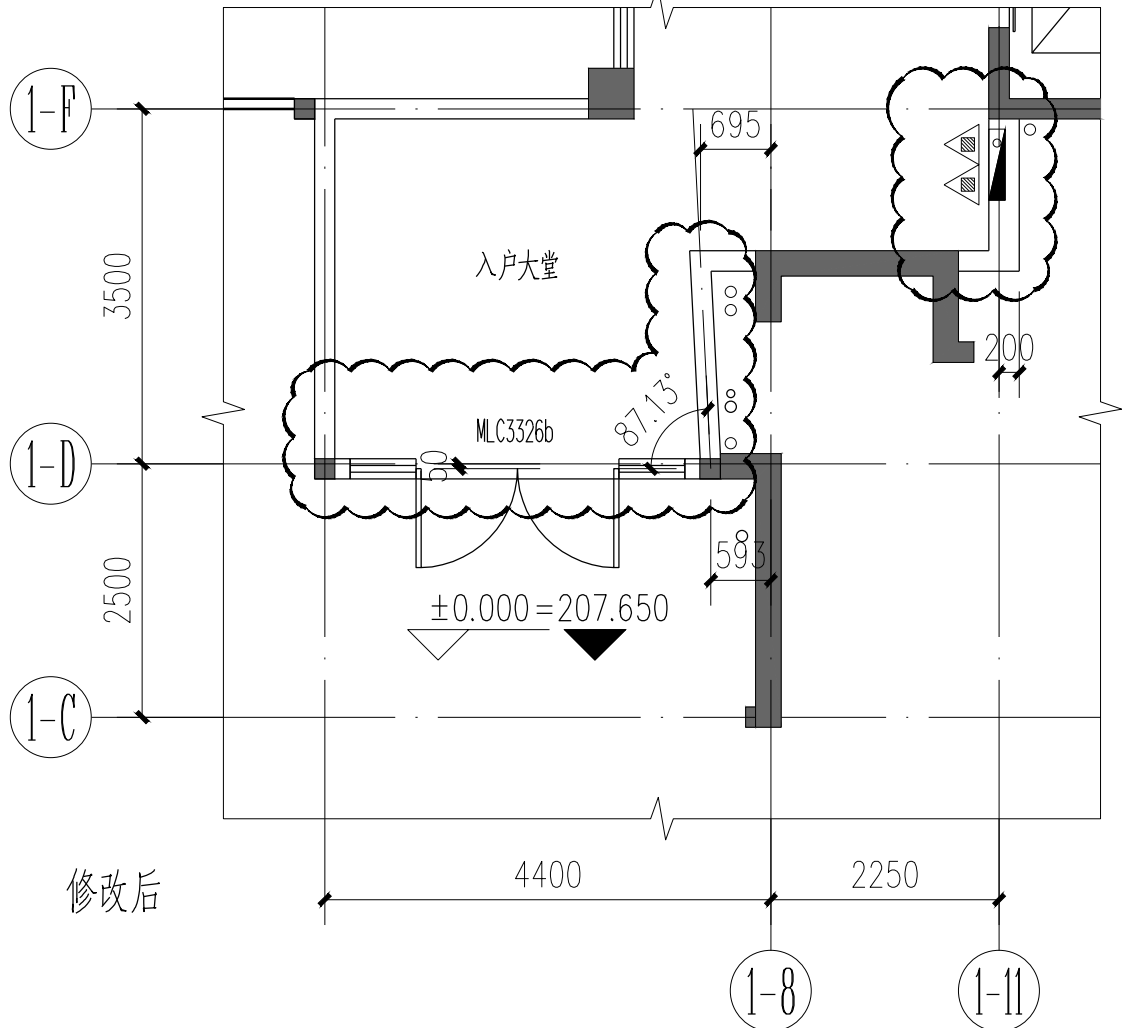


1#楼 一层局部平面图 1:100

2、2#楼一层平面图中，大堂侧边墙体向2-7轴移动0.10m，2-10轴处消火栓所在的墙体加厚0.10m，详下图云线圈注所示。

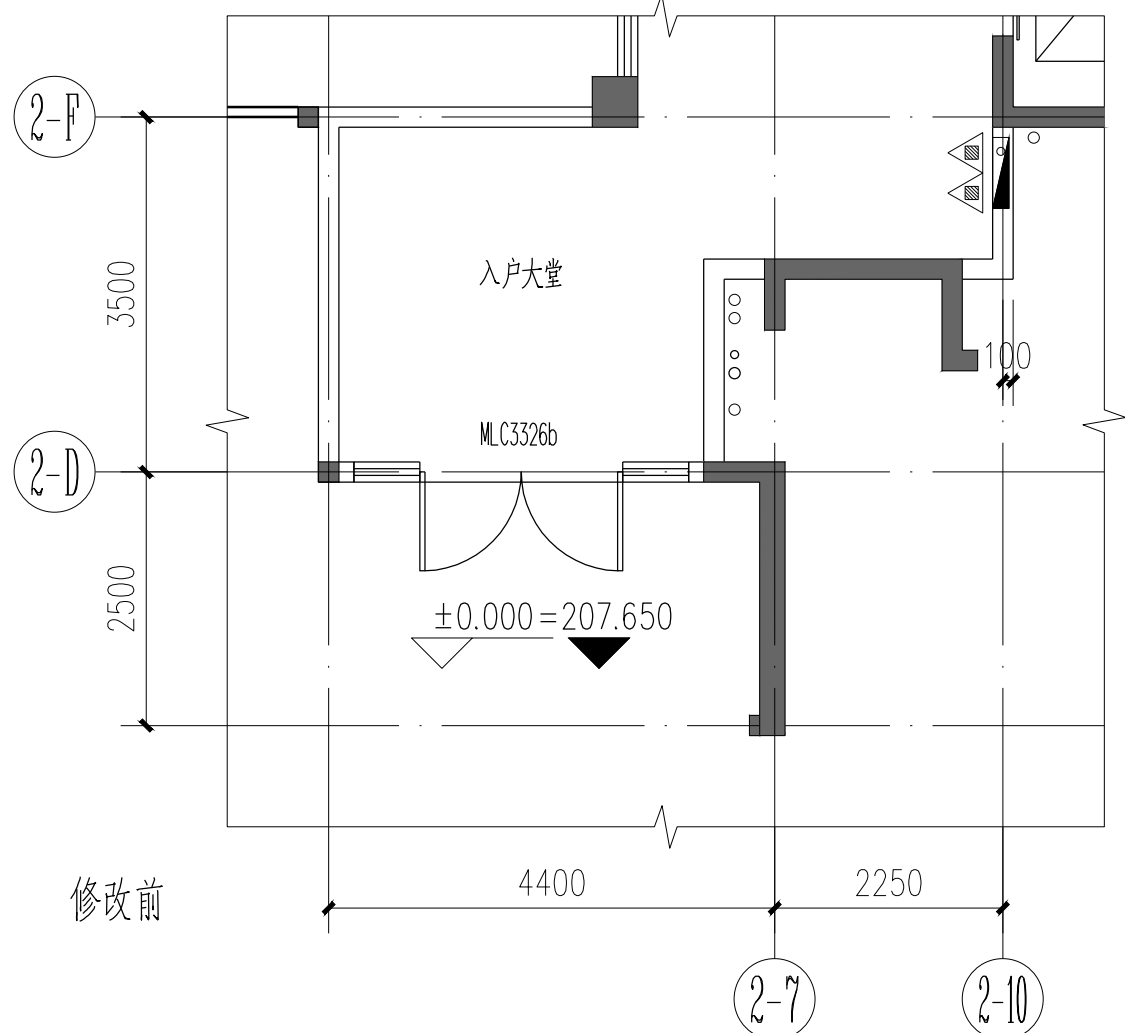


2#楼 一层局部平面图 1:100

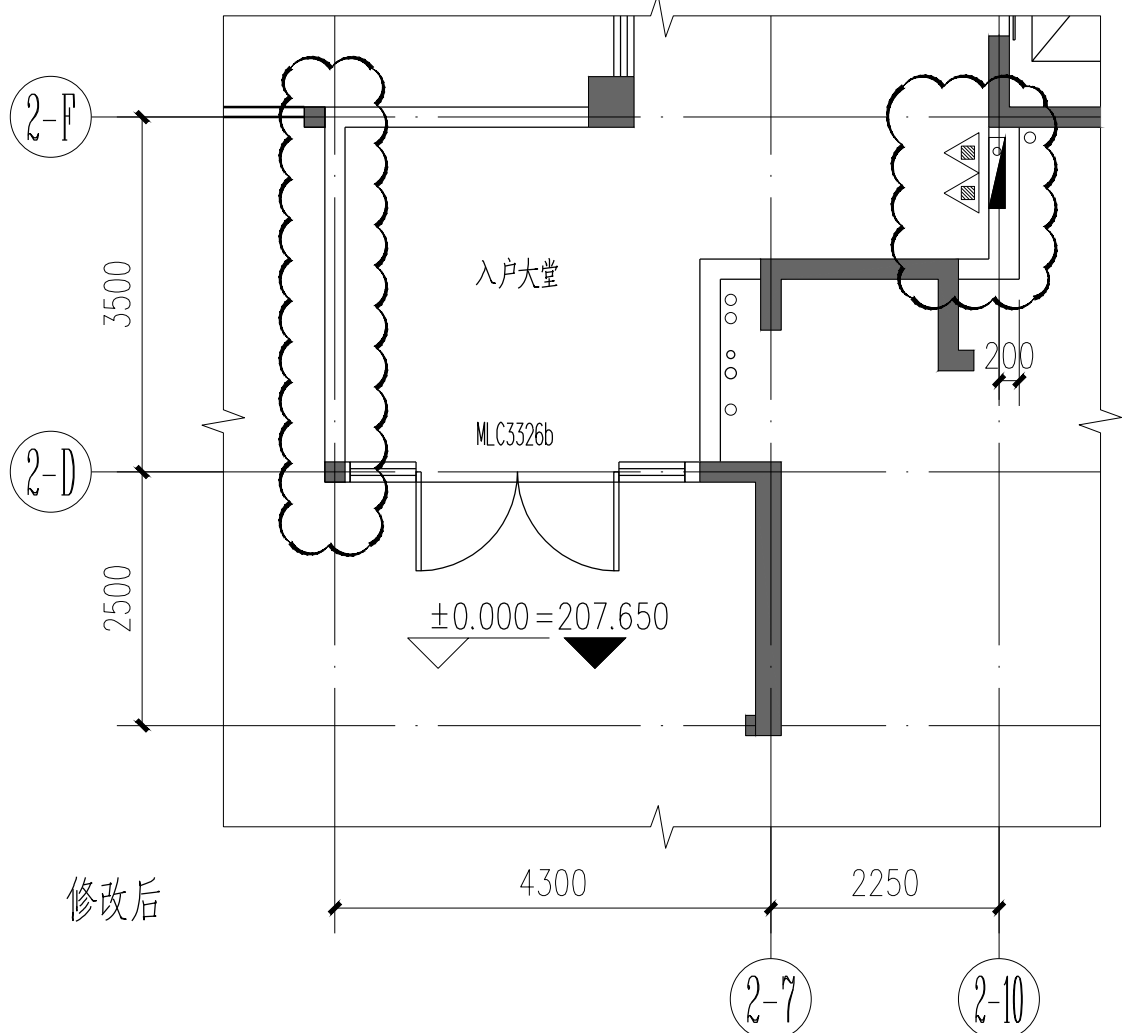


2#楼 一层局部平面图 1:100

3、3#、5#楼一层平面图中，3-10轴、5-11轴处消火栓所在的墙体加厚0.1m，详下图云线圈注所示。

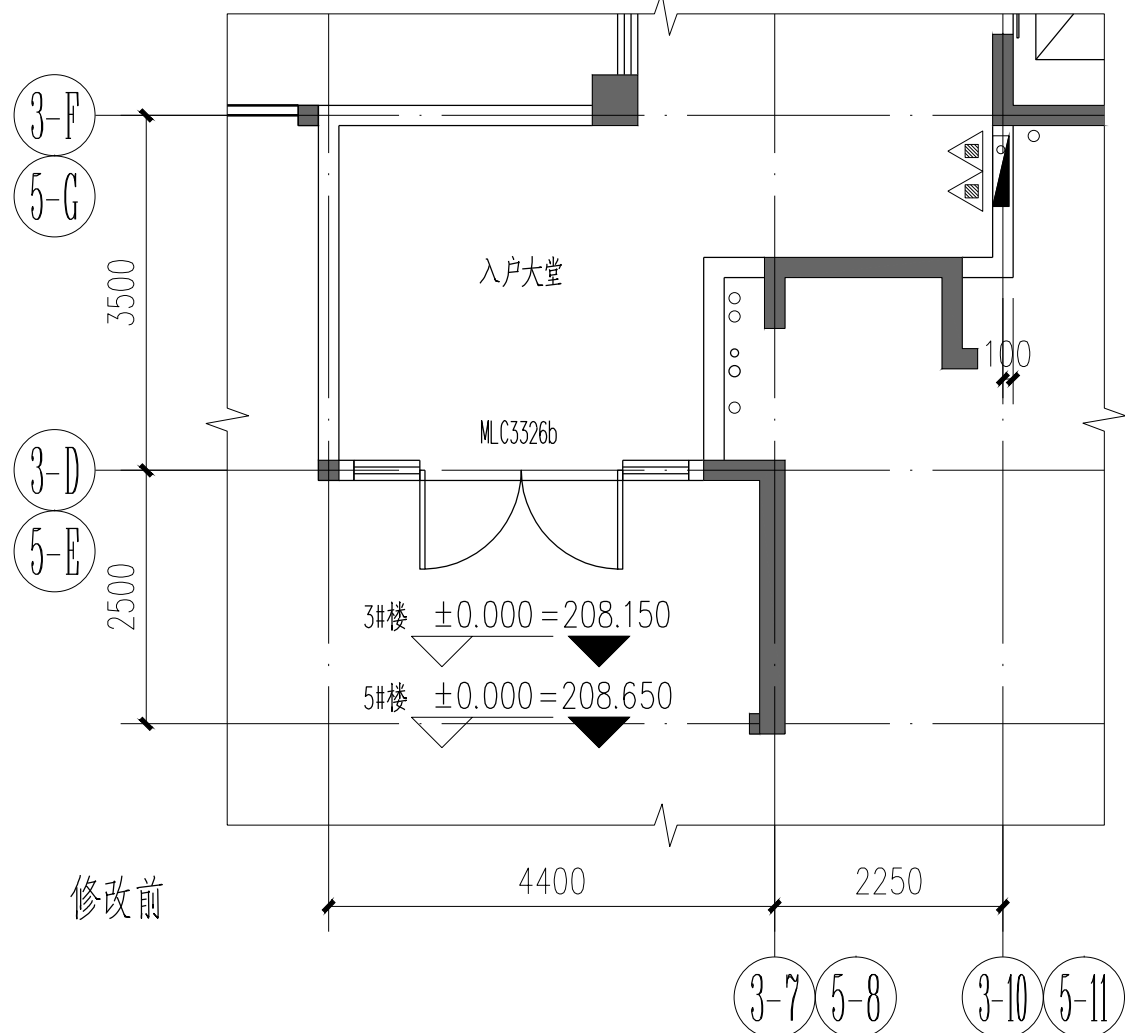


3#、5#楼 一层局部平面图 1:100

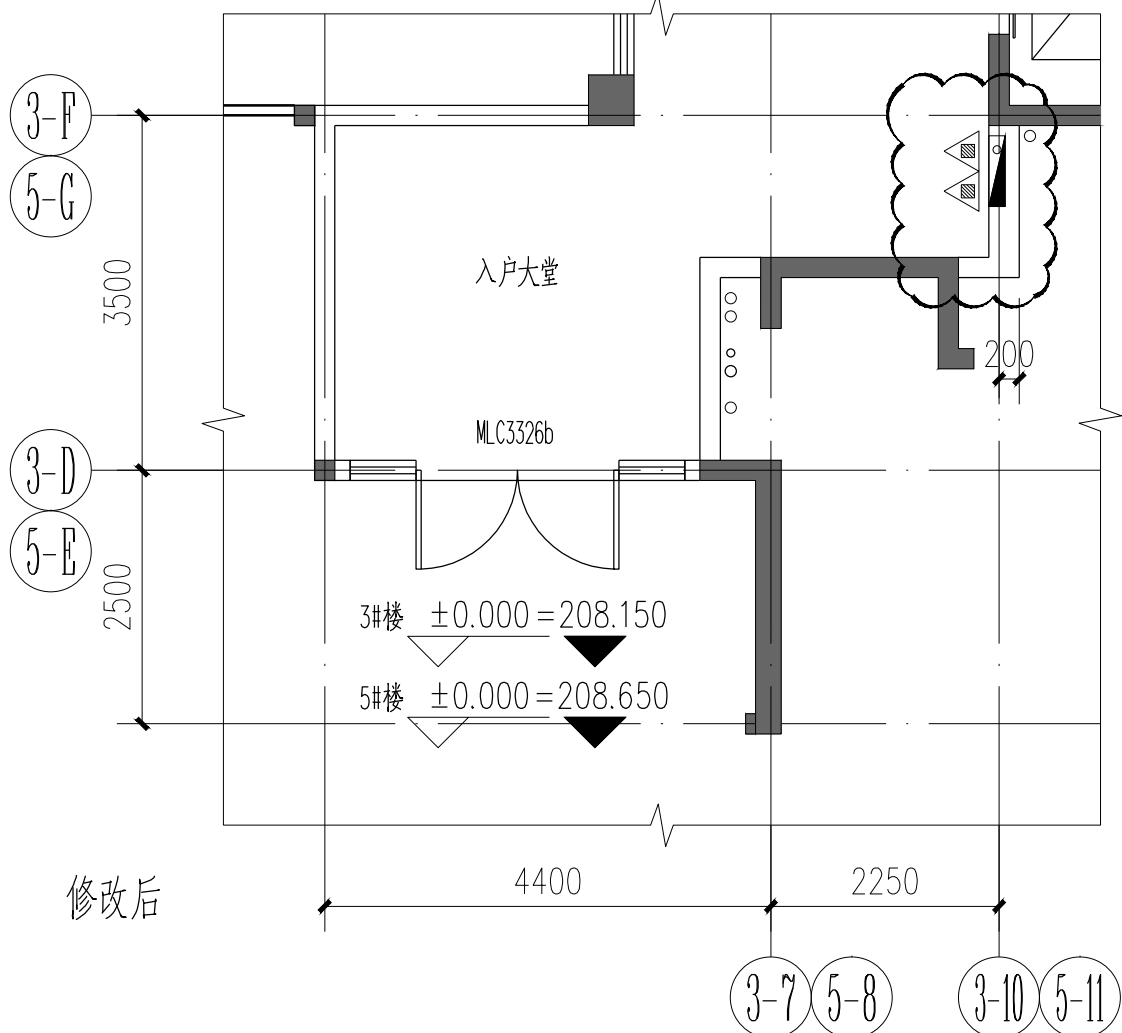


3#、5#楼 一层局部平面图 1:100

工程名称	三明融侨观邸	工程编号	3504022008260101	会签栏	建筑	结构	给排水	电气	暖通
更改原因	根据实测和建设单位要求修改	子项名称	1#、2#、3#、5#、7#楼	专业	建施	审定	审核	设计变更发起专业	专业负责人助理
				校对	李永成	更改人	李永成	备注	


4、1#、2#、3#、5#、7#楼屋面层平面图中，电梯机房的防火门和室外钢梯调整至右侧，详下图云线圈注所示。

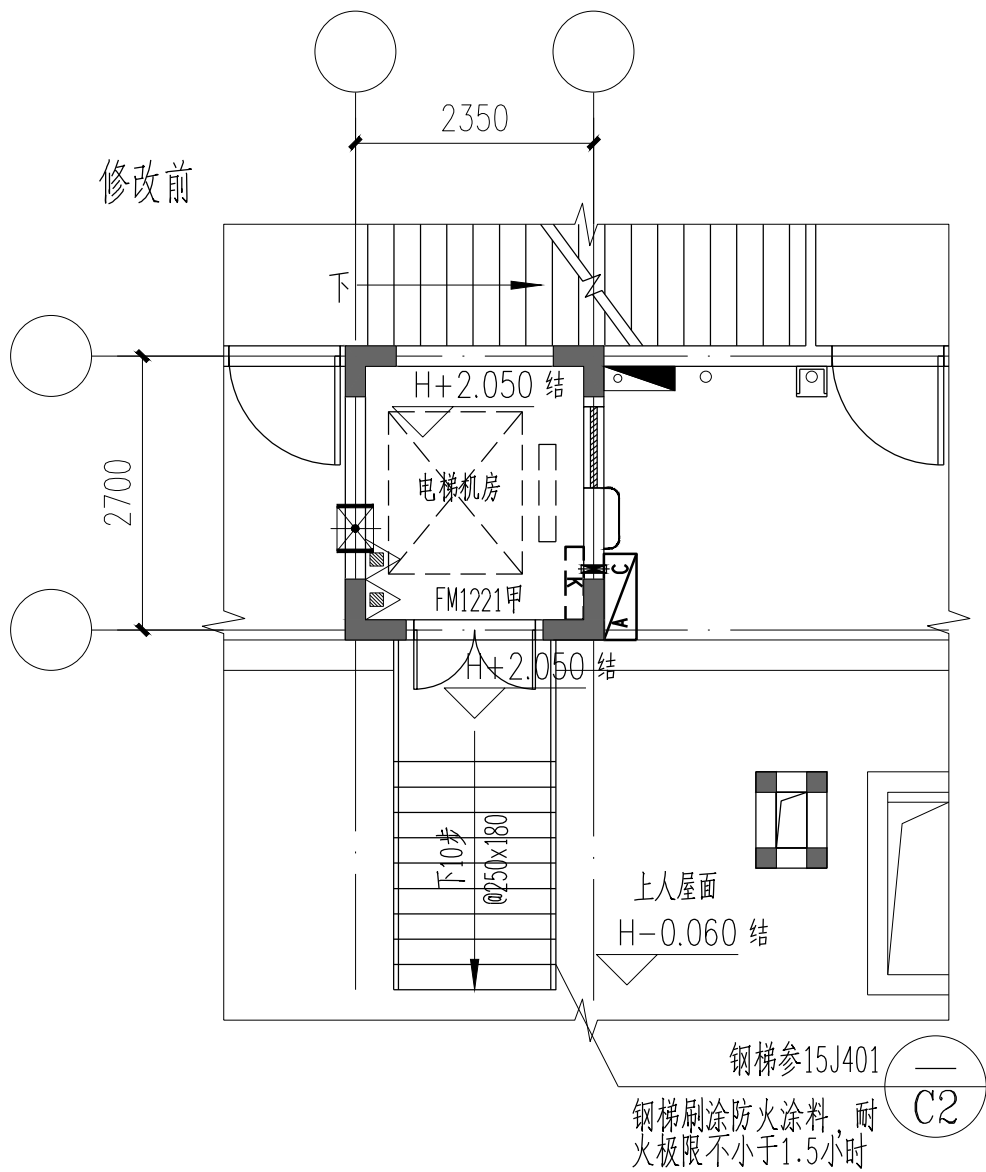

1#、2#、3#、5#、7#楼 一层局部平面图

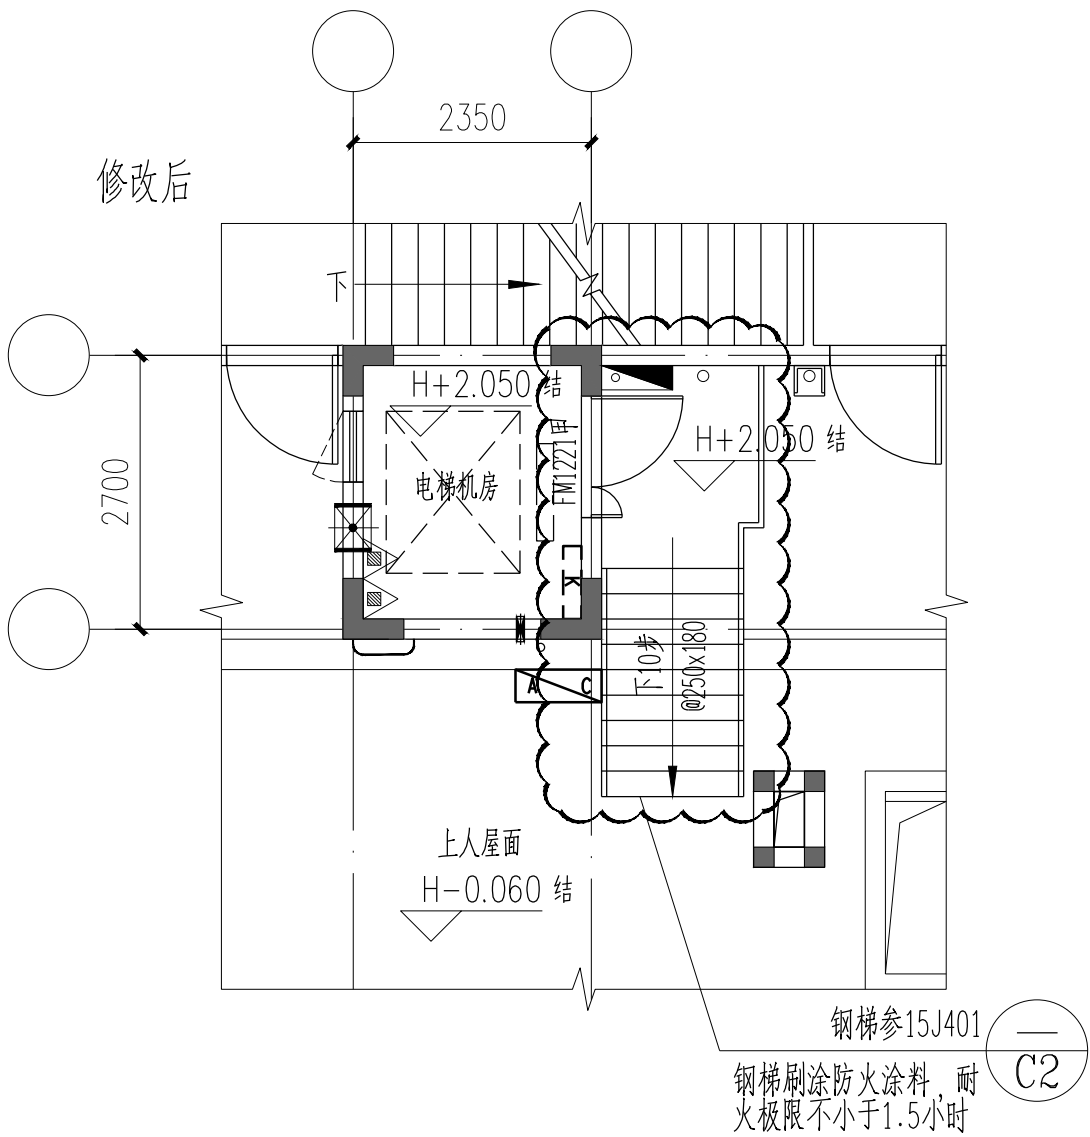


1#、7#楼 一层局部平面图

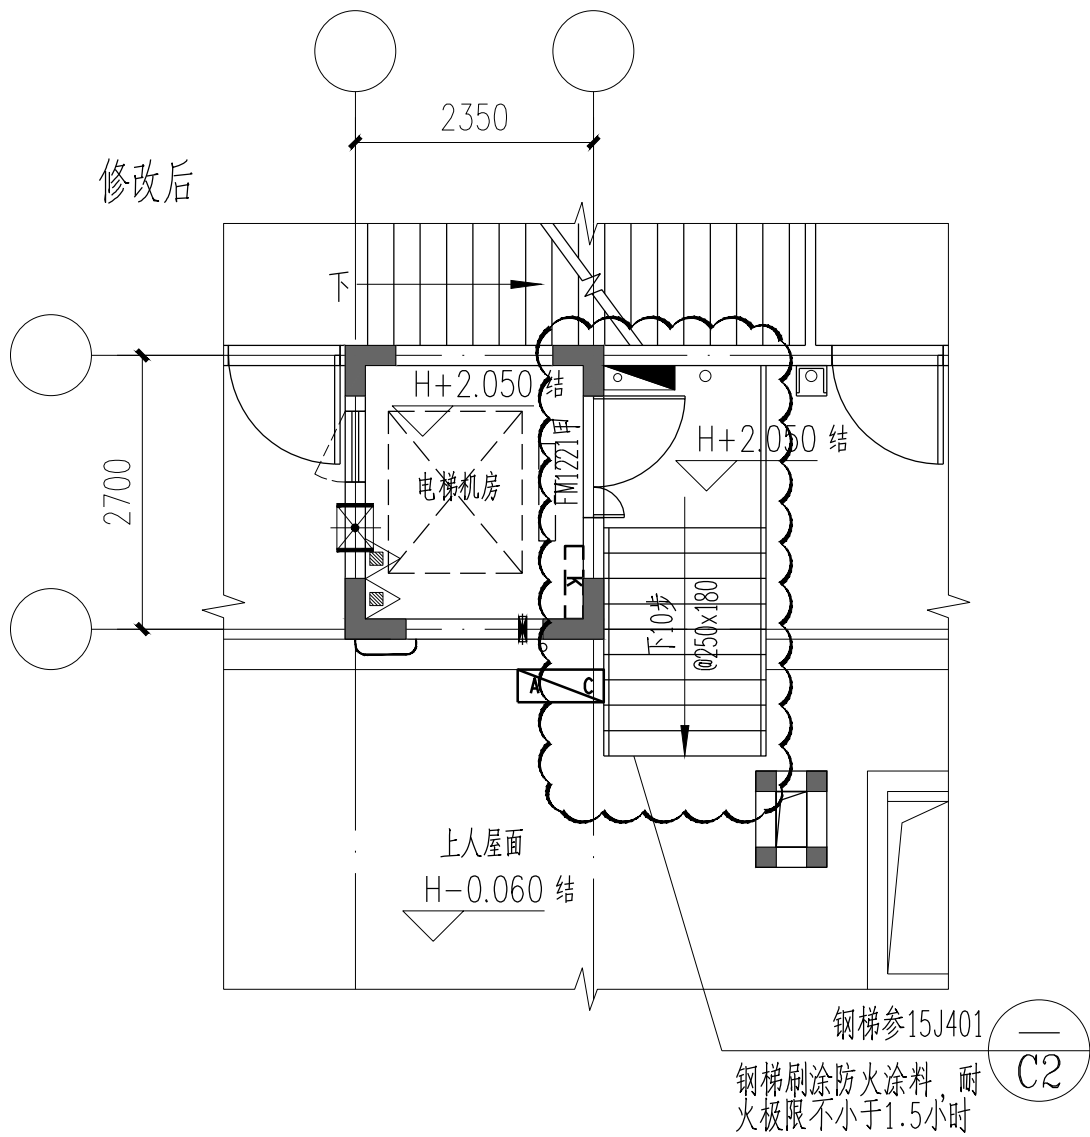


2#、3#、5#楼 一层局部平面图

5、8#楼一层平面图中，8-B~8-D轴交8-1~8-3周处补充人防出地面楼梯，平时预制盖板封堵，详下图云线圈注所示。

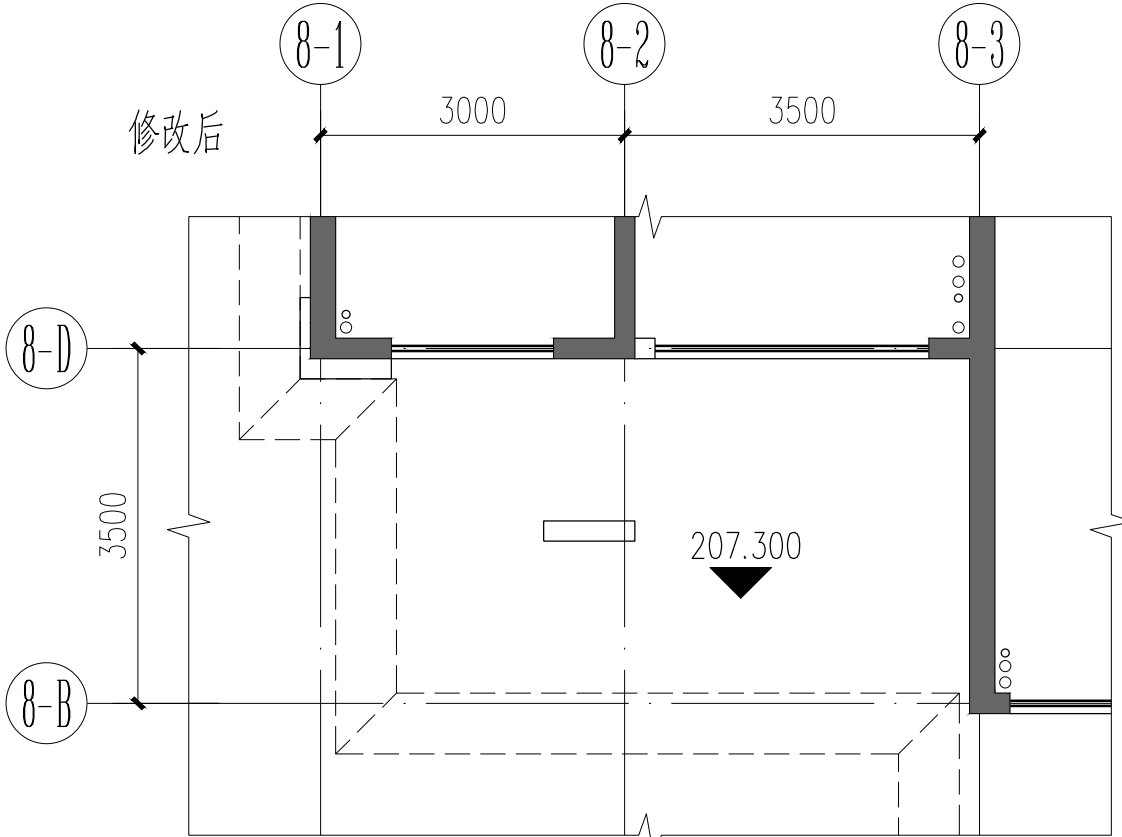


8#楼 一层局部平面图

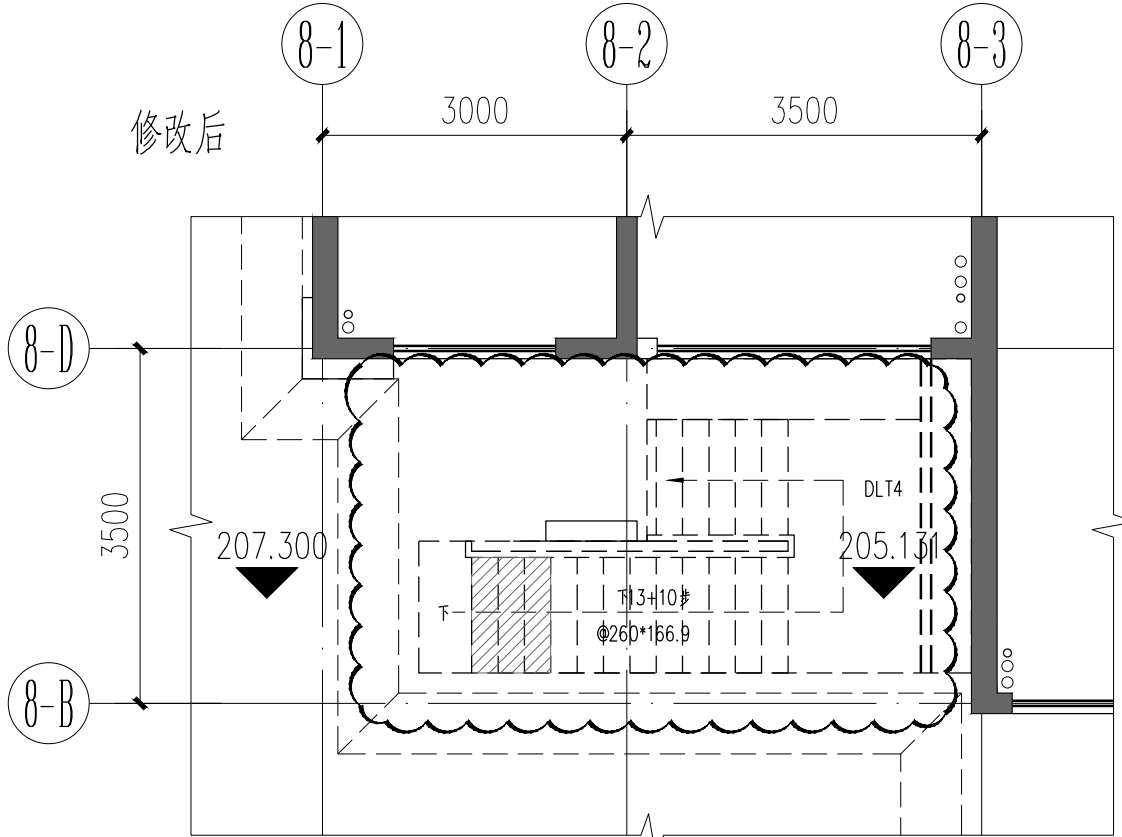


8#楼 一层局部平面图

工程名称	三明融侨观邸			工程编号	3504022008260101			会签栏	建筑	结构	给排水	电气	暖通
更改原因	根据实测和建设单位要求修改			子项名称	8#楼	专业	建施	审定	审核	设计变更 发起专业	备注		
								校对 人	更改 人				

5、8#楼标高-5.500平面图中，开闭所局部增加砖墙，（原开闭所空间变化为覆土空间），详下图云线圈注所示。


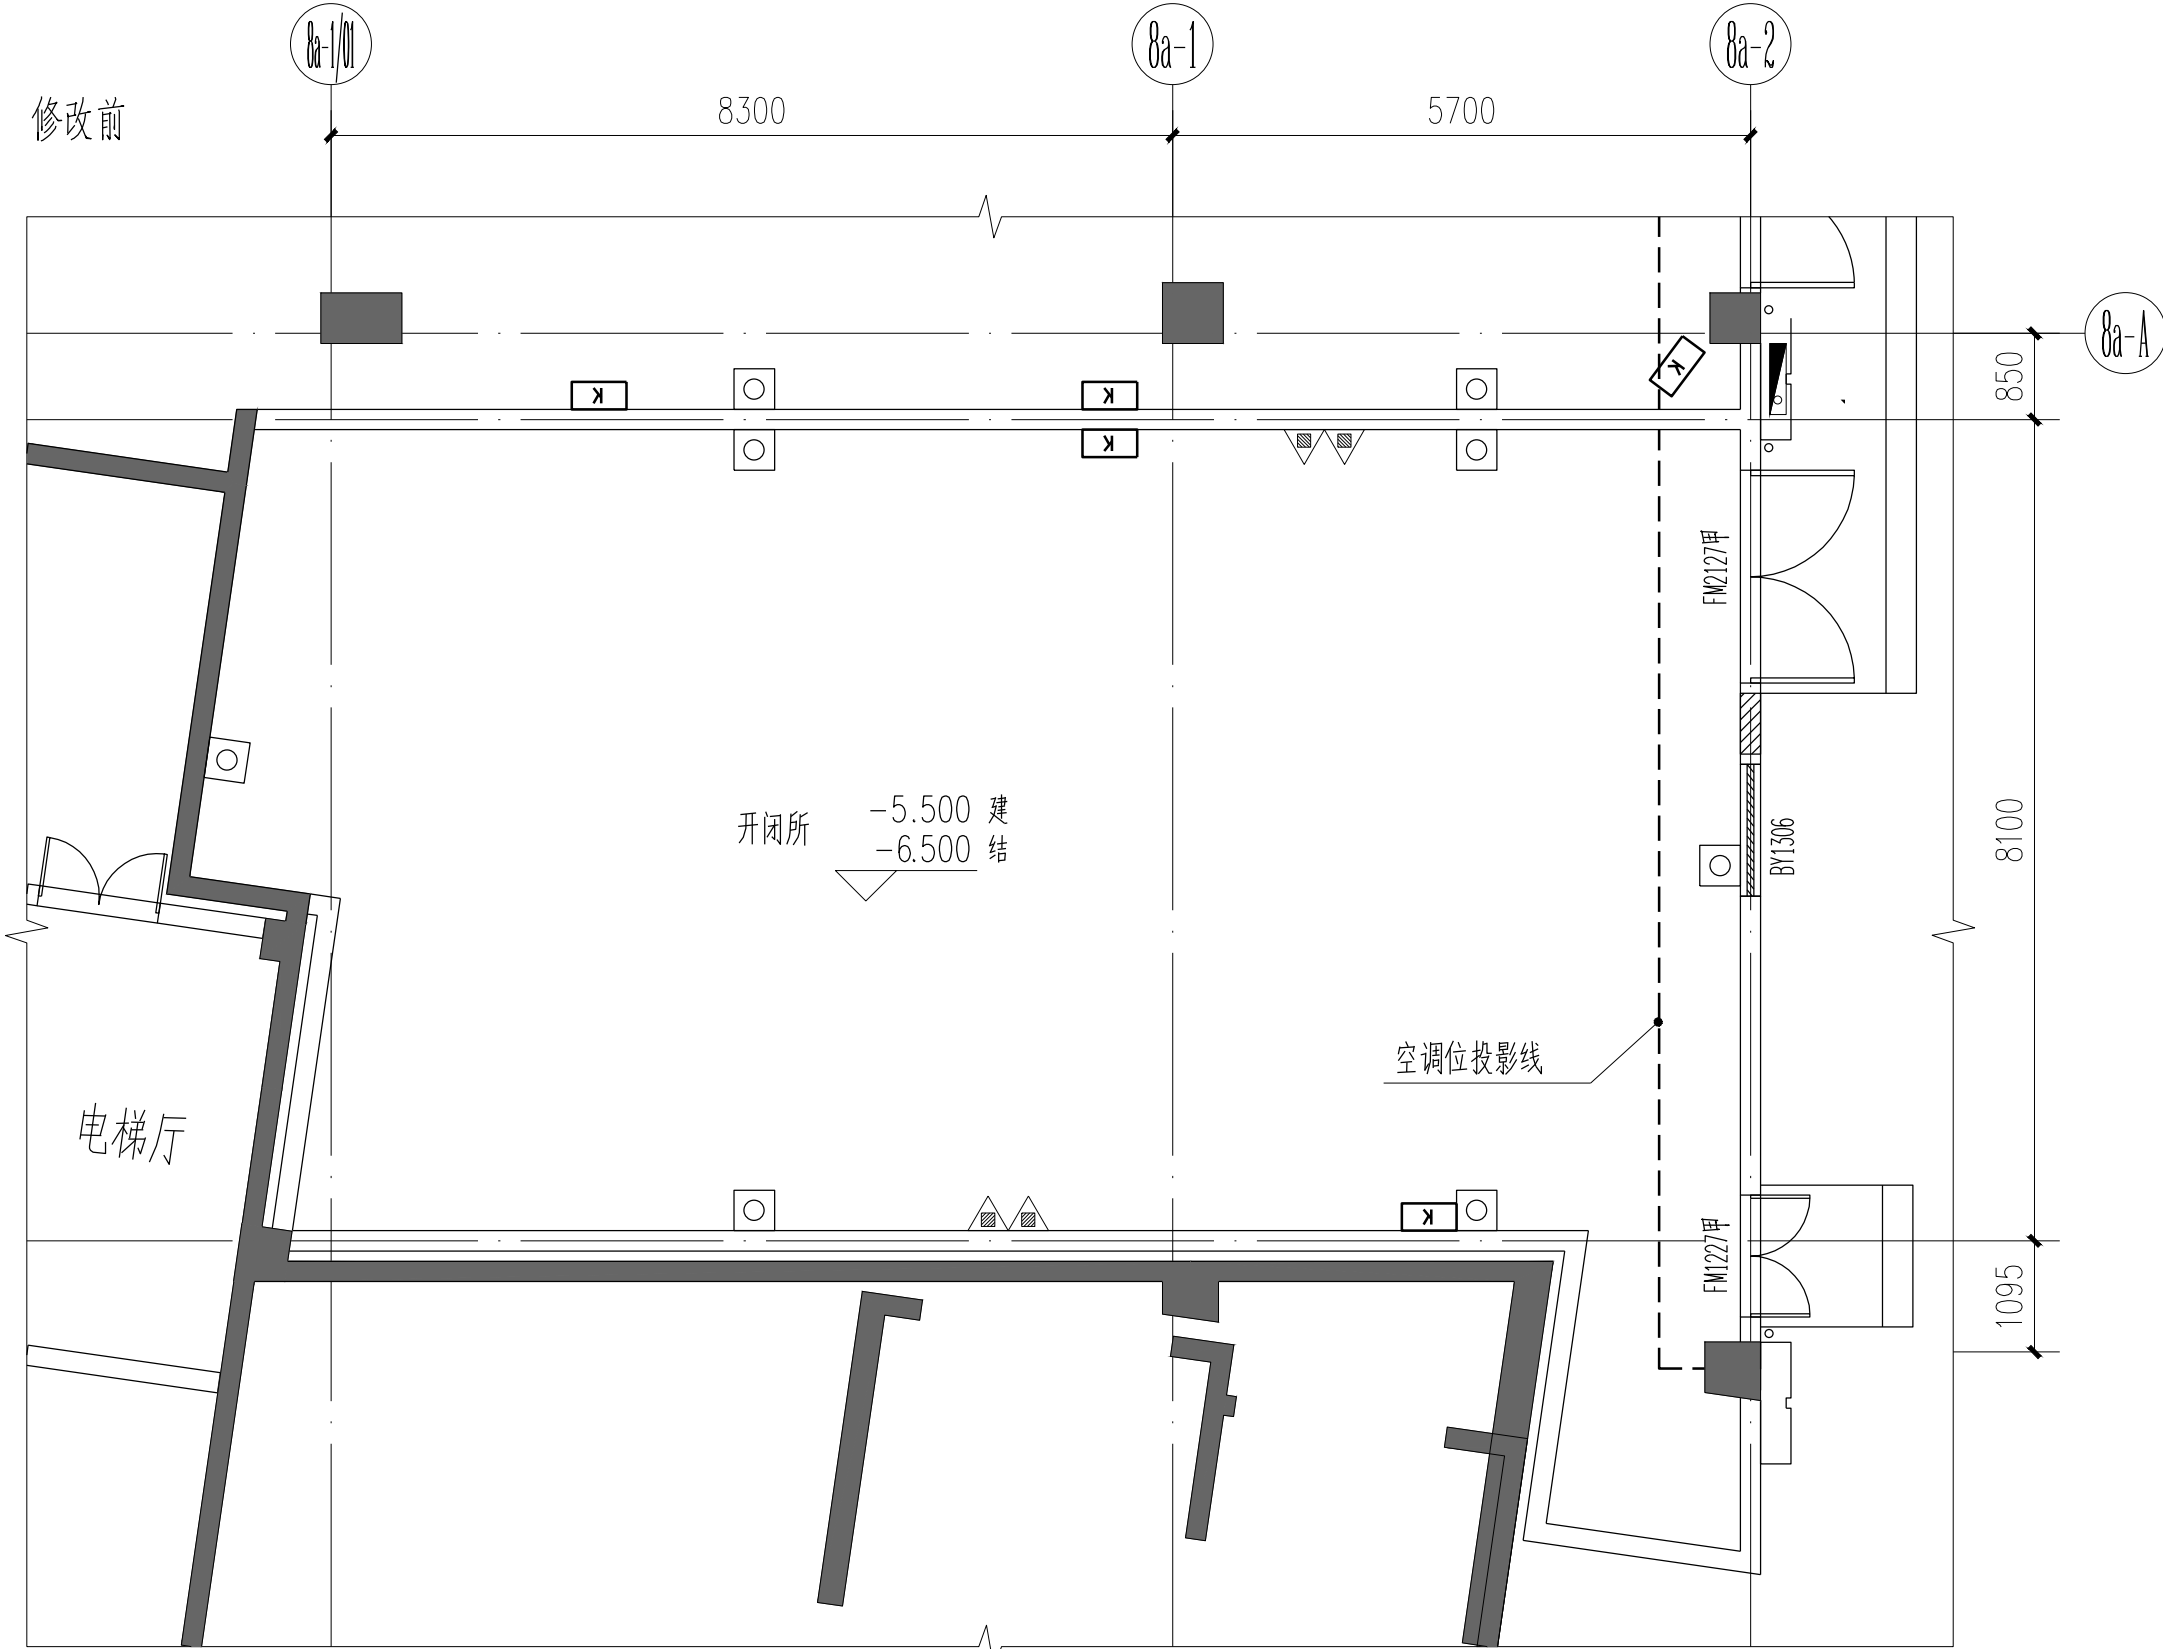


8#楼 标高-5. 500局部平面图 1:100

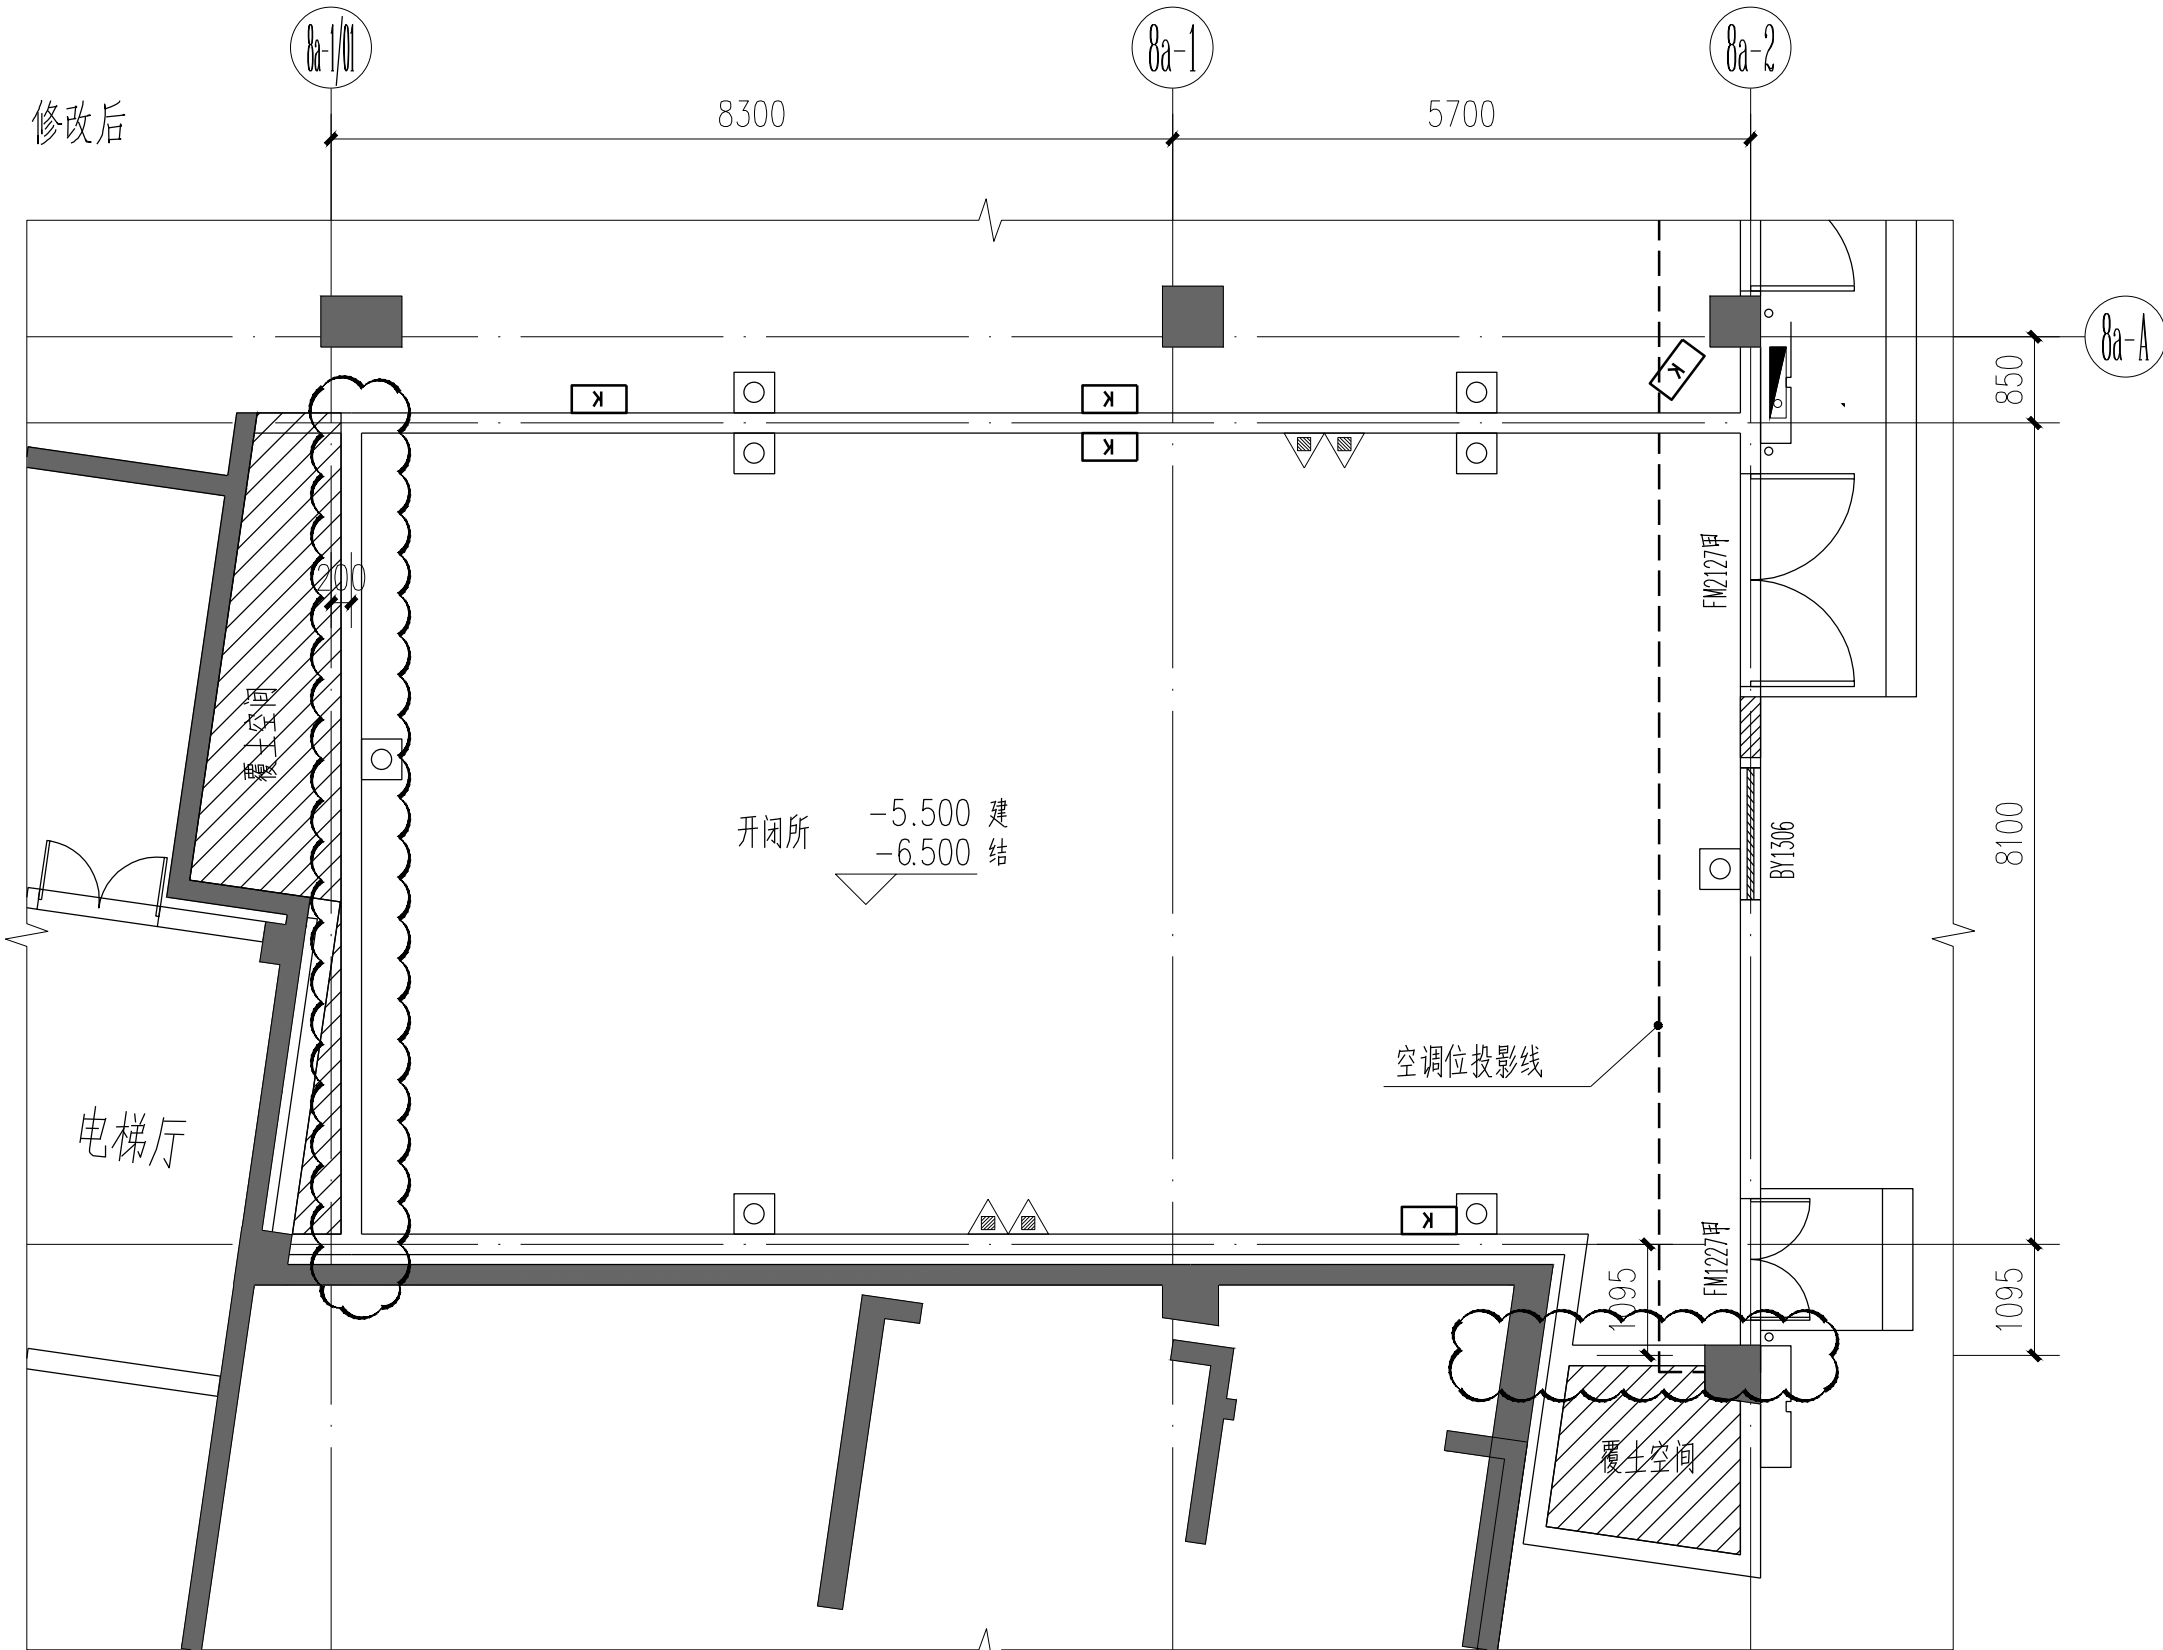

8#楼 标高-5. 500局部平面图 1:100


工程名称	三明融侨观邸	子项名称	9#楼	专业	建施	审定	审核	给排水	电气	暖通
更改原因	根据实测和建设单位要求修改					校对	更改人	设计变更 发起专业	备注	

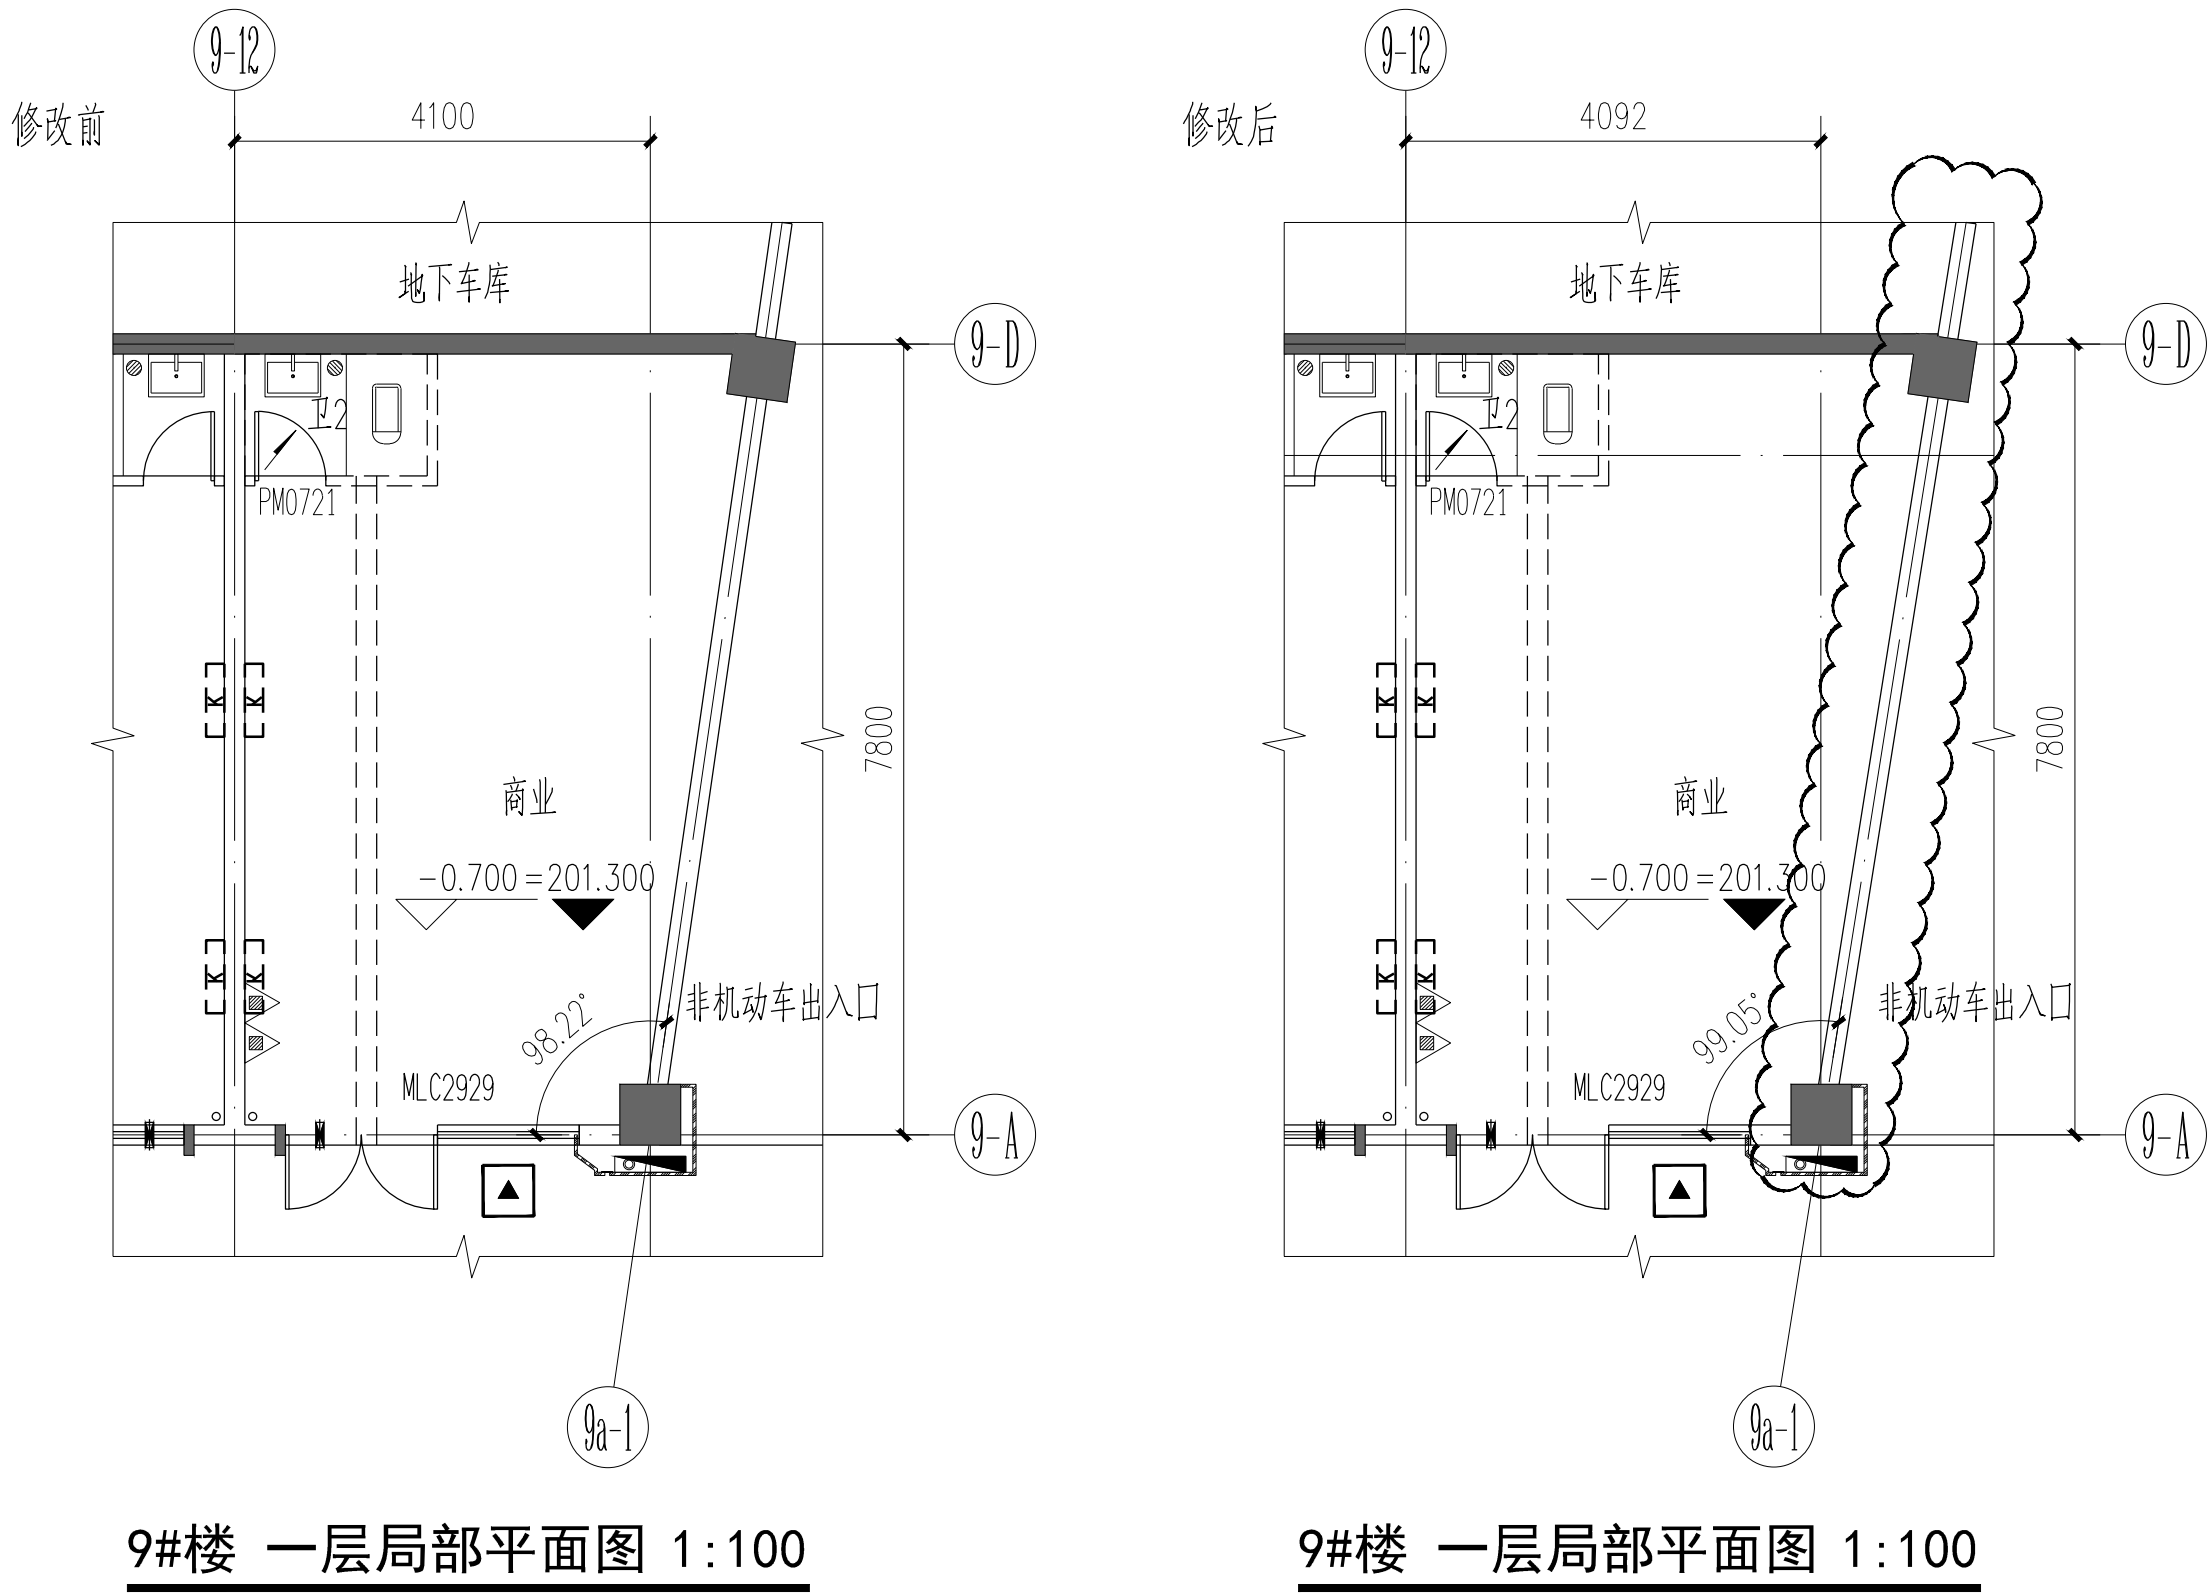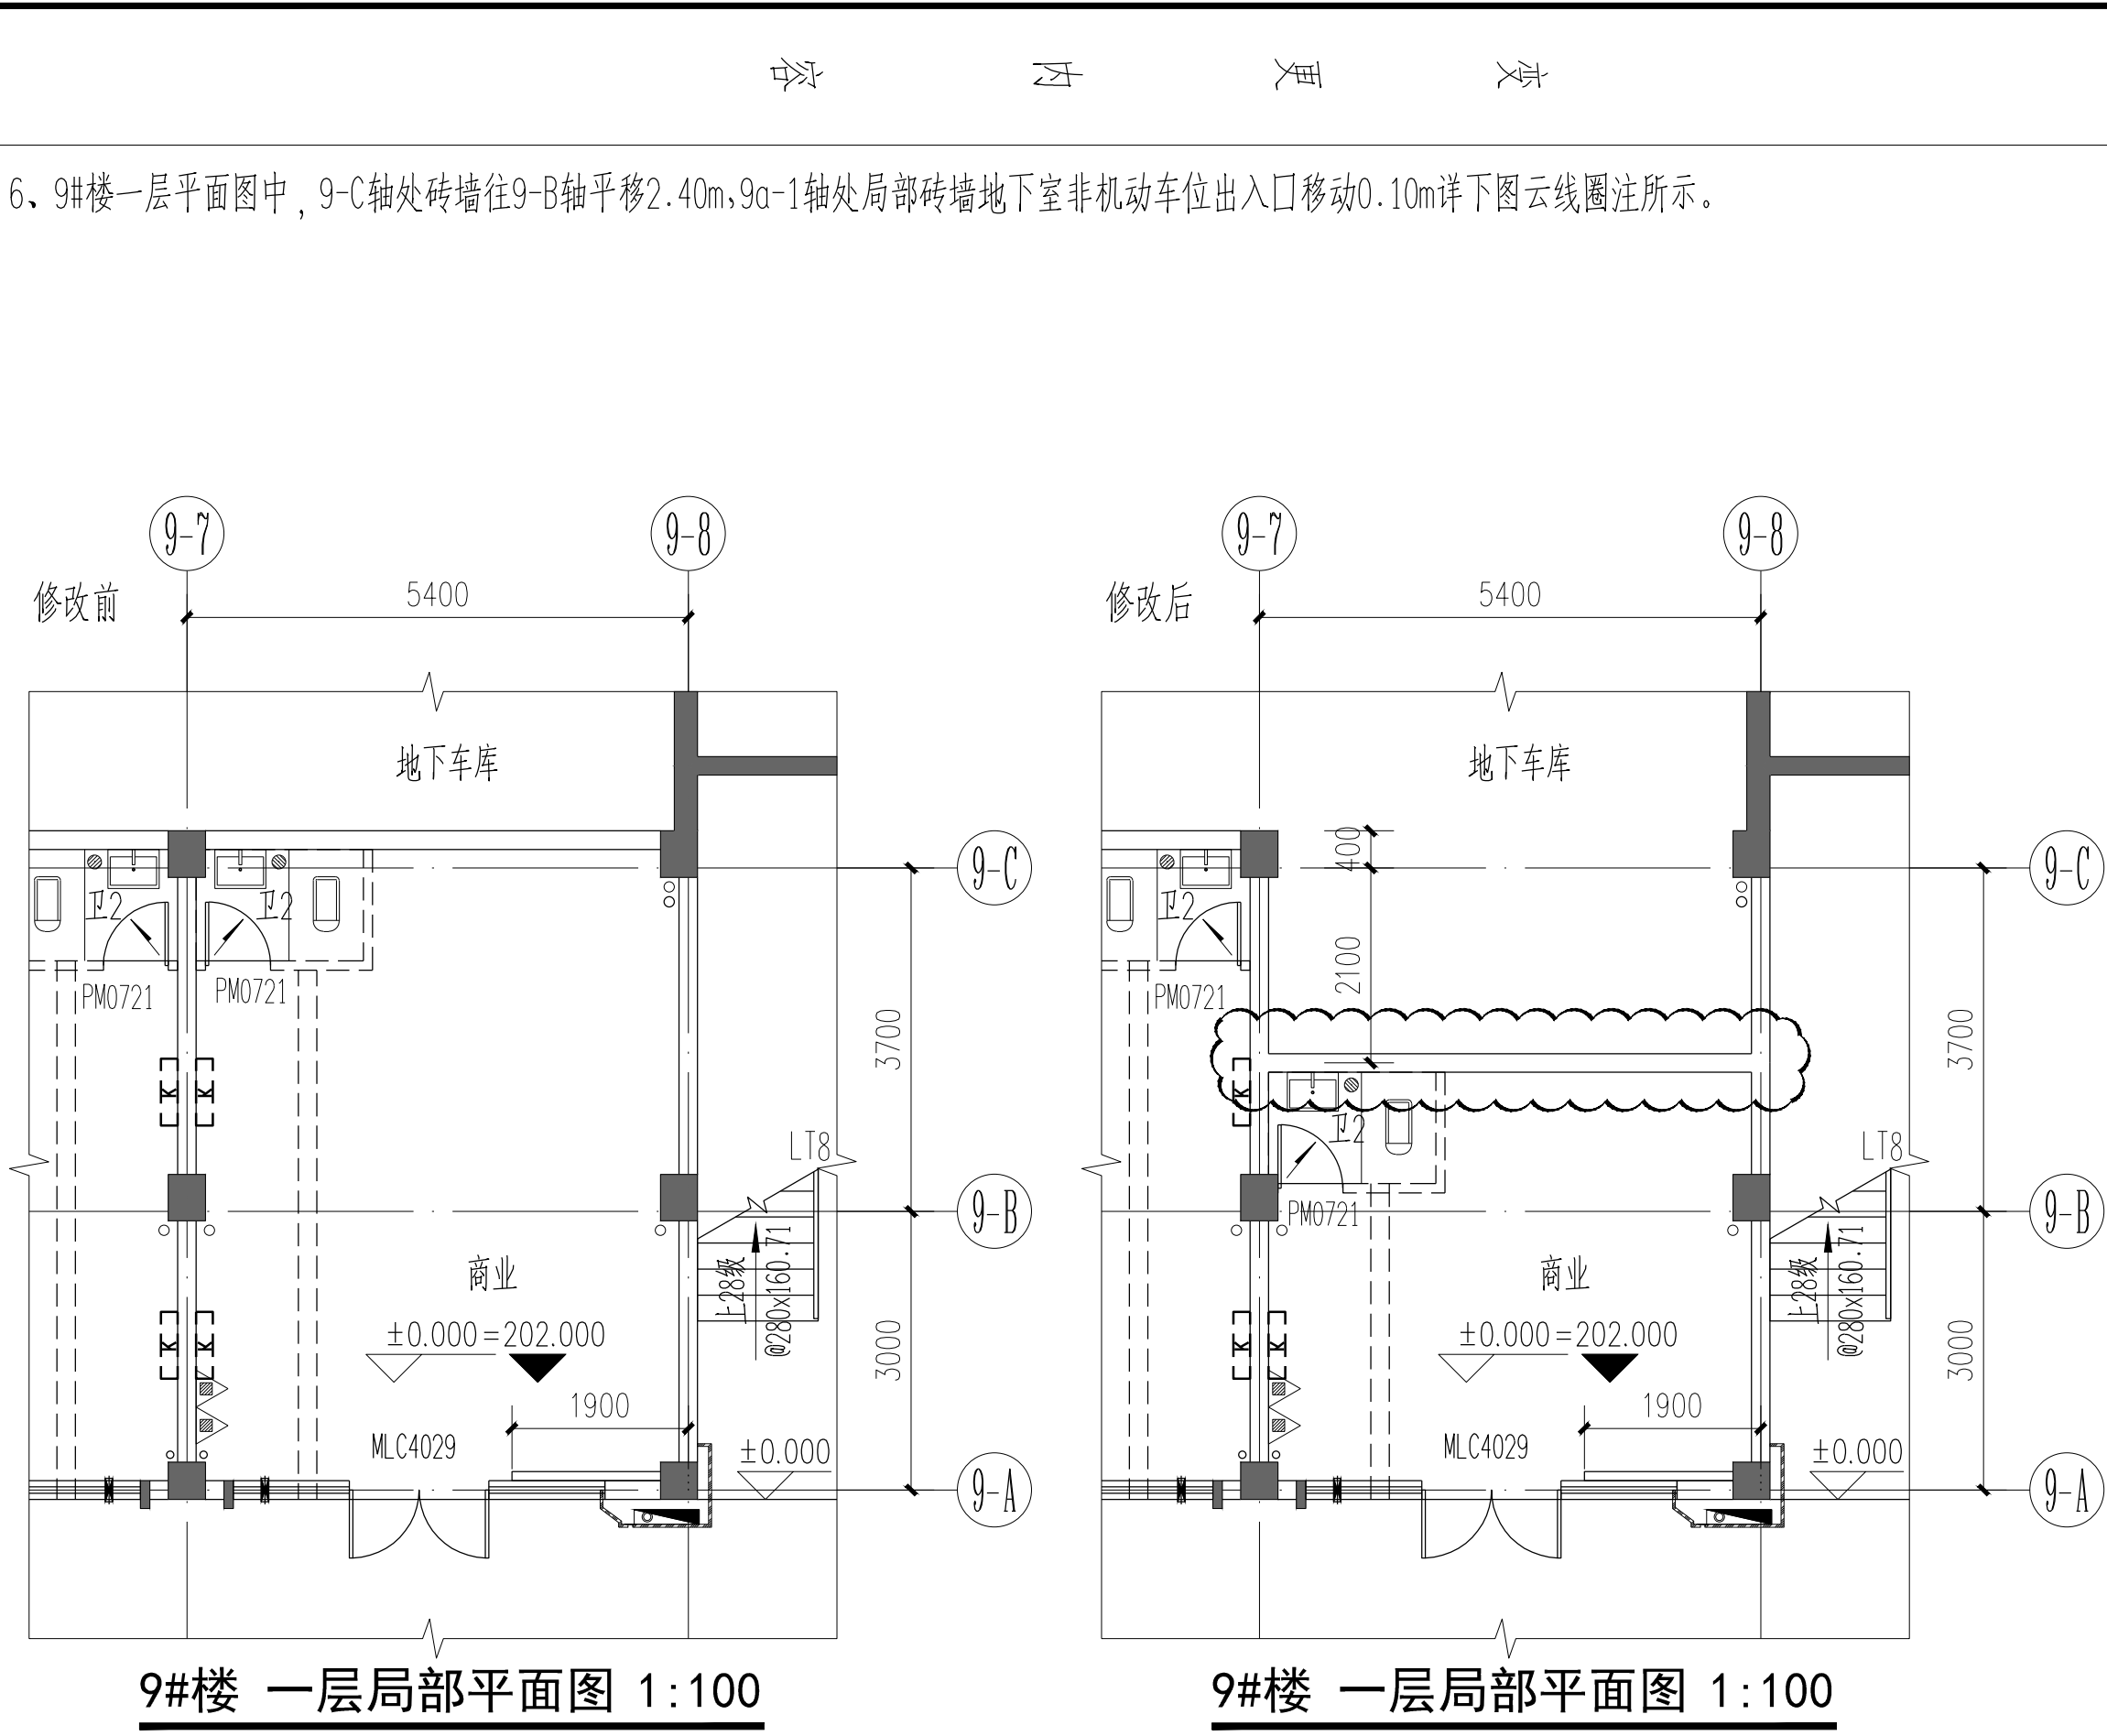

工程名称	三明融侨观邸	工程编号	3504022008260101	会签栏	建筑	结构	给排水	电气	暖通
更改原因	根据实测和建设单位要求修改	子项名称	11#楼	专业	建施	审定	审核	设计变更 发起专业	专业负责人 助理
				校对	更改人	李永杰	李永杰	备注	


设计更改内容

7、11#楼一层平面图中，11-D轴处玻璃门M03834b往外平移0.10m，玻璃门M05434b往外平移0.20m，详下图云线圈注所示。

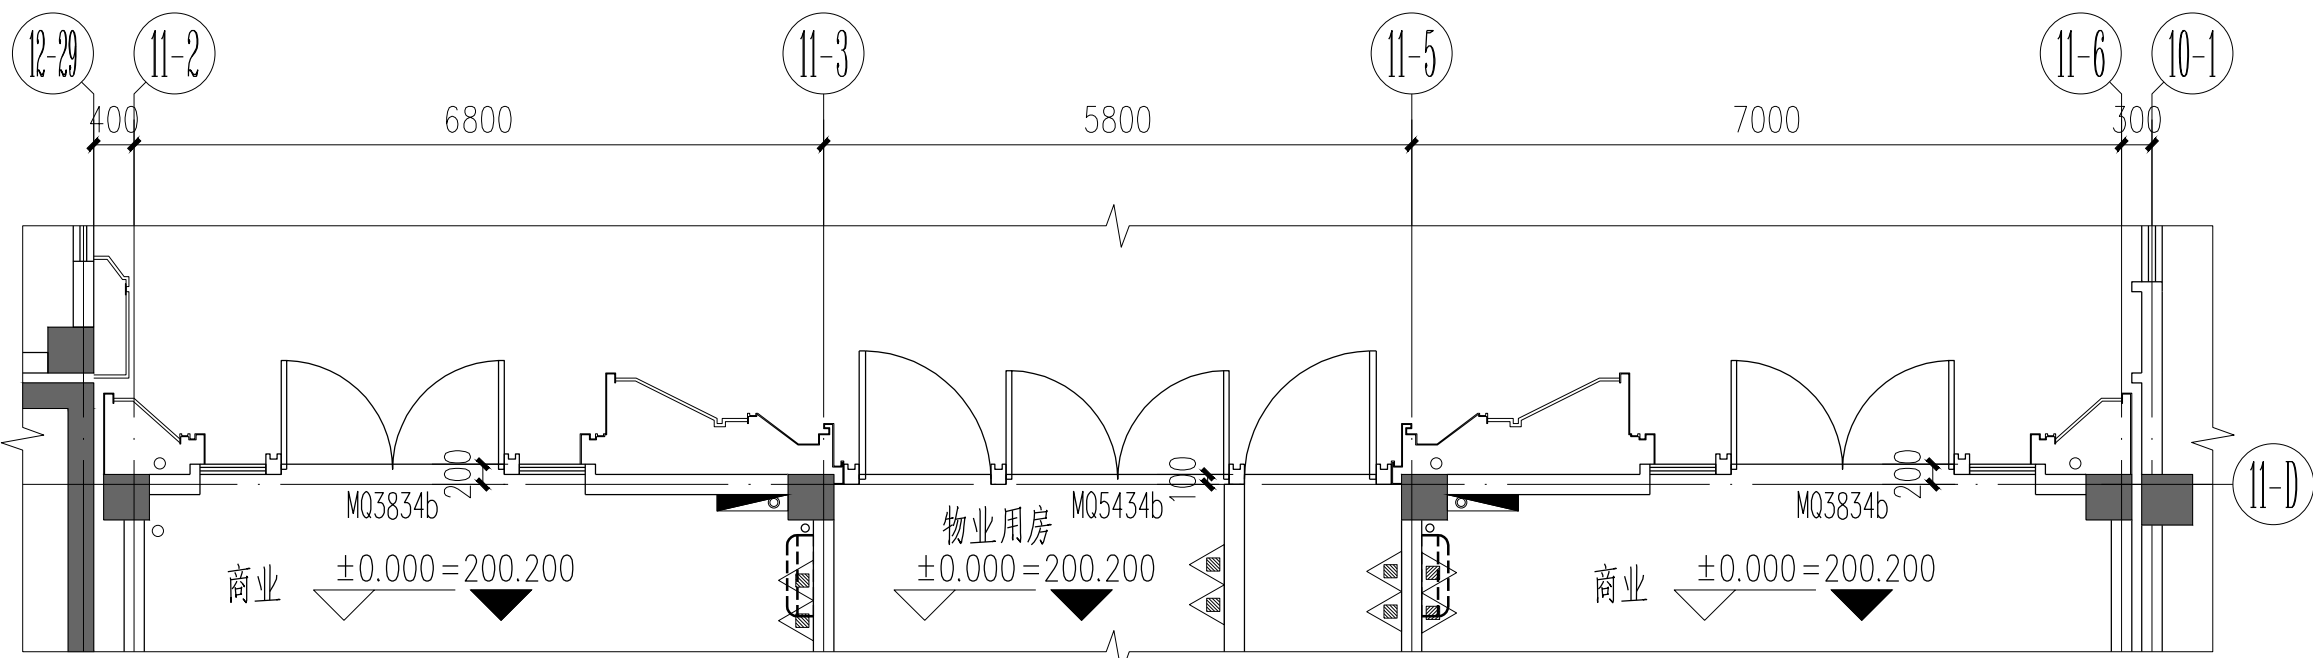

修改前


11#楼 一层局部平面图 1:100

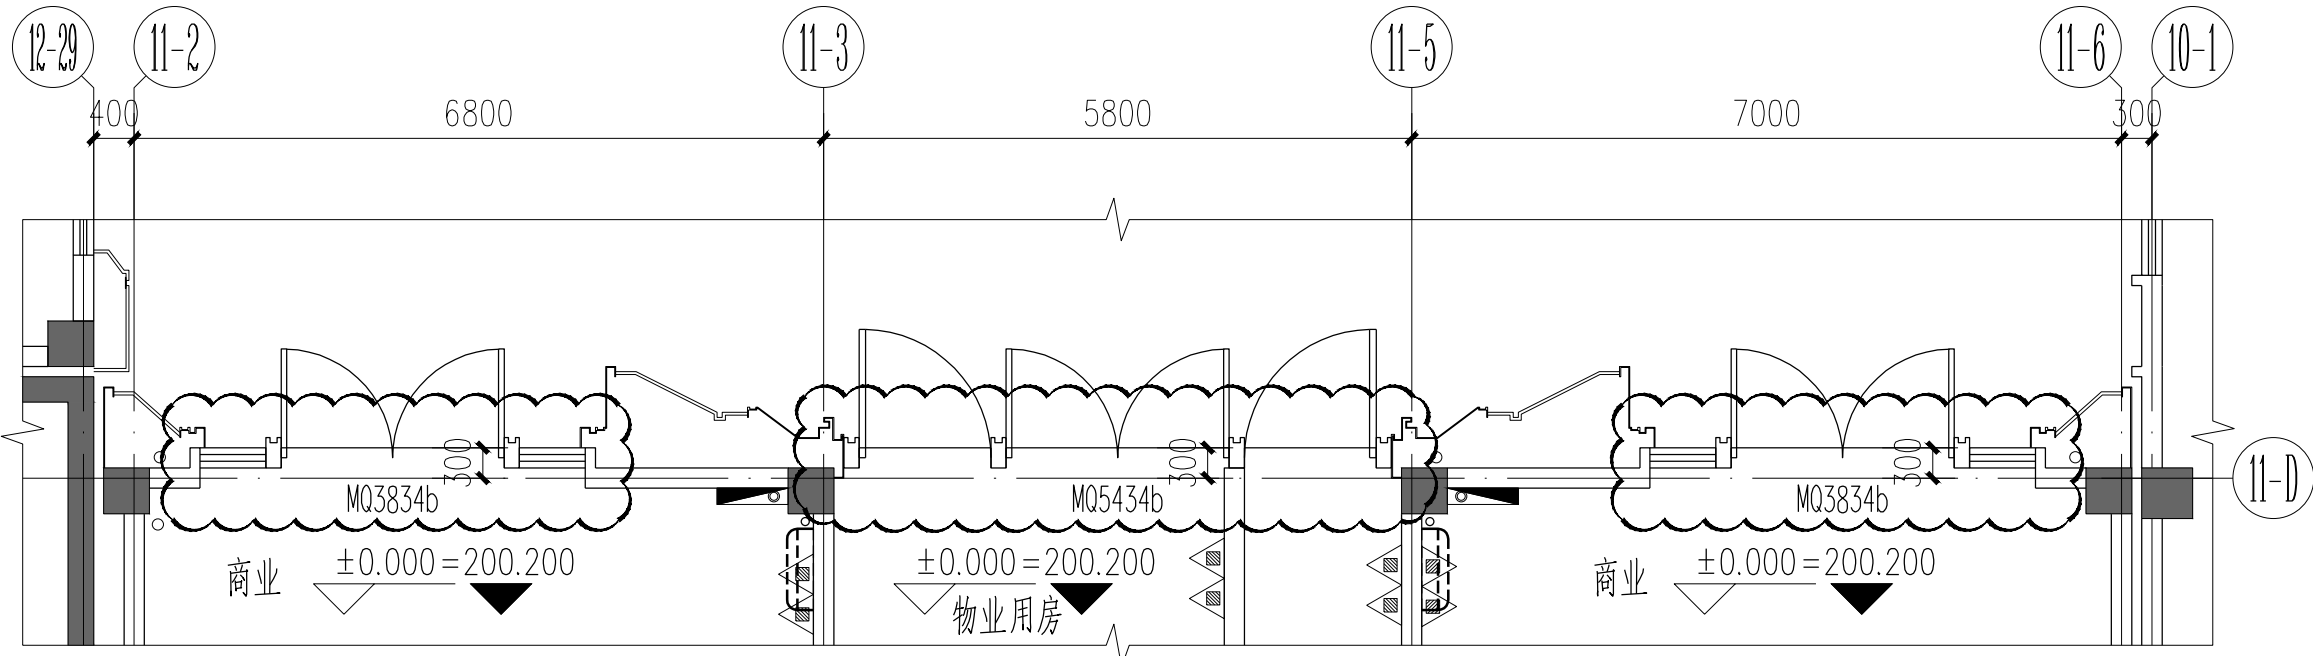

修改后


11#楼 一层局部平面图 1:100

8、11#楼二层平面图中，11-D轴处玻璃窗M03837往外平移0.10m，玻璃窗M05416b往外平移0.20m，详下图云线圈注所示。

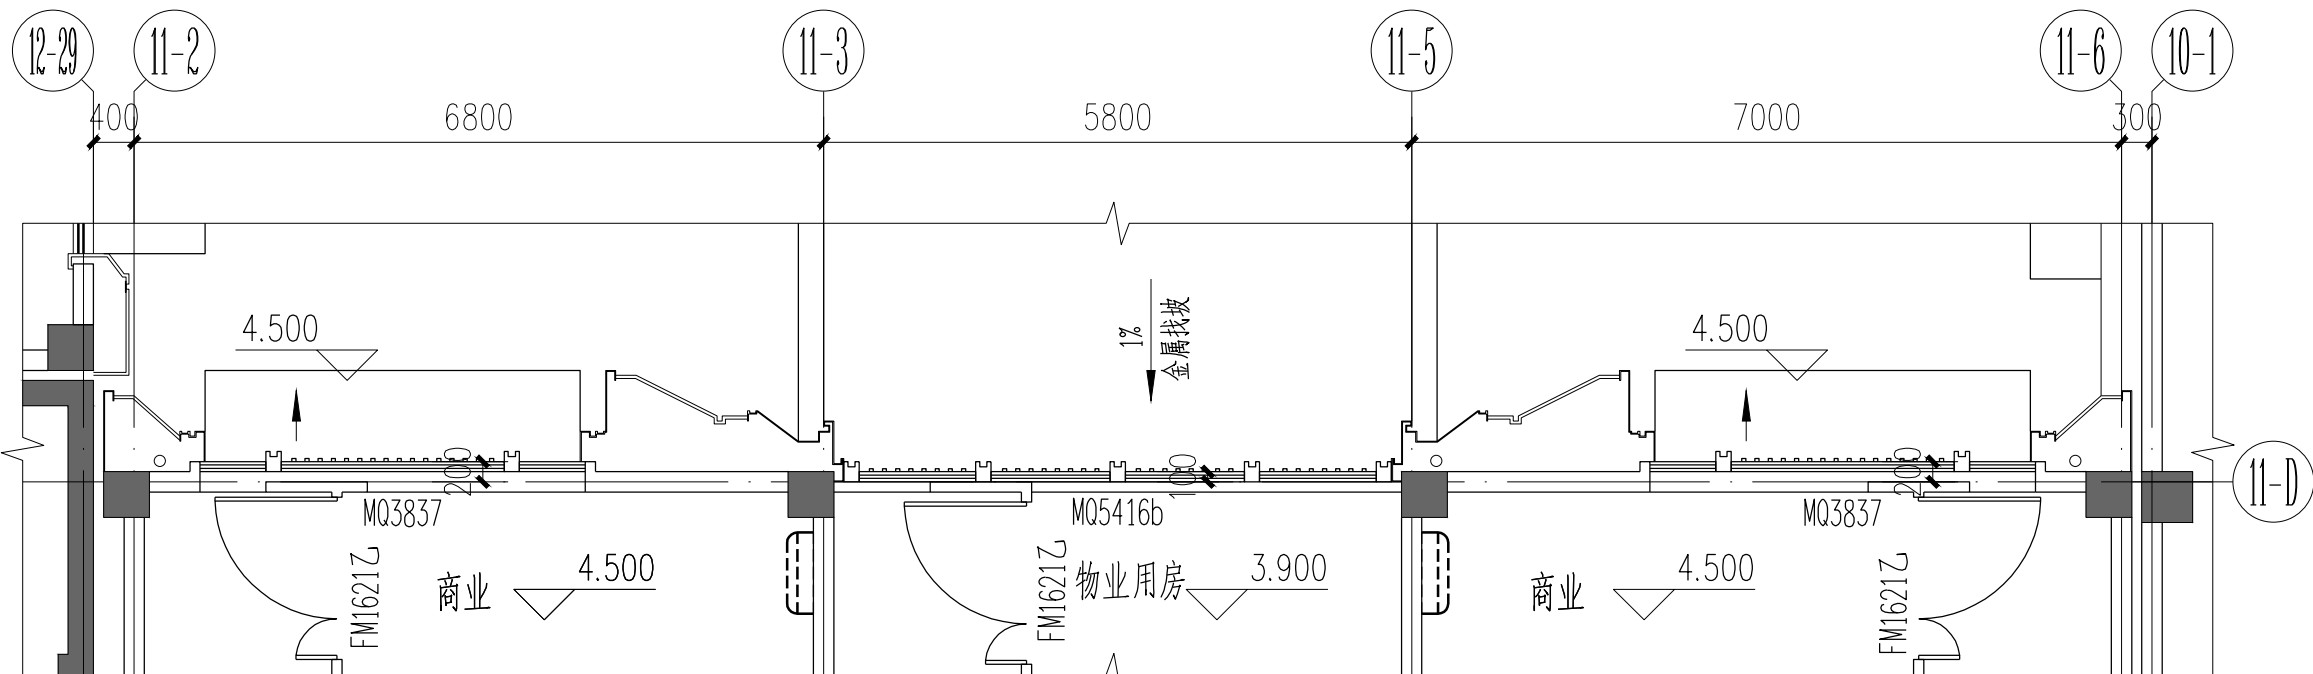

修改前

11#楼 二层局部平面图 1:100


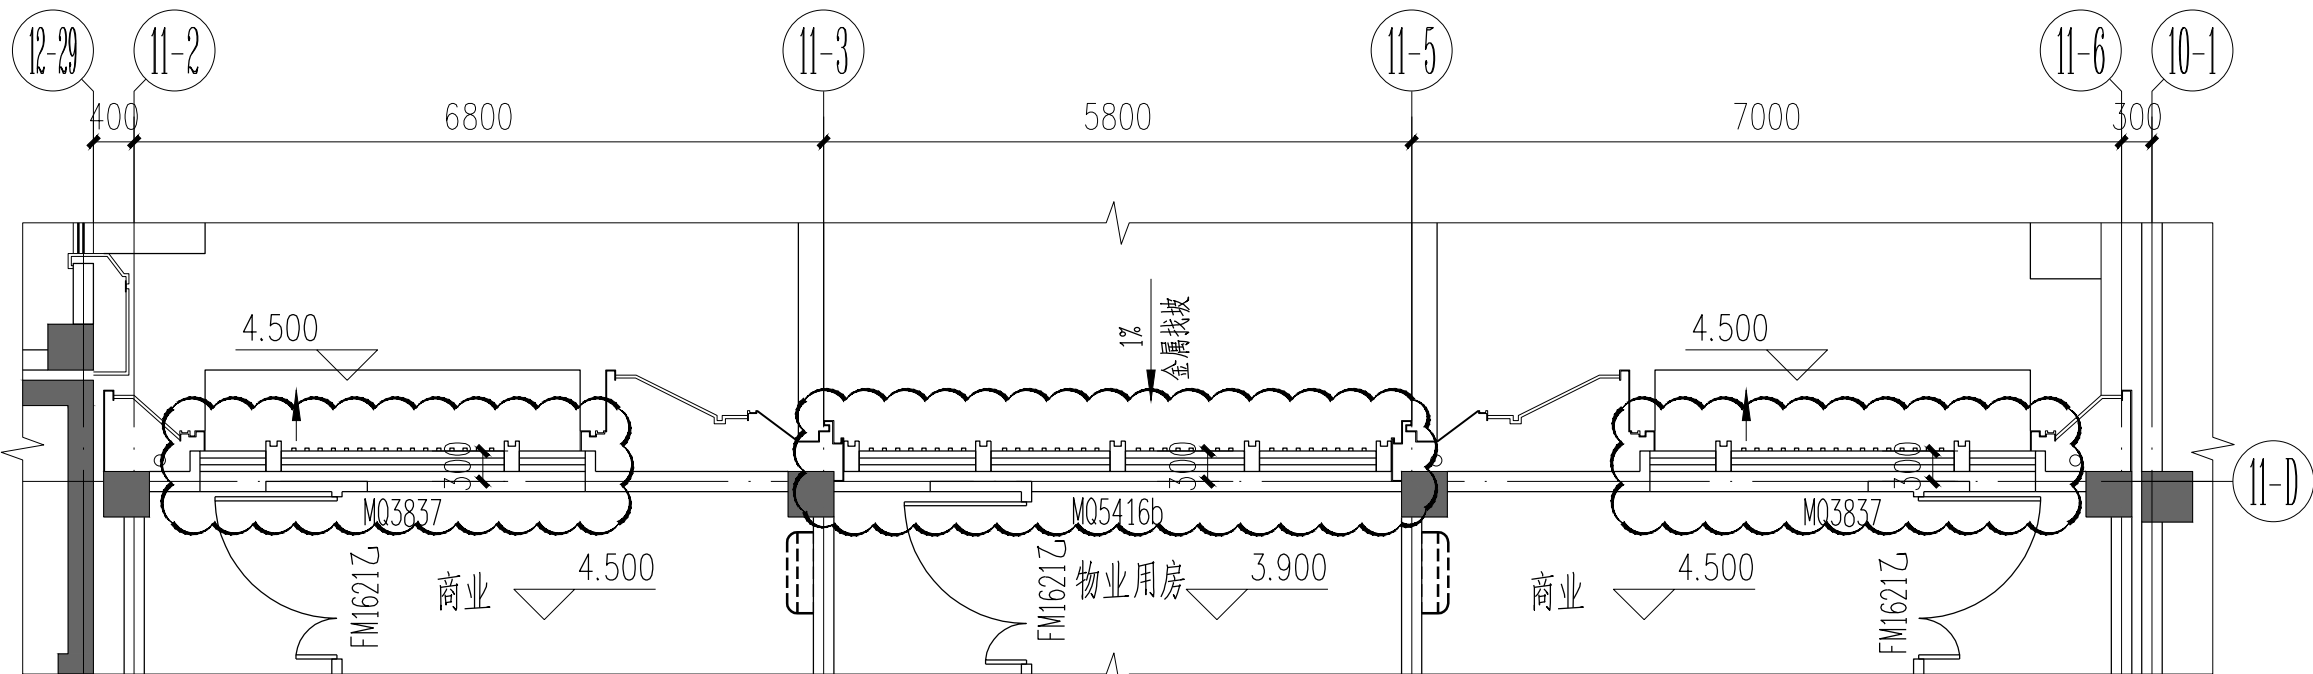


修改后



11#楼 二层局部平面图 1:100

工程名称	三明融侨观邸	工程编号	3504022008260101	会签栏	建筑	结构	给排水	电气	暖通
更改原因	根据实测和建设单位要求修改				校对	审核	设计变更发起专业	备注	
子项名称	11#、12#楼	专业	建施	审定	更改人	李永杰	专业负责人	李永杰	专业负责人助理

9、11#楼三层平面图中，11-B轴处玻璃门MQ5430b往下平移0.10m，扶梯南侧的上空区域封板；物业用房功能标注有误，实际为小区公共电梯厅，详下图云线圈注所示。

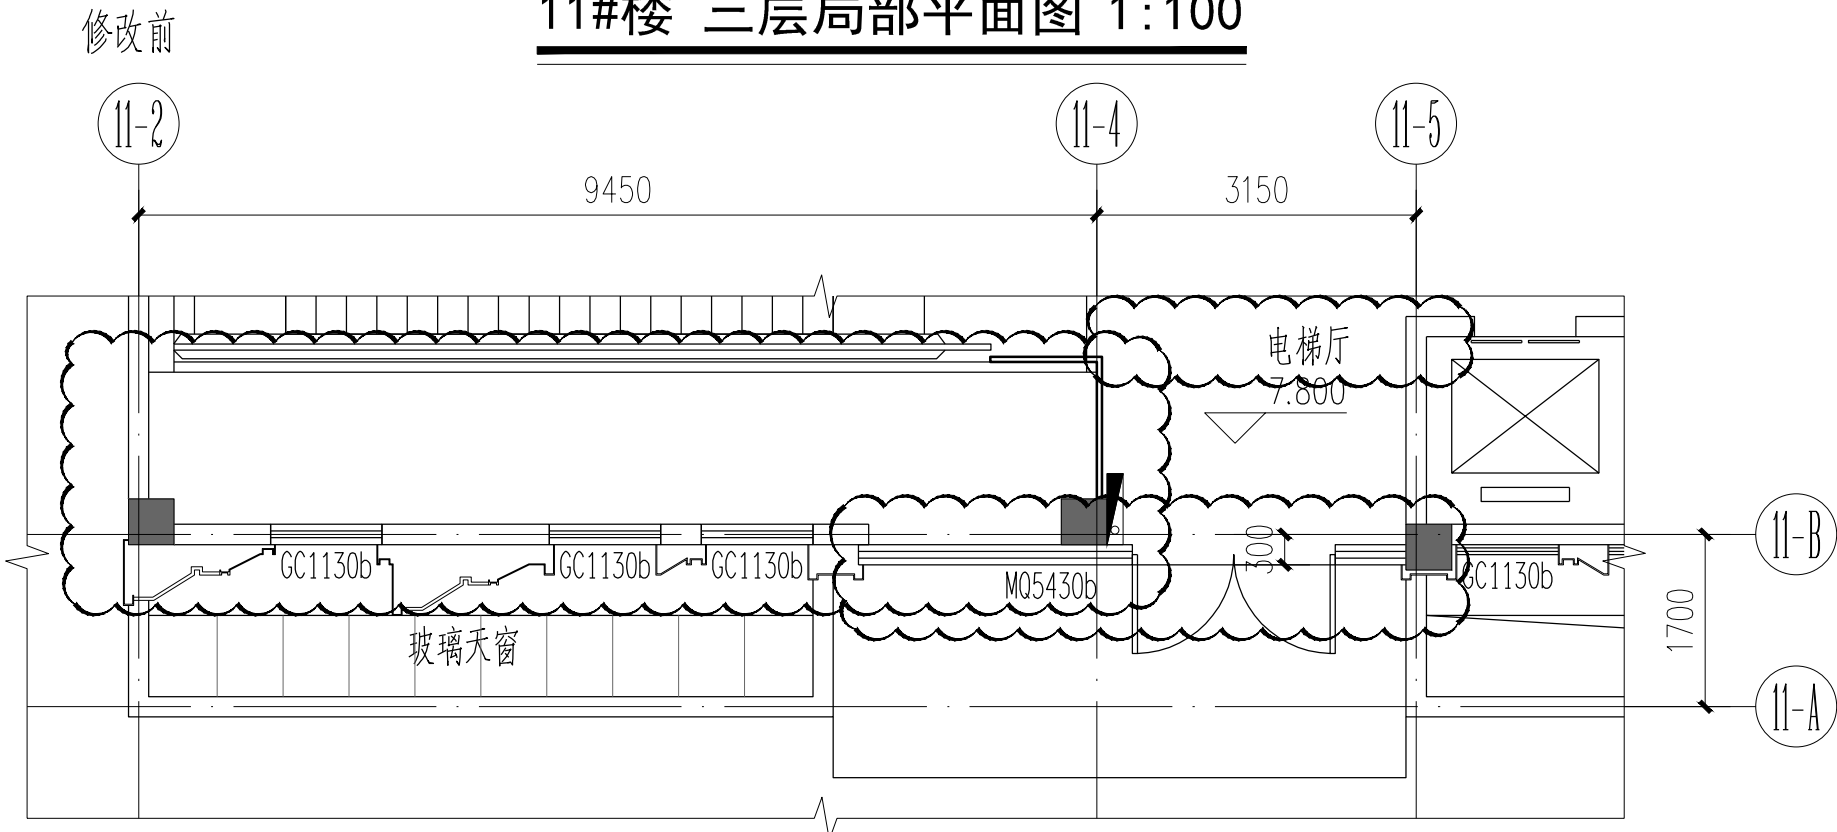
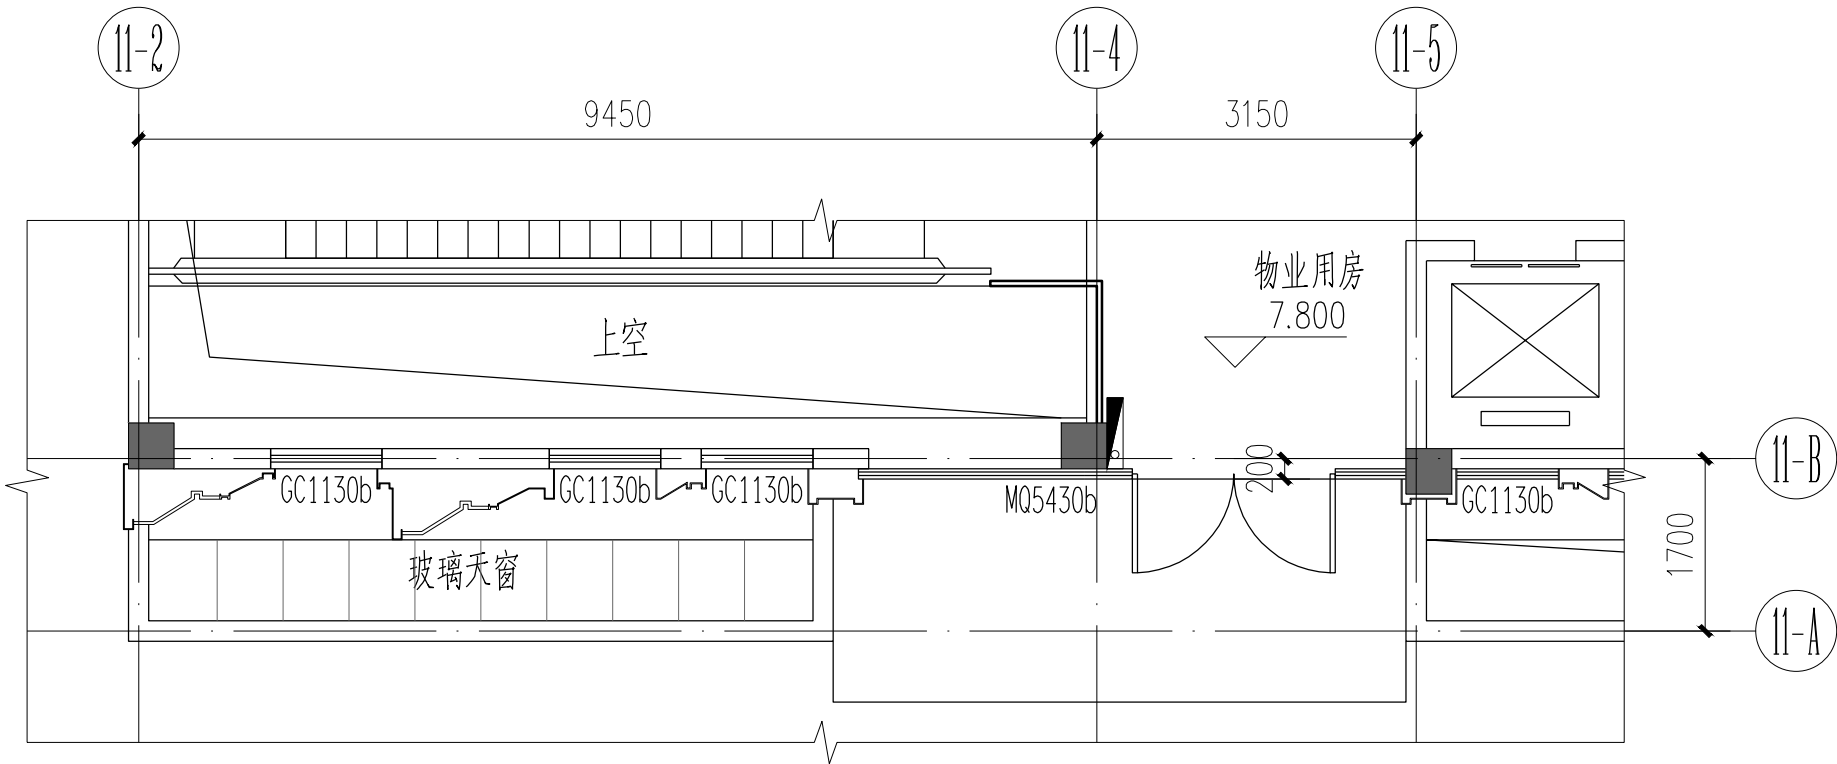


10、12#楼二层平面图中，12B-1轴处墙体和玻璃门窗往外移0.10m，详下图云线圈注所示。

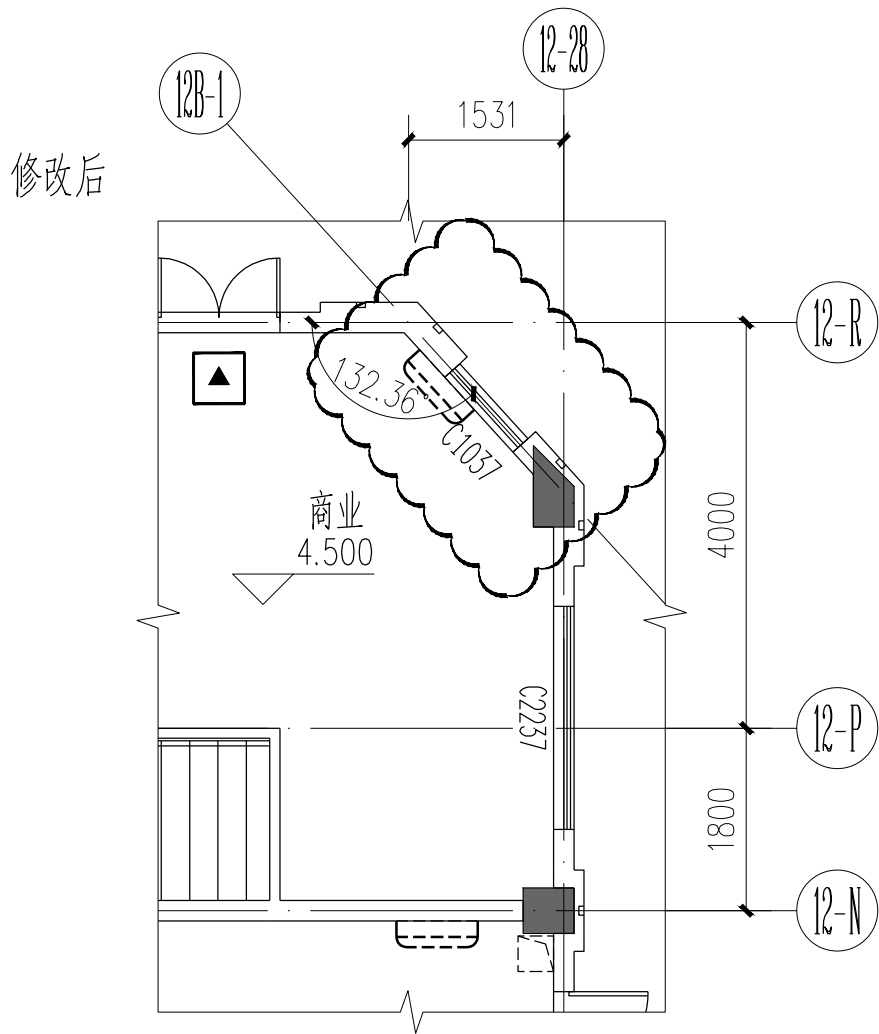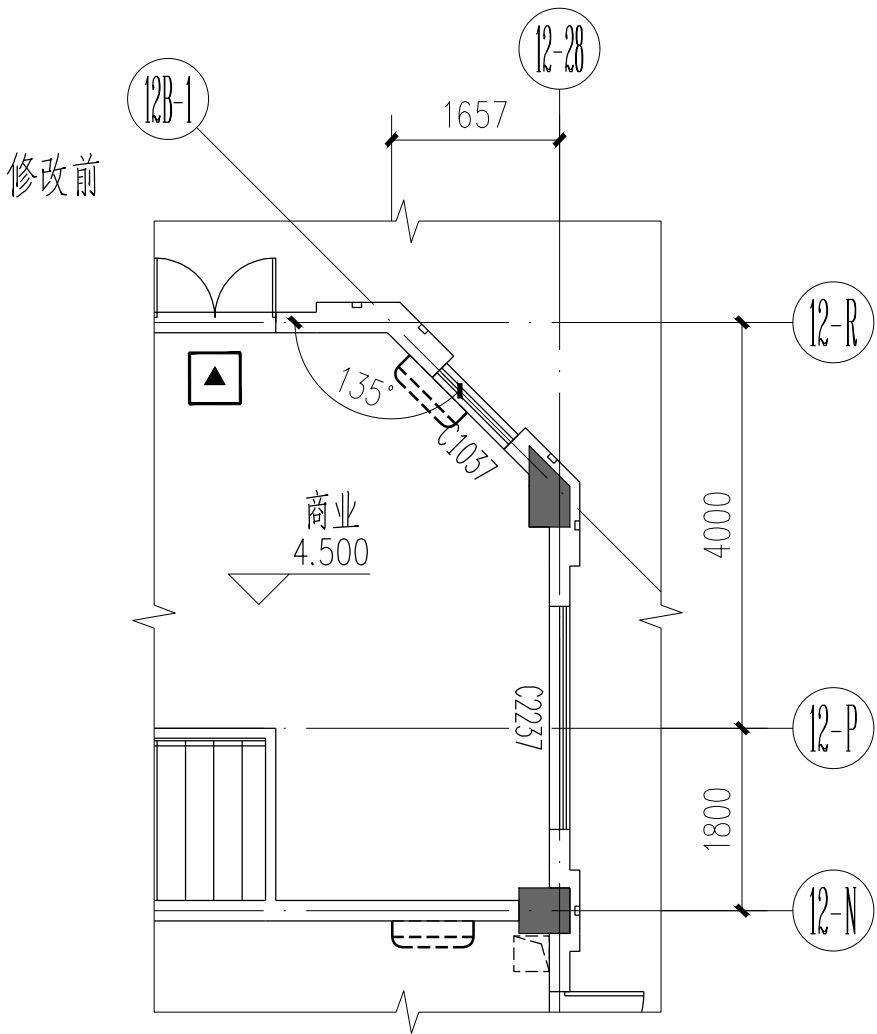

工程名称	三明融侨观邸	项目编号	3504022008260101	会签栏	建筑	结构	给排水	电气	暖通
更改原因	根据实测和建设单位要求修改				12#楼	专业	建施	审定	审核
		子项名称						设计变更 发起专业	专业负责人 助理
								备注	

12、8#柴油发电机房排风井墙体及百叶位置调整，详下图云线圈注所示。

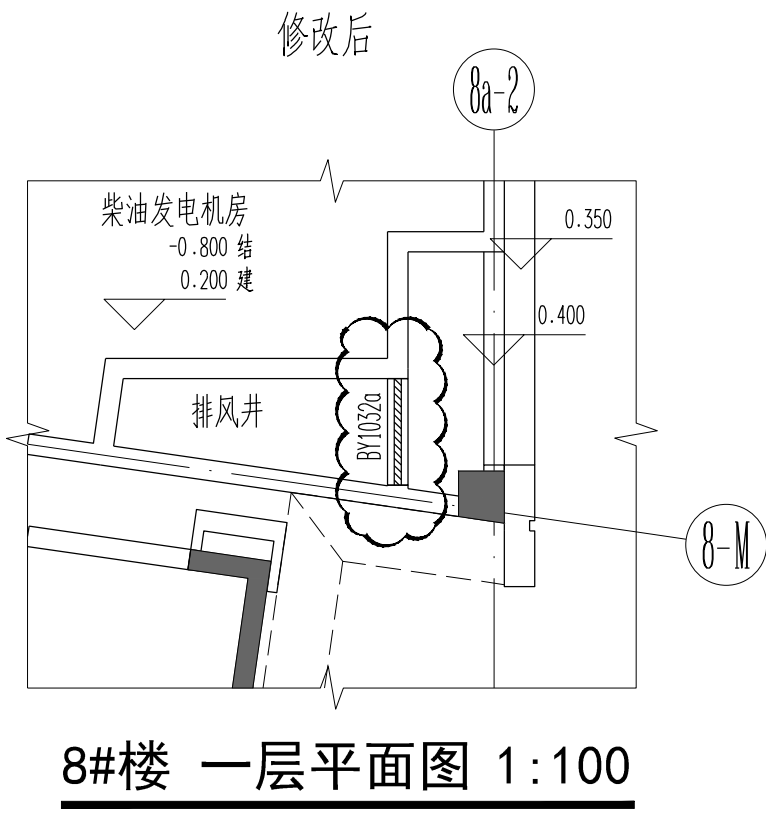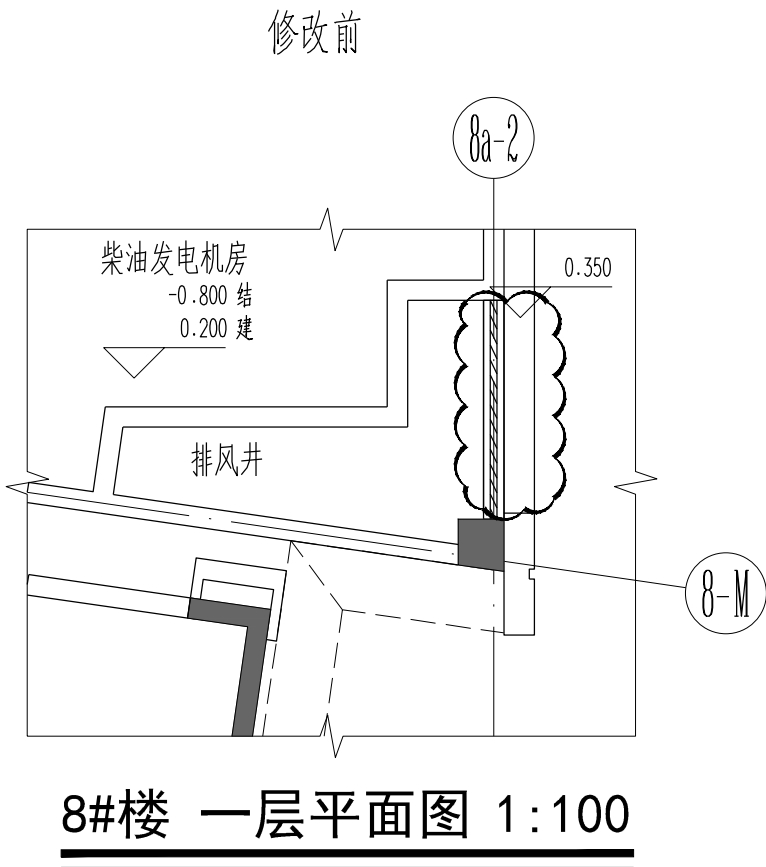

11、12#楼一层平面图中，12A-1轴处墙体和玻璃门窗往外移0.13m，详下图云线圈注所示。

