





荆东安置房及周边附属配套工程（安置房）建筑方案设计 方案变更

建设单位：三明市三元区城市建设投资有限责任公司
设计单位：福建一建集团有限公司

 福建一建集团有限公司 FuJian First Construction Group Co.,Ltd.		福建一建集团有限公司 设计资质： 甲级 证书编号： A135004919		建设单位	三明市三元区城市建设投资有限责任公司
		工程名称	荆东安置房及周边附属配套工程（安置房）		
方案设计				专业负责	
建筑设计	王海帆、方毓荣、罗裘华、 谢雨歆、温邵昌、 吴昊岑			建筑专业负责	周成才
结构设计	谢煜辉			结构专业负责	王锦星
电气设计	李镇鸿			电气专业负责	李镇鸿
给排水设计	郑伯辉			给排水专业负责	郑伯辉
暖通设计	元平华			暖通专业负责	许龙杰
图纸专用章：				建筑师注册章：	

变更前

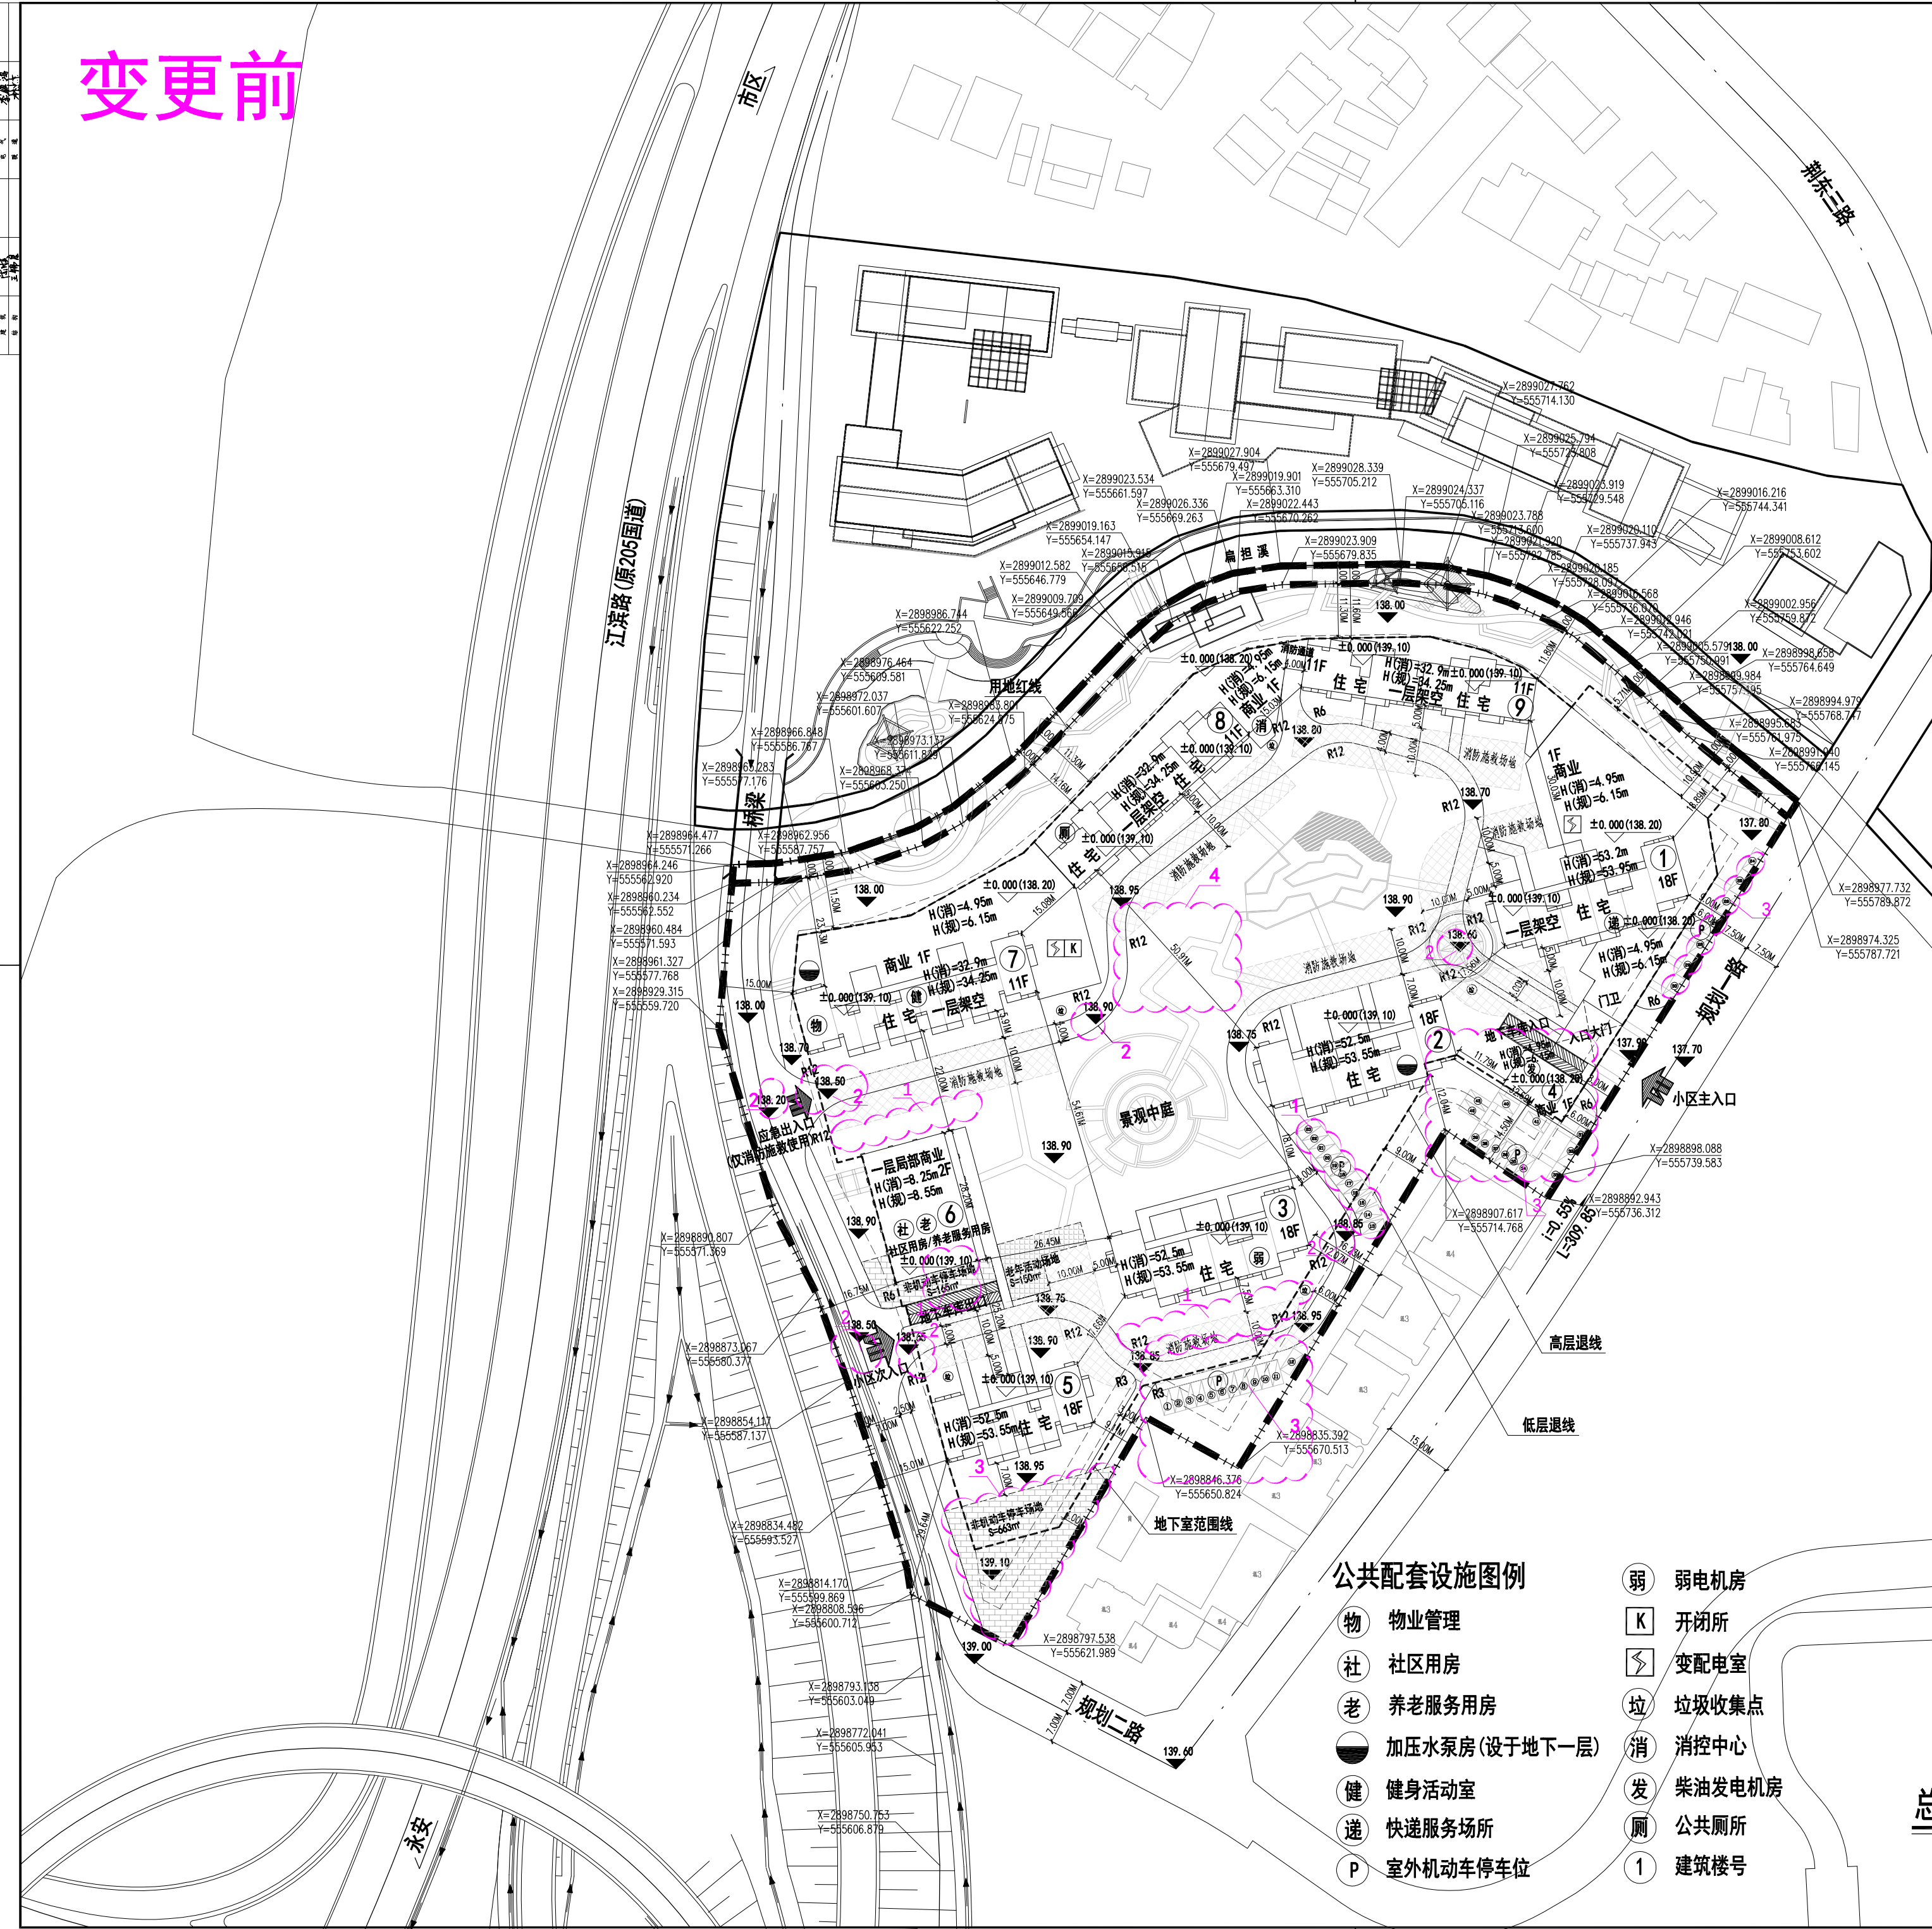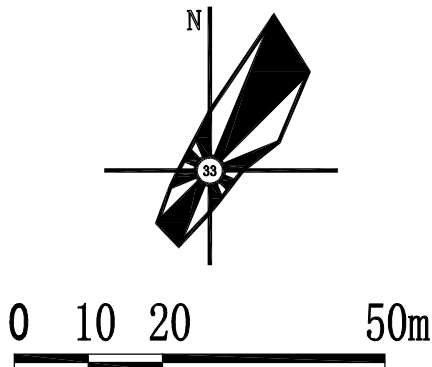

主要技术经济指标表

名称	数值	规划条件
总用地面积	28375.95m ²	约42.56亩
总建筑面积	77700.00m ²	
容积率	1.474	≤2.0
地上建筑面积(计容)	55994.90m ²	
住宅	50878.17m ²	
商业	2960.58m ²	
公共配套	2156.15m ²	
其中		
物业管理用房	192.94m ²	
社区用房	774.26m ²	
快递服务场所	54.70m ²	
健身活动室	141.50m ²	
养老服务用房	216.72m ²	
公共厕所	137.97m ²	
变配电室及开闭所	477.34m ²	
计量间	77.39m ²	
发电机房	44.10m ²	
消控室	39.23m ²	
不计容建筑面积	21705.10m ²	
其中		
架空建筑面积	1061.76m ²	
地下建筑面积	20643.34m ²	
机动车停车位	620个	1.1个/100m ² 计容面积
其中		
地上机动车位	43个	
地下机动车位	577个	
非机动车停车位面积	1127m ²	2m ² /100m ² 计容面积
建筑基底面积	7500.00m ²	
建筑密度	26.44%	≤30%
绿地面积	8515.00m ²	
绿地率	30.0%	≥30%
户数	606户	

公共配套设施图例

- 物

物业管理
- 社

社区用房
- 老

养老服务用房
- 加

加压水泵房(设于地下一层)
- 健

健身活动室
- 递

快递服务场所
- P

室外机动车停车位
- 弱

弱电机房
- K

开闭所
- 变

变配电室
- 垃

垃圾收集点
- 消

消控中心
- 发

柴油发电机房
- 厕

公共厕所
- 1

建筑楼号

总平面图

图纸专用章

注册建筑师执业章

注册结构师执业章

施工图审查单位

施工图审查合格书编号

工程名称

荆东安置房及周边附属配套工程(安置房)

子项名称

建设单位

三明市三元城市建设投资有限公司

审定

陈强

项目负责人

陈国英

专业负责人

陈国英

审核

王海航

校对

王海航

设计

方毓荣

制图

方毓荣


图纸名称

总平面图

工程编号: 2023-0101 设计阶段: 方案报批
图别: 方案 版本: 第一版
图号: 出图日期: 2028.12

变更后

1. 非机动车停车场地调整
2. 室外标高调整
3. 室外停车位位置调整
4. 新增室外休息凉亭
5. 技术指标调整

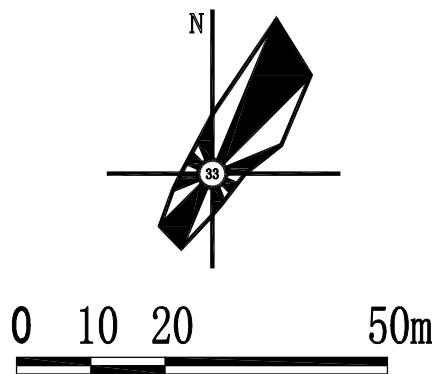

主要经济技术指标		
项目	数值	规划条件要求
总用地面积(m ²)	28375.850	
总建筑面积(m ²)	77522.261	
其中	地上建筑面积(m ²)	57046.299
	商业区	2971.524
	架空及架空非机动车	1002.845
	快速服务场所	54.600
	变电室及开闭所	481.743
	计量间	80.848
	住宅区	50922.372
	发电机房	44.100
	养老服务用房	212.325
	社区用房	761.110
	健身活动室	144.820
	物业管理用房	189.010
	消控室	42.632
	其他面积 (社区养老外墙)	16.915
	公共厕所	121.455
其中	地下建筑面积(m ²)	20475.962
	地下室	20210.073
	洗车场	265.889
	不计容建筑面积(m ²)	0.000
	计容建筑面积	56043.454
其中	不计容建筑面积	21478.807
	建筑基底面积(m ²)	7590.172
	绿地面积(m ²)	8586.002
	容积率	1.975
	建筑密度(%)	26.75%
其中	绿地率(%)	30.26%
	机动车位 (个)	623
	地上车位 (公共停车位数)	45
	地下车位	578
	其中	
其中	微型车位	9
	普通车位	569
	住宅户数 (套)	606
	非机动车位(m ²)	1193.39
	室内非机动车停车(m ²)	618.23
其中	室外非机动车停车(m ²)	575.16
	充电车位 (辆)	128

总平面图

单位名称:



福建一建集团有限公司
Fujian First Construction Group Co., Ltd.
工程设计资质证书编号: A135084919
Design Certificate No:
地址: 三明市新市中路395号9-11层
邮编: POSTCODE: 365800
电话: TEL: 0598-8318995
传真: FAX: 0598-8318995
网站: http://www.fyj1jt.com

备注:

1. 本图纸应以所标注尺寸为准, 不得以比例量取;
2. 本图纸仅供规划主管部门、施工审查、消防、人防等部门审查使用, 不得用于其他用途;
3. 本图纸之版权归福建一建集团有限公司所有;
4. 本图纸之版权归福建一建集团有限公司所有;
5. 本图纸之版权归福建一建集团有限公司所有;
6. 本图纸之版权归福建一建集团有限公司所有;
7. 本图纸之版权归福建一建集团有限公司所有;
8. 本图纸之版权归福建一建集团有限公司所有;
9. 本图纸之版权归福建一建集团有限公司所有;
10. 本图纸之版权归福建一建集团有限公司所有;

图例专用章

注册建筑师执业章

注册结构师执业章

施工图审查单位

施工图审查合格书编号

工程名称

子项名称

建设单位

三明市三元区城市建设投资有限公司

审定

陈强

项目负责人

陈国英

专业负责人

陈国英

审核

王海航

校对

王海航

设计

方毓荣

制图

方毓荣

图底名称

总平面图

工程编号

2023-07

设计阶段

方案报批

图别

方案


版本

第一版

图号

2023.07

变更前

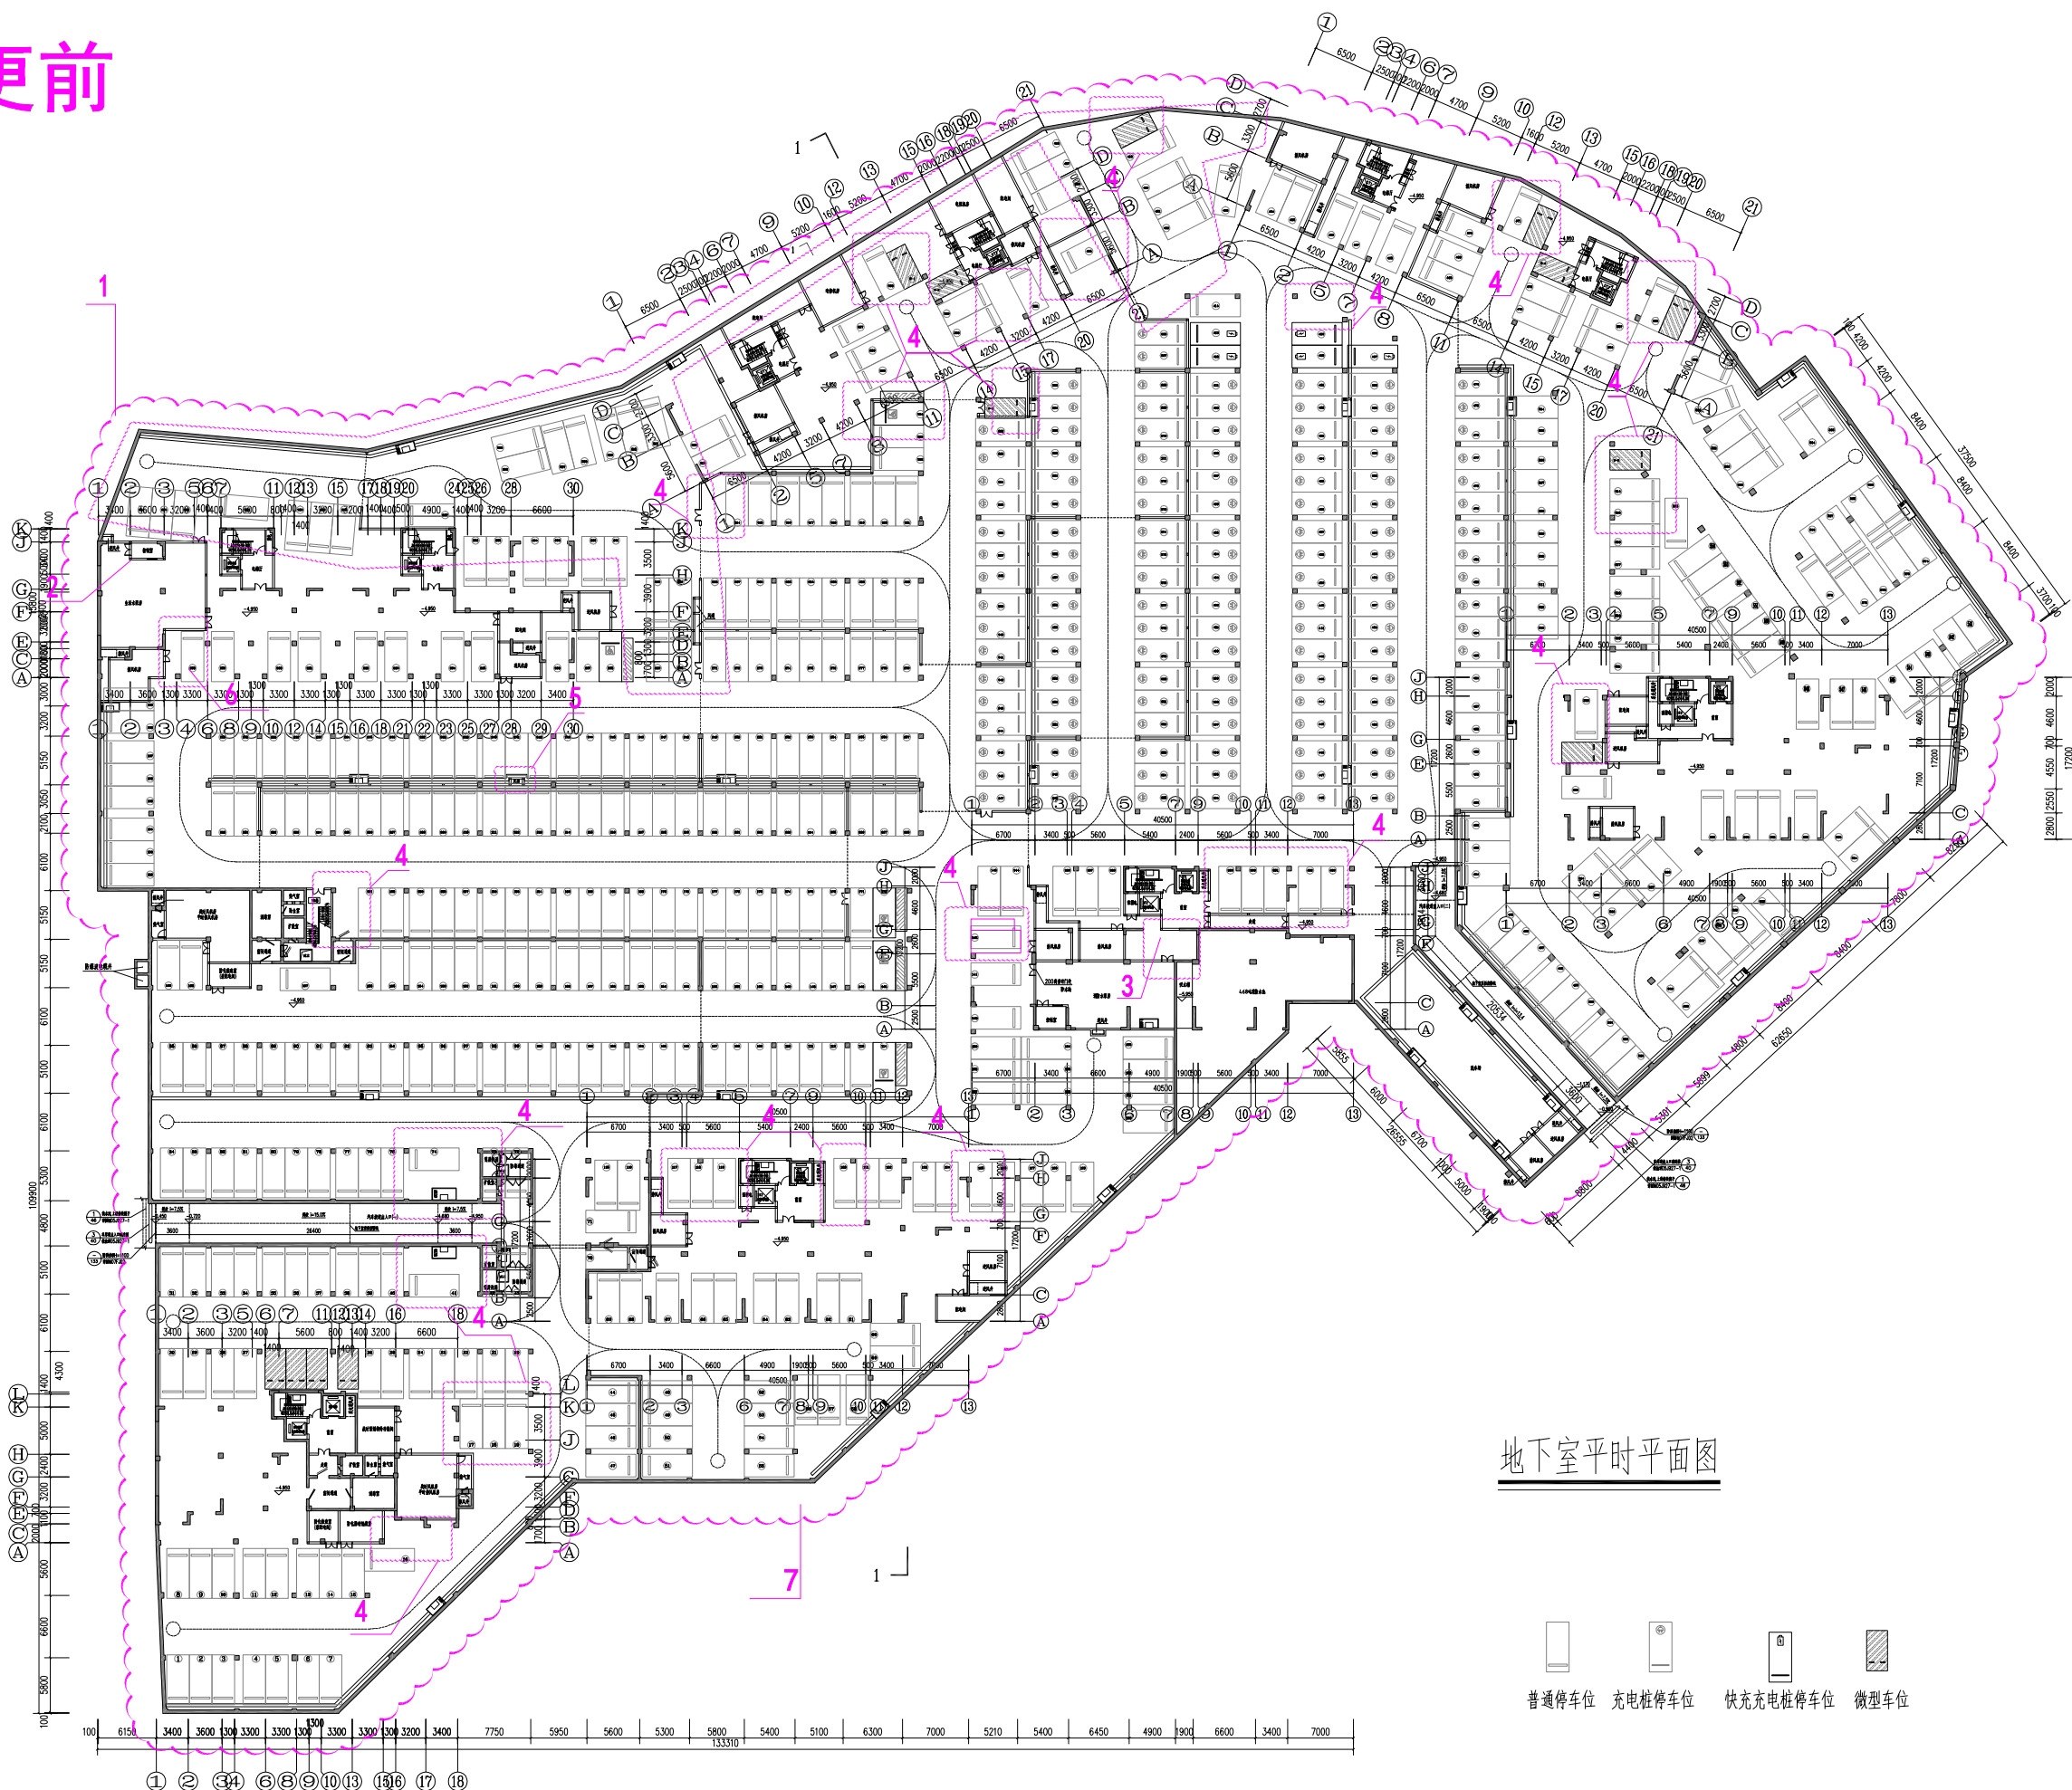

地下室平时平面图

- 普通停车位
- 充电桩停车位
- 快充充电桩停车位
- 微型车位



福建第一建设集团有限公司
Fujian First Construction Group Co., Ltd.
工程设计资质证书编号: A130004919
Design Certificate No.:
地址: 三明市城市中路399号9-11层
邮编: 361000
电话: TEL: 0598-8310095
传真: FAX: 0598-8310095
邮箱: fjjy@fjyjt.com
网址: http://www.fjyjt.com

备注:
1. 本图须经设计单位盖章及设计人签字后方可使用。
2. 本图须经监理单位盖章及监理工程师签字后方可使用。
3. 本图须经建设单位盖章及项目负责人签字后方可使用。
4. 本图须经设计单位盖章及设计人签字后方可使用。
5. 本图须经监理单位盖章及监理工程师签字后方可使用。
6. 本图须经建设单位盖章及项目负责人签字后方可使用。

图例

普通停车位	充电桩停车位	快充充电桩停车位	微型车位
-------	--------	----------	------

图名: 地下室平时平面图


图号: 地下室平时平面图

设计: 方雅捷

审核: 方雅捷

制图: 方雅捷

日期: 2020.12

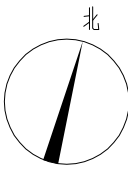[illegible]


原车位总数：577个，其中标准车位：574个、微型车位：5个折算后3个
现车位总数：578个，其中标准车位：569个、微型车位：13个折算后9个

备注:

1. 本图所标尺寸以所注尺寸为准, 不得以比例量取;
2. 本图所标管道均为主管部门, 属工程重要, 消防主管部门审批审查后方可使用;
3. 本图之版权归福建一建集团有限公司所有, 仅限本工程使用, 未经本公司提供不得转让第三方, 或以任何形式复制和重复使用;
4. 本图所标尺寸并加量设计专用效力可用于施工;
5. 本图所标中设计专用章与公章具有同等效力。

地下室平时平面图			
工程编号	FJBJ-设计2023-1017	设计阶段	方案报批
图 别	方 案	版 本	第一版
图 号		出图日期	2023. 07

变更前

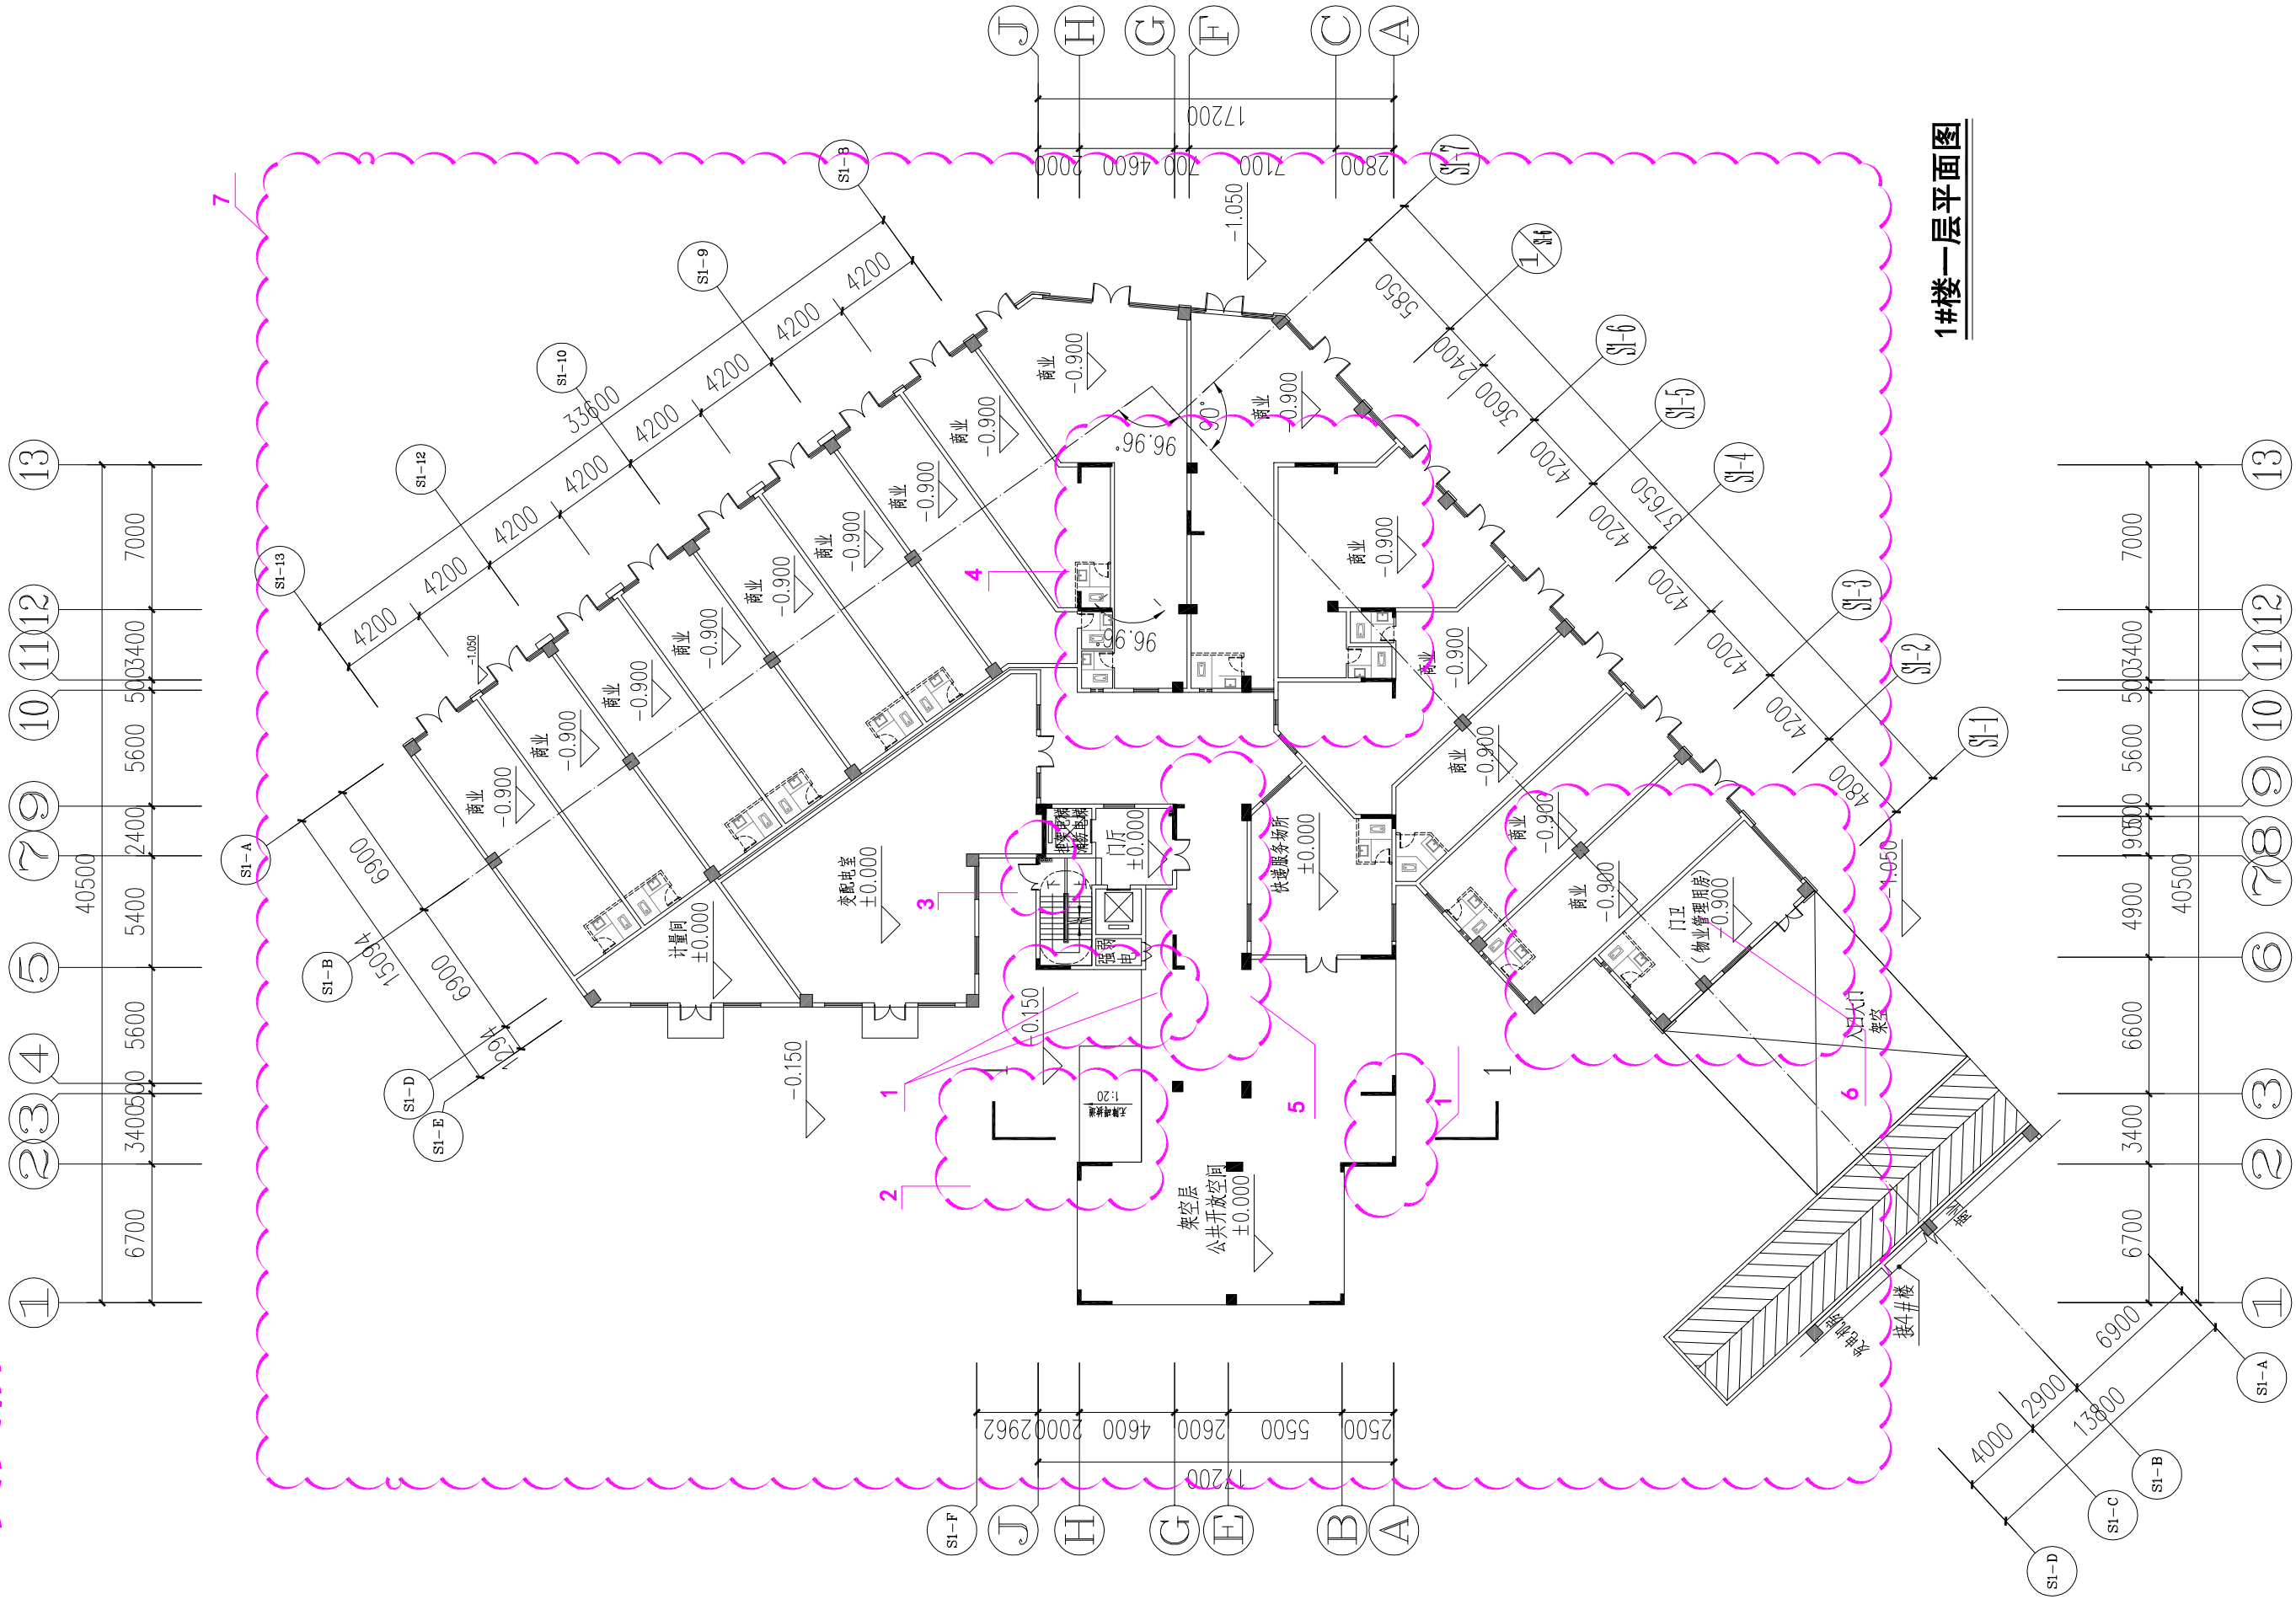


1#楼一层平面图


设计单位	福建一建集团有限公司	建设单位	三明市三元区城市建设投资有限责任公司	工程名称	荆东安置房及周边附属配套工程（安置房）	图 名	1#楼一层平面图	图 别	方 案
								日 期	2020. 12

山
風
歌

1. 增设风井、进风井、排风井
2. 无障碍坡道位置变化
3. 取消对外开门
4. 商业部分墙体调整，卫生间位置调整
5. 架空层、门厅标高调整，增设坡道楼梯
6. 门卫及入口大门移至4#楼，面积计算至4#楼。
7. 一至屋顶柱网整体调整

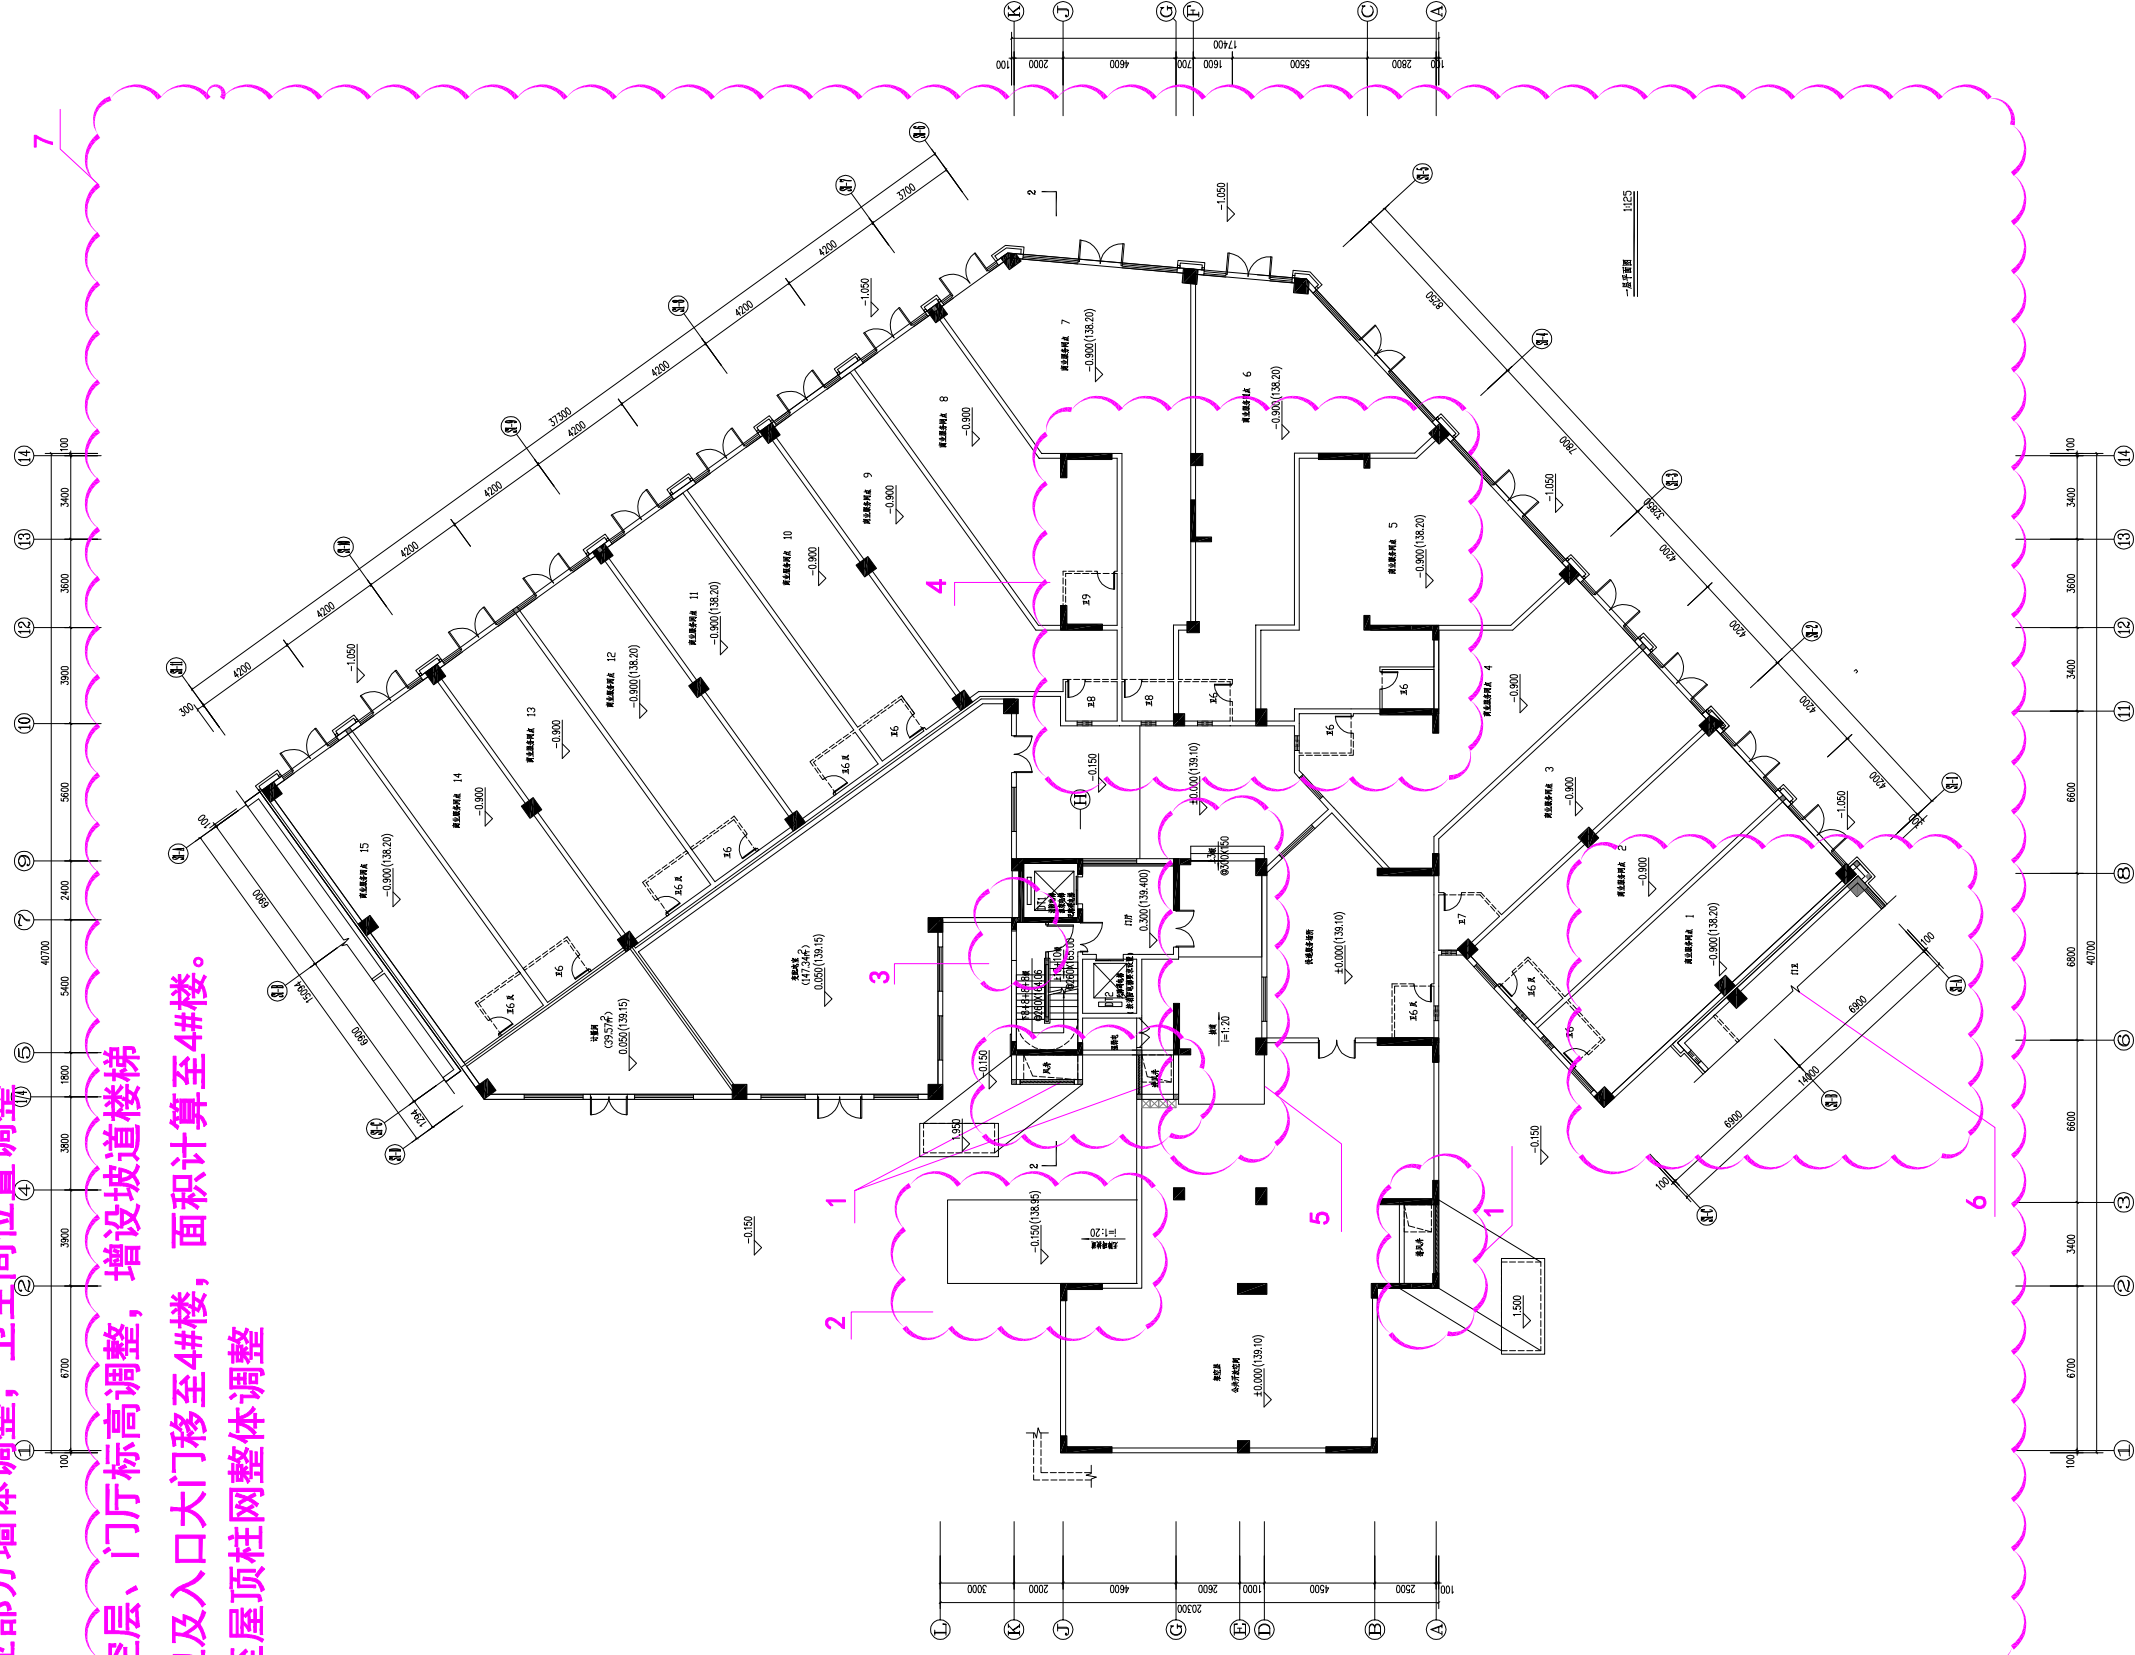[illegible]

变更前

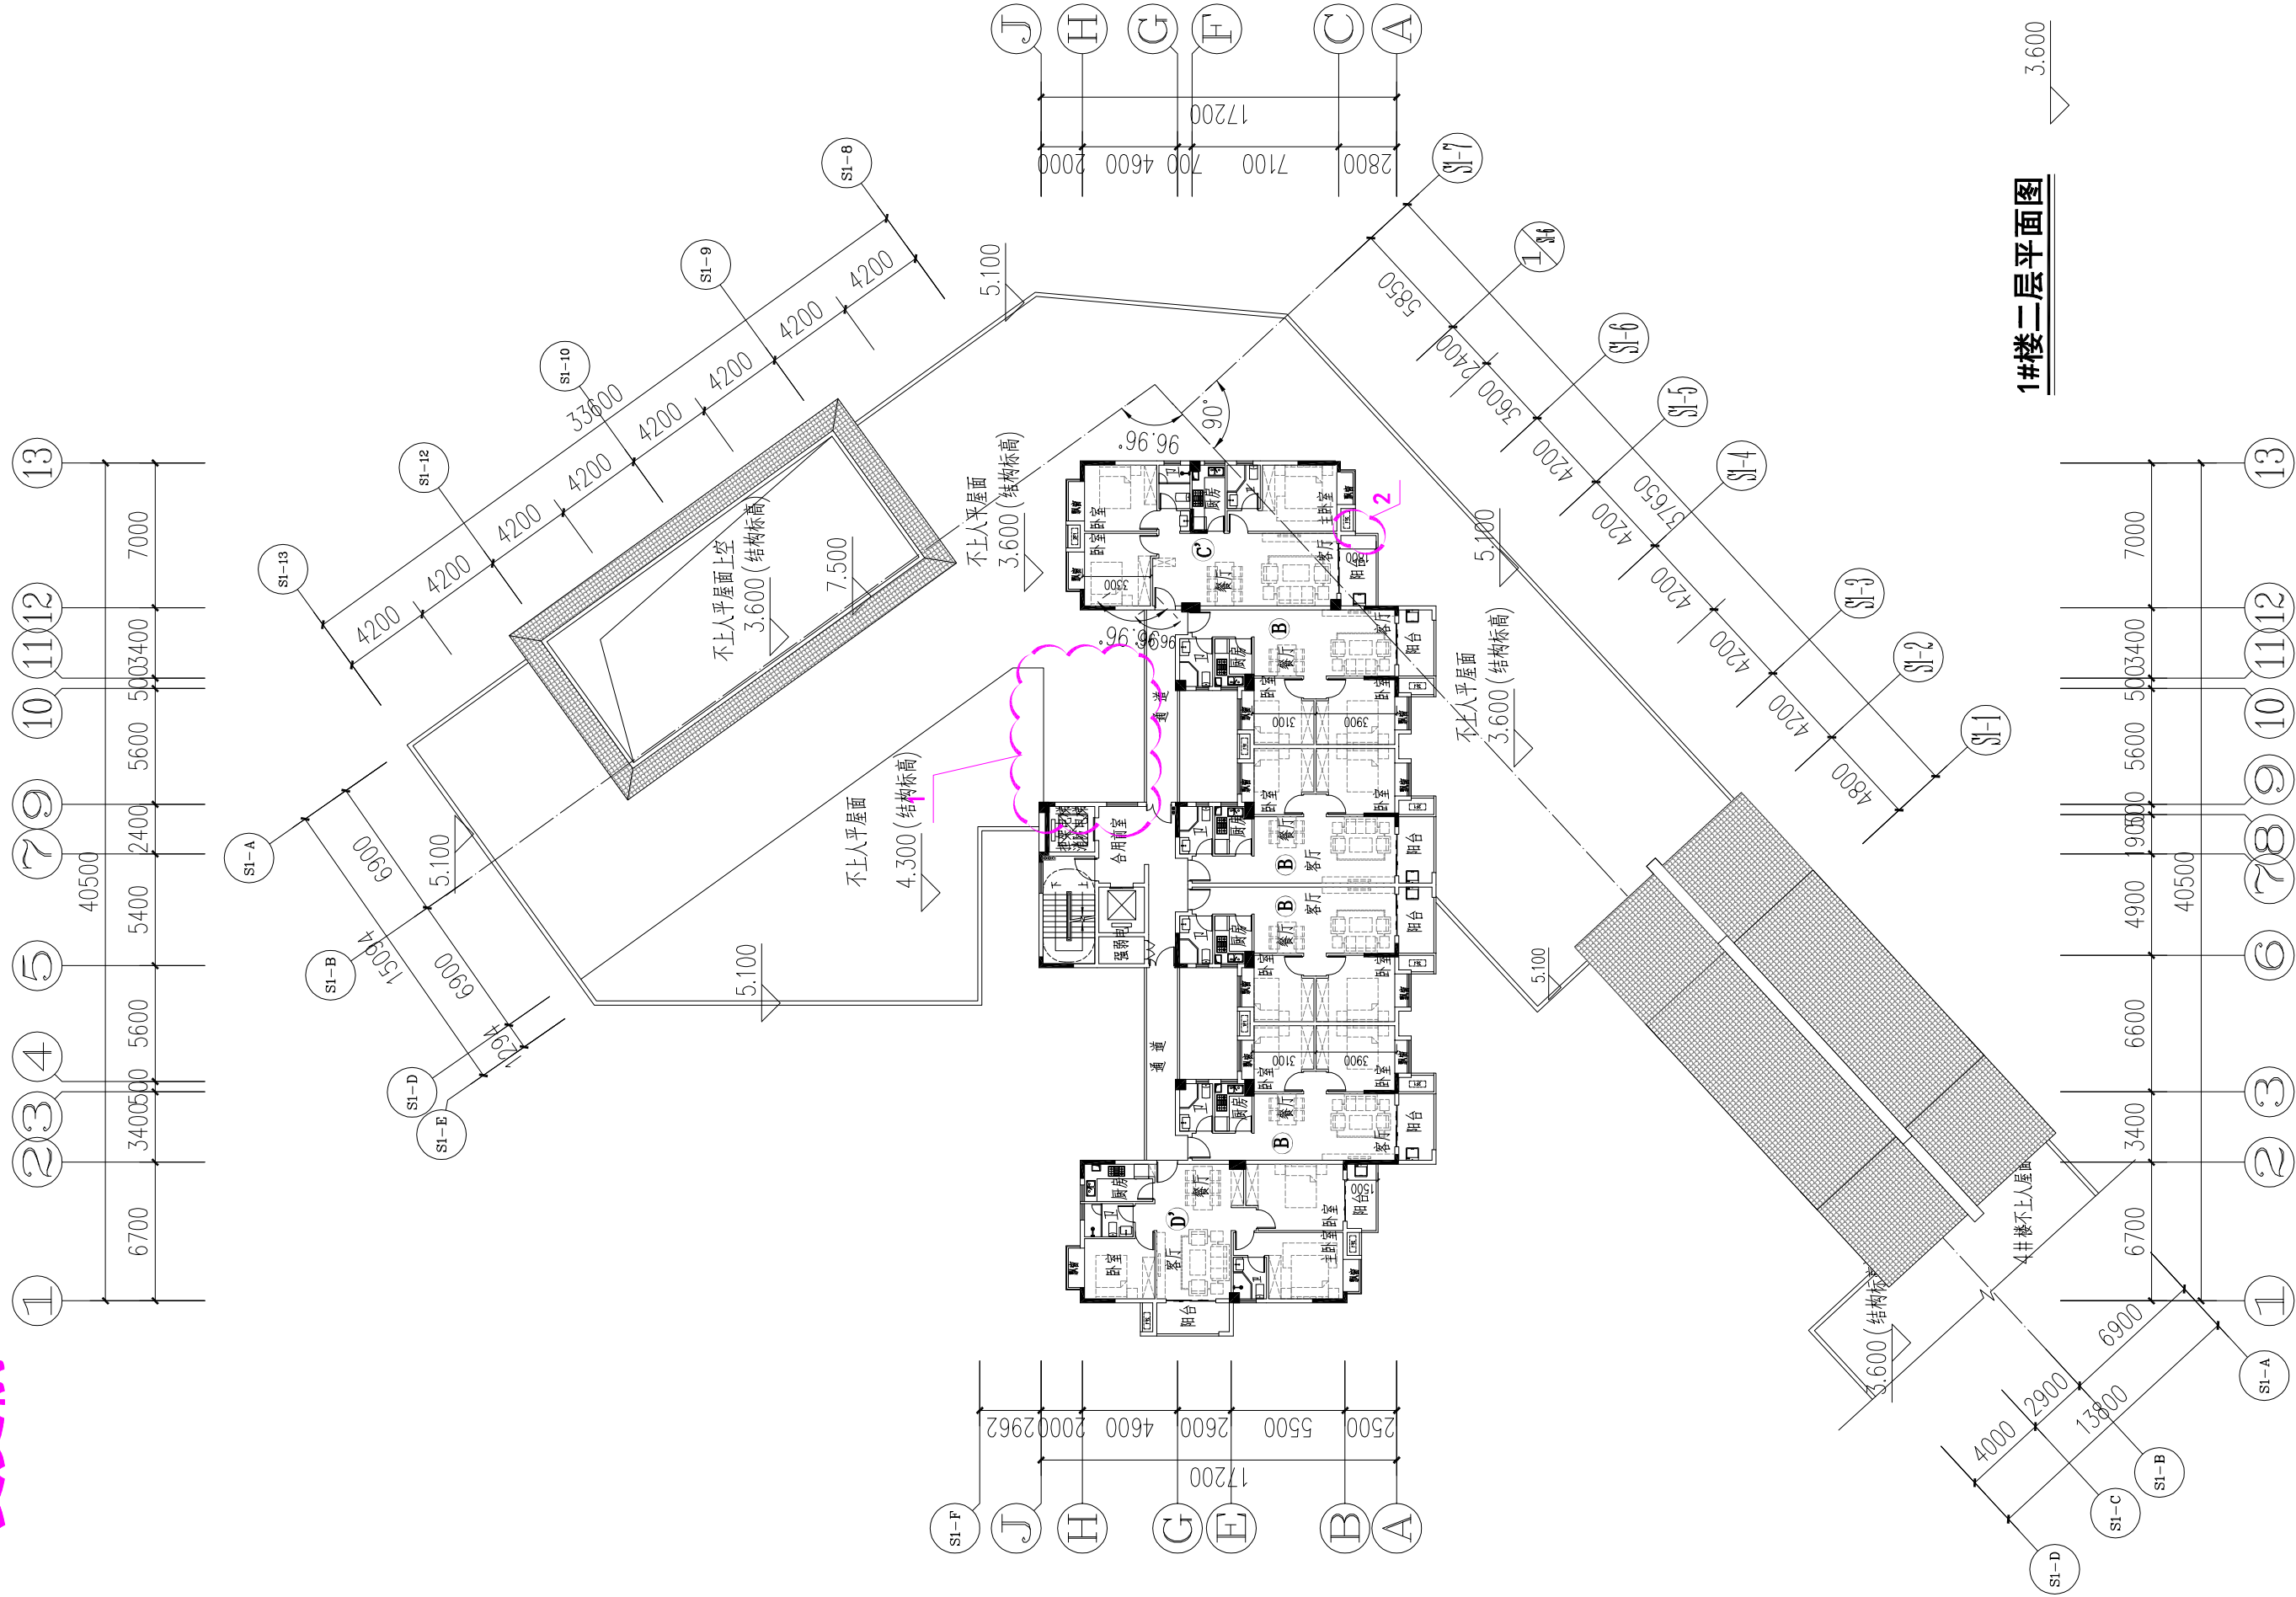


设计单位	福建一建集团有限公司	建设单位	三明市三元区城市建设投资有限责任公司	工程名称	荆东安置房及周边附属配套工程（安置房）	图 名	1#楼二层平面图	图 别	方 案
								日 期	2020. 12

山
東
文


1. 增设上空

2.13轴交A~C轴阳台长度3.5米调整为3.6米

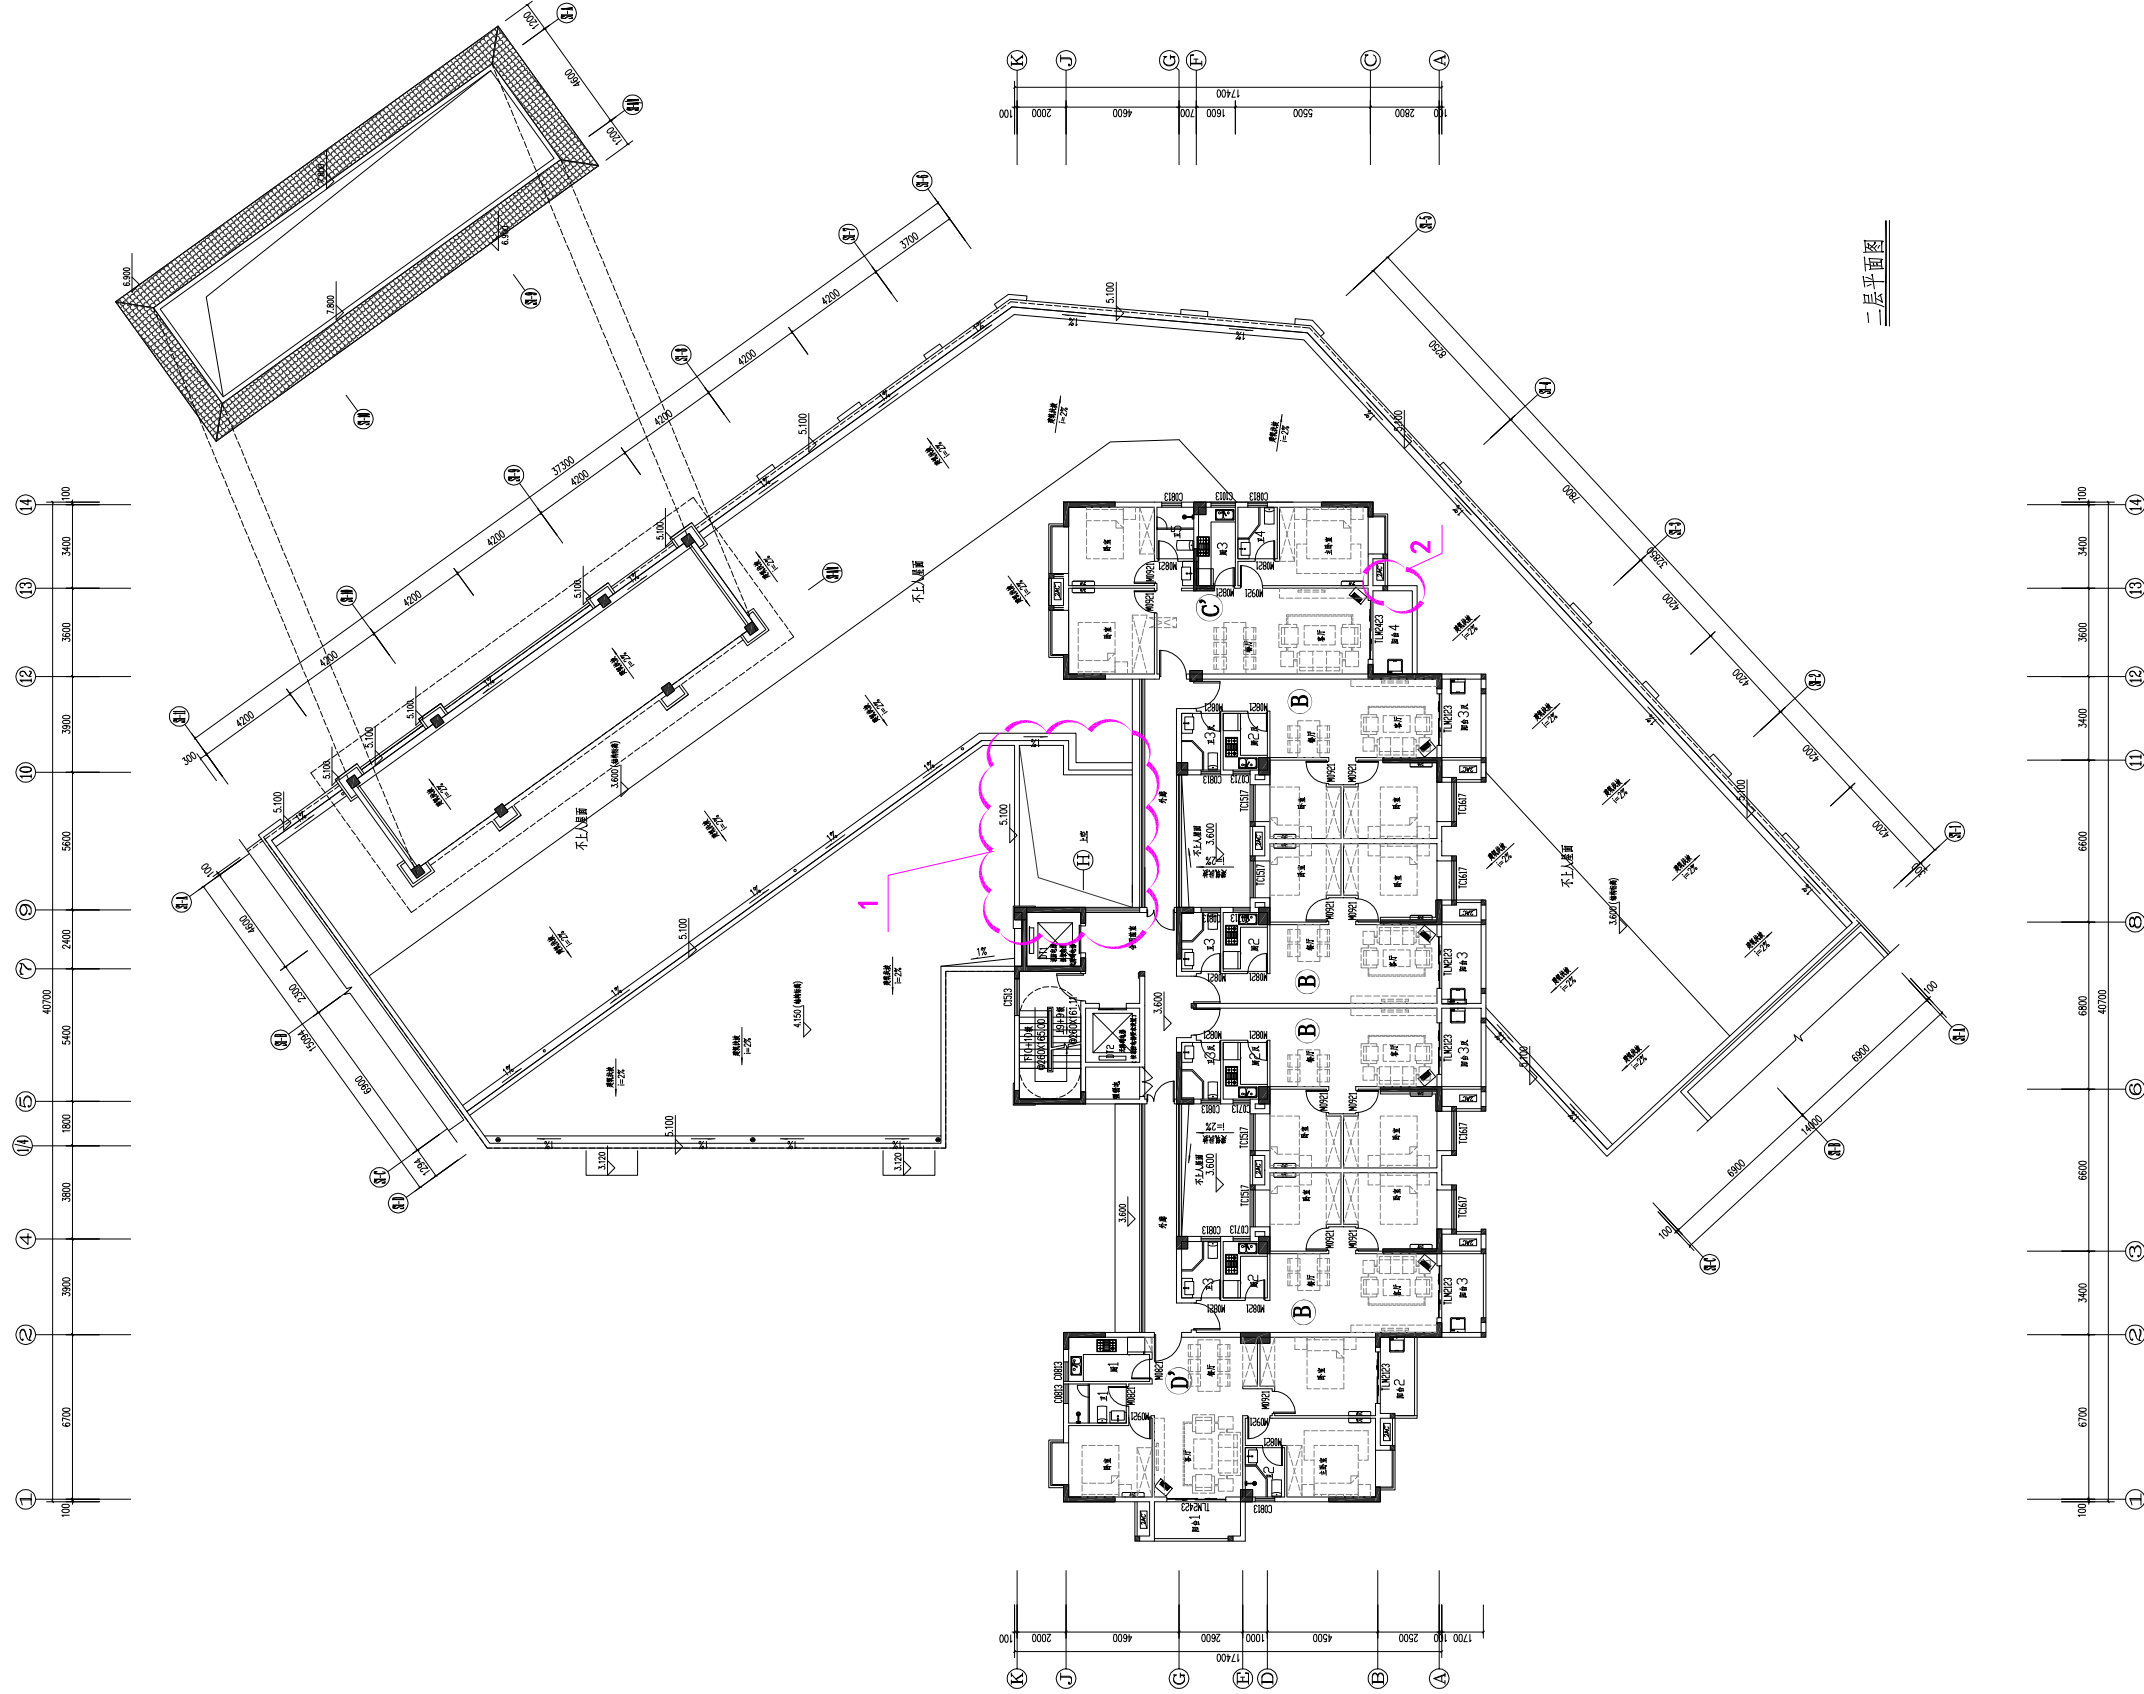


设计单位	福建一建集团有限公司	建设单位	三明市三元区城市建设投资有限责任公司	工程名称	荆东安置房及周边附属配套工程（安置房）	图 名	1#楼二层平面图	图 别	方 案
								日 期	2023. 07

变更前

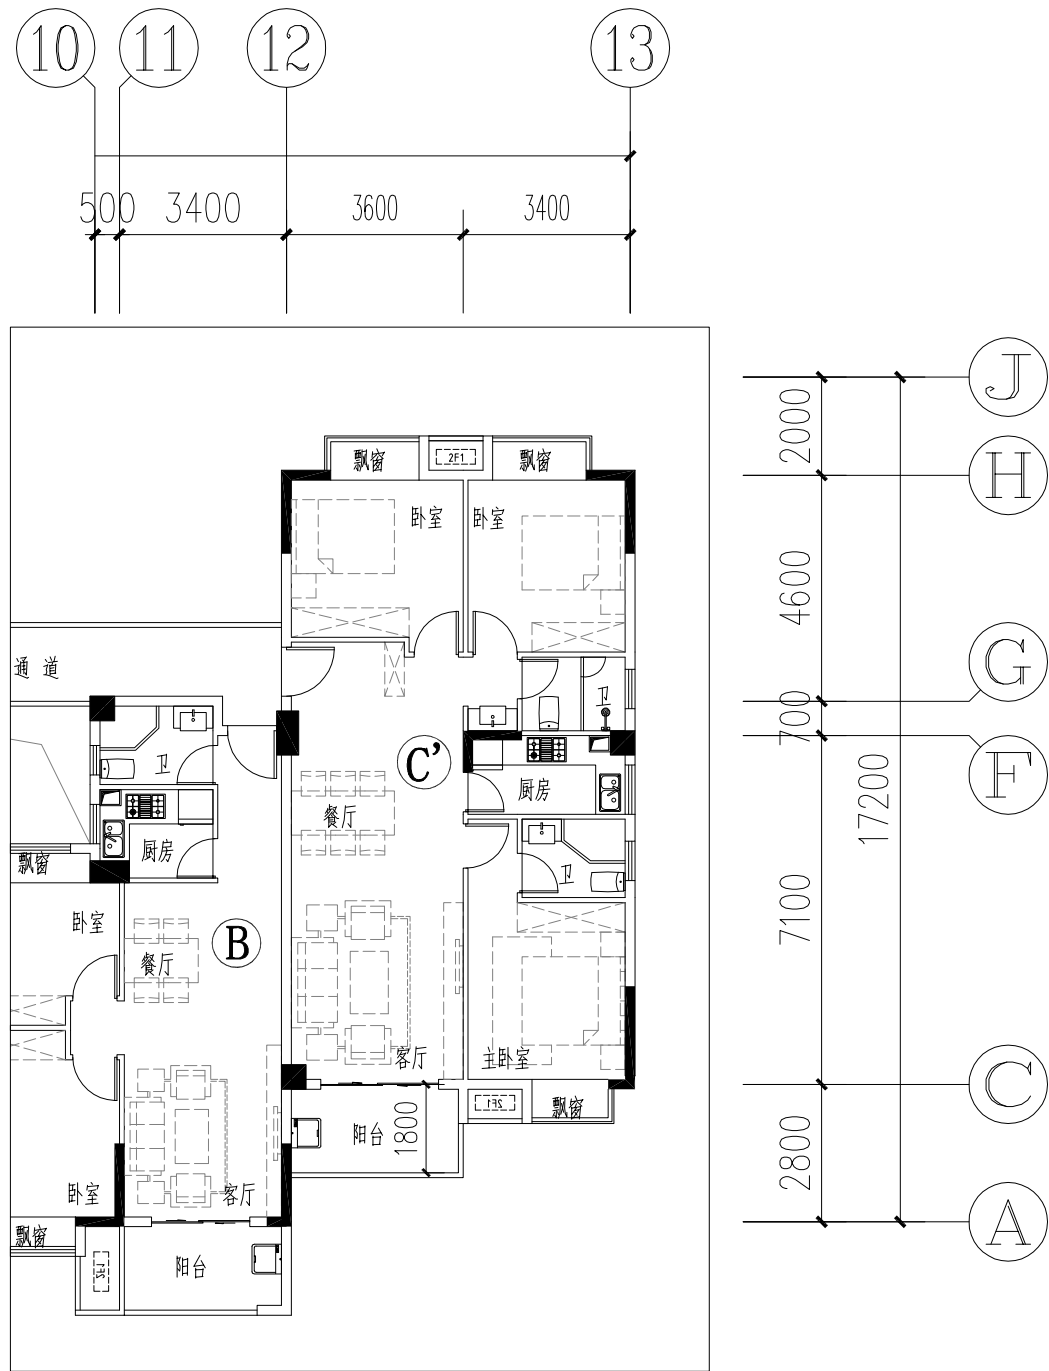

1#楼三~十八层平面图

变更后

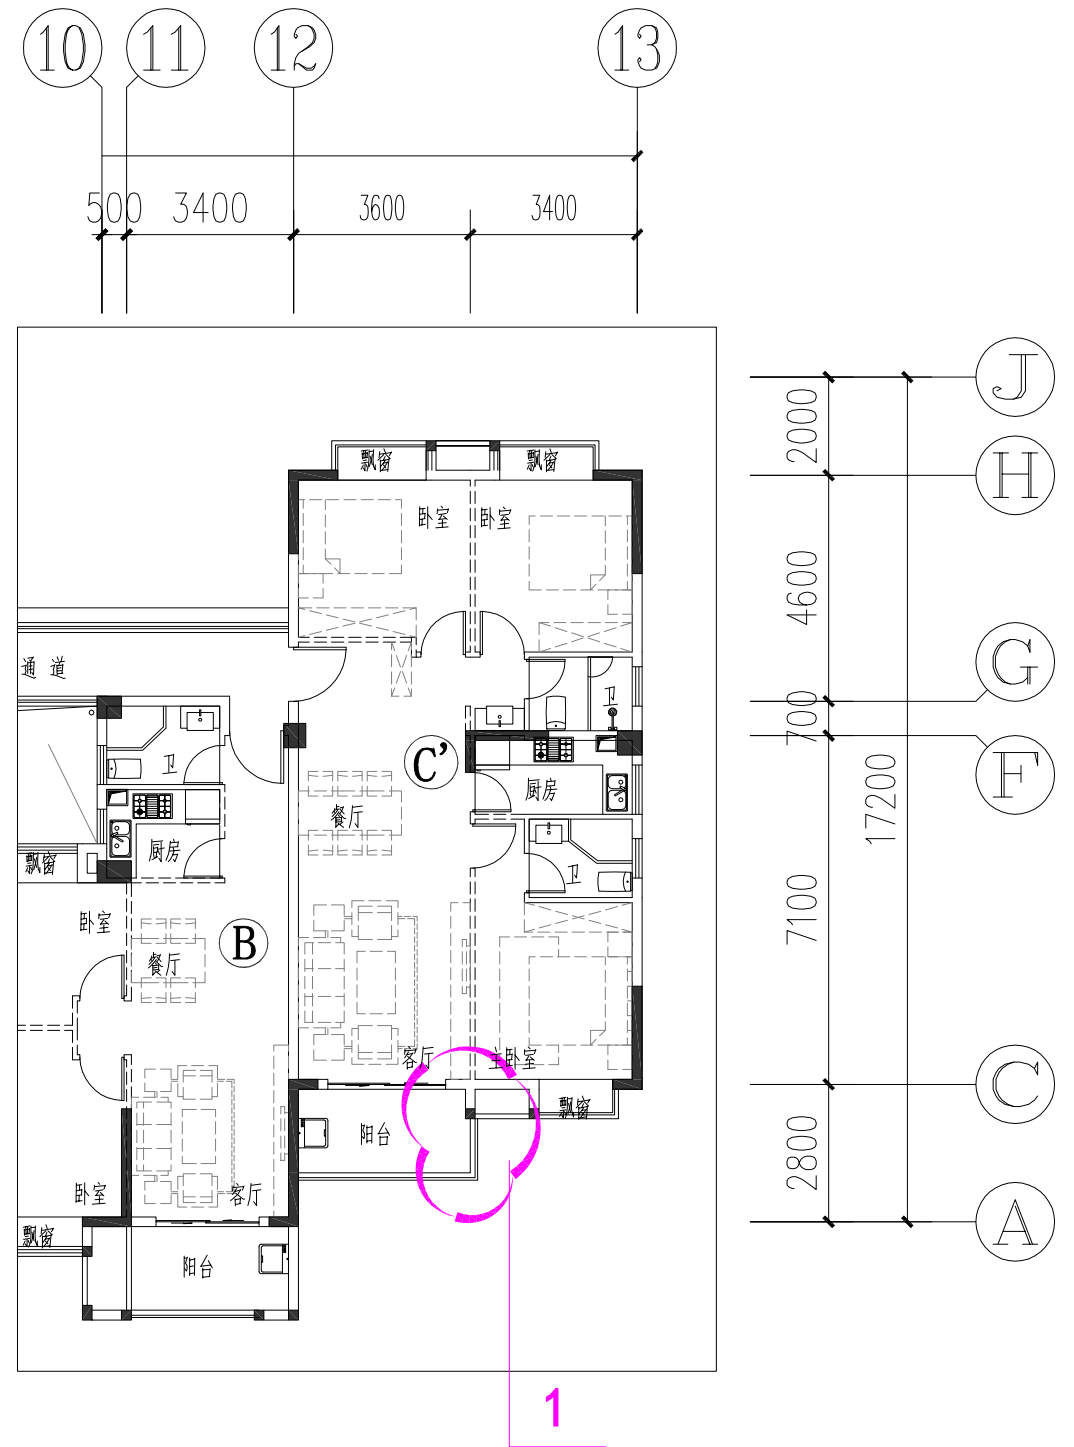


1#楼三~十八层平面图

1. 三至十八层13轴交A~C轴阳台长度3.5米调整为3.6米


[illegible]

变更前

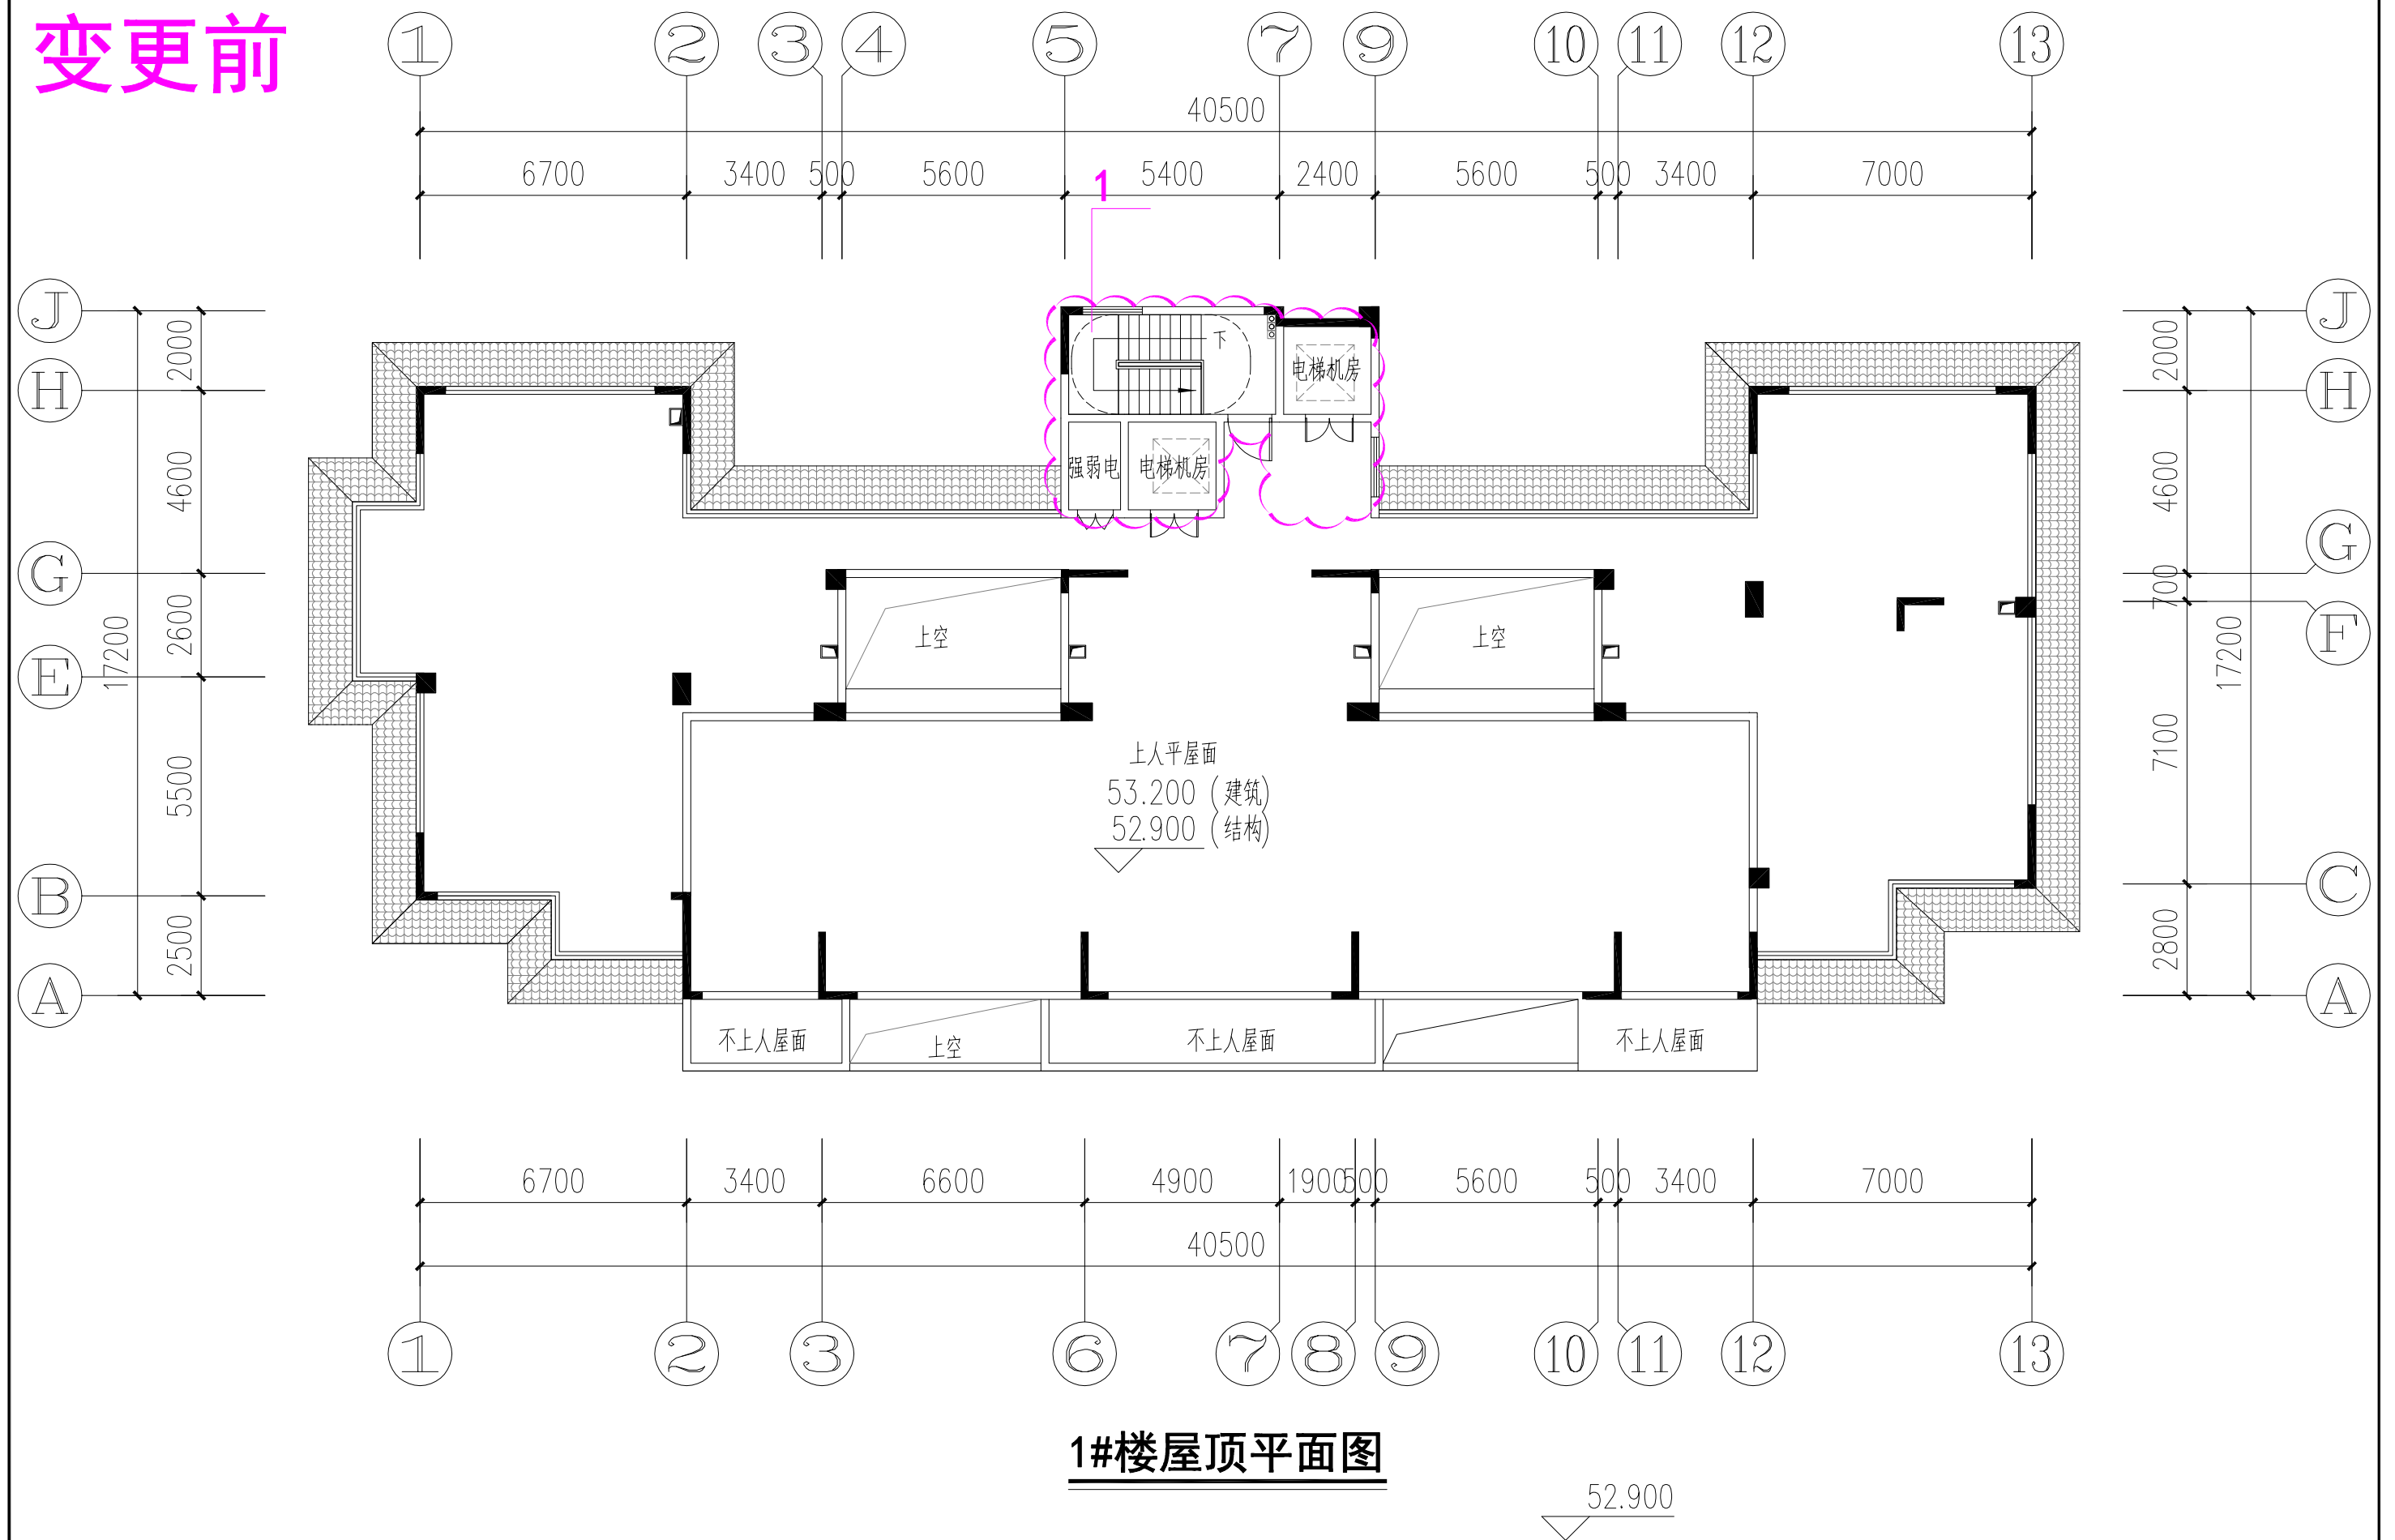

设计单位	福建一建集团有限公司	建设单位	三明市三元区城市建设投资有限责任公司	工程名称	荆东安置房及周边附属配套工程（安置房）	图 名	1#楼屋顶平面图	图 别	方 案
								日 期	2020. 12

变更后

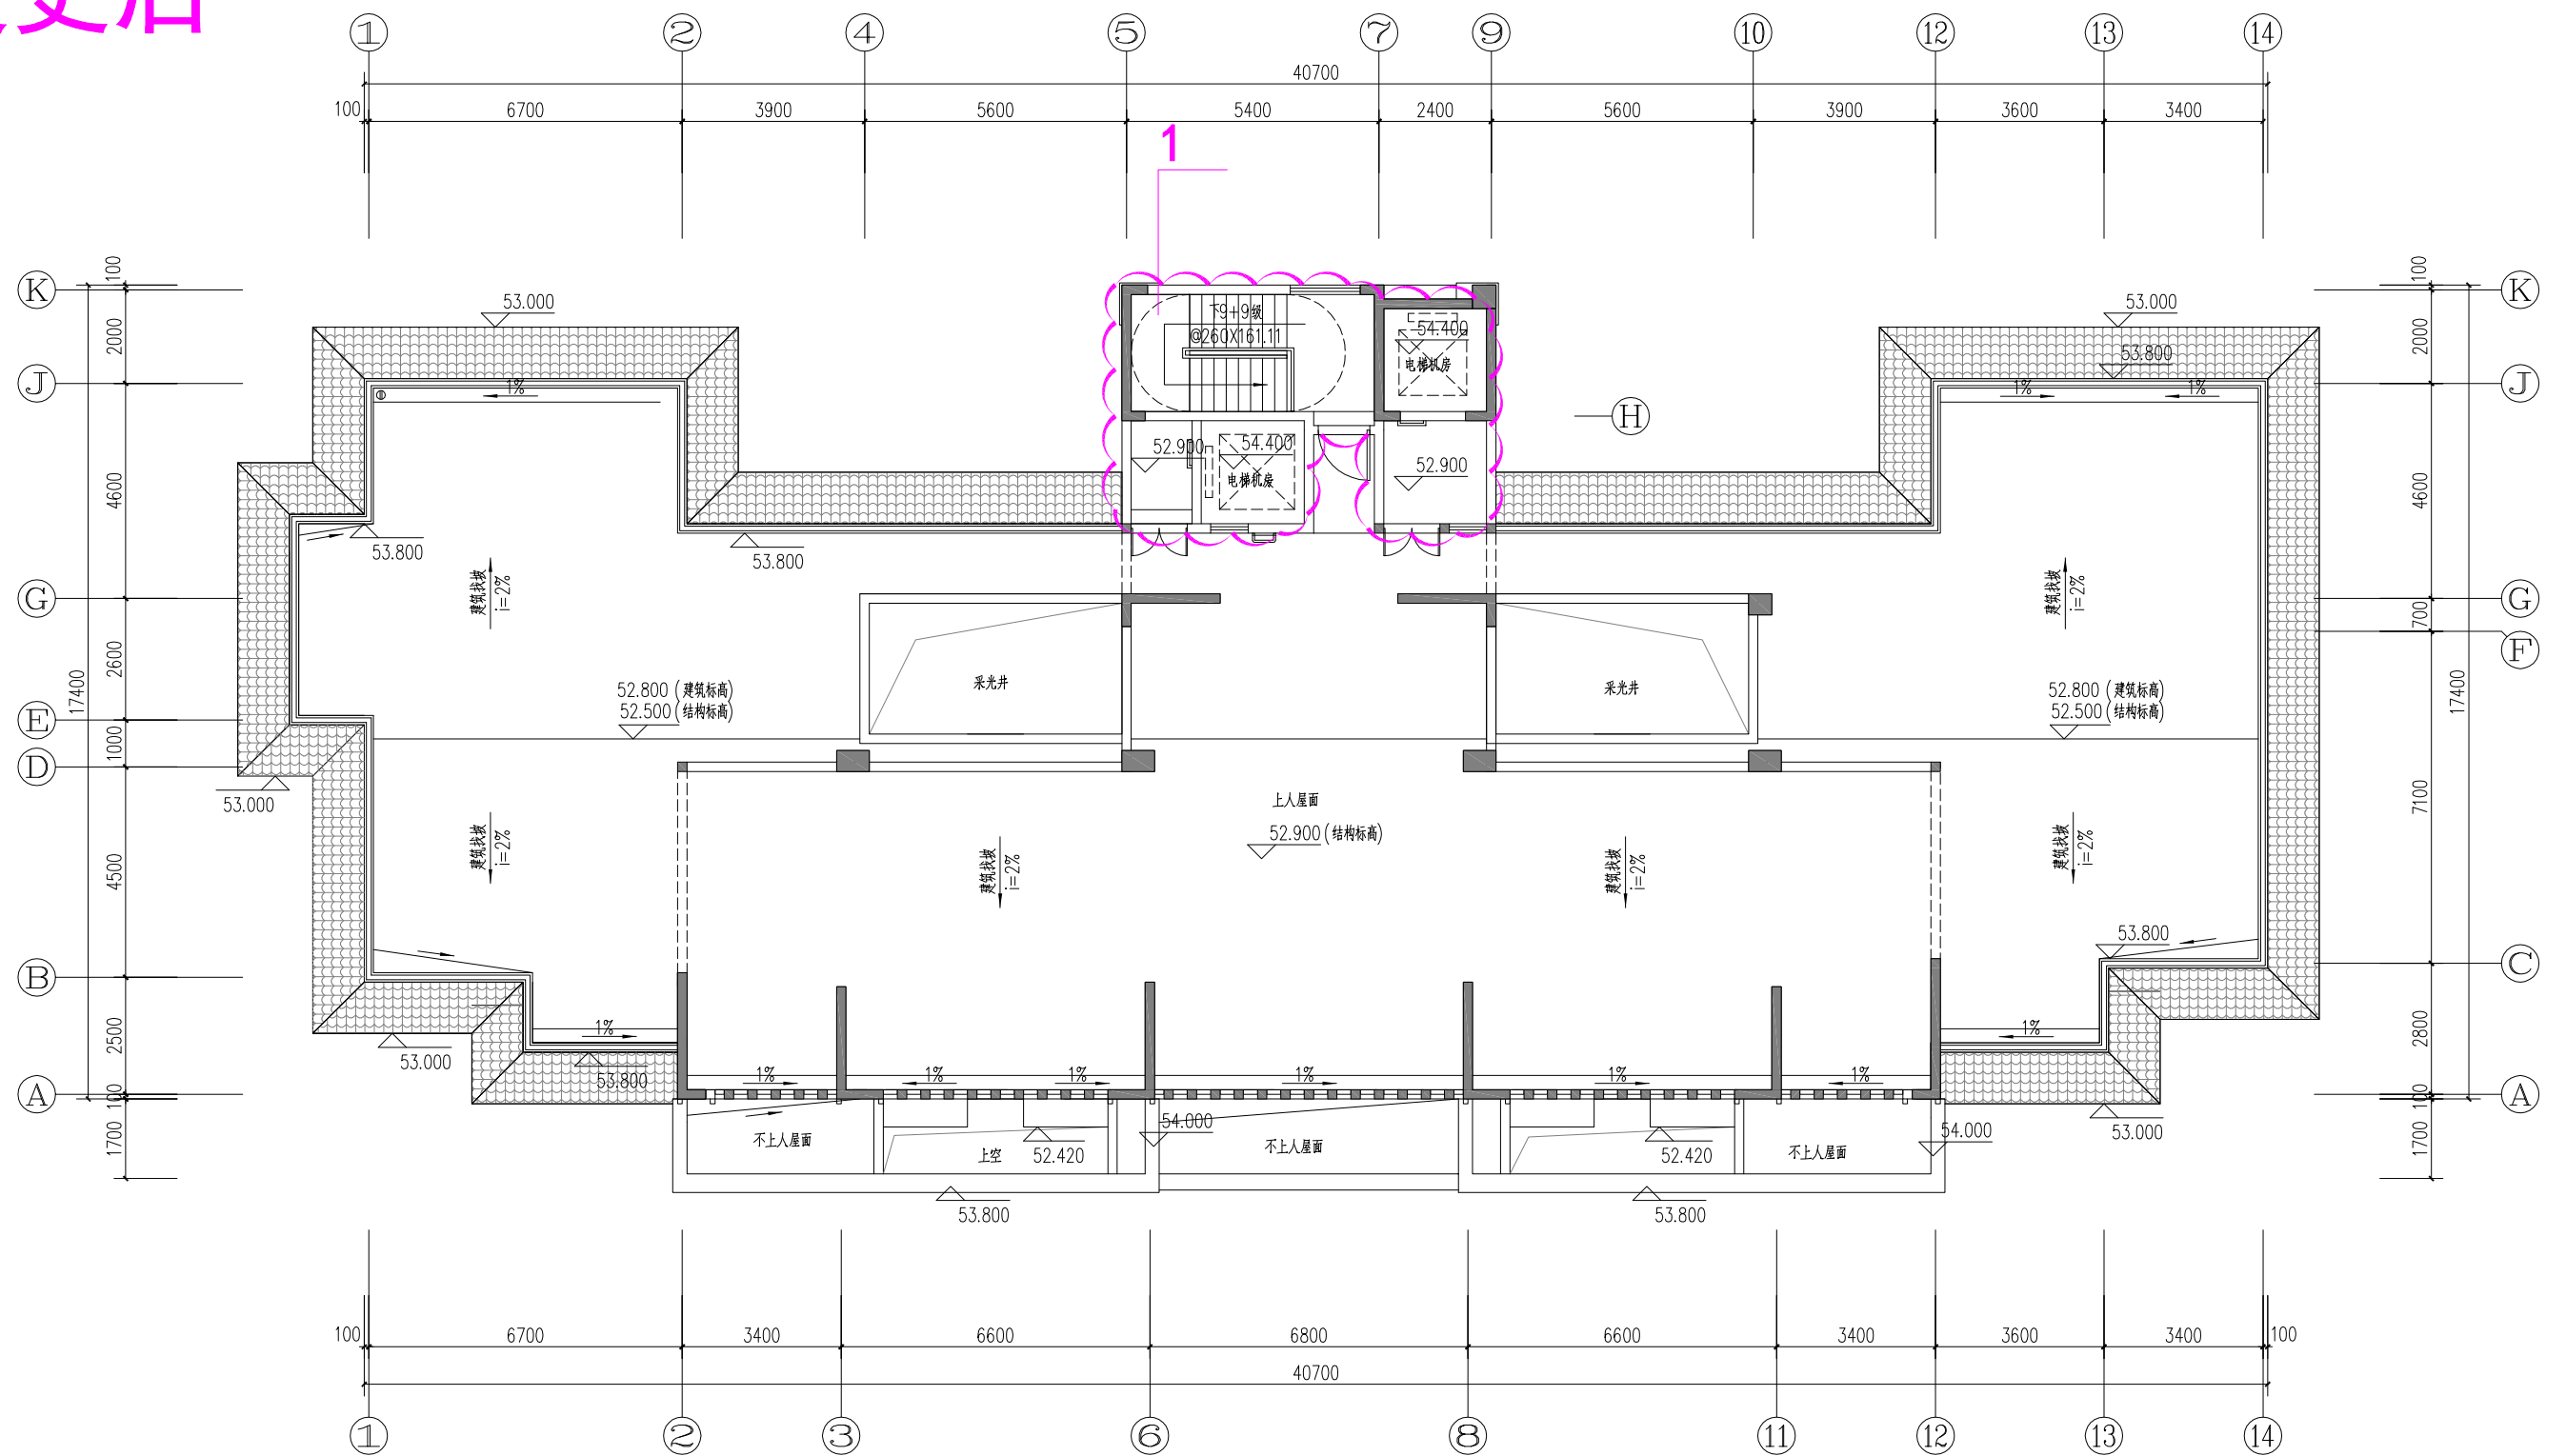


1#楼屋顶平面图

1. 电梯机房调整, 强弱电井取消

[illegible]


变更前

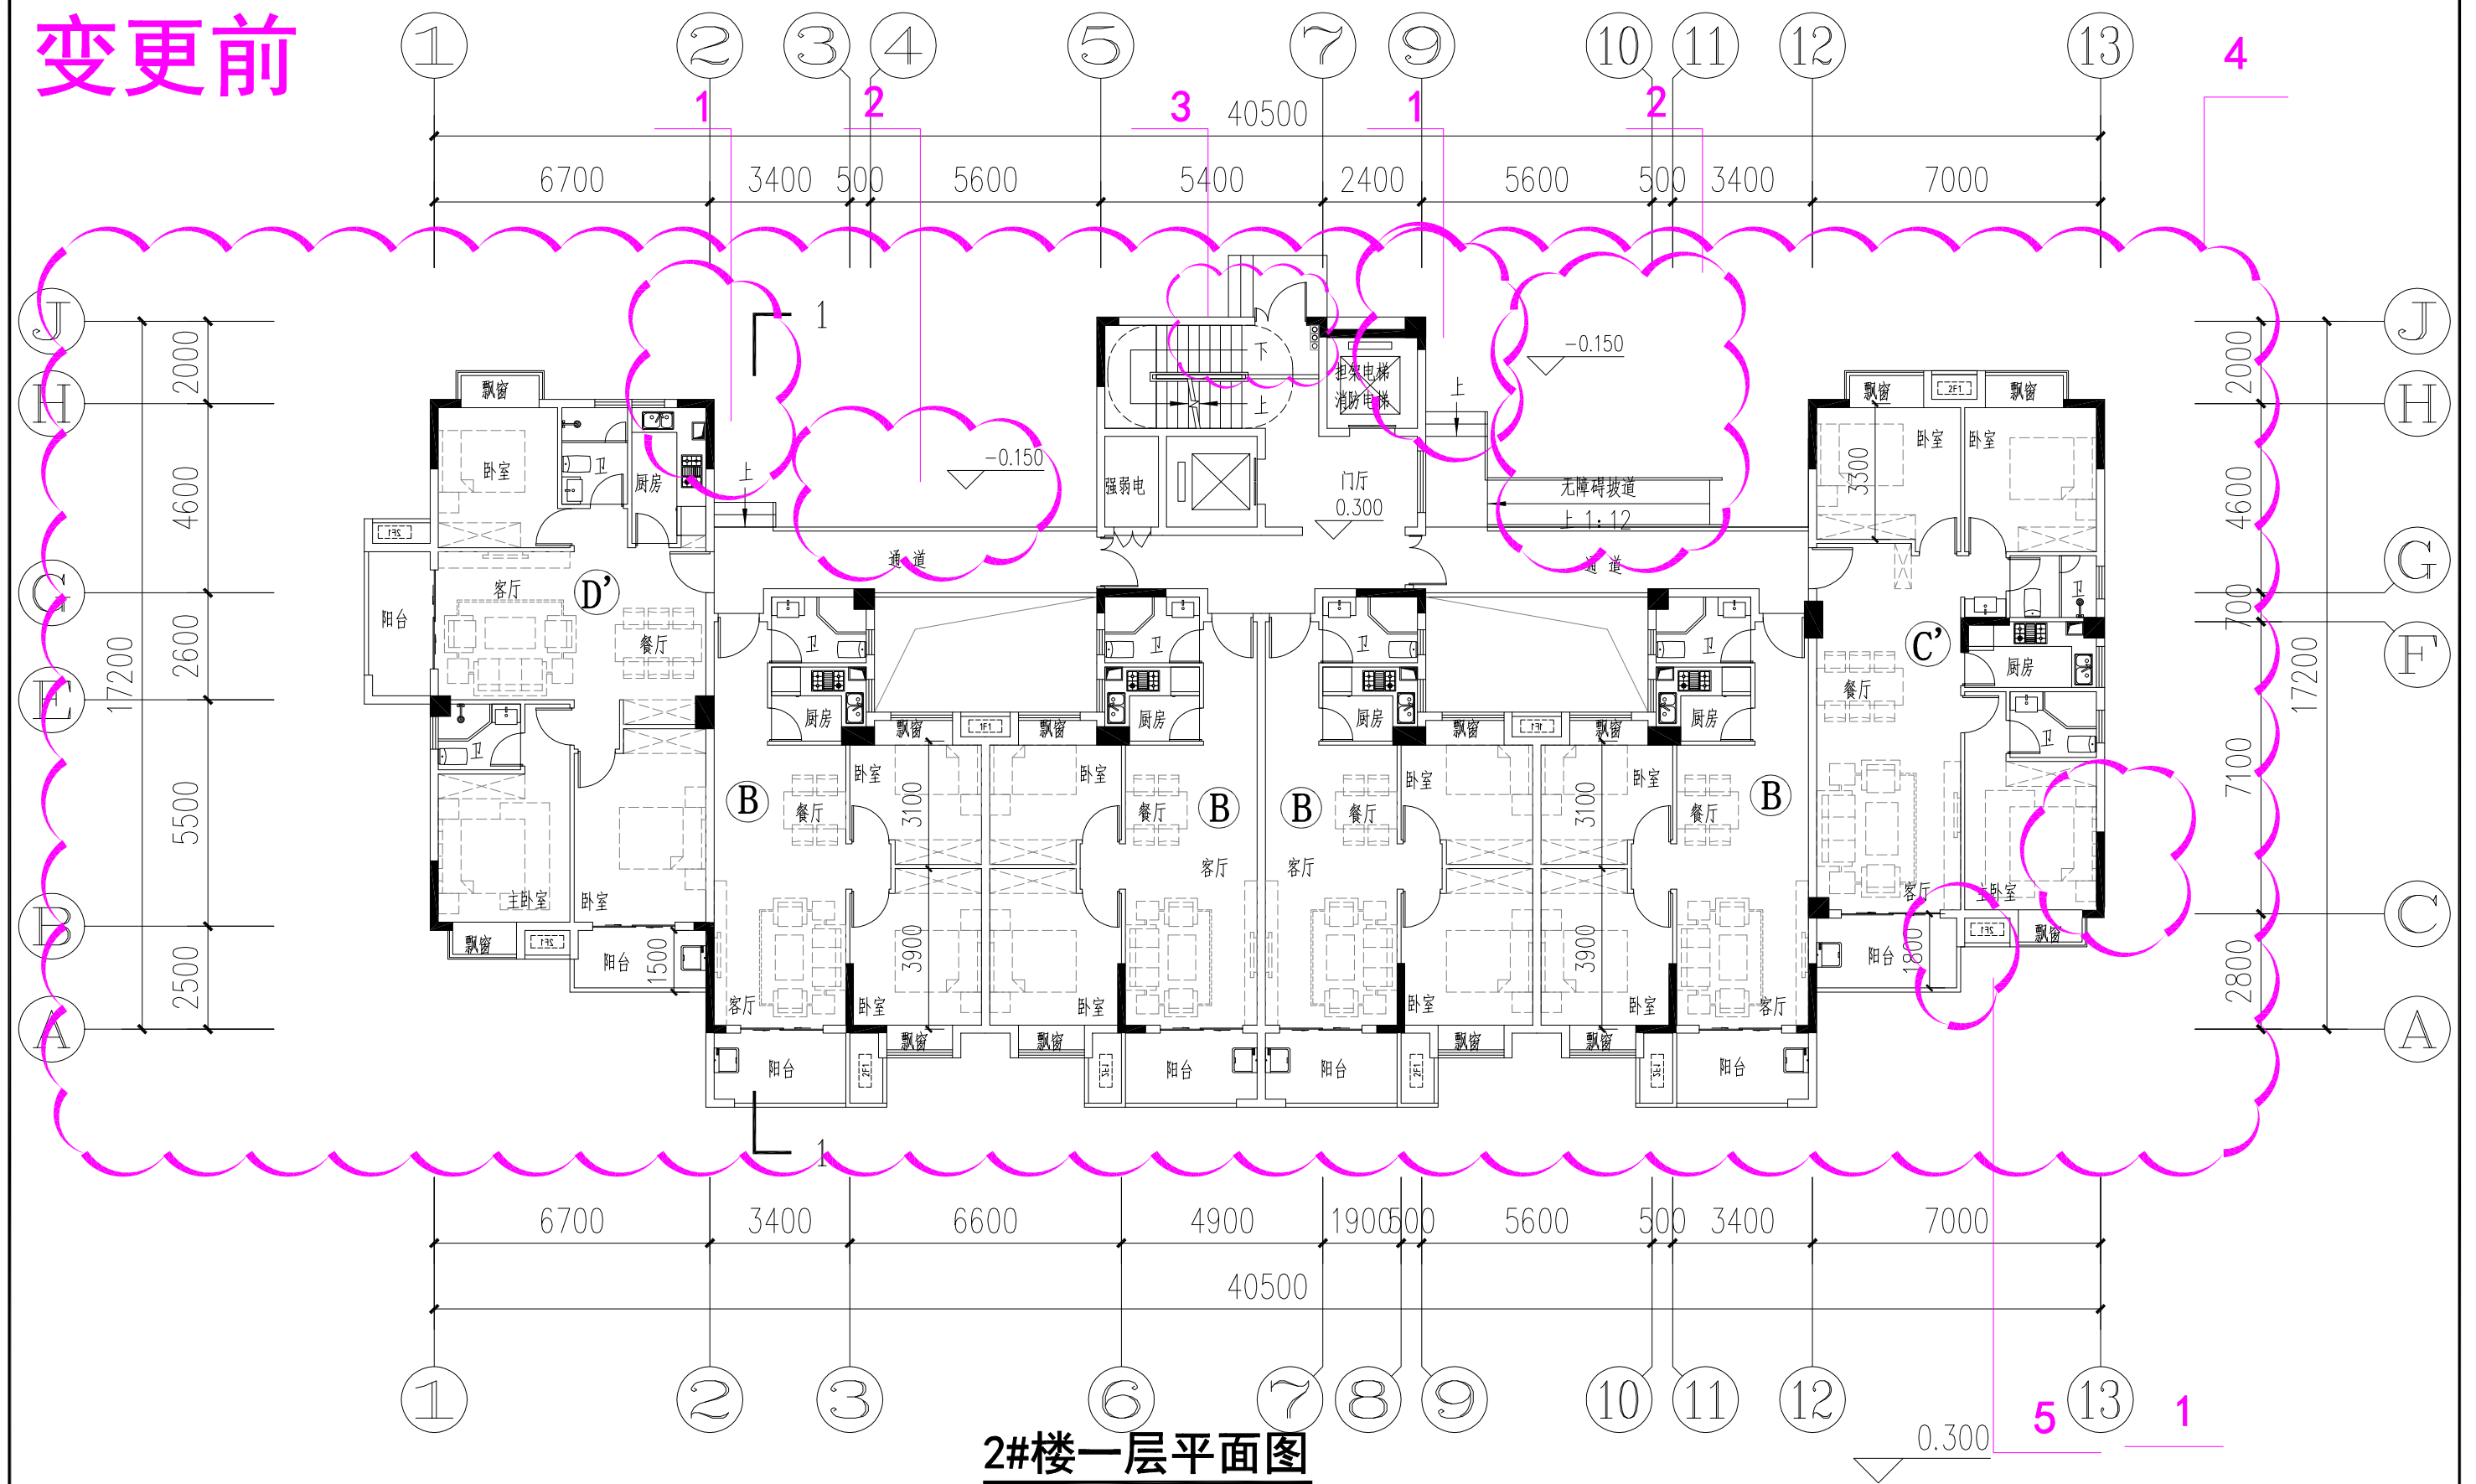

2#楼一层平面图

[illegible]

变更后

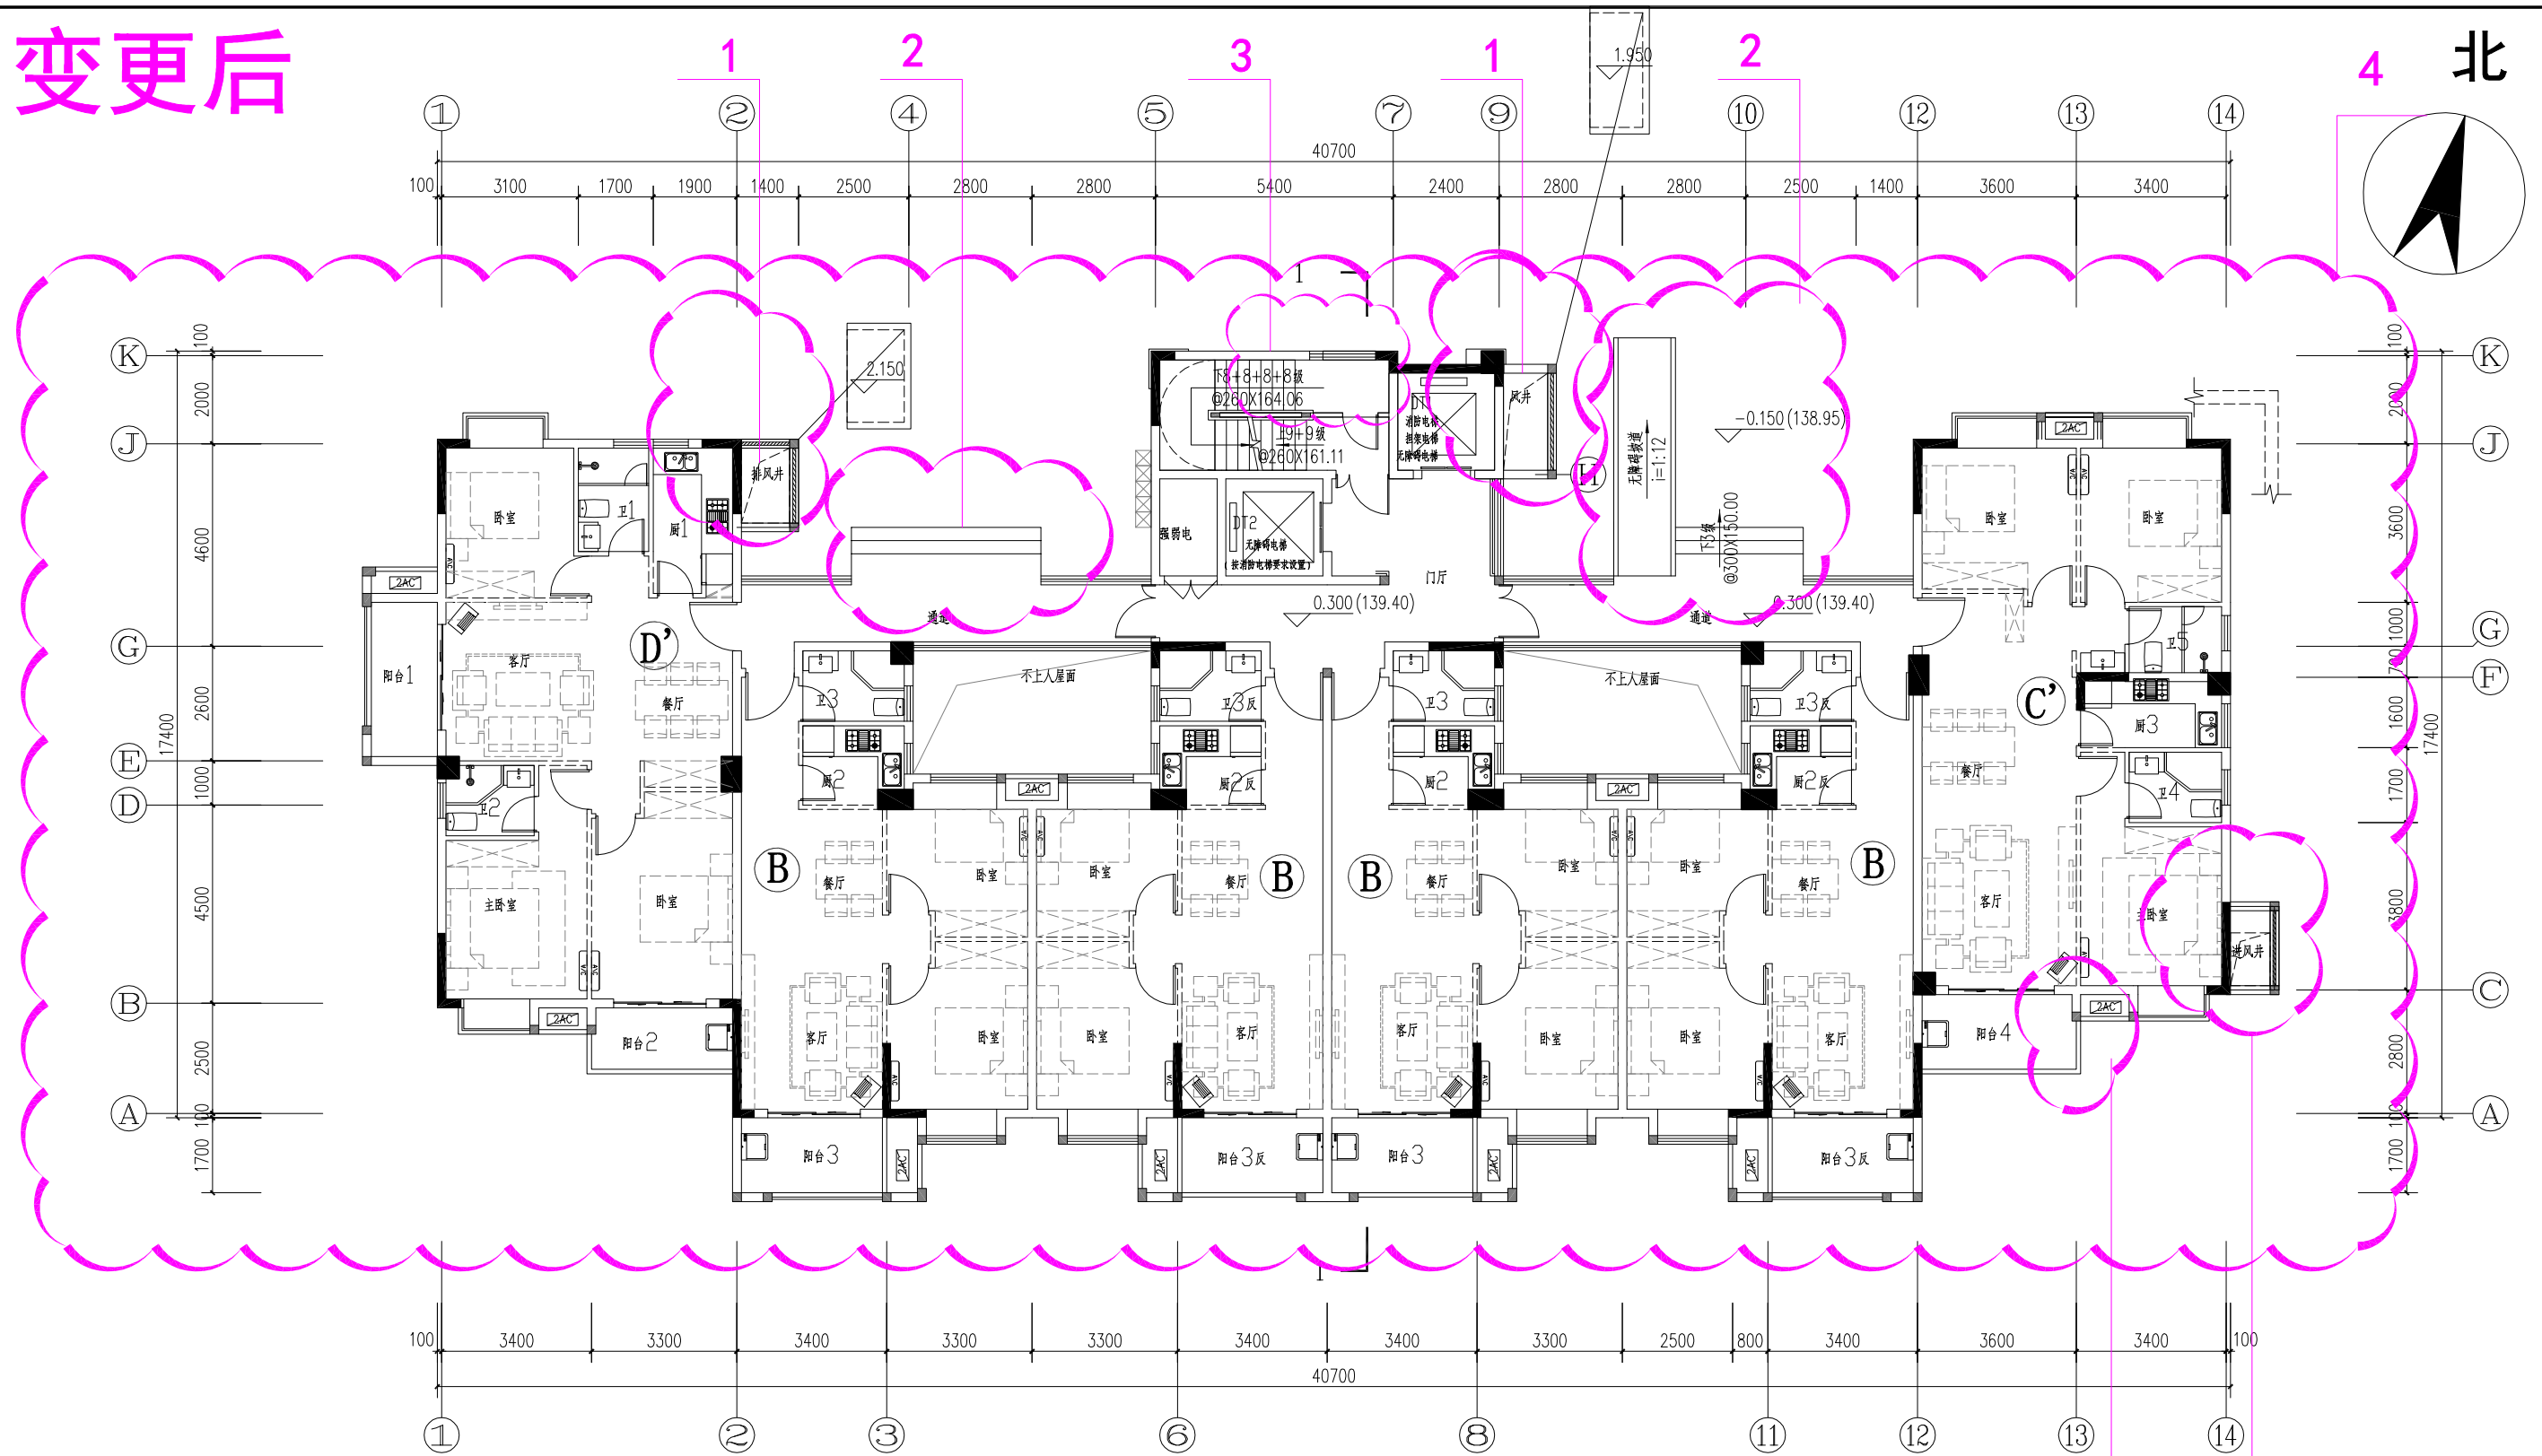


1. 增设排风井、风井、进风井
2. 无障碍坡道及室外台阶位置调整
3. 取消对外开门
4. 一至屋顶层柱网整体调整
5. 13轴交A~C轴阳台长度3.5米调整为3.6米

2#楼一层平面图

设计单位	福建一建集团有限公司	建设单位	三明市三元区城市建设投资有限责任公司	工程名称	荆东安置房及周边附属配套工程（安置房）	图 名	2#楼一层平面图	图 别	方 案
								日 期	2023. 07


变更前

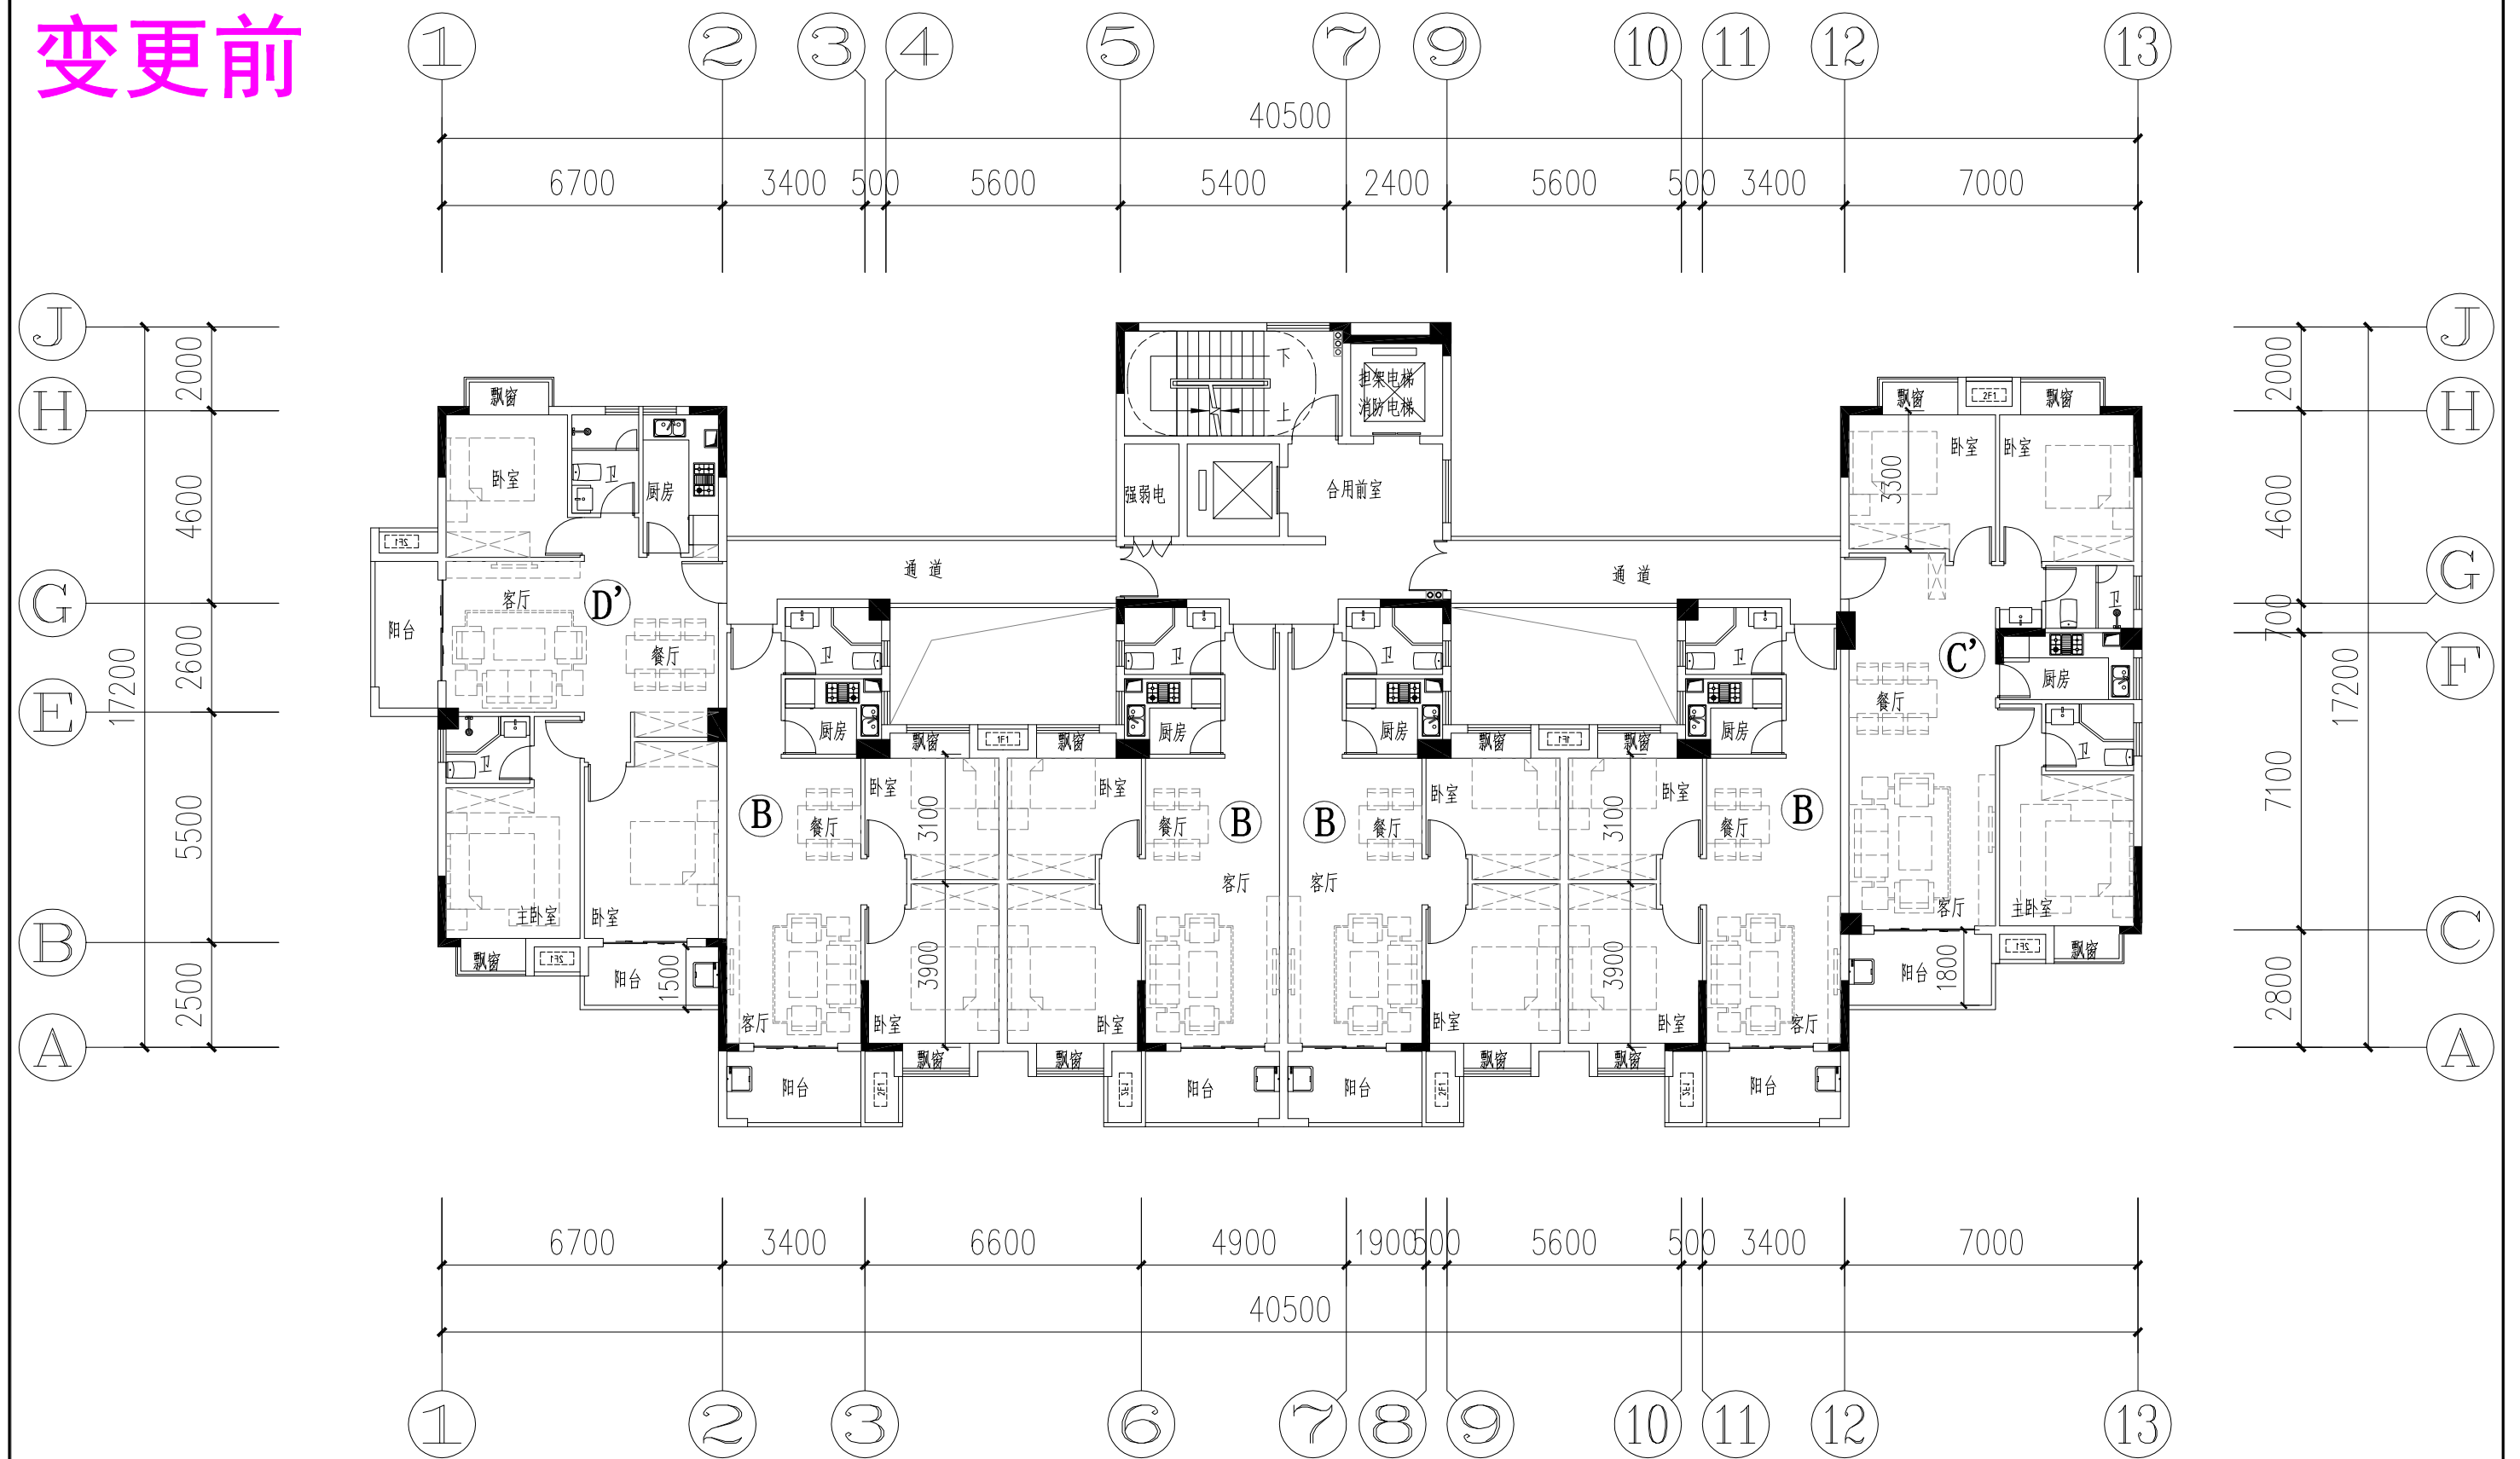

2#楼二~十八层平面图

设计单位	福建一建集团有限公司	建设单位	三明市三元区城市建设投资有限责任公司	工程名称	荆东安置房及周边附属配套工程（安置房）	图 名	2#楼二~十八层平面图	图 别	方 案
								日 期	2020. 12

变更后

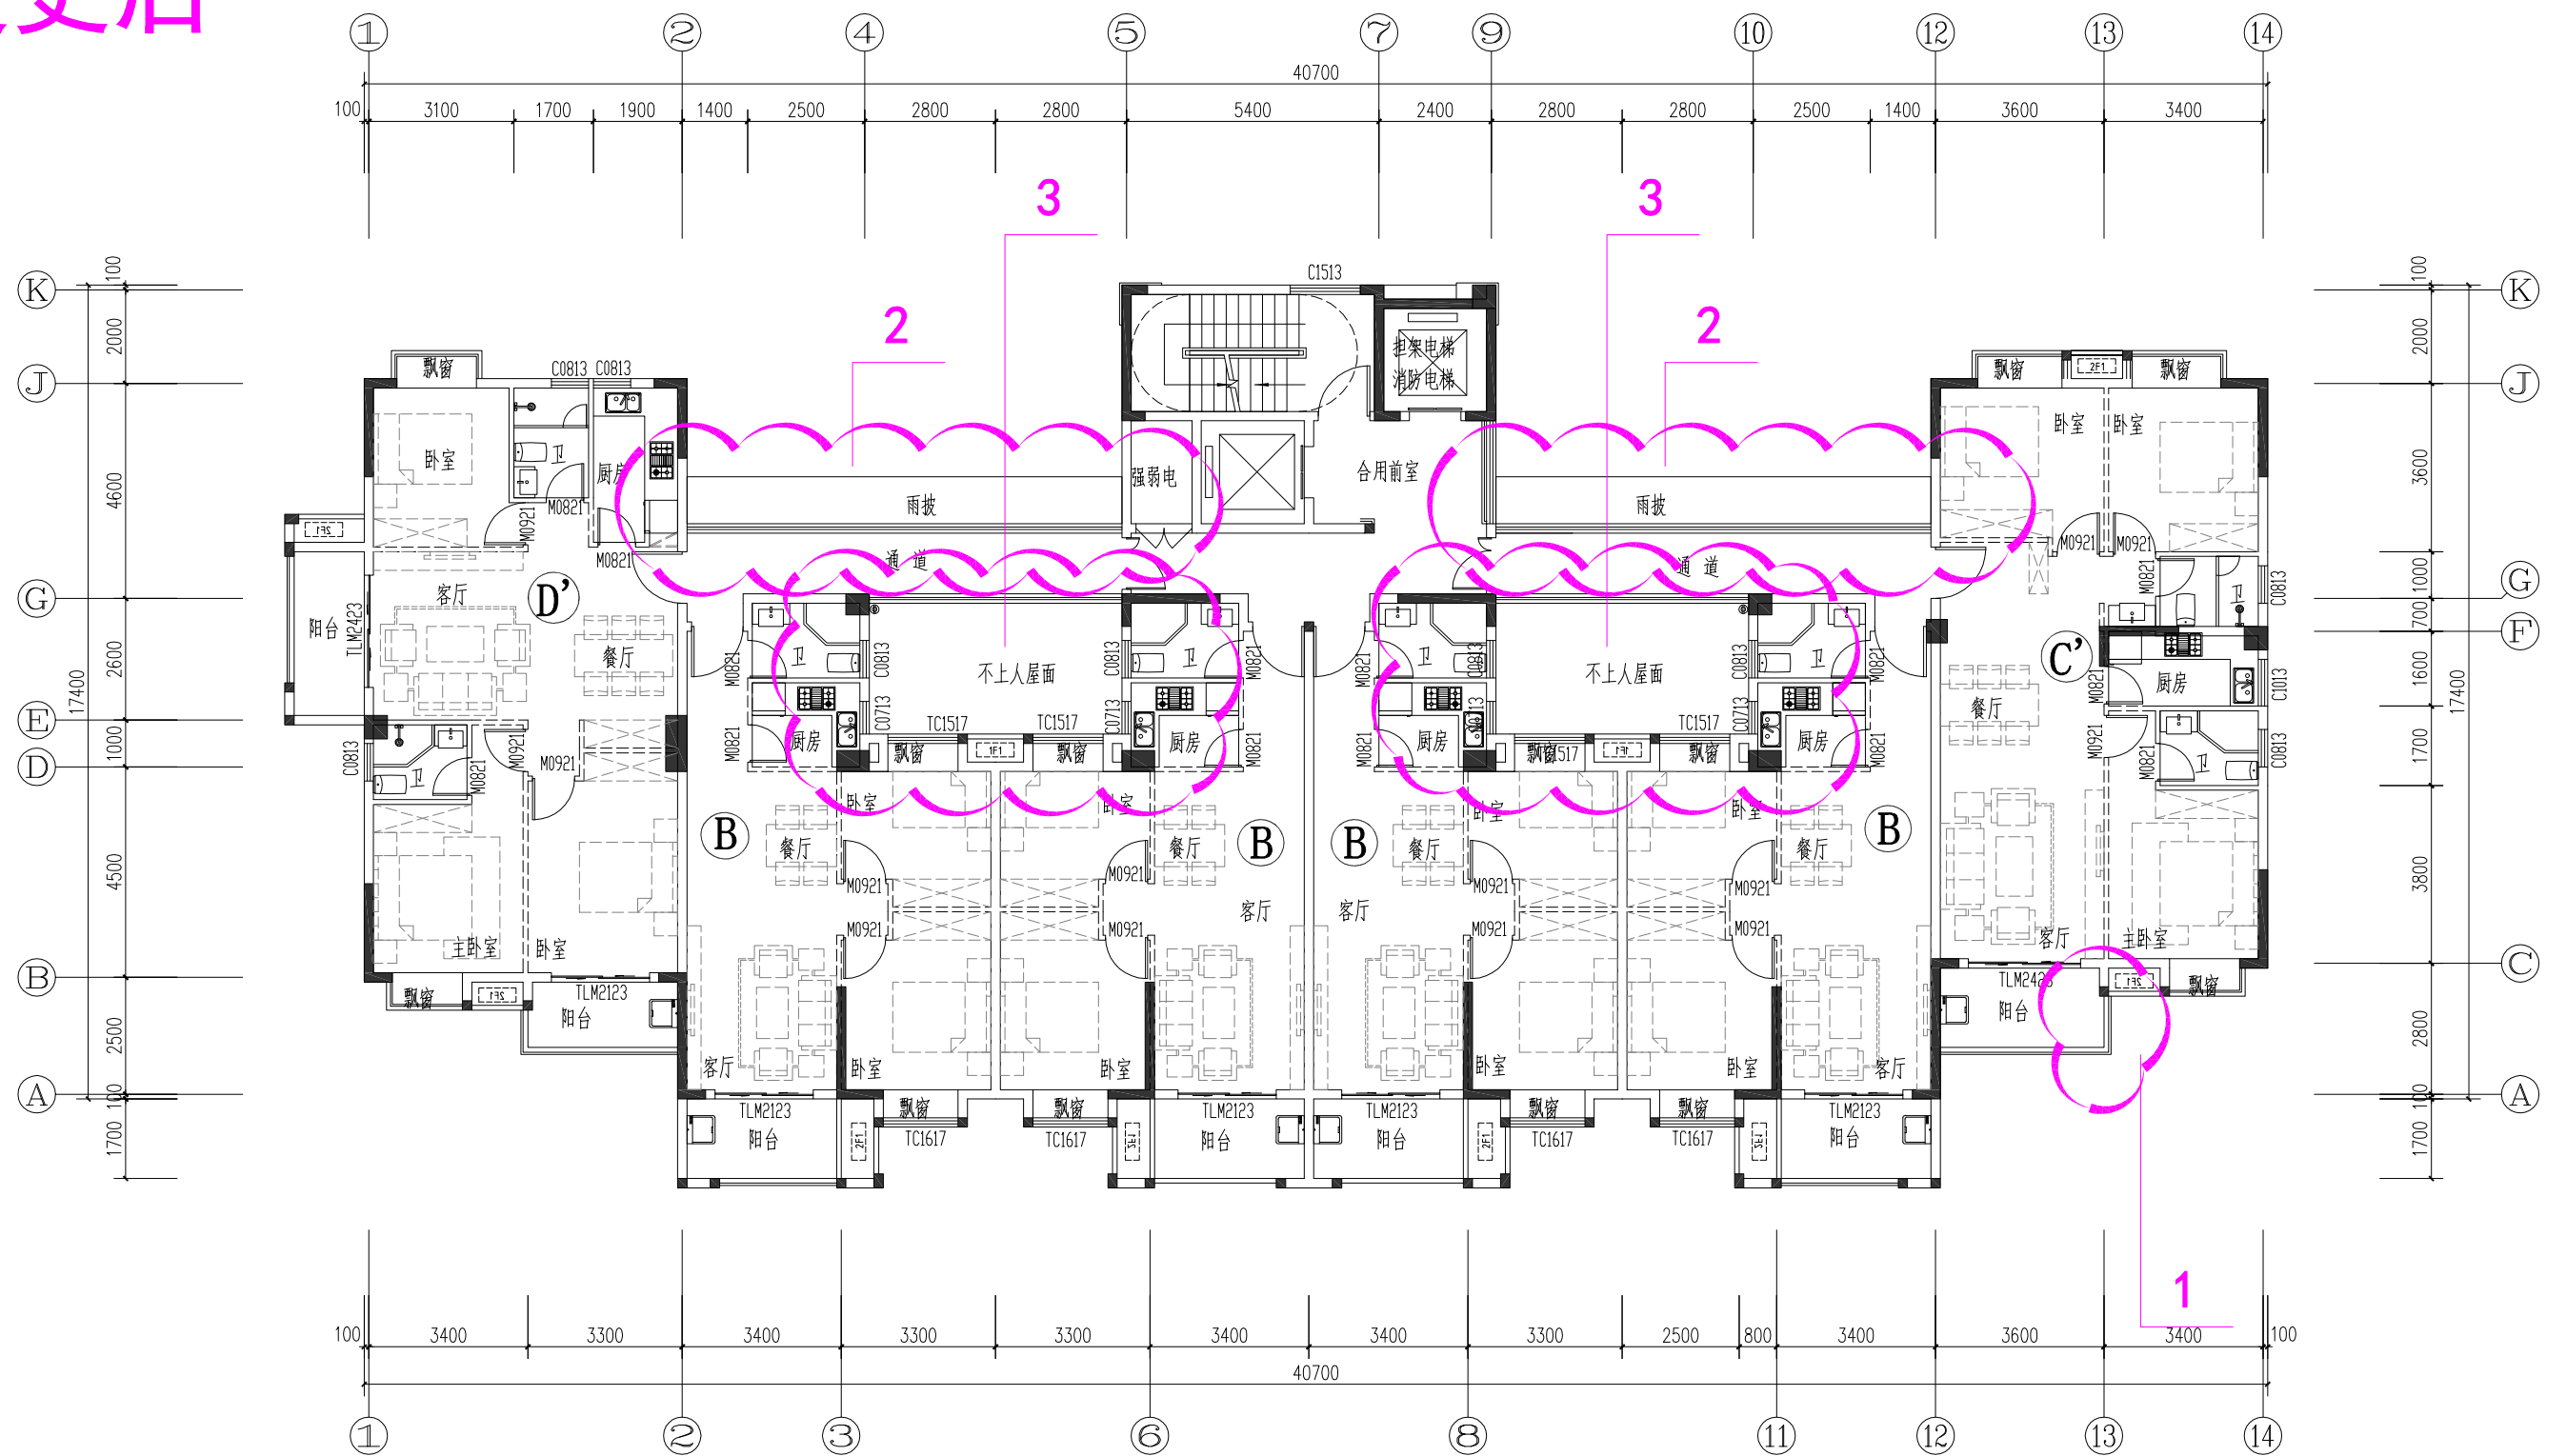


1. 13轴交A~C轴阳台长度3.5米调整为3.6米
2. 新增雨披
3. 采光井调整为不上人屋面

2#楼二层平面图


设计单位	福建一建集团有限公司	建设单位	三明市三元区城市建设投资有限责任公司	工程名称	荆东安置房及周边附属配套工程（安置房）	图 名	2#楼二层平面图	图 别	方 案
								日 期	2023. 07

变更前

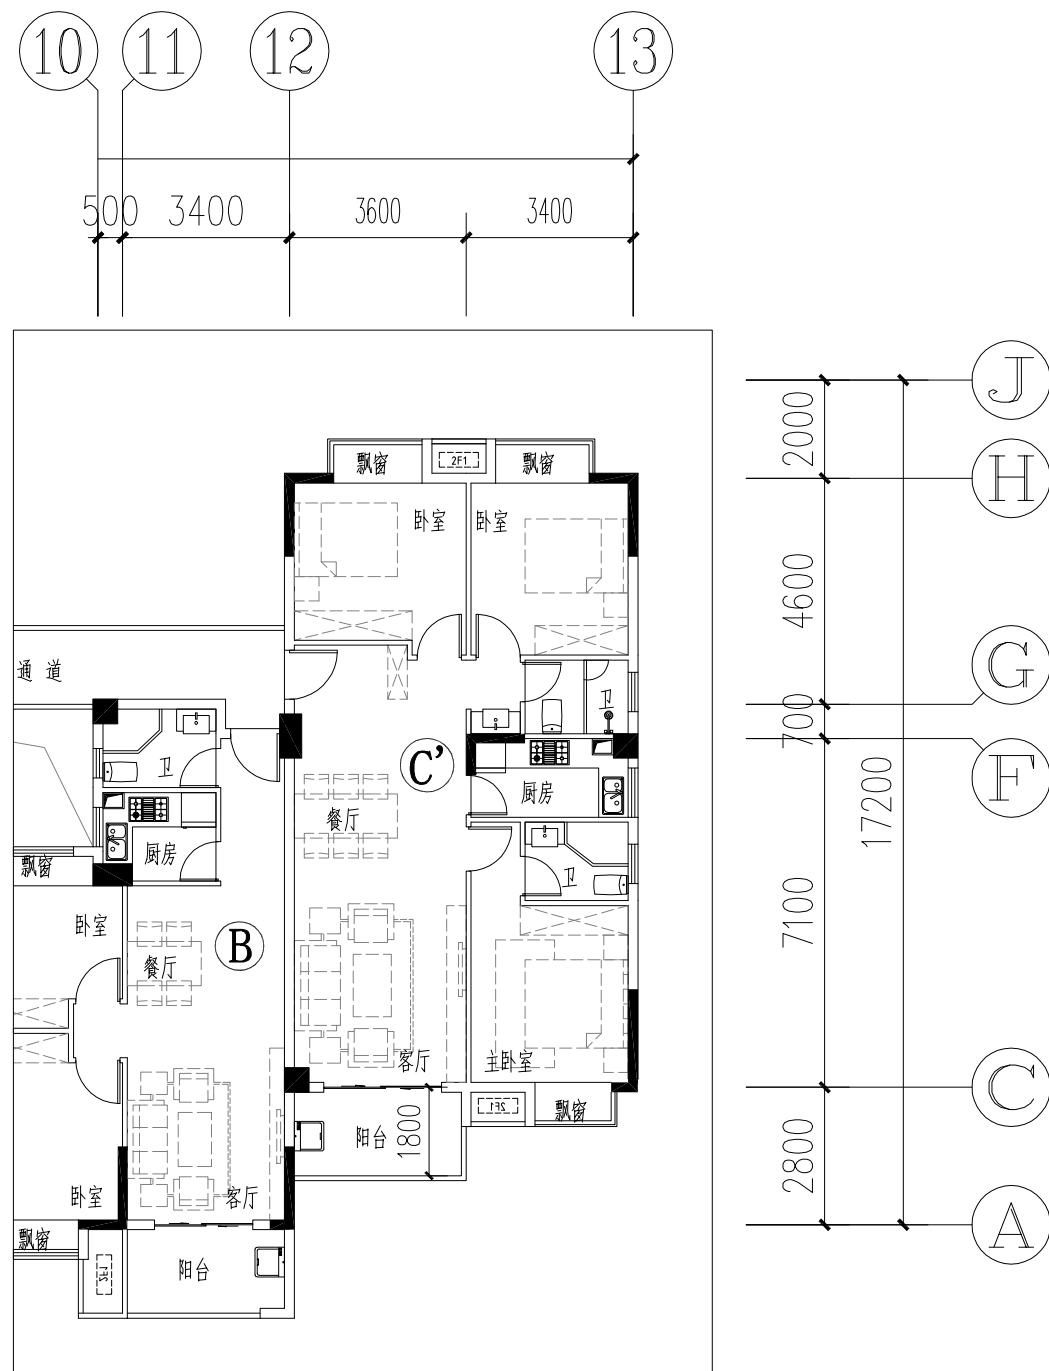

2#楼三~十八层平面图

变更后

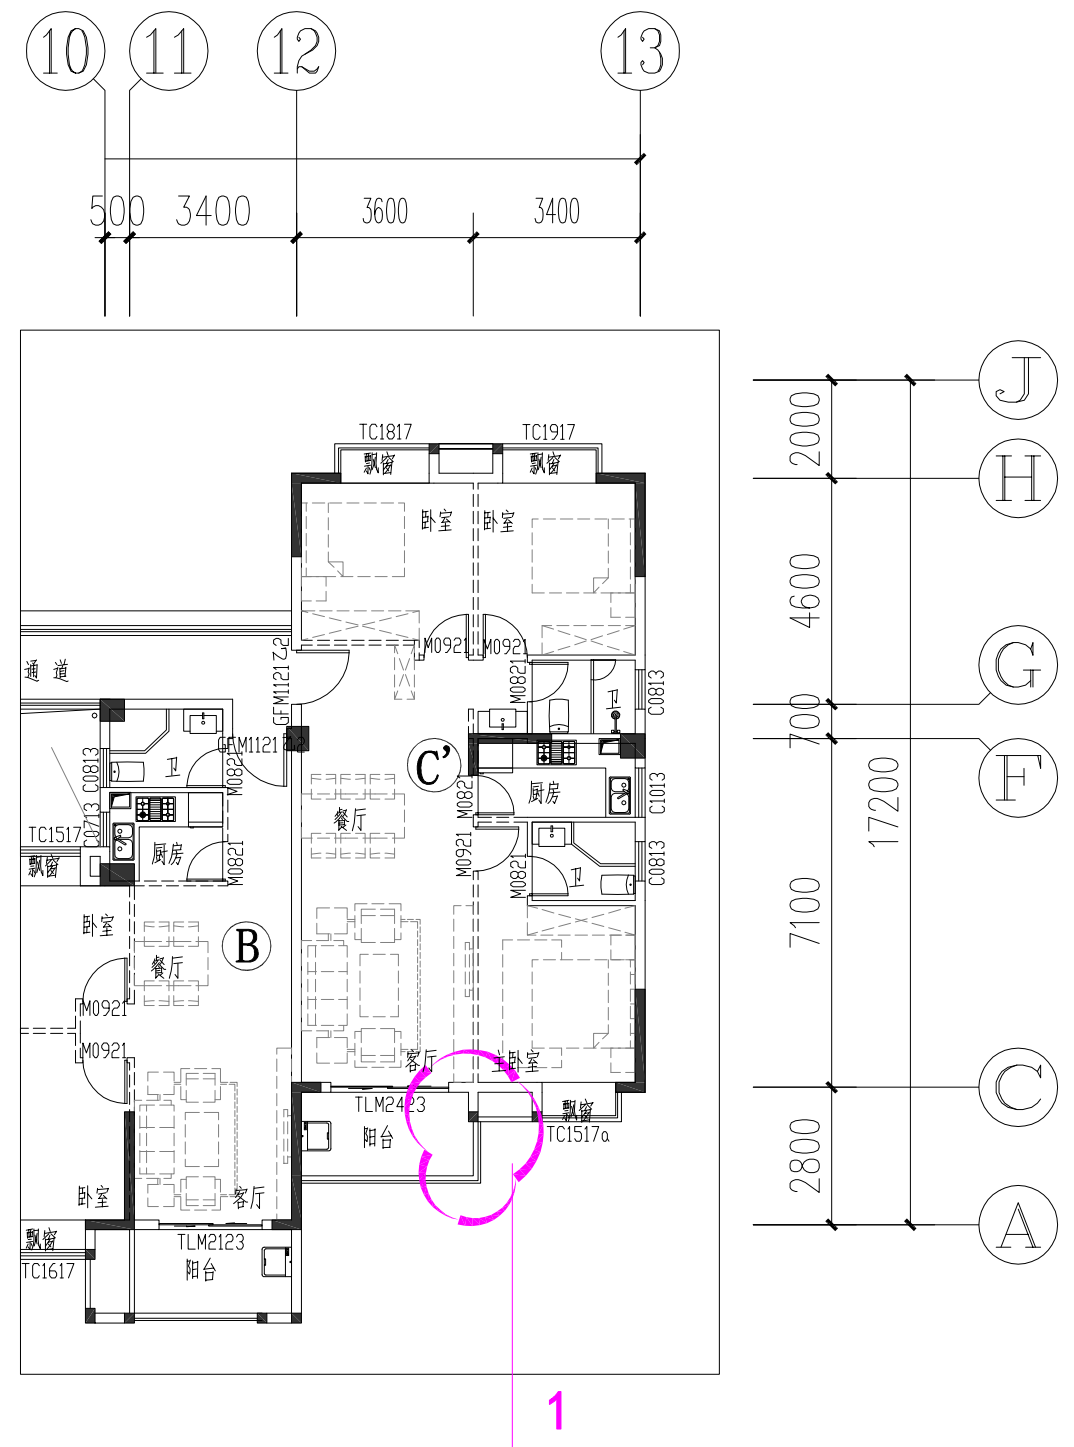


2#楼三~十八层平面图

1. 二至十八层13轴交A~C轴阳台长度3.5米调整为3.6米


[illegible]

变更前

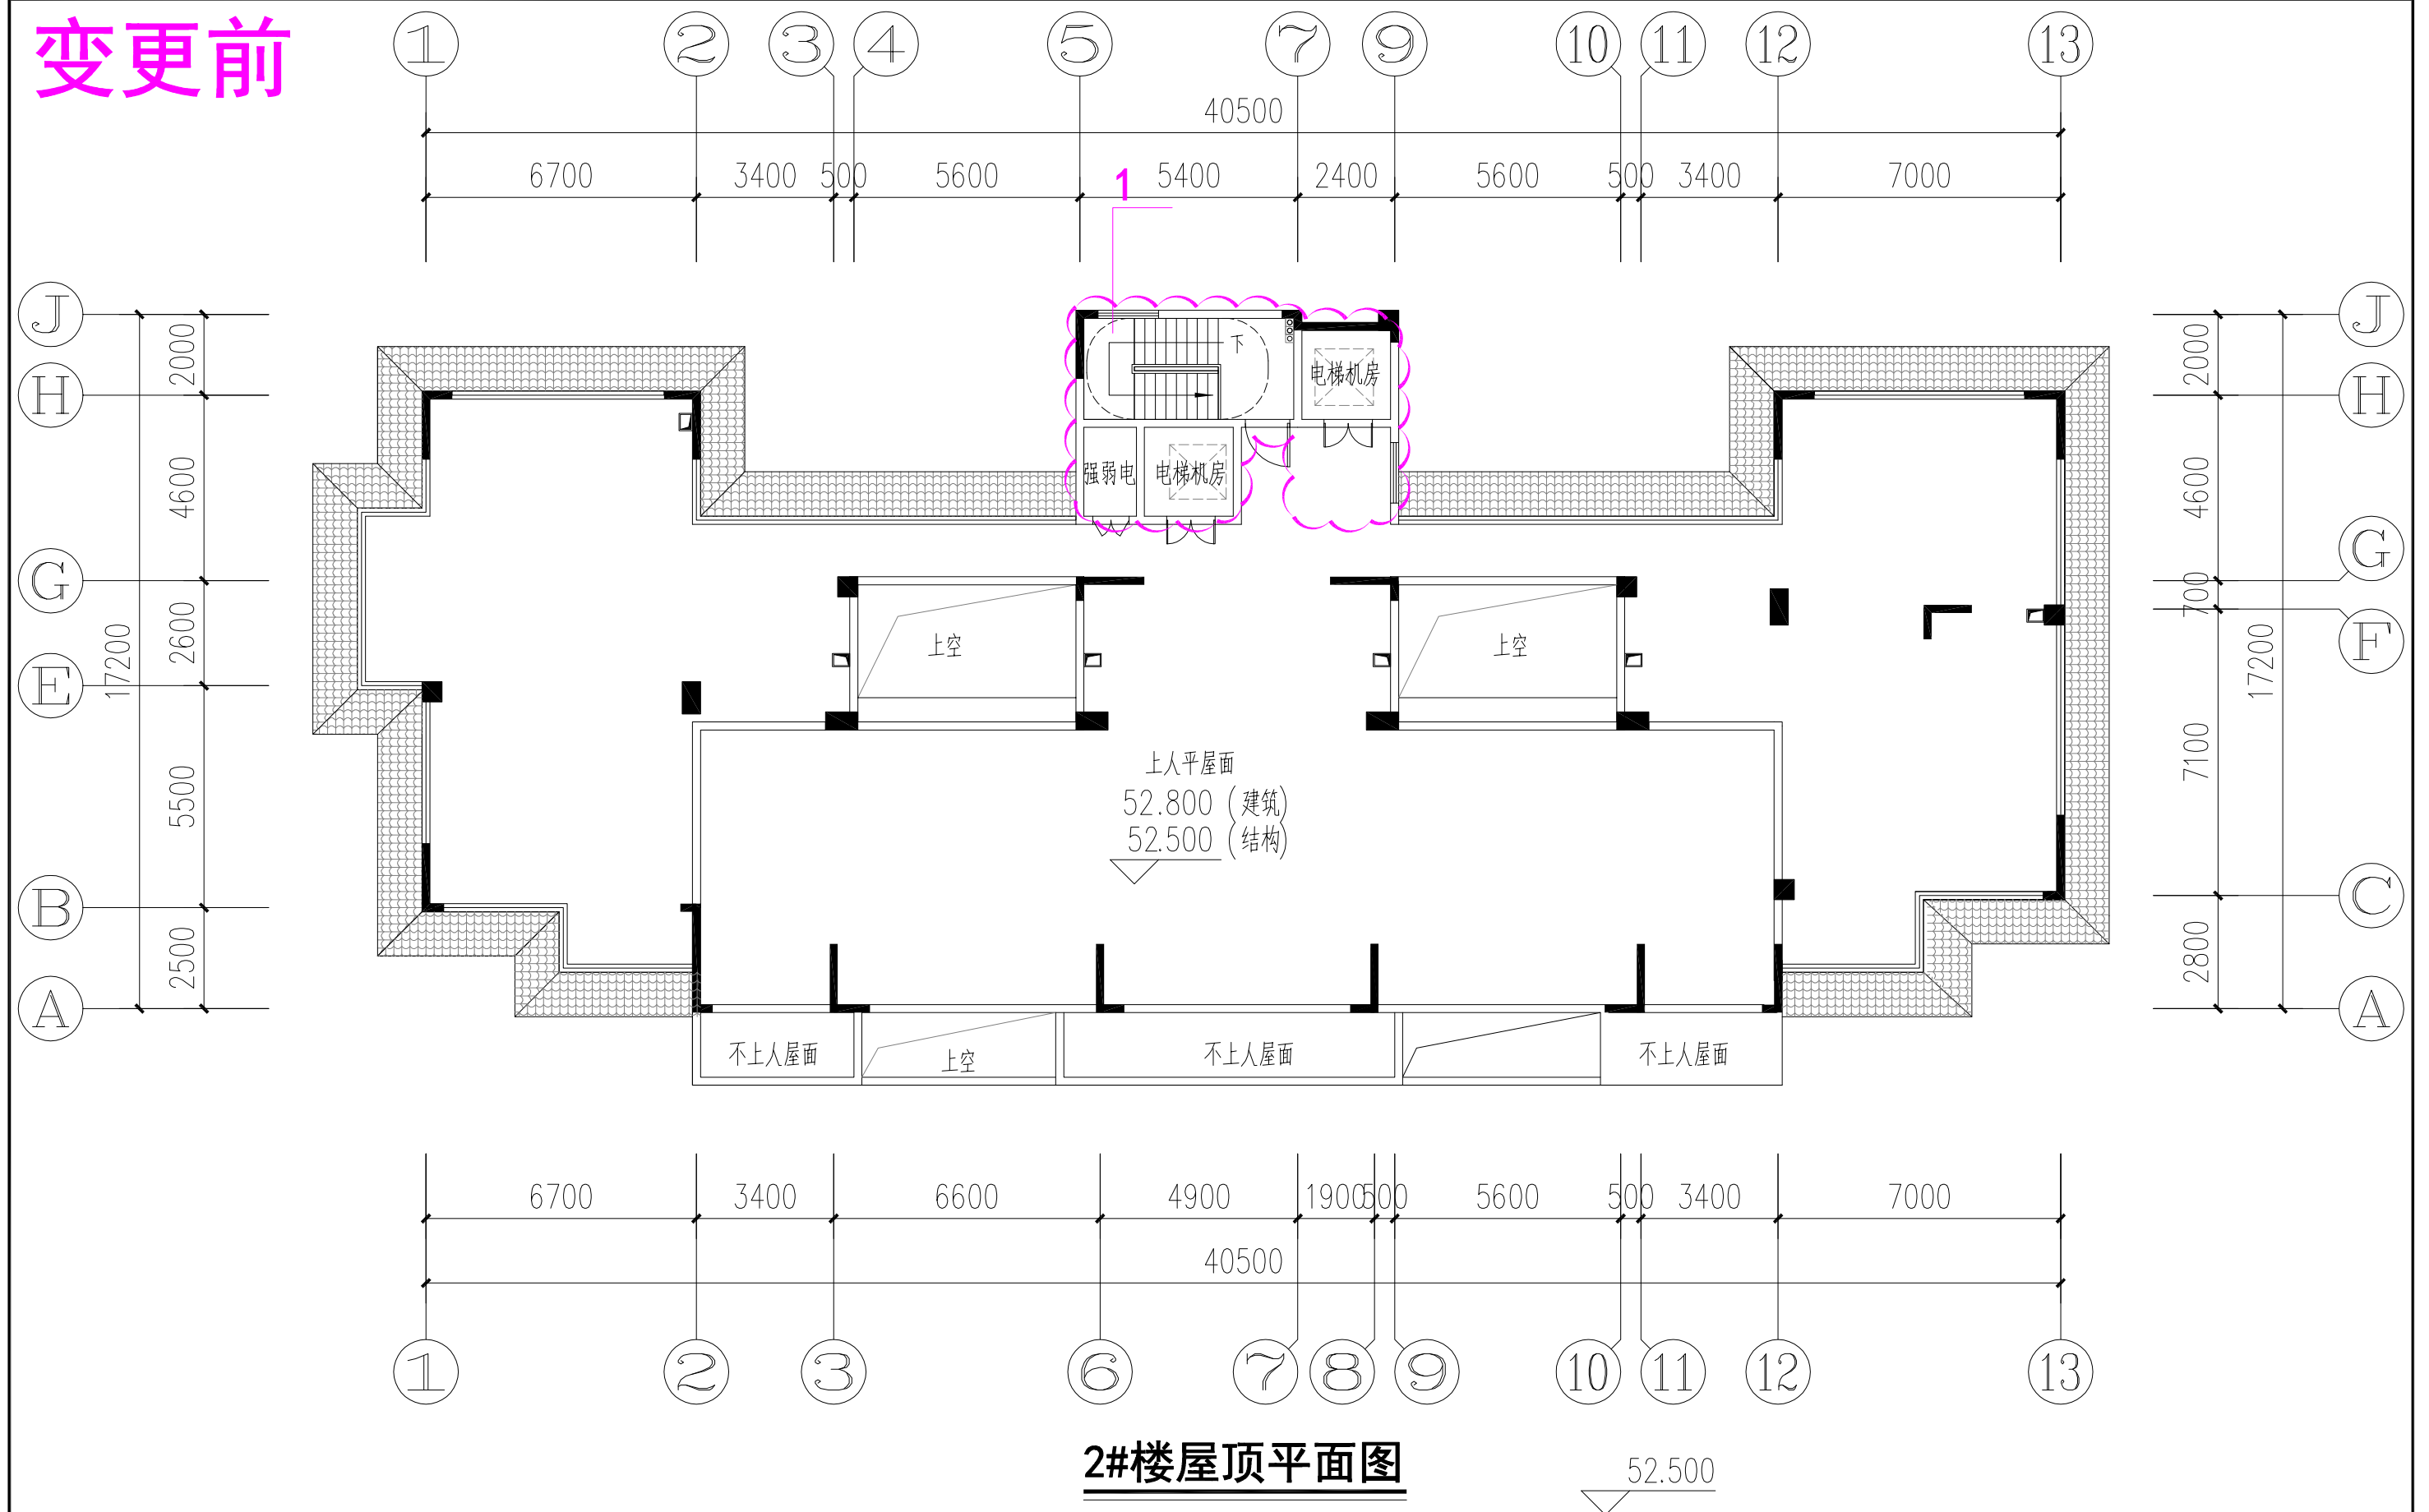

设计单位	福建一建集团有限公司	建设单位	三明市三元区城市建设投资有限责任公司	工程名称	荆东安置房及周边附属配套工程（安置房）	图 名	2#楼屋顶平面图	图 别	方 案
								日 期	2020. 12

变更后

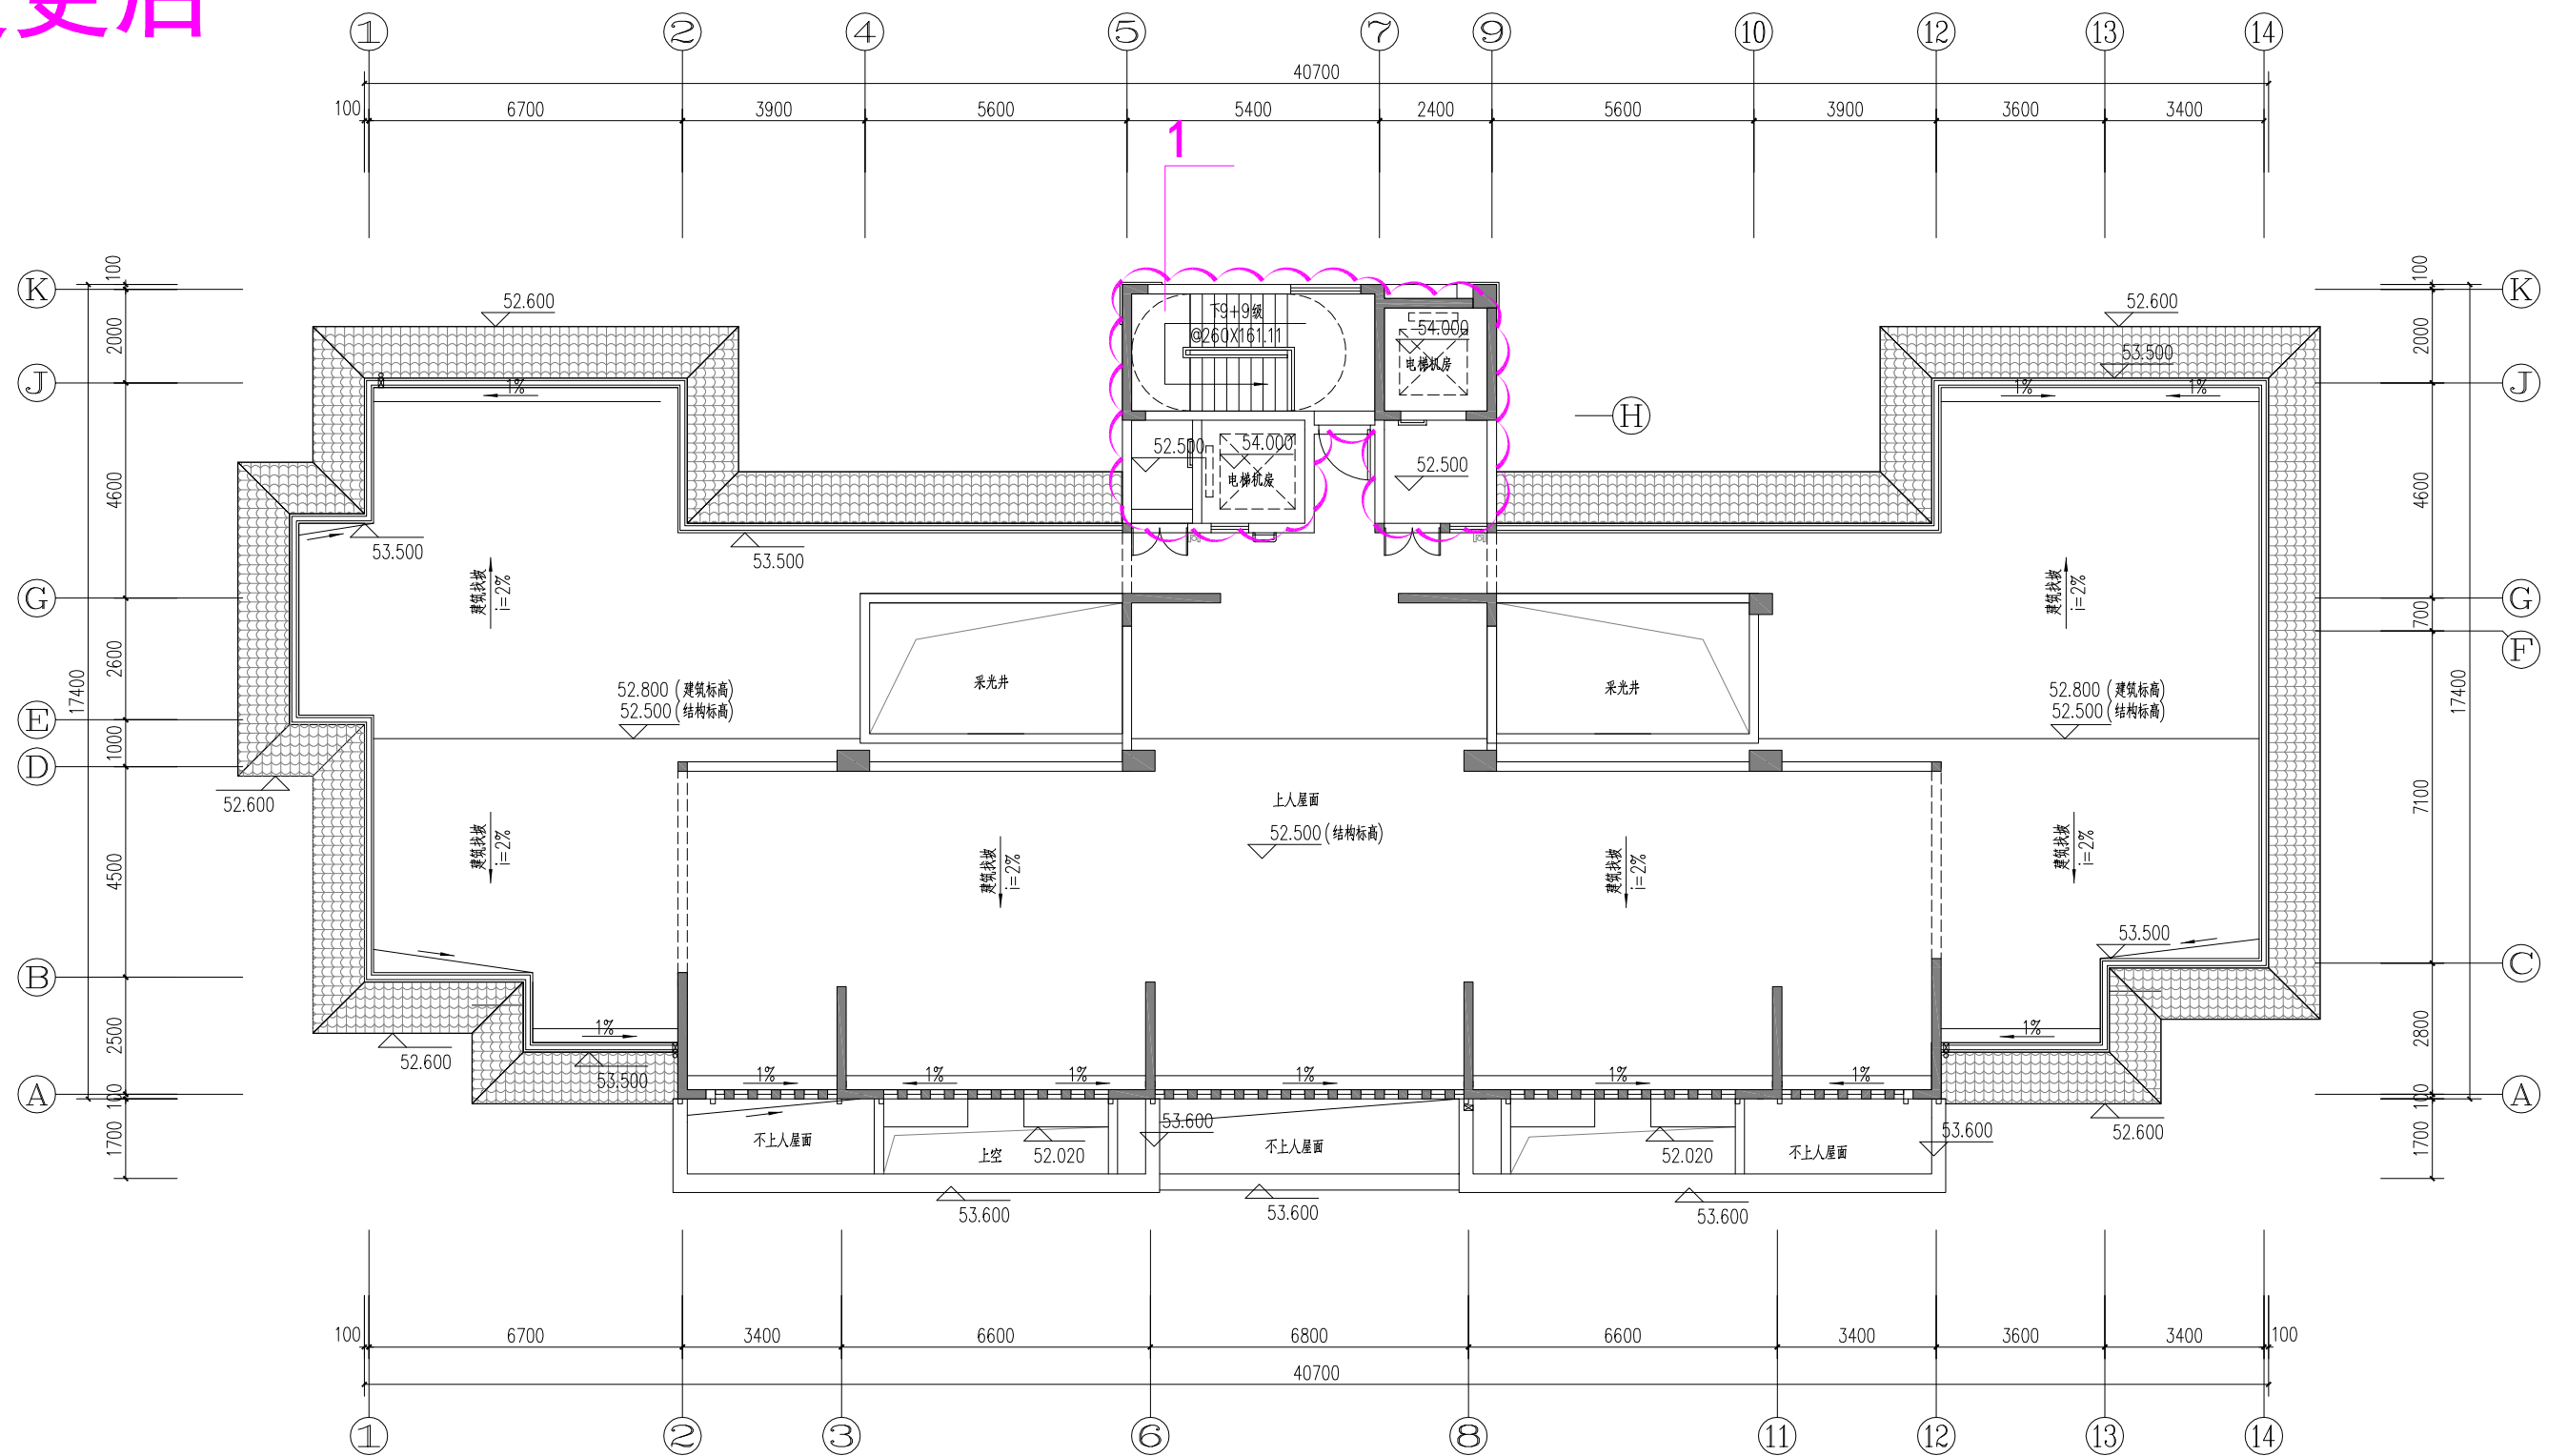


2#楼屋顶平面图

1. 电梯机房调整, 强弱电井取消

设计单位	福建一建集团有限公司	建设单位	三明市三元区城市建设投资有限责任公司	工程名称	荆东安置房及周边附属配套工程（安置房）	图 名	2#楼屋顶平面图	图 别	方 案
								日 期	2023. 07


变更前

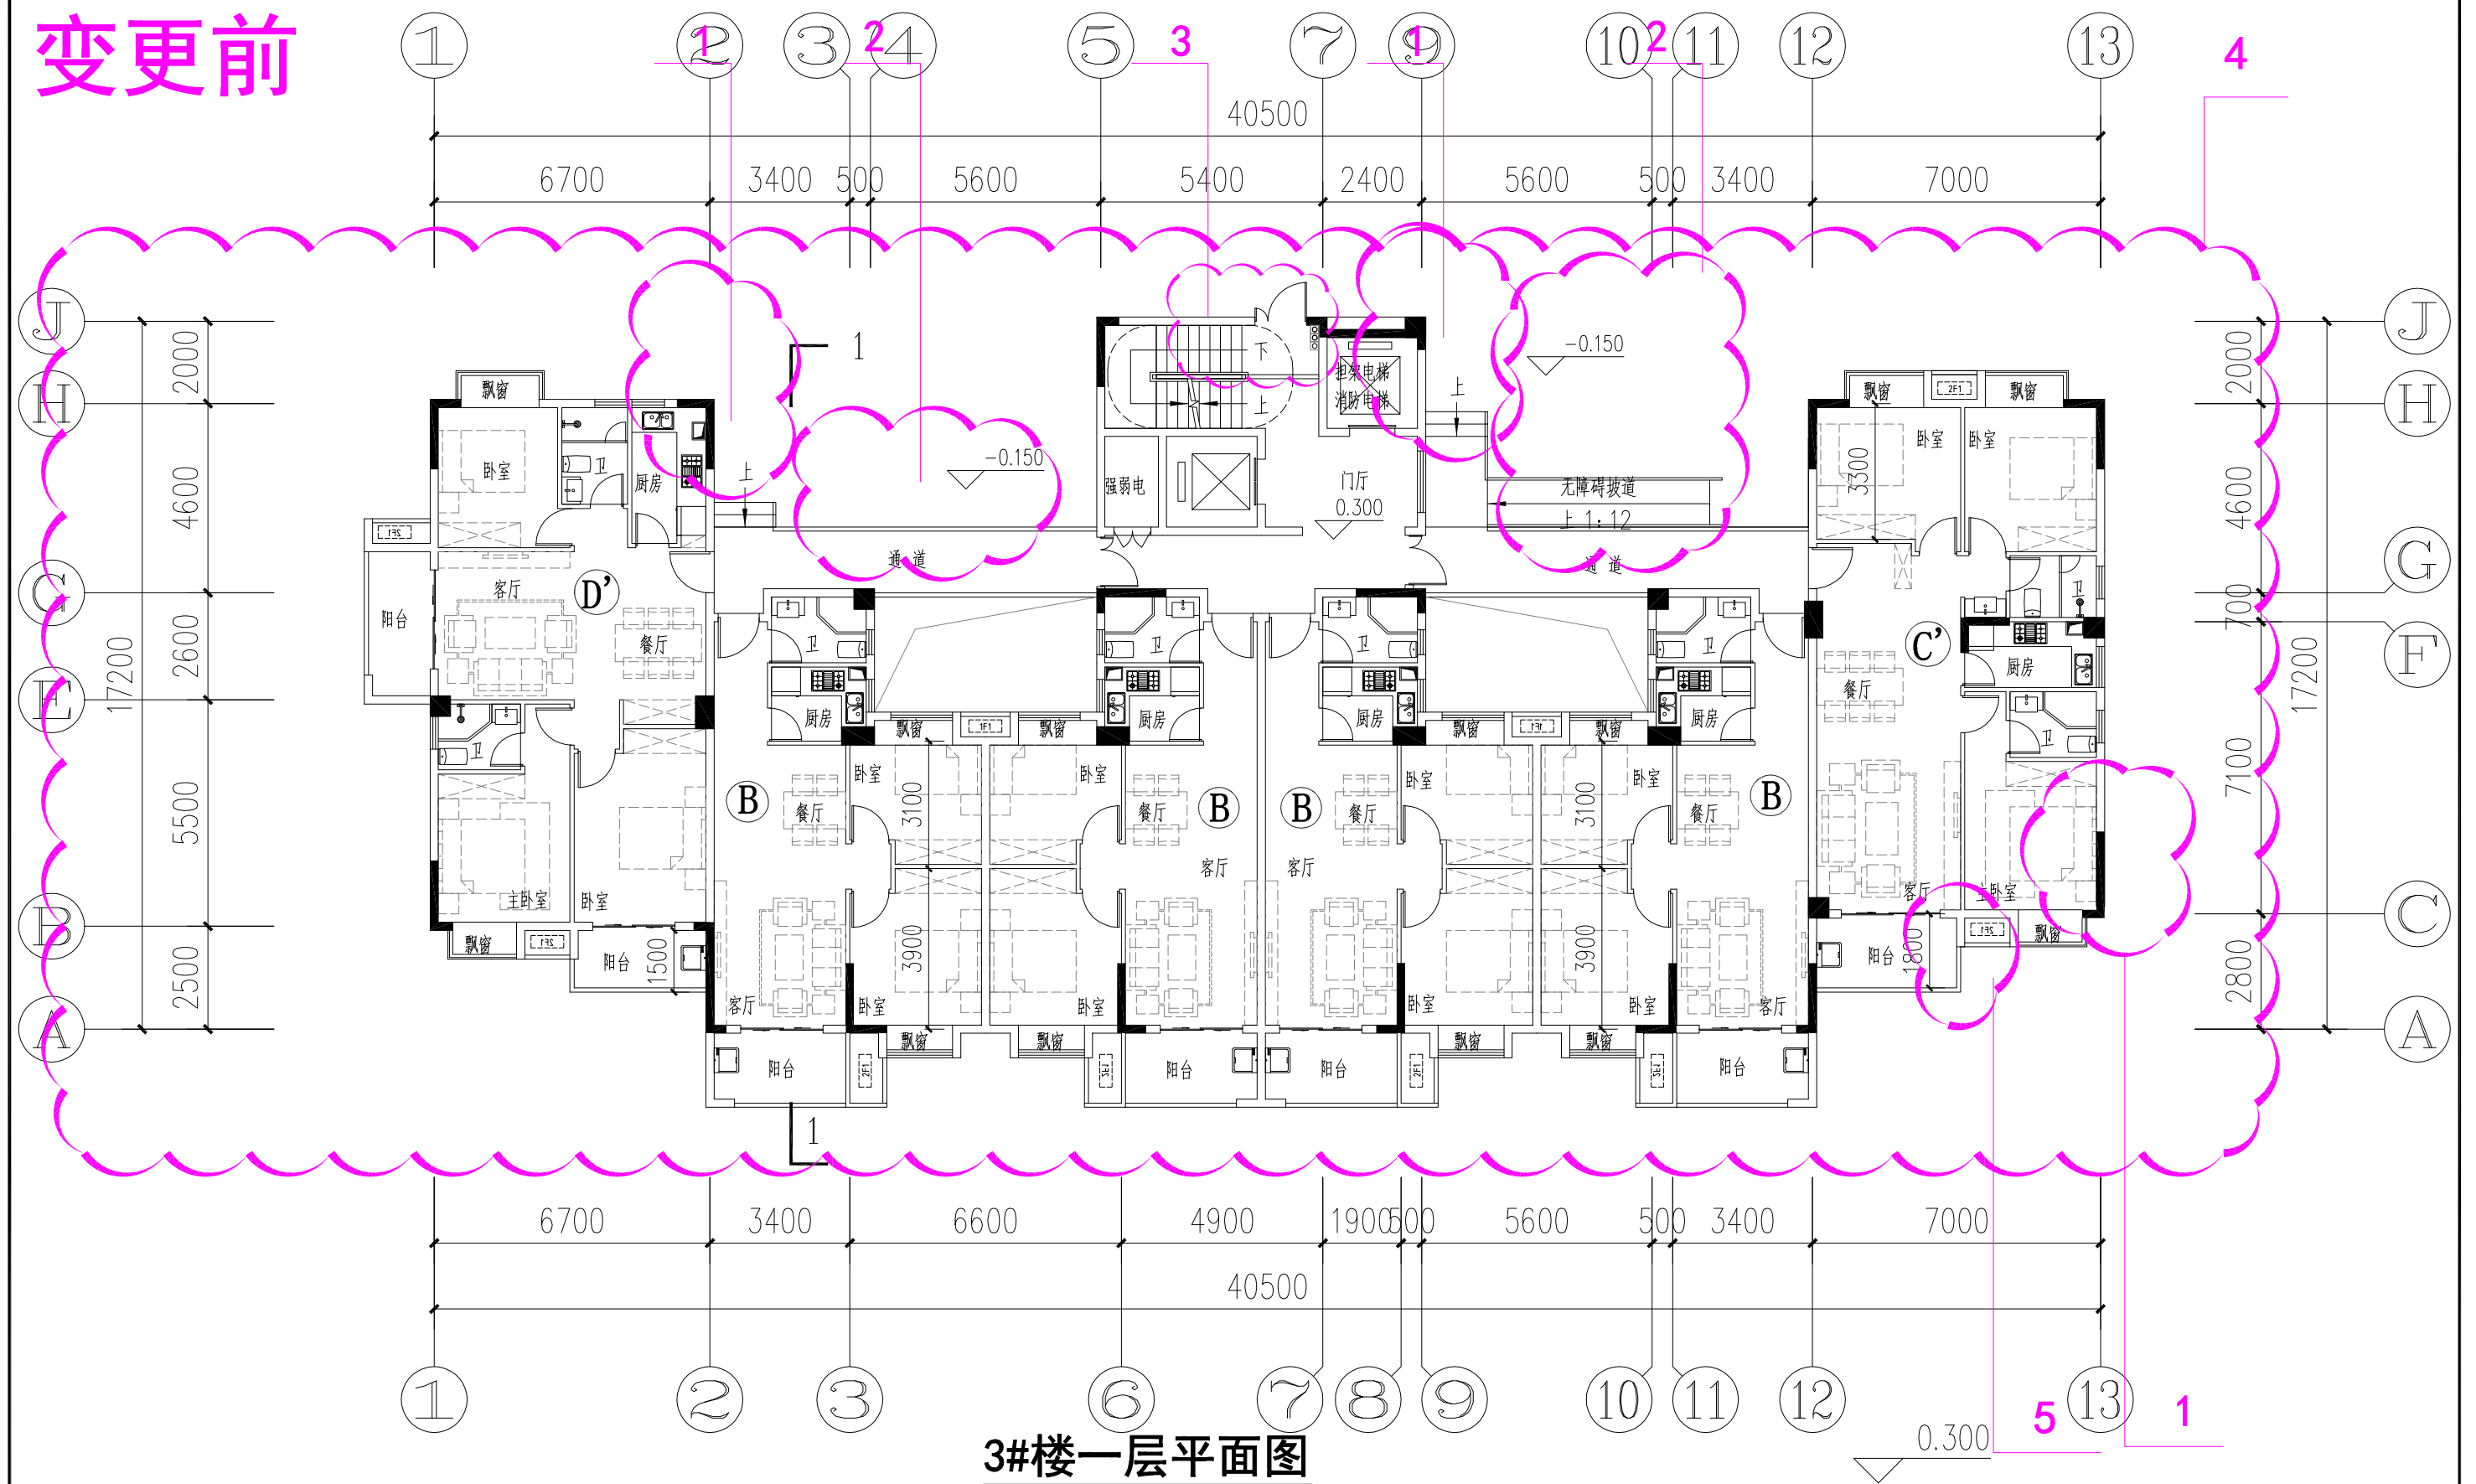

3#楼一层平面图

[illegible]

变更后

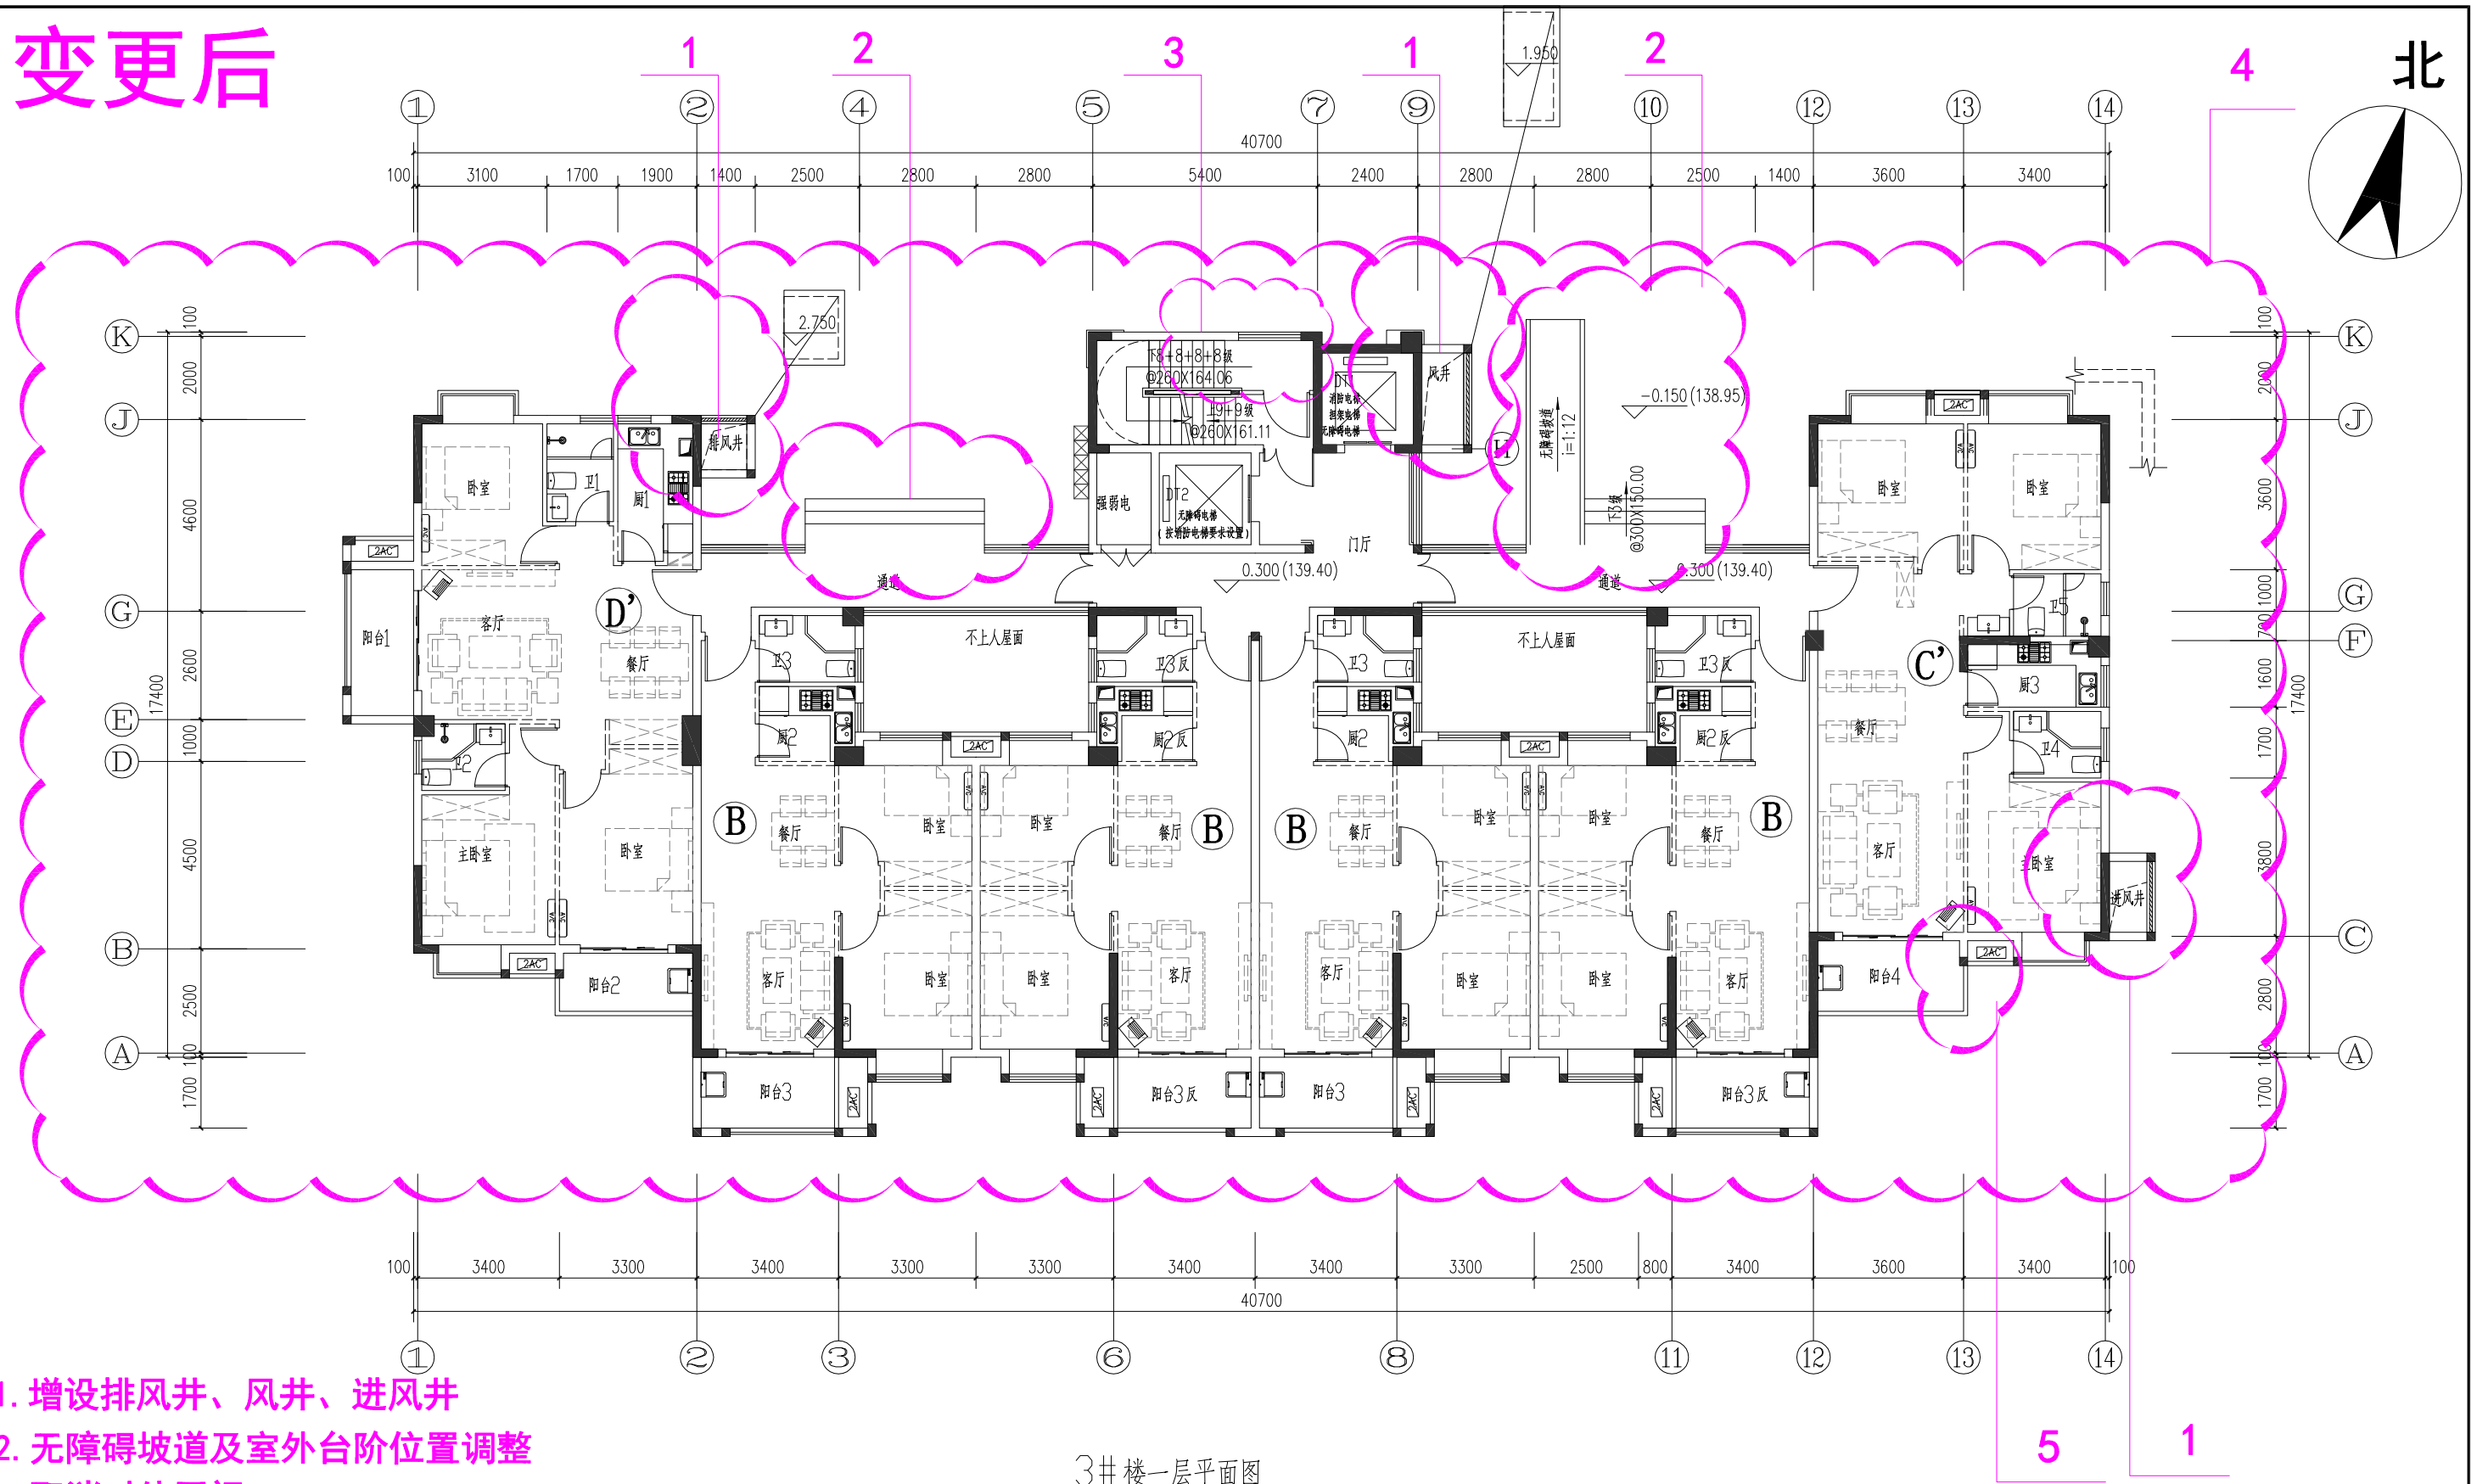


1. 增设排风井、风井、进风井
2. 无障碍坡道及室外台阶位置调整
3. 取消对外开门
4. 一至屋顶层柱网整体调整
5. 13轴交A~C轴阳台长度3.5米调整为3.6米

3#楼一层平面图

设计单位	福建一建集团有限公司	建设单位	三明市三元区城市建设投资有限责任公司	工程名称	荆东安置房及周边附属配套工程（安置房）	图 名	3#楼一层平面图	图 别	方 案
								日 期	2023. 07


变更前

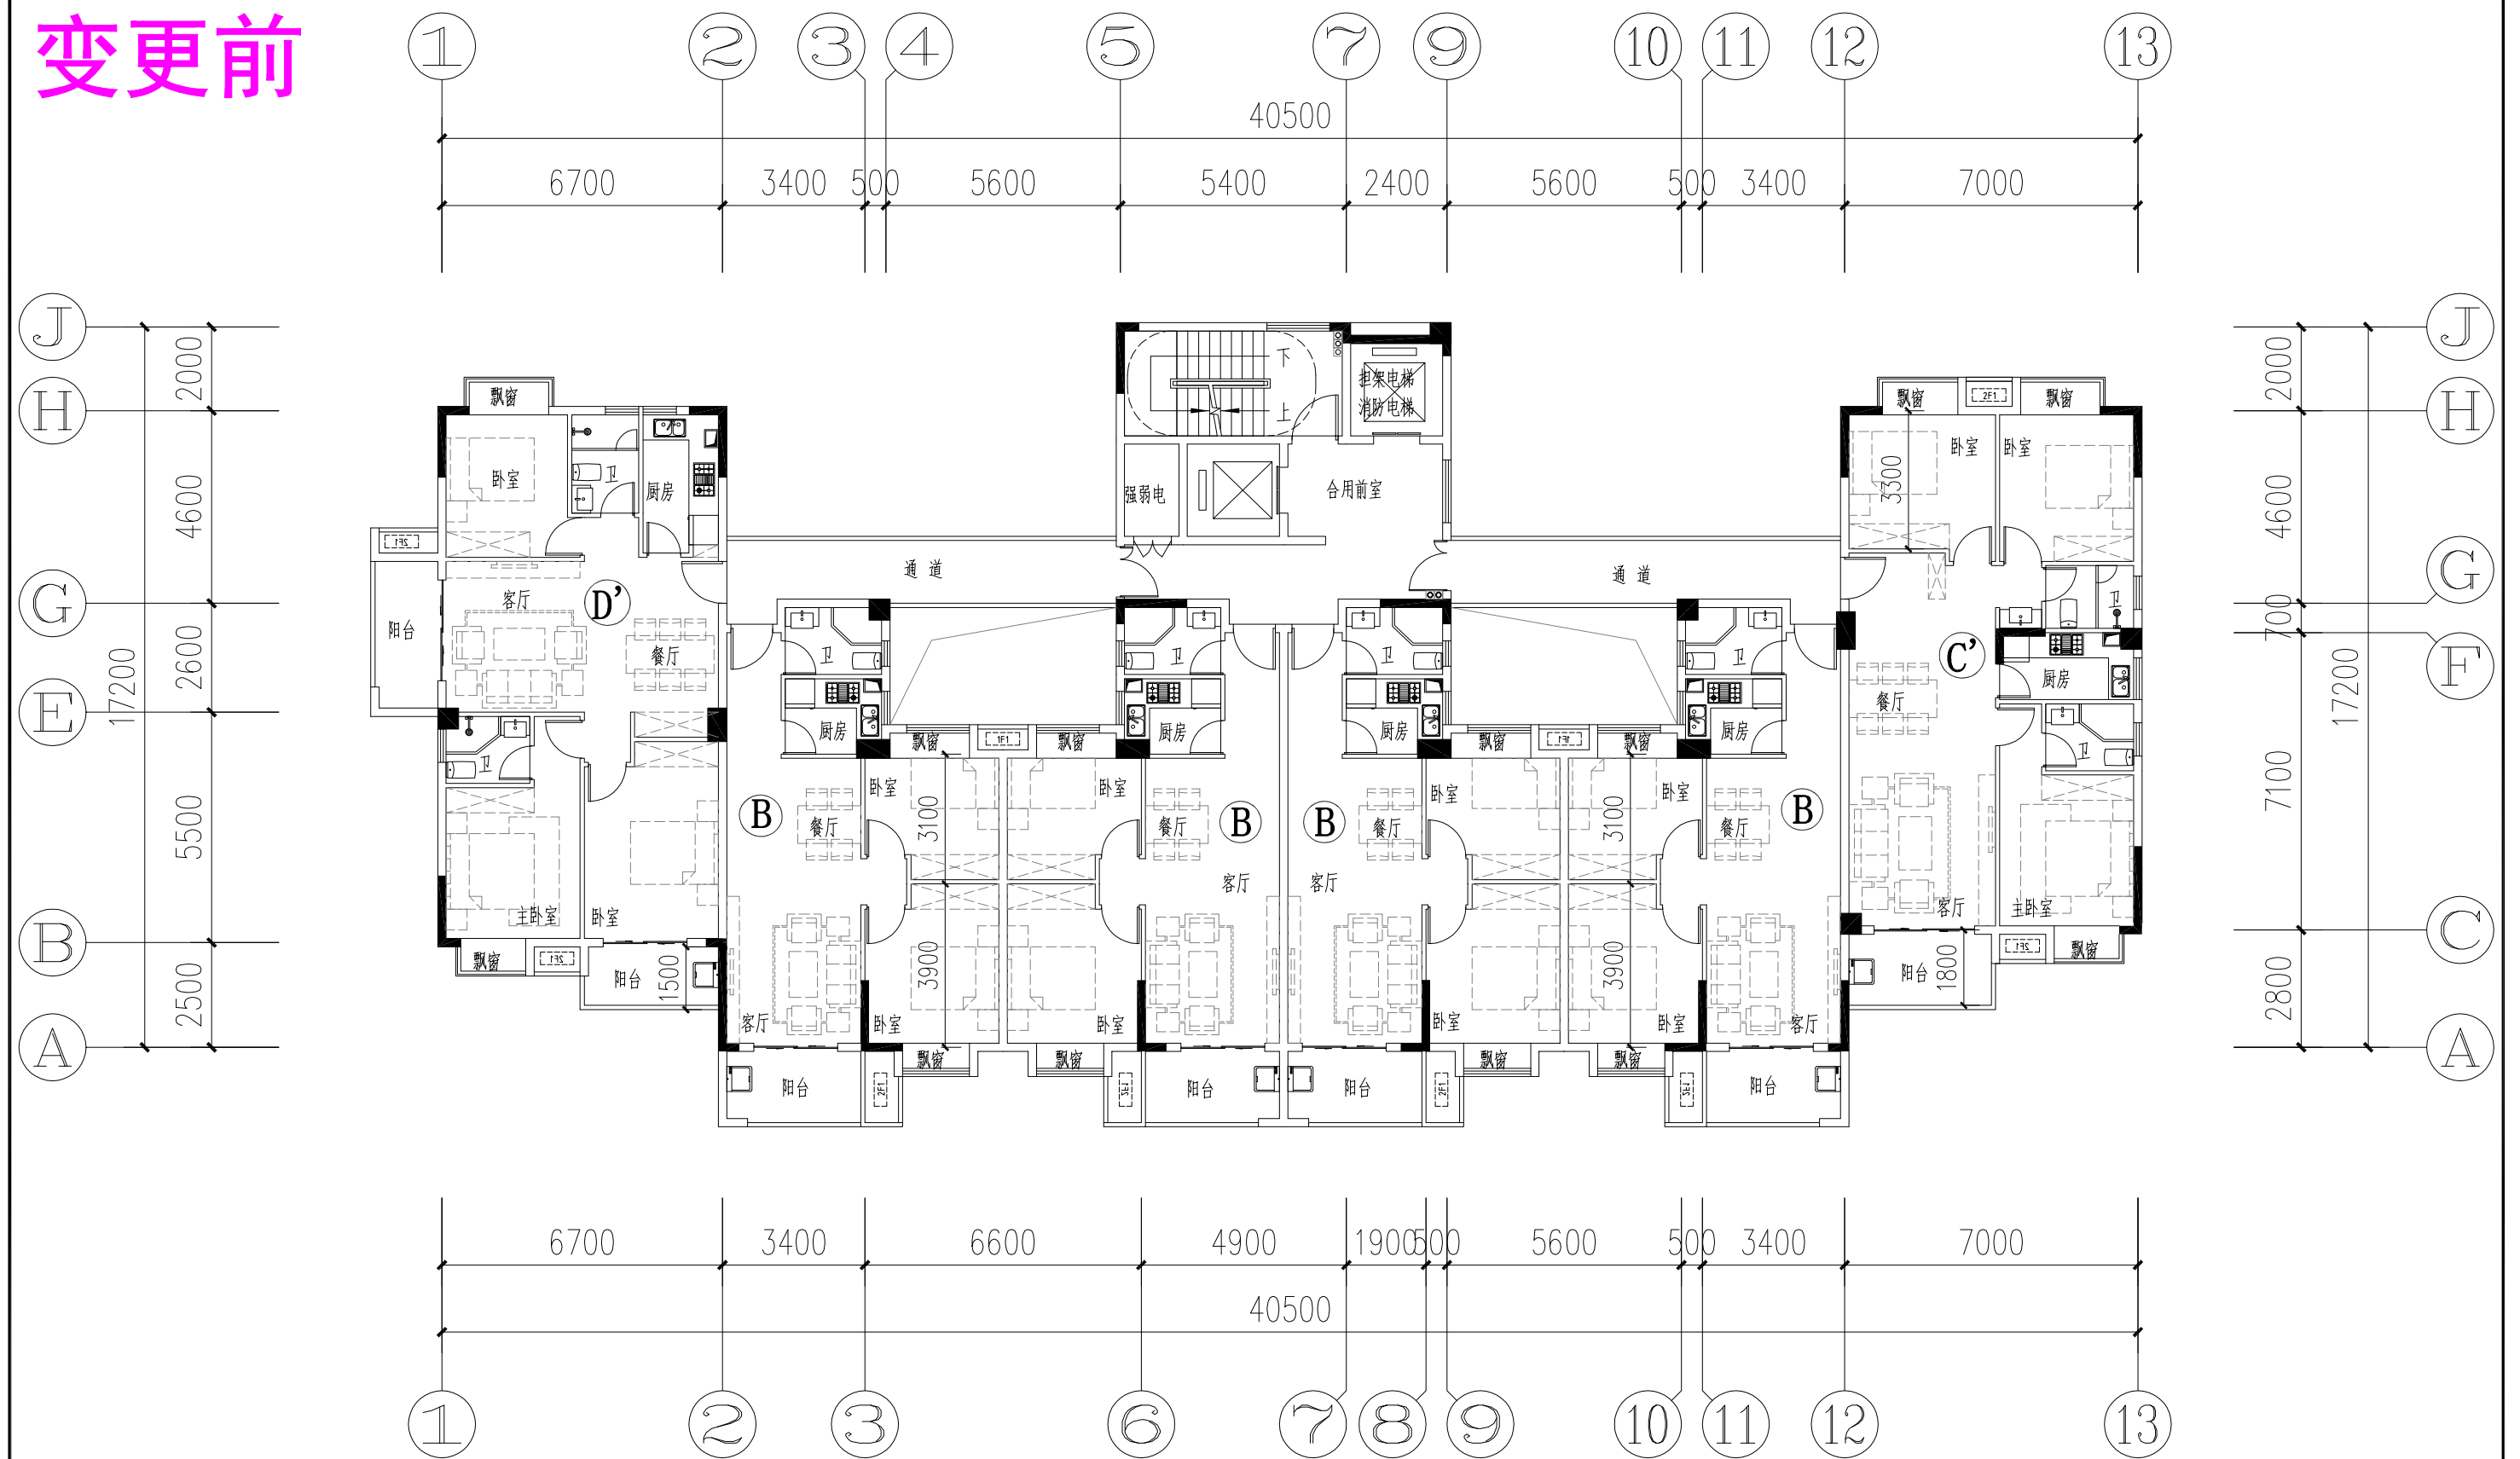

3#楼二~十八层平面图

设计单位	福建一建集团有限公司	建设单位	三明市三元区城市建设投资有限责任公司	工程名称	荆东安置房及周边附属配套工程（安置房）	图 名	3#楼二~十八层平面图	图 别	方 案
								日 期	2020. 12

变更后

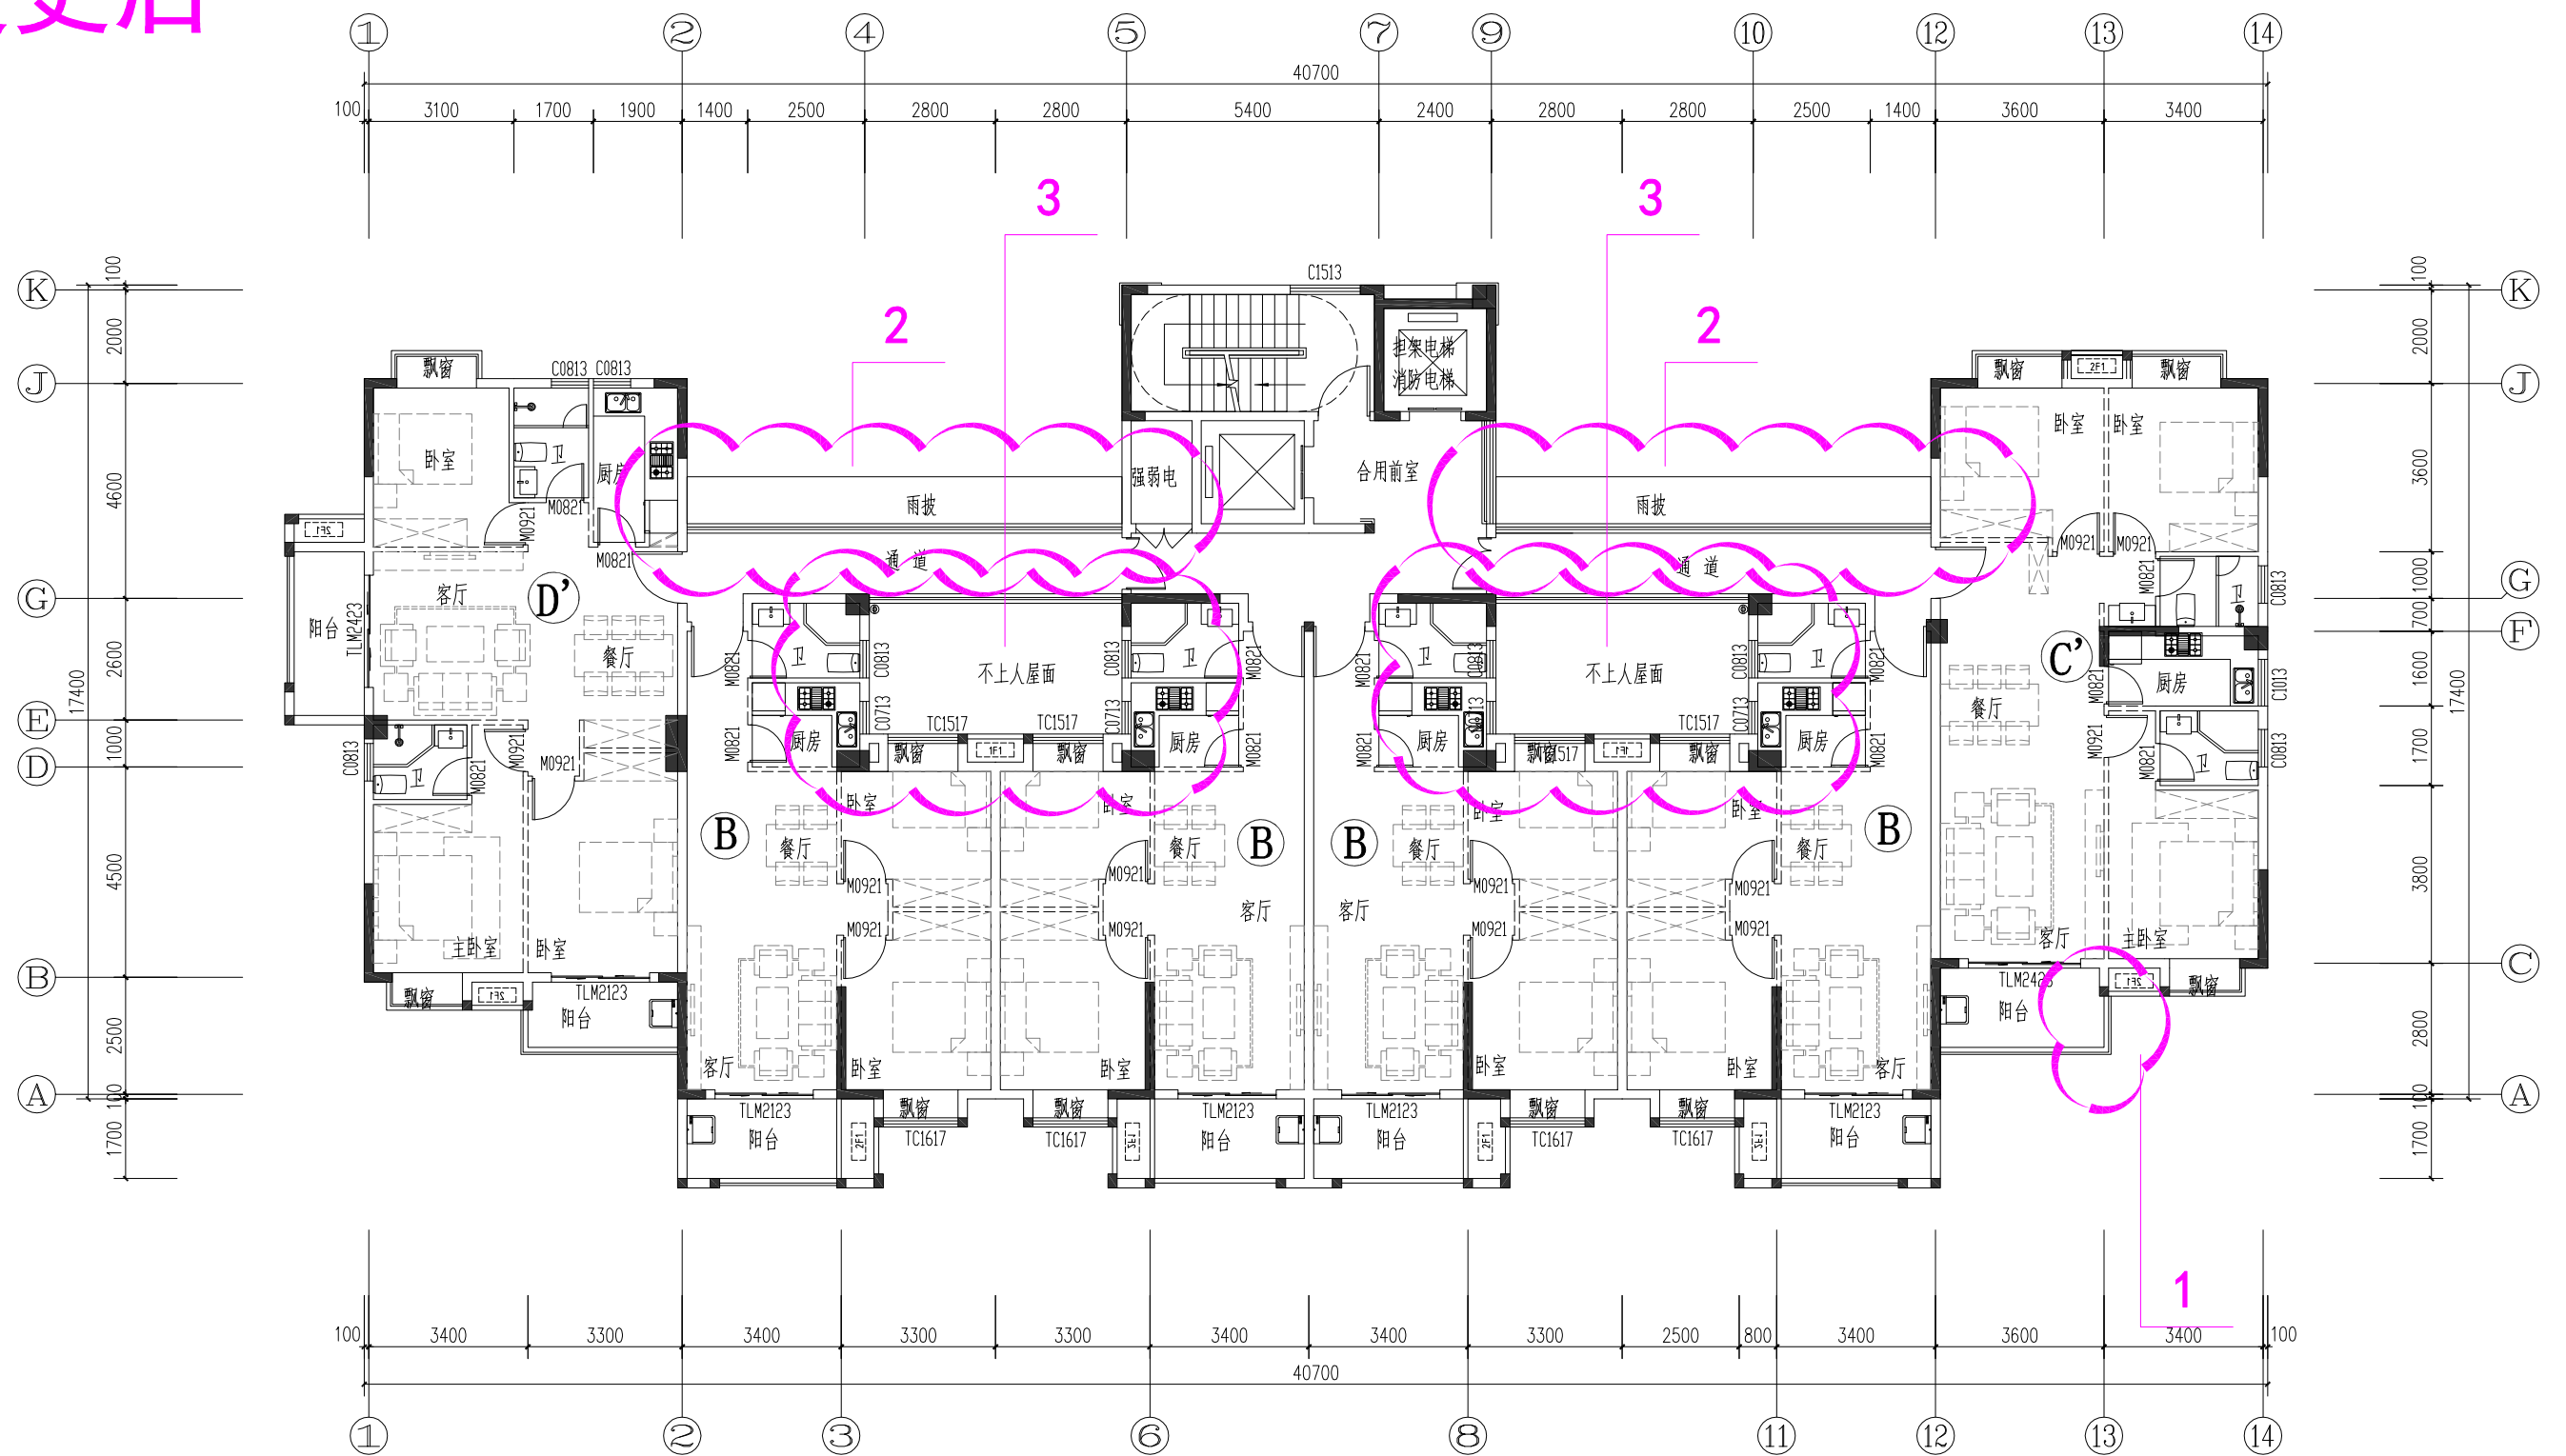


1. 13轴交A~C轴阳台长度3.5米调整为3.6米
2. 新增雨披
3. 采光井调整为不上人屋面

3#楼二层平面图


设计单位	福建一建集团有限公司	建设单位	三明市三元区城市建设投资有限责任公司	工程名称	荆东安置房及周边附属配套工程（安置房）	图 名	3#楼二层平面图	图 别	方 案
								日 期	2023. 07

变更前

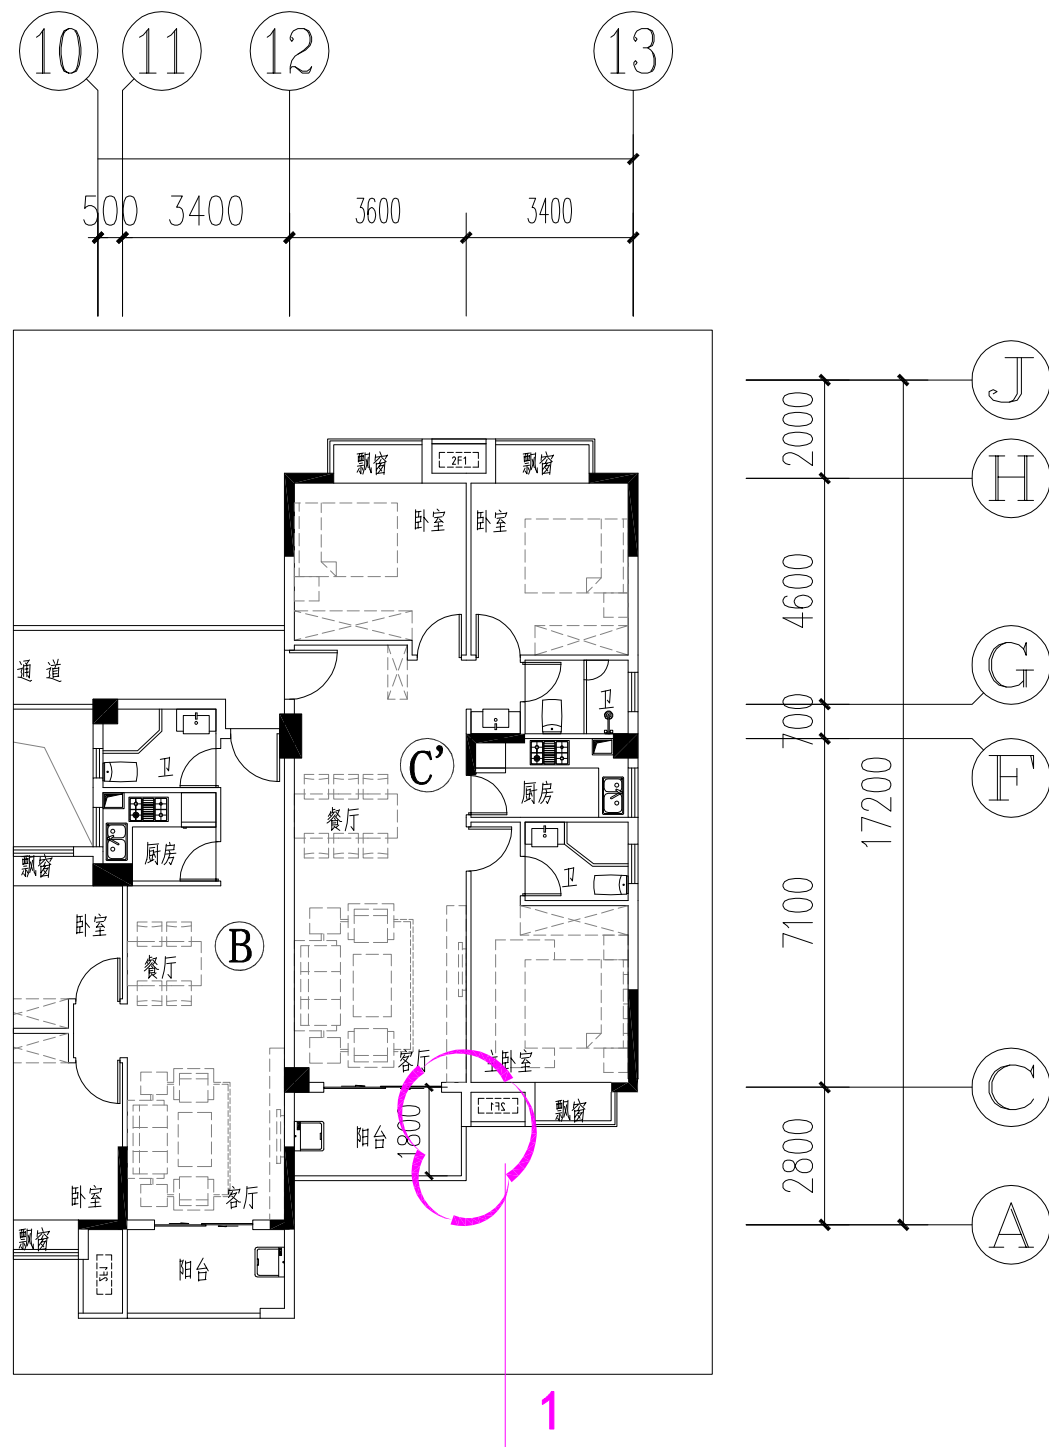

3#楼三~十八层平面图

变更后

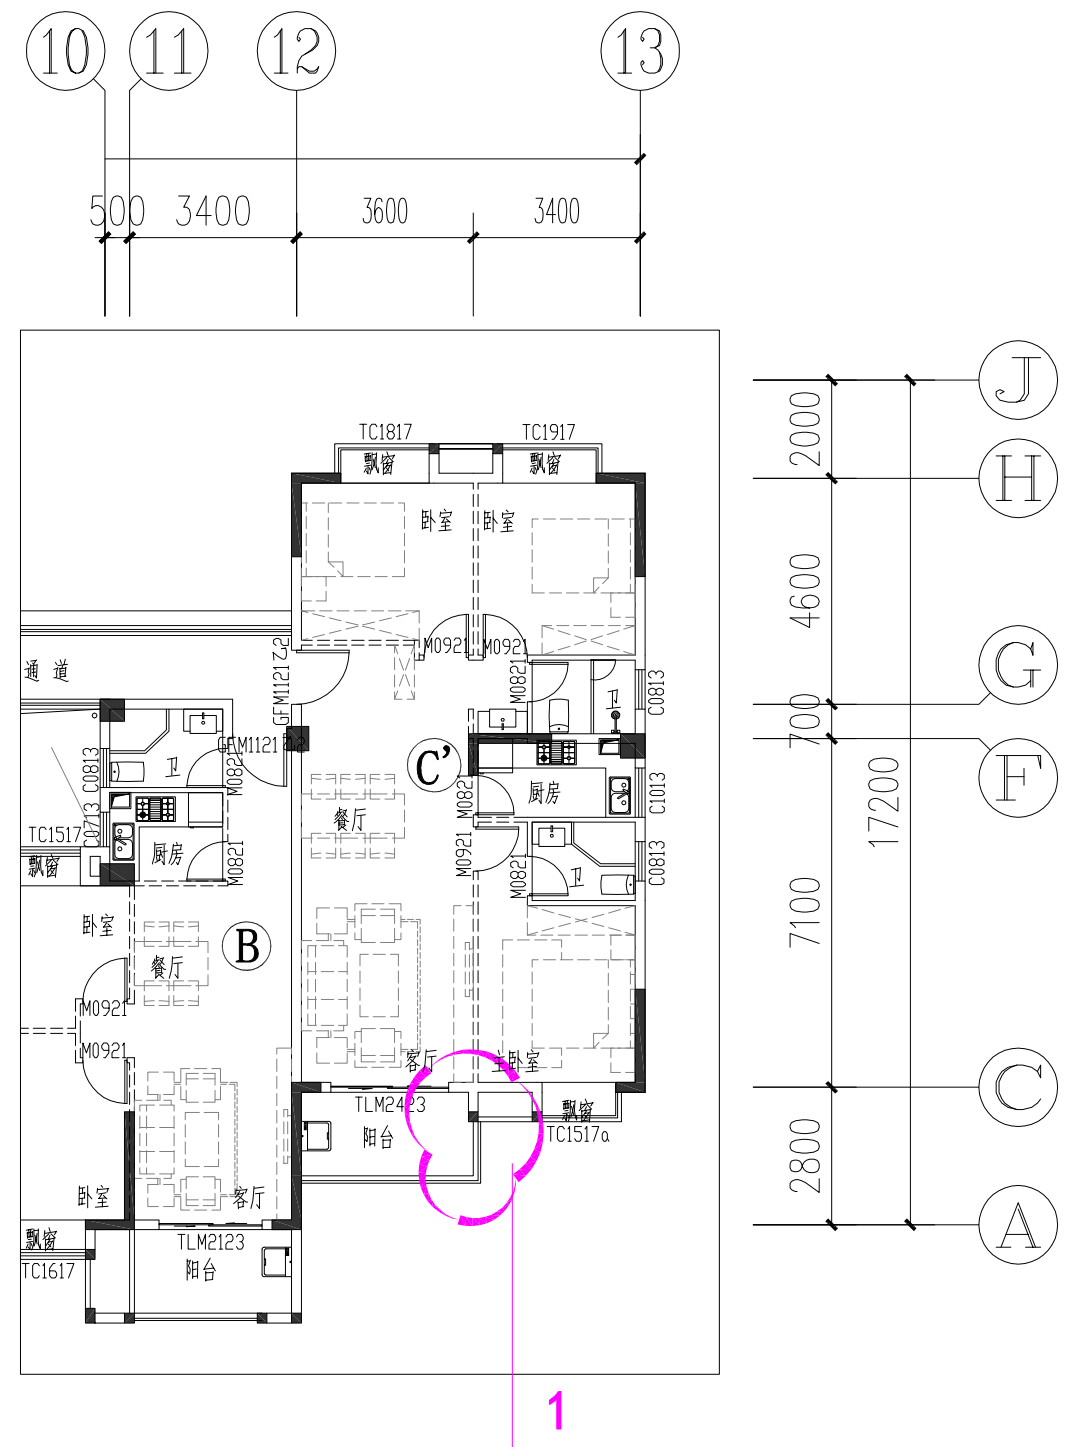


3#楼三~十八层平面图

1. 二至十八层13轴交A~C轴阳台长度3.5米调整为3.6米


设计单位	福建一建集团有限公司	建设单位	三明市三元区城市建设投资有限责任公司	工程名称	荆东安置房及周边附属配套工程（安置房）	图 名	3#楼三~十八层平面图	图 别	方 案
								日 期	2023. 07

变更前

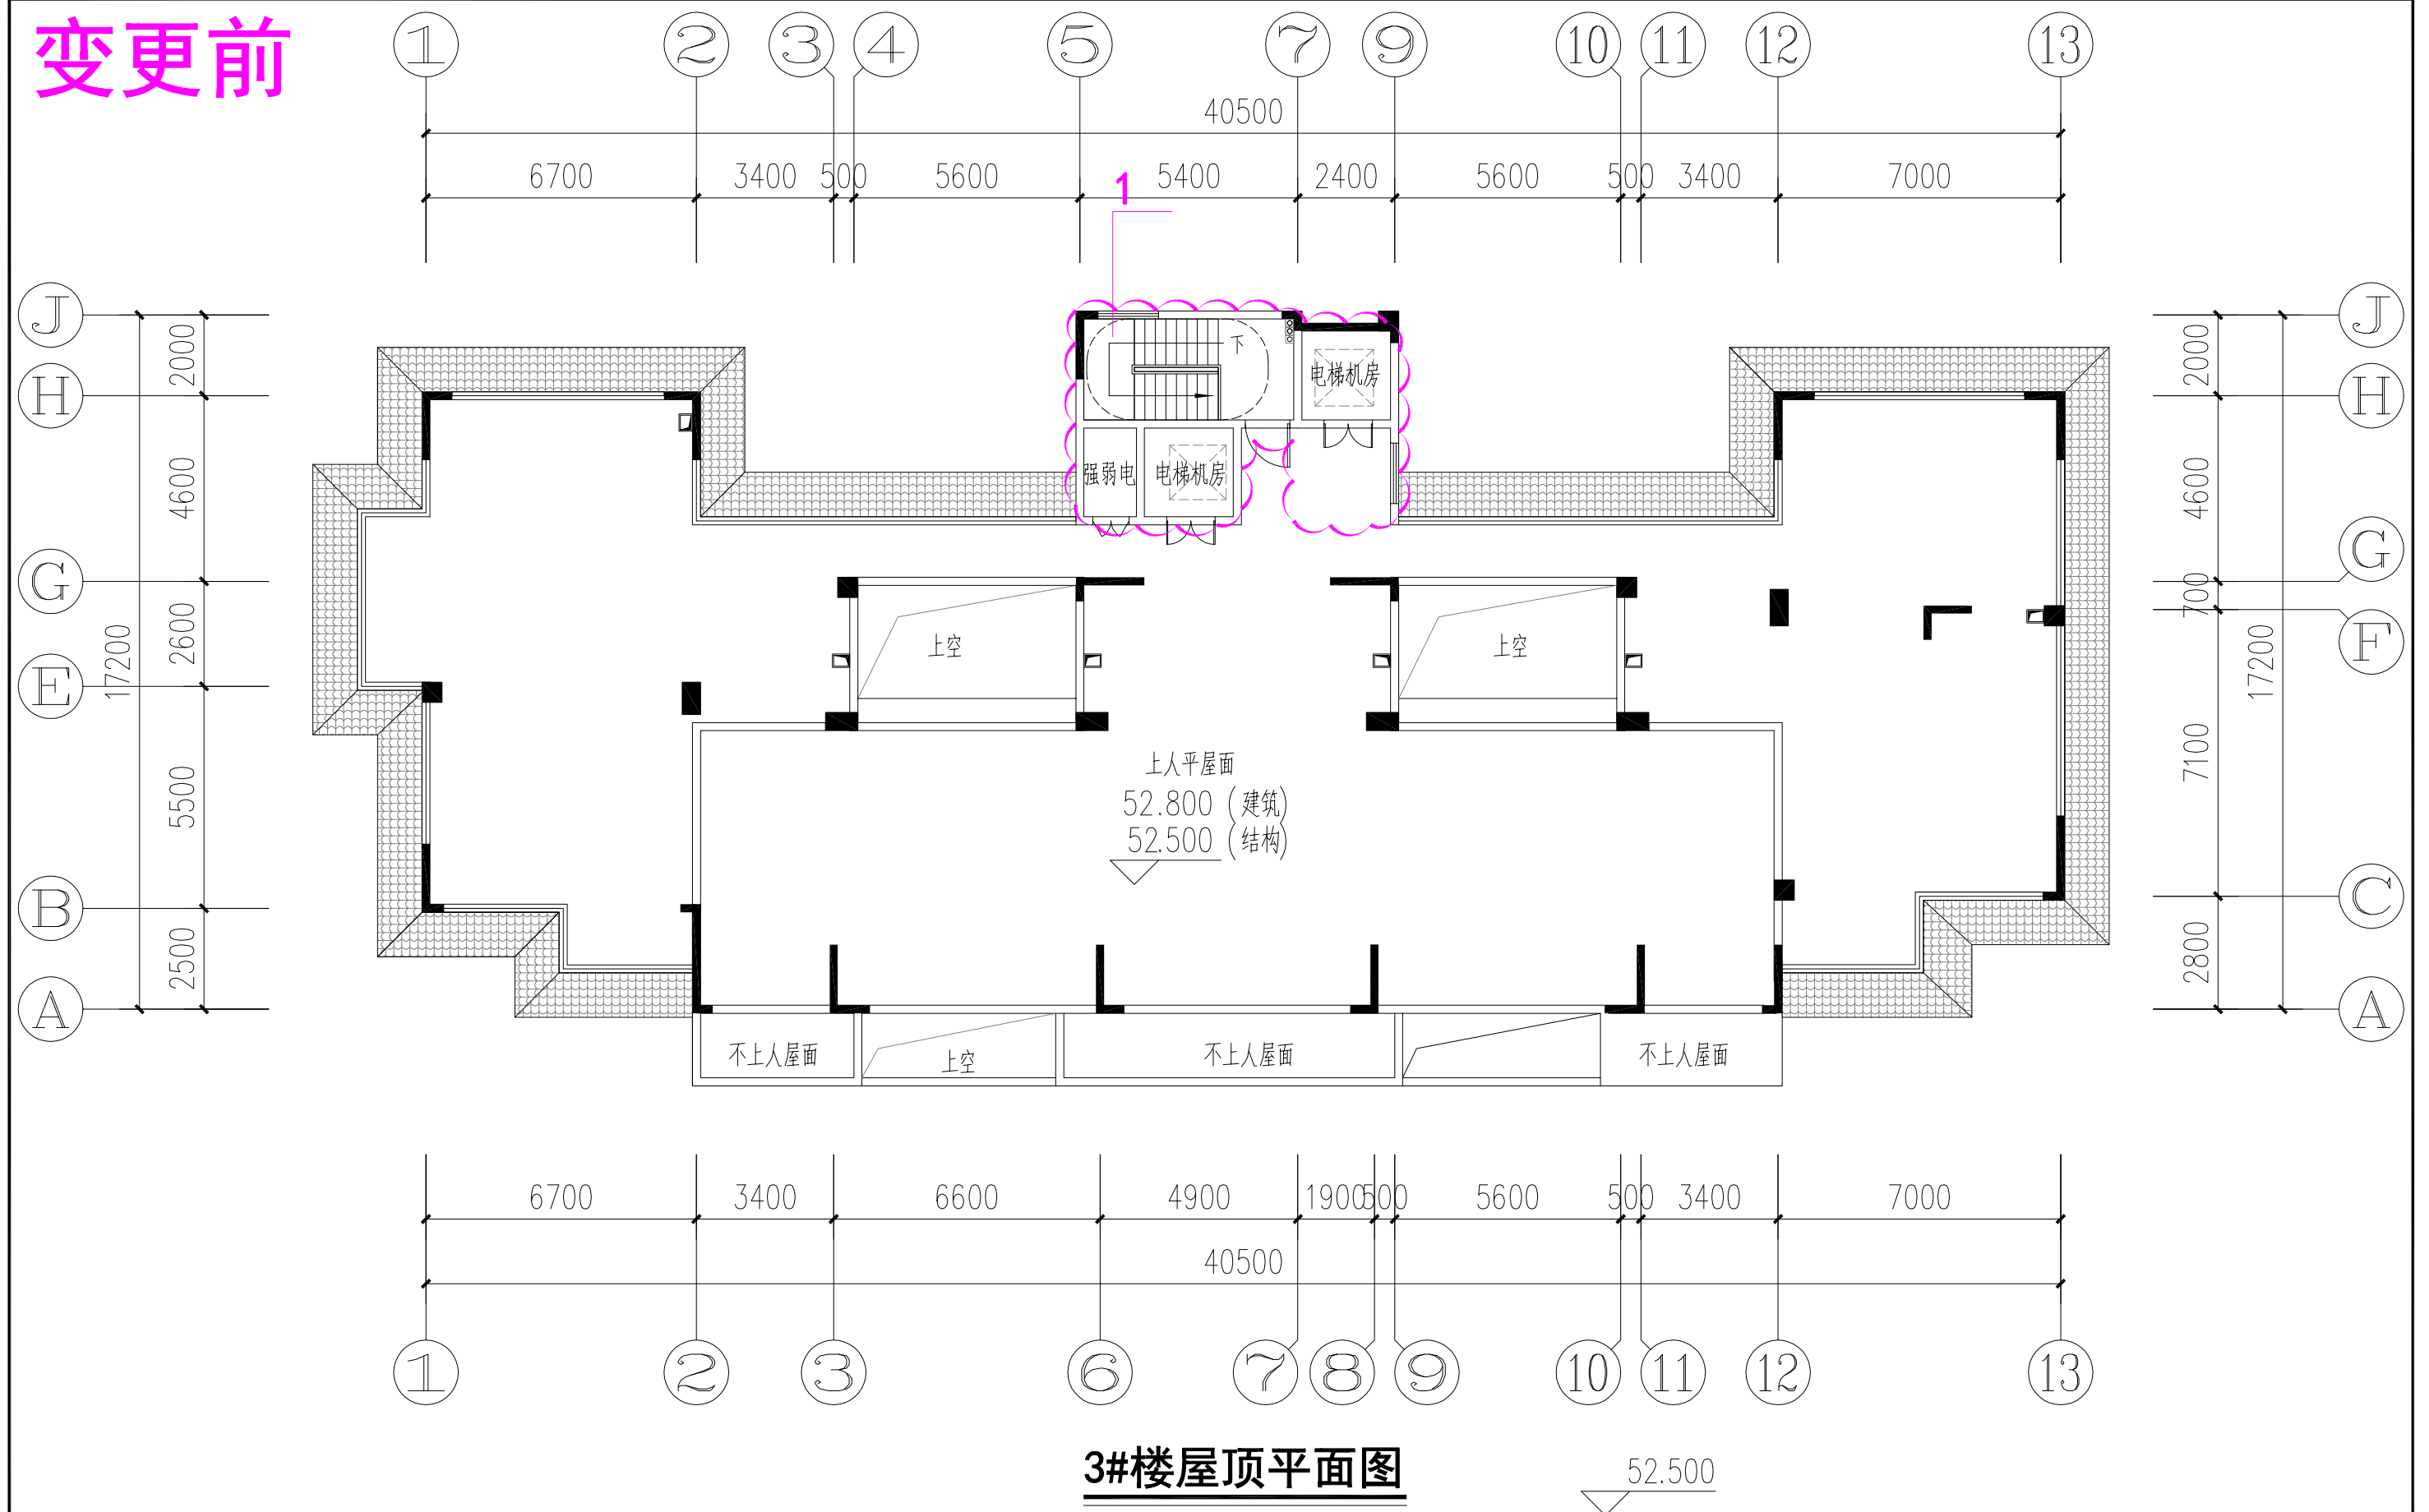

设计单位	福建一建集团有限公司	建设单位	三明市三元区城市建设投资有限责任公司	工程名称	荆东安置房及周边附属配套工程（安置房）	图 名	3#楼屋顶平面图	图 别	方 案
								日 期	2020. 12

变更后

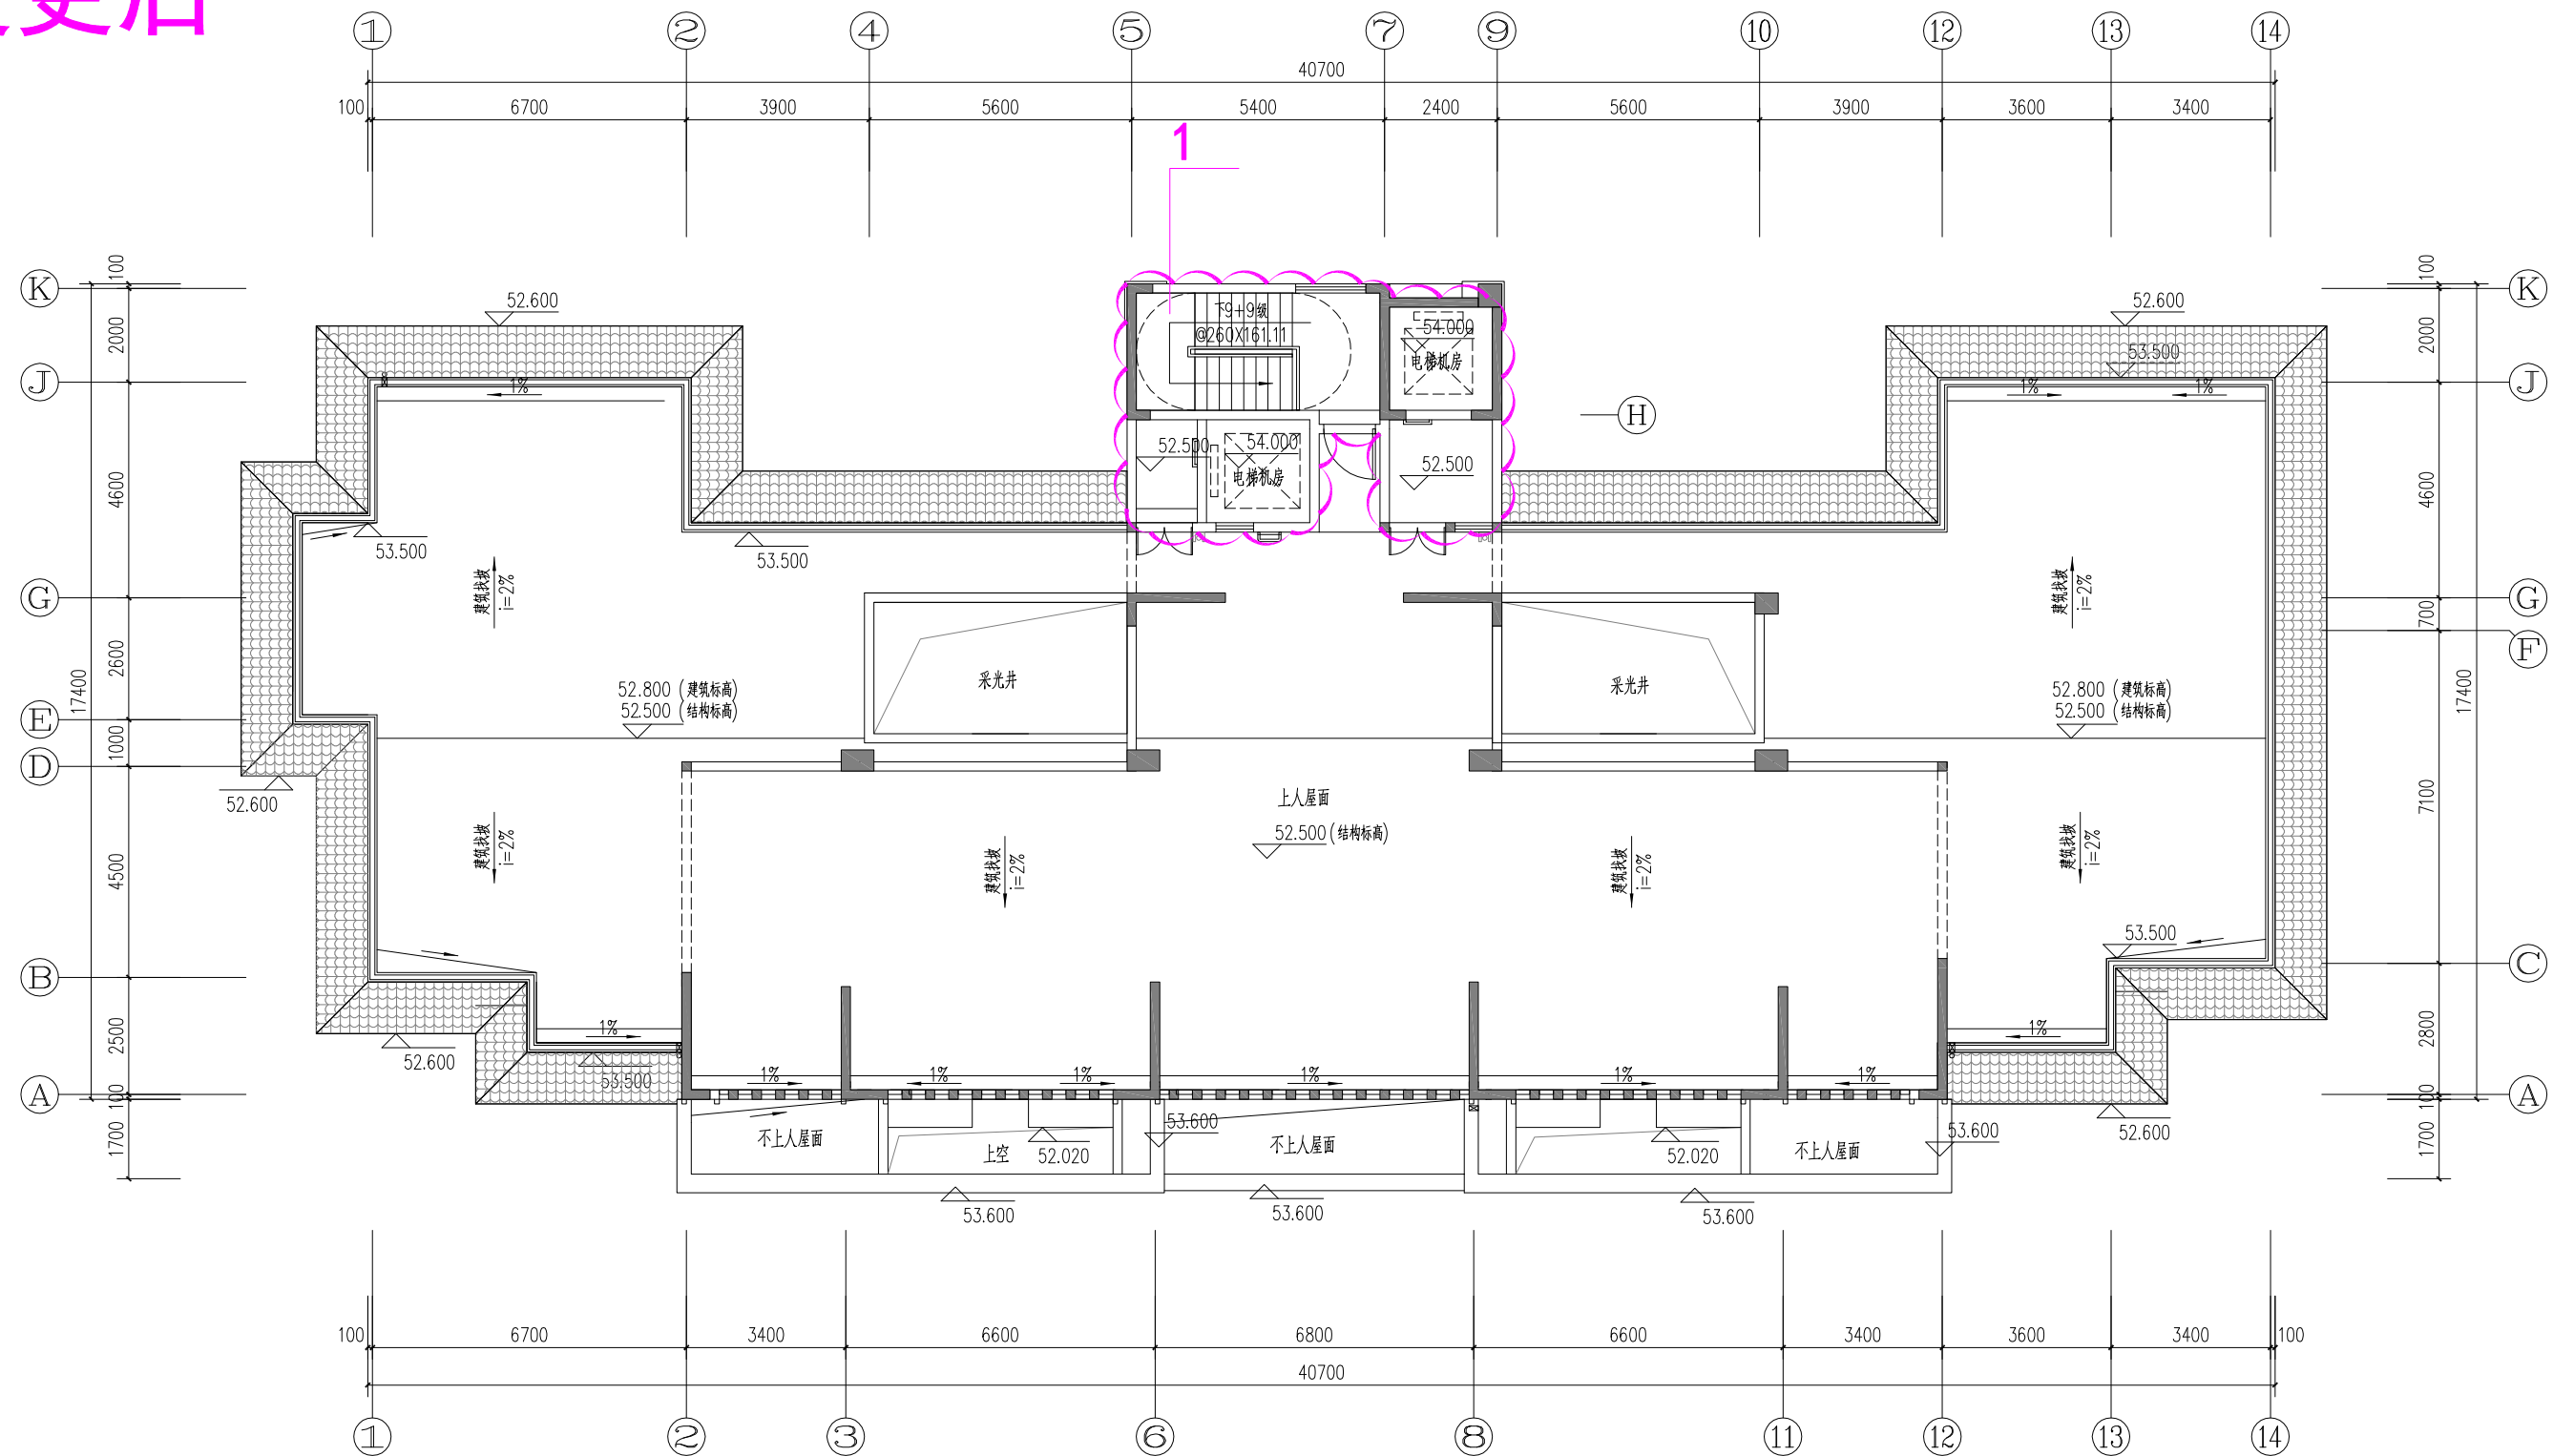


3#楼屋顶平面图

1. 电梯机房调整, 强弱电井取消

设计单位	福建一建集团有限公司	建设单位	三明市三元区城市建设投资有限责任公司	工程名称	荆东安置房及周边附属配套工程（安置房）	图 名	3#楼屋顶平面图	图 别	方 案
								日 期	2023. 07

变更前

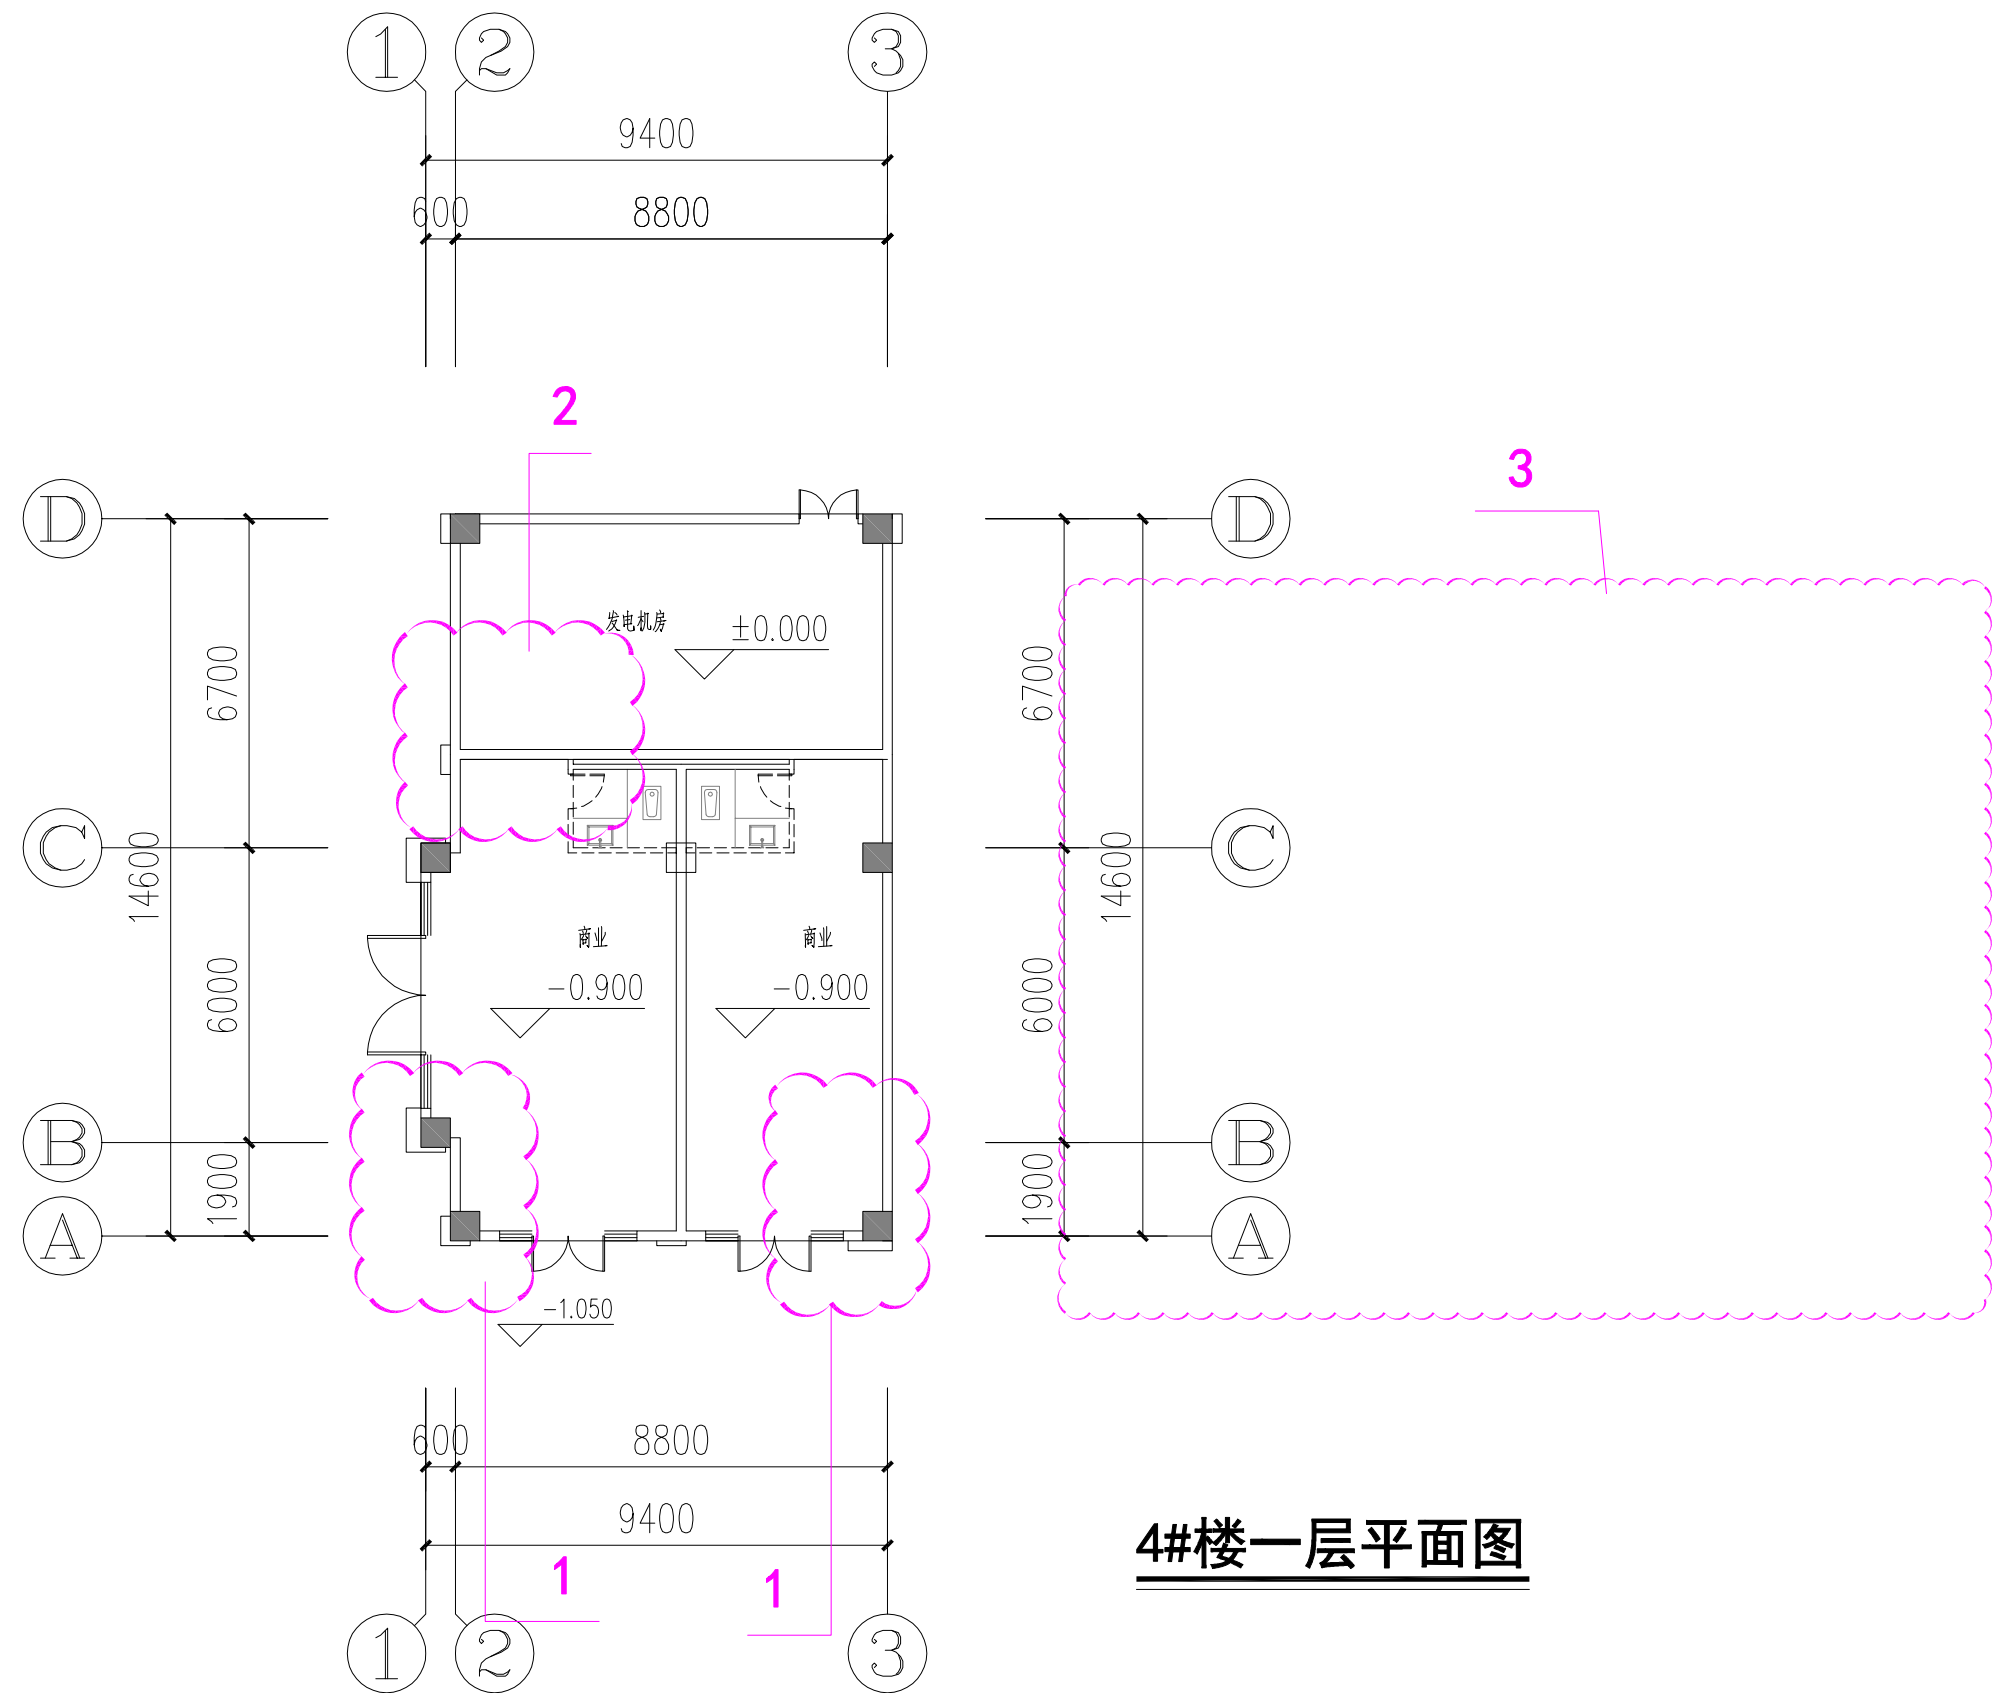


4#楼一层平面图

设计单位	福建一建集团有限公司	建设单位	三明市三元区城市建设投资有限责任公司	工程名称	荆东安置房及周边附属配套工程（安置房）	图 名	4#楼一层平面图	图 别	方 案
								日 期	2020. 12

变更后


1. 增设墙体, 柱子尺寸变更
2. 发电机房内增设储油间
3. 门卫平面图原绘制在1#楼, 现绘制在4#楼, 宽度减少0.3m, 计容面积减少2m², 不计容面积增加2m²

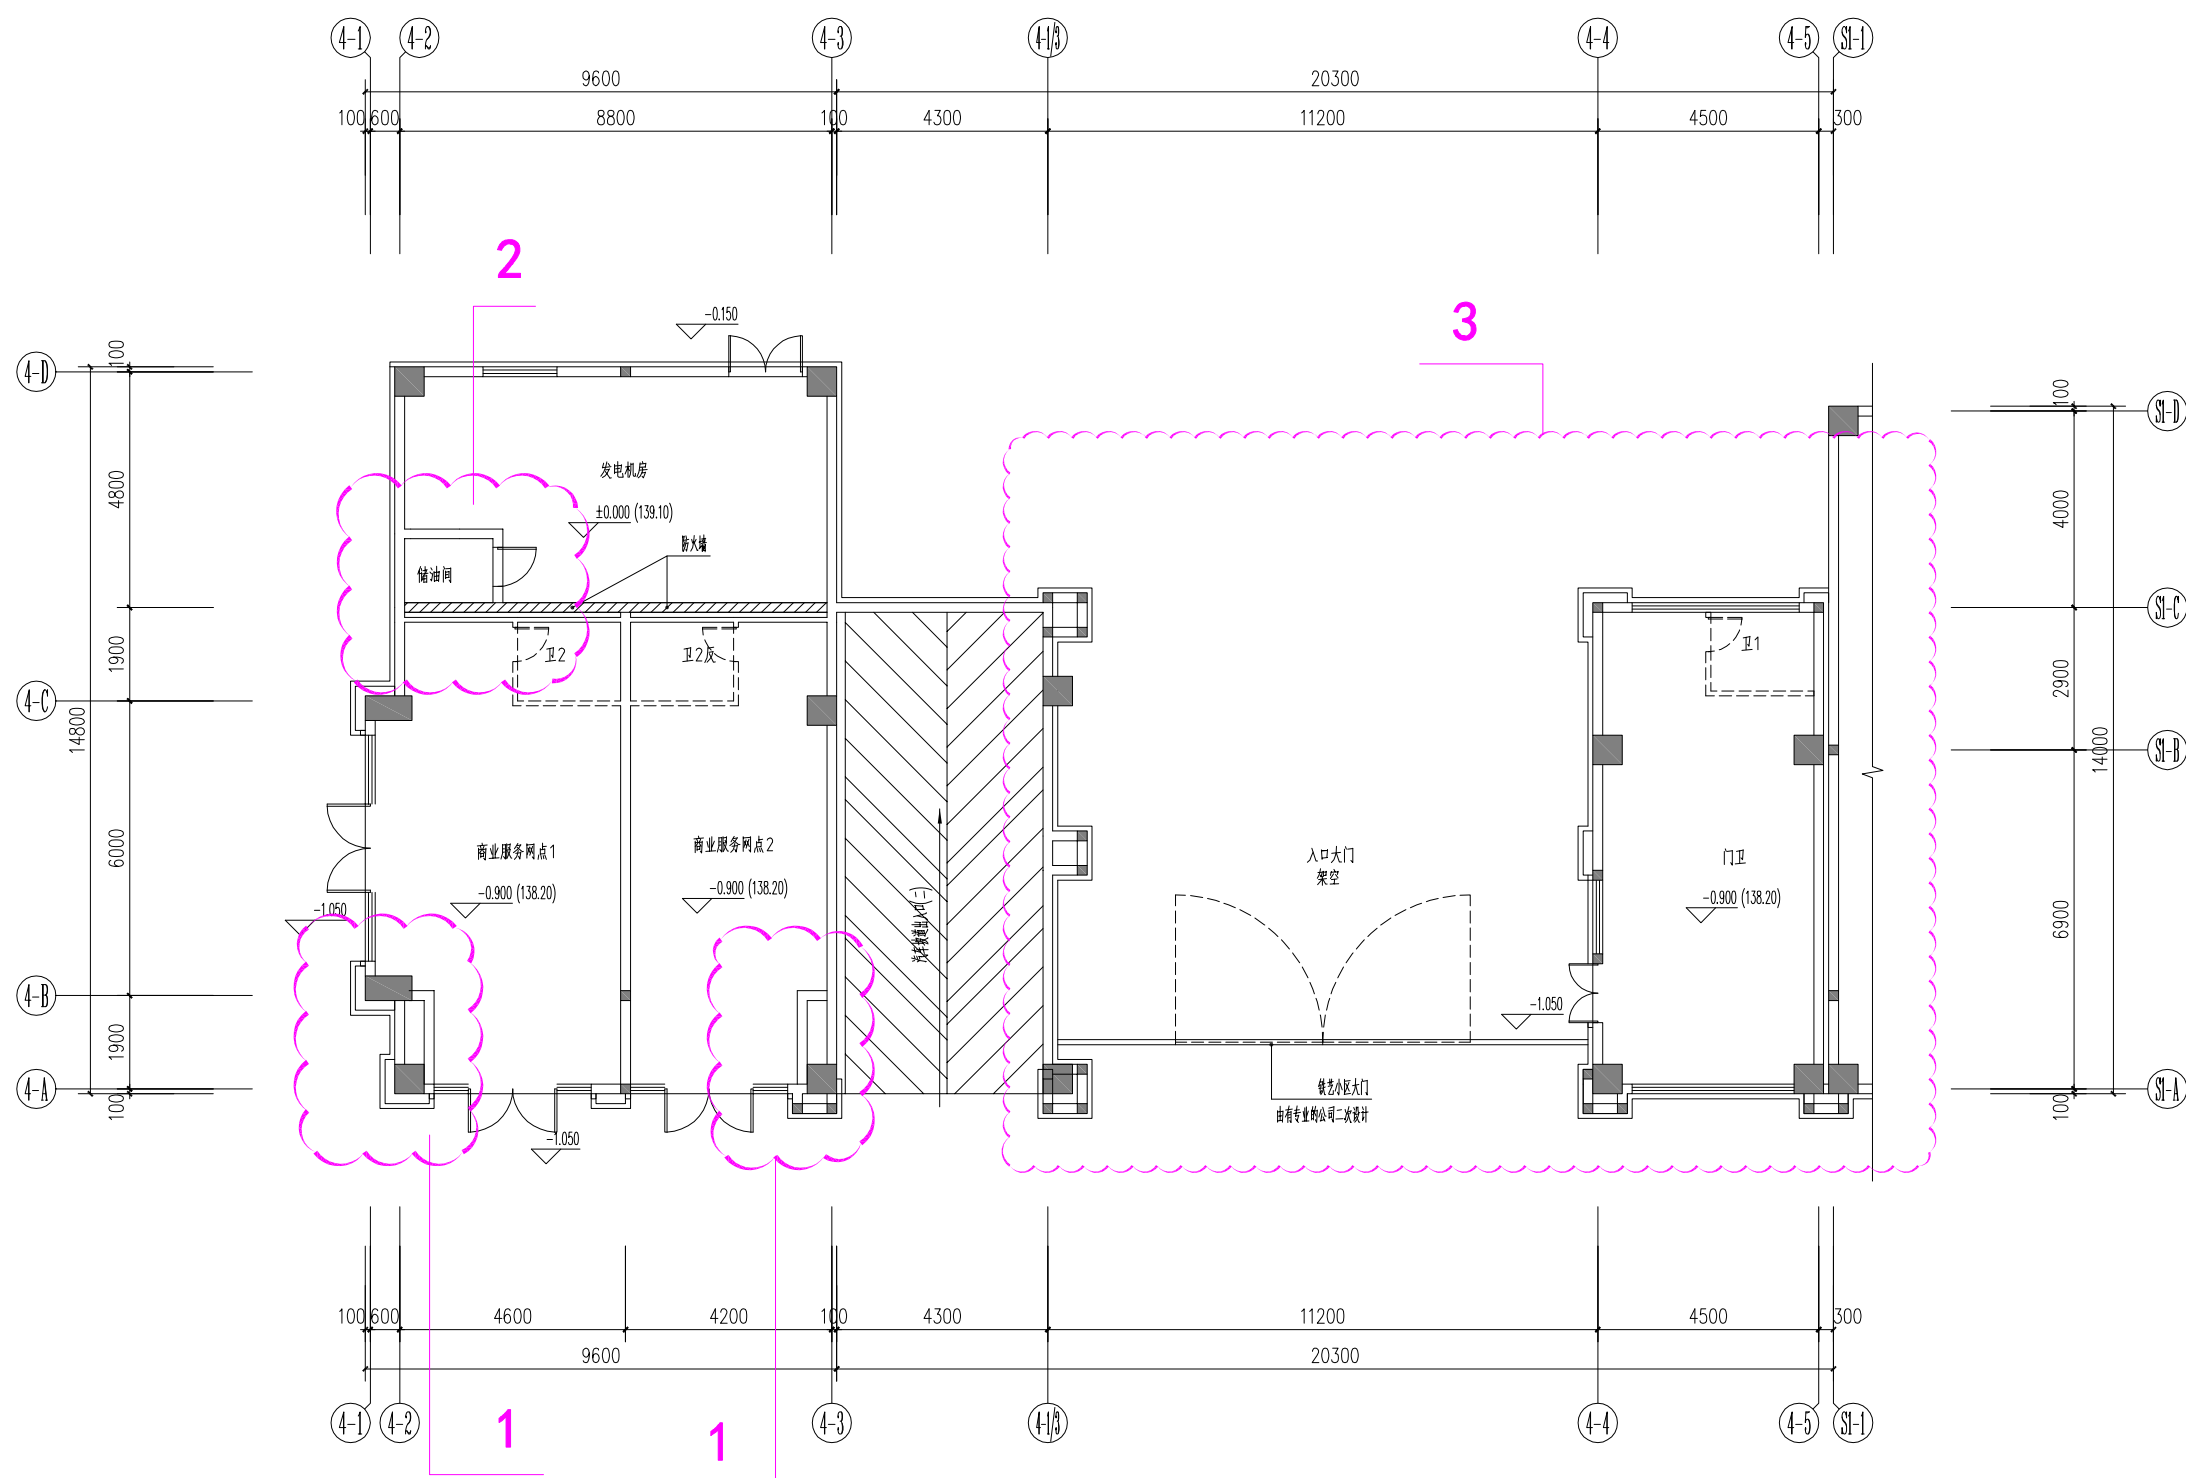

4#楼、门卫一层平面图

设计单位	福建一建集团有限公司	建设单位	三明市三元区城市建设投资有限责任公司	工程名称	荆东安置房及周边附属配套工程（安置房）	图 名	4#楼一层平面图	图 别	方 案
								日 期	2023.07

变更前

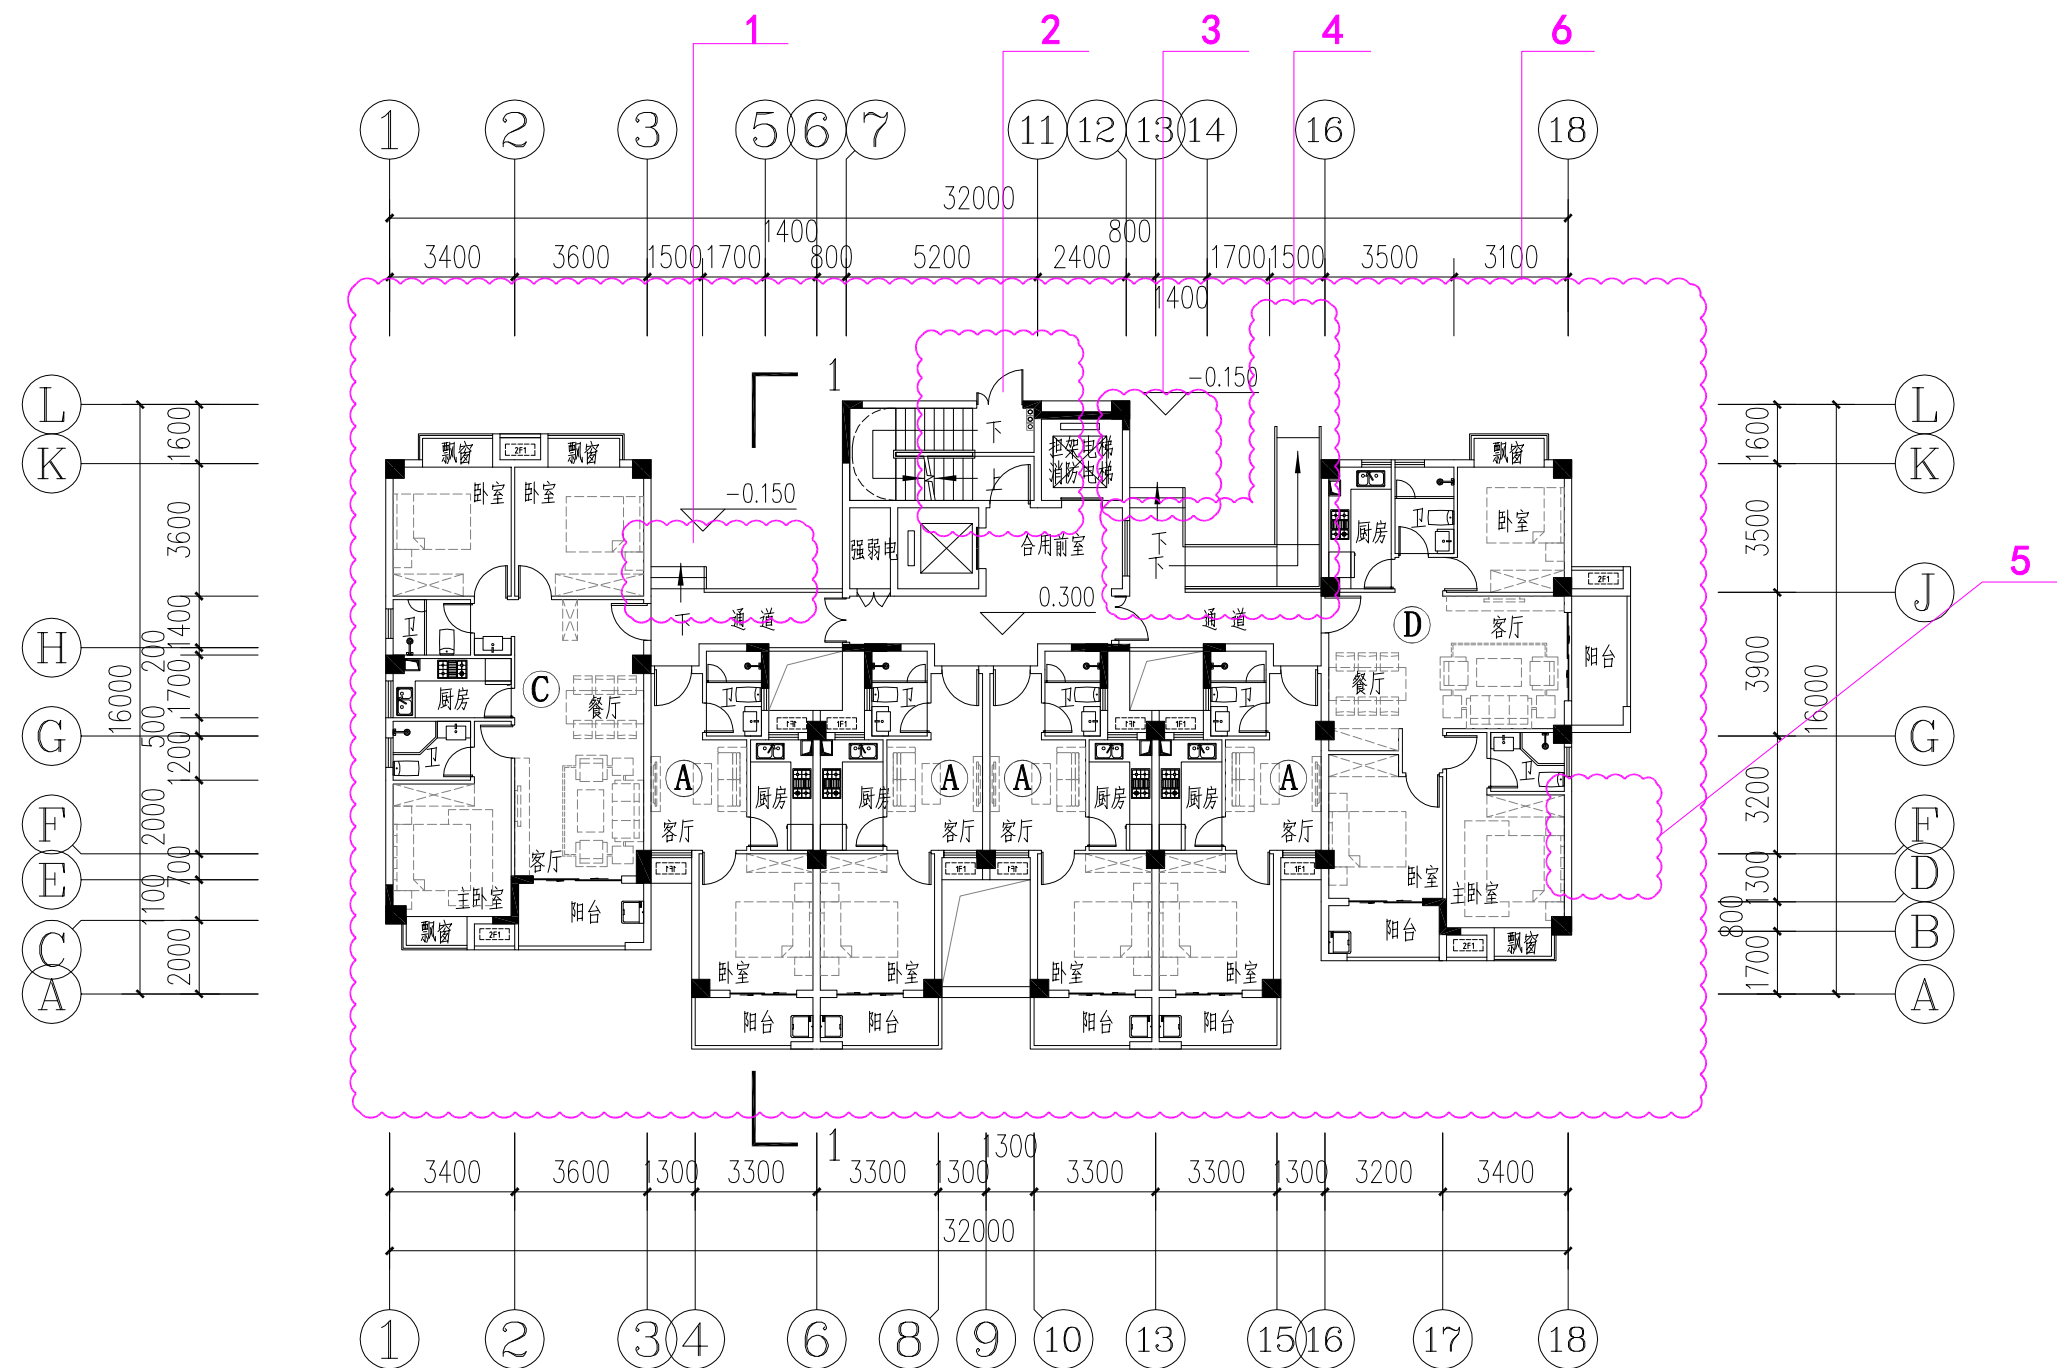


5#楼一层平面图

0.300


设计单位	福建一建集团有限公司	建设单位	三明市三元区城市建设投资有限责任公司	工程名称	荆东安置房及周边附属配套工程（安置房）	图 名	5#楼一层平面图	图 别	方 案
								日 期	2020. 12

- 1、5-K~5-L轴交5-3~5-5轴室外台阶位置调整
- 2、5-L~5-N轴交5-7~5-10轴楼梯间内增设门，外部取消门
- 3、5-L~5-N轴交5-12~5-13轴新增采光通风井
- 4、5-K~5-N轴交5-12~5-15轴无障碍坡道及室外台阶位置调整
- 5、5-F~5-G轴交5-17轴新增排风井
- 6、一至屋顶层柱网及剪力墙调整

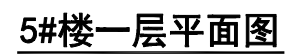

设计单位	福建一建集团有限公司	建设单位	三明市三元区城市建设投资有限责任公司	工程名称	荆东安置房及周边附属配套工程（安置房）	图名	5#楼一层平面图	图别	方 案
								日期	2023. 07

变更前

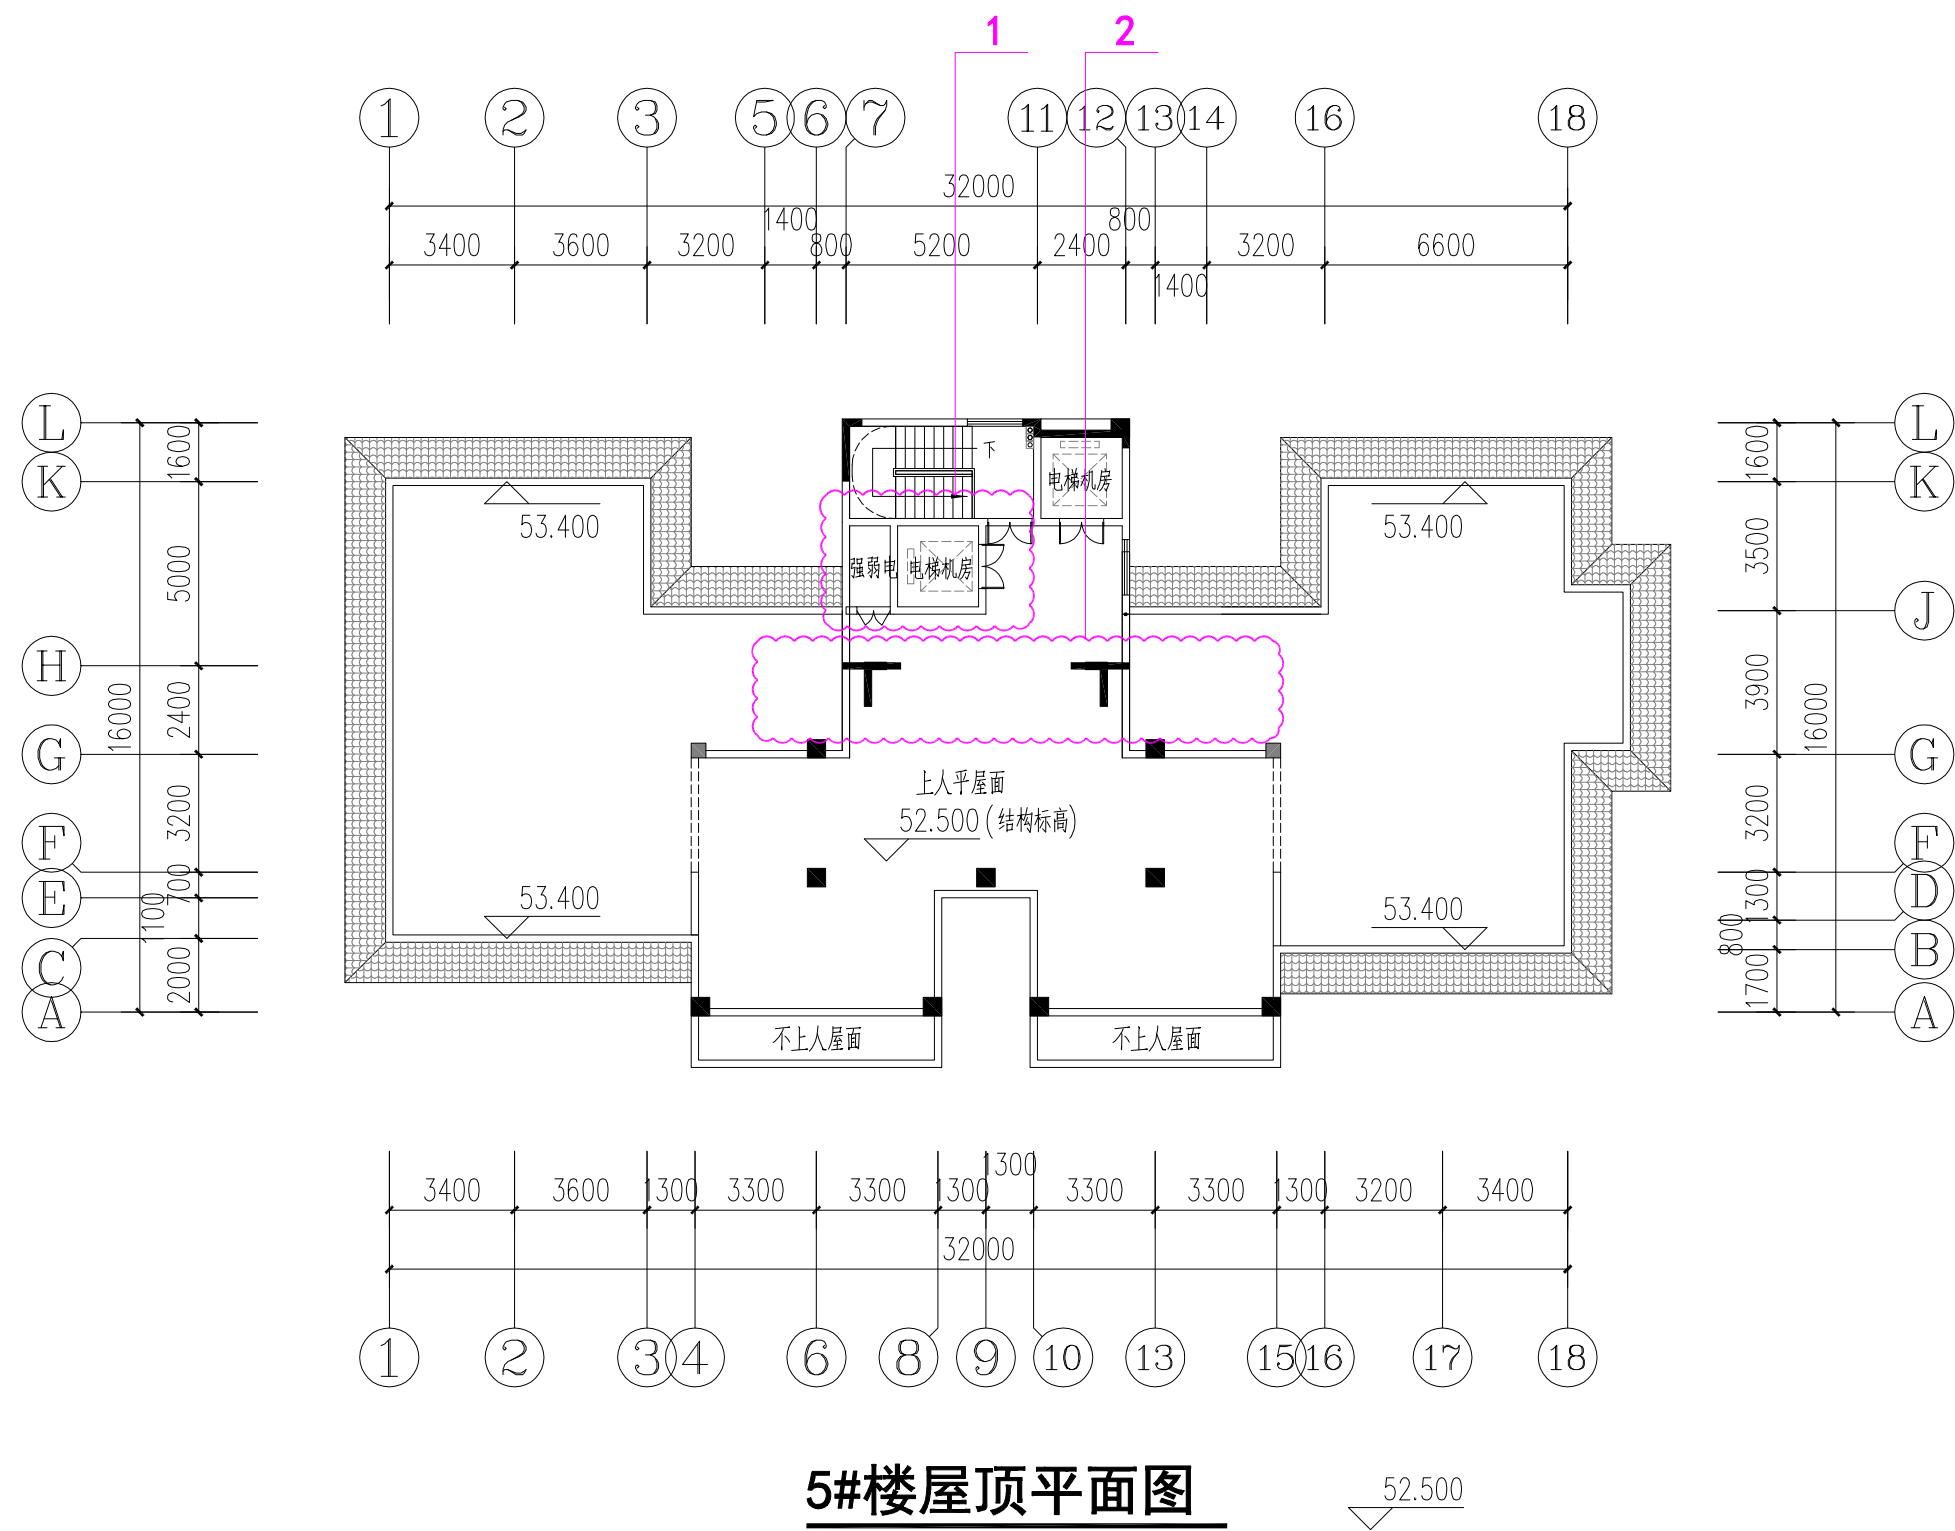
[illegible]

- 1、5-J~5-L轴交5-5~5-10轴电梯机房调整,强弱电井取消
- 2、5-G~5-J轴交5-4~5-14轴电增设天井上空



设计单位	福建一建集团有限公司	建设单位	三明市三元区城市建设投资有限责任公司	工程名称	荆东安置房及周边附属配套工程（安置房）	图 名	5#楼屋顶平面图	图 别	方 案
								日 期	2023. 07

变更前

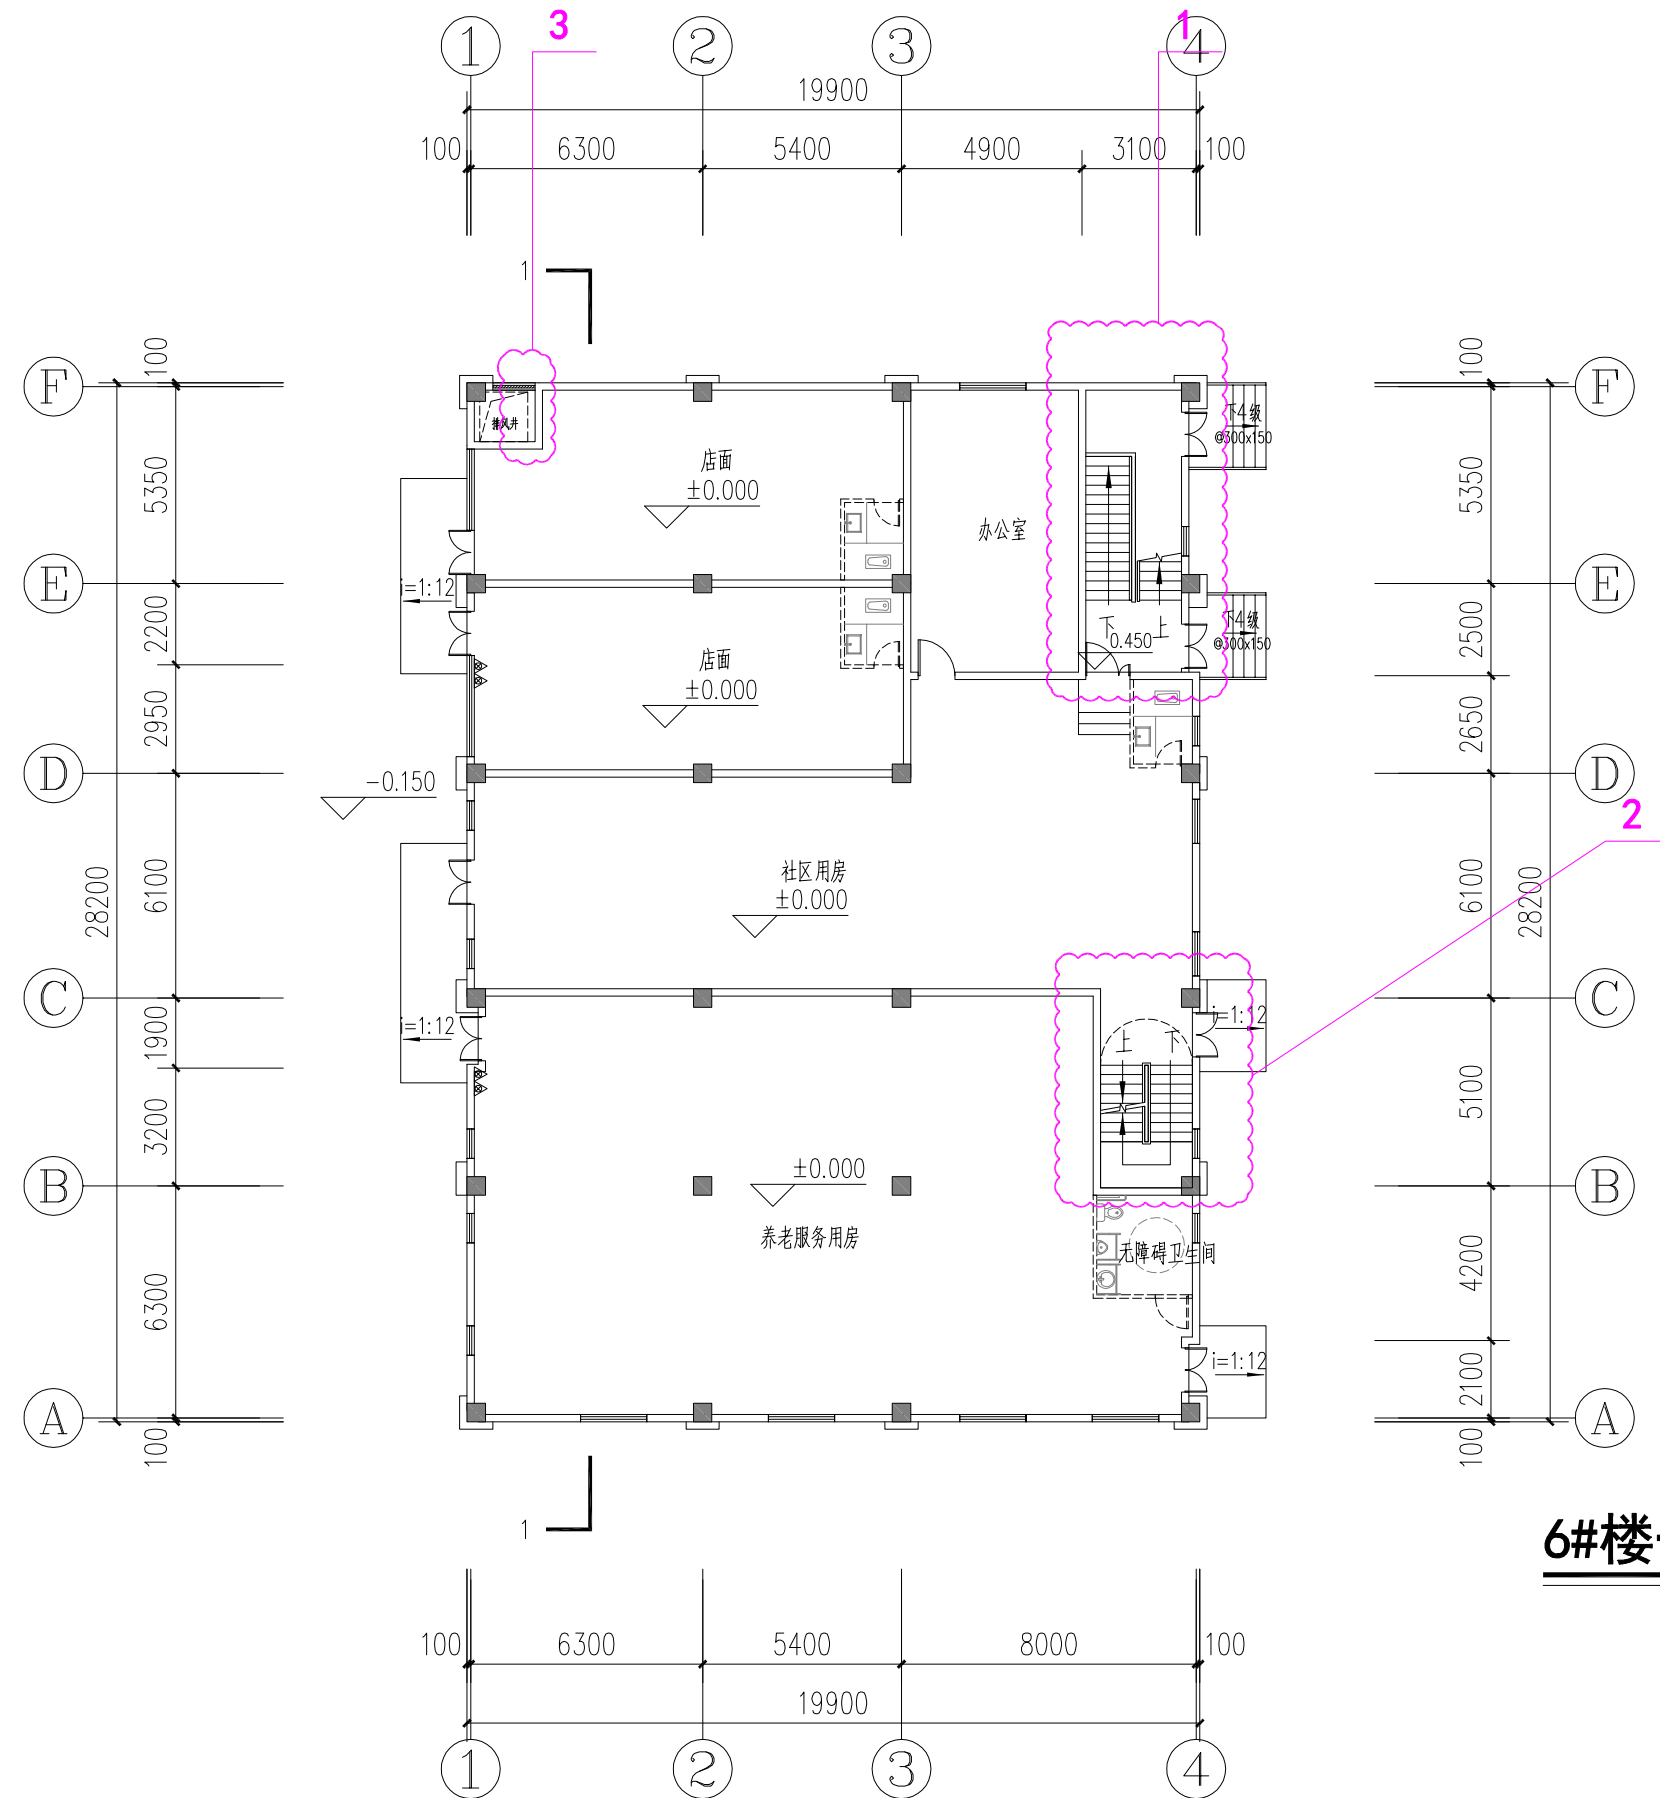


6#楼一层平面图

设计单位	福建一建集团有限公司	建设单位	三明市三元区城市建设投资有限责任公司	工程名称	荆东安置房及周边附属配套工程（安置房）	图名	6#楼一层平面图	图别	方 案
								日期	2020. 12

变更后


- 1、6-D~6-F轴交6-3~6-4轴楼梯上下方向调整
- 2、6-B~6-C轴交6-3~6-4轴楼梯取消向下方向
- 3、6-E~6-F轴交6-1~6-2轴墙体向6-1轴方向移动0.2米

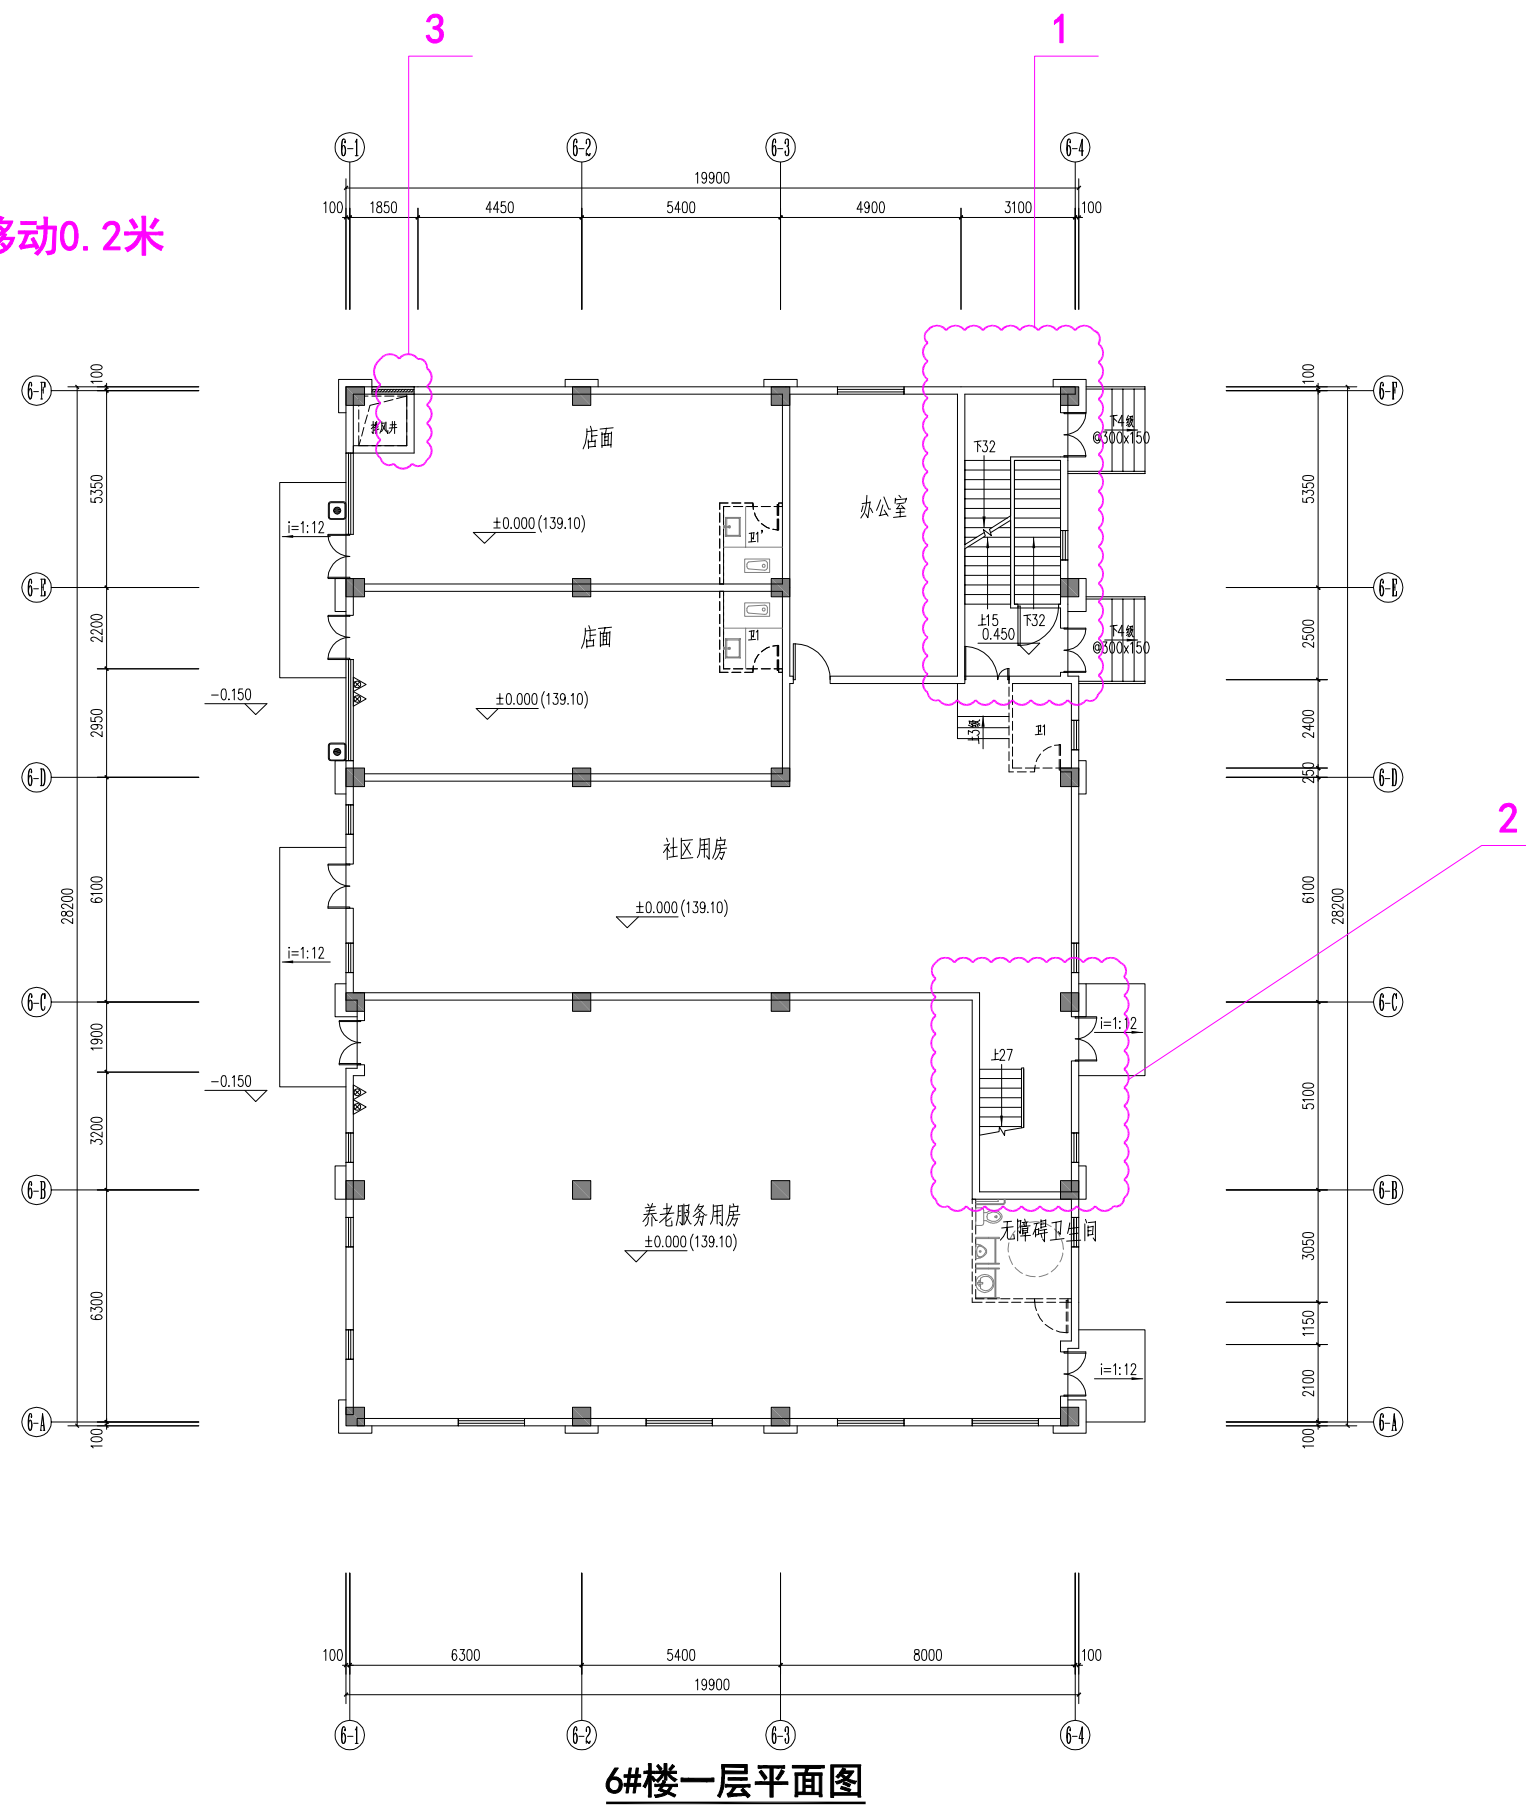

6#楼一层平面图

[illegible]

变更前

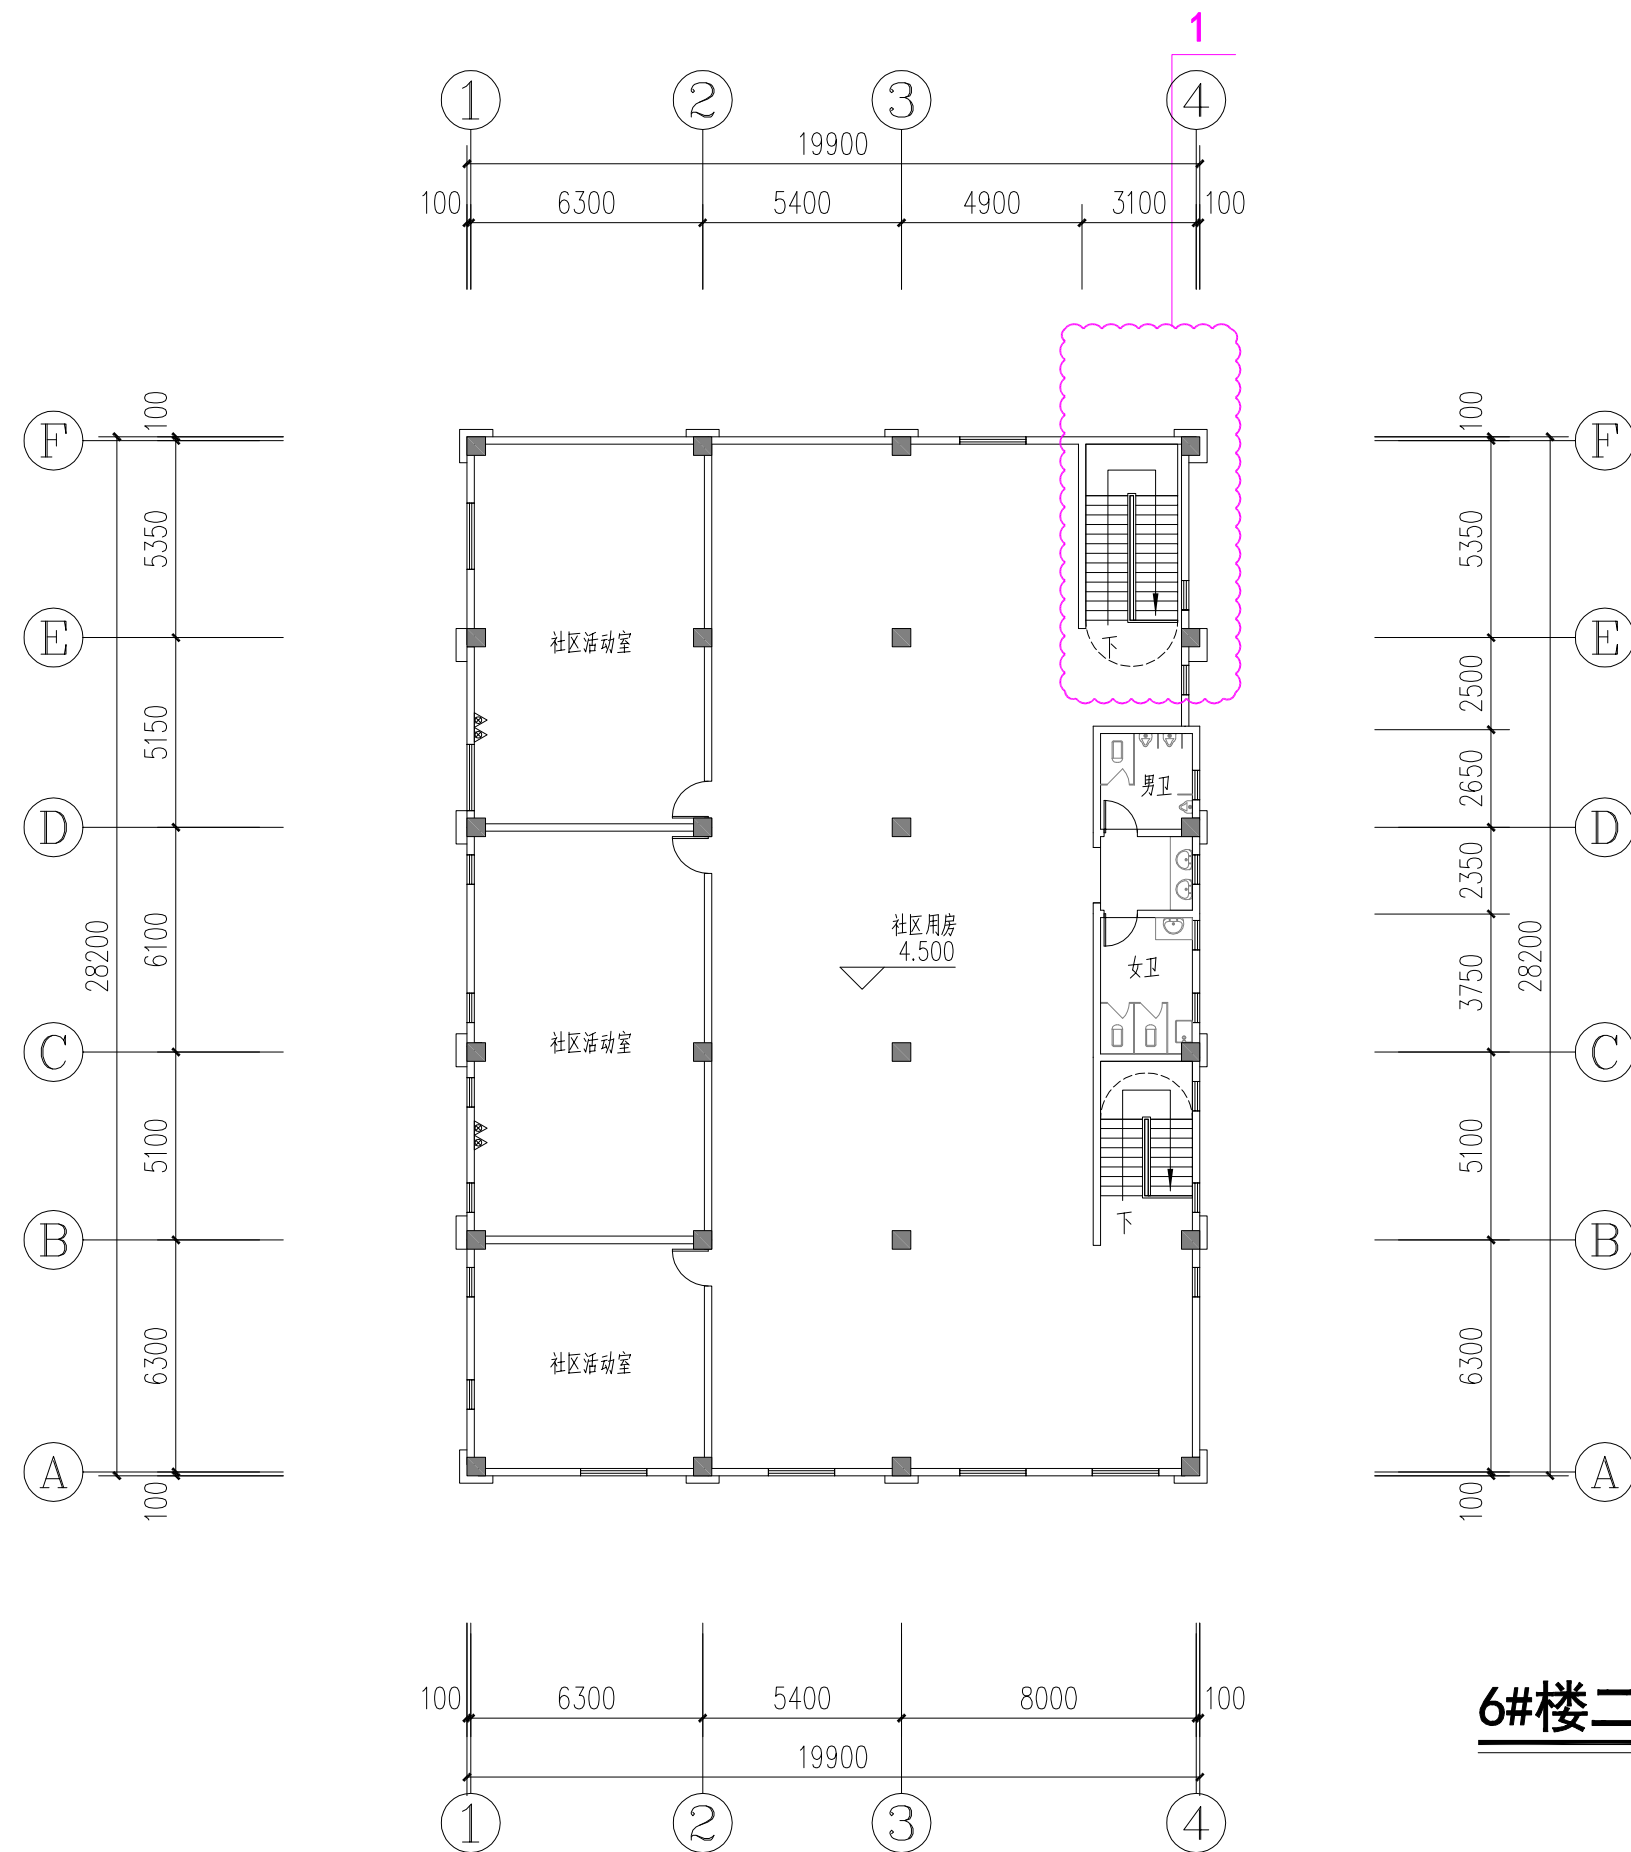


6#楼二层平面图

设计单位	福建一建集团有限公司	建设单位	三明市三元区城市建设投资有限责任公司	工程名称	荆东安置房及周边附属配套工程（安置房）	图 名	6#楼二层平面图	图 别	方 案
								日 期	2020. 12

变更后


1、6-D~6-F轴交6-3~6-4轴楼梯上下方向调整

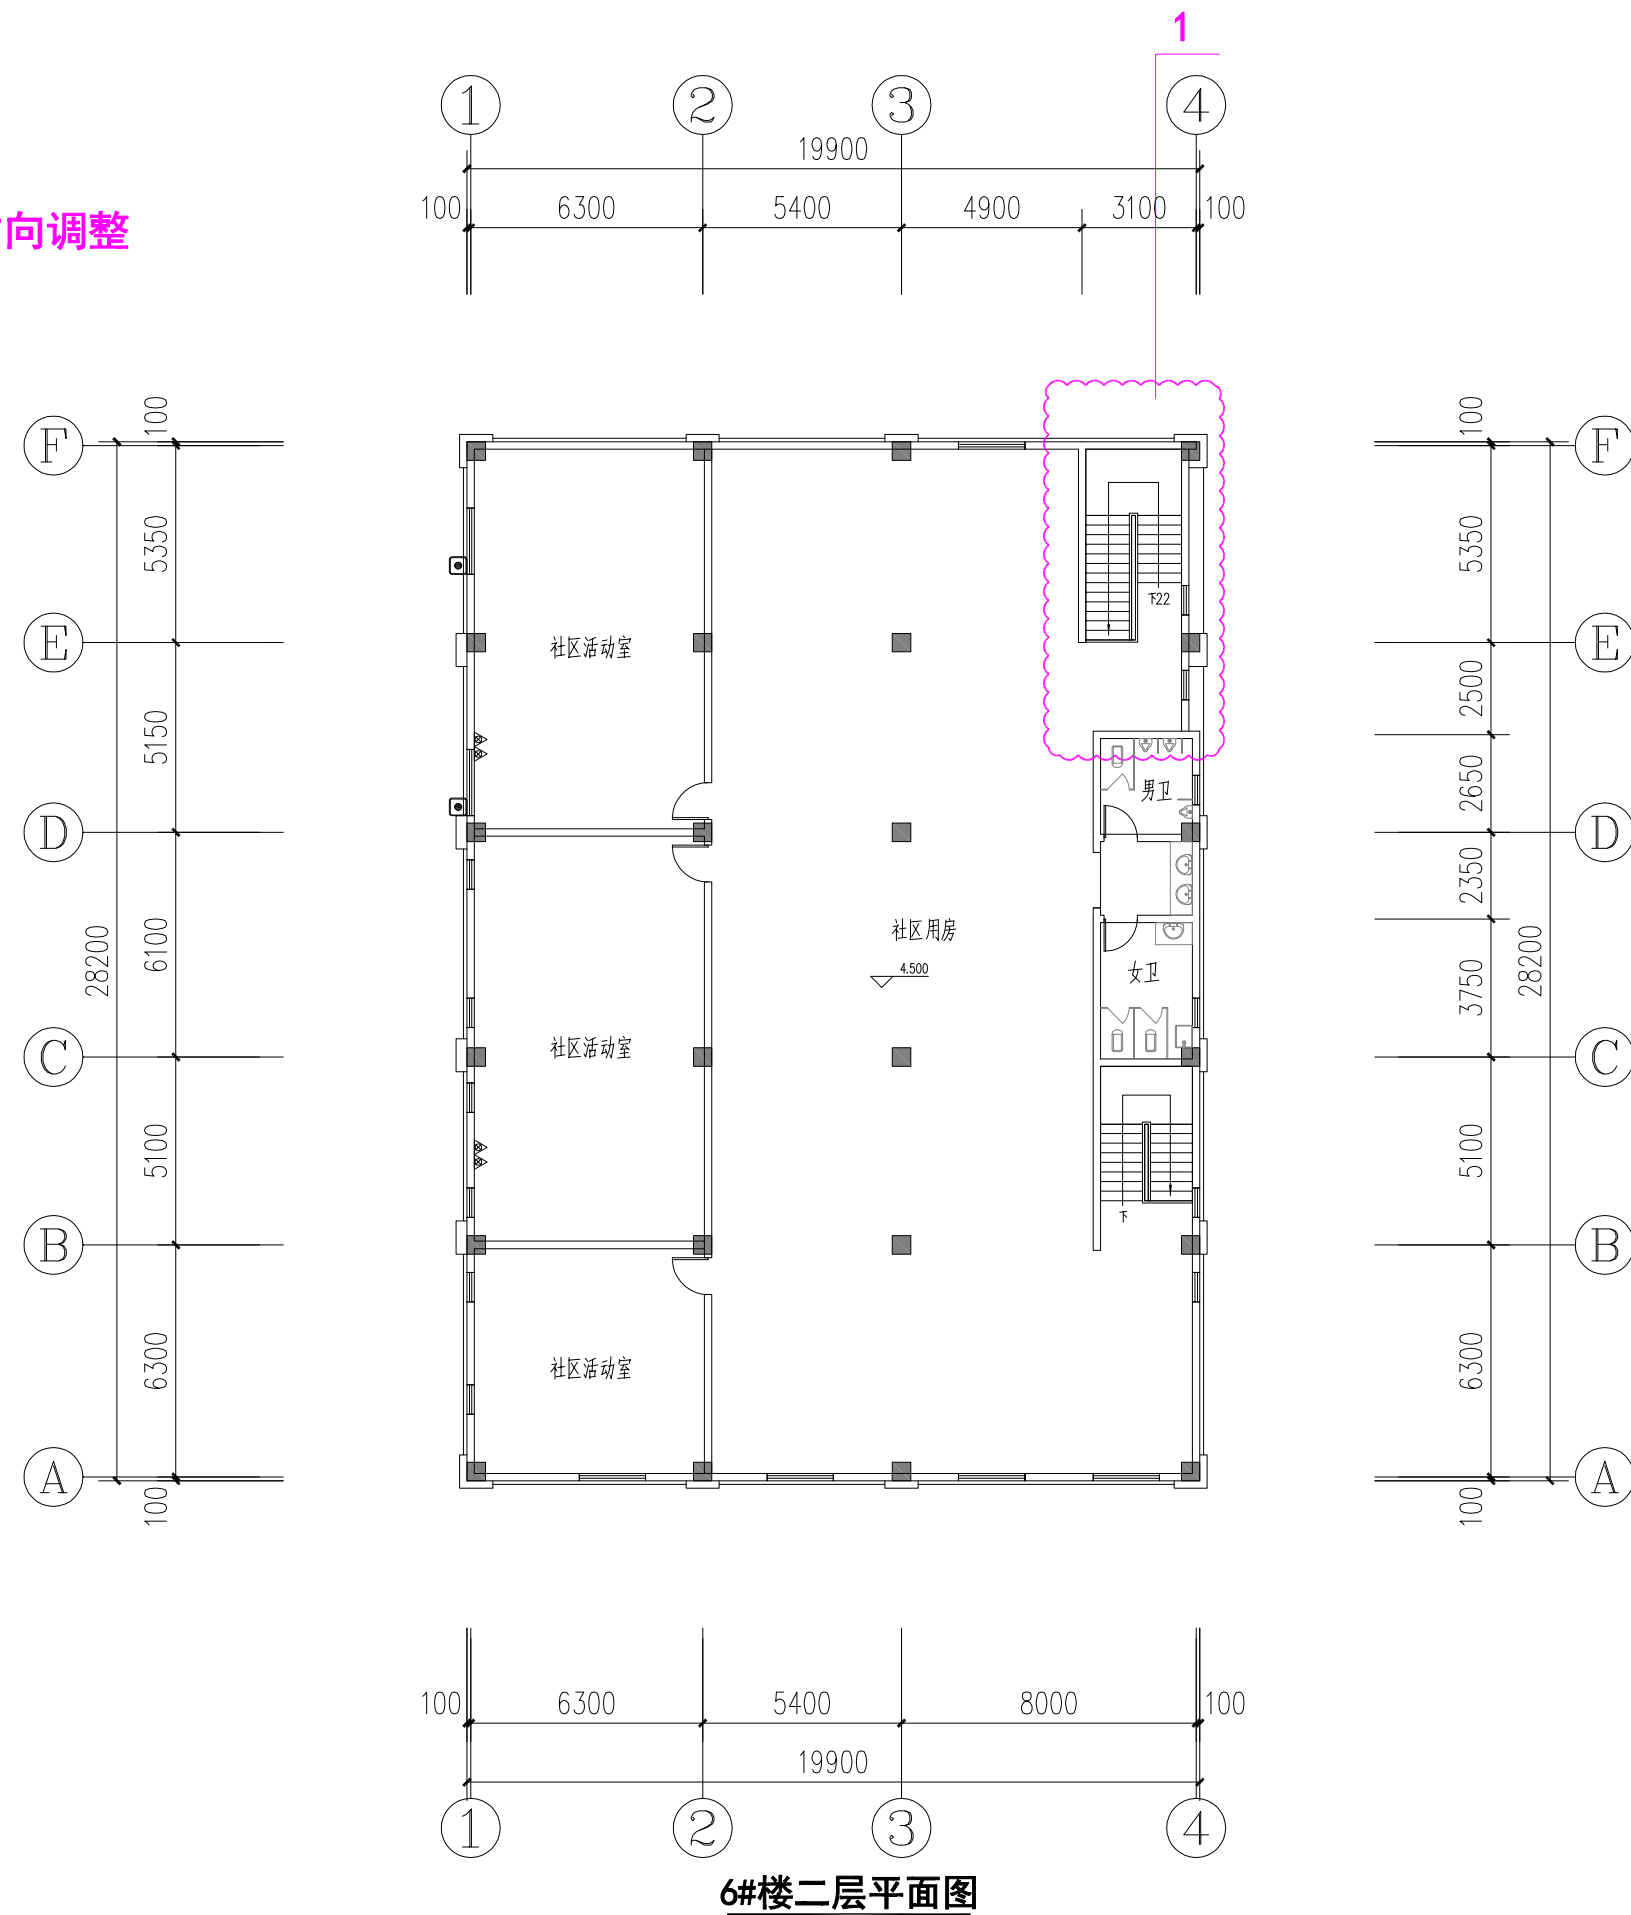

6#楼二层平面图

设计单位	福建一建集团有限公司	建设单位	三明市三元区城市建设投资有限责任公司	工程名称	荆东安置房及周边附属配套工程（安置房）	图 名	6#楼二层平面图	图 别	方 案
								日 期	2023. 07

变更前

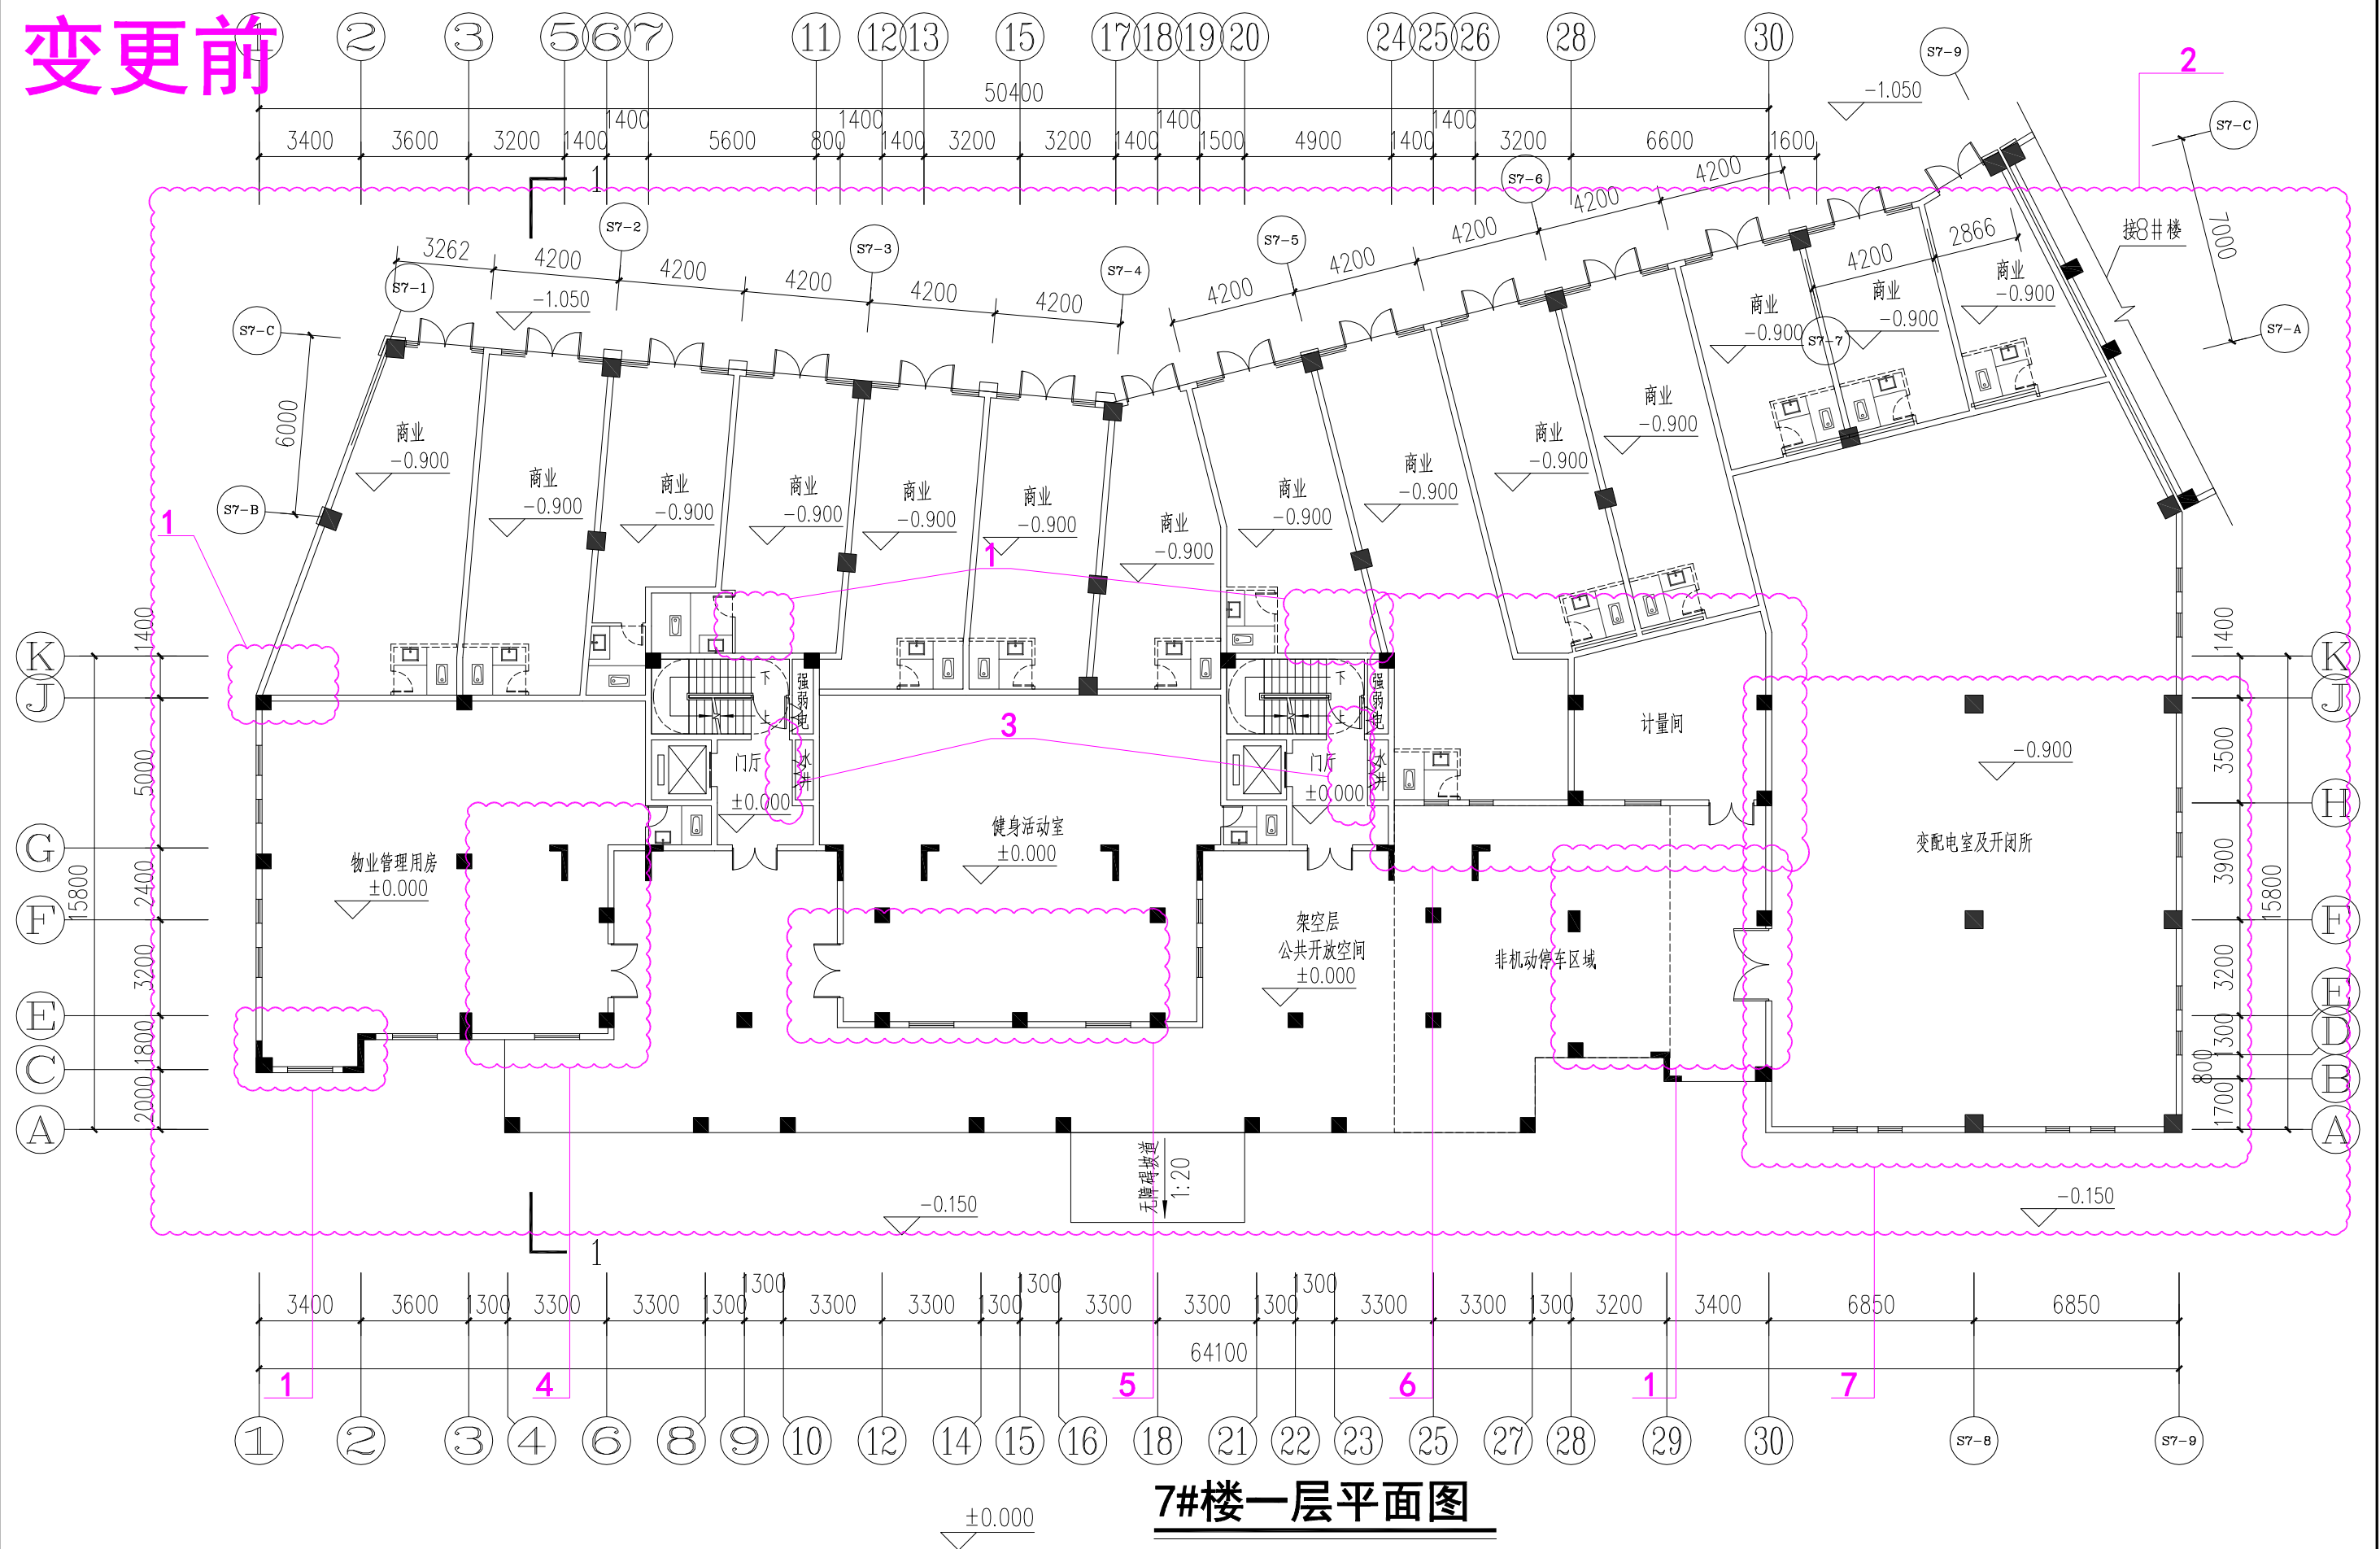


7#楼一层平面图

[illegible]

变更后


- 1、7-C~7-E轴交7-1~7-2轴、7-L~7-M轴交7-1~7-2轴、7-M轴交7-7~7-9轴、7-M轴交7-22~7-24轴、7-D轴~7-K轴交7-27~7-29轴增设风井、进风井、排风井
- 2、一至屋顶层柱网及剪力墙调整
- 3、7-J~7-L轴交7-9~7-10轴墙体向7-9轴方向移动0.1米、7-J~7-L轴交7-23~7-24轴墙体向7-23轴方向移动0.1米
- 4、7-E~7-G轴交7-4~7-5轴门位置调整、7-E~7-G轴交7-5轴墙体向7-4轴方向移动0.05米
- 5、7-E轴交7-10~7-21轴健身活动室出入口调整
- 6、7-G~7-M轴交7-23~7-29轴计量间位置调整, 墙体外移1.5m
- 7、7-A~7-L轴交7-29~7-31轴变配电室及开闭所布局、室内标高调整

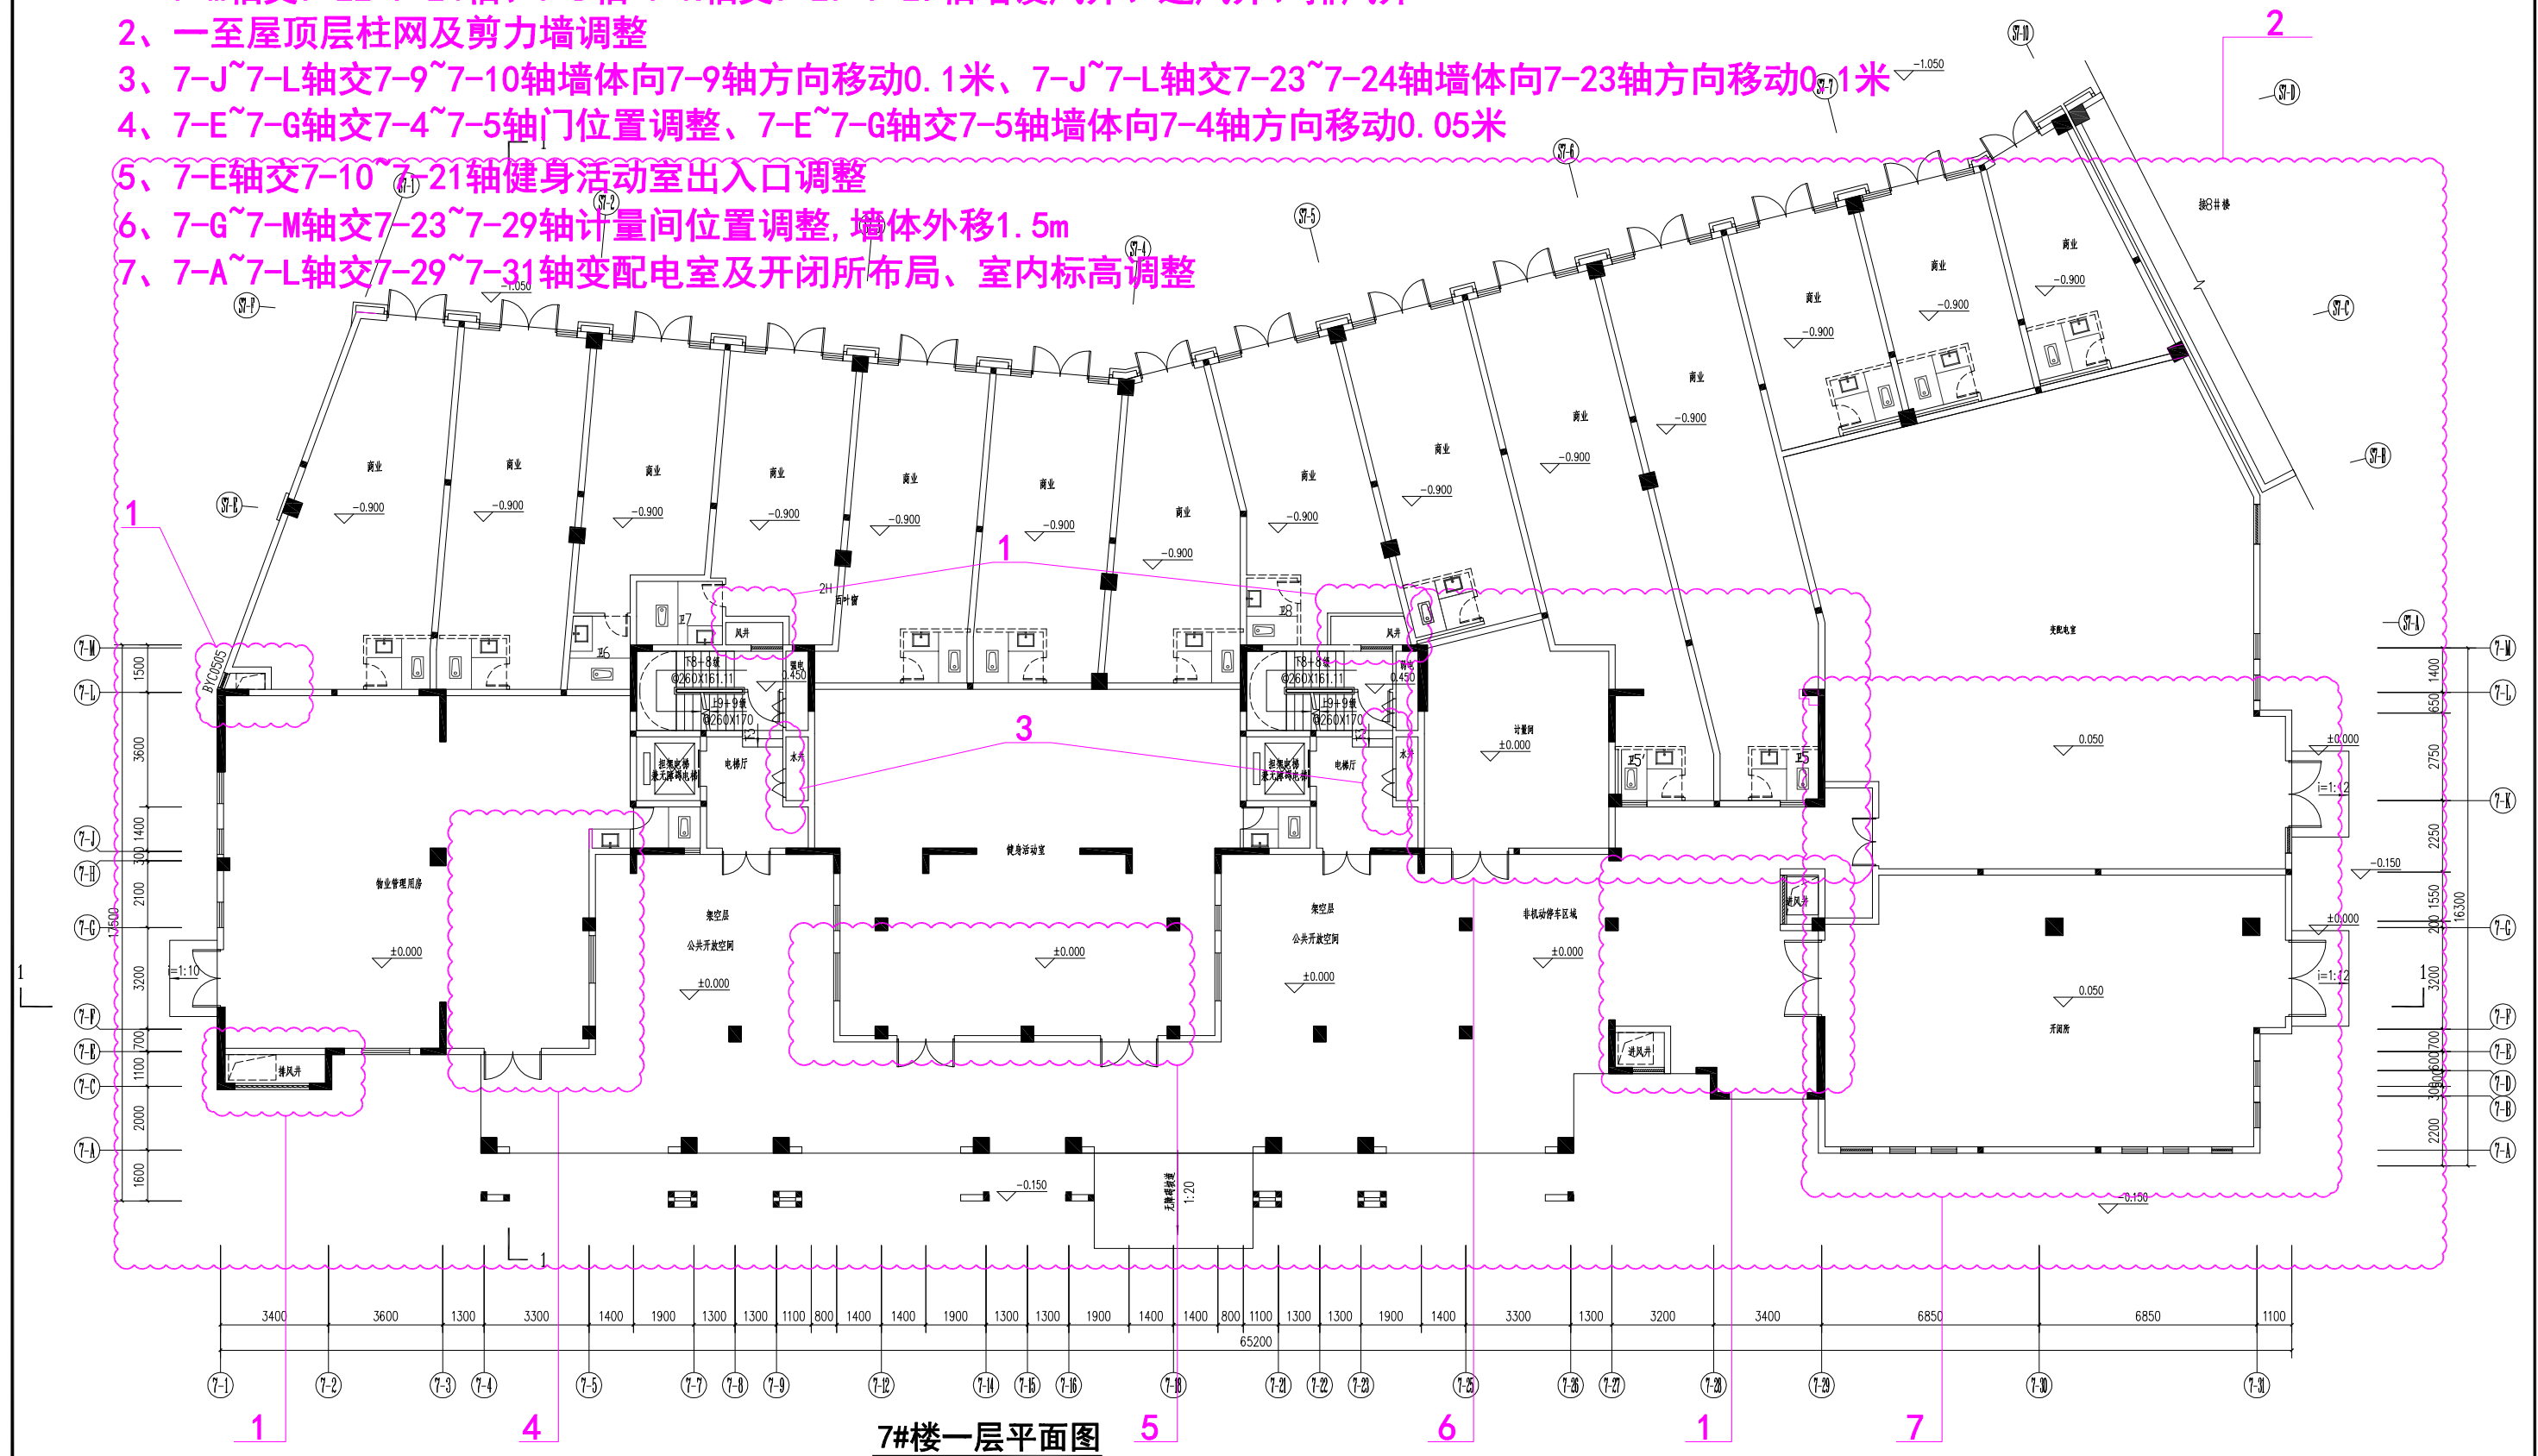

7#楼一层平面图

[illegible]

变更前

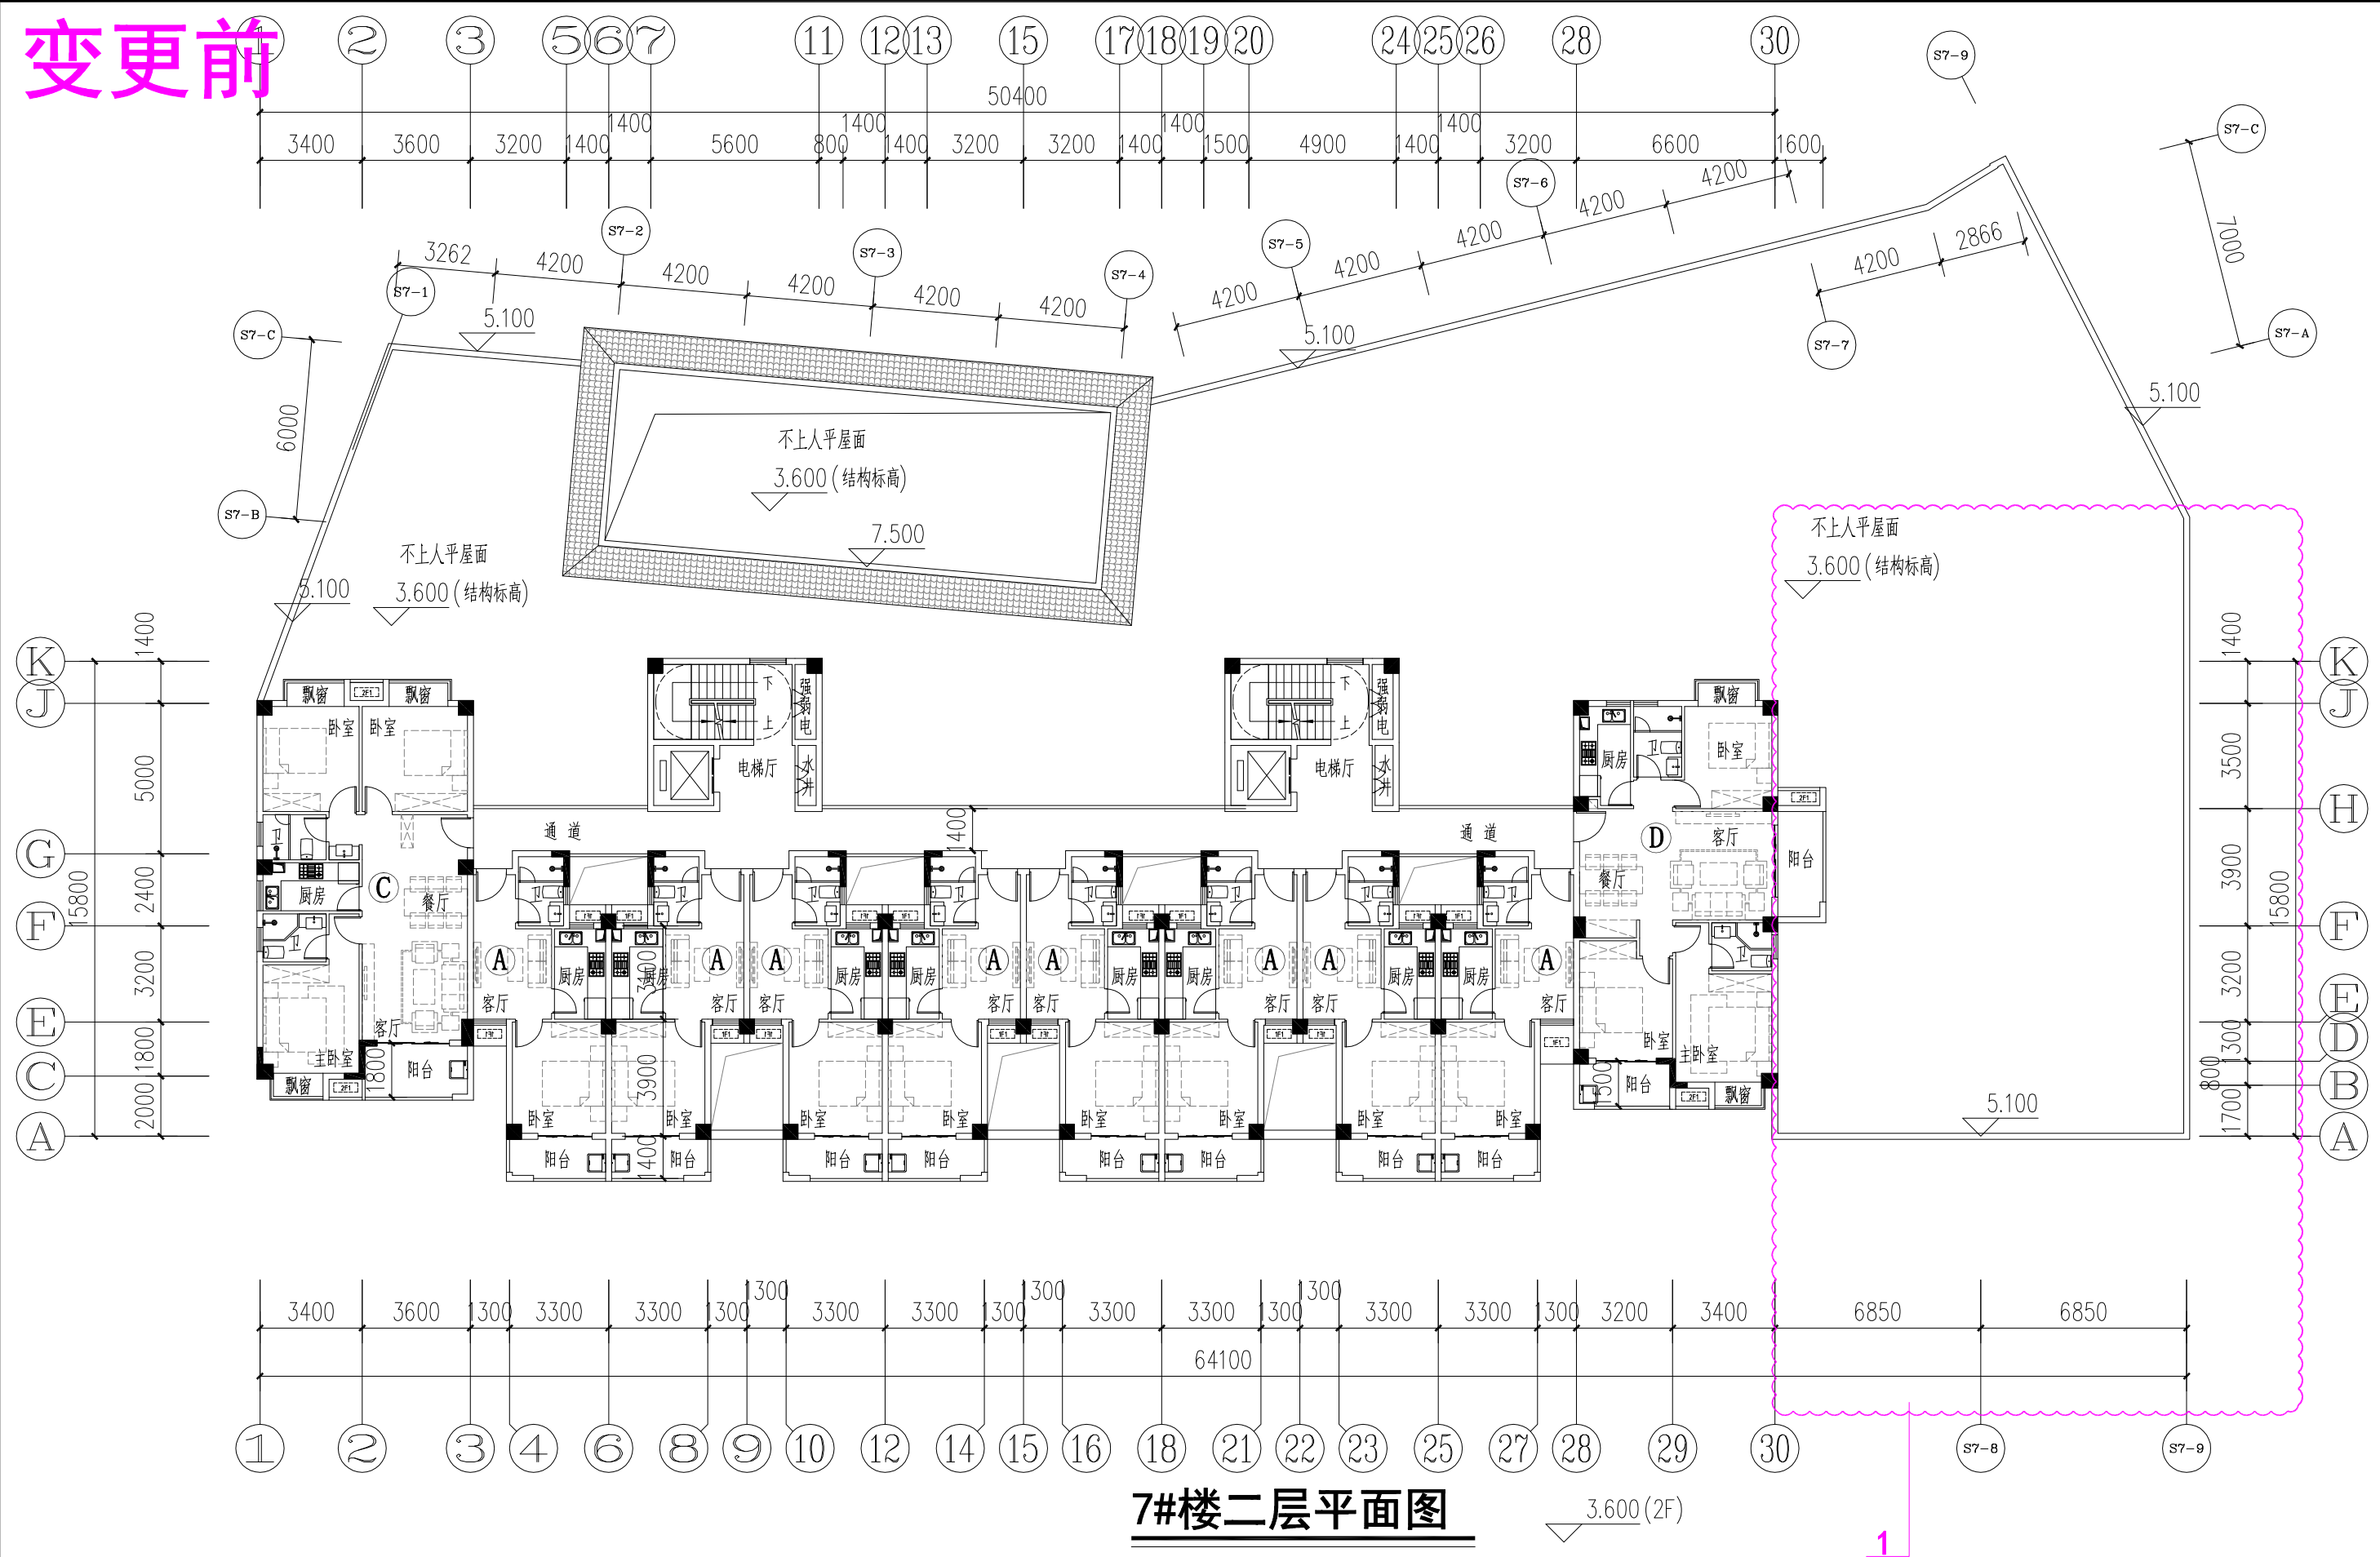

设计单位	福建一建集团有限公司	建设单位	三明市三元区城市建设投资有限责任公司	工程名称	荆东安置房及周边附属配套工程（安置房）	图 名	7#楼二层平面图	图 别	方 案
								日 期	2020. 12


1、变配电室及开闭屋顶标高调整



7#楼二层平面图


设计单位	福建一建集团有限公司	建设单位	三明市三元区城市建设投资有限责任公司	工程名称	荆东安置房及周边附属配套工程（安置房）	图 名	7#楼二层平面图	图 别	方 案
								日 期	2023. 07

变更前

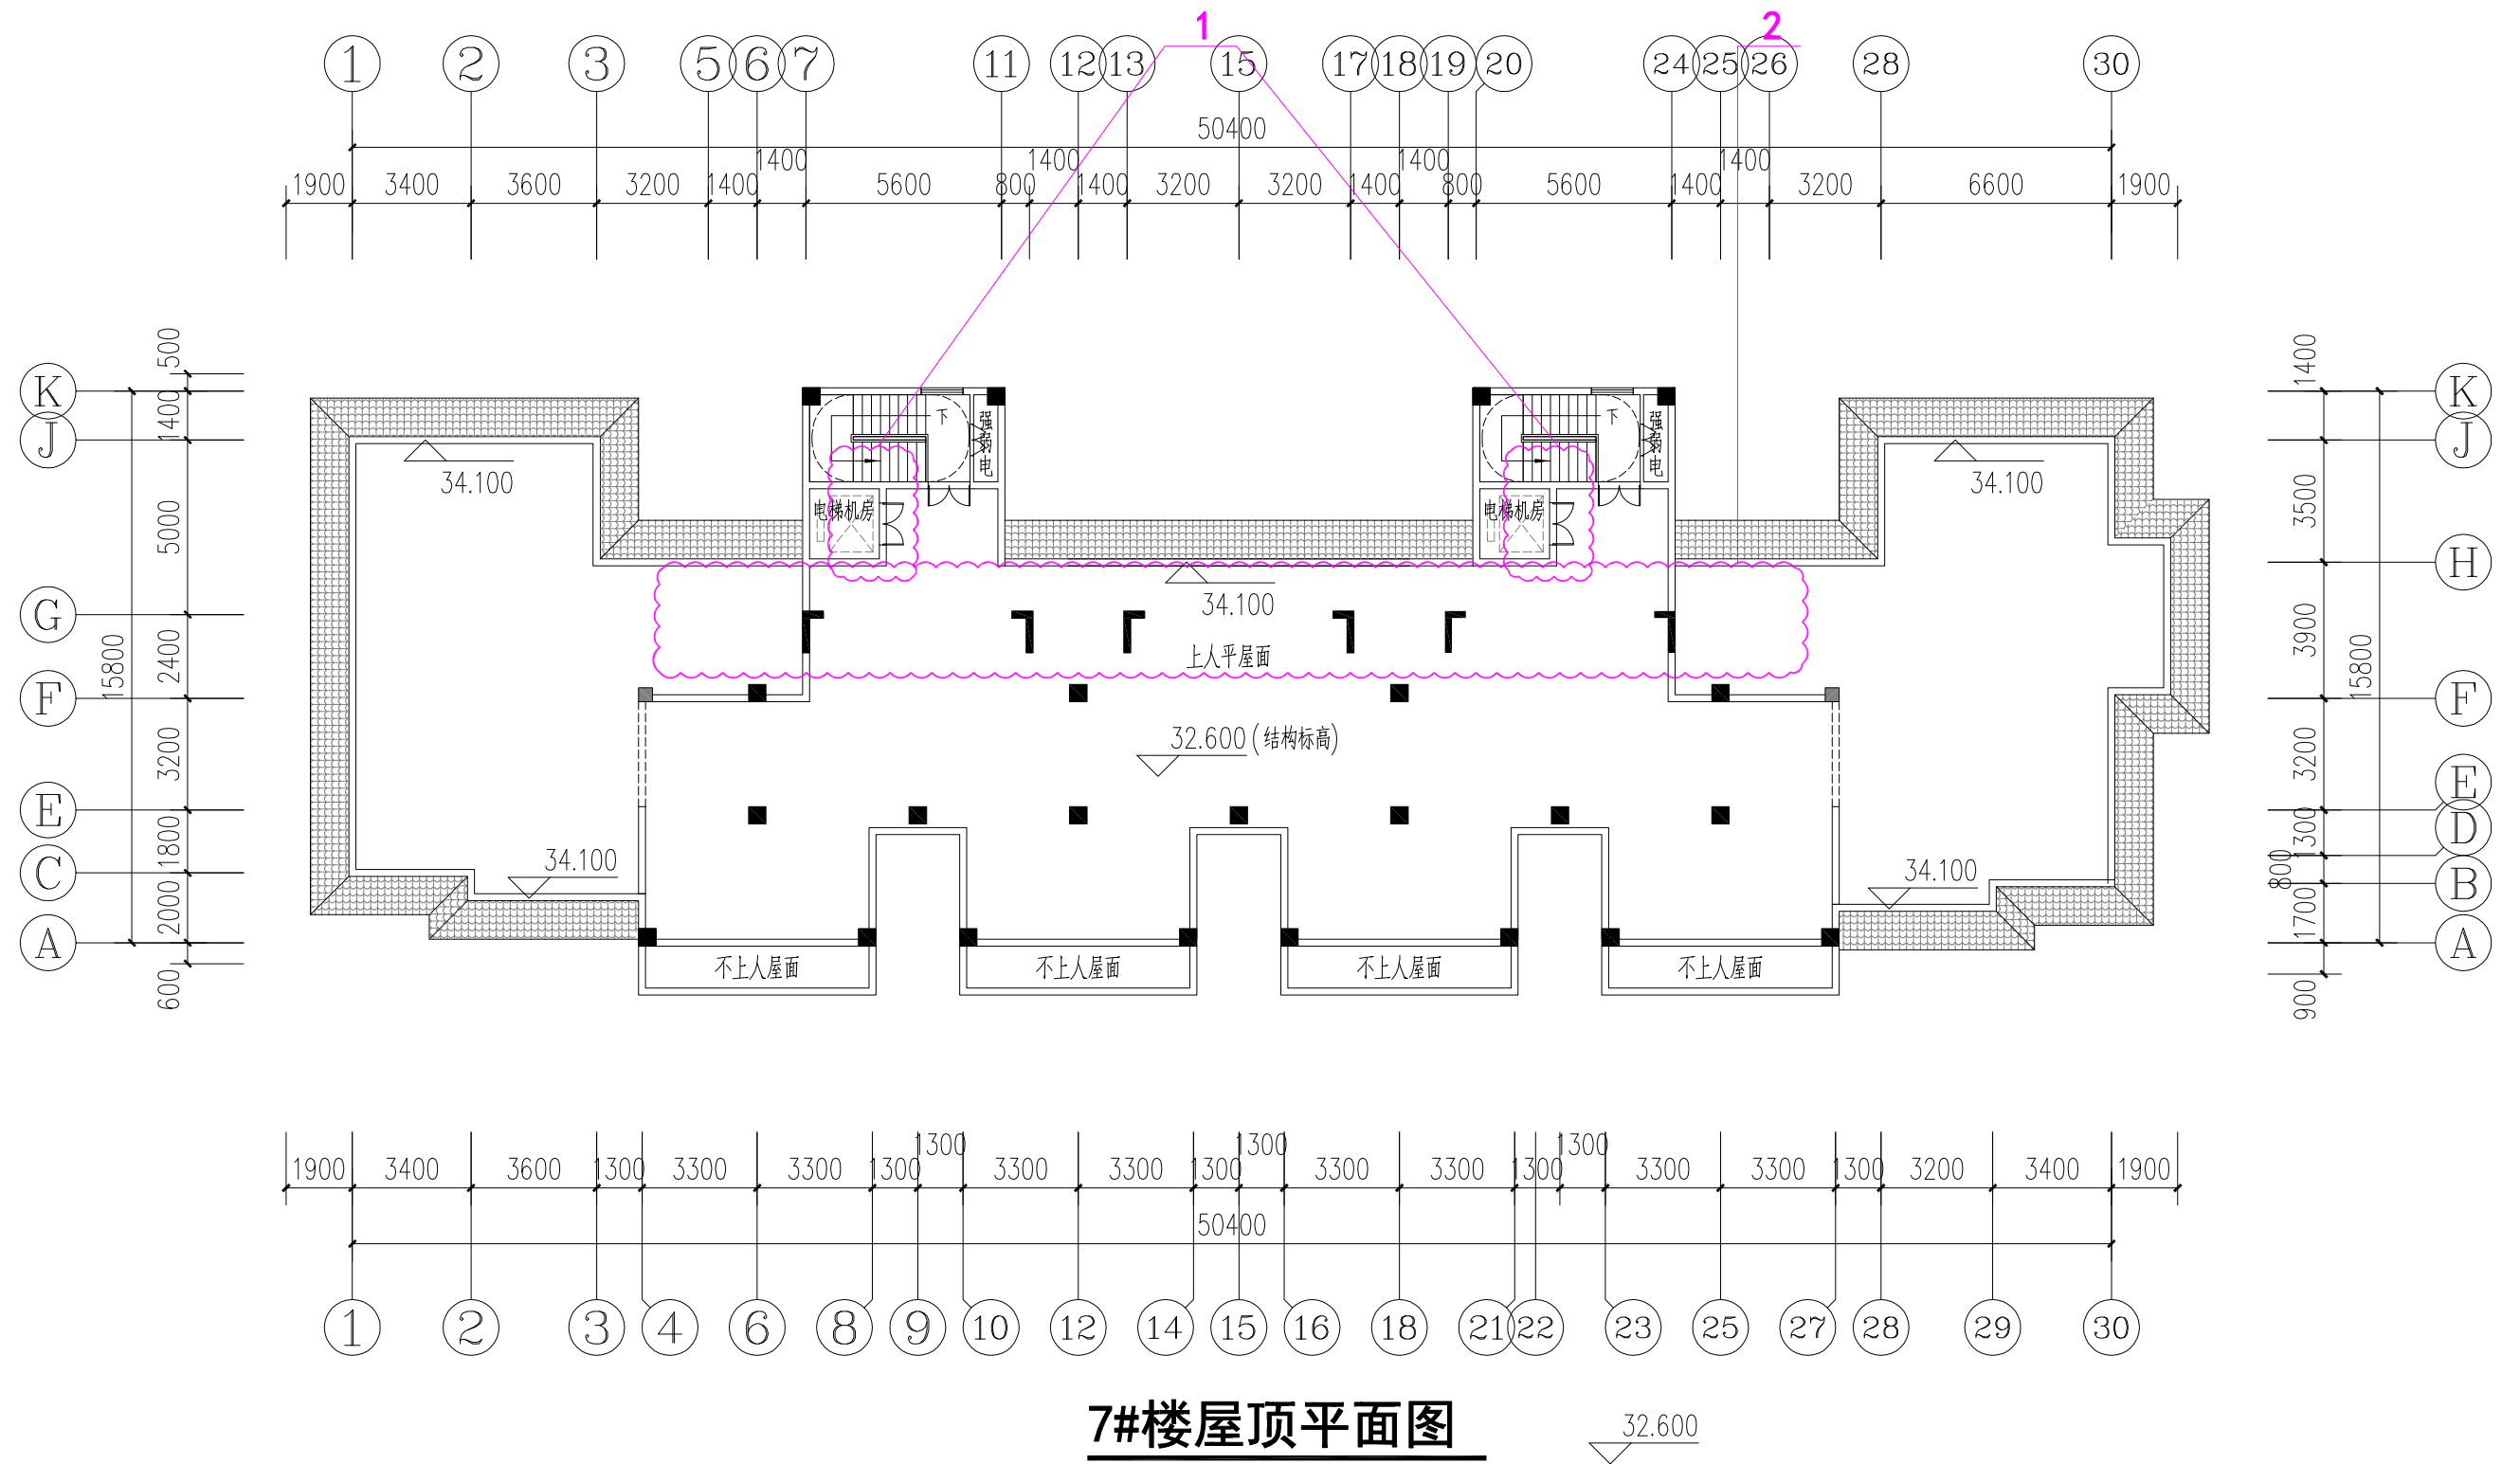[illegible]

变更后


- 1、7-J~7-L轴交7-7~7-9轴、7-J~7-L轴交7-21~7-23轴电梯机房调整
2、7-G~7-J轴交7-4~7-26轴增设天井上空

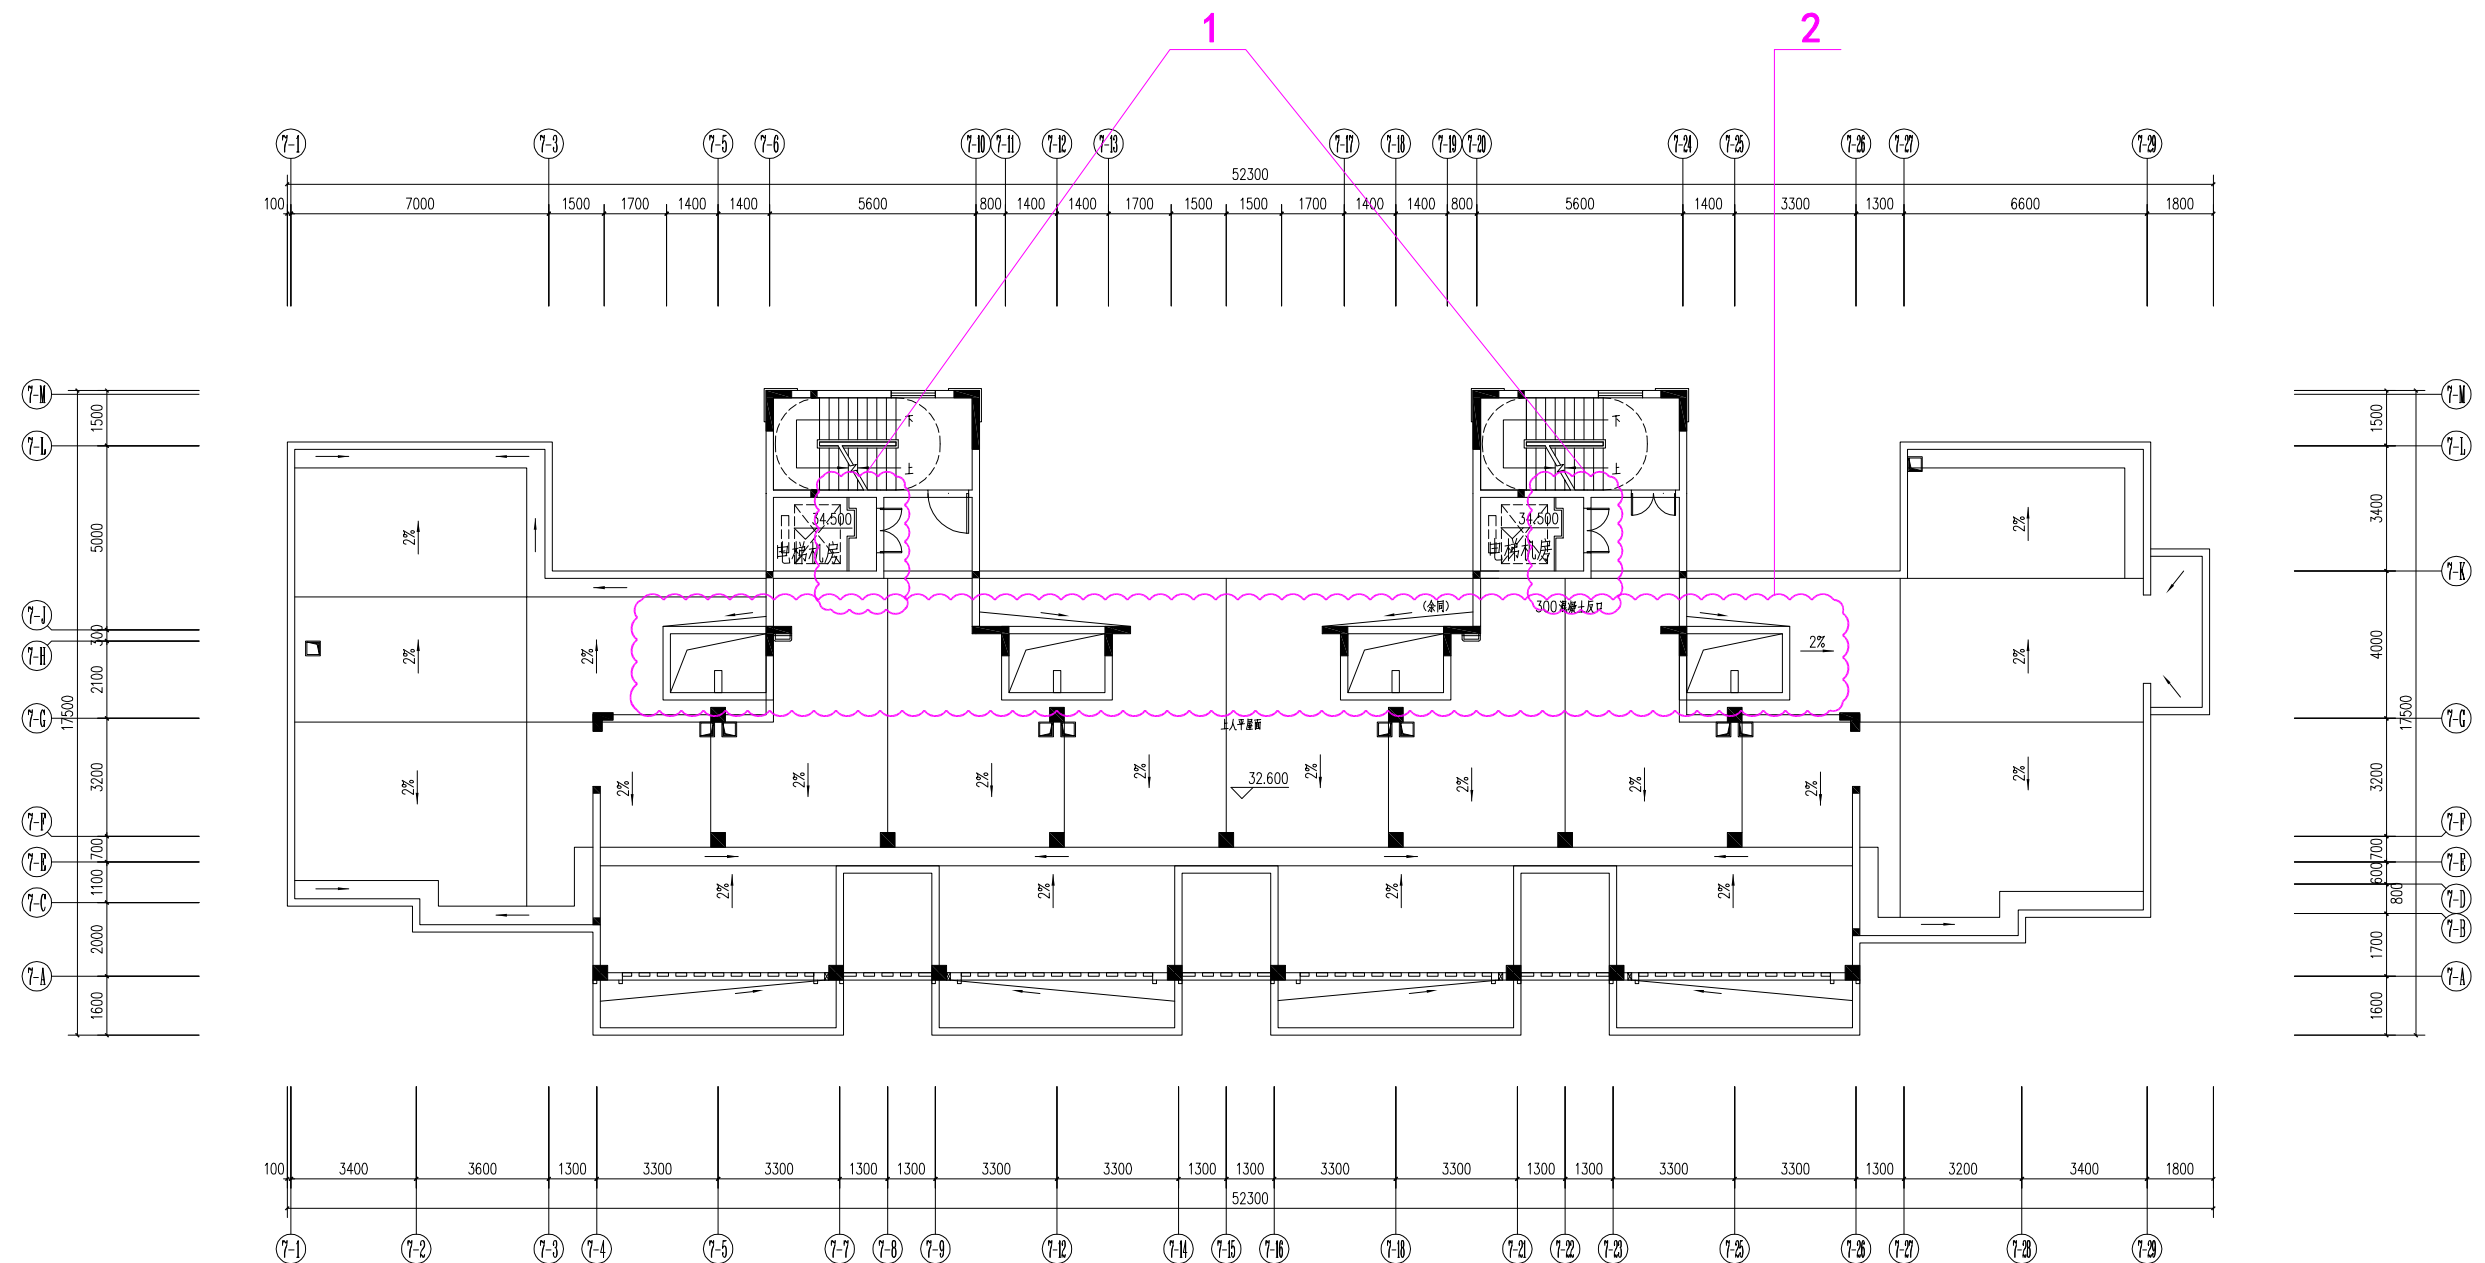

7#楼屋顶平面图

设计单位	福建一建集团有限公司	建设单位	三明市三元区城市建设投资有限责任公司	工程名称	荆东安置房及周边附属配套工程（安置房）	图 名	7#楼屋顶平面图	图 别	方 案
								日 期	2023. 07

变更前

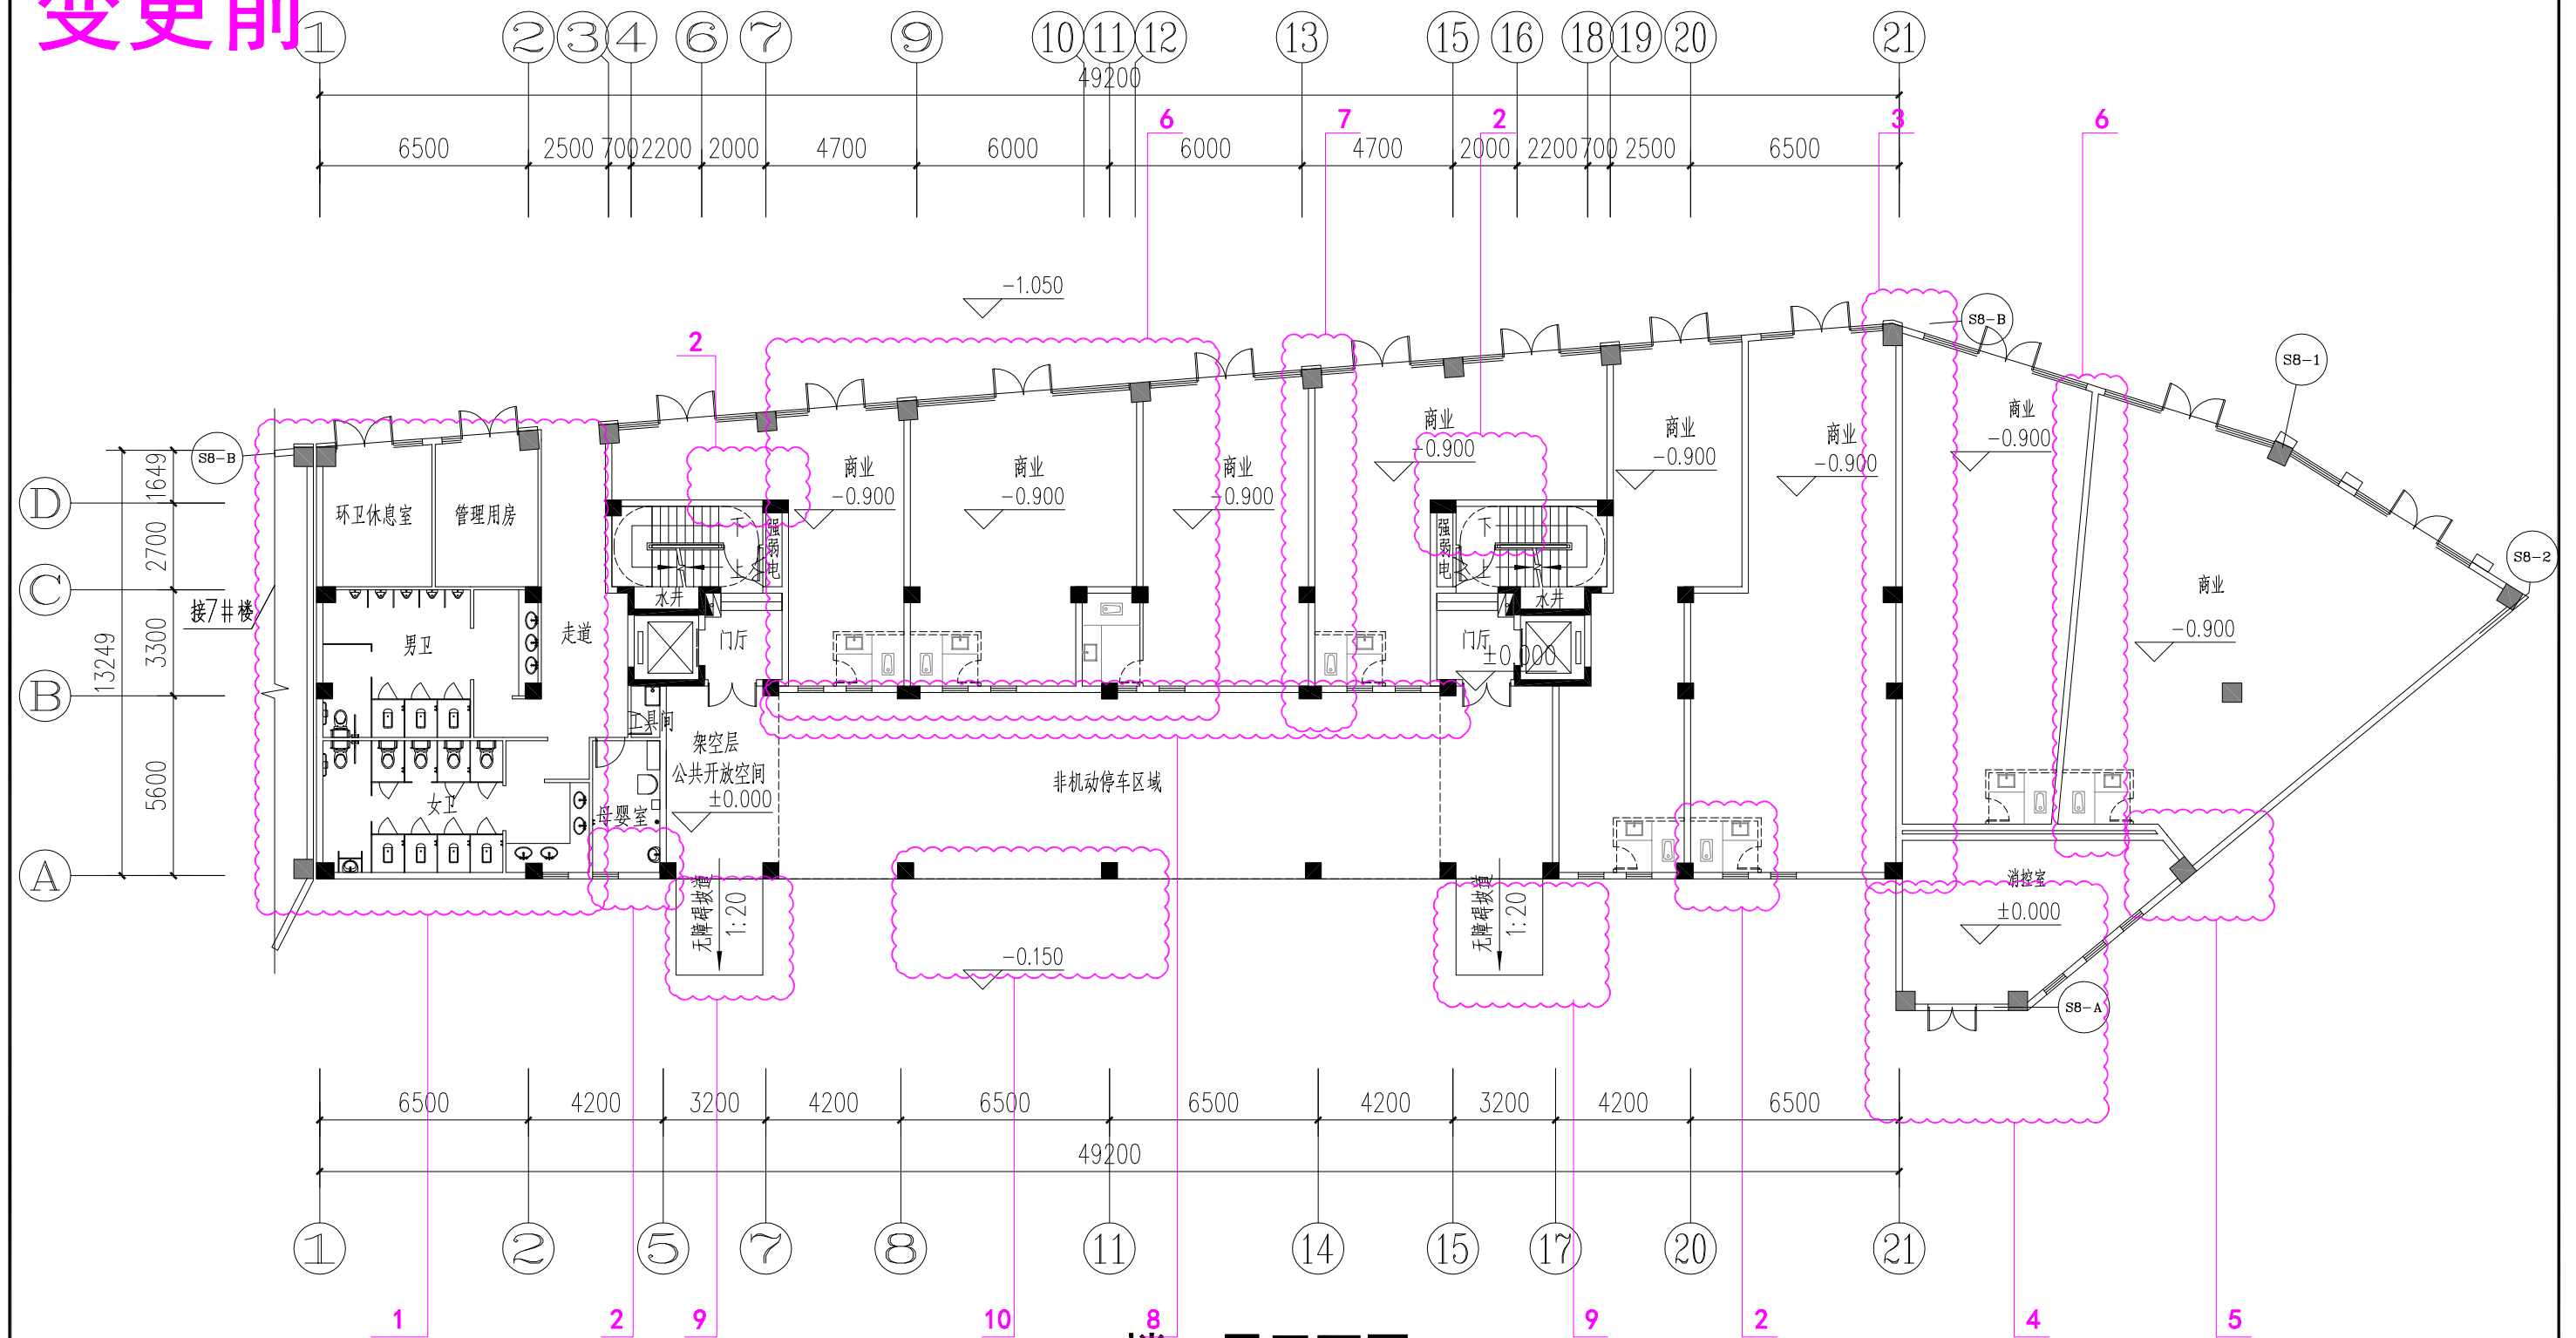


8#楼一层平面图

设计单位	福建一建集团有限公司	建设单位	三明市三元区城市建设投资有限责任公司	工程名称	荆东安置房及周边附属配套工程（安置房）	图 名	8#楼一层平面图	图 别	方 案
								日 期	2020. 12

变更后

- 1、8-A~S8-J轴交8-1~8-2轴环卫室、管理用房、公厕布局调整
- 2、8-A~8-B轴交8-2~8-5轴、8-F~S8-J轴交8-6~8-8轴增设风井、排风井
8-F~S8-J轴交8-16~8-18轴、8-A~8-B轴交8-19~8-22轴增设风井、排风井
- 3、8-A~S8-J轴交8-23~S8-1轴、8-F~S8-J轴交8-6~8-8轴增设伸缩缝
- 4、8-A轴交8-23~S8-3轴消控室墙体外移2M
- 5、8-A~8-B轴交S8-3~S8-4轴消控室和商业隔墙调整


- 6、8-B~S8-J轴交8-7~8-13轴、8-A~S8-J轴交S8-2轴商业布局调整
- 7、8-B~S8-J轴交8-14轴剪力墙、柱网位置调整
- 8、8-B~8-C轴交8-7~8-16轴商业墙体外移0.2米
- 9、8-A轴交8-5~8-7、8-17~8-19轴无障碍坡道调整
- 10、8-A轴交8-9~8-12轴防护栏杆取消

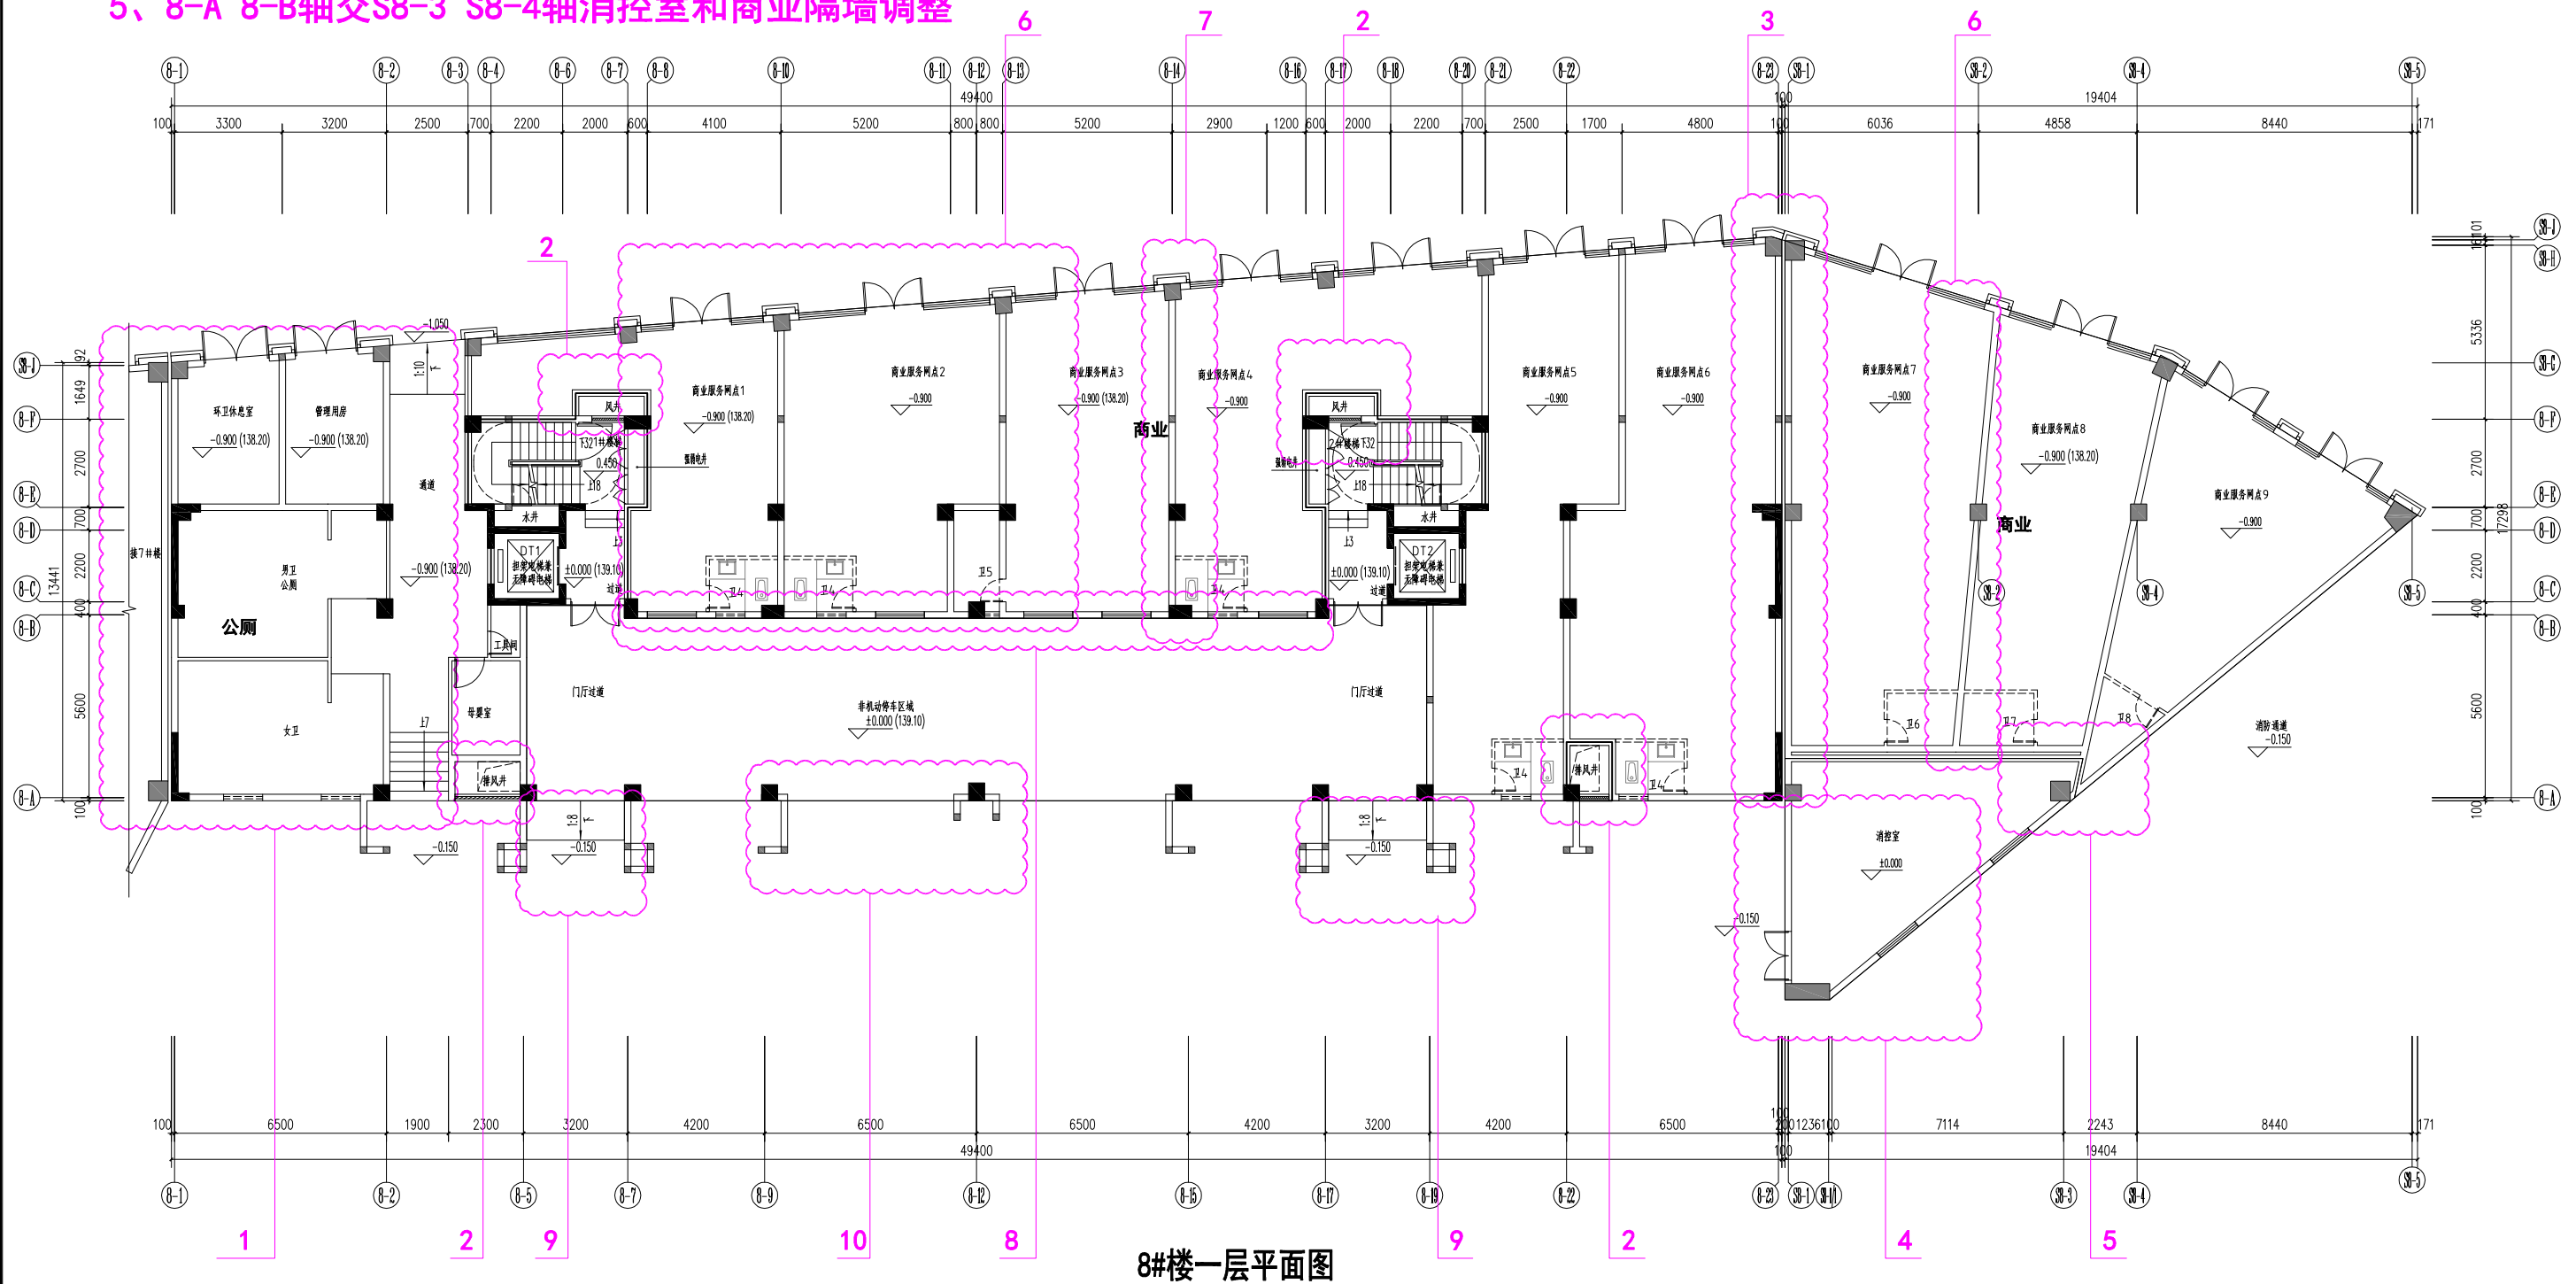

8#楼一层平面图

设计单位	福建一建集团有限公司	建设单位	三明市三元区城市建设投资有限责任公司	工程名称	荆东安置房及周边附属配套工程（安置房）	图 名	8#楼一层平面图	图 别	方 案
								日 期	2023. 07

变更前

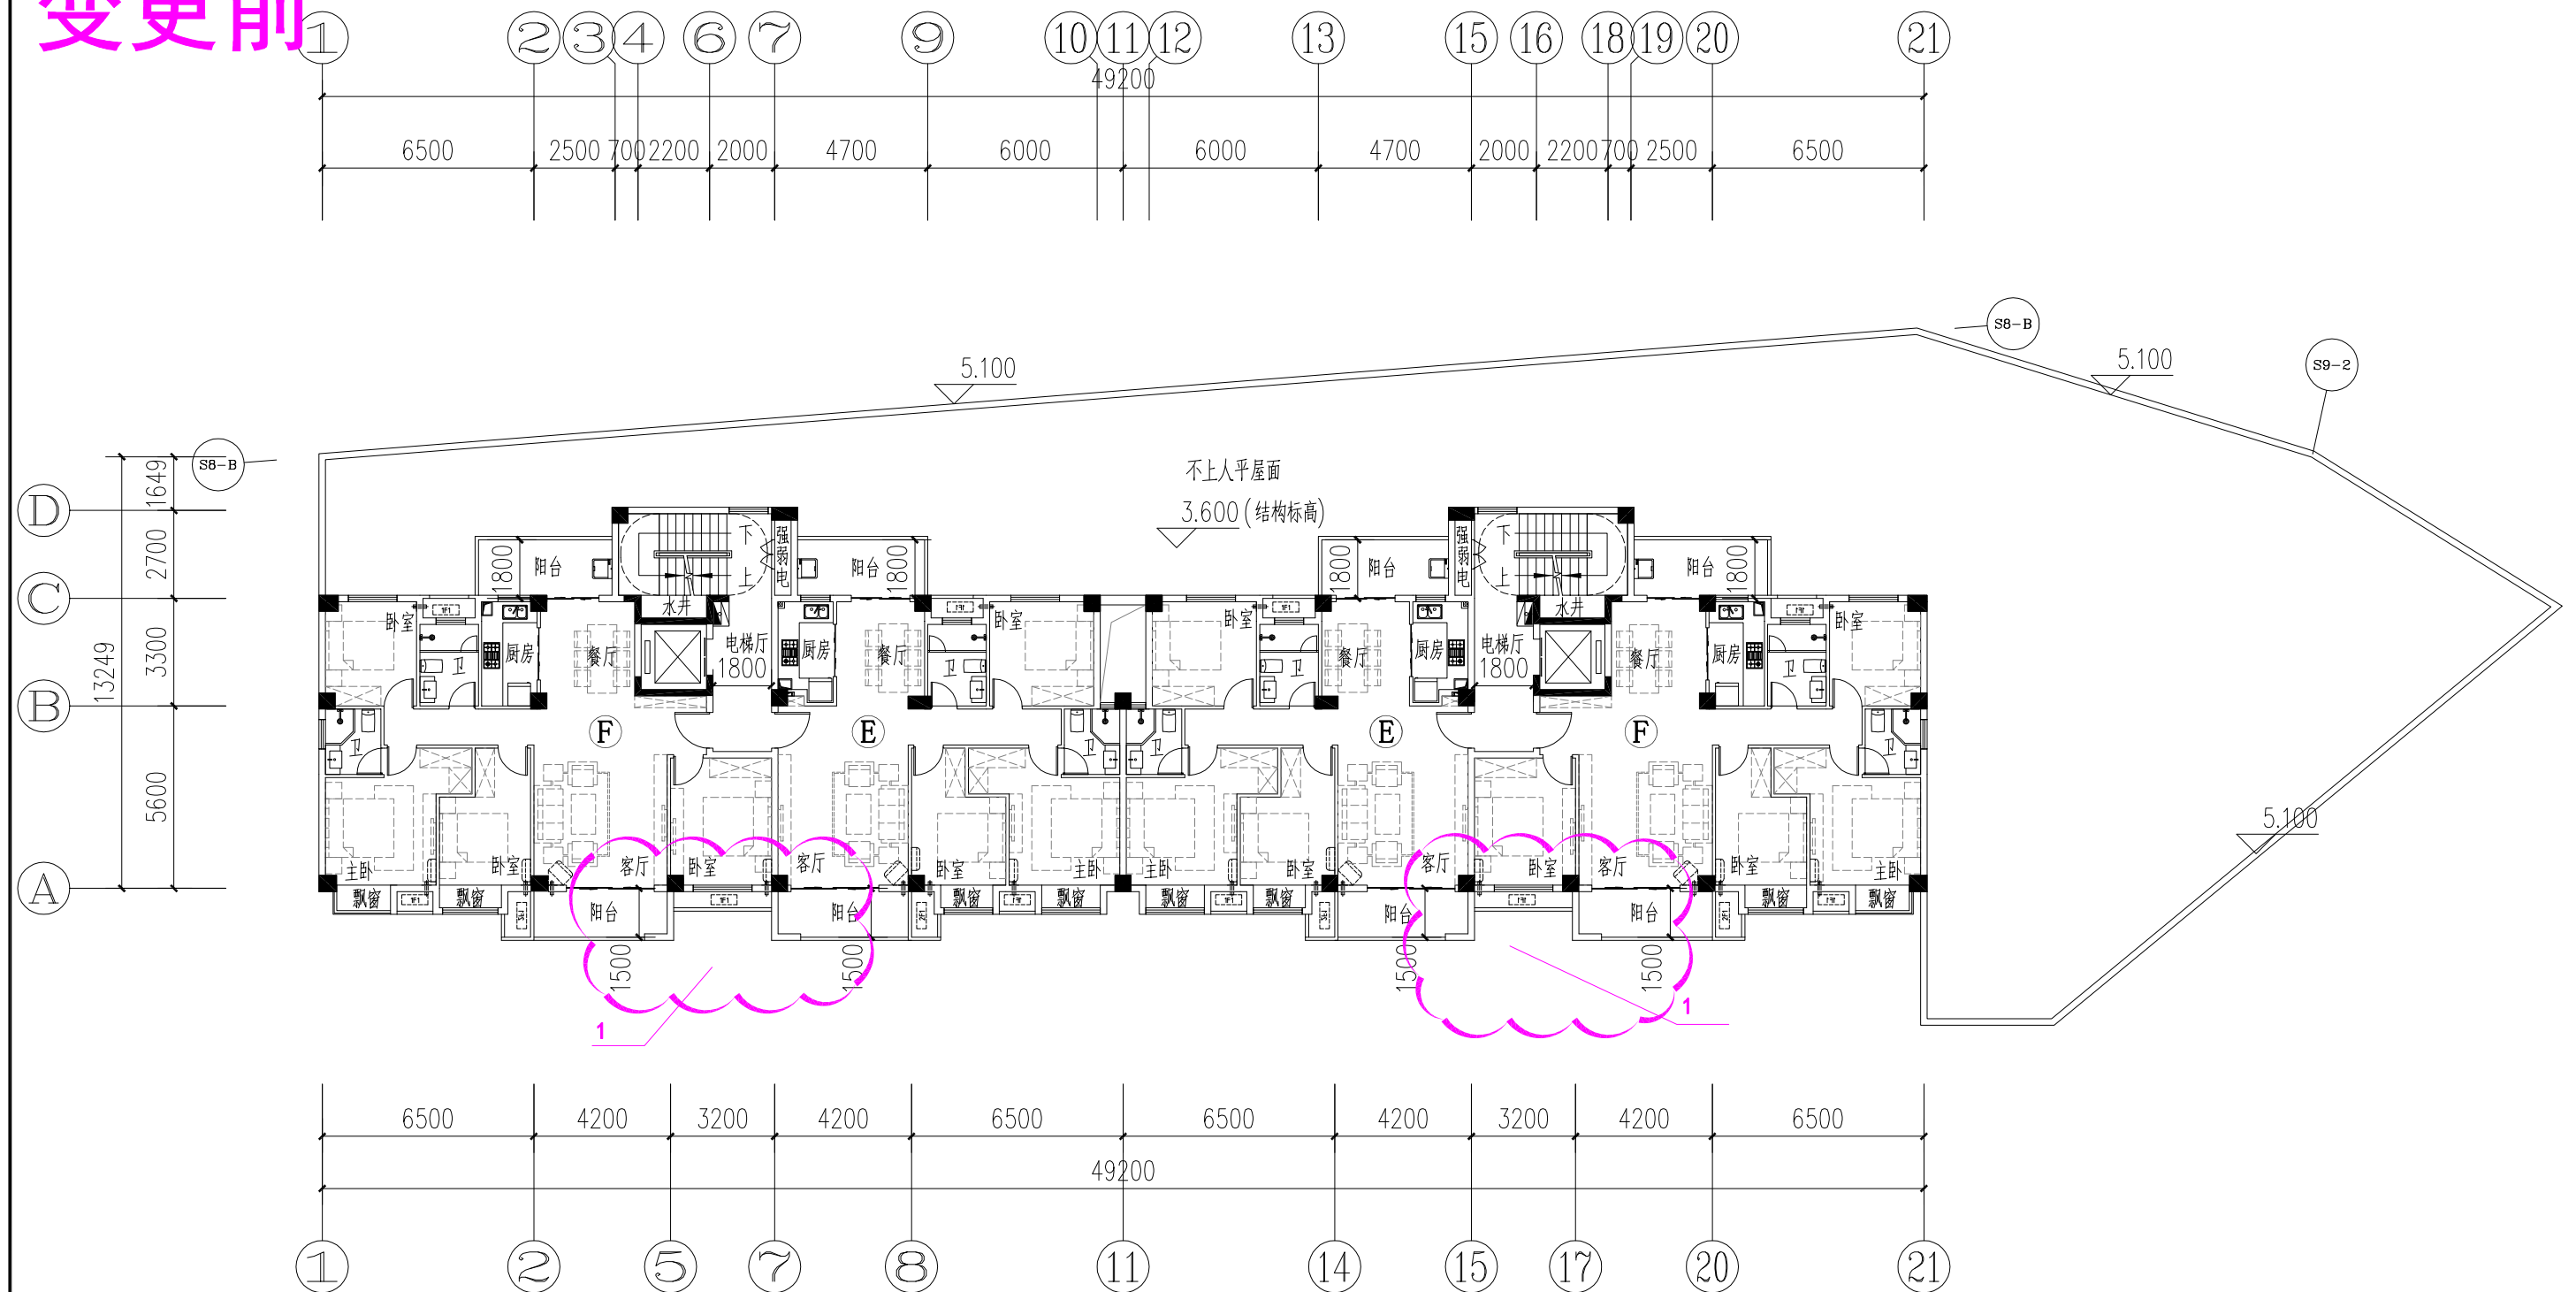



8#楼二层平面图

$$\underline{3.600(2F)}$$

设计单位	福建一建集团有限公司	建设单位	三明市三元区城市建设投资有限责任公司	工程名称	荆东安置房及周边附属配套工程（安置房）	图 名	8#楼二层平面图	图 别	方 案
								日 期	2020. 12

变更后


1. 增设雨披

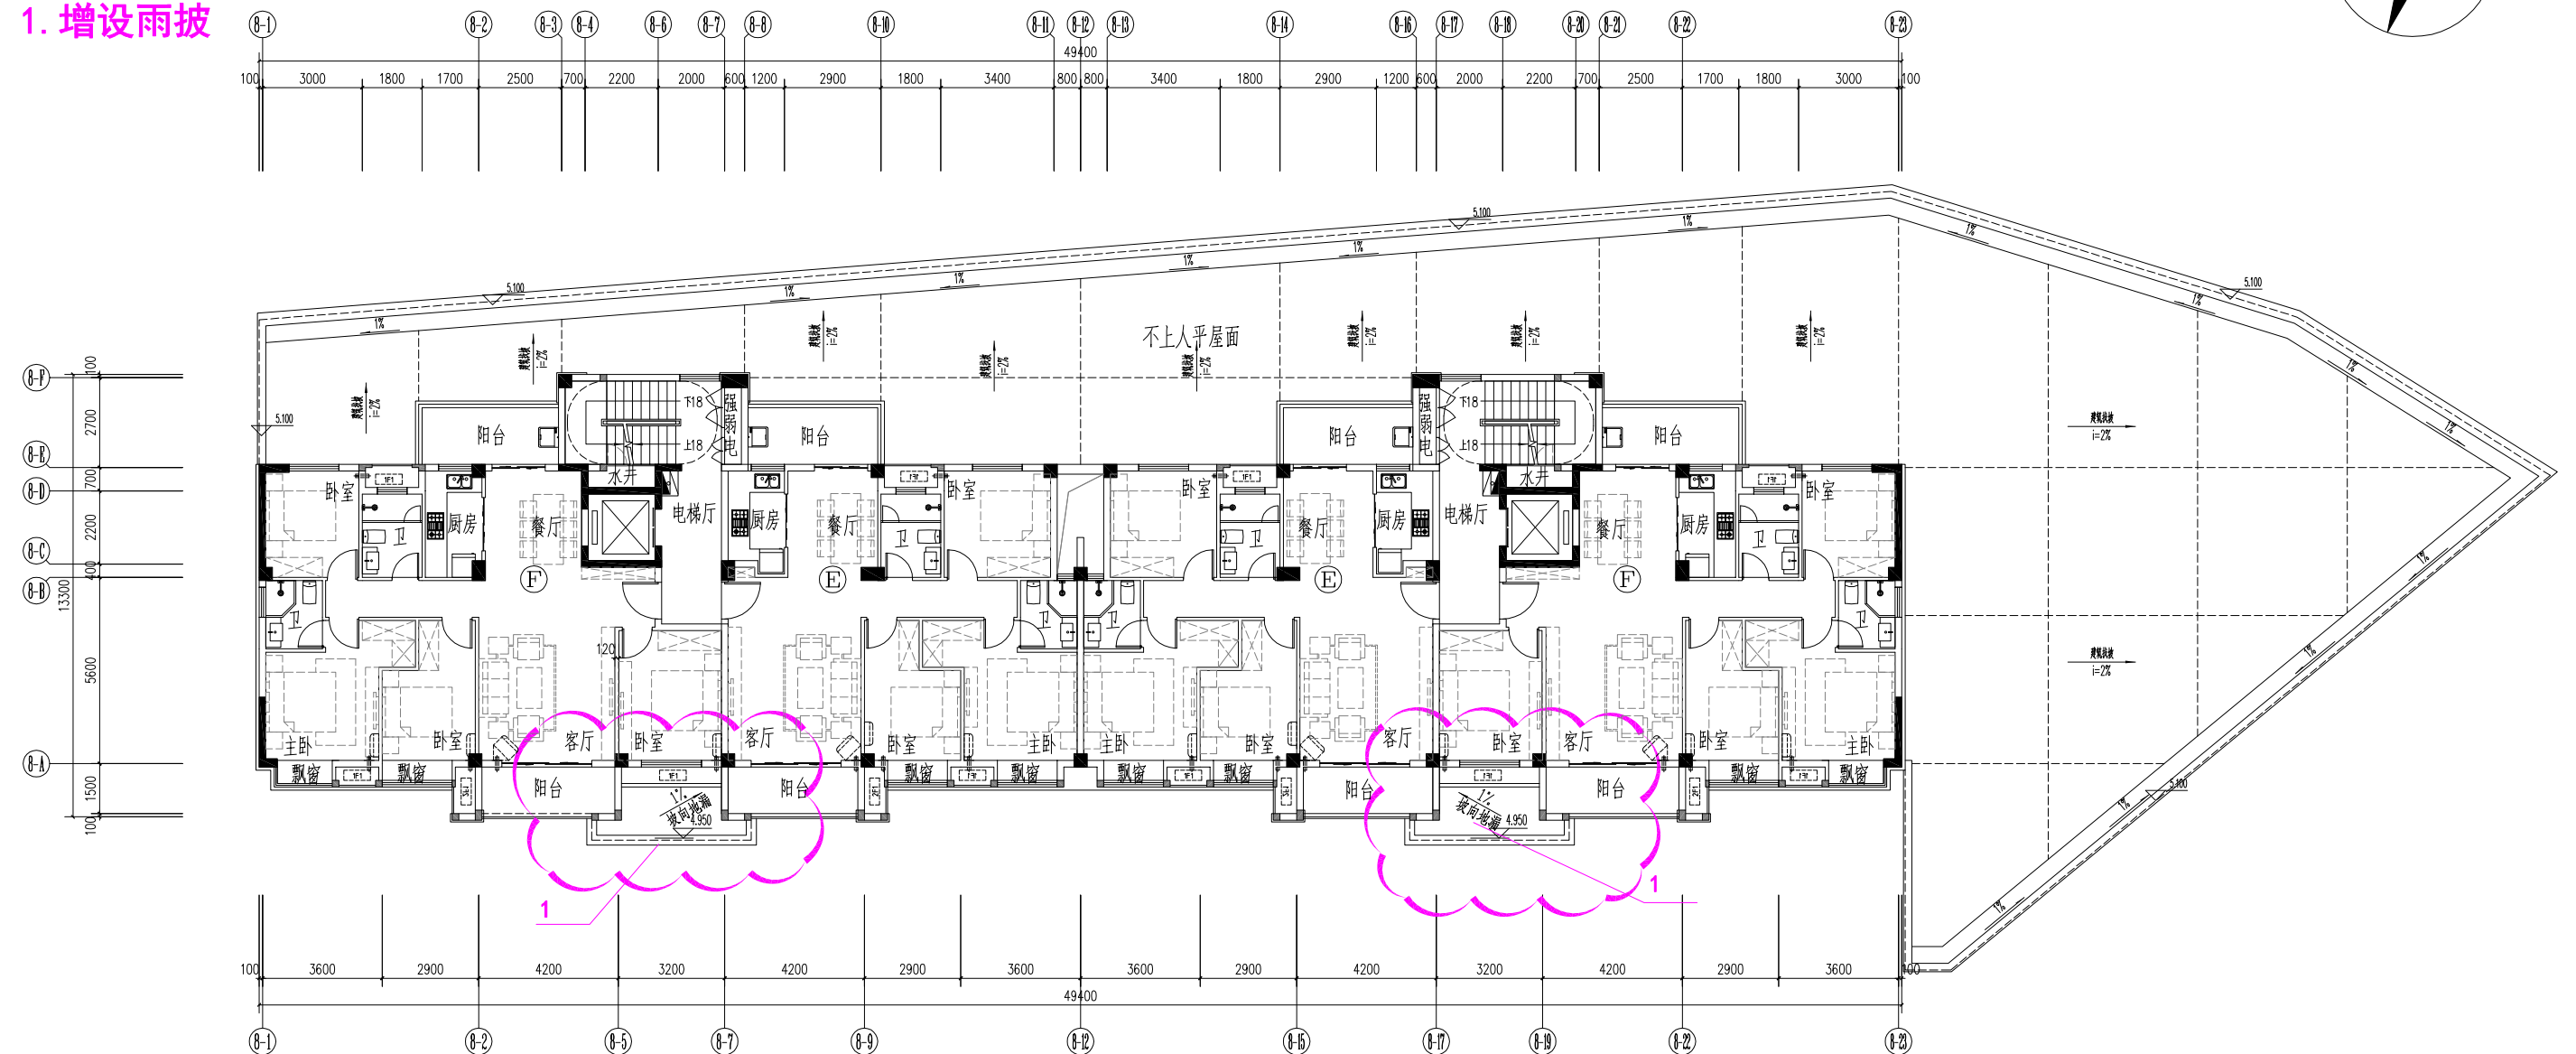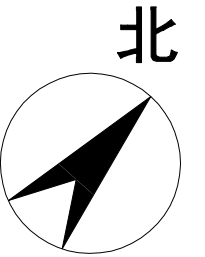

8#楼二层平面图

设计单位	福建一建集团有限公司	建设单位	三明市三元区城市建设投资有限责任公司	工程名称	荆东安置房及周边附属配套工程（安置房）	图 名	8#楼二层平面图	图 别	方 案
								日 期	2023. 07

变更前

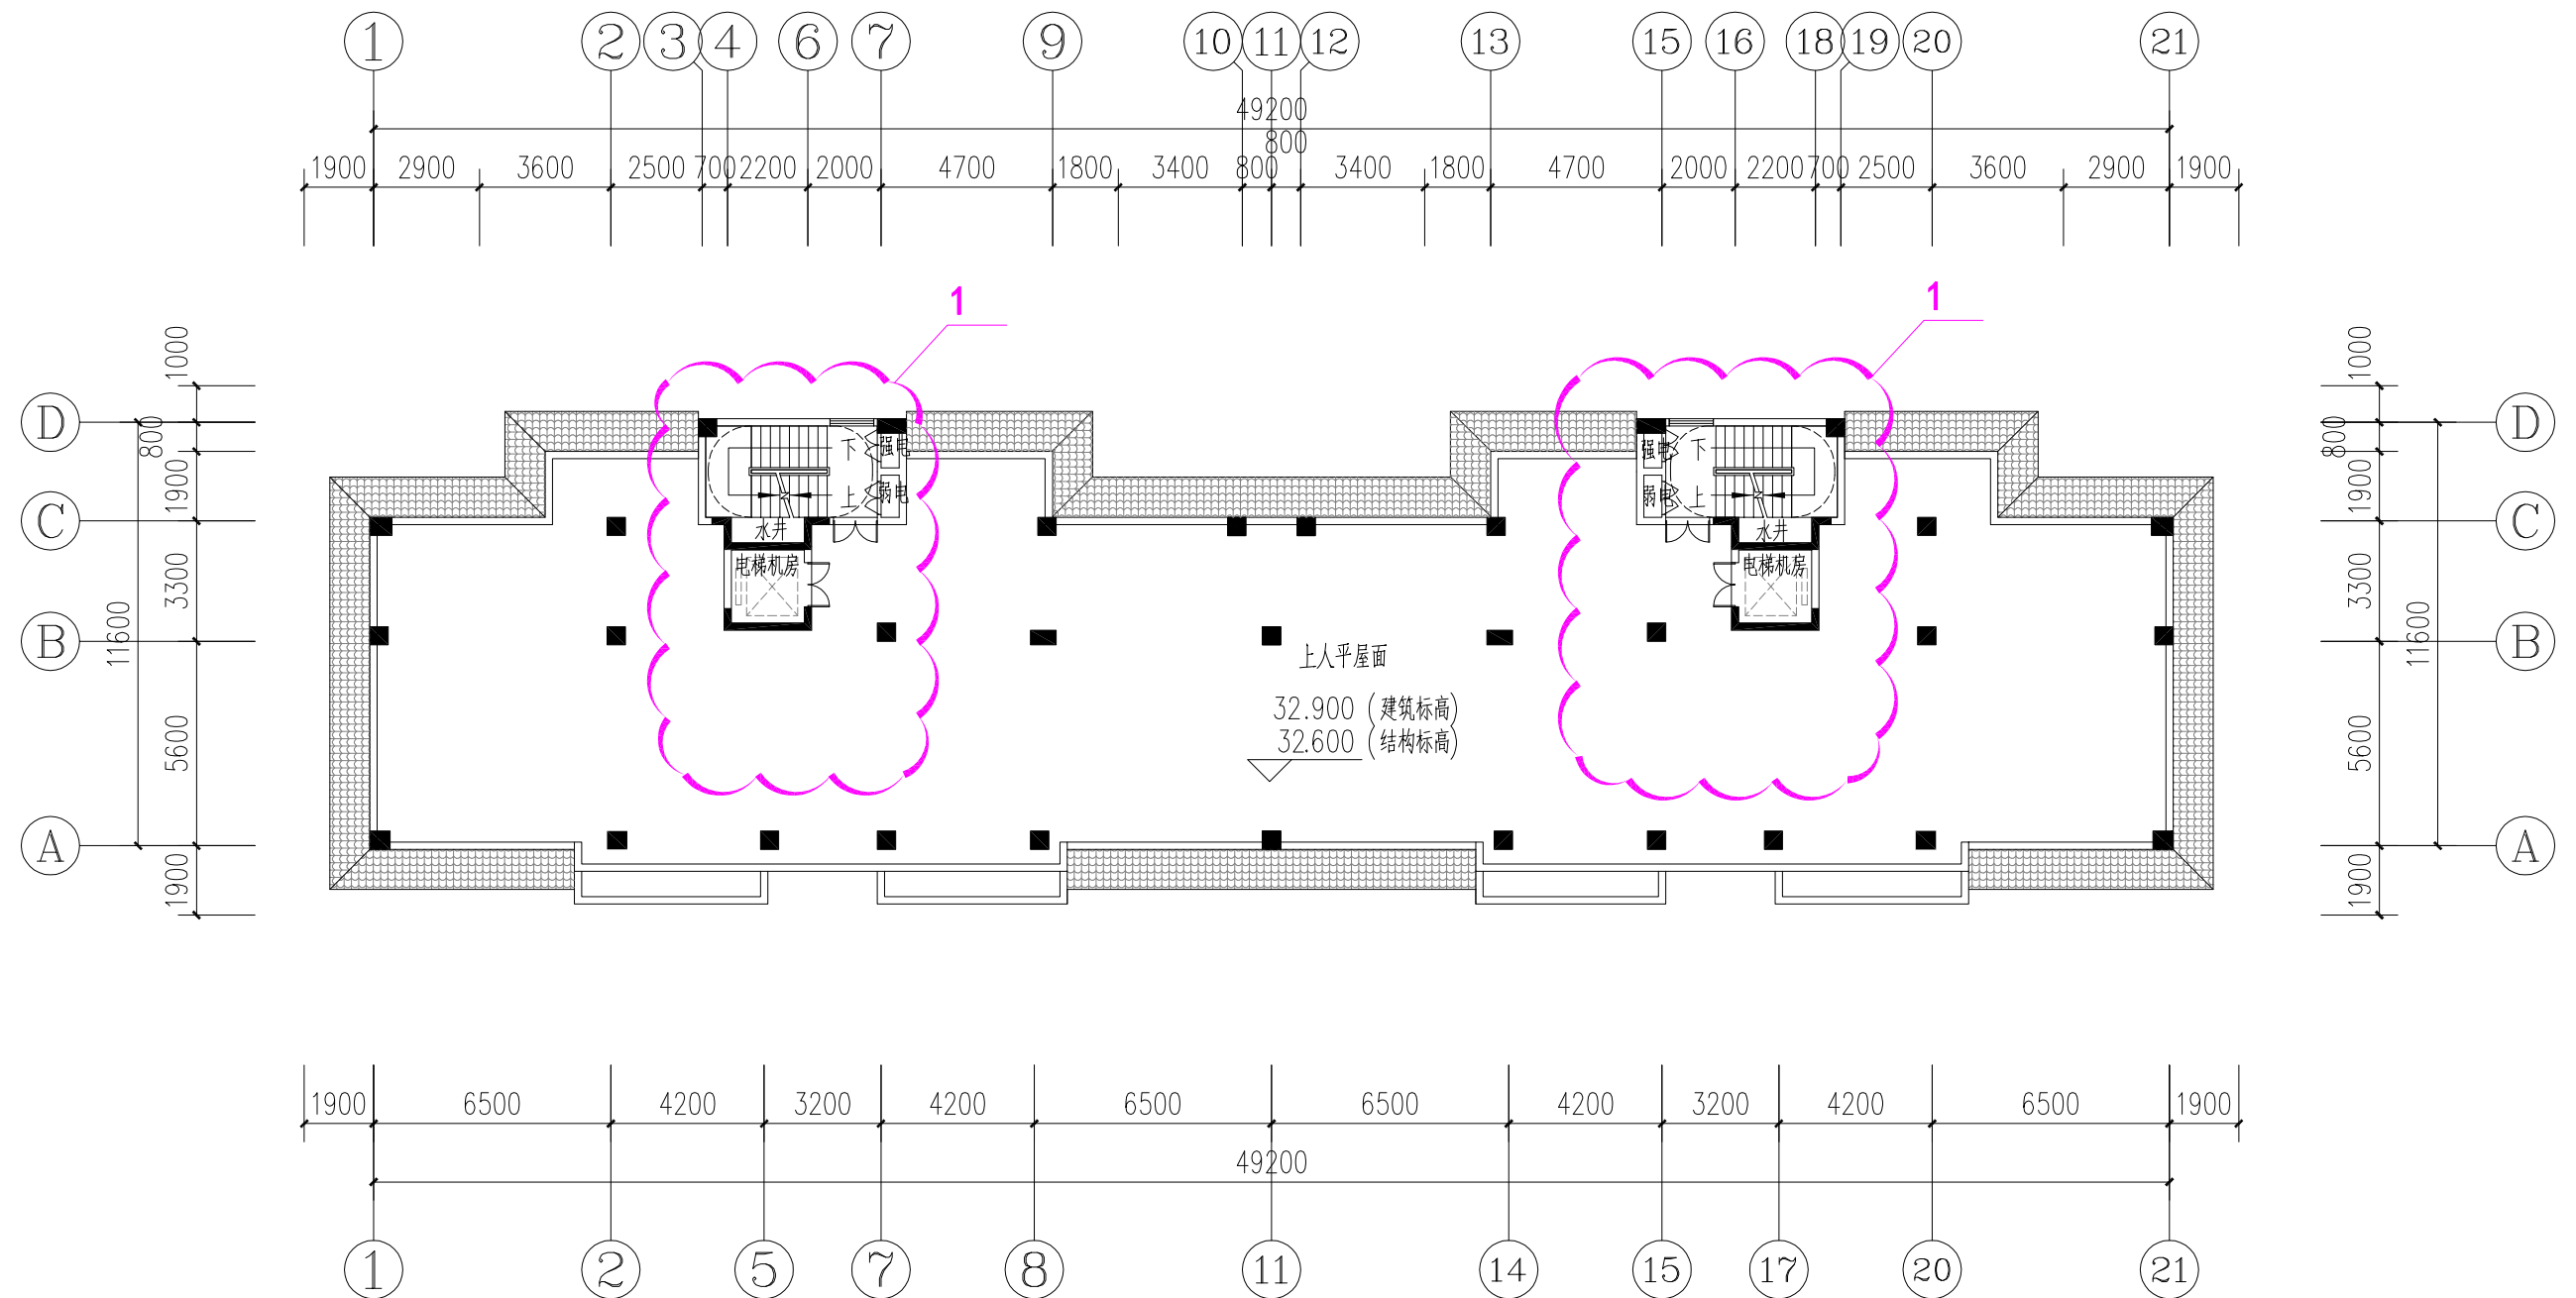


8#楼屋顶平面图

设计单位	福建一建集团有限公司	建设单位	三明市三元区城市建设投资有限责任公司	工程名称	荆东安置房及周边附属配套工程（安置房）	图 名	8#楼屋顶平面图	图 别	方 案
								日 期	2020. 12

变更后


1. 电梯机房范围调整

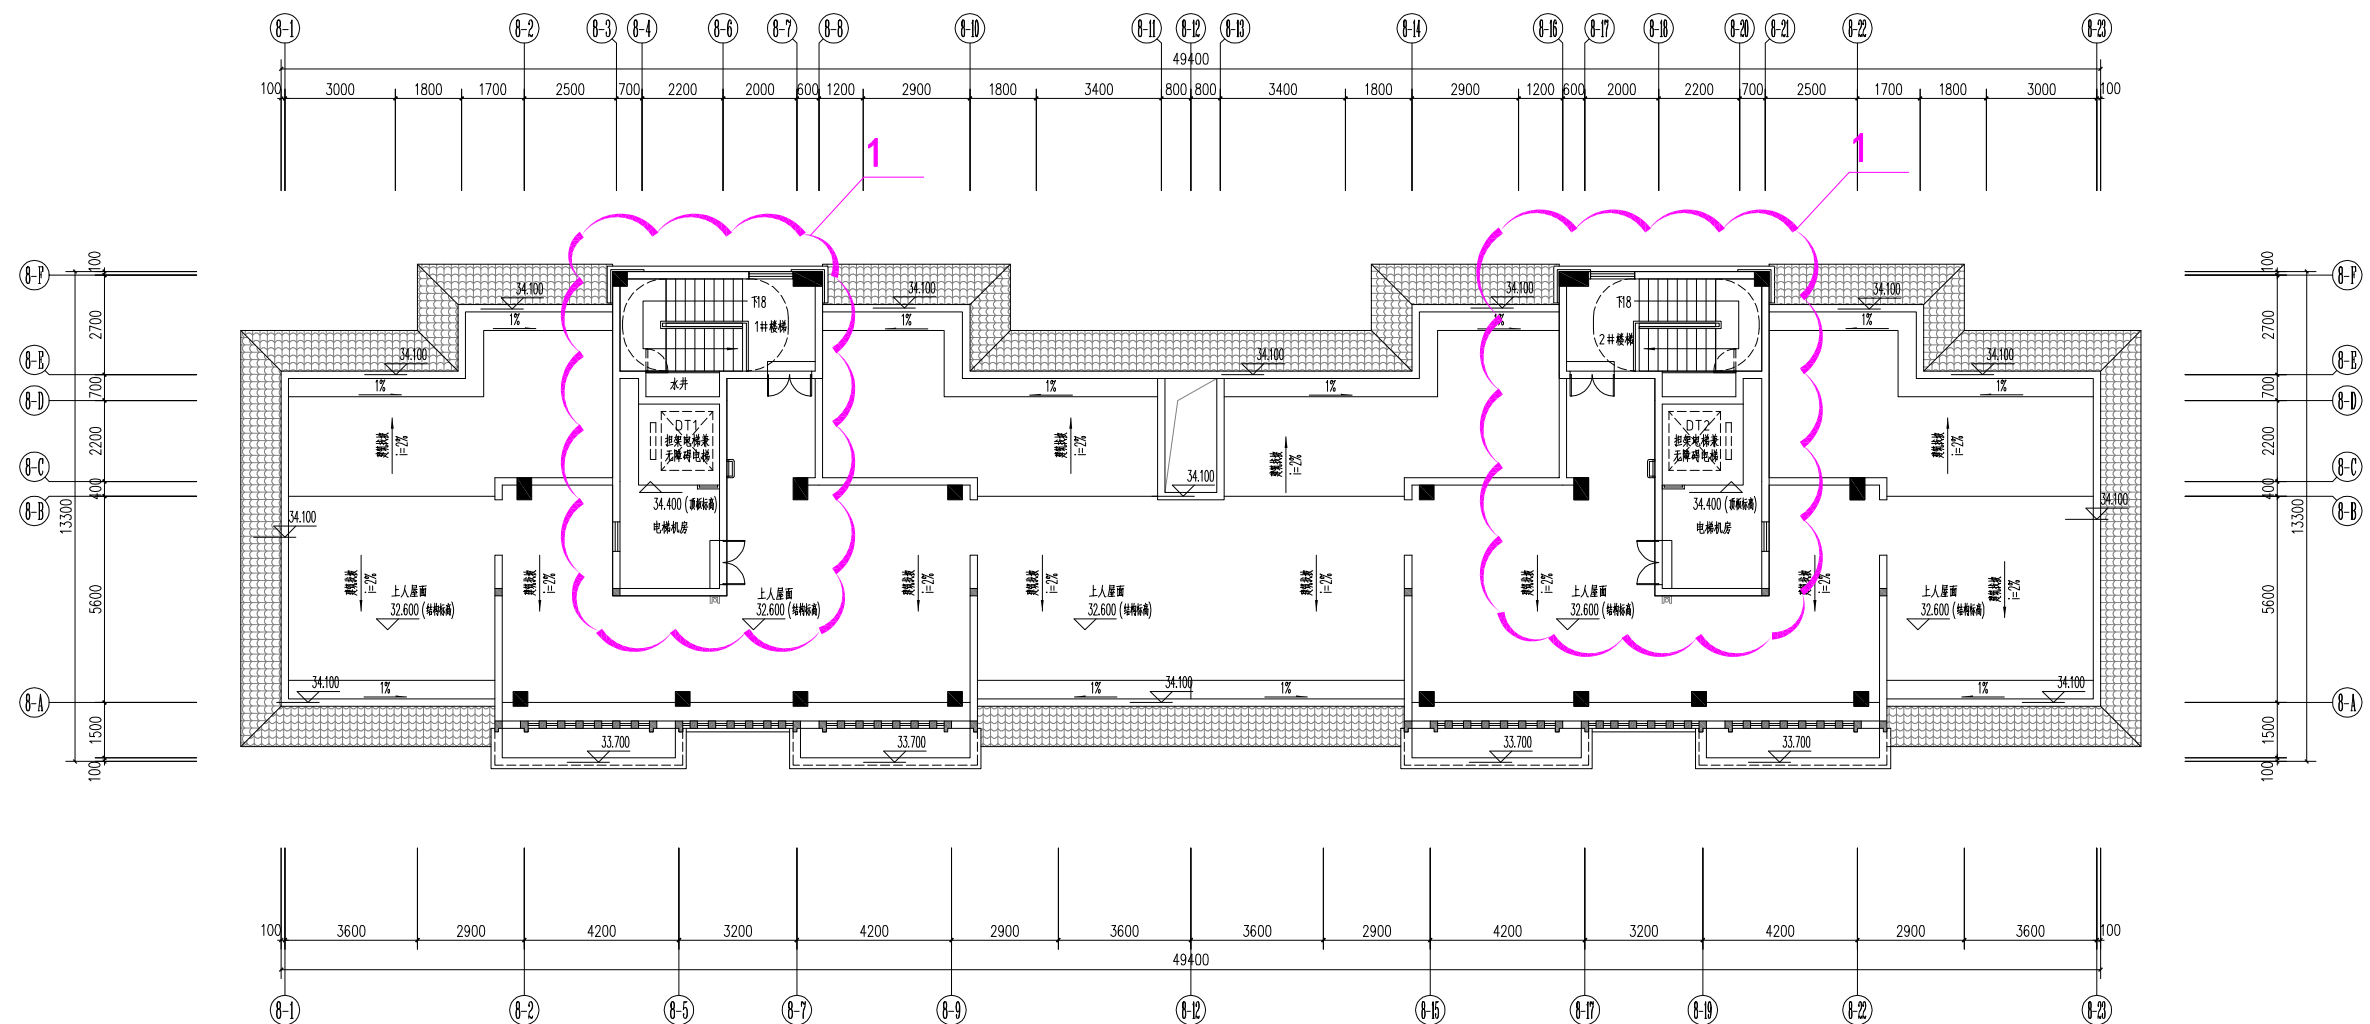


8#楼屋面层平面图

设计单位	福建一建集团有限公司	建设单位	三明市三元区城市建设投资有限责任公司	工程名称	荆东安置房及周边附属配套工程（安置房）	图 名	8#楼屋面层平面图	图 别	方 案
								日 期	2023. 07

变更前

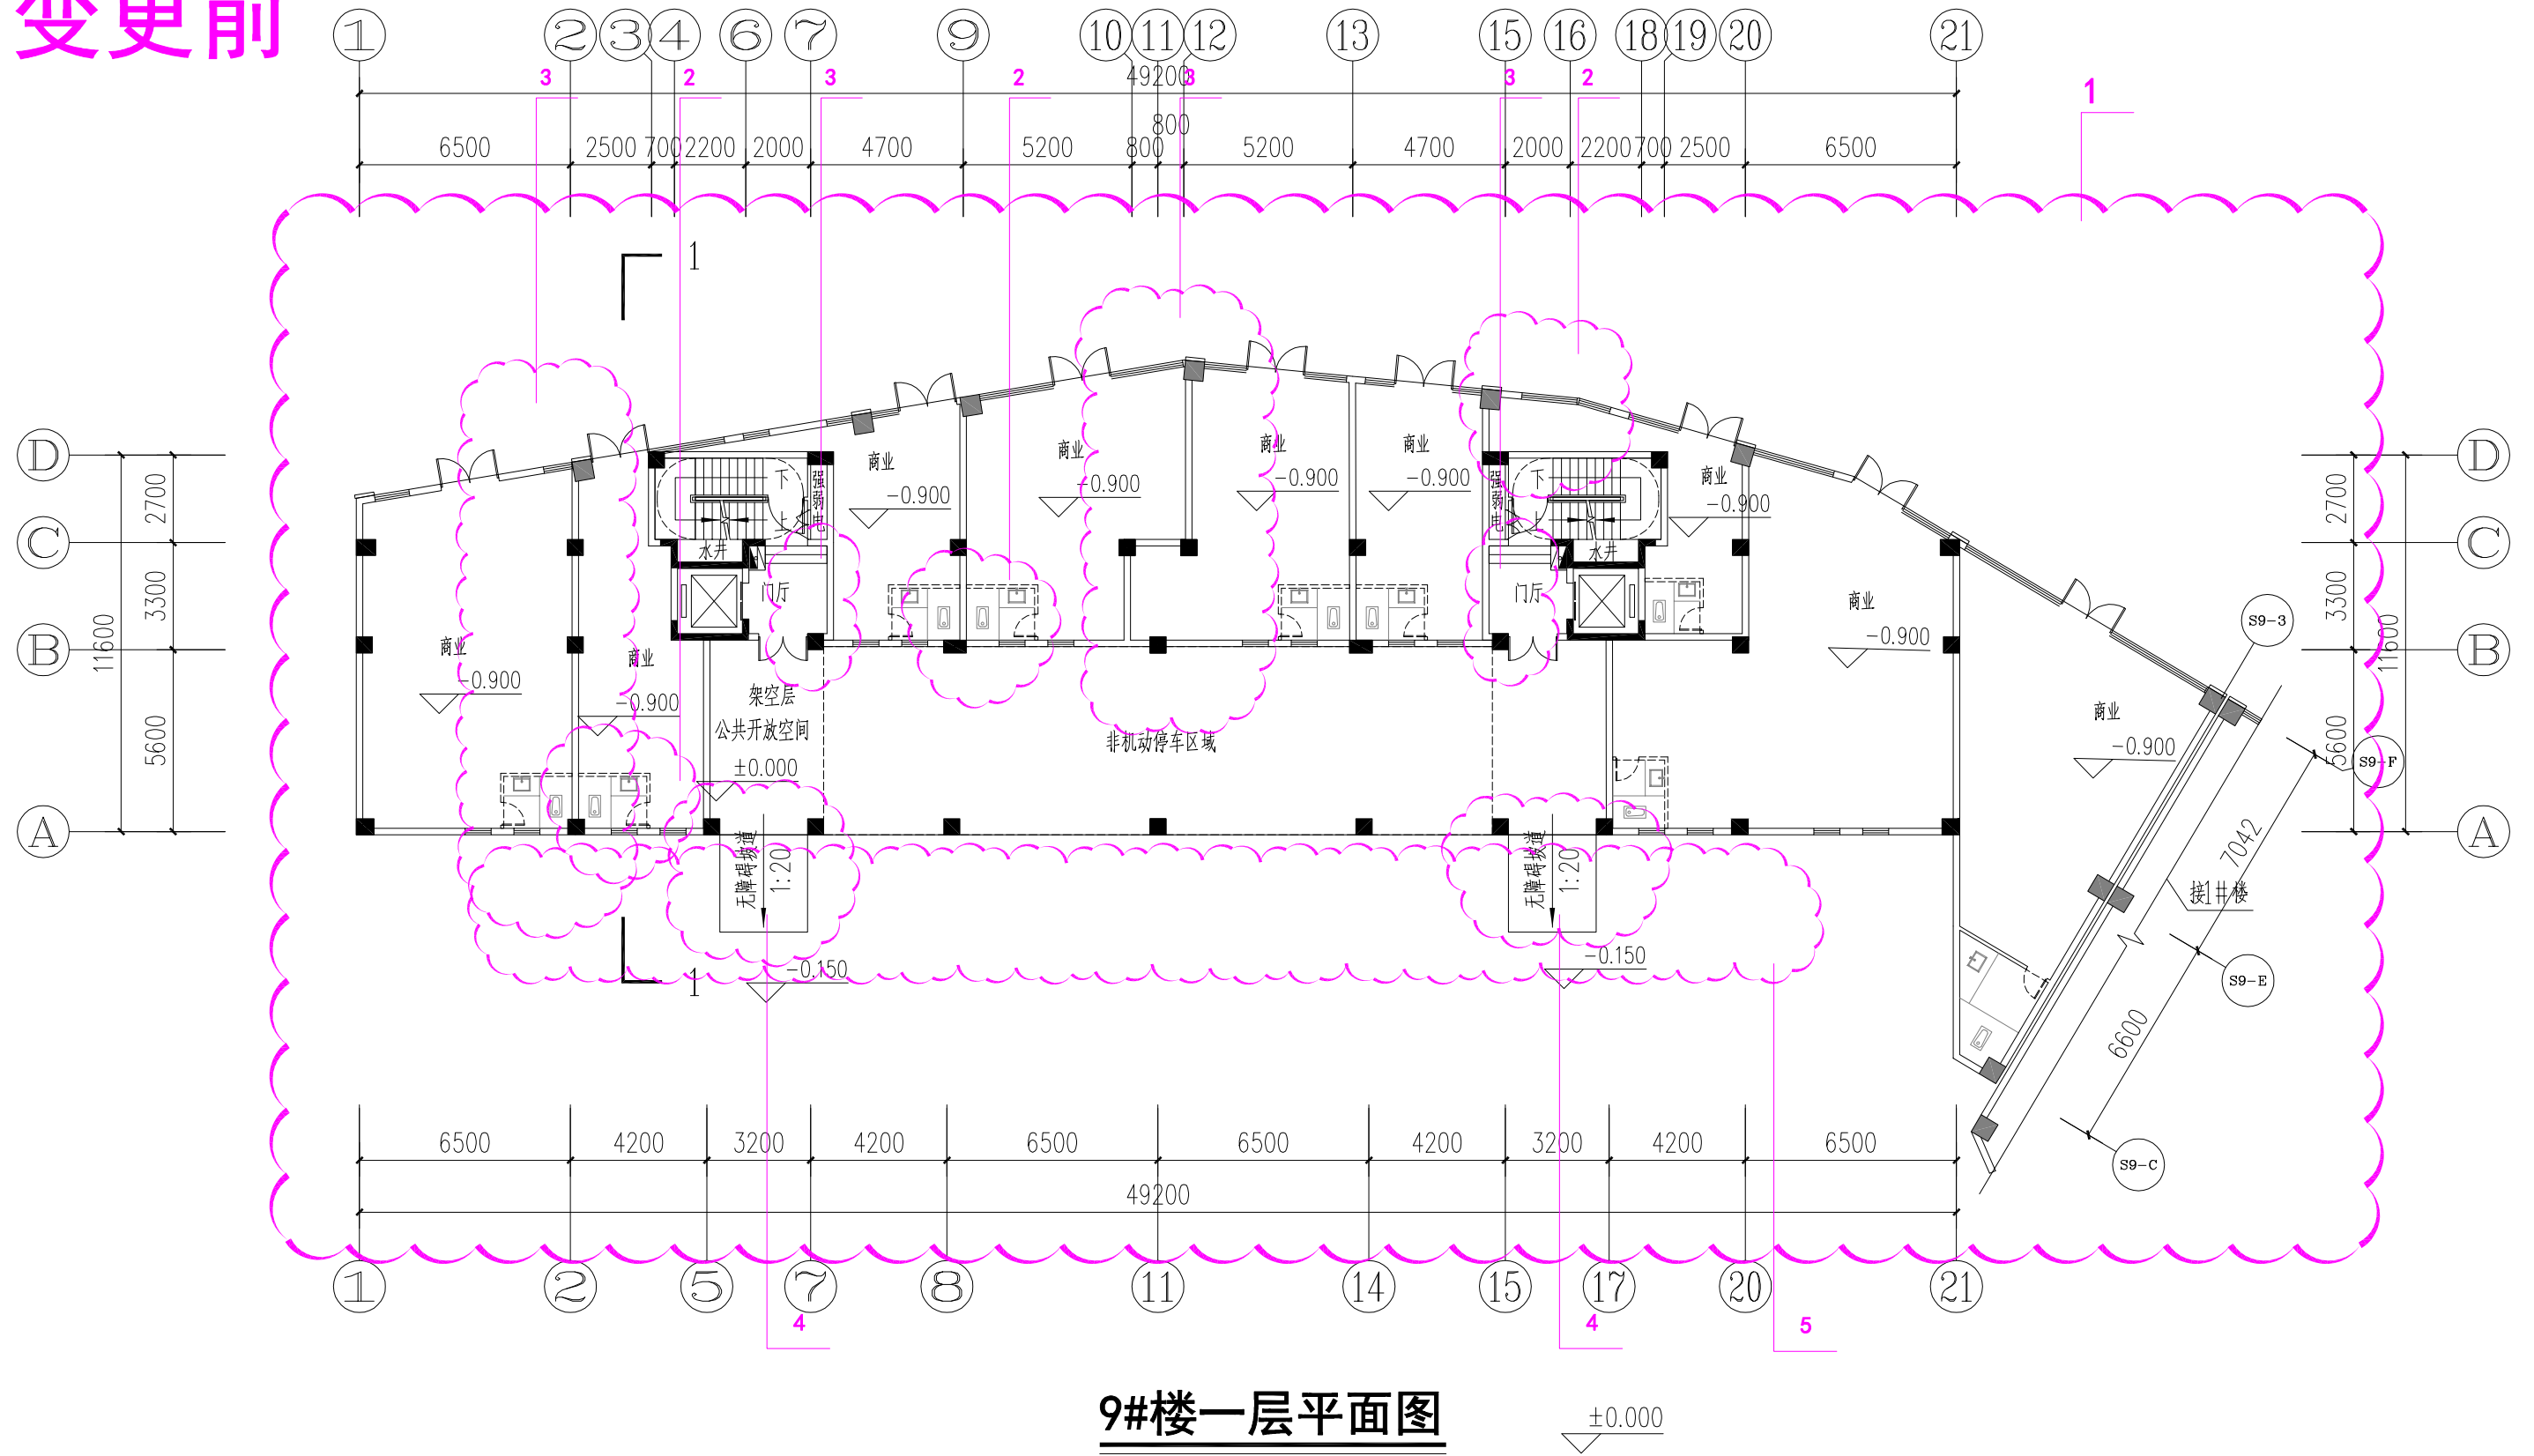[illegible]

变更后

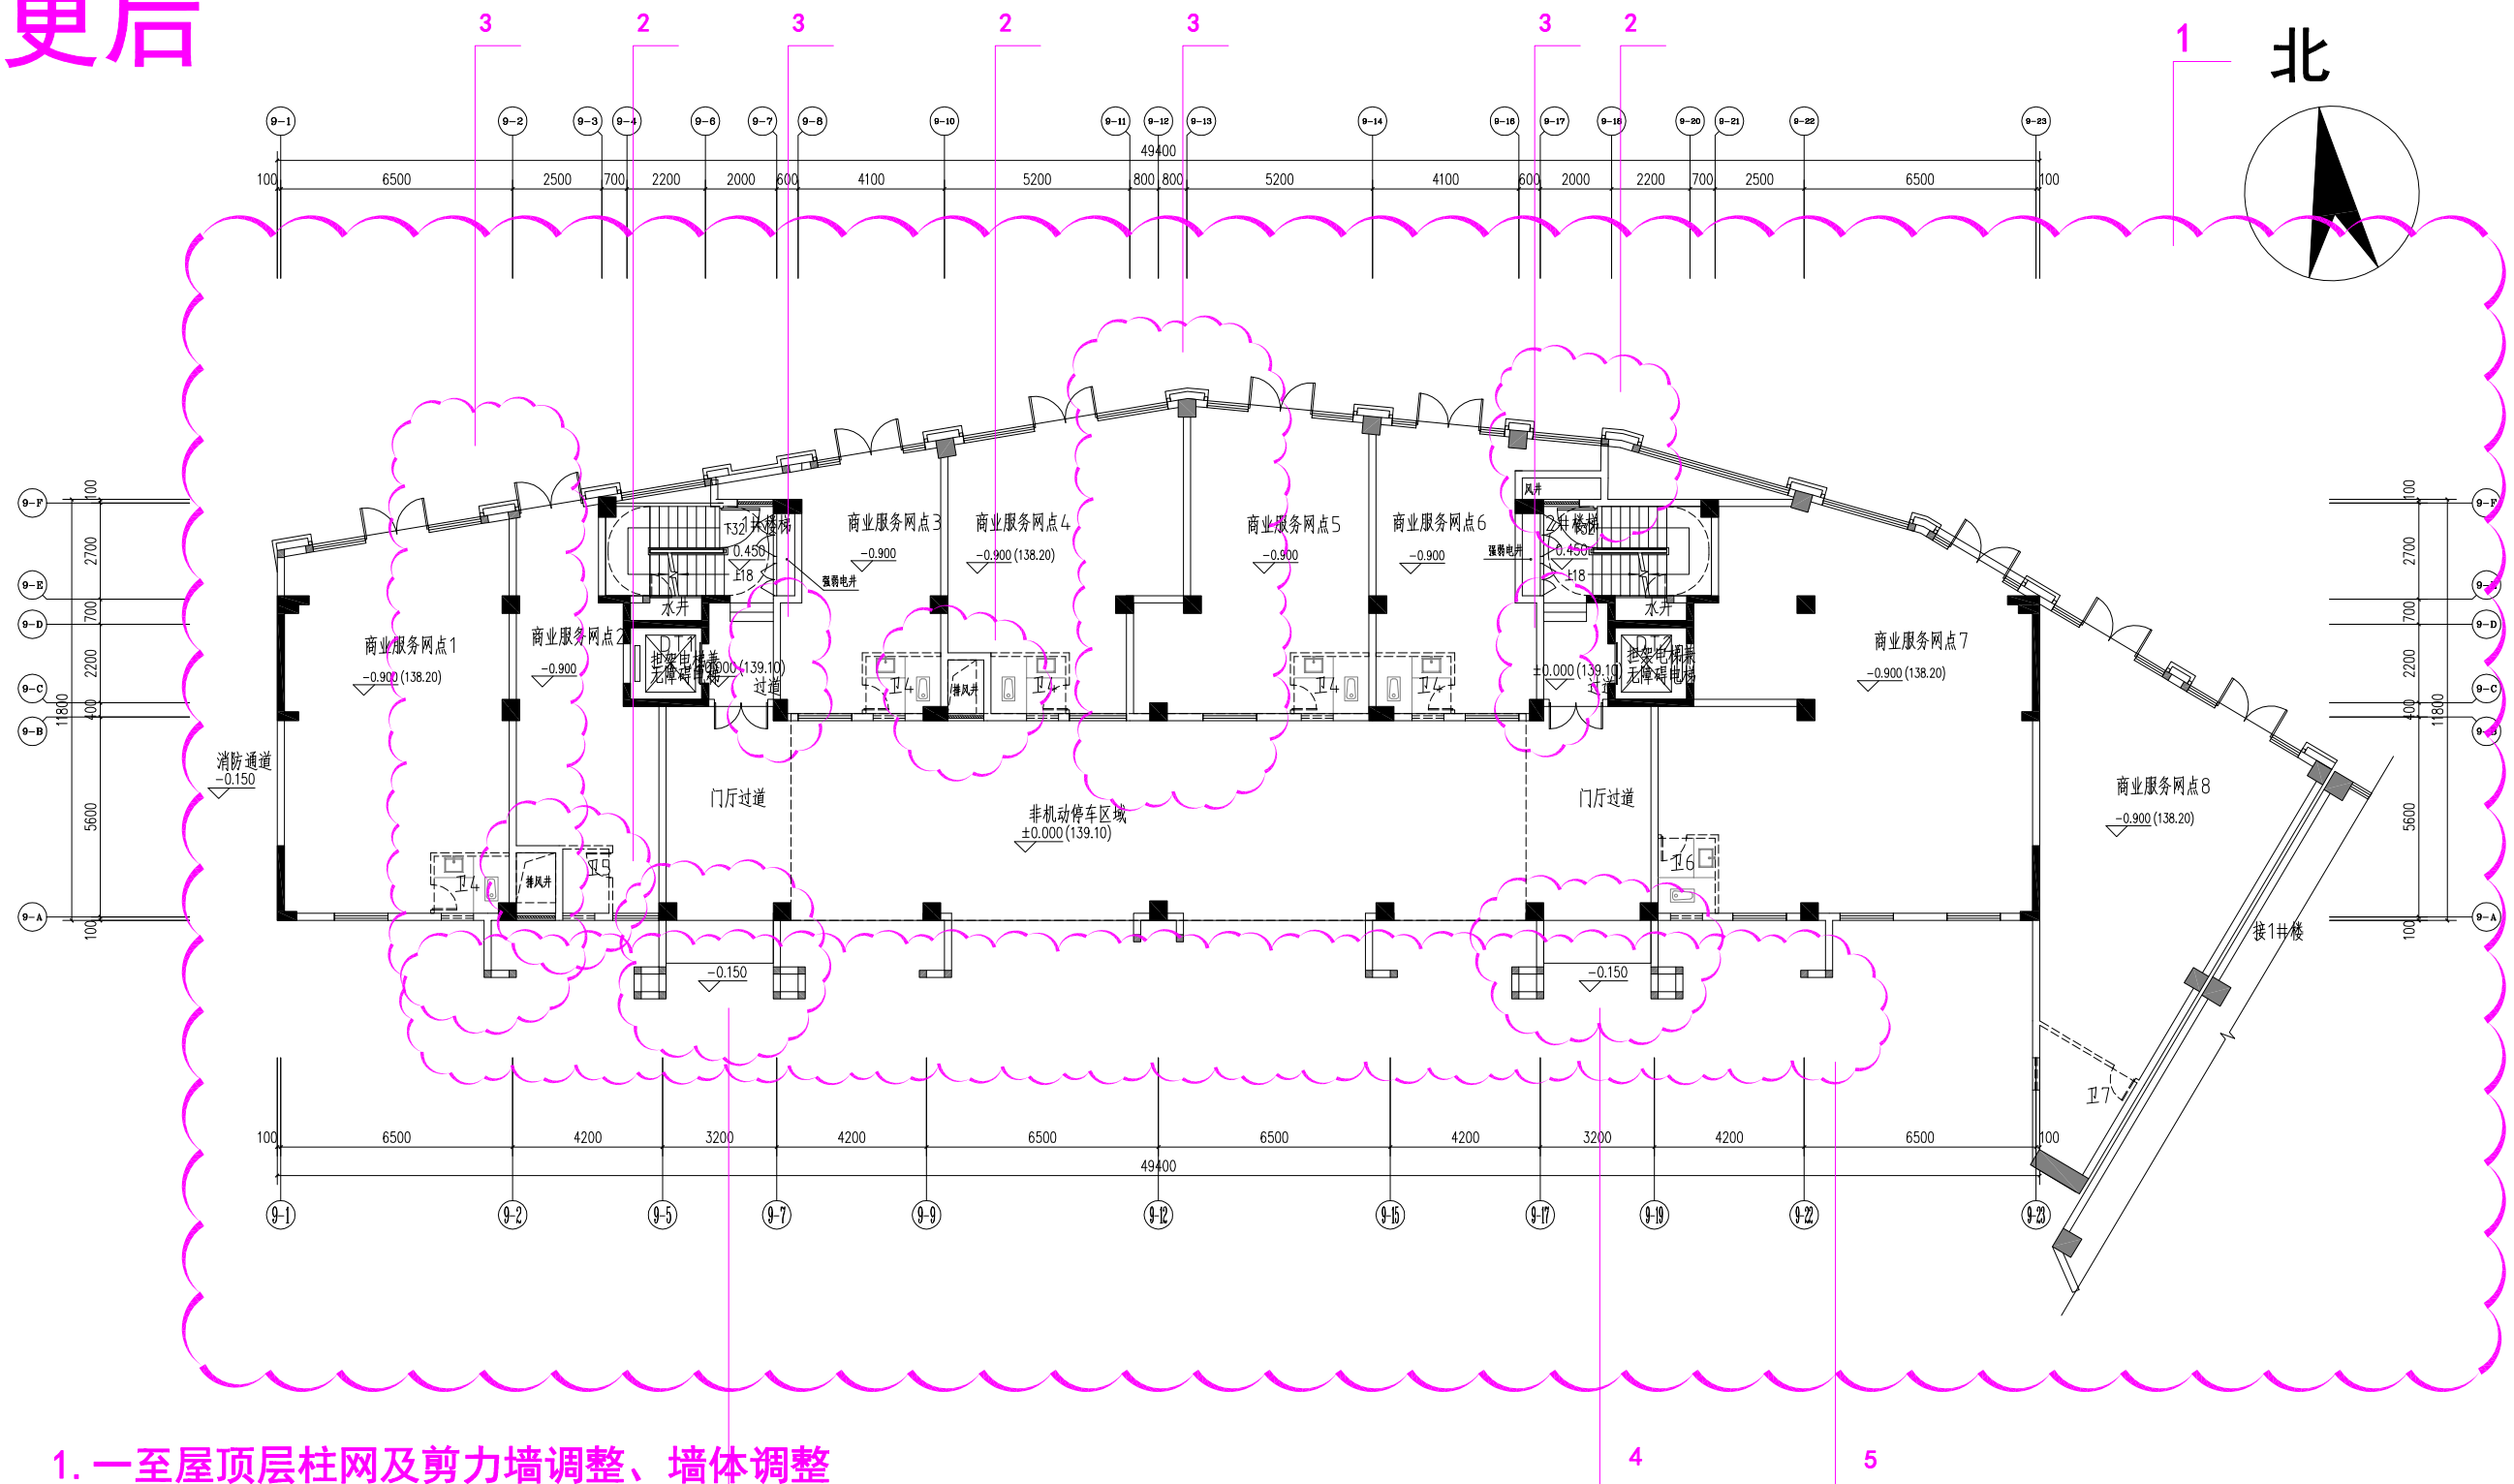


9#楼一层平面图

1. 一至屋顶层柱网及剪力墙调整、墙体调整
2. 增设风井、排风井
3. 商业内隔墙调整，9-B轴墙体外移0.2米，计容面积增加4.32m²
4. 无障碍坡道长度调整
5. 9-A轴增设装饰墙

设计单位	福建一建集团有限公司	建设单位	三明市三元区城市建设投资有限责任公司	工程名称	荆东安置房及周边附属配套工程（安置房）	图 名	9#楼一层平面图	图 别	方 案
								日 期	2023. 07

变更前

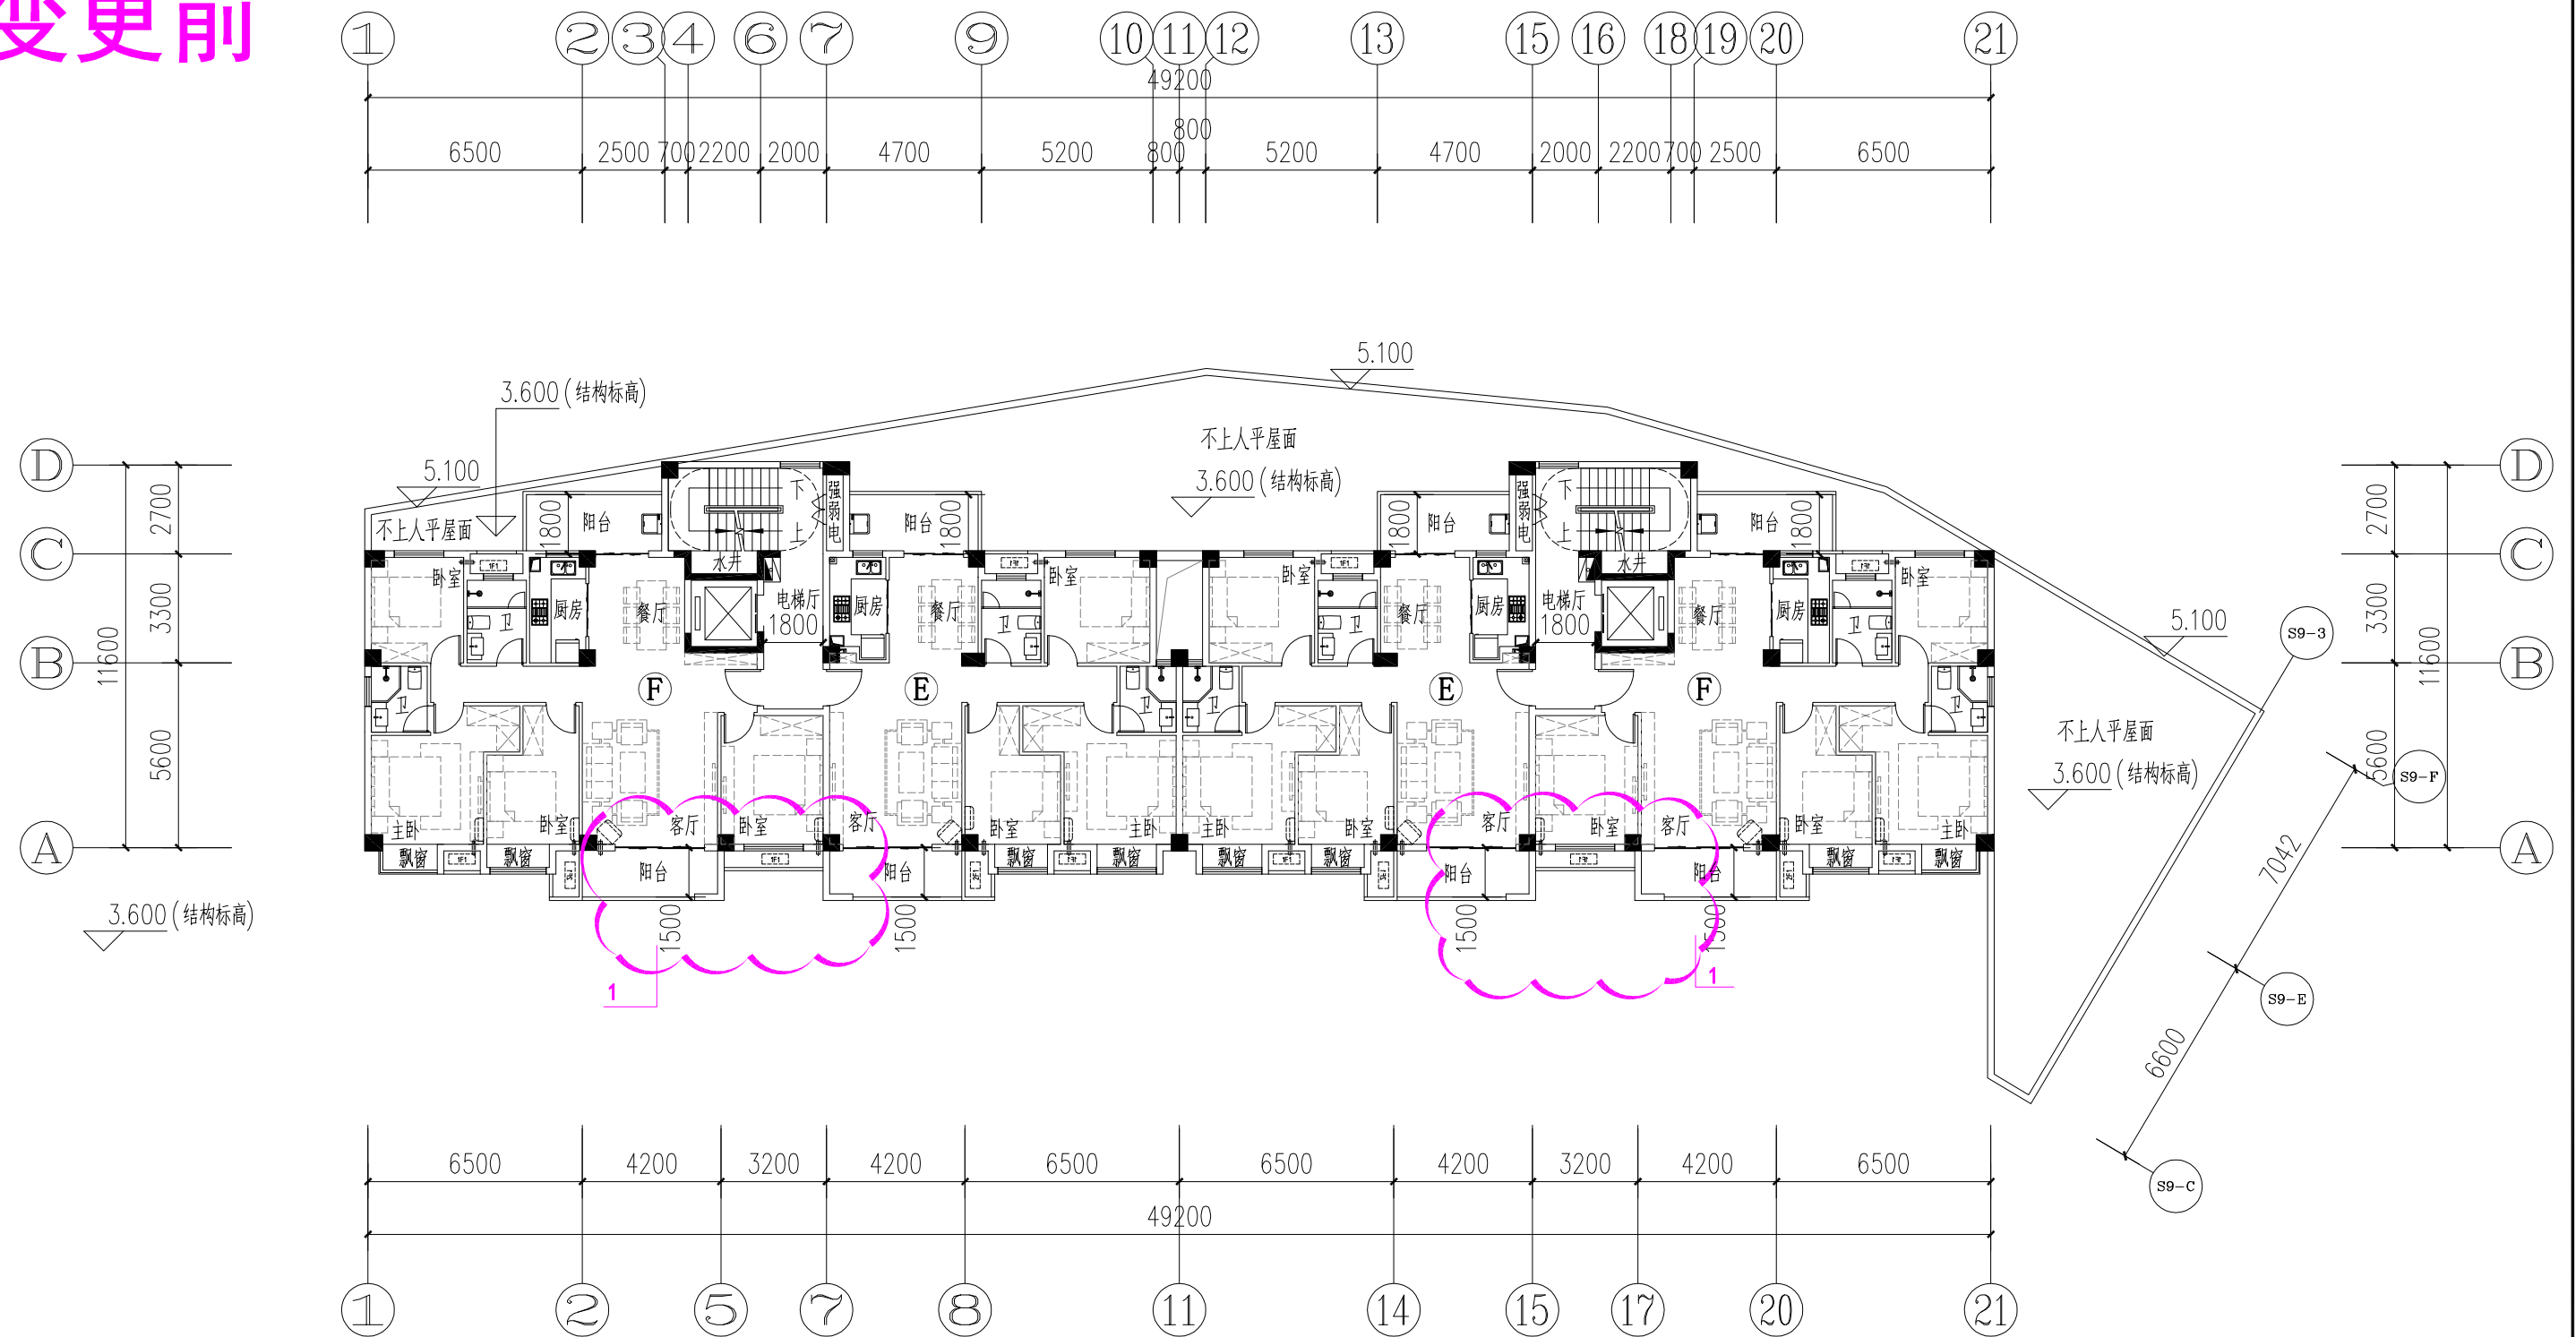


9#楼二层平面图

设计单位	福建一建集团有限公司	建设单位	三明市三元区城市建设投资有限责任公司	工程名称	荆东安置房及周边附属配套工程（安置房）	图 名	9#楼二层平面图	图 别	方 案
								日 期	2020. 12

变更后


1. 增设雨披

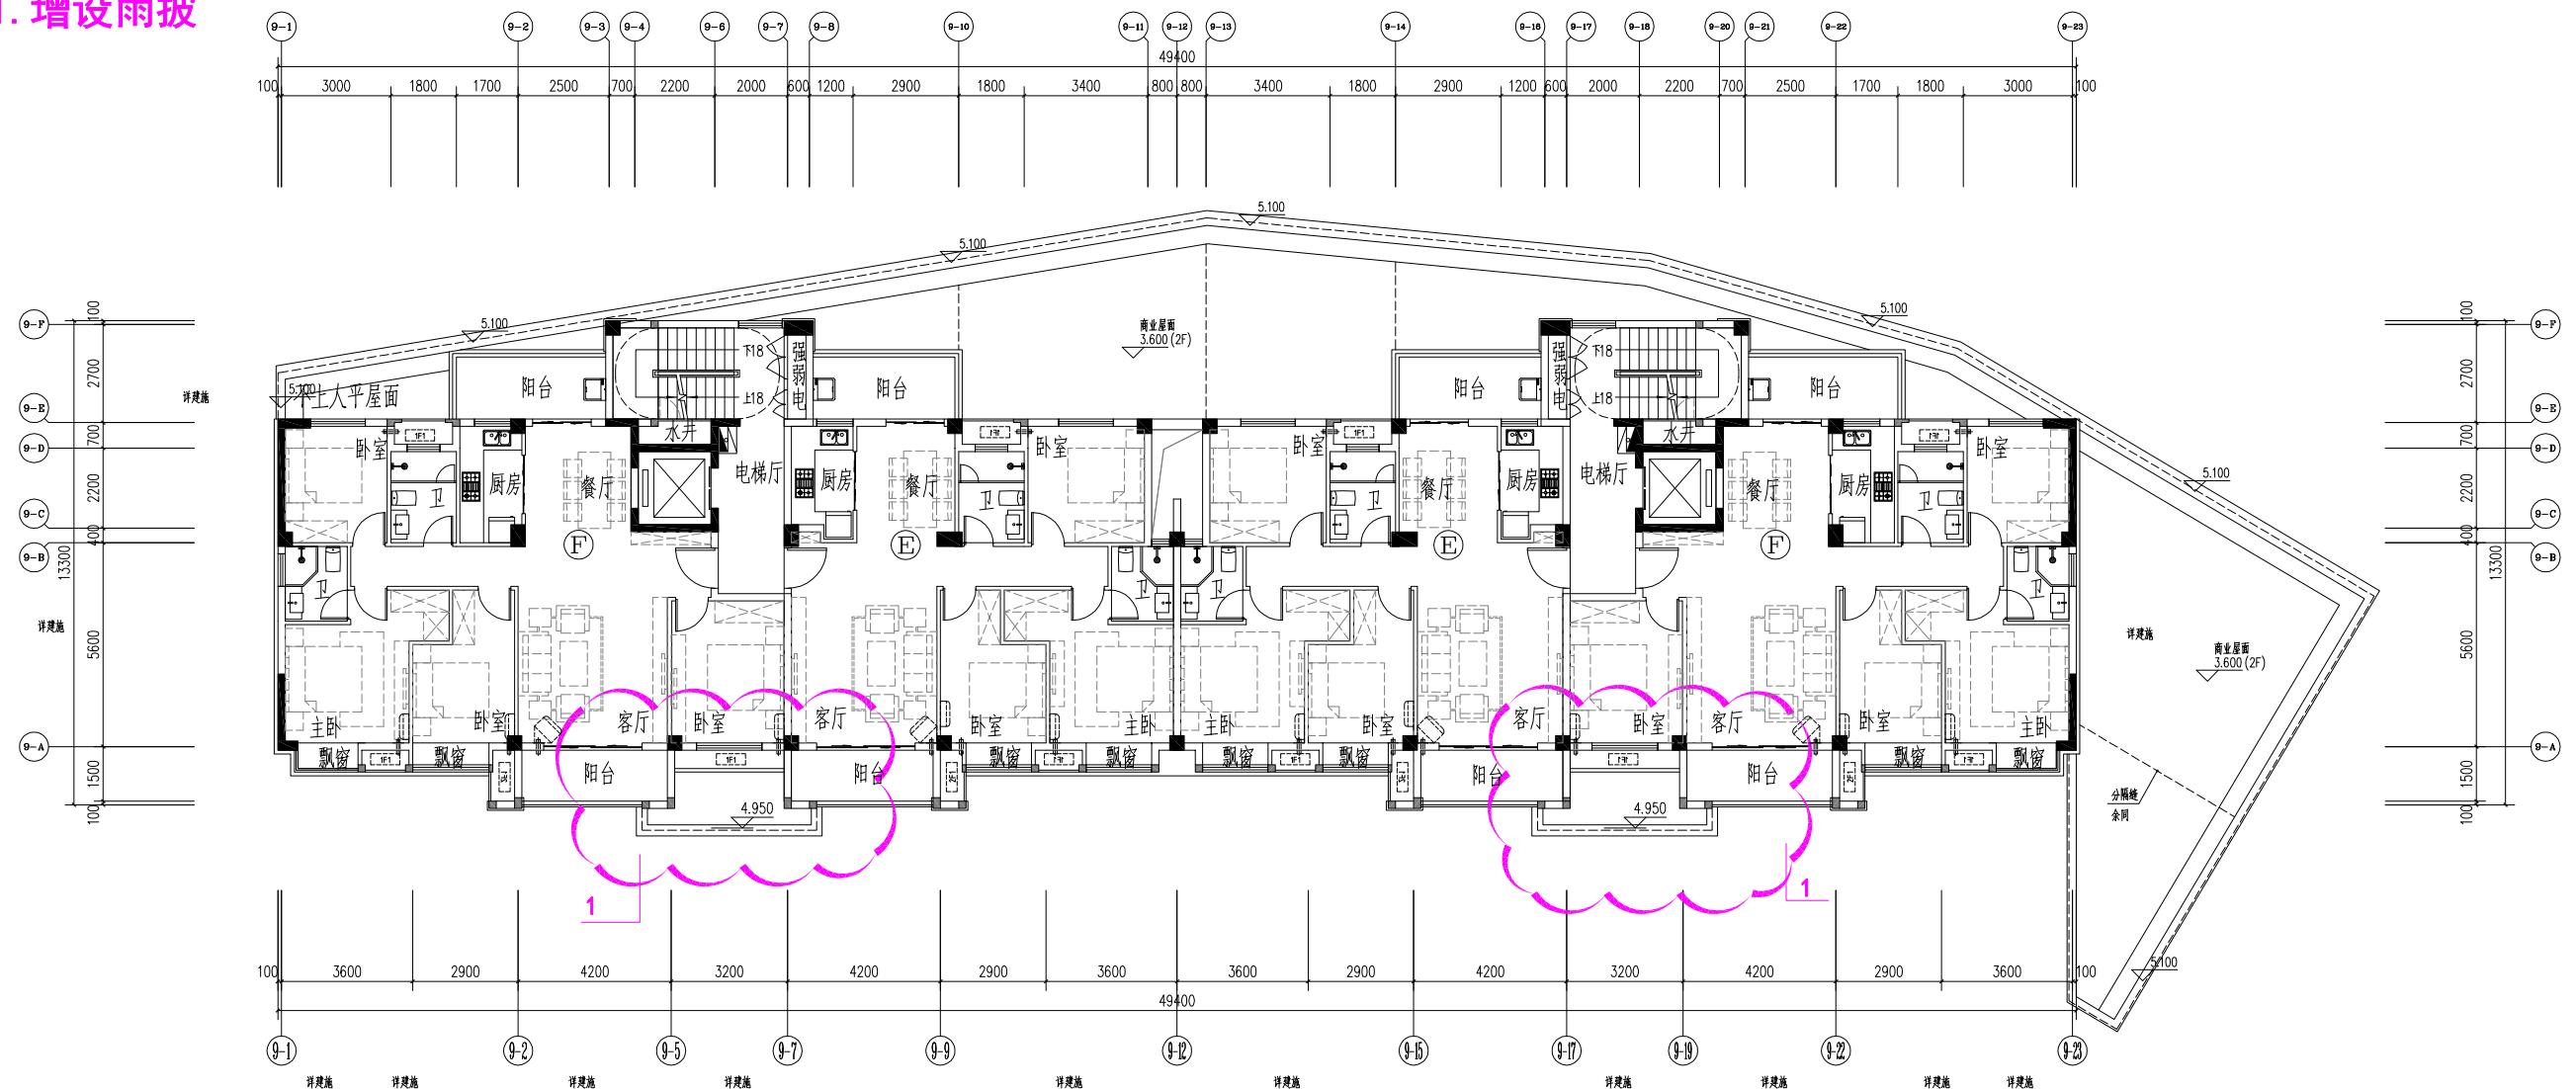

9#楼二层平面图

设计单位	福建一建集团有限公司	建设单位	三明市三元区城市建设投资有限责任公司	工程名称	荆东安置房及周边附属配套工程（安置房）	图 名	9#楼二层平面图	图 别	方 案
								日 期	2023. 07

变更前

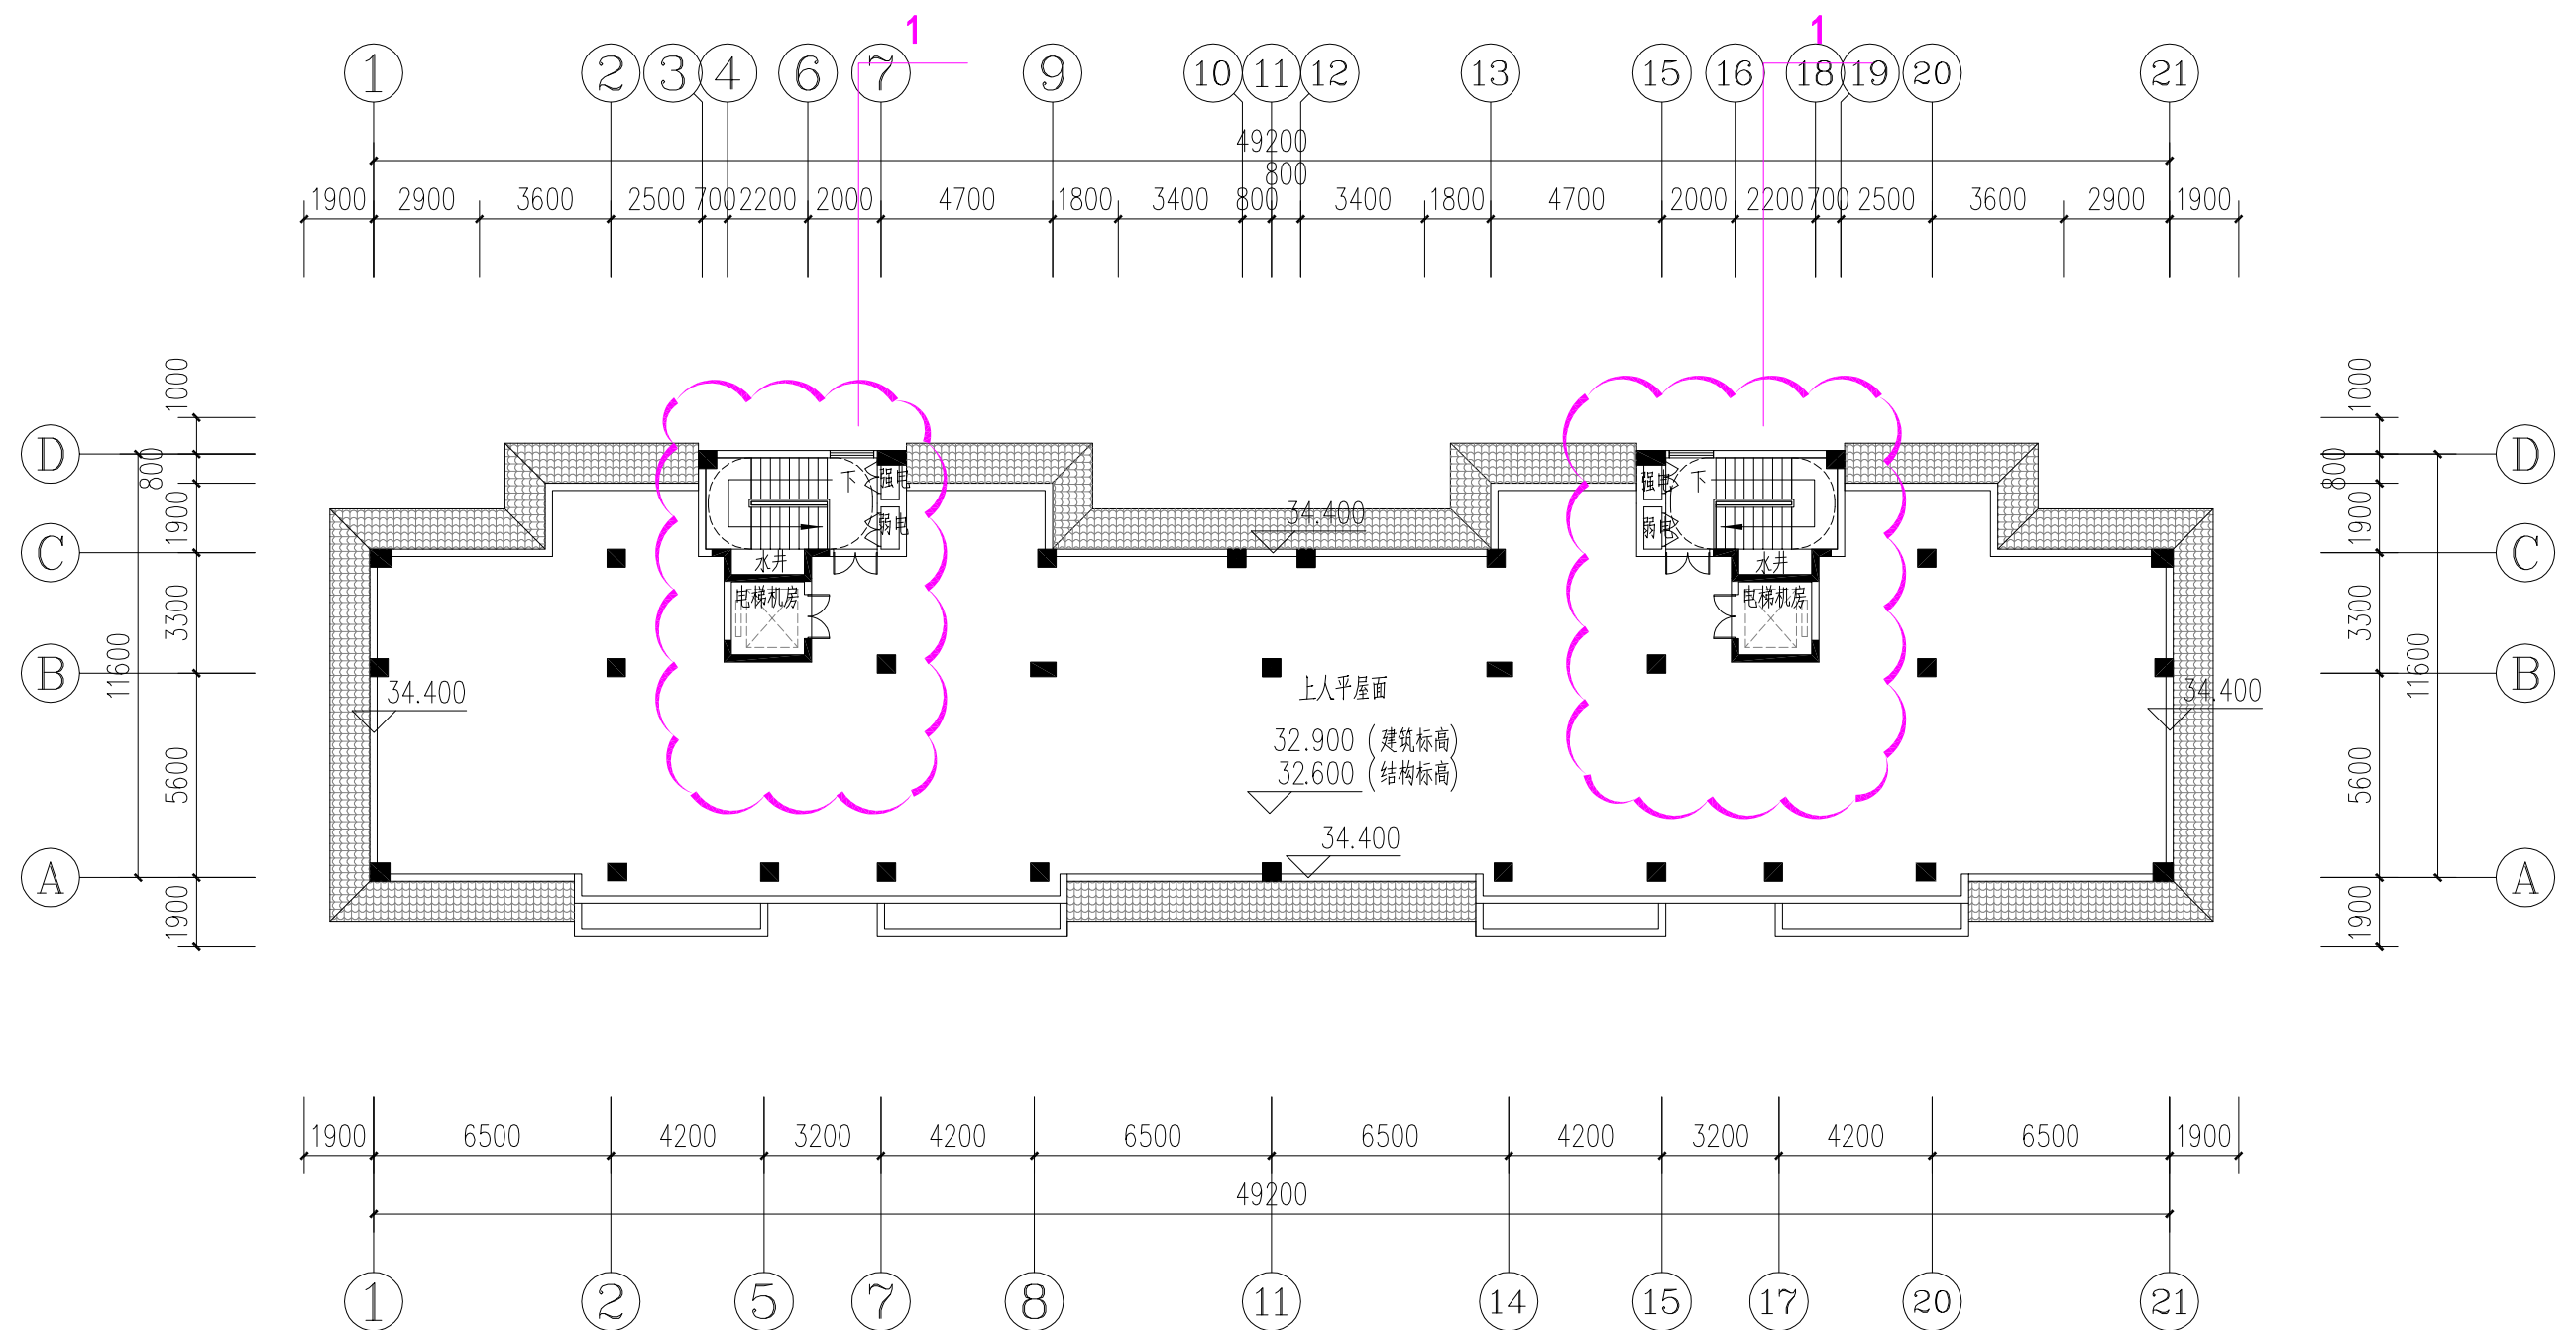


9#楼屋顶平面图

32.600

设计单位	福建一建集团有限公司	建设单位	三明市三元区城市建设投资有限责任公司	工程名称	荆东安置房及周边附属配套工程（安置房）	图 名	9#楼屋顶平面图	图 别	方 案
								日 期	2020. 12

变更后

1. 取消强弱电井、电梯机房范围调整

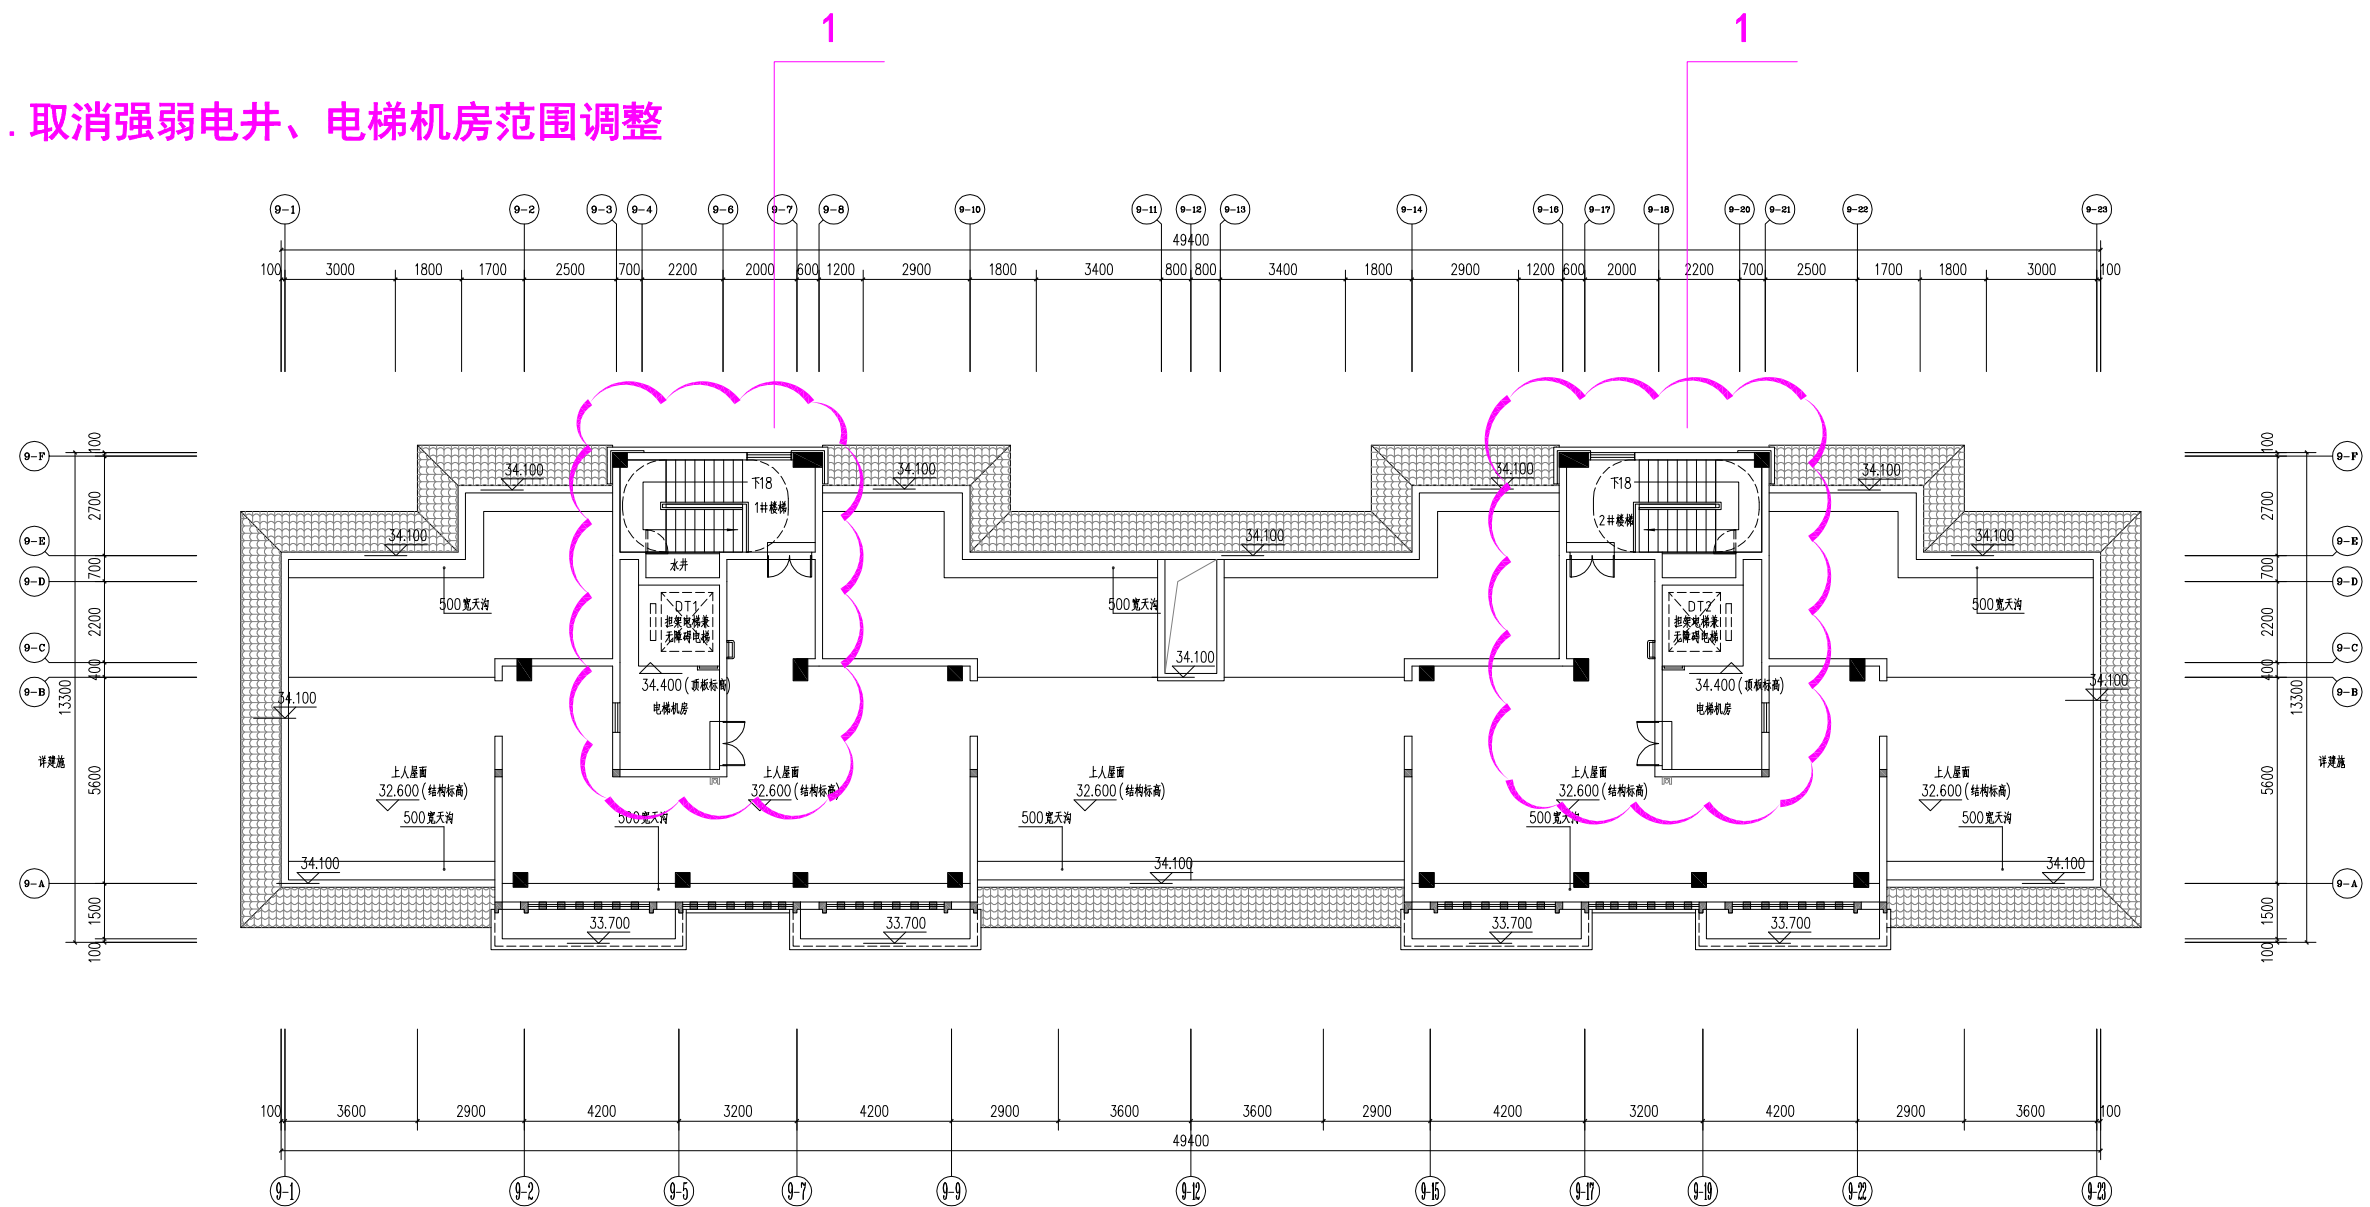

9#楼屋面层平面图

[illegible]