

设计修改通知便函(C16-ZTJZ-BG-40)


建设单位	三明生态新城明城康养投资开发有限公司	主送单位	建设单位
工程名称	三明生态康养城建设项目（C-16地块）	抄送单位	质检 监理 施工单位
工程编号	J2020-12-C16	发文日期	2023. 08

更改理由

1. 原设计图纸错、漏、碰、缺的更正。
2. 原设计计算的更正。
3. 原构造设计的改进或完善。
- √ 4. 其它工种设计人员要求配合更改。
5. 地质条件与原资料有出入造成的修改。
- √ 6. 建设单位要求更改。
7. 施工单位要求更改。
8. 施工条件变化。
9. 施工图审查意见。

一、根据现场实际情况对以下内容进行变更：

- 1、19#楼14至18轴交A至G轴结构板调整，具体详附图一；
- 2、地下室出屋面楼梯间造型由混凝土材质改为钢结构及玻璃材质，具体详附图二；
- 3、根据设备专业功能需求调整消控室面积，具体详附图三。

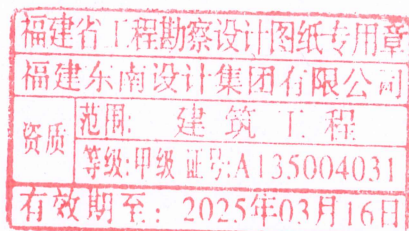

福建东南设计集团有限公司	审 定	陈玉玲		项目负责	李榕燕		设 计	黄荣彬	
	审 核	陈玉玲		专业负责	李榕燕		校 对	雷照丽	


本函一式4份，盖章方可生效

领单人：


领单日期：

第 1 页 共 4 页

日期	姓名	专业	日期	姓名	专业
		电气			暖通
		电			暖
		通			通
专业	姓名	专业	专业	姓名	专业
建筑		建筑	建筑		建筑
结构		结构	结构		结构
给排水		给排水	给排水		给排水

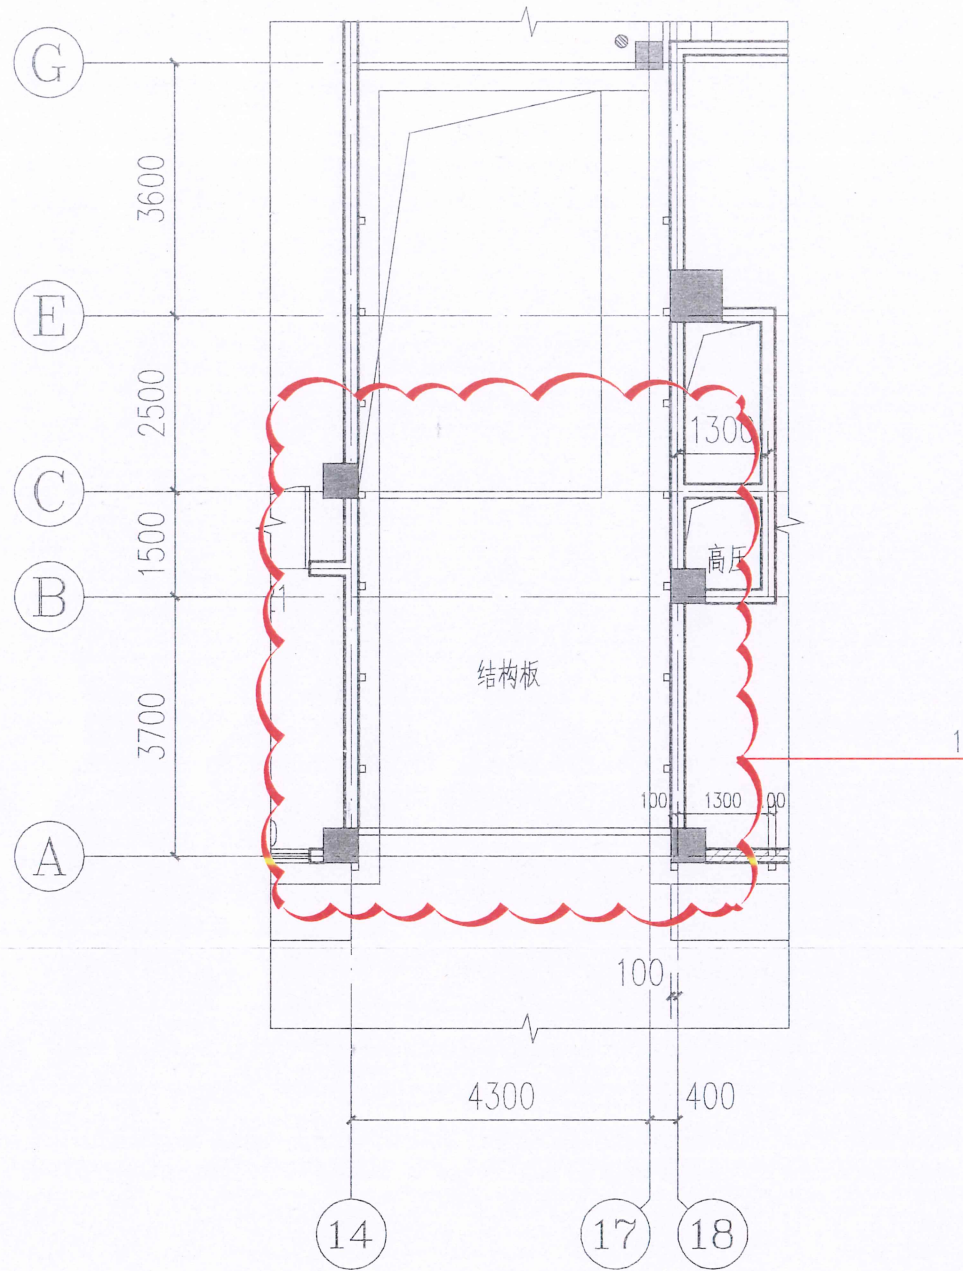

19#楼二层局部平面图
(原审批图)

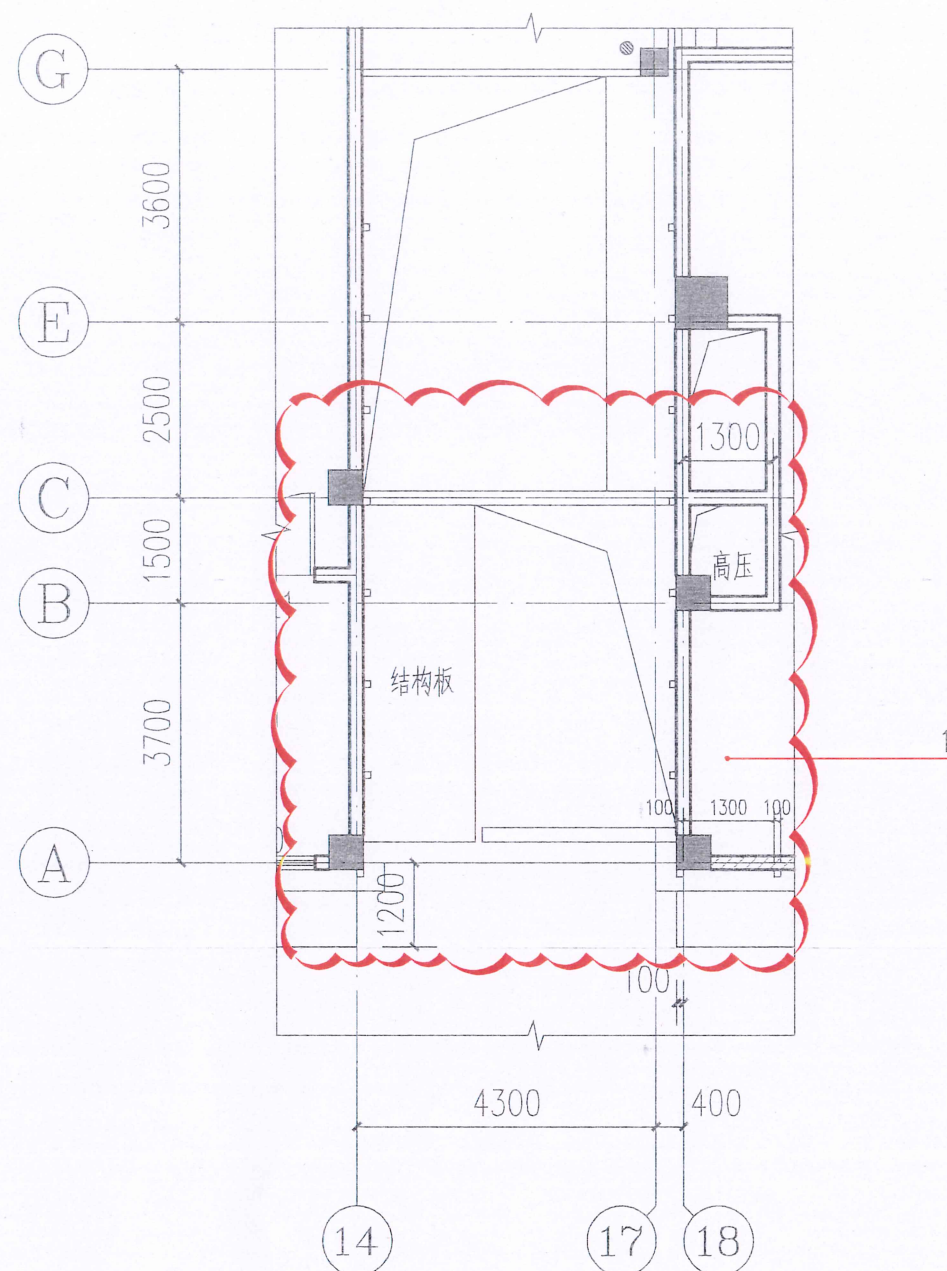

19#楼二层局部平面图
(拟变更图)

根据19#楼现场实际情况更改以下变更:

1、原14-18轴A-G轴结构板调整,具体详云线部分。




福建东南设计集团有限公司

建设部甲级证号:A135004031

施工图审查批准单位:

施工图审查批准书证号:

图纸专用章:

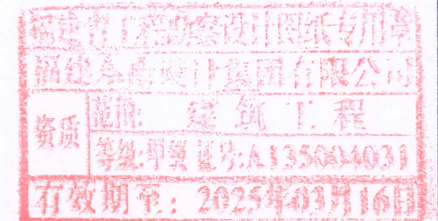

注册建筑师执业章:
中华人民共和国一级注册建筑师

姓名: 李榕燕
注册号: 3500403-011
有效期: 至2023年10月

注册结构师执业章:

工程名称:

三明生态康养城建设项目(C-16地块)

建设单位: 三明生态新城明城康养投资开发有限公司



审 定	陈玉玲	陈玉玲
项目负责	李榕燕	李榕燕
专业负责	李榕燕	李榕燕
审 核	陈玉玲	陈玉玲
校 对	雷照丽	雷照丽
设 计	黄荣斌	黄荣斌
制 图	黄荣斌	黄荣斌

图名:

附图一

图 别	建 施	工程编号	J2020-12-C16
图 号	02	日 期	2023. 8

日期		姓名		专业	电气	暖通		日期		姓名		专业	建筑	结构	给排水
----	--	----	--	----	----	----	--	----	--	----	--	----	----	----	-----

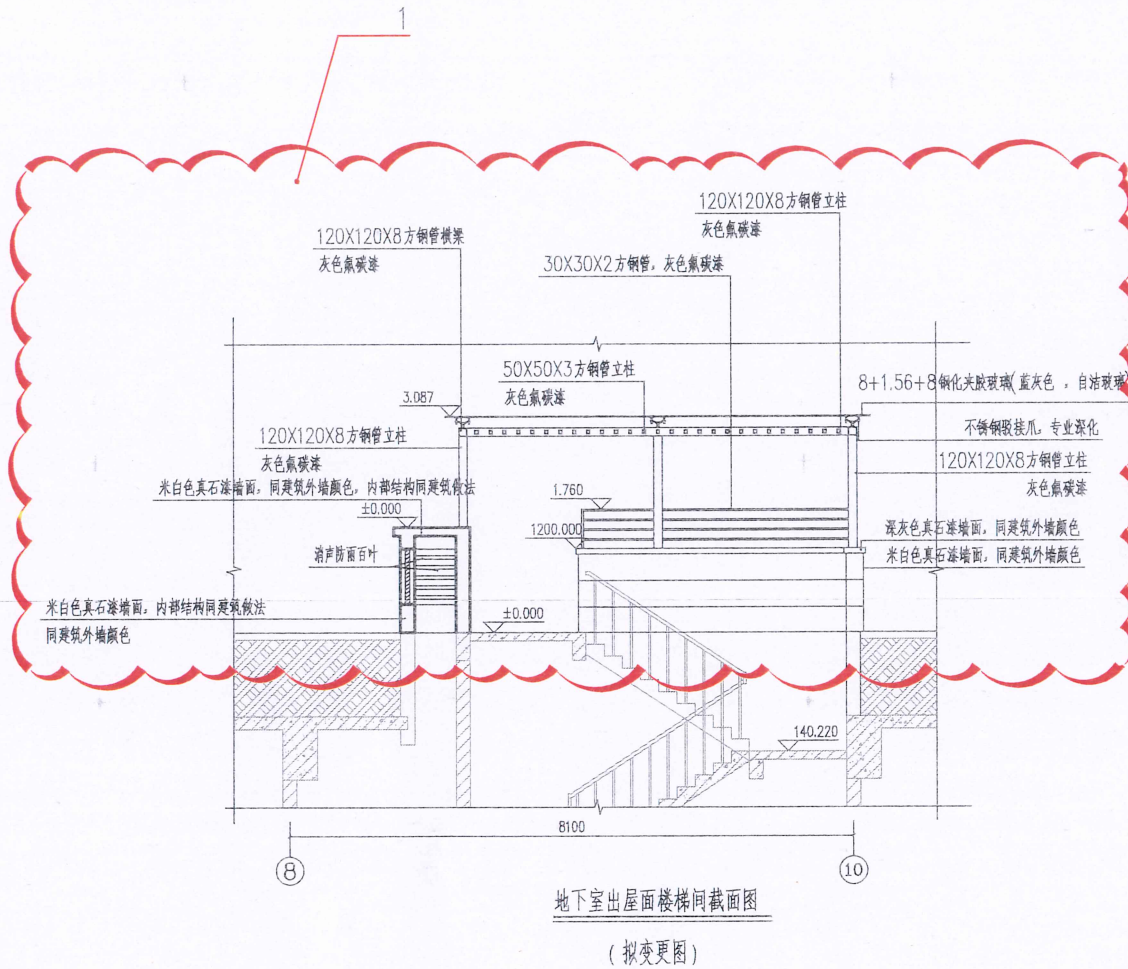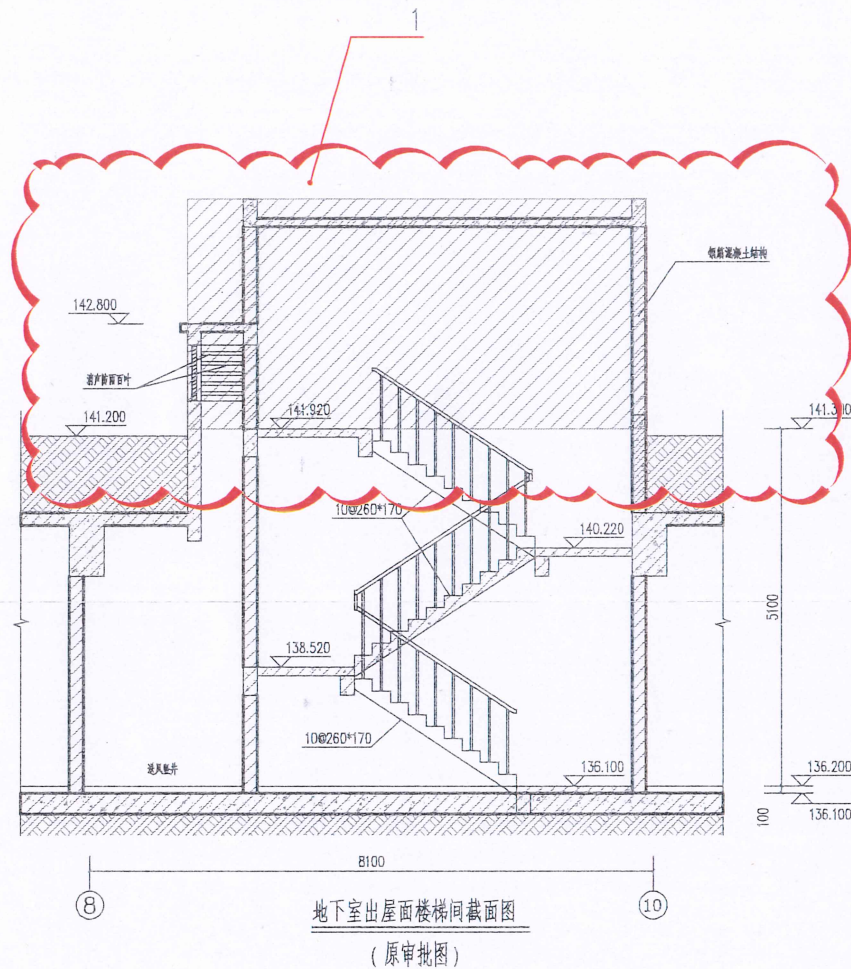

根据地下室现场实际情况更改以下变更:

1、地下室屋面楼梯间造型调整,由混凝土材质改为钢结构及玻璃材质,具体详云线部分.




福建东南设计集团有限公司

建设部甲级证号:A135004031

施工图审查批准单位:

施工图审查批准书证号:

图纸专用章:

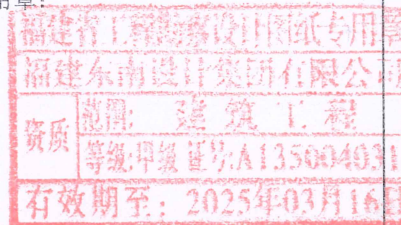

中华人民共和国一级注册建筑师

注册建筑师执业章:

姓名: 李榕燕
注册号: 3500403-011
有效期: 至2023年10月

注册结构师执业章:

工程名称:

三明生态康养城建设项目(C-16地块)

建设单位: 三明生态新城明城康养投资开发有限公司


审定	陈玉玲	陈玉玲
项目负责	李榕燕	李榕燕
专业负责	李榕燕	李榕燕
审核	陈玉玲	陈玉玲
校对	陈有贤	陈有贤
设计	雷照丽	雷照丽
制图	雷照丽	雷照丽

图名:


附图二

图别	建施	工程编号	J2020-12-C16
图号	03	日期	2023.8

日期		姓名		专业	电气	暖通	
日期		姓名		专业	建筑	结构	给排水

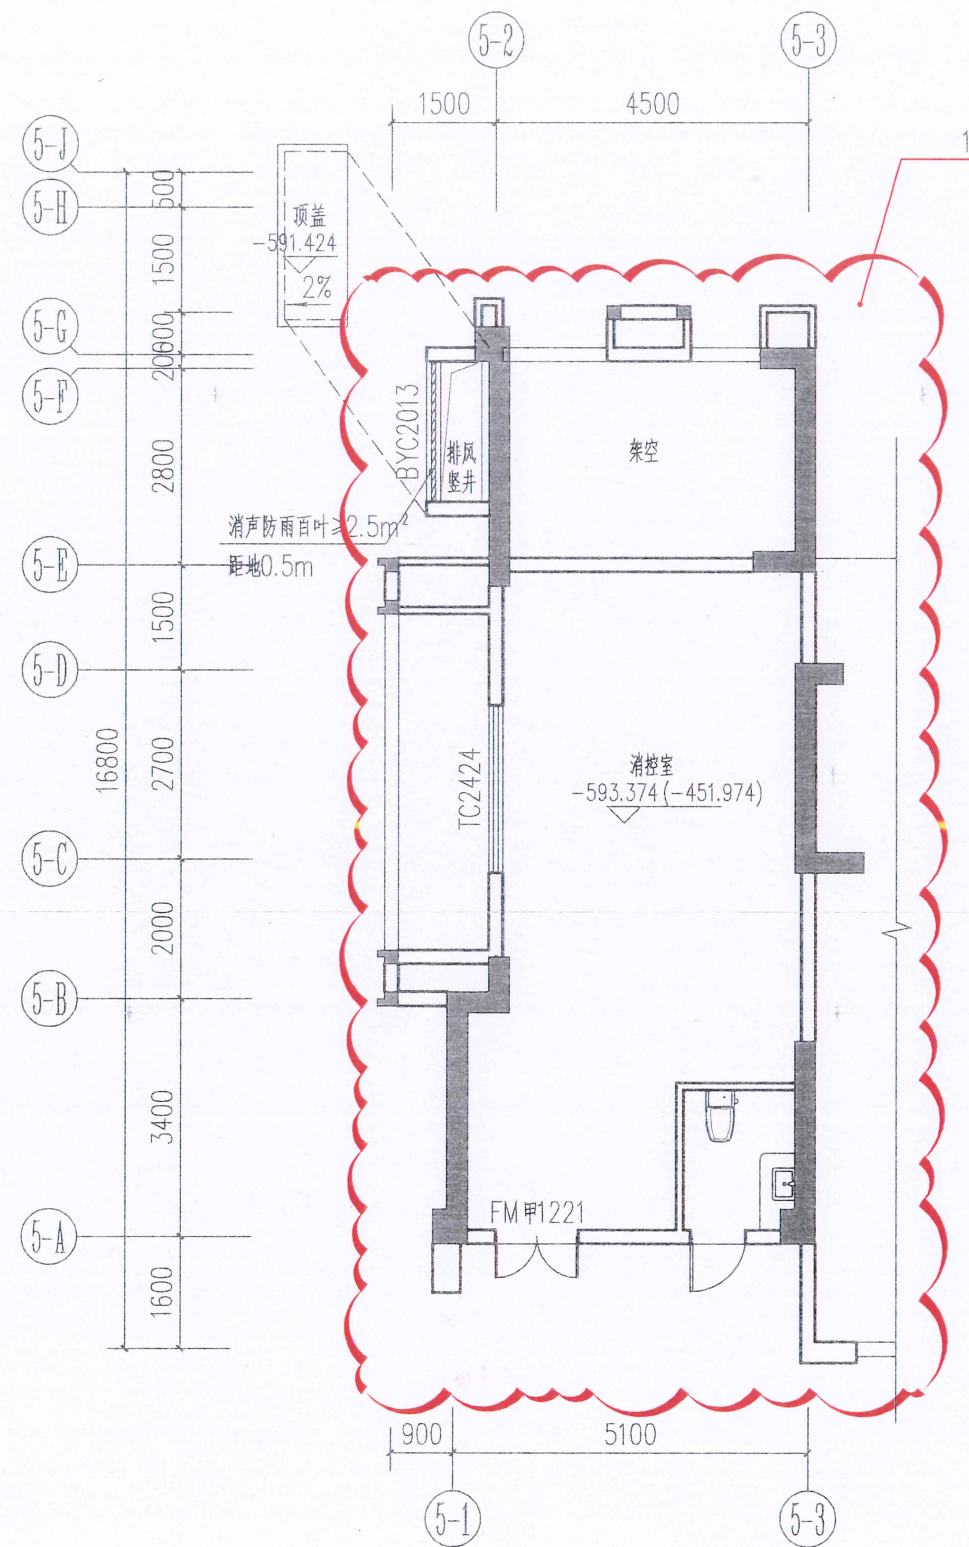

5#一层局部平面图
(原审批图)

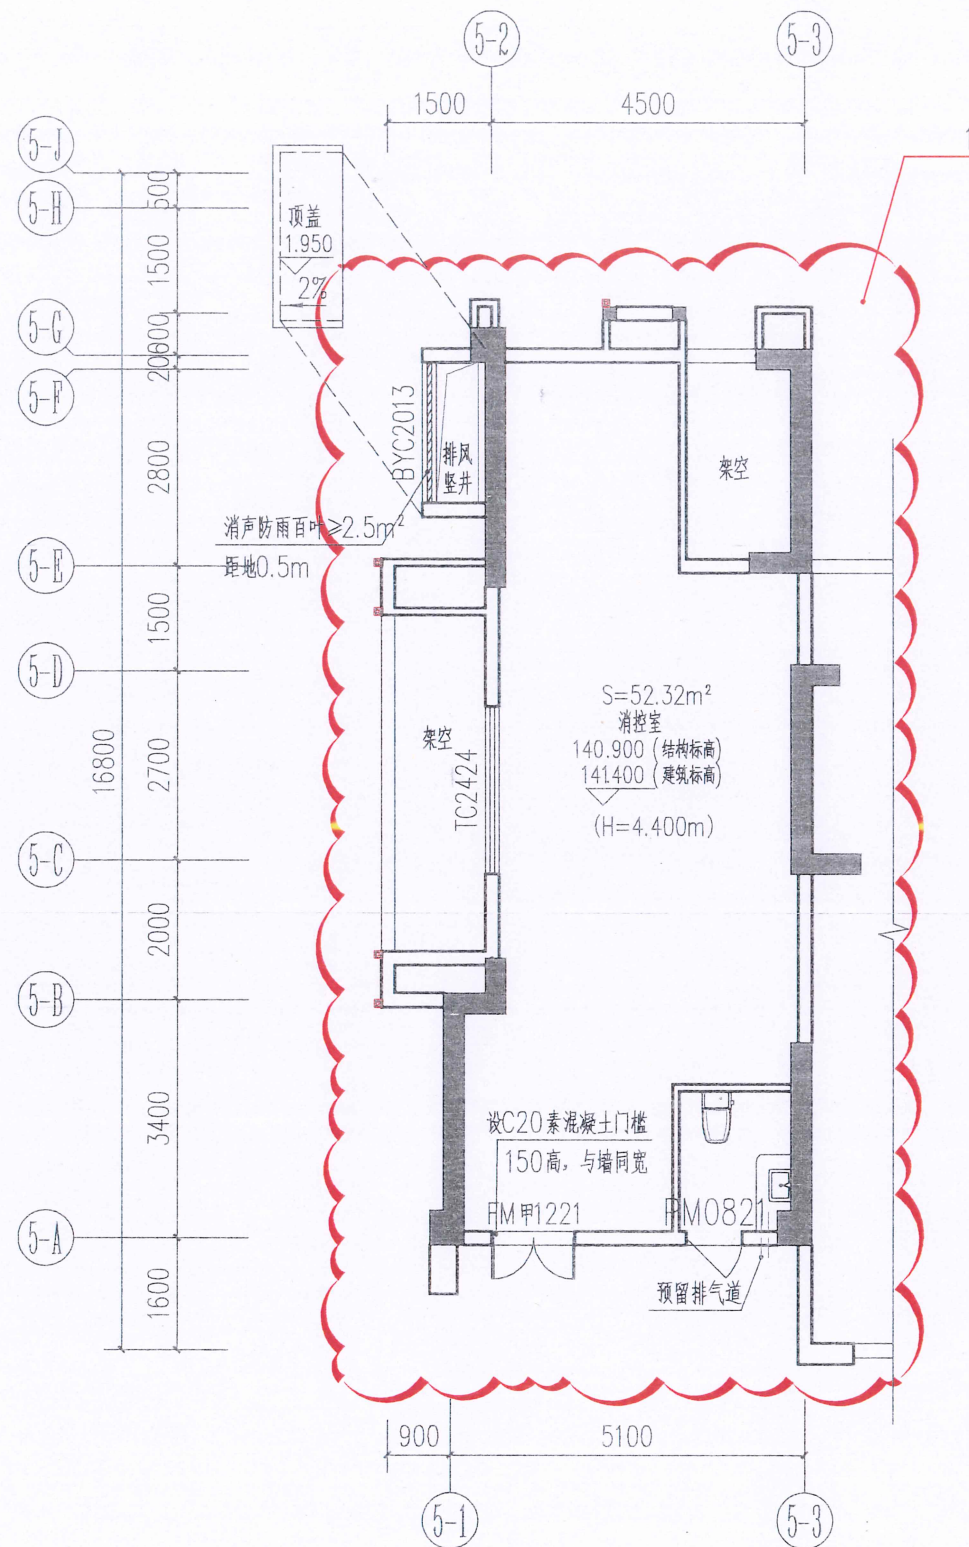

5#一层局部平面图
(拟变更图)

根据地下室现场实际情况更改以下变更:

- 根据设备专业功能需求调整消防室面积,具体详云线部分.



福建东南设计集团有限公司

建设部甲级证号:A135004031

施工图审查批准单位:

施工图审查批准书证号:

图纸专用章:

福建省工程勘察设计图纸专用章
福建东南设计集团有限公司
资质范围: 建筑工程
等级: 甲级 证号: A135004031
有效期至: 2025年03月16日

注册建筑师执业章:

中华人民共和国一级注册建筑师

姓名: 李榕燕
注册号: 3500403-011
有效期: 至2023年10月

注册结构师执业章:

工程名称:

三明生态康养城建设项目(C-16地块)

建设单位: 三明生态新城明城康养投资开发有限公司

审定	陈玉玲	陈玉玲
项目负责	李榕燕	李榕燕
专业负责	李榕燕	李榕燕
审核	陈玉玲	陈玉玲
校对	陈有贤	陈有贤
设计	鄢樟胜	鄢樟胜
制图	鄢樟胜	鄢樟胜

图名:

附图三

图别	建施	工程编号	J2020-12-C16
图号	04	日期	2023.8