



总平面图 变更前

序号	图例	说明
1		新建建筑及层数
2		道路
3		用地红线
4		建筑退让线
5		地下室轮廓线
6		主要出入口
7		消防应急出入口
8		地下车库出入口
9		建筑出入口
10		黄海高程
11		消防登高操作场地
12		室外地面至屋面高度 室外地面至女儿墙高度
	垃圾收集点	变配电室
	非机动车停车位	消防控制室
	地面公共停车位	物业管理服务用房
	地面停车位	发电机房
	快充车位	开闭所
	公共计量间	社区卫生服务站
	社区用房	邮政快递服务场所
	公厕	小区公共服务设施
	垃圾分类收集点	

项目		指标	单位	备注
用地红线规划面积		55026.77	m²	约82.54亩
总建筑面积		132944.9	m²	
其中	计容总建筑面积	104000.0	m²	
	住宅建筑面积	94900.6	m²	
	安置住宅	10000.0	m²	
	配建住宅	8300.0	m²	
	销售住宅	76600.6	m²	
其中	高层住宅	69580.6	m²	
	叠拼住宅	7020.0	m²	
商业建筑面积		3099.4	m²	其中1059.5m²为生鲜超市
配套建筑面积		6000.0	m²	
其中	片区配套设施	5320.0	m²	
	幼儿园	4300.0	m²	
	社区用房	700.0	m²	
	社区卫生服务站	200.0	m²	
	公厕	120.0	m²	
其中	小区配套设施	680.0	m²	
	小区公共服务设施	400.0	m²	
	邮政快递服务场所	60.0	m²	
	垃圾分类收集点	10.0	m²	场地面积
物业管理用房		220.00	m²	
不计容总建筑面积		28944.90	m²	
其中	住宅架空层	3400.00	m²	
	地下室	25544.90	m²	
户外健身休息场所		400.00	m²	场地面积
建筑占地面积		12656.16	m²	
建筑密度		23.00%		规划要求≤23%
容积率		1.8900		1<FAR<1.9
绿地面积		16508.03	m²	
绿地率		30.00%		规划要求≥30%
户数		875	户	
住宅人口		2800	人	3.2人/户
规划机动车停车位		1144	辆	1.1位/100m²计容面积
其中	地面停车	114	辆	其中快充车位为12位
	地下停车	1030	辆	其中慢冲车位为217位
规划非机动车停车场		2080	m²	2m²停车面积/100m²计容面积

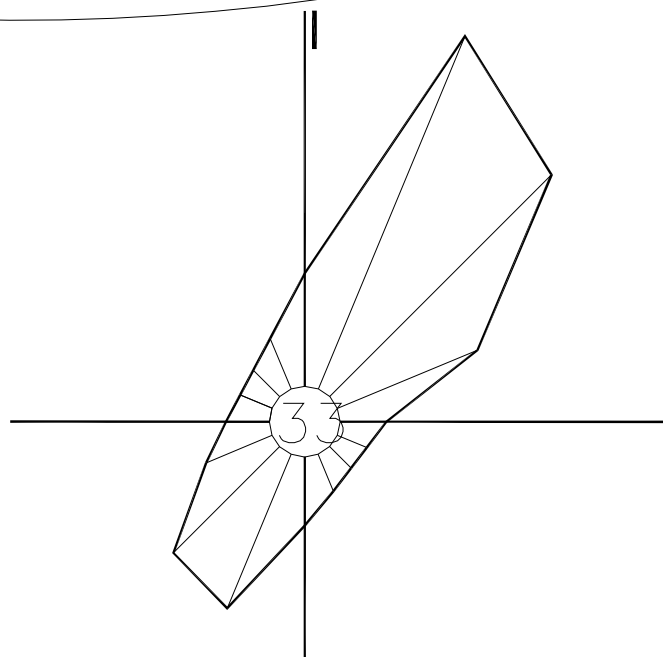

总平面图

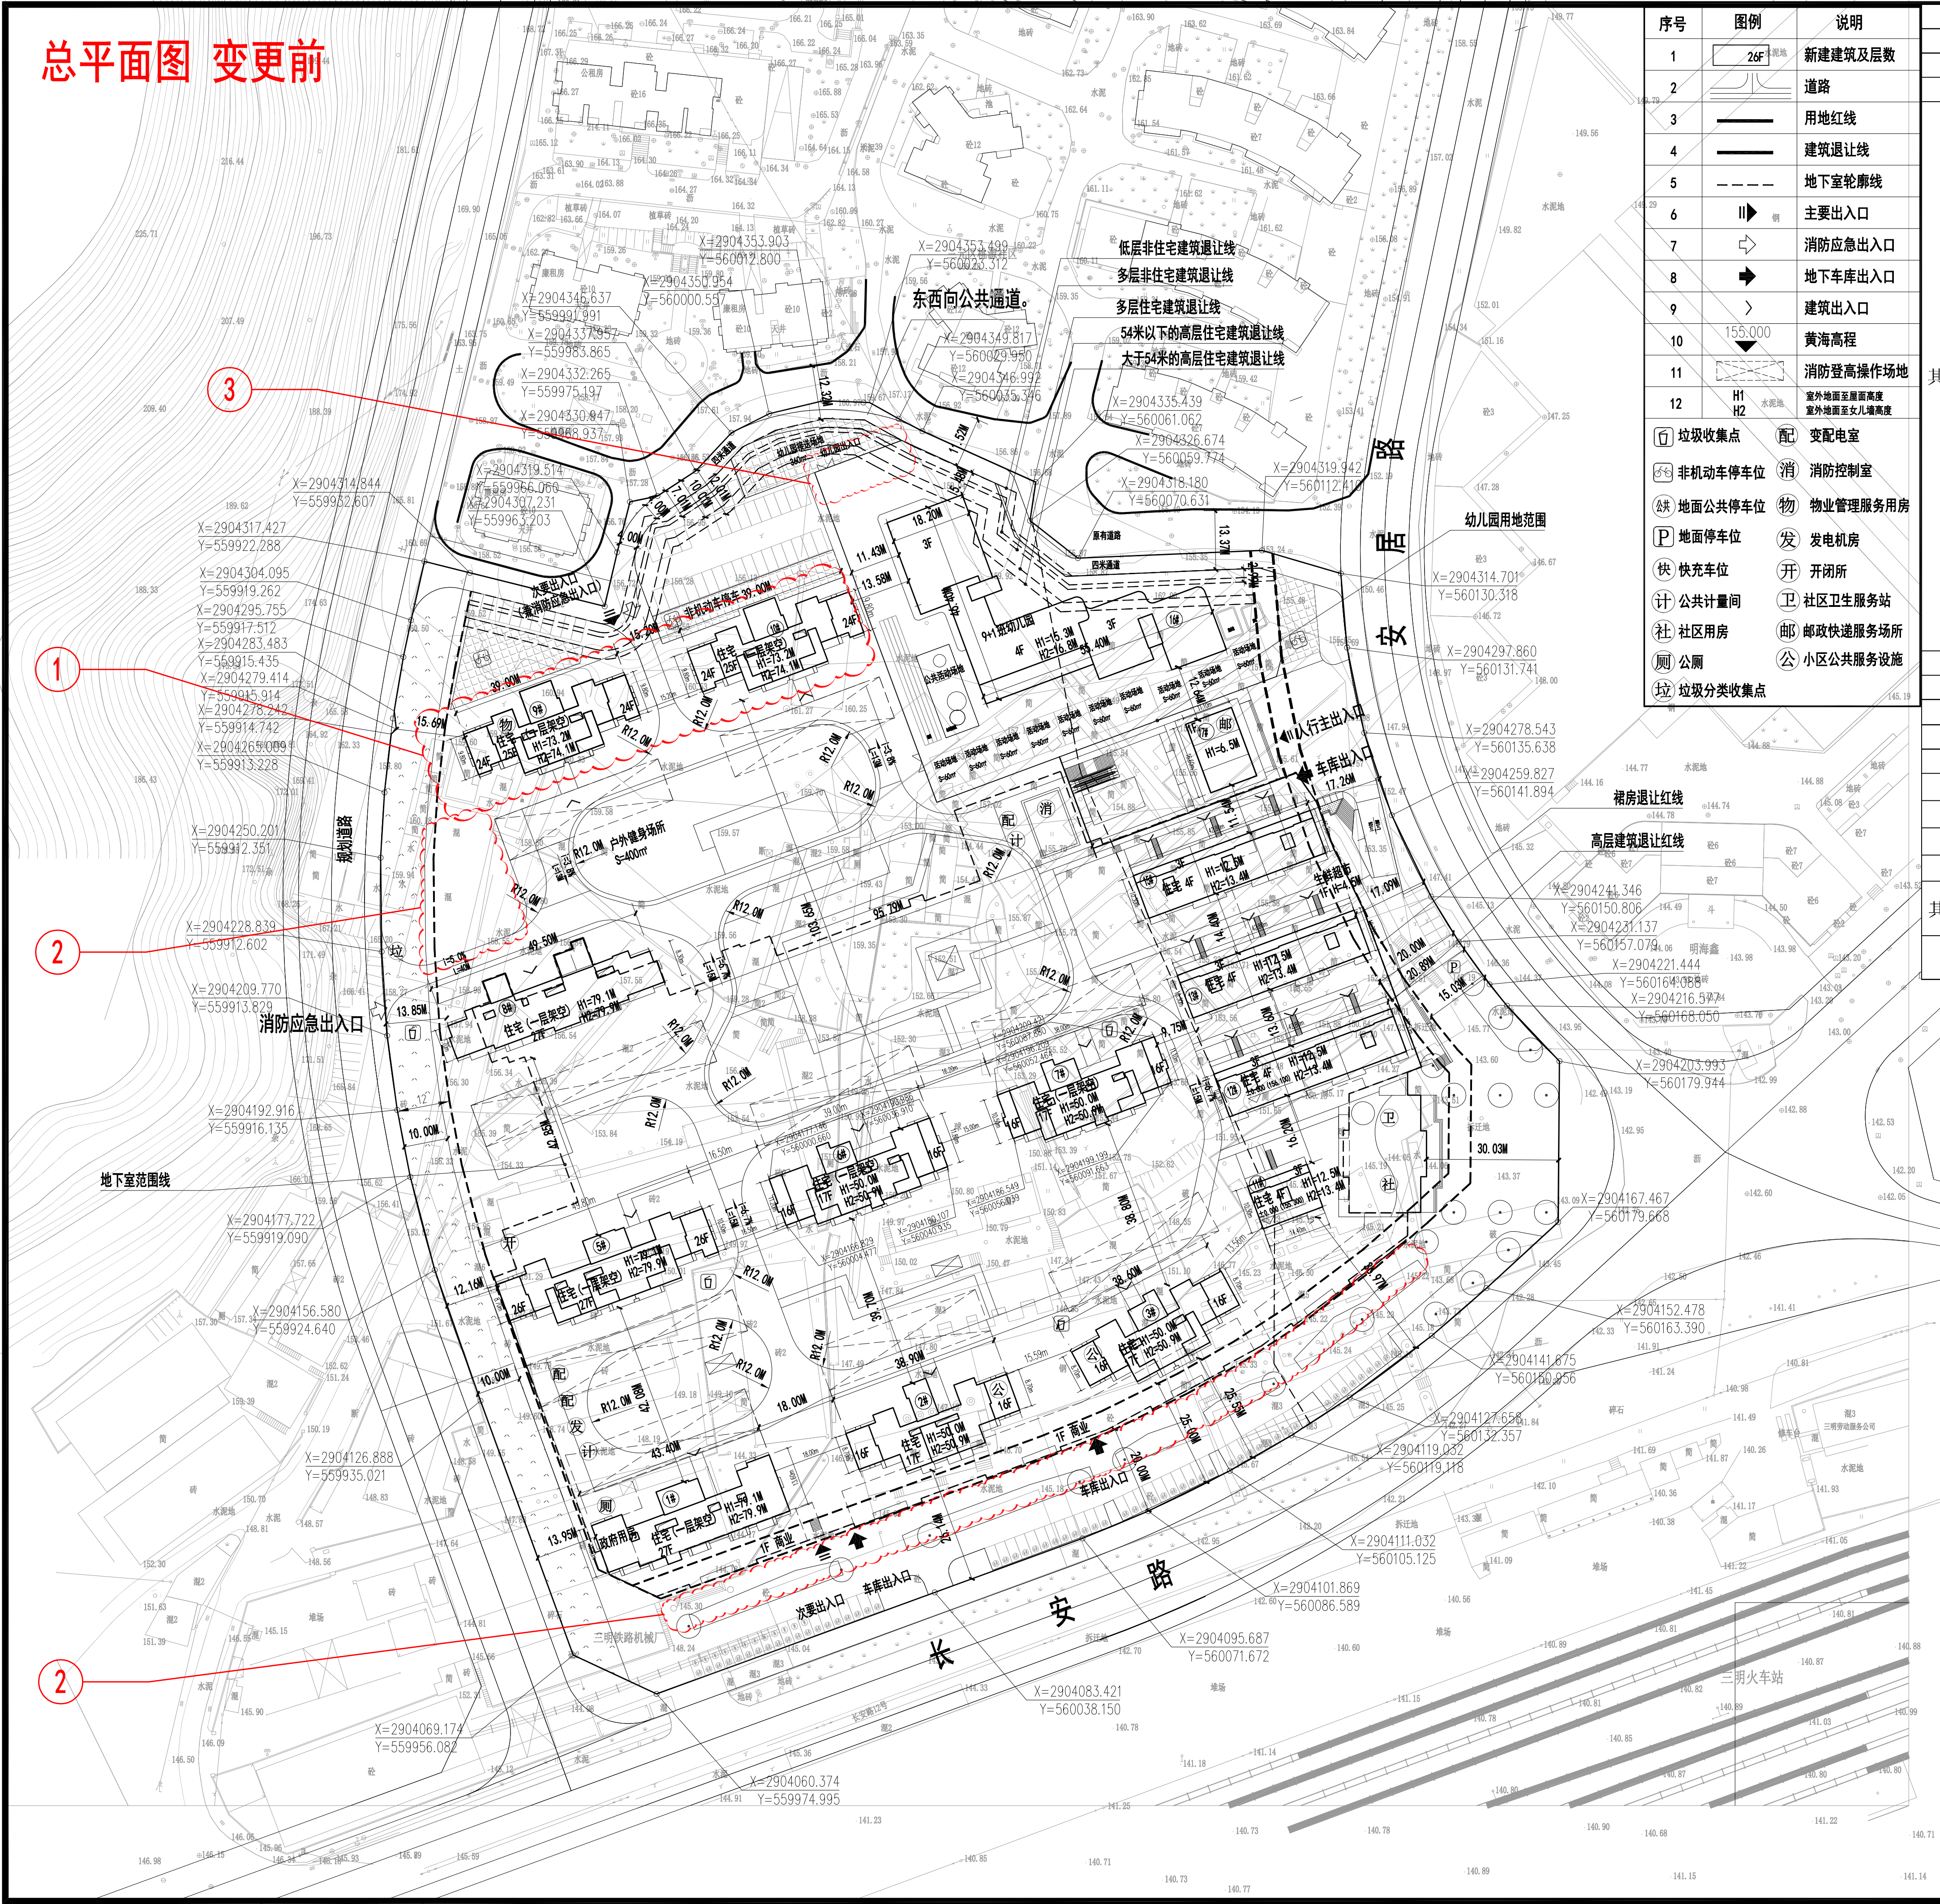

总平面图 变更后

变更内容:

- 1、9#10#楼位置向左移动, 层高增加, 建筑高度增加
- 2、增加地面非机动车停车位
- 3、增加幼儿园大门

序号	图例	说明
1		新建建筑及层数
2		道路
3		用地红线
4		建筑退让线
5		地下室轮廓线
6		主要出入口
7		消防应急出入口
8		地下车库出入口
9		建筑出入口
10		黄海高程
11		消防登高操作场地
12		室外地面至屋面高度 室外地面至女儿墙高度
	垃圾收集点	变配电室
	非机动车停车位	消防控制室
	地面公共停车位	物业管理服务用房
	地面停车位	发电机房
	快充车位	开闭所
	公共计量间	社区卫生服务站
	社区用房	邮政快递服务场所
	公厕	小区公共服务设施
	垃圾分类收集点	


项目		指标	单位	备注
用地红线规划面积		55026.77	m²	约82.54亩
总建筑面积		132944.9	m²	
其中	计容总建筑面积	104000.0	m²	
	住宅建筑面积	94900.6	m²	
	安置住宅	10000.0	m²	
	配建住宅	8300.0	m²	
	销售住宅	76600.6	m²	
	其中 高层住宅	69580.6	m²	
其中	叠拼住宅	7020.0	m²	
	商业建筑面积	3099.4	m²	其中1059.5m²为生鲜超市
	配套建筑面积	6000.0	m²	
	片区配套设施	5320.0	m²	
	幼儿园	4300.0	m²	
	社区用房	700.0	m²	
	社区卫生服务站	200.0	m²	
	公厕	120.0	m²	
	小区配套设施	680.0	m²	
	小区公共服务设施	400.0	m²	
	邮政快递服务场所	60.0	m²	
	垃圾分类收集点	10.0	m²	场地面积
其中	物业管理用房	220.00	m²	
	不计容总建筑面积	28944.90	m²	
其中	住宅架空层	3400.00	m²	
	地下室	25544.90	m²	
户外健身休息场所		400.00	m²	场地面积
建筑占地面积		12656.16	m²	
建筑密度		23.00%		规划要求≤23%
容积率		1.8900		1<FAR<1.9
绿地面积		16508.03	m²	
绿地率		30.00%		规划要求≥30%
户数		875	户	
住宅人口		2800	人	3.2人/户
规划机动车停车位		1144	辆	1.1位/100m²计容面积
其中	地面停车	114	辆	其中快充车位为12位
	地下停车	1030	辆	其中慢冲车位为217位
规划非机动车停车场		2080	m²	2m²停车面积/100m²计容面积

3

1


2

2

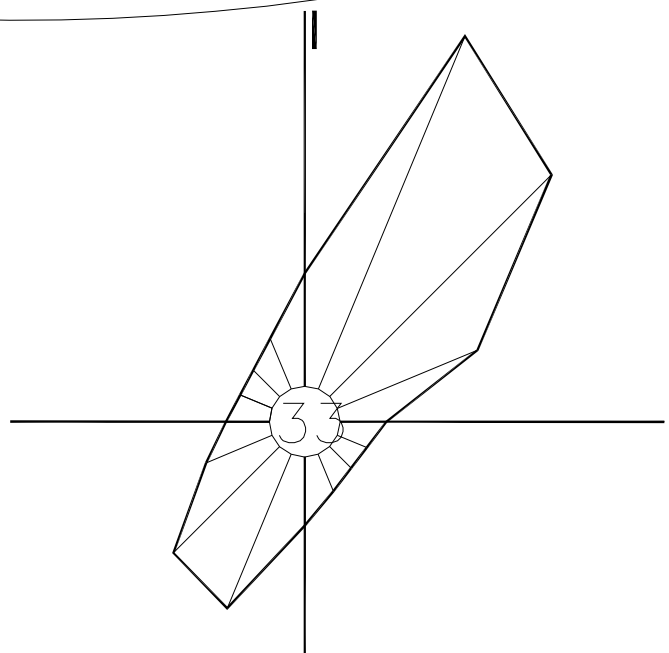


总平面图


8#楼屋面层平面图 变更前

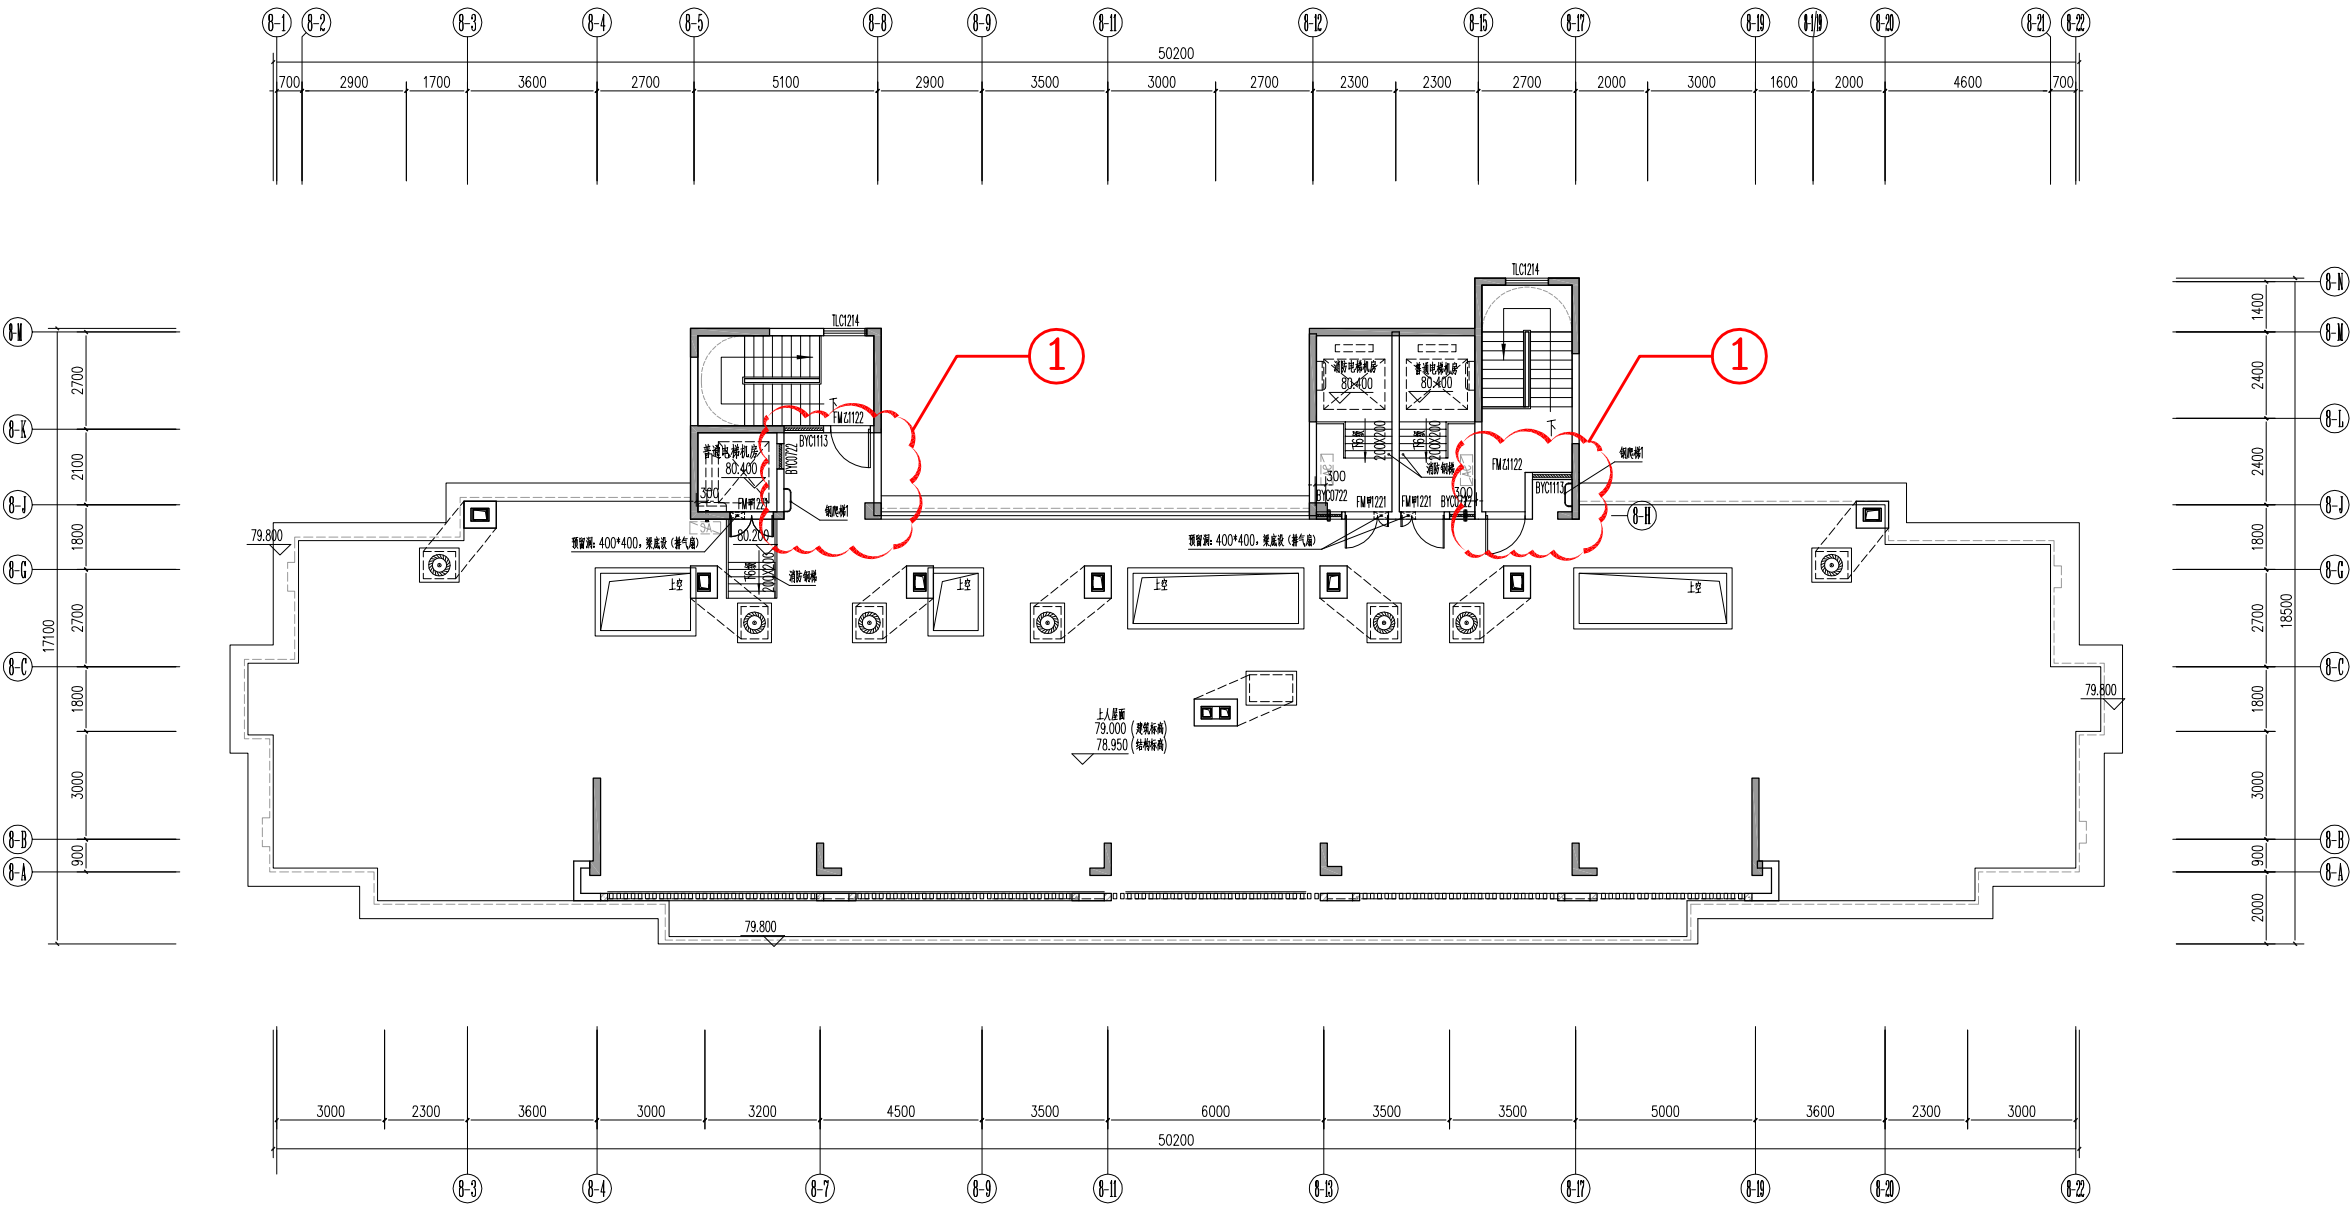


8#楼屋面层平面图 1:200

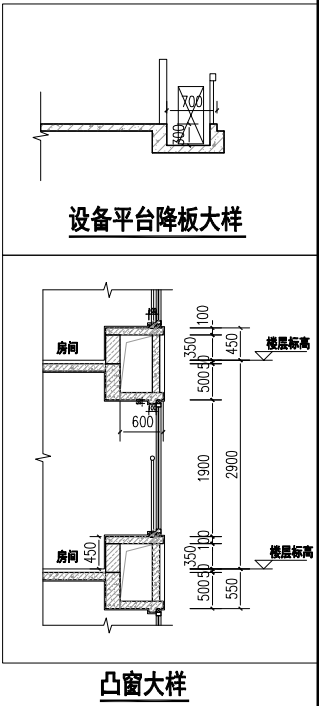

8#楼屋架层平面图 变更前

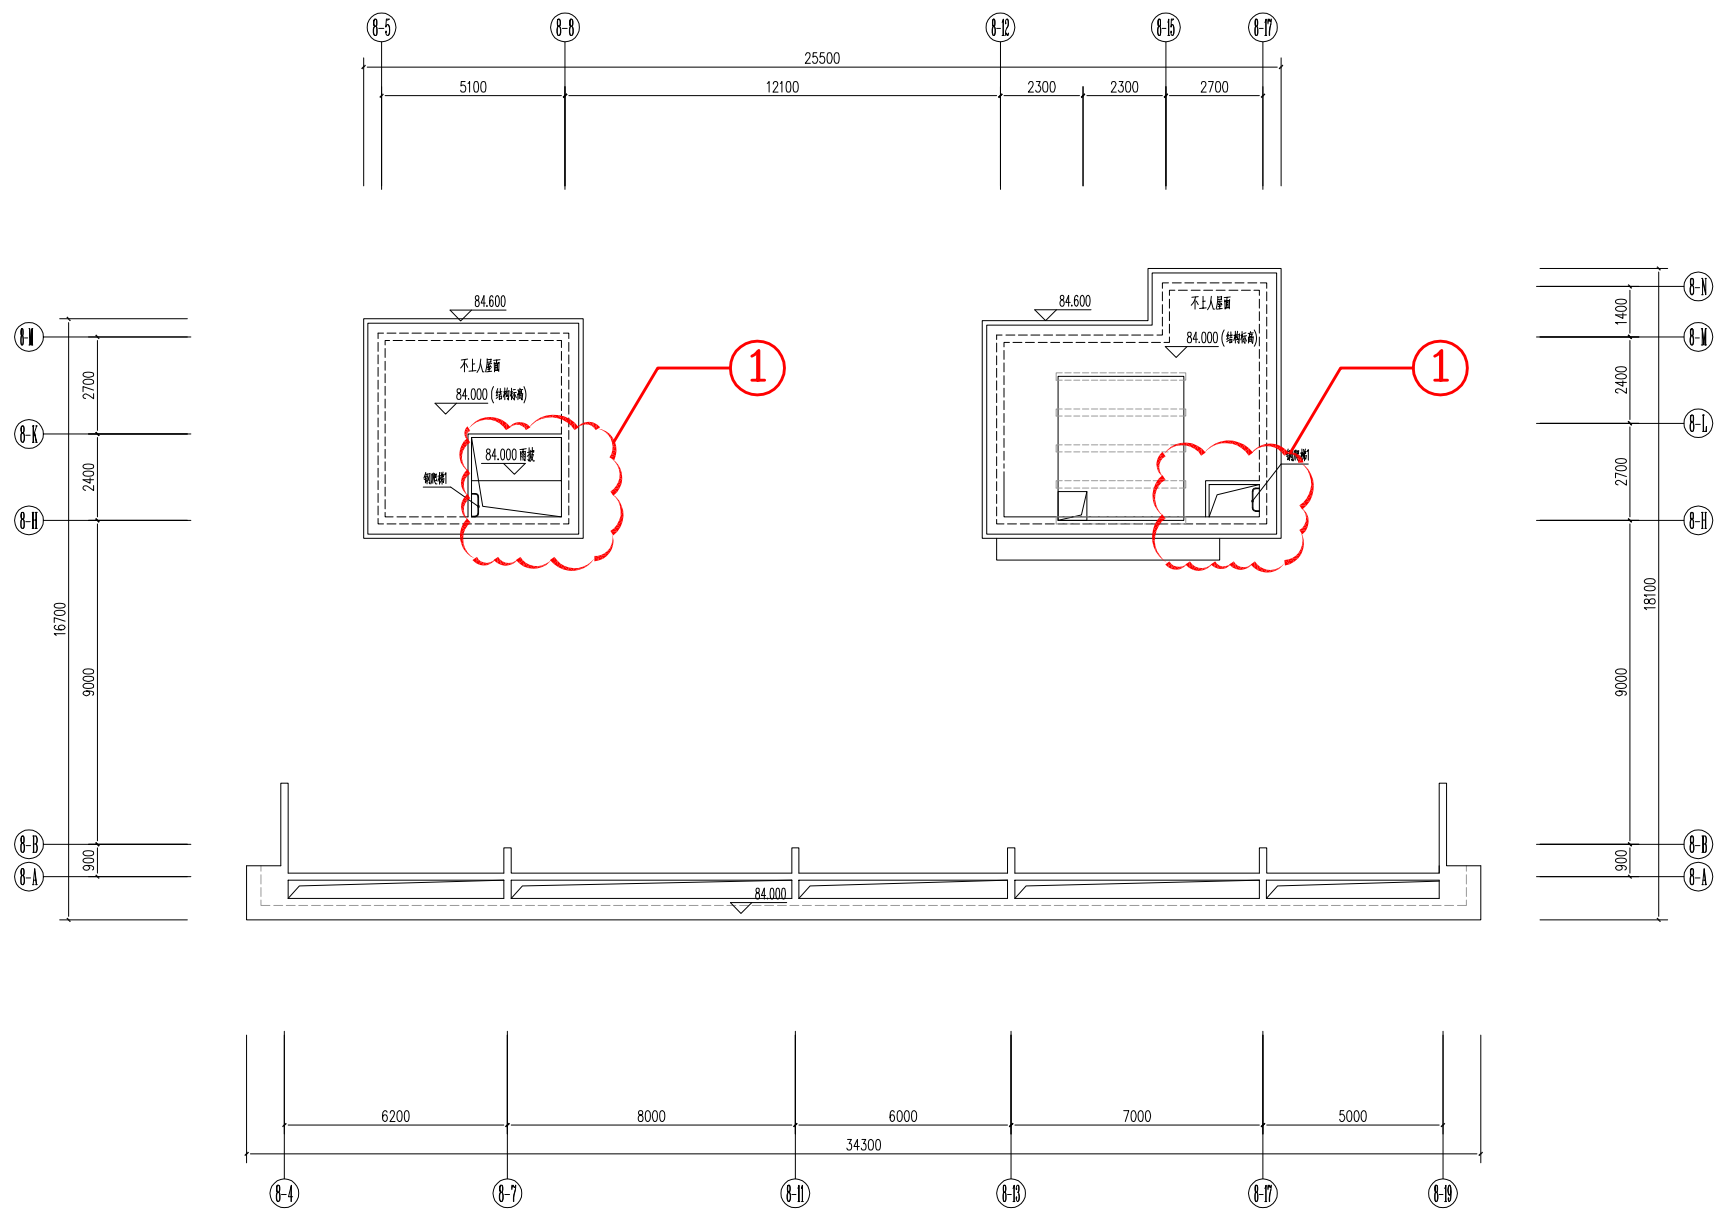


8#楼屋面层平面图 1:200

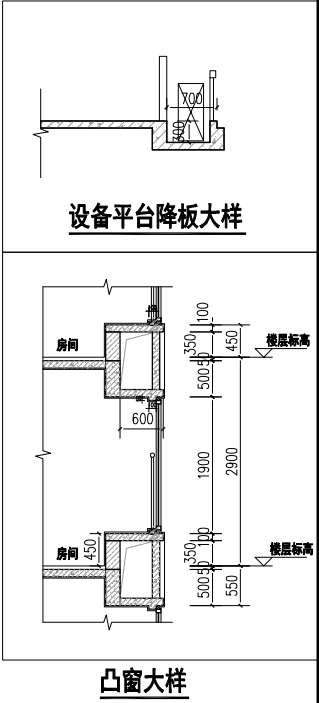


8#楼屋面层平面图 变更后


变更内容：
1、屋面楼梯间扩大。

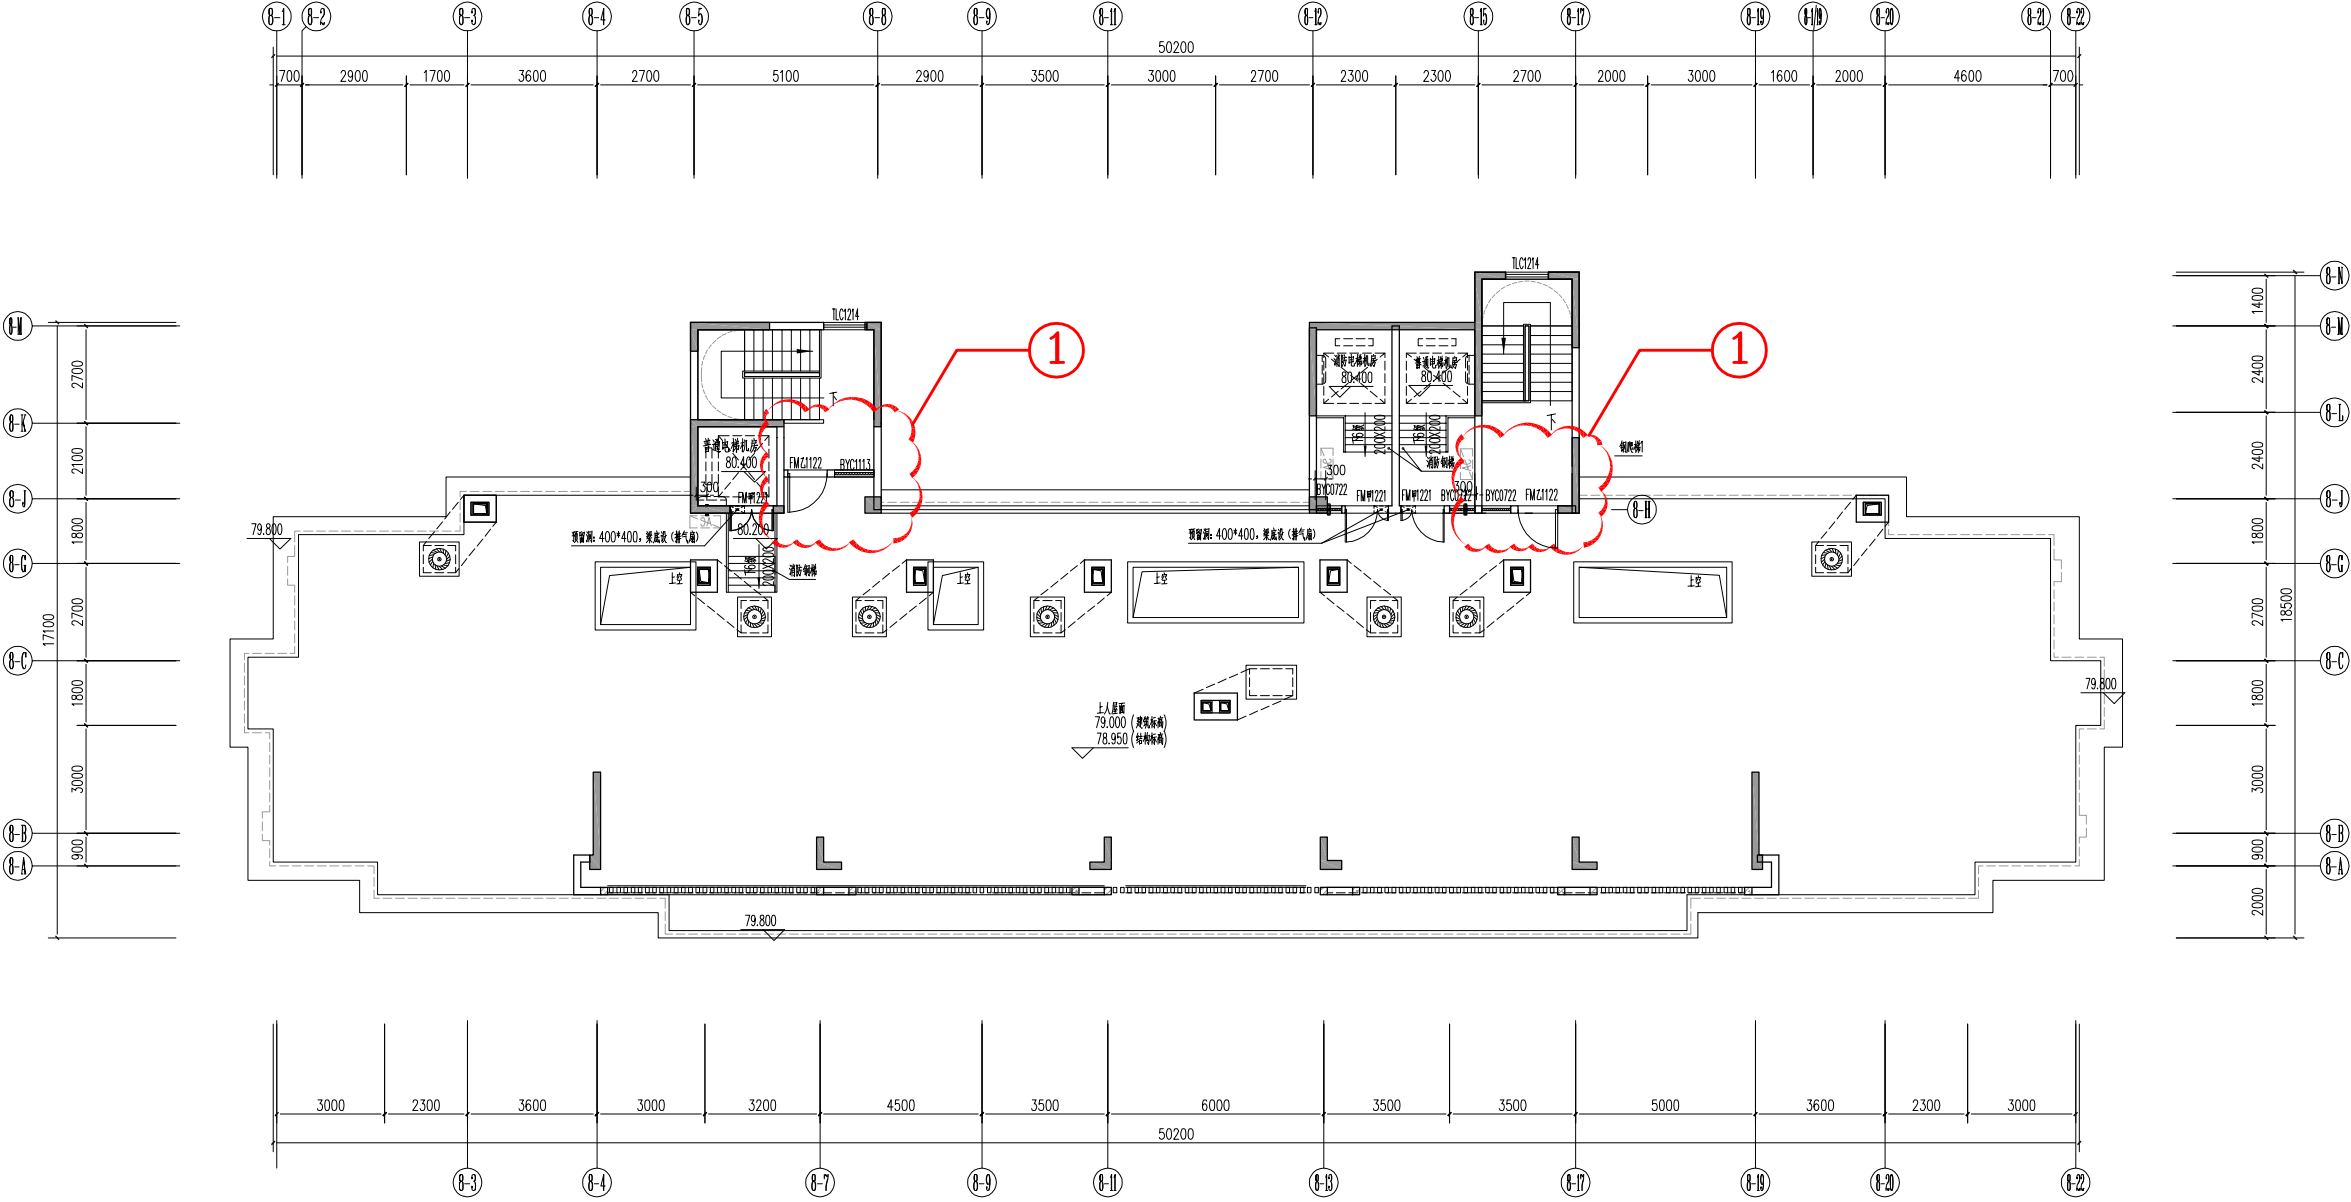

8#楼屋面层平面图 1:200

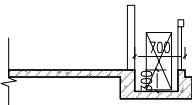

设备平台降板大样

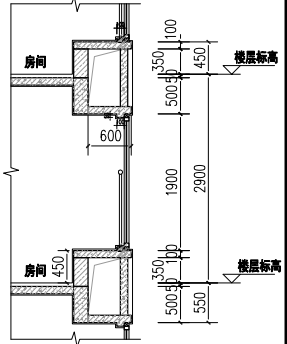


凸窗大样


8#楼屋架层平面图 变更后

变更内容:



1、屋面楼梯间屋面板扩大。

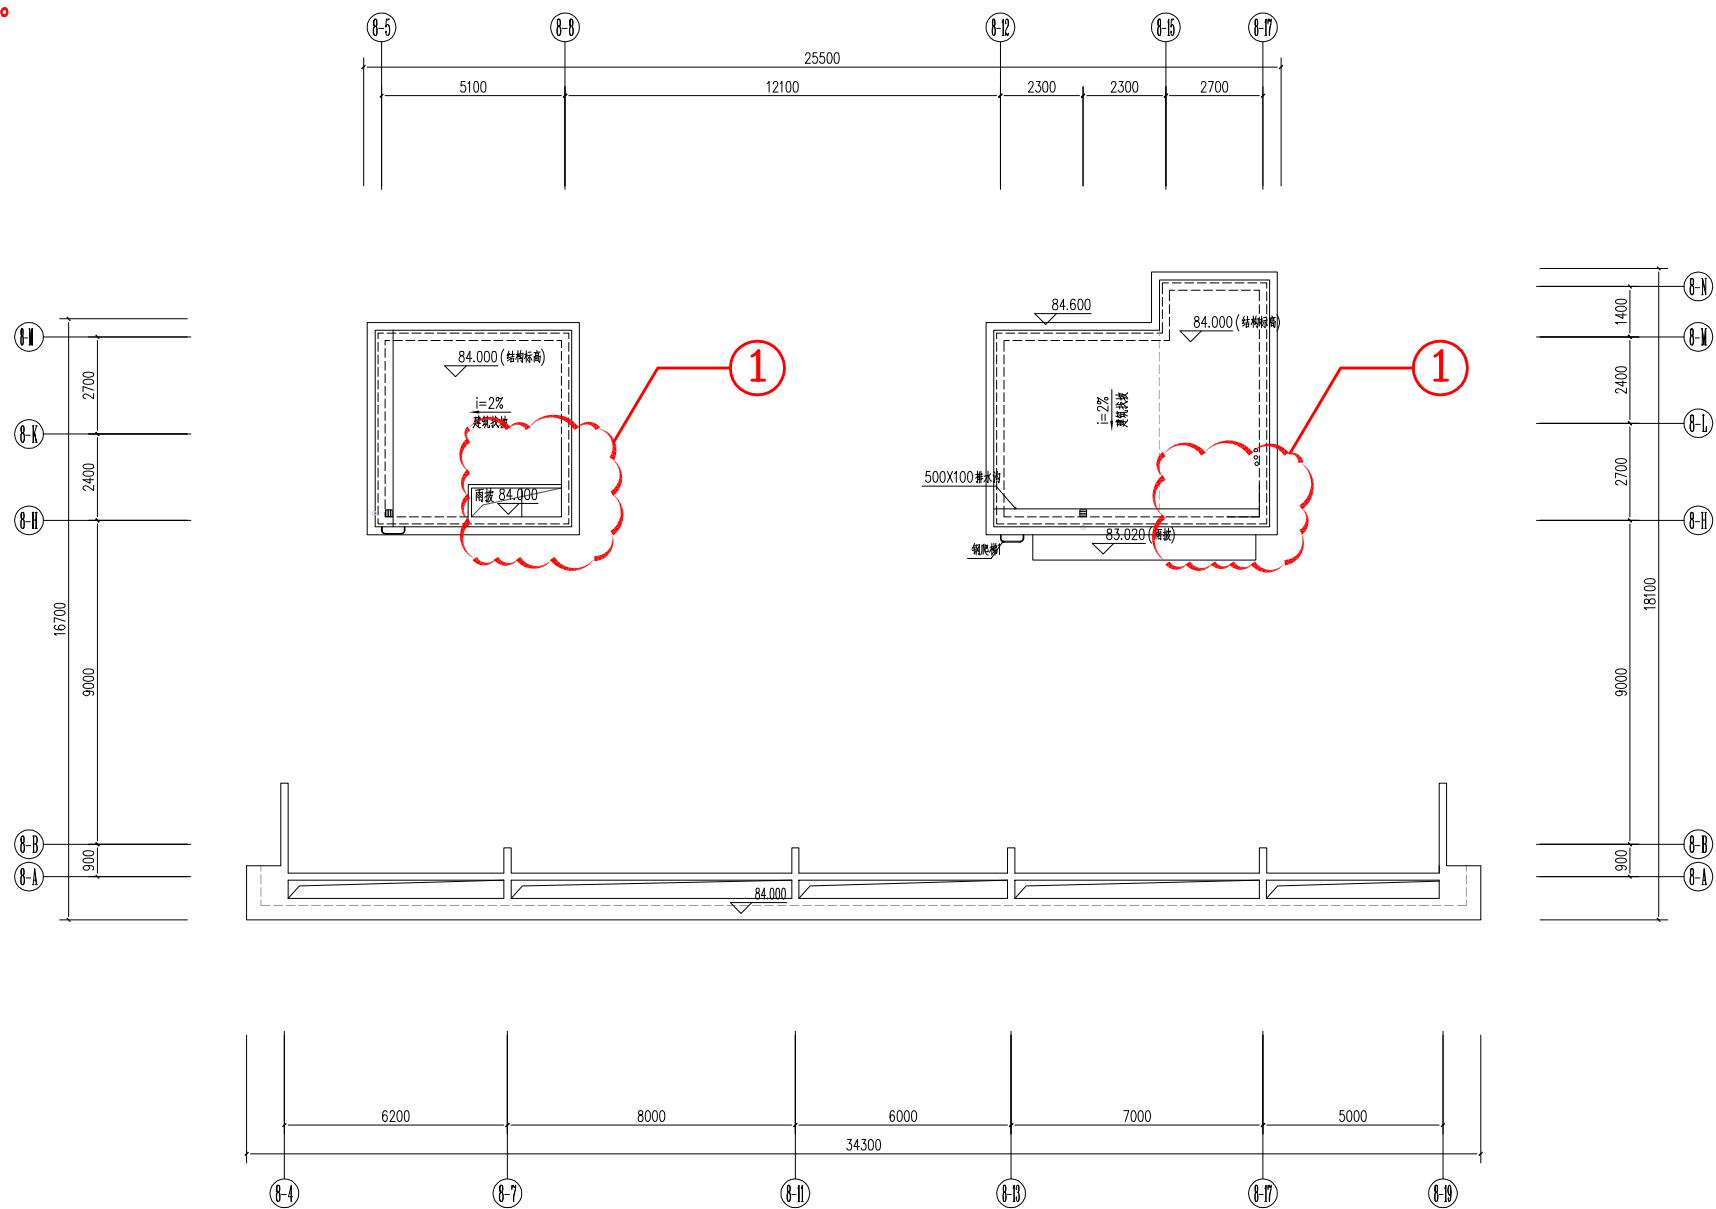

8#楼屋面层平面图 1:200

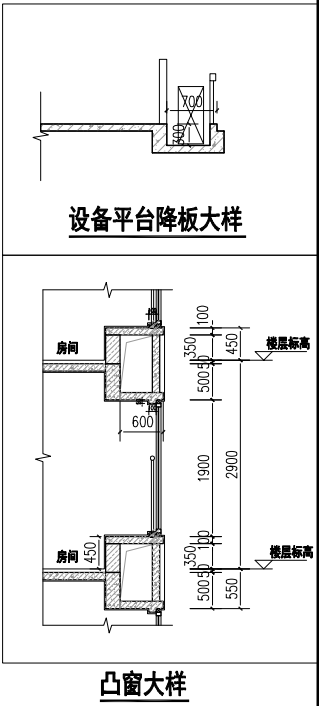



9#楼一层平面图 变更前

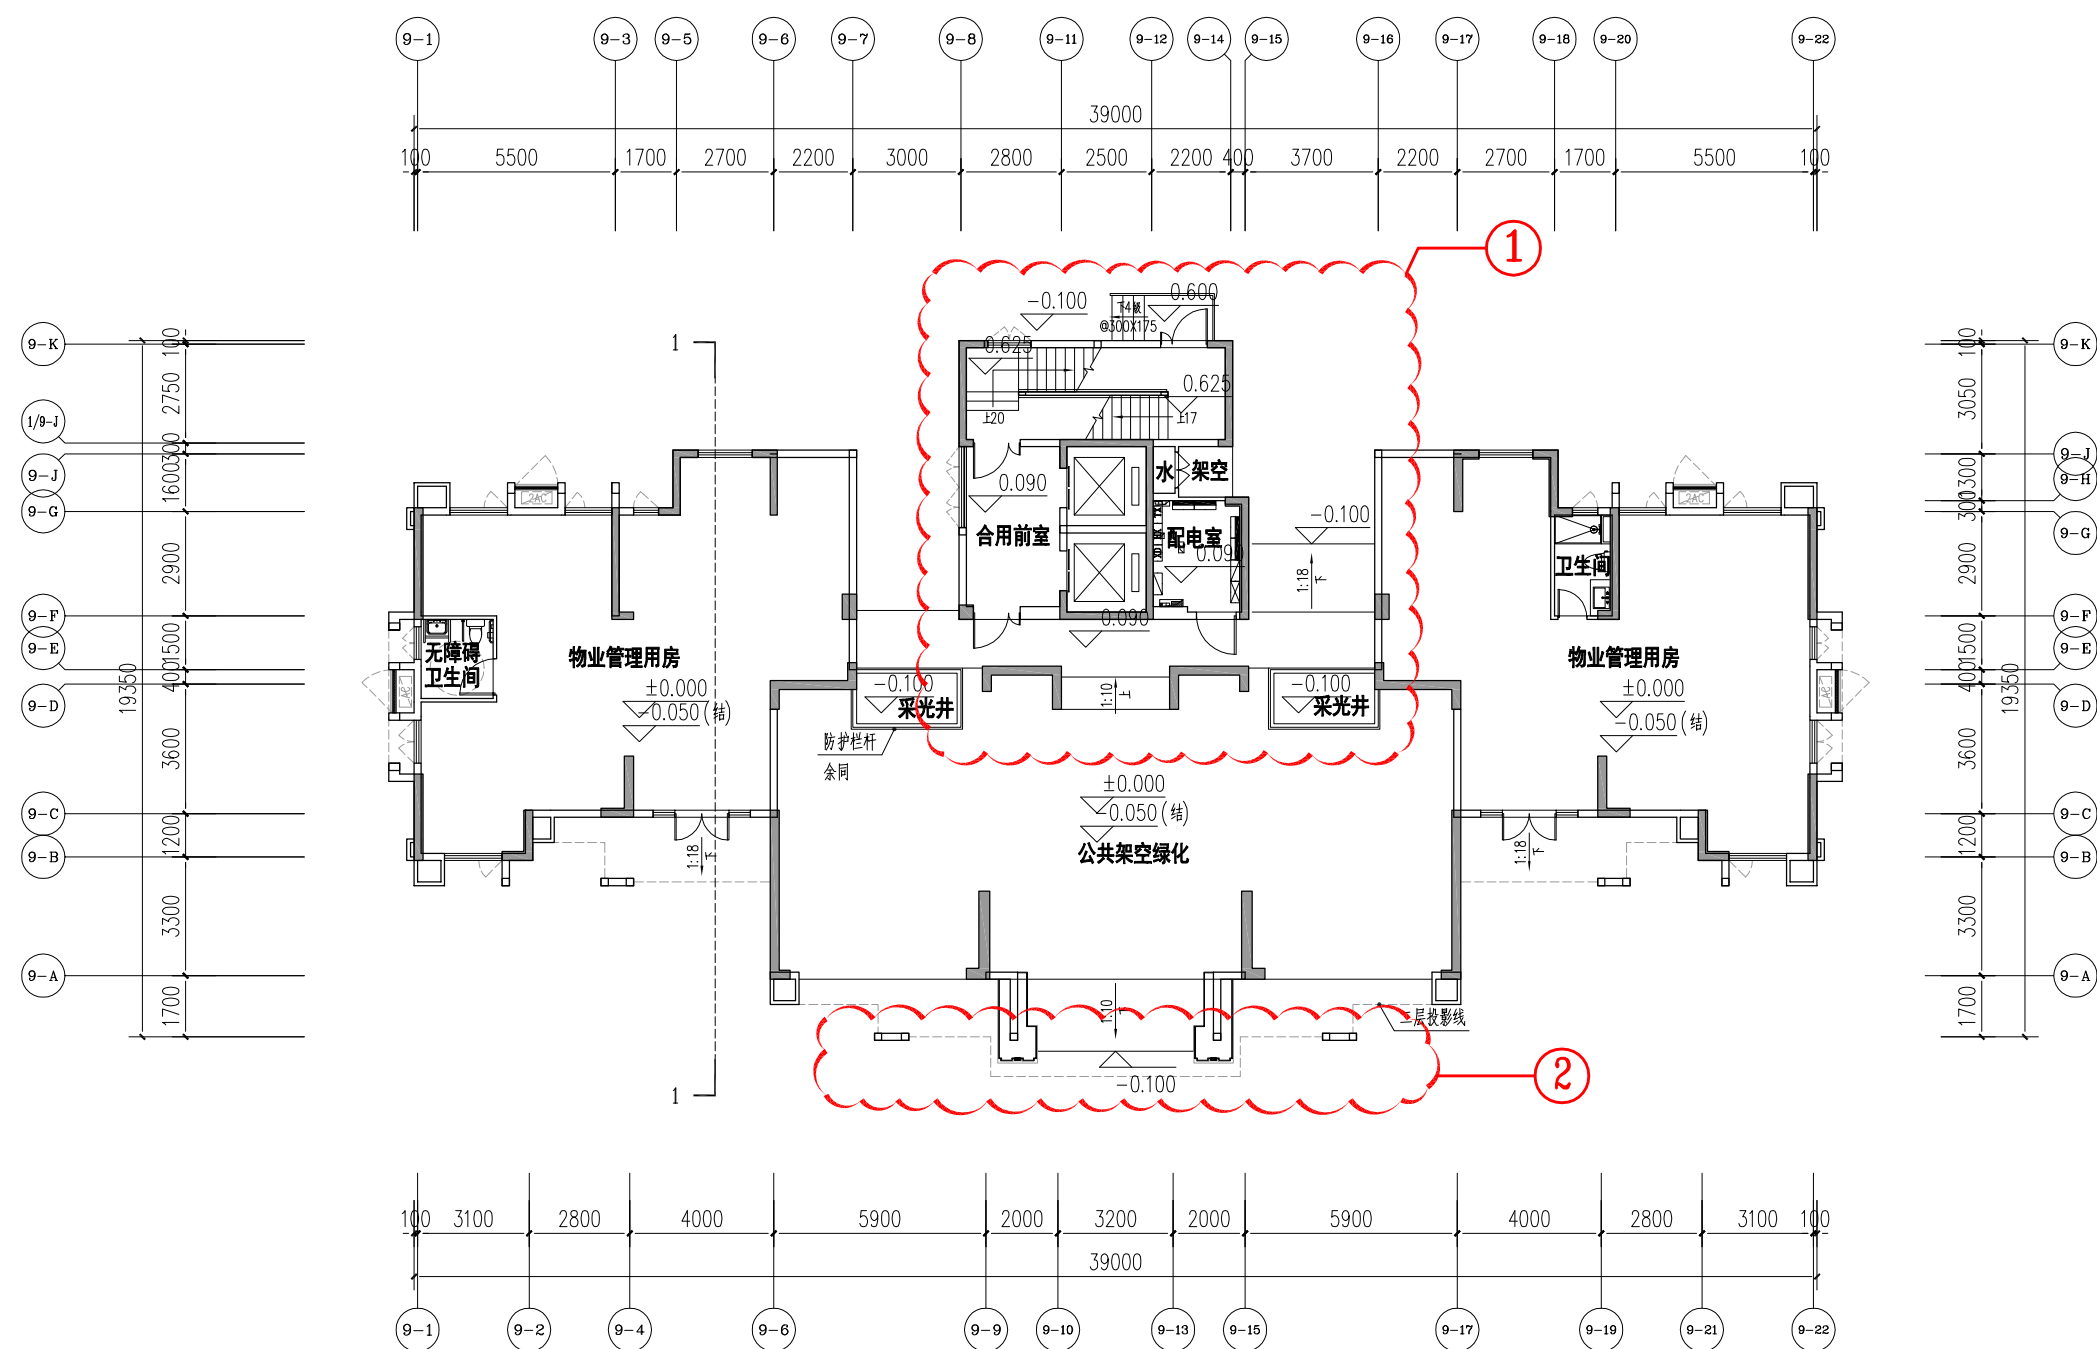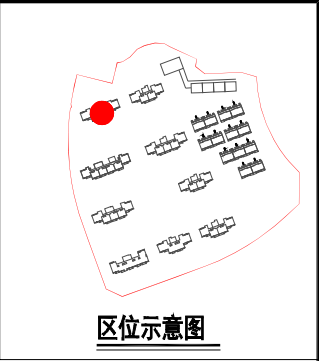

9#楼一层平面图 1:200 ±0.000(158.00)

本栋计容面积: 10630.70m²
本层计容面积: 280.67m²
其中: 住宅面积: 60.43m²
物业管理用房面积: 220.24m²
本层不计容架空面积: 184.25m²


9#楼二层平面图 变更前

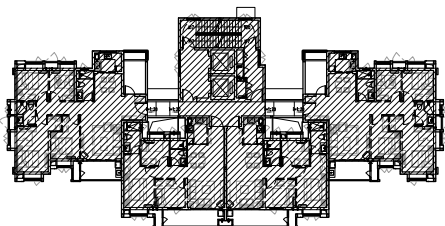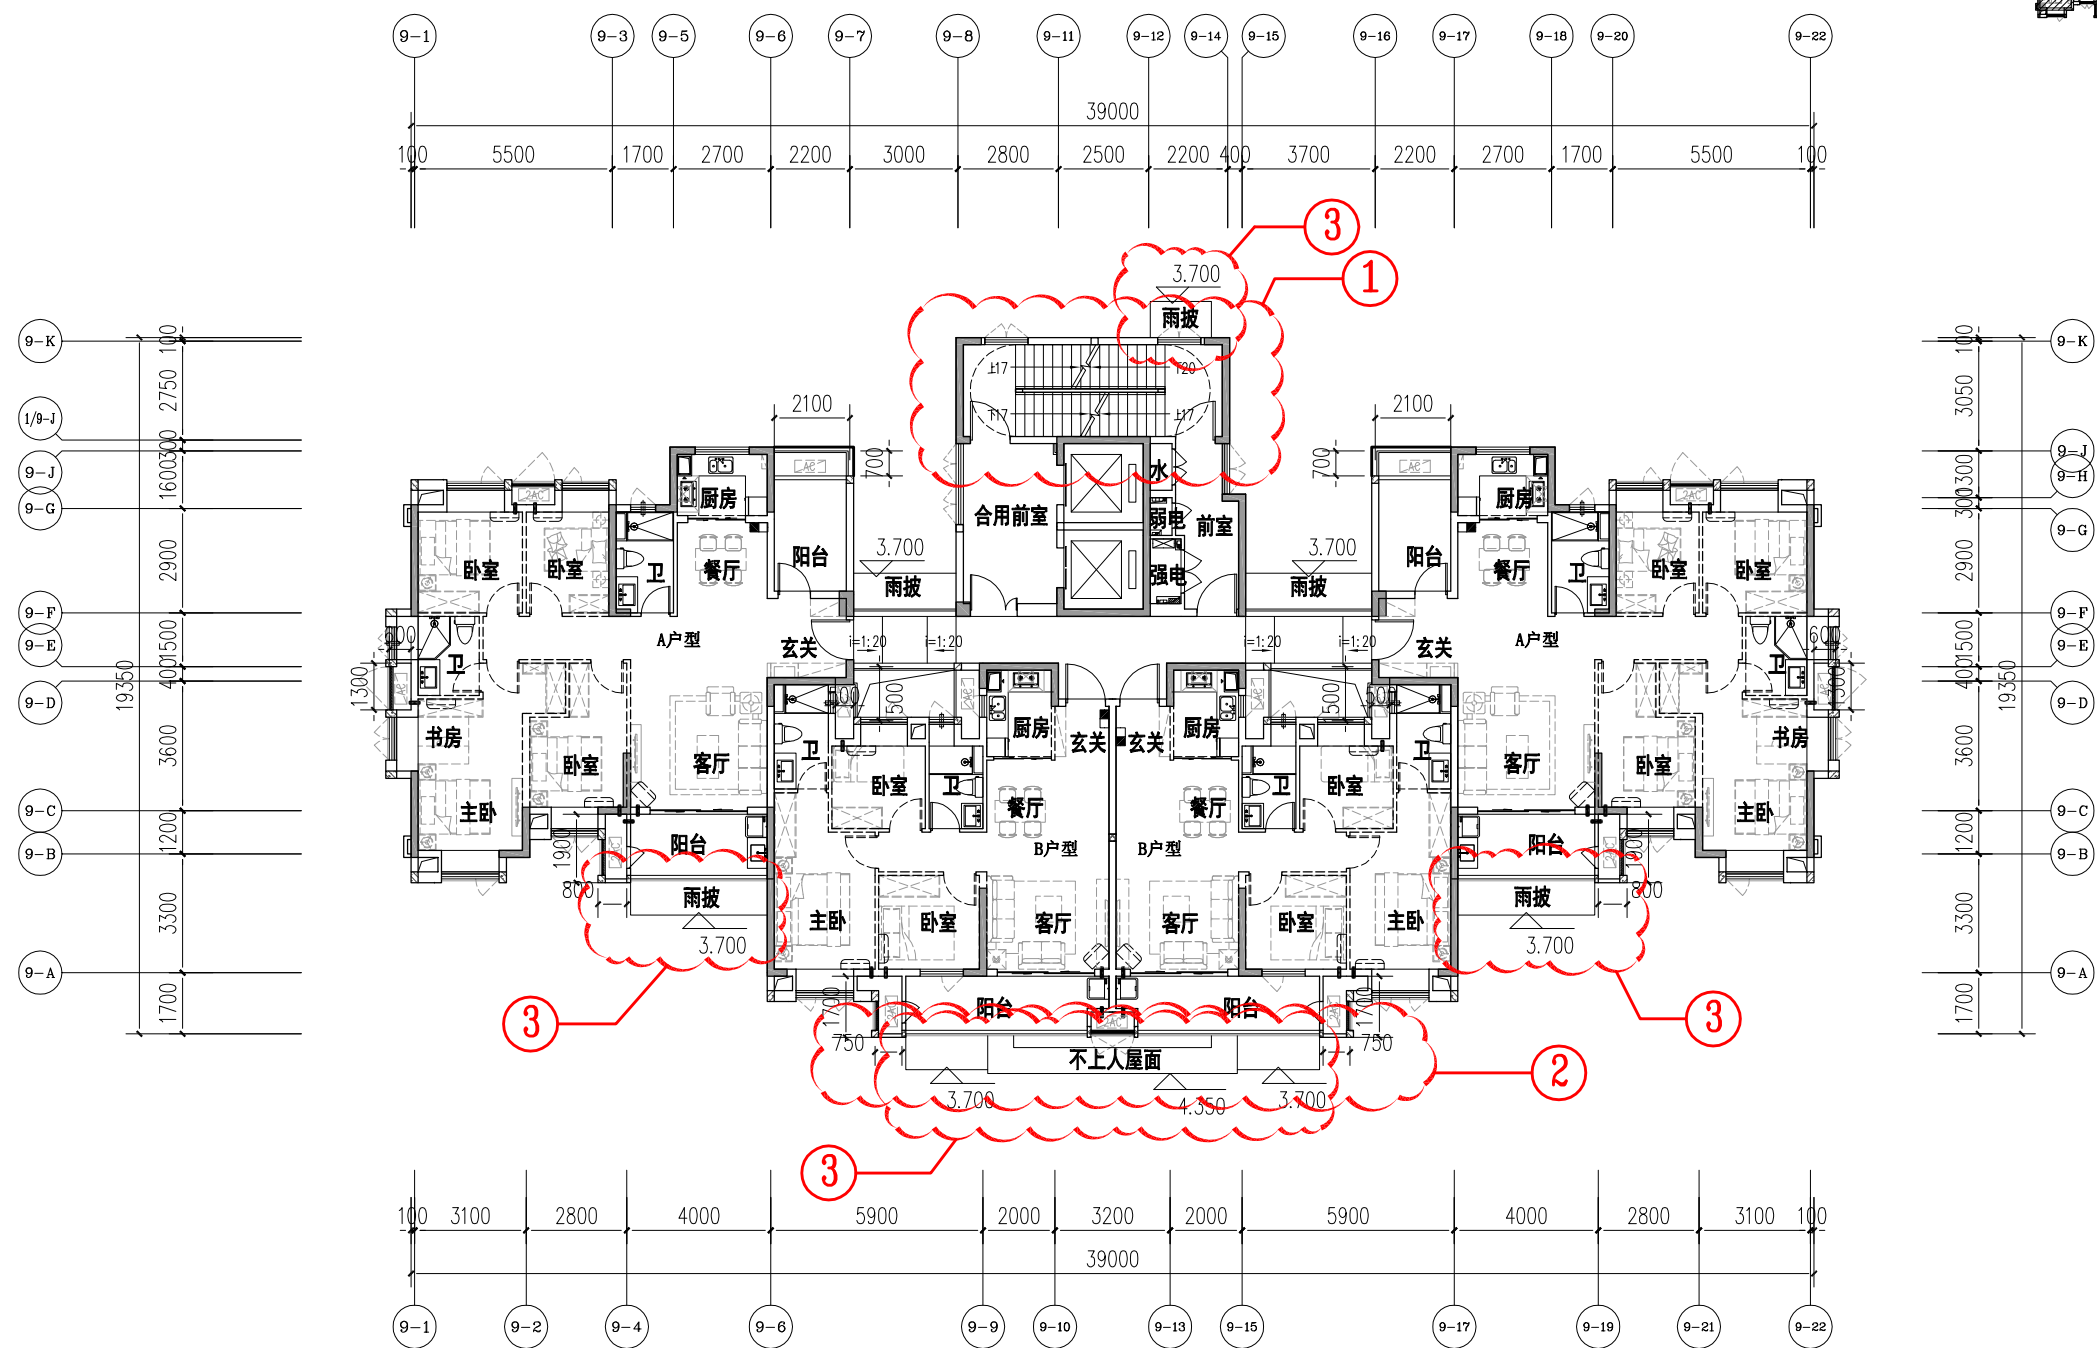

9#楼结构走向示意图

9#楼二层平面图 1:200

3.600

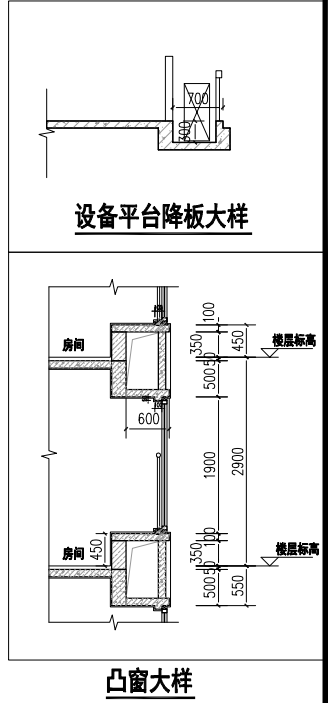


设备平台降板大样

凸窗大样


户型编号	户型	户型面积	户内面积	阳台水平投影面积	阳台面积	套内面积 (阳台+户内)	阳台占套内投影面积比例 (不含套内阳台)	公摊面积	公摊率	本层面积 (计容)
A	4房2厅2卫	128.39	98.01	14.00	7.00	105.01	14.28%	23.38	18.21%	446.12
B	3房2厅2卫	90.23	69.22	9.16	4.58	73.80	13.23%	16.43	18.21%	

9#楼三、四层平面图 变更前

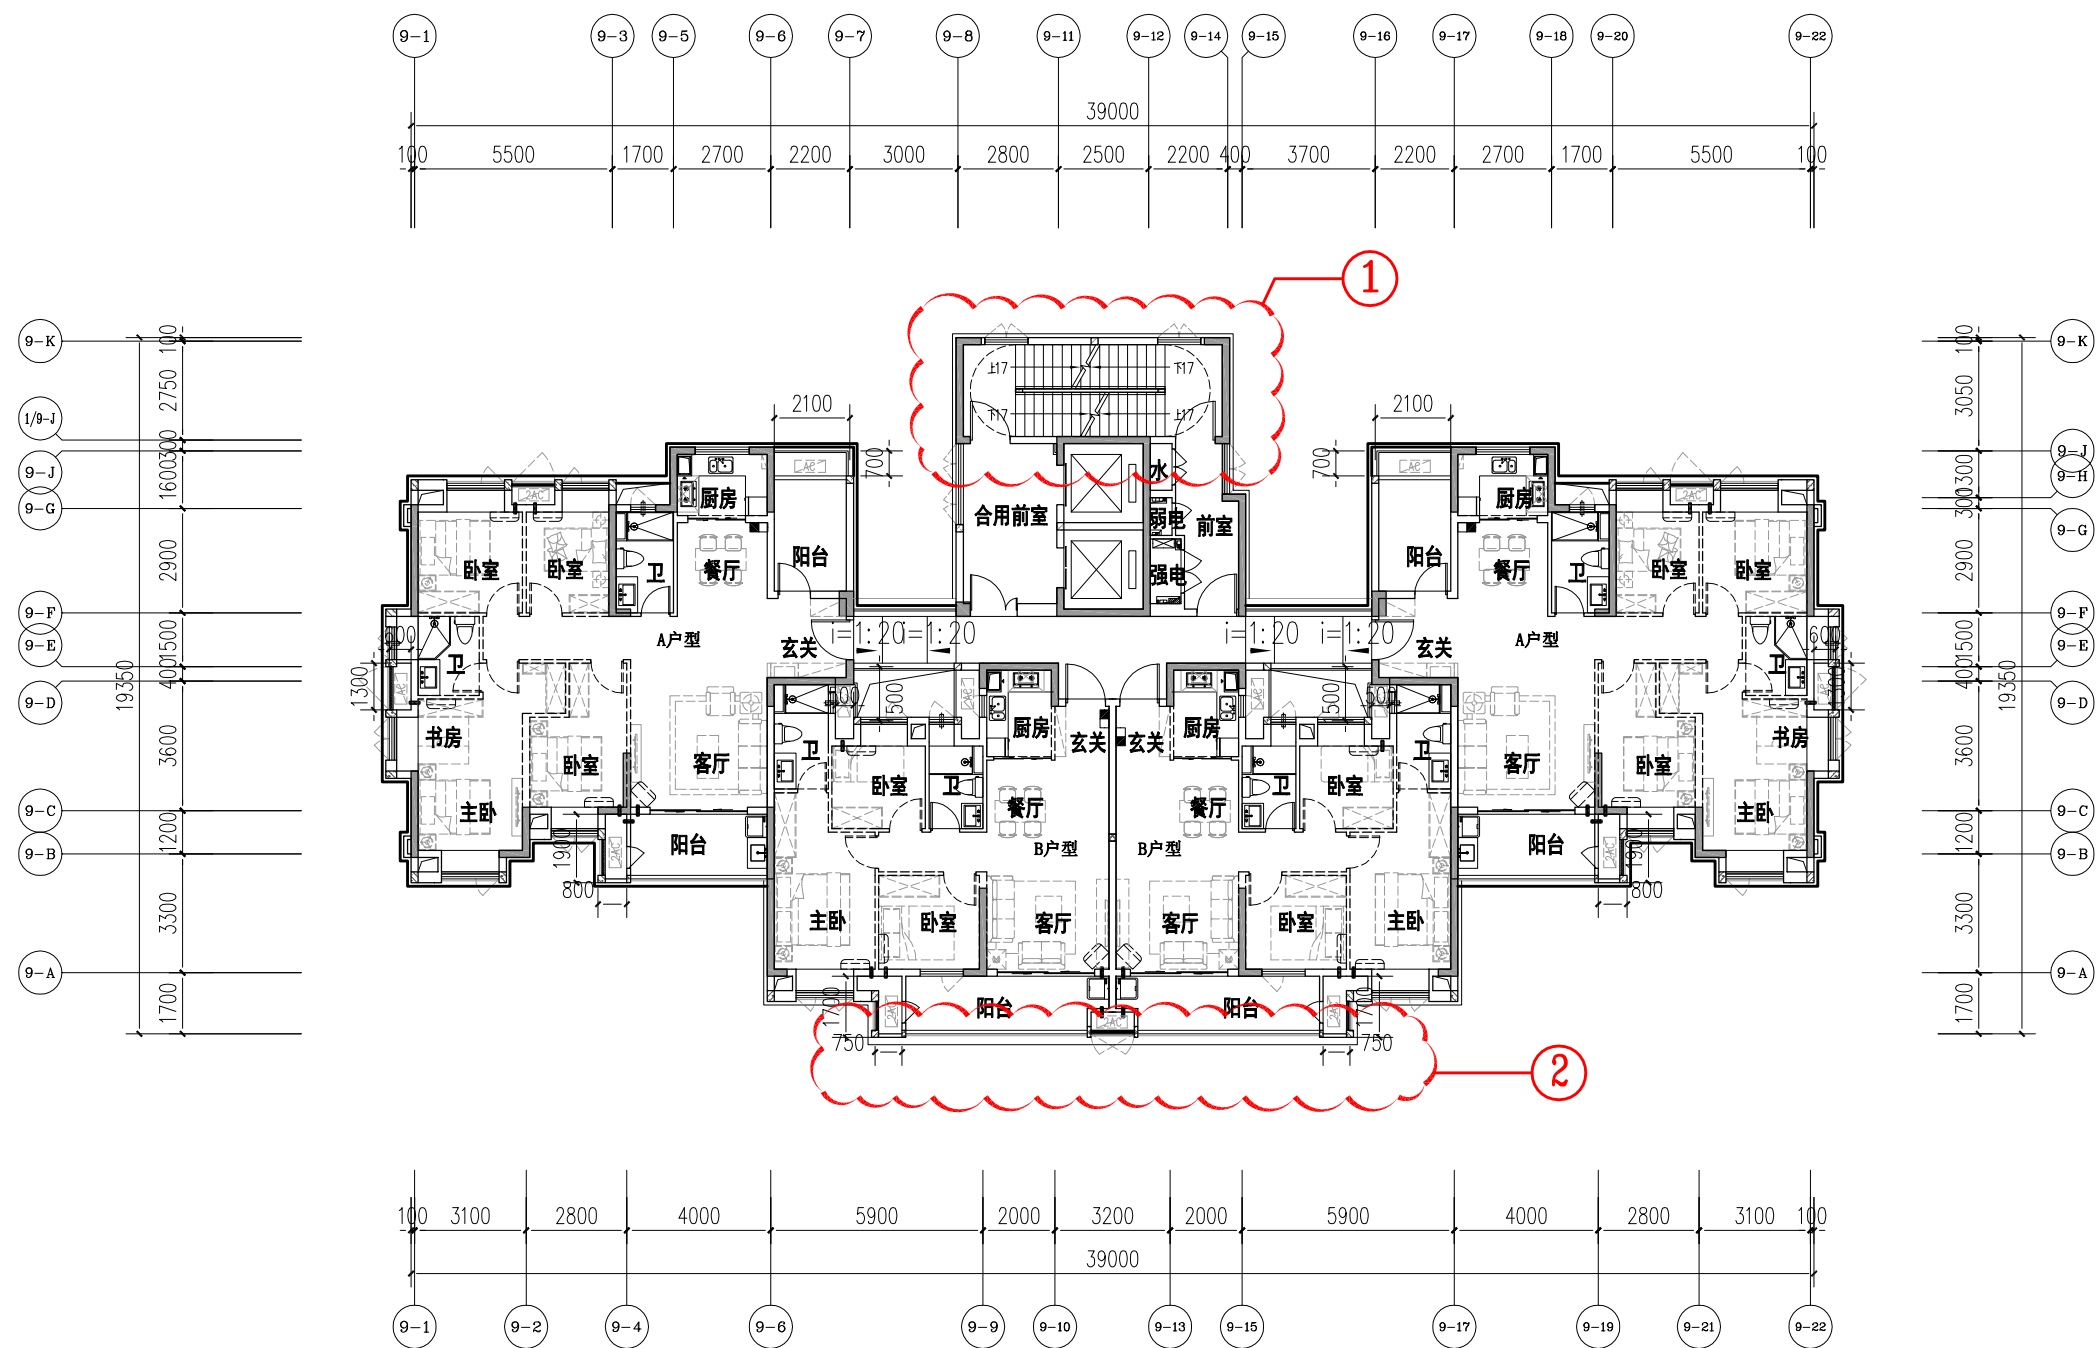


9#楼三、四层平面图 1:200

(9.400) 4F
6.500 3F

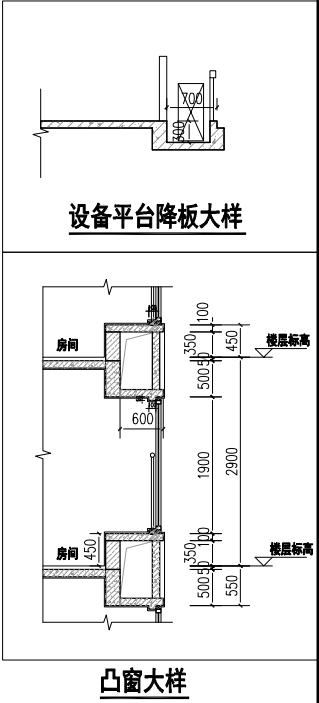

户型编号	户型	户型面积	户内面积	阳台水平投影面积	阳台面积	套内面积 (阳台+户内)	阳台占套内投影面积比例 (不含套内阳台)	公摊面积	公摊率	本层面积 (计容)
A	4房2厅2卫	128.39	98.01	14.00	7.00	105.01	14.28%	23.38	18.21%	446.12
B	3房2厅2卫	90.23	69.22	9.16	4.58	73.80	13.23%	16.43	18.21%	


9#楼五至二十三层平面图 变更前

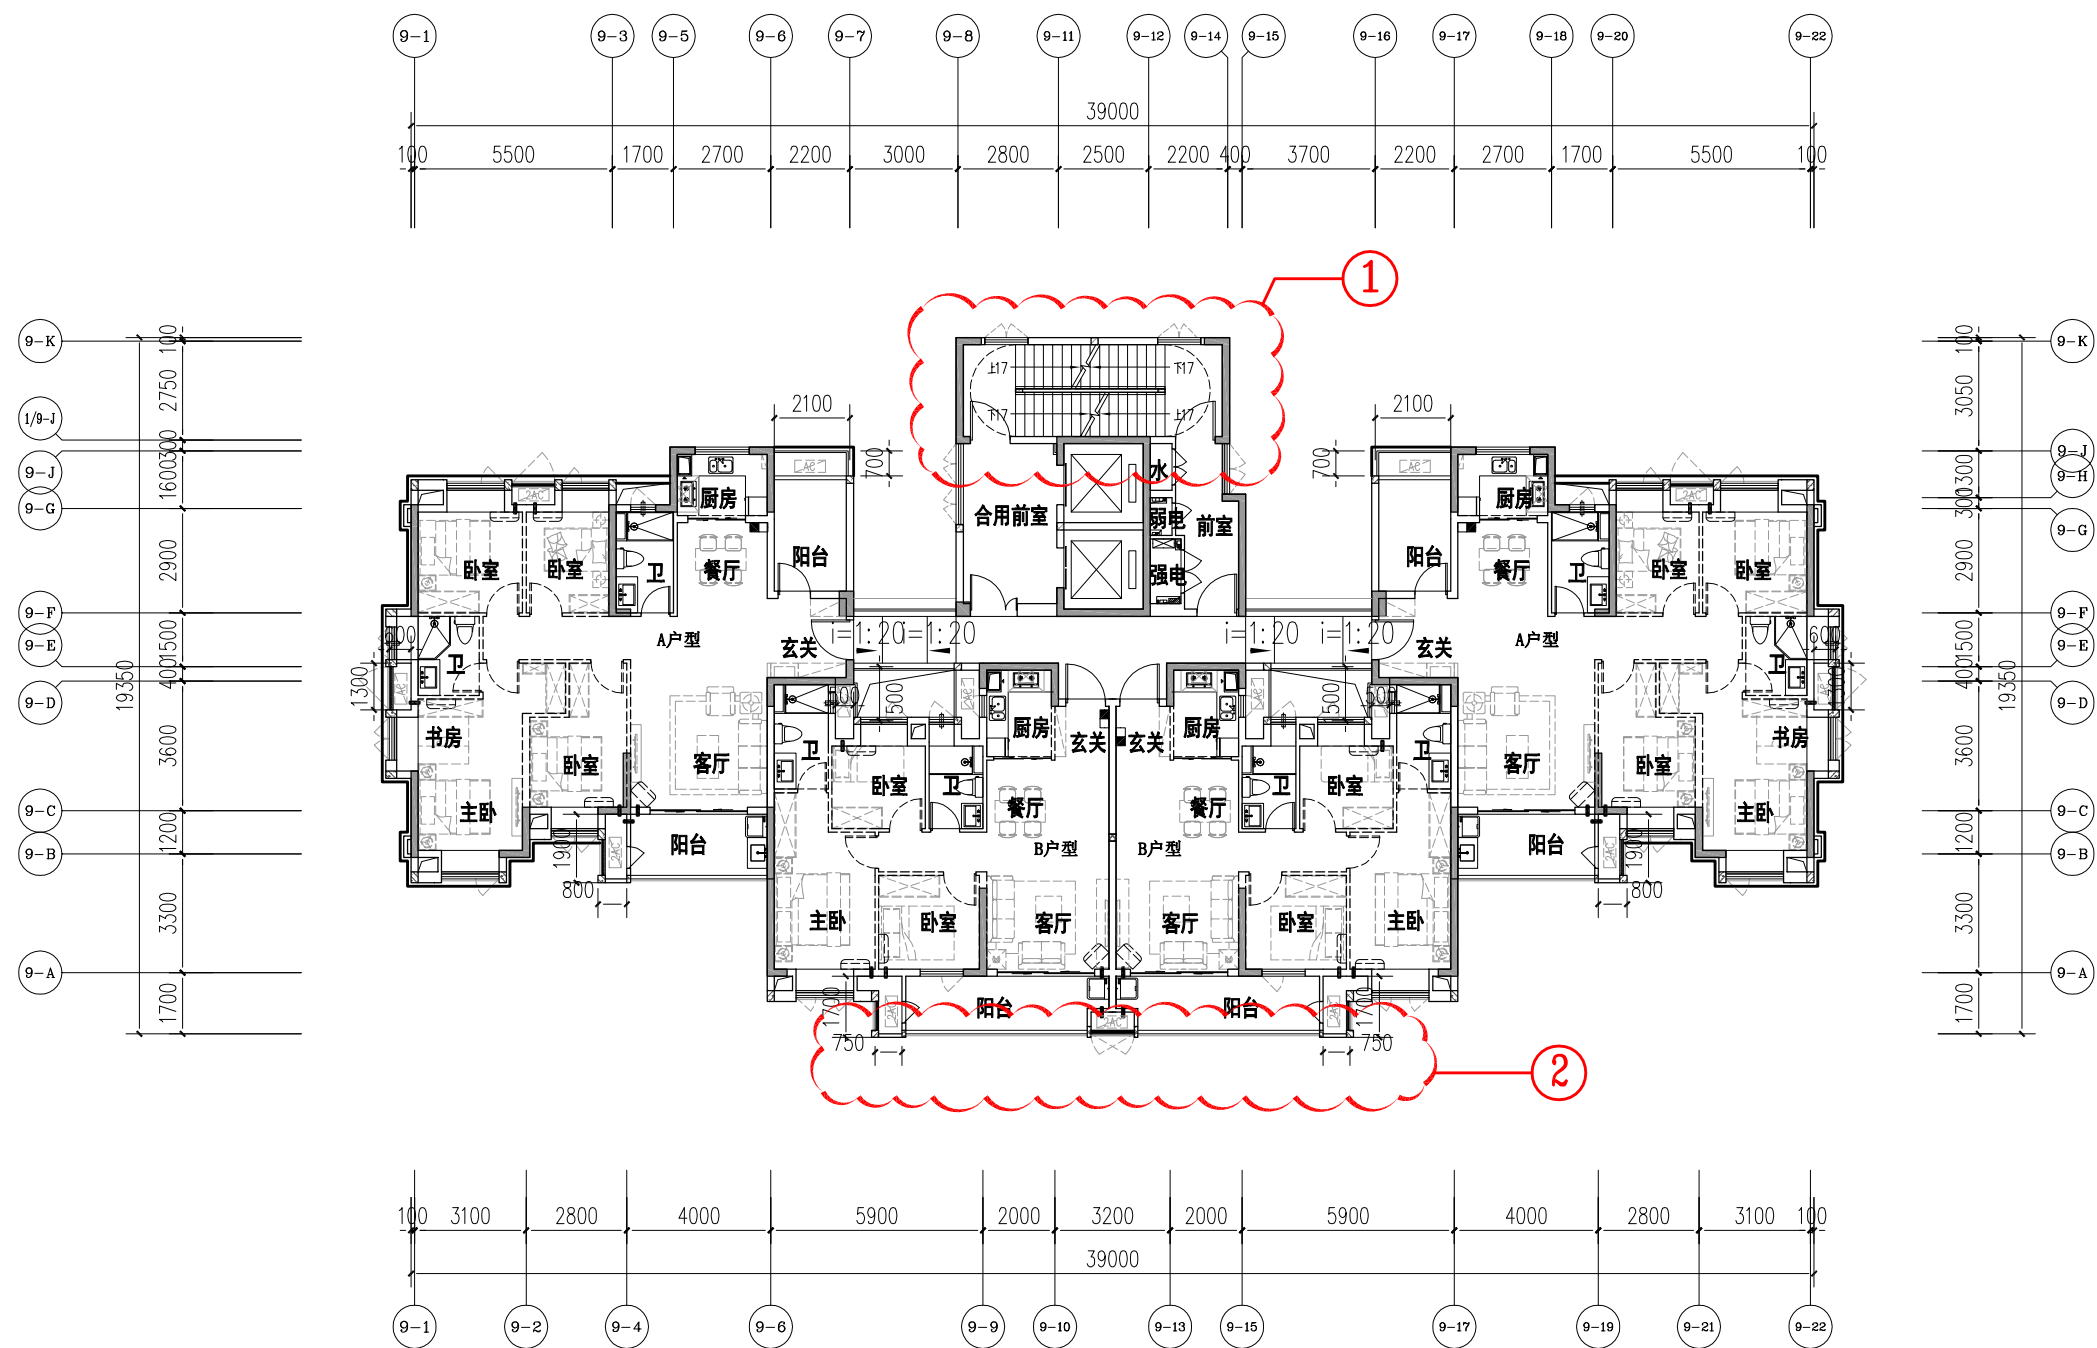


9#楼五至二十三层平面图 1:200

64.500 (23F)
~
12.300 (5F)


户型编号	户型	户型面积	户内面积	阳台水平投影面积	阳台面积	套内面积 (阳台+户内)	阳台占套内投影面积比例 (不含套内阳台)	公摊面积	公摊率	本层面积 (计容)
A	4房2厅2卫	128.39	98.01	14.00	7.00	105.01	14.28%	23.38	18.21%	446.12
B	3房2厅2卫	90.23	69.22	9.16	4.58	73.80	13.23%	16.43	18.21%	

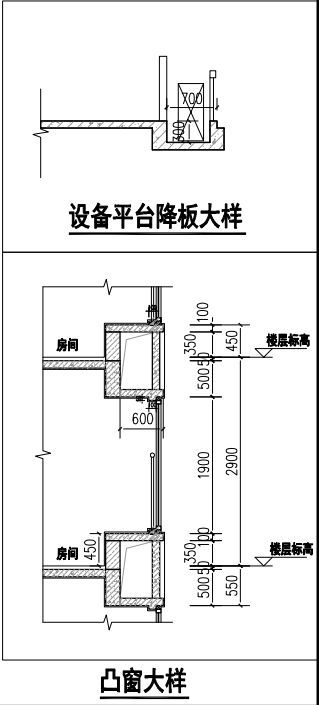

9#楼二十四层平面图 变更前

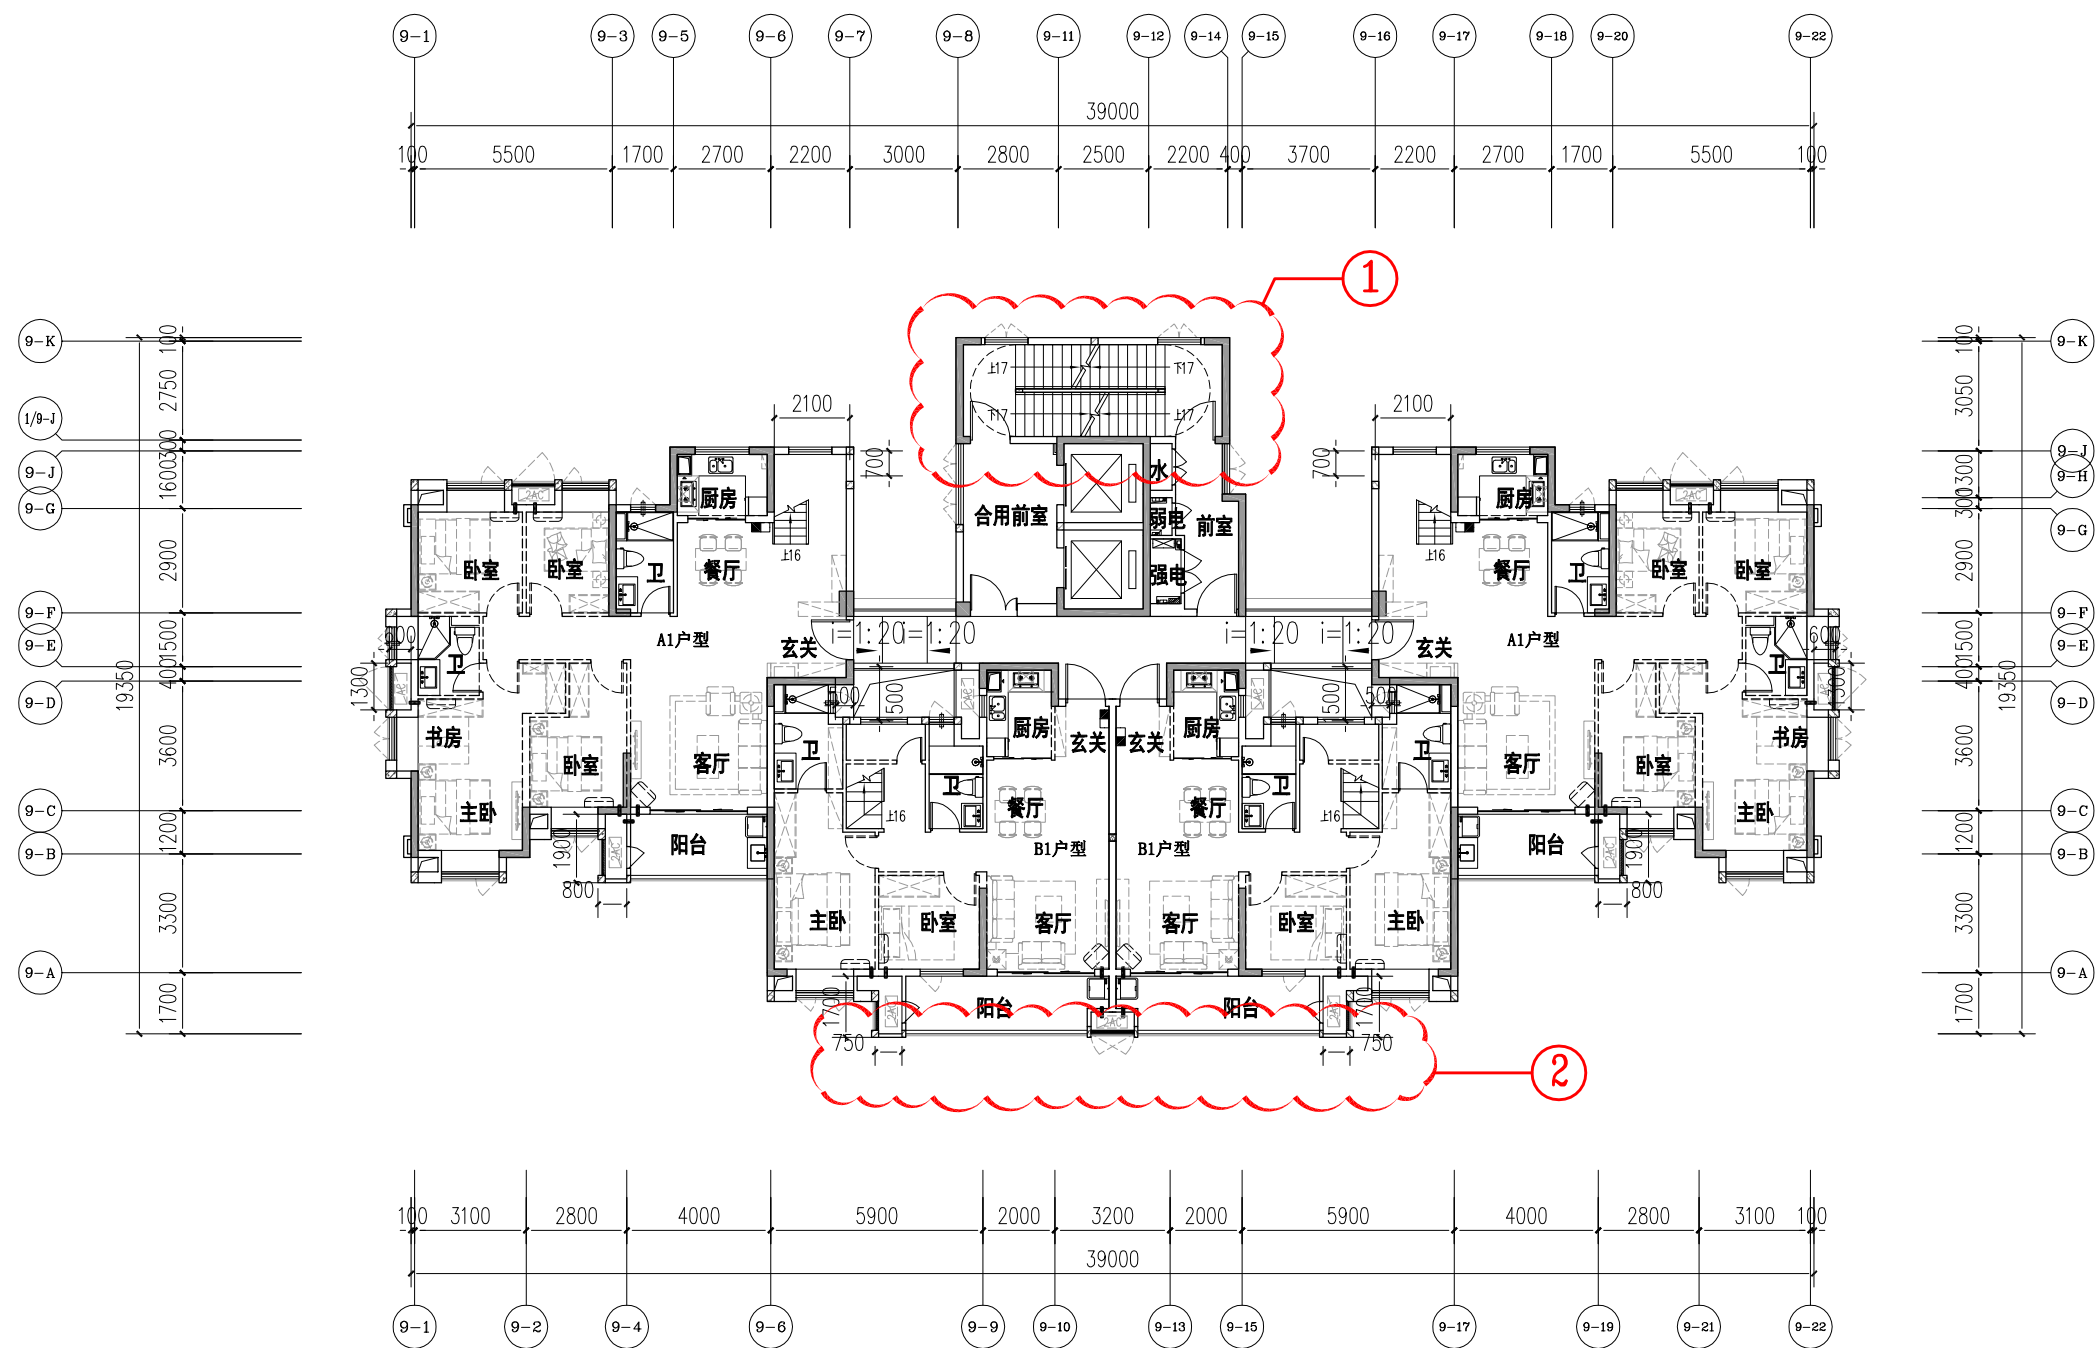


9#楼二十四层平面图 1:200 67.400

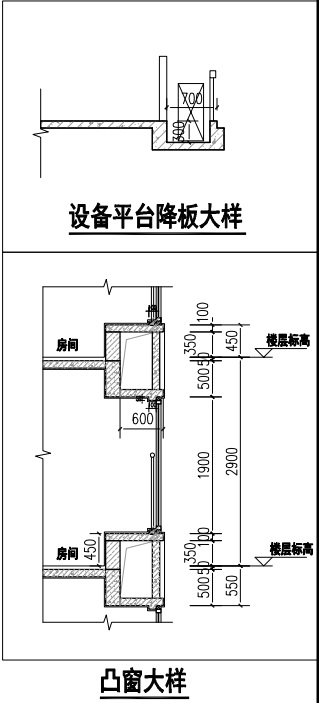


户型编号	户型	户型面积	户内面积	阳台水平投影面积	阳台面积	套内面积 (阳台+户内)	阳台占套内投影面积比例 (不含套内阳台)	公摊面积	公摊率	23+24层 面积(计容)
A1	4房3厅2卫	180.67	140.01	7.02	3.51	143.52	5.01%	37.15	20.56%	692.30
B1	2房3厅2卫	139.53	106.26	9.16	4.58	110.84	8.62%	28.69	20.56%	

9#楼二十五层平面图 变更前

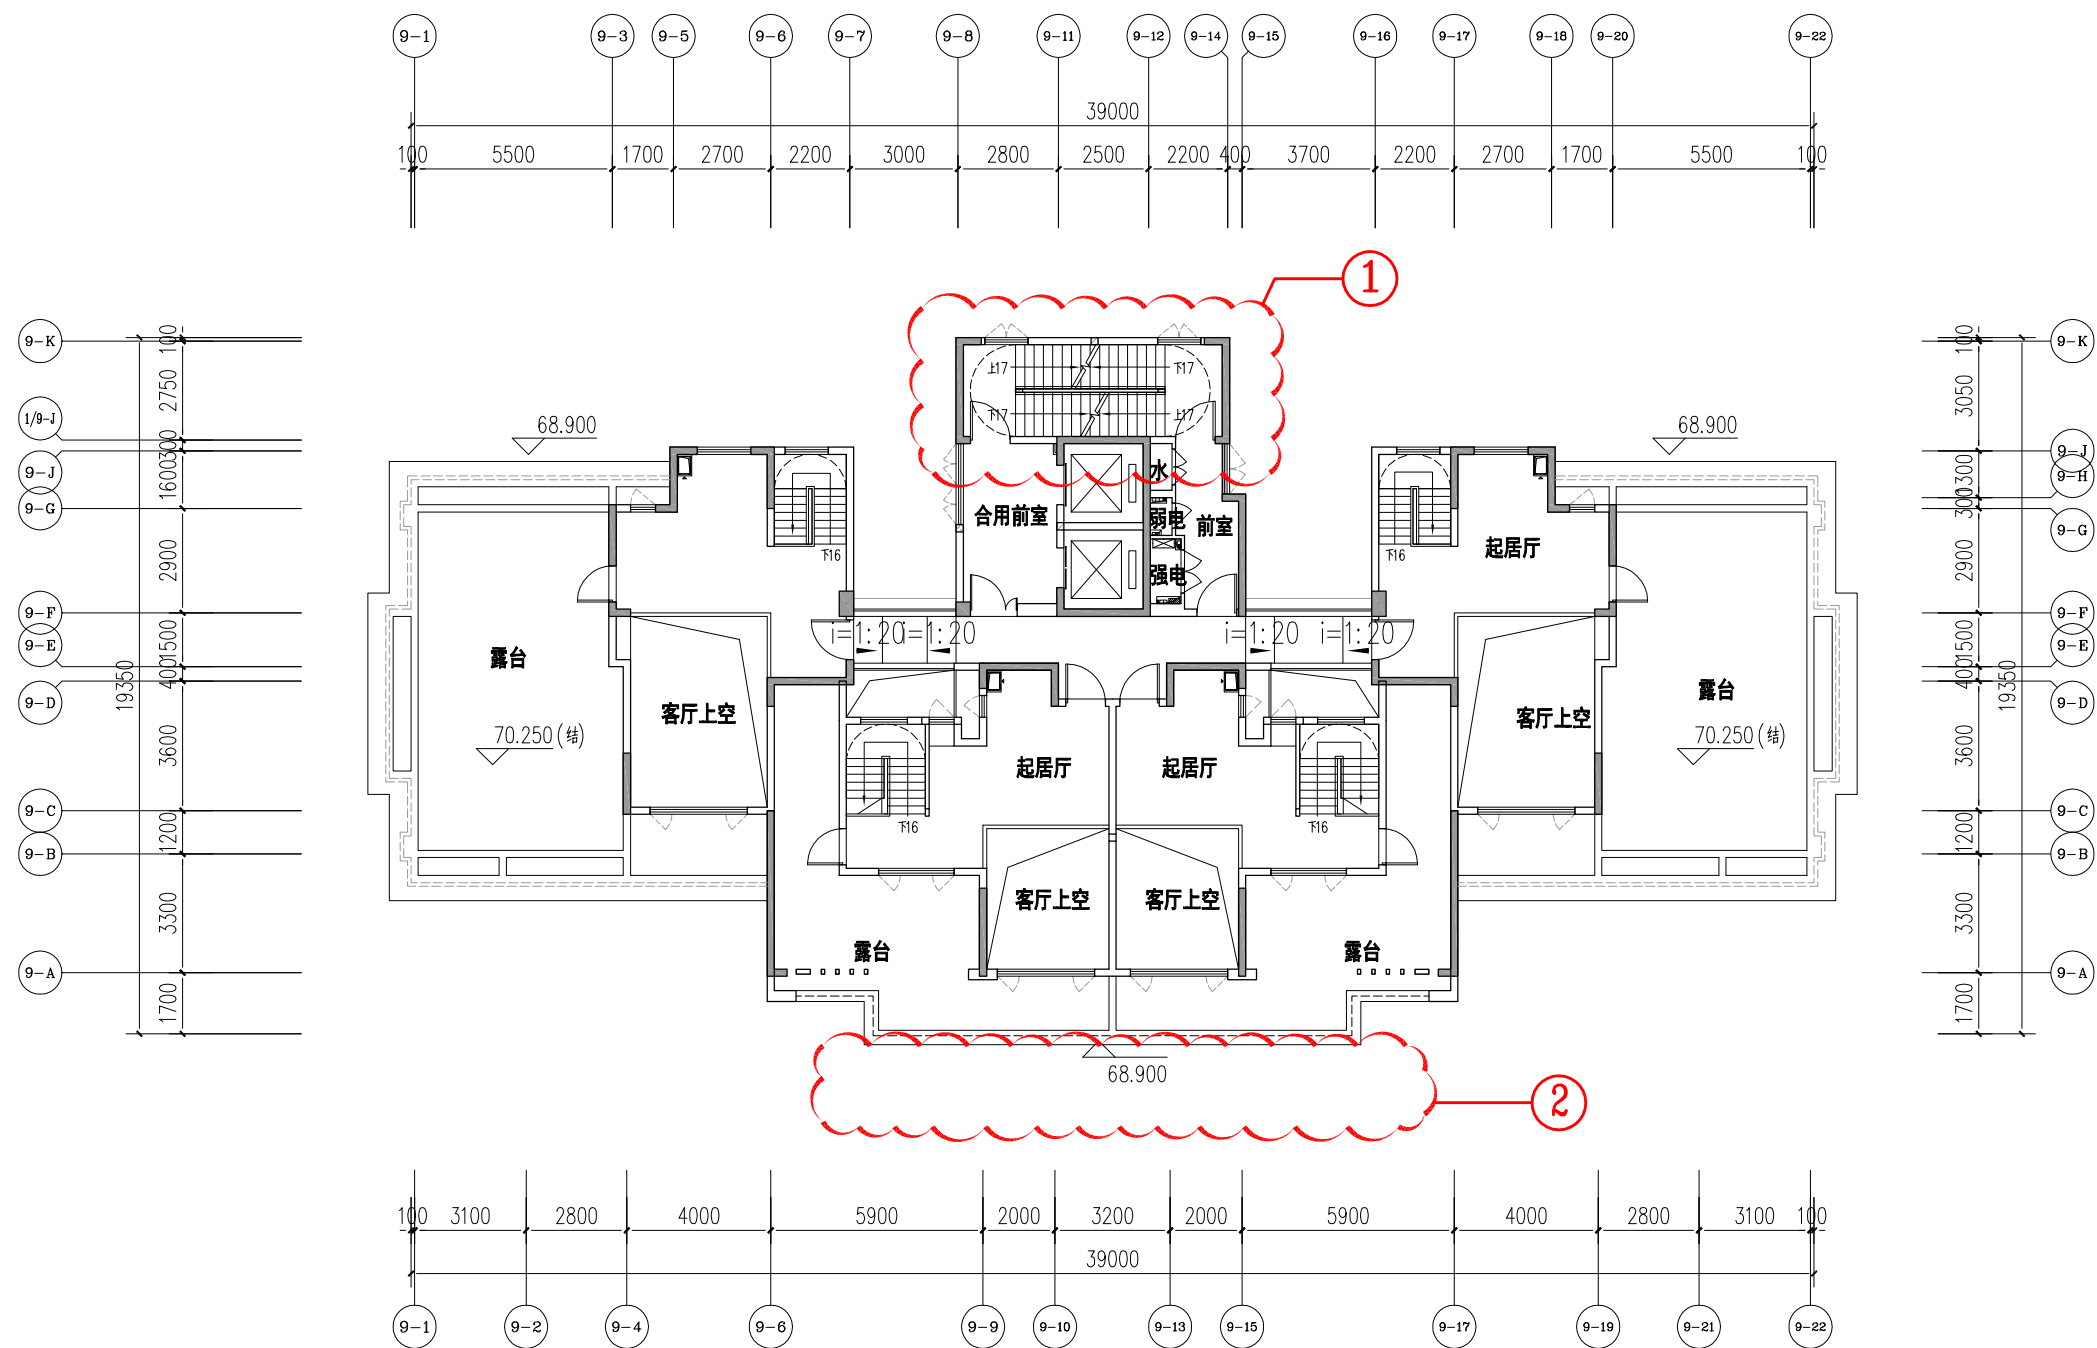

9#楼二十五层平面图 1:200

9#楼屋面层平面图 变更前

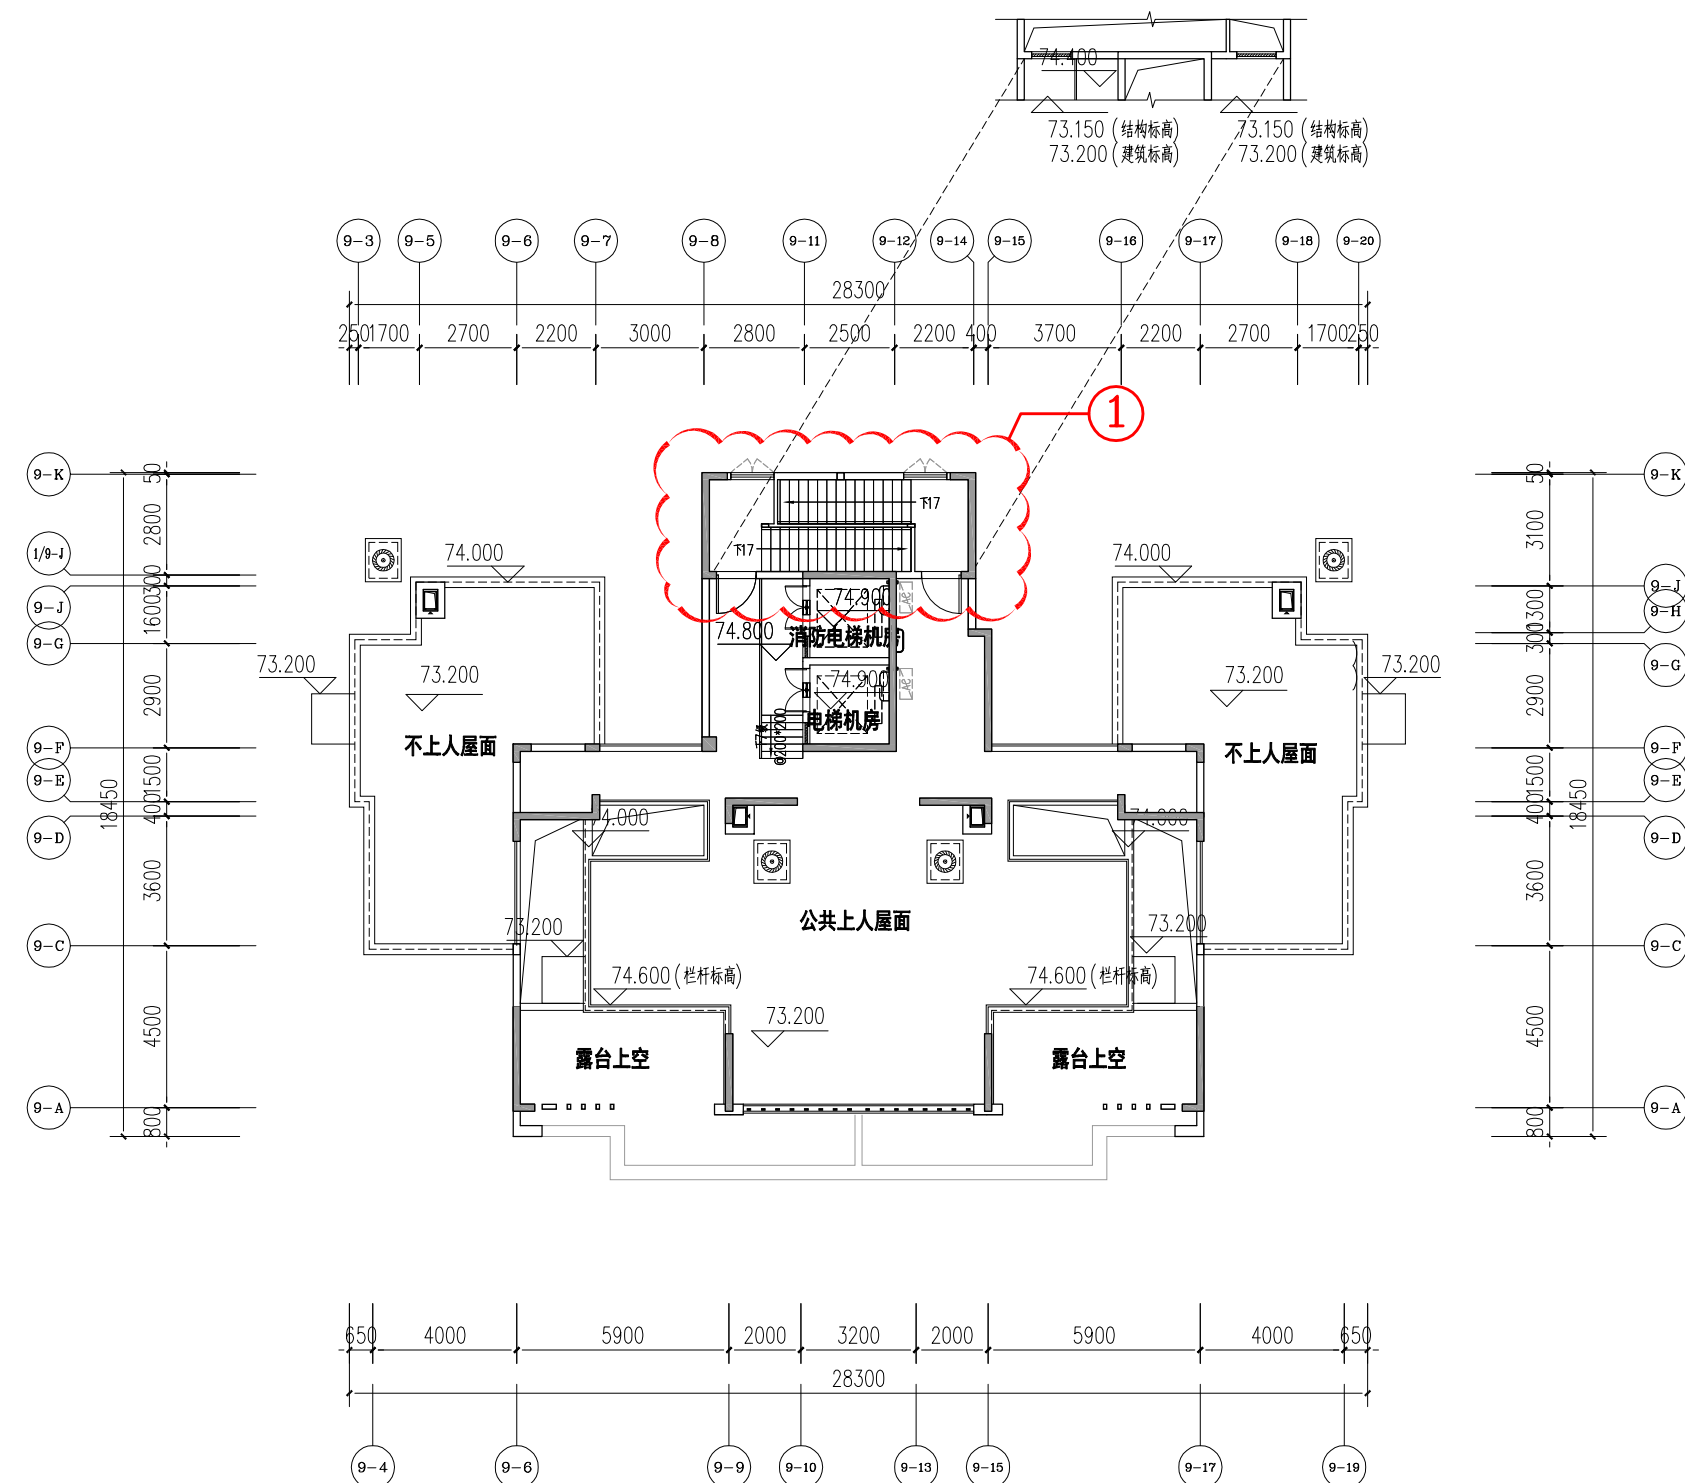


9#楼屋面层平面图 1:200

本层计容面积: 34.90m²


73.200

9#楼屋架层平面图 变更前

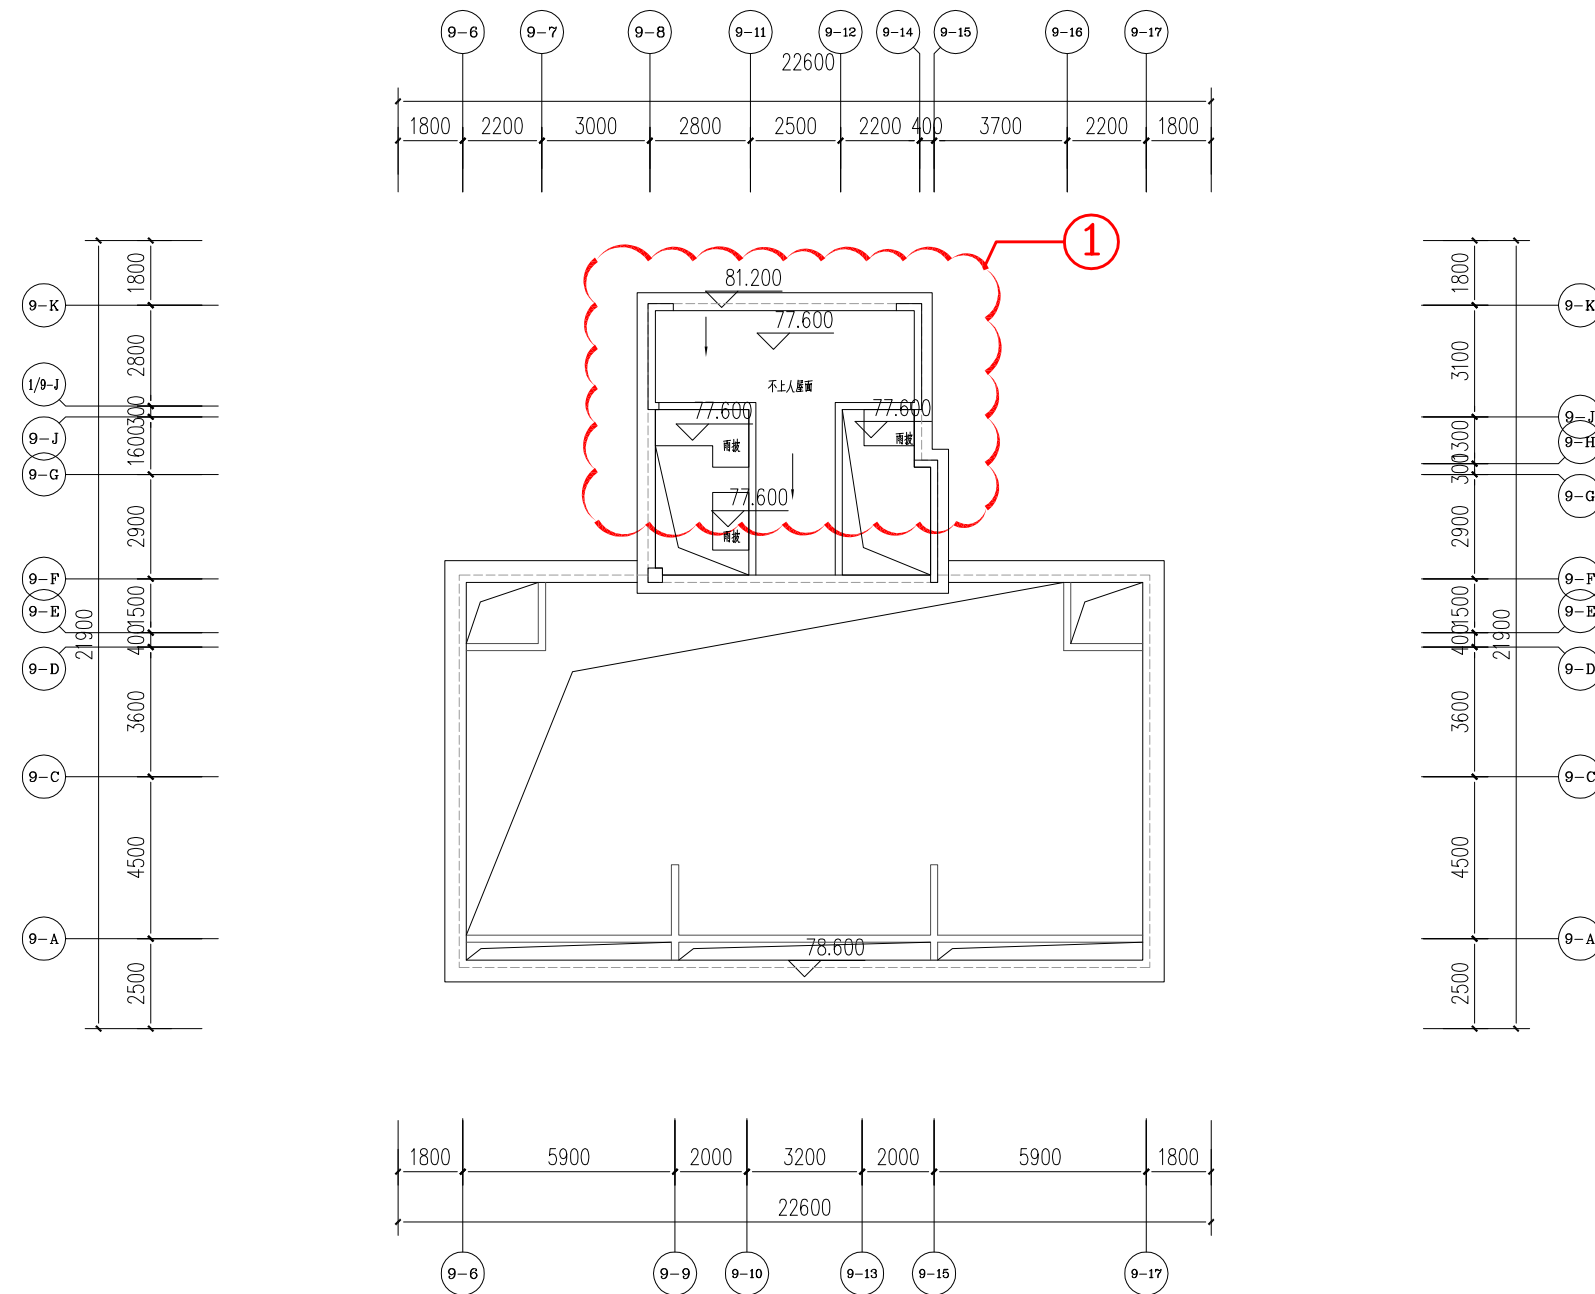


9#楼屋架层平面图 1:200

9#楼立面图变更前

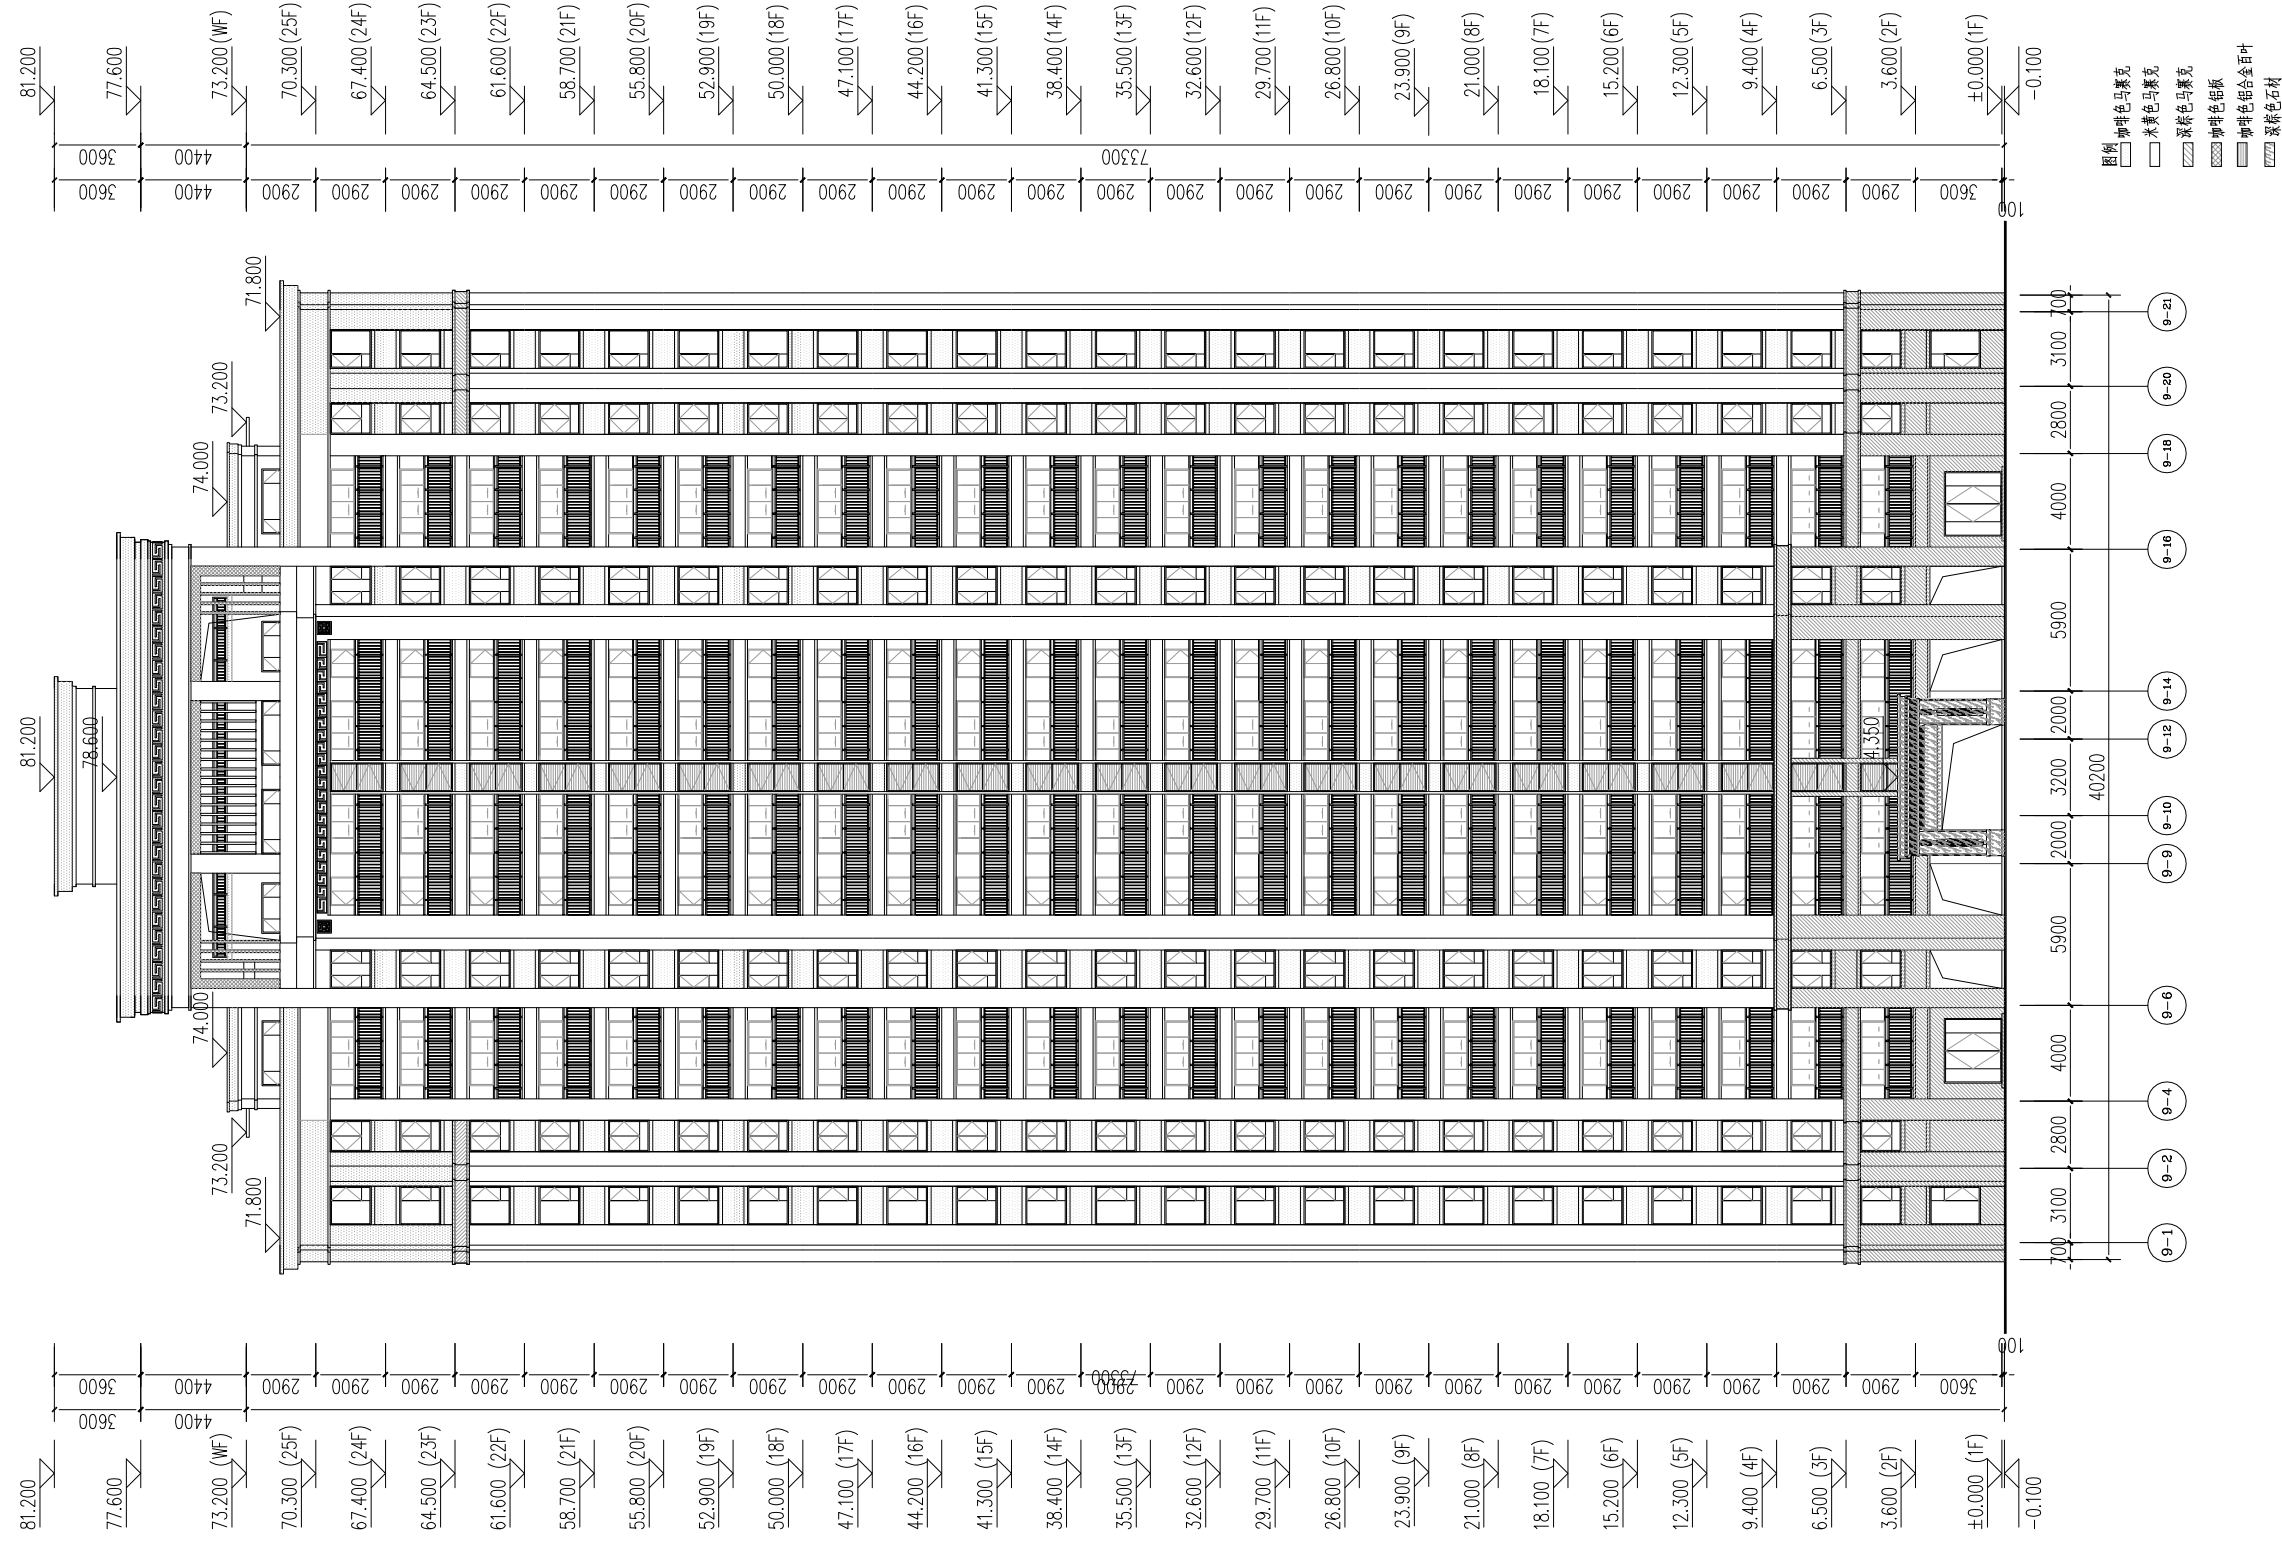


轴立面图 1:300

9#楼立面图 变更前

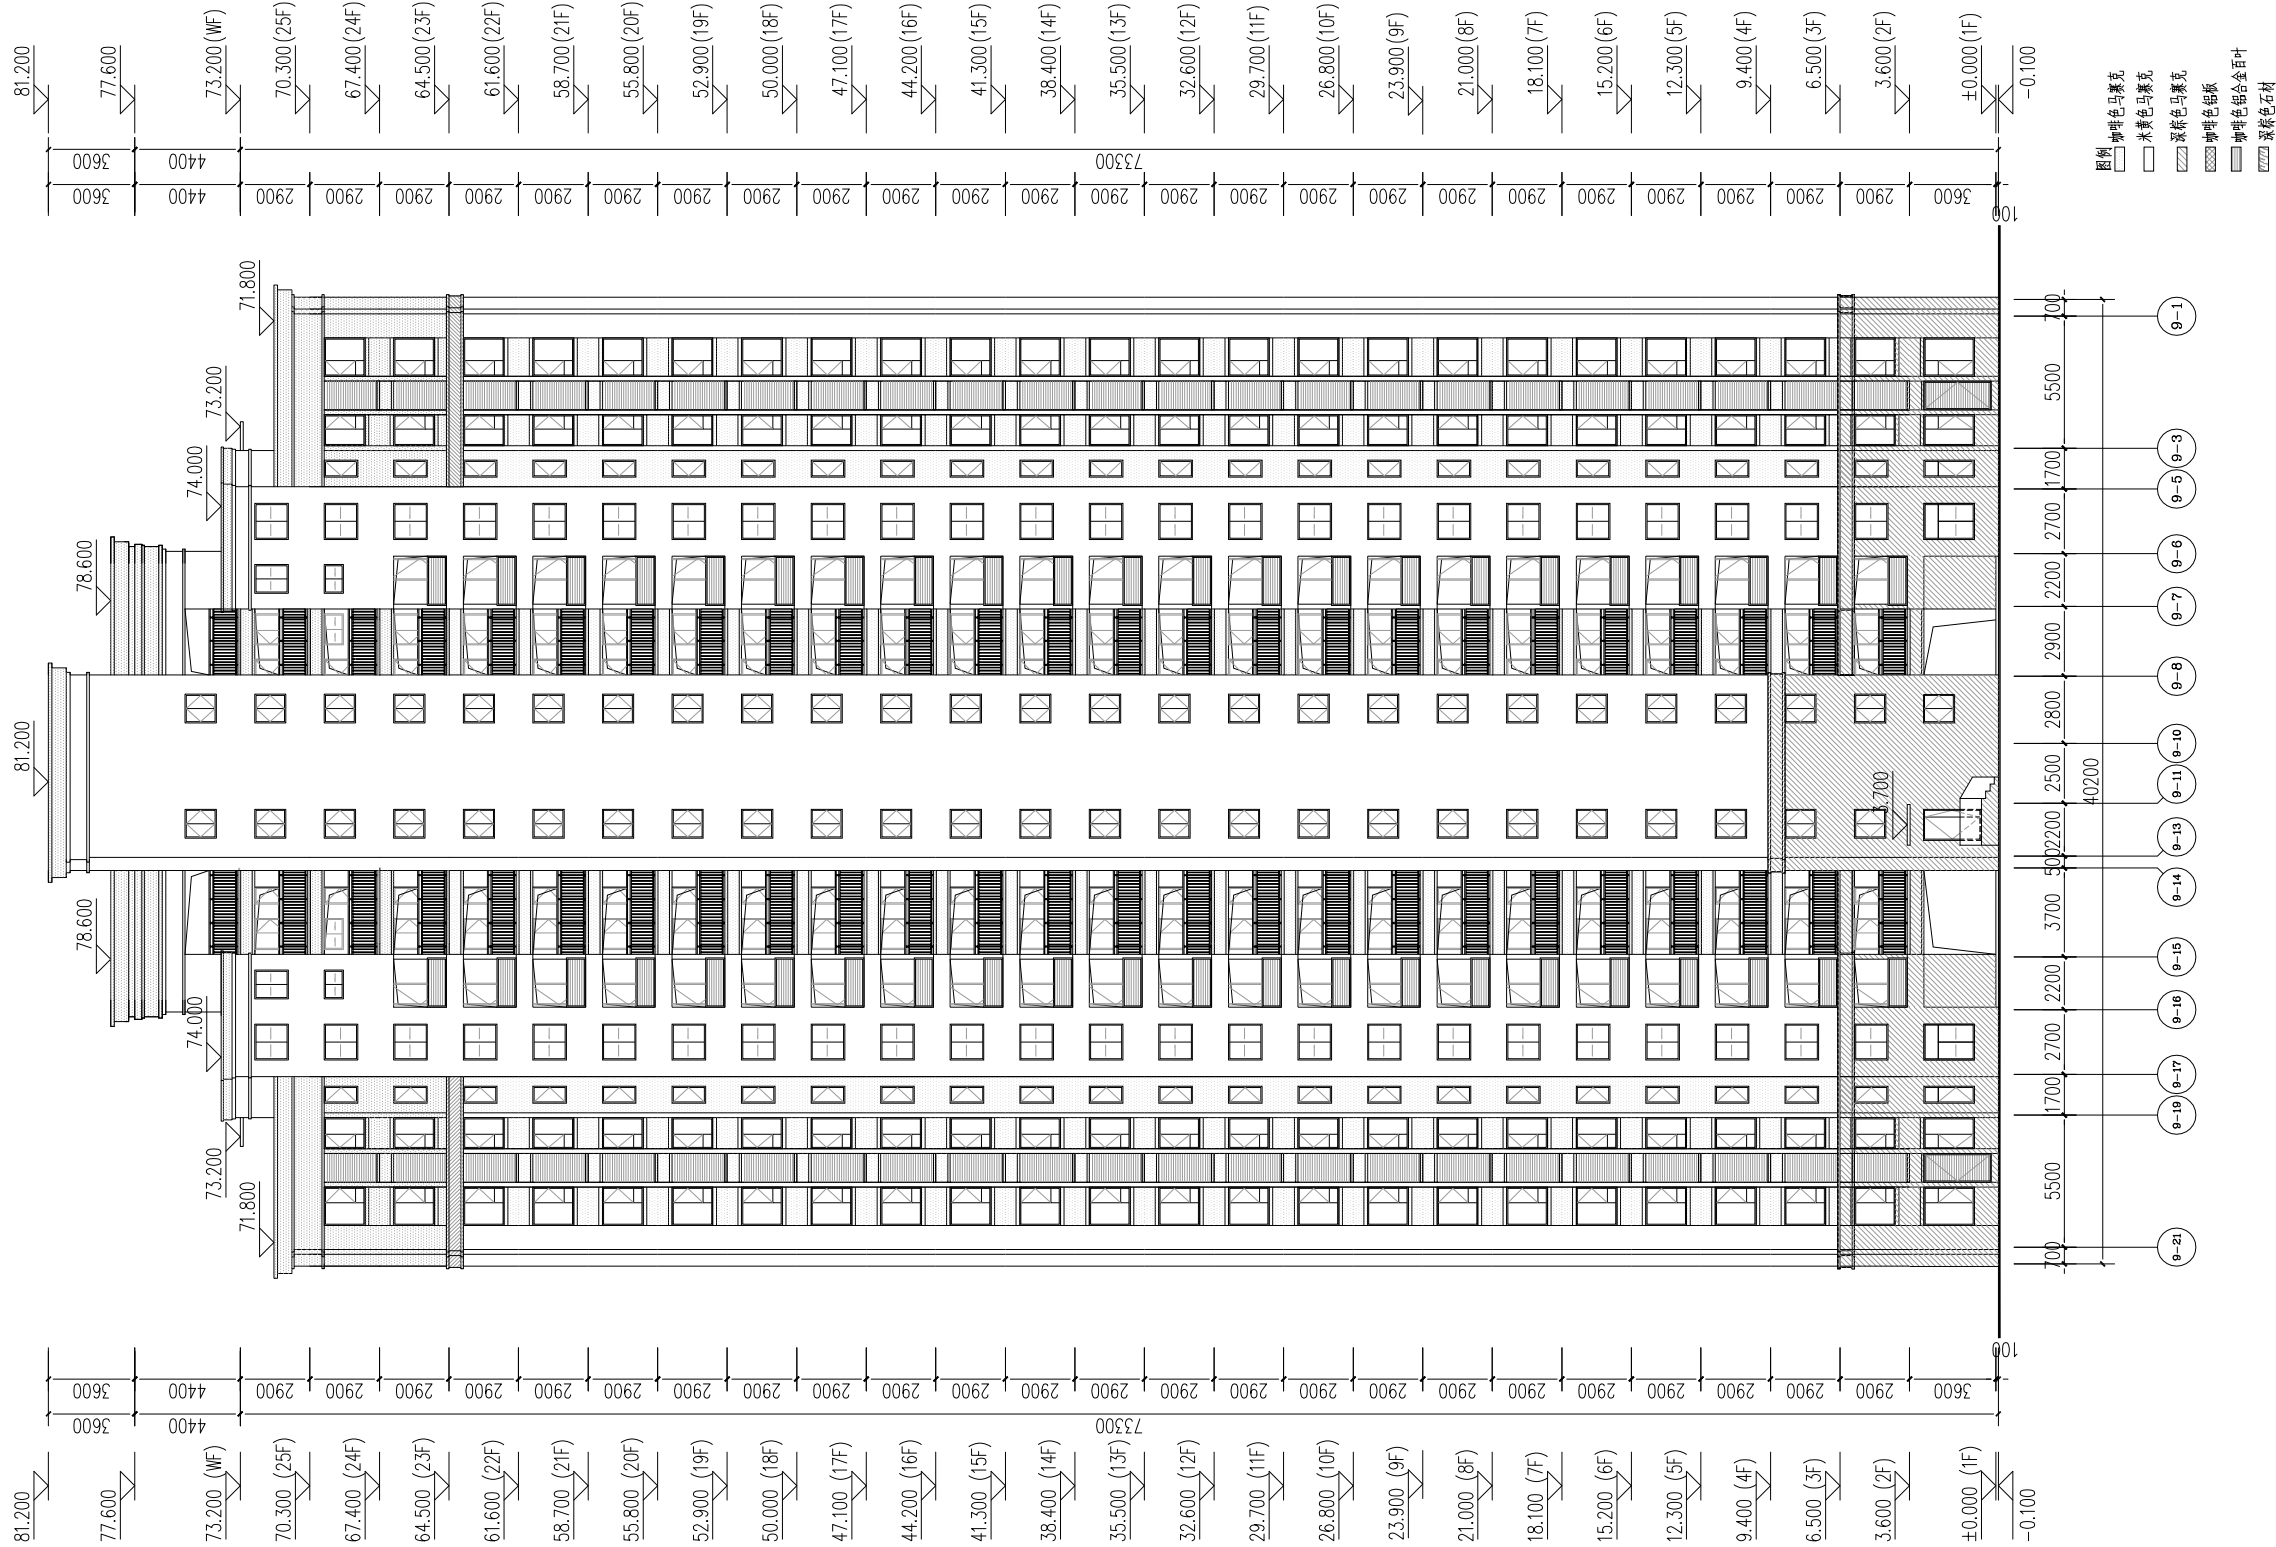

9-21 ~ 9-1 轴立面图 1:300


9#楼立面图 变更前

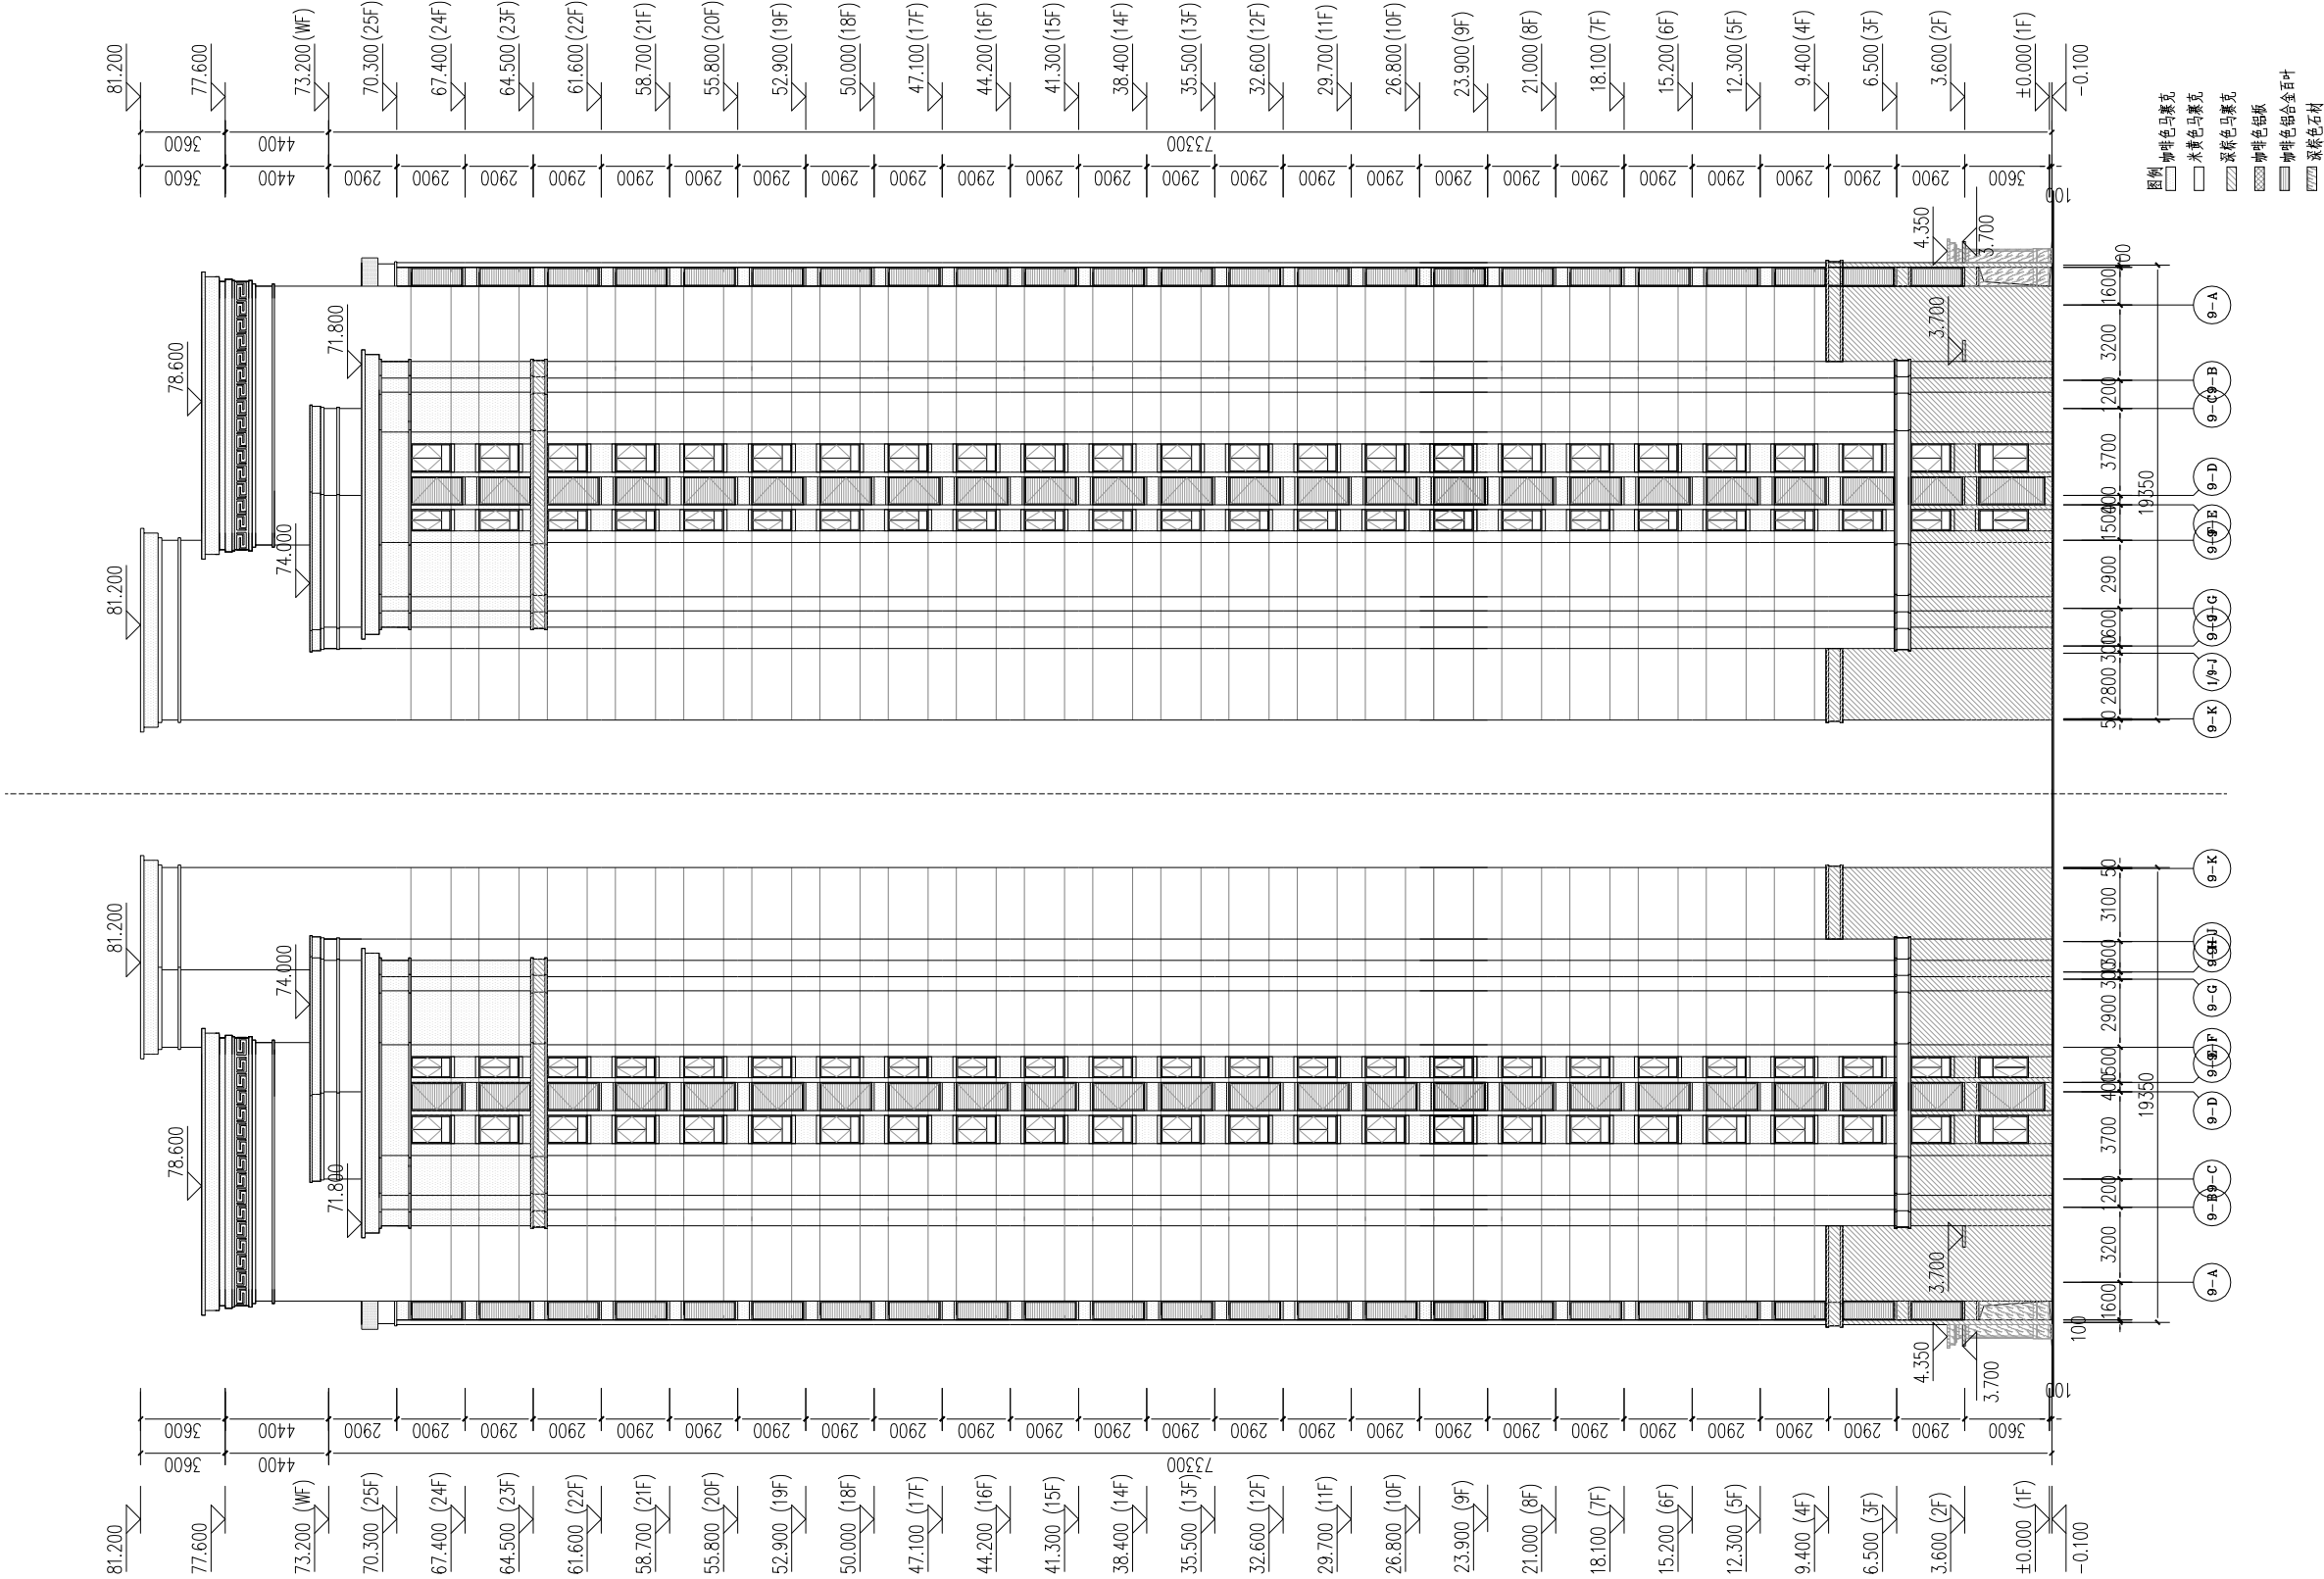

9-A ~ 9-K 轴立面图 1:300

9-K ~ 9-A 轴立面图 1:300

9#楼立面图 变更前

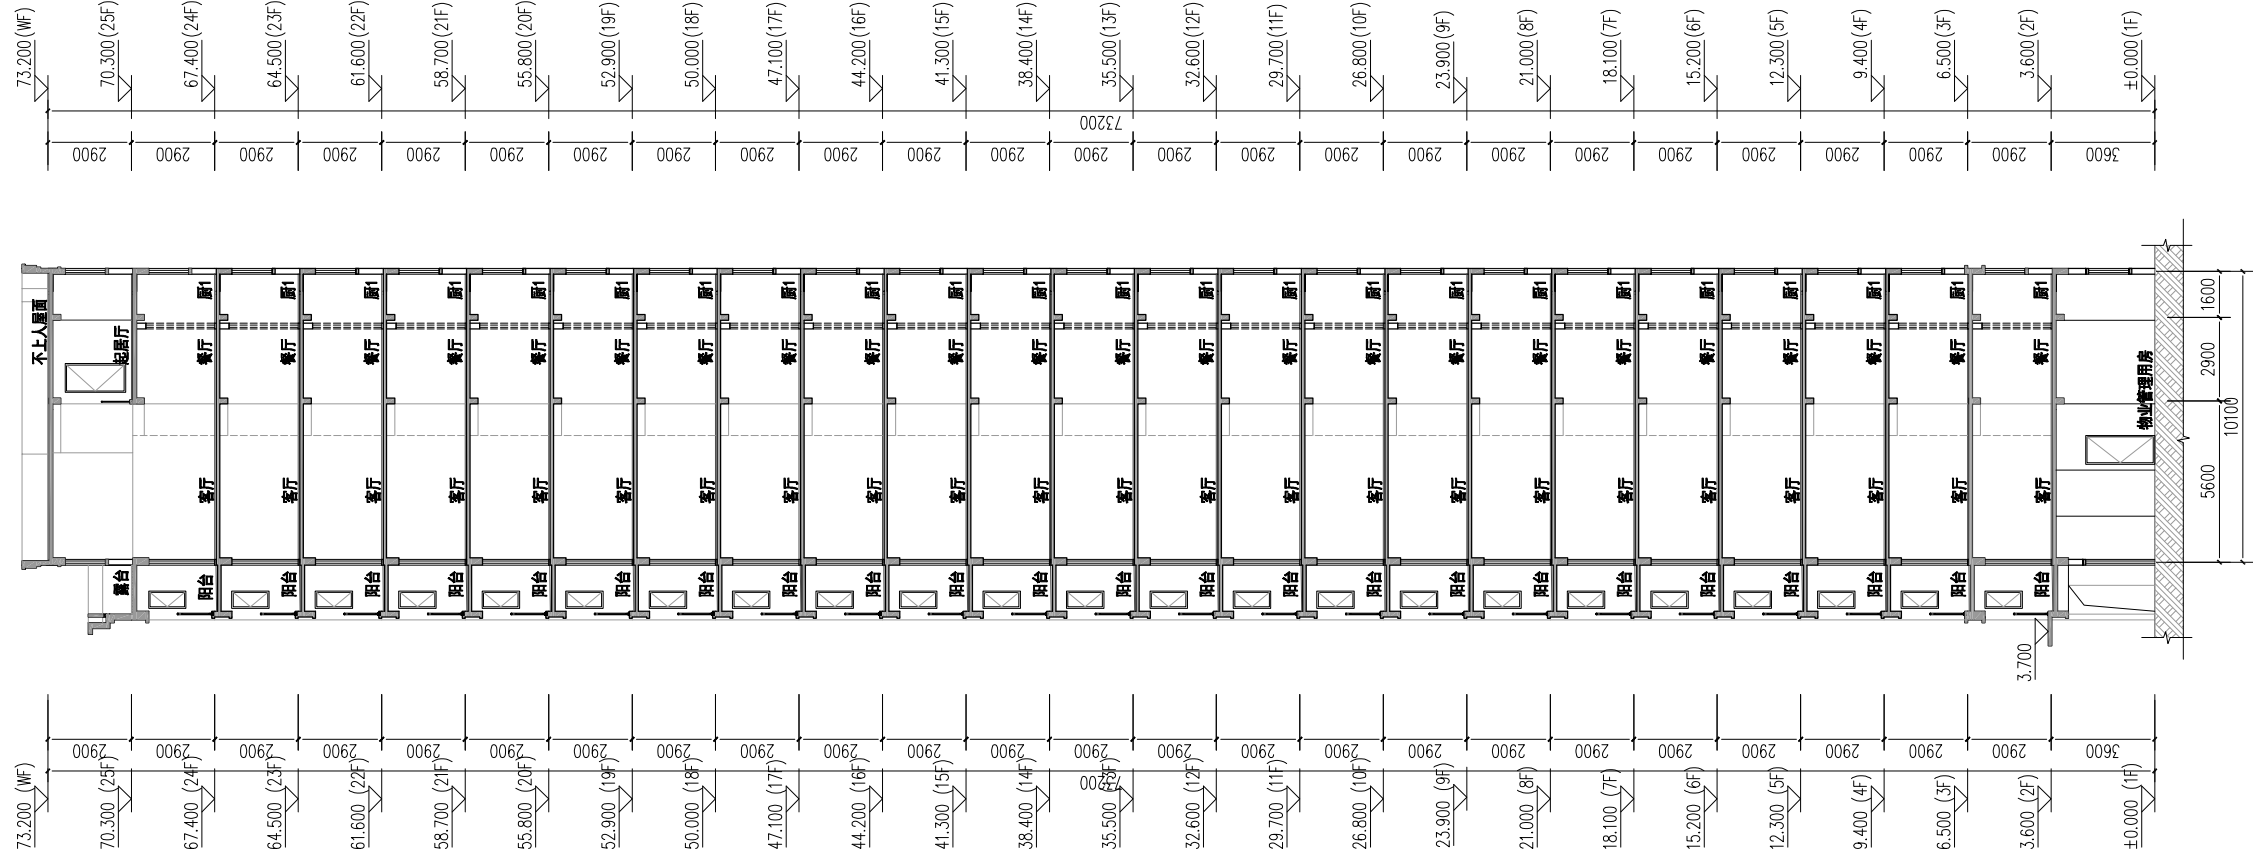


9#楼1-1剖面图 1:200

9#楼一层平面图 变更后


变更内容:

1:一层层高由3.6米改为4.2米, 楼梯踏步及无障碍坡道相应修改, 水井墙体外移至9-14轴处。

2: 此区域造型向9-A轴移100。

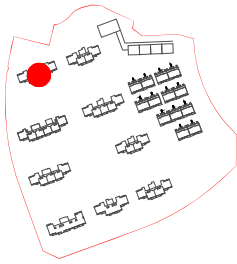

区位示意图

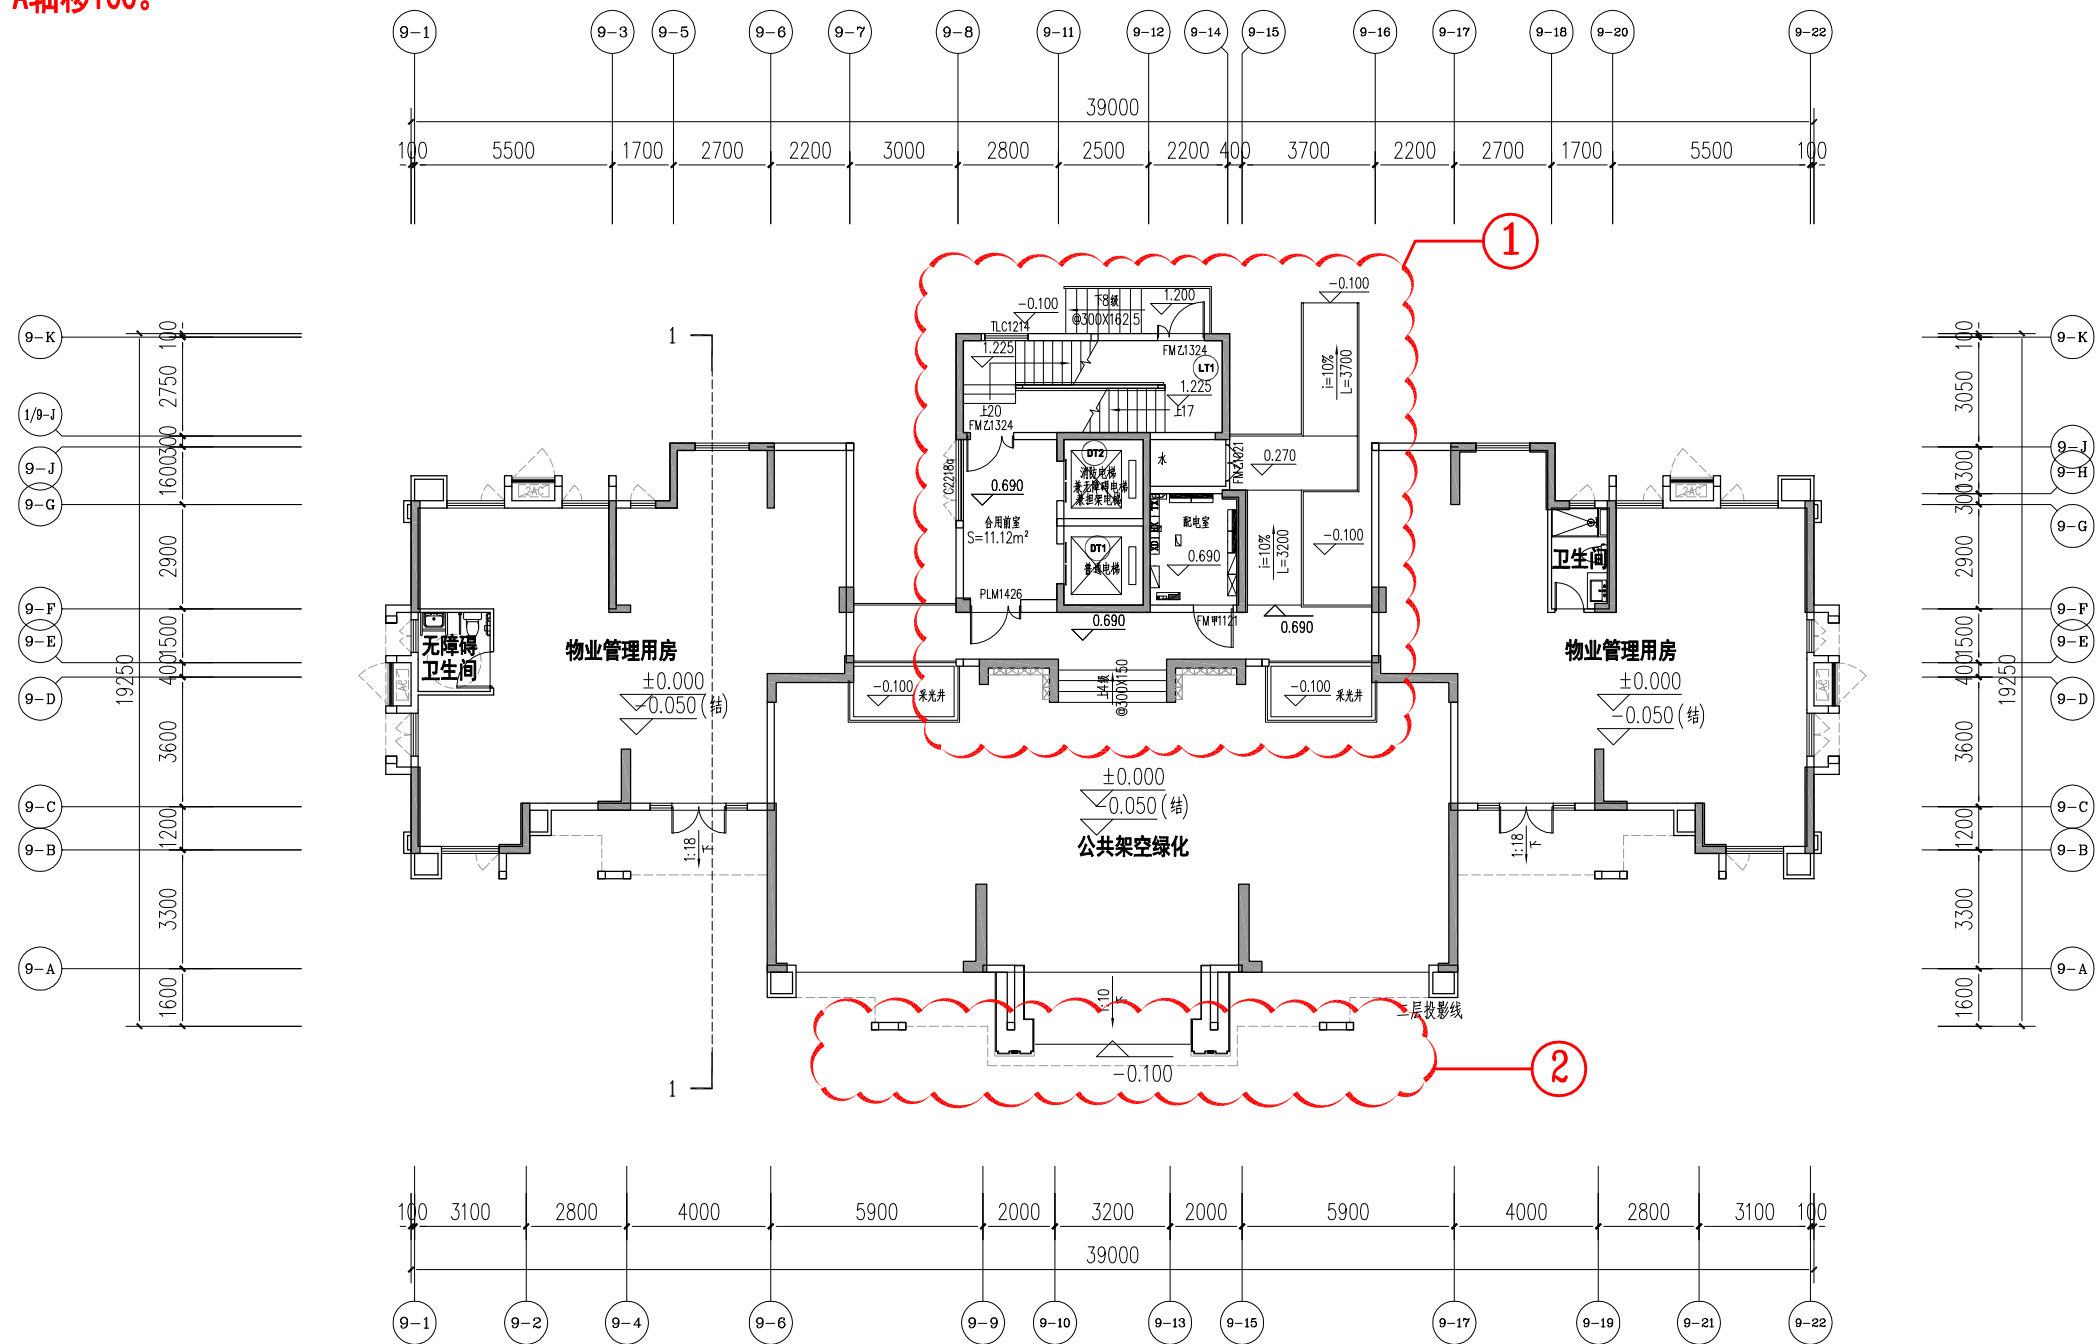

9#楼一层平面图 1:200



±0.000 (158.00)

本栋计容面积: 10630.70m²
本层计容面积: 280.67m²
其中: 住宅面积: 60.43m²
物业管理用房面积: 220.24m²
本层不计容架空面积: 184.25m²

9#楼二层平面图 变更后

变更内容:


- 1:层高由2.9m改为3.0m, 楼梯踏步相应修改。
- 2:此区域阳台底板及造型墙体向9-A轴移100。
- 3:雨披标高相应调整。

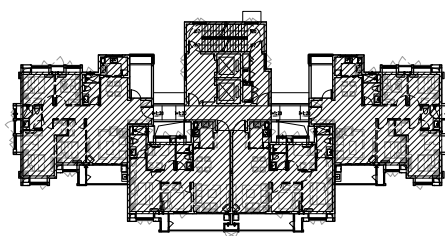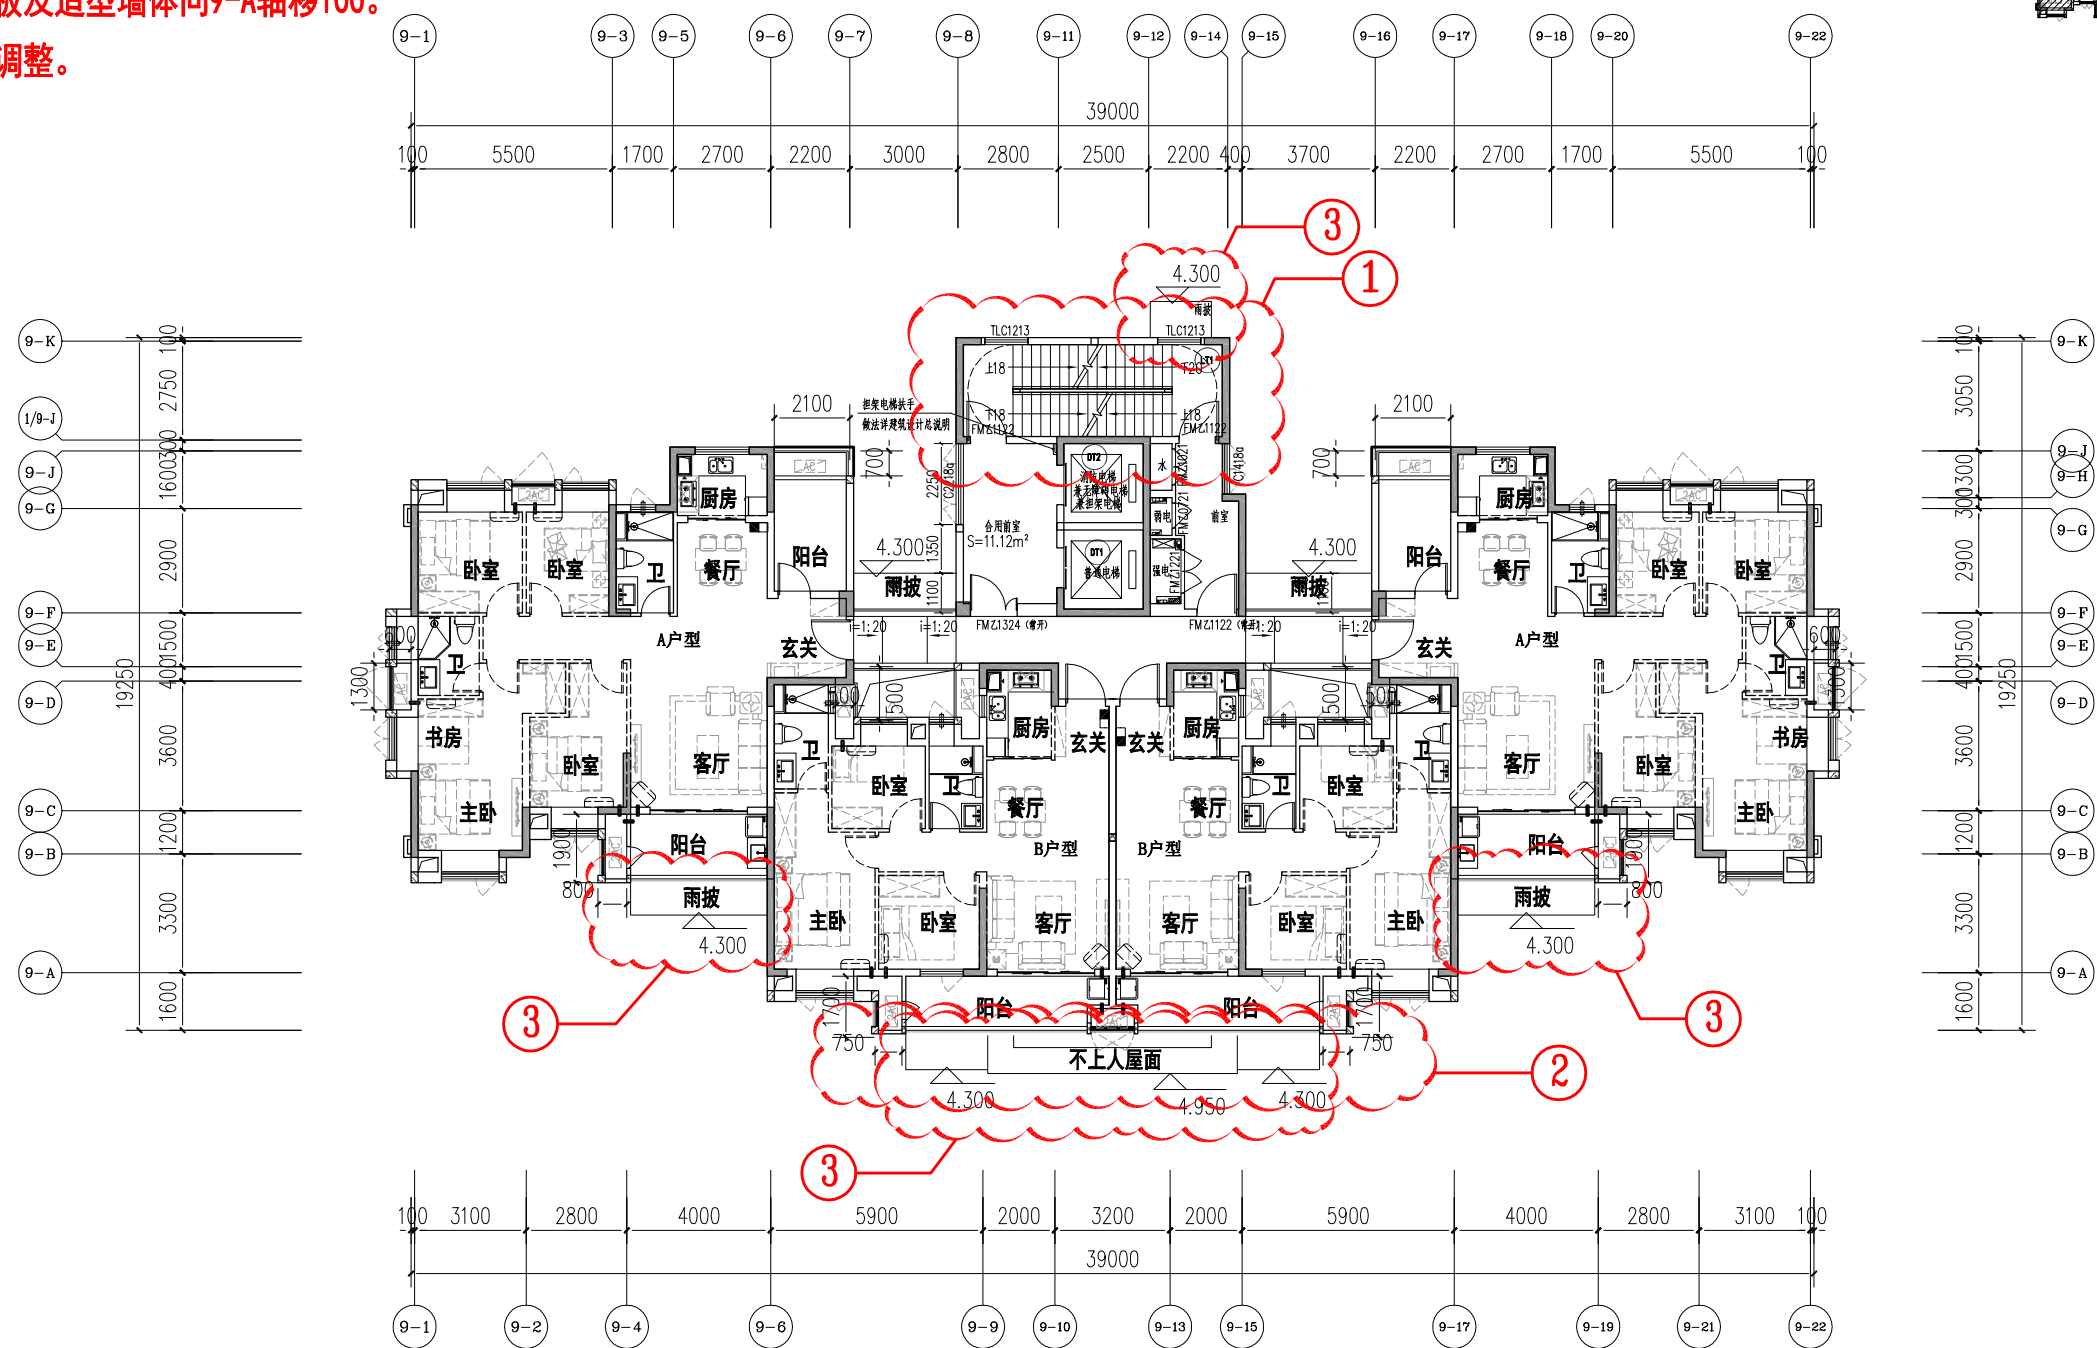

9#结构走向示意图

9#楼二层平面图 1:200

户型编号	户型	户型面积	户内面积	阳台水平投影面积	阳台面积	套内面积 (阳台+户内)	阳台占套内投影面积比例 (不含套内阳台)	公摊面积	公摊率	本层面积 (计容)
A	4房2厅2卫	128.39	98.01	14.00	7.00	105.01	14.28%	23.38	18.21%	446.12
B	3房2厅2卫	90.23	69.22	9.16	4.58	73.80	13.23%	16.43	18.21%	

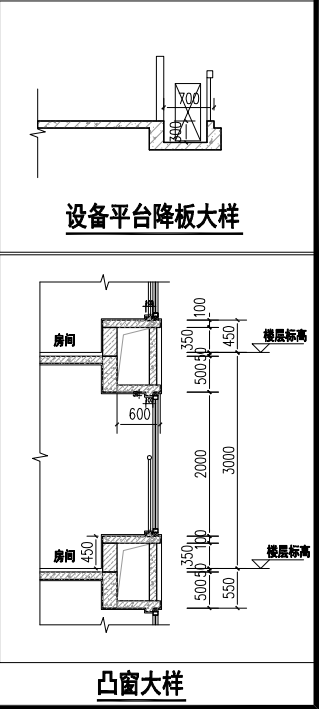

设备平台降板大样


凸窗大样

9#楼三、四层平面图 变更后

变更内容:

1:层高由2.9m改为3.0m, 楼梯踏步相应修改。


2:此区域阳台底板及造型墙体向9-A轴移100。

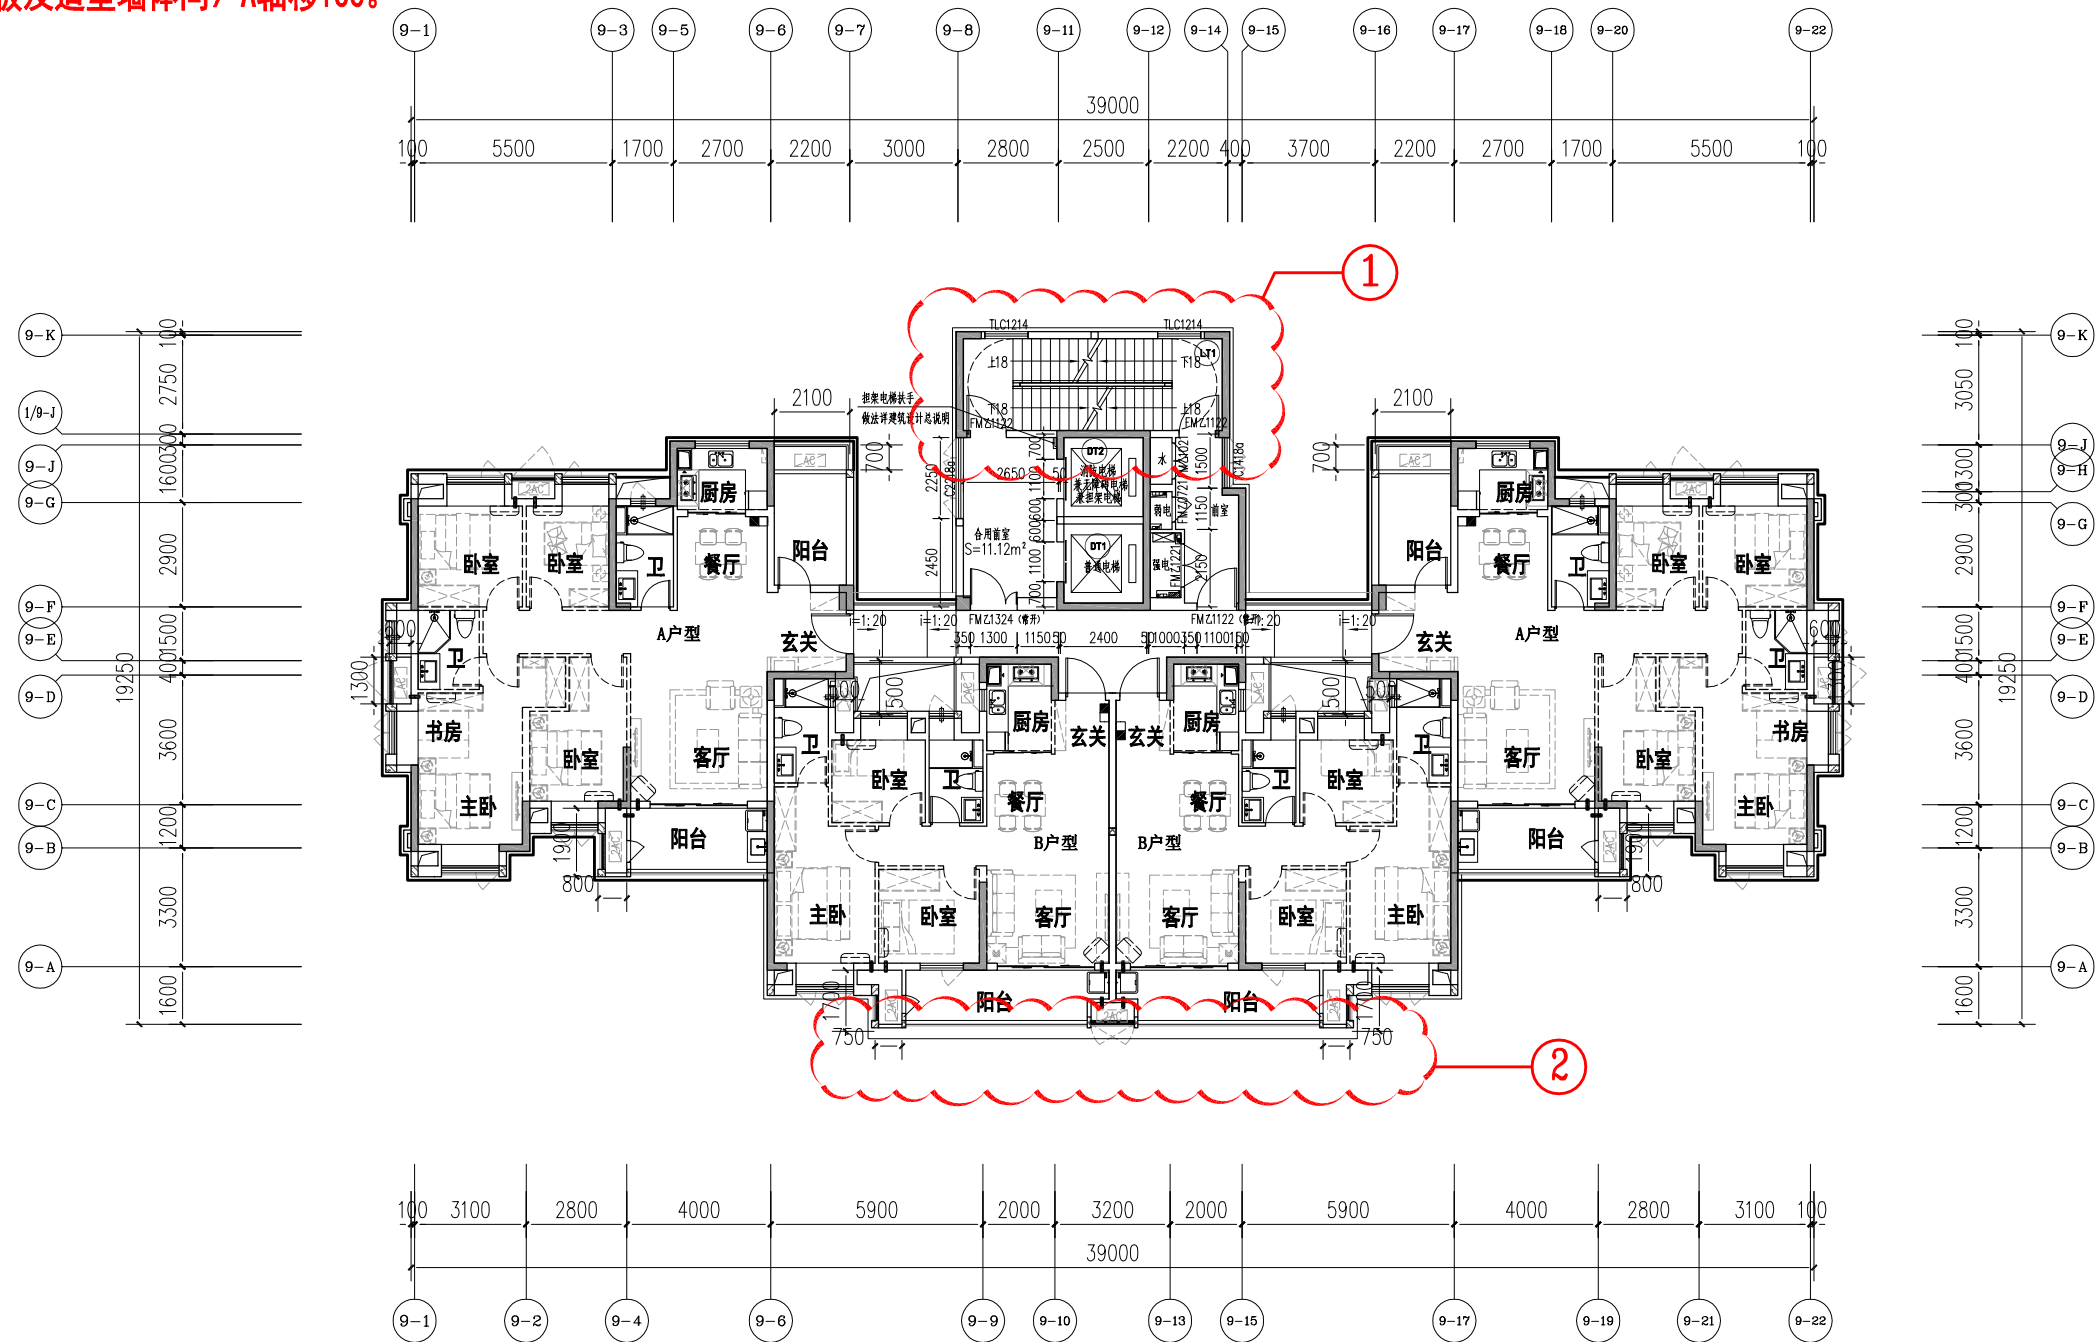

9#楼三、四层平面图 1:200

(10.200)4F
7.200 3F

户型编号	户型	户型面积	户内面积	阳台水平投影面积	阳台面积	套内面积 (阳台+户内)	阳台占套内投影面积比例 (不含套内阳台)	公摊面积	公摊率	本层面积 (计容)
A	4房2厅2卫	128.39	98.01	14.00	7.00	105.01	14.28%	23.38	18.21%	446.12
B	3房2厅2卫	90.23	69.22	9.16	4.58	73.80	13.23%	16.43	18.21%	

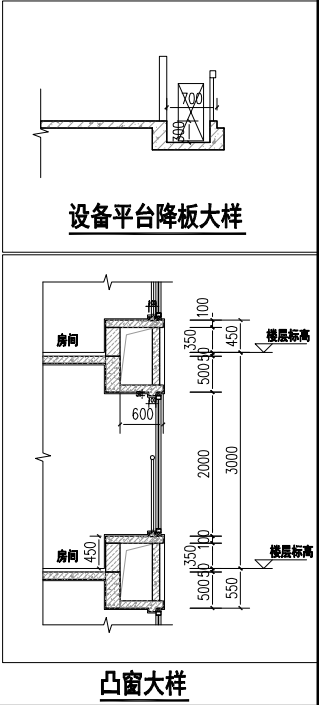


9#楼五至二十三层平面图 变更后

变更内容:

1:层高由2.9m改为3.0m, 楼梯踏步相应修改。


2:此区域阳台底板及造型墙体向9-A轴移100。

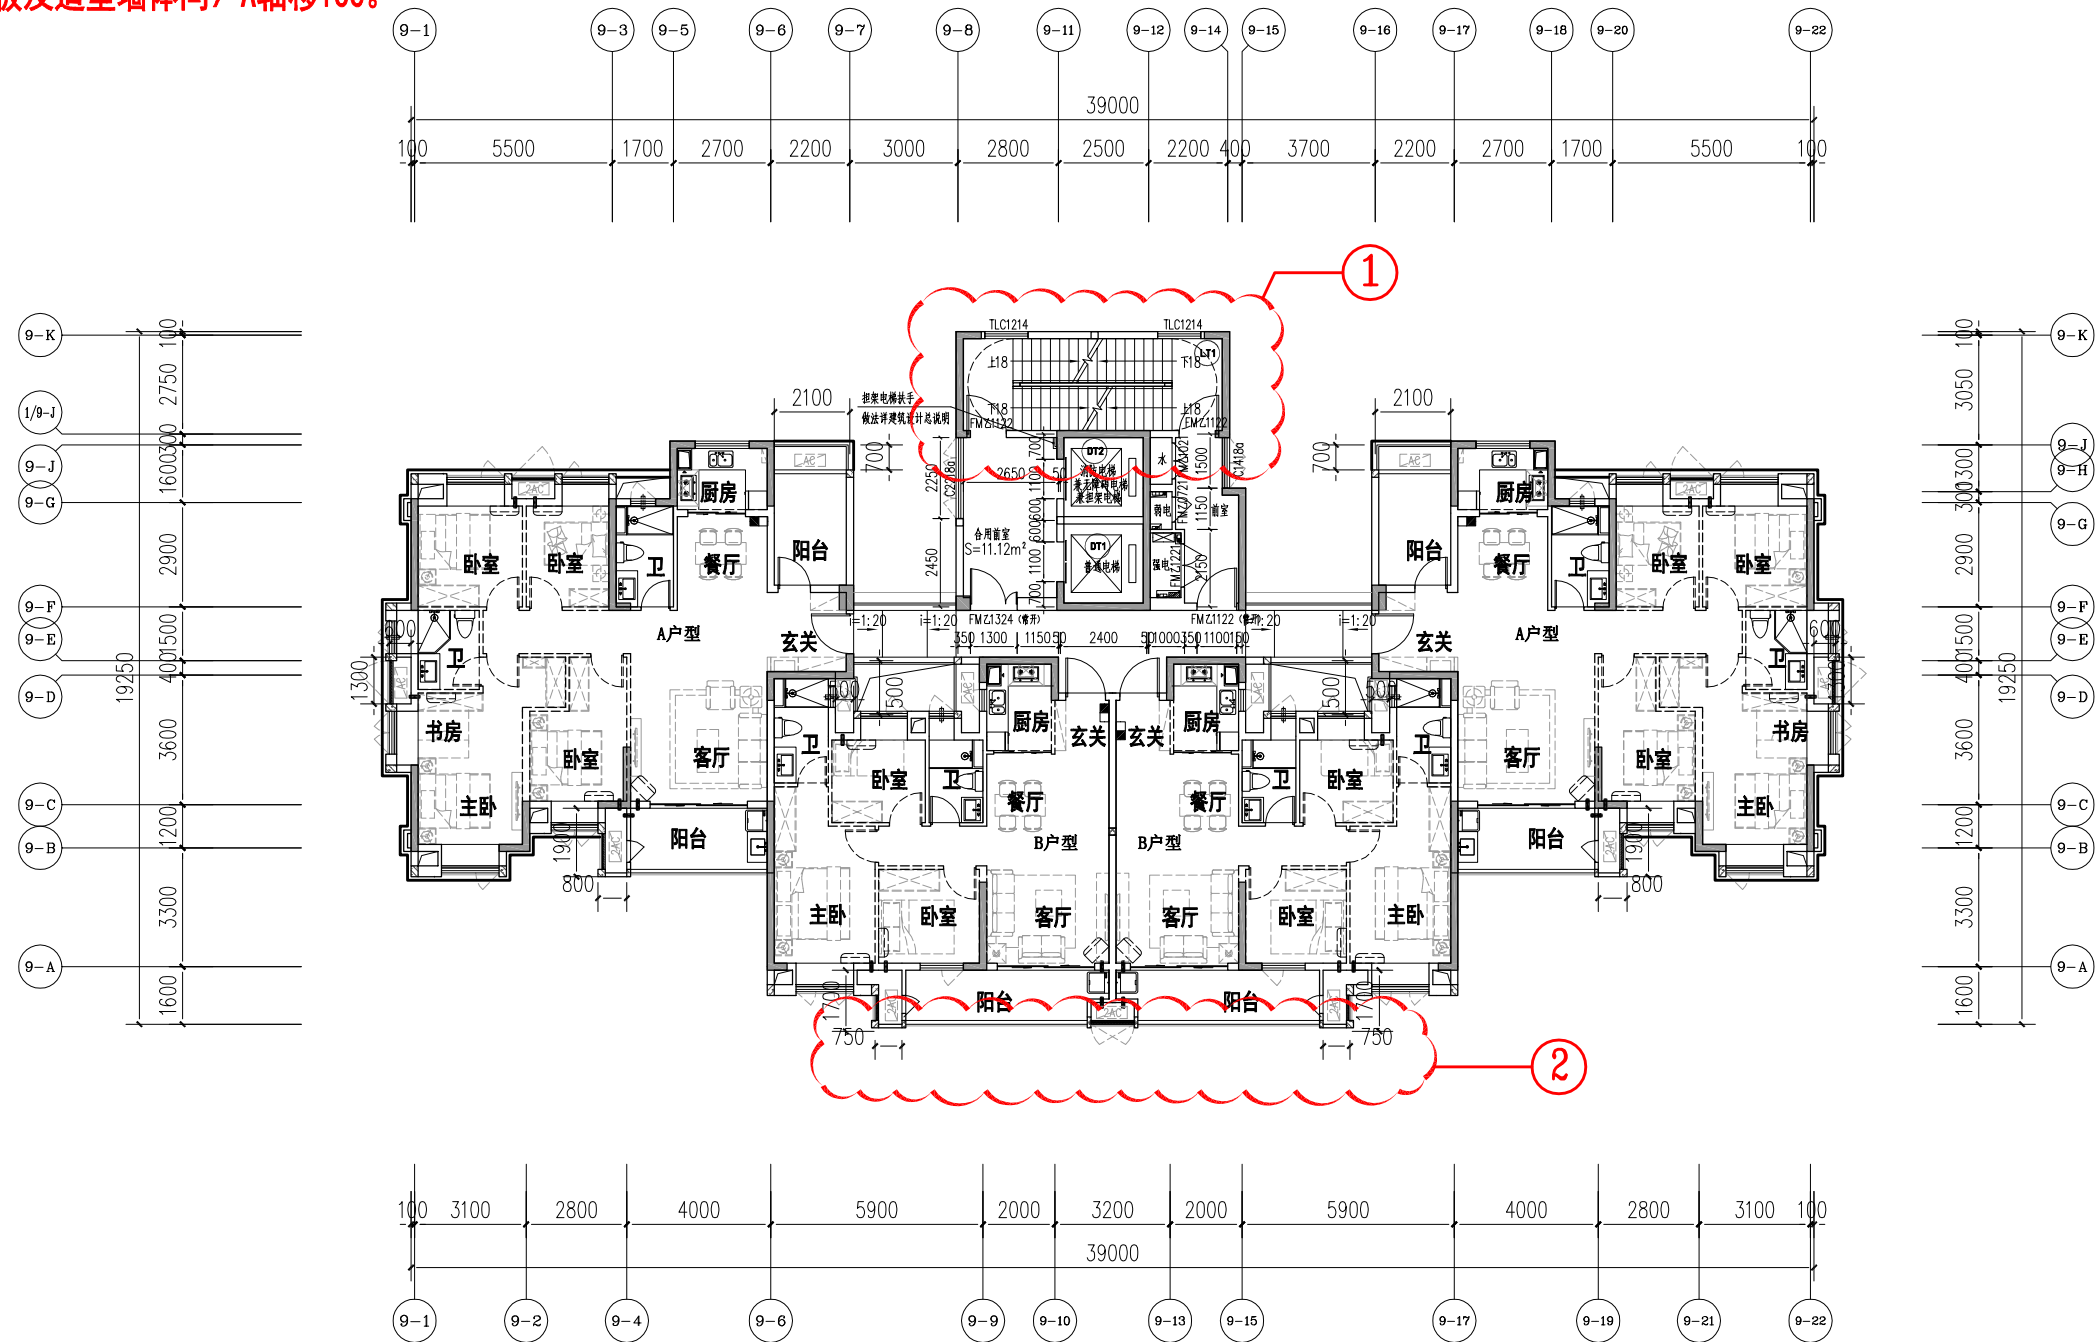

9#楼五至二十三层平面图 1:200

67.200 (23F)
~
13.200 (5F)

户型编号	户型	户型面积	户内面积	阳台水平投影面积	阳台面积	套内面积 (阳台+户内)	阳台占套内投影面积比例 (不含套内阳台)	公摊面积	公摊率	本层面积 (计容)
A	4房2厅2卫	128.39	98.01	14.00	7.00	105.01	14.28%	23.38	18.21%	446.12
B	3房2厅2卫	90.23	69.22	9.16	4.58	73.80	13.23%	16.43	18.21%	

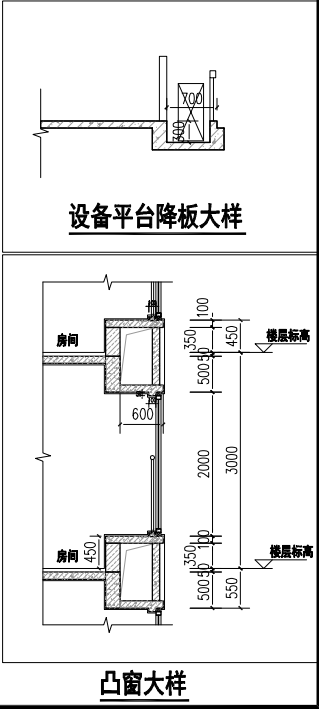


9#楼二十四层平面图 变更后


变更内容:

1:层高由2.9m改为3.0m, 楼梯踏步相应修改。

2:此区域阳台底板及造型墙体向9-A轴移100。

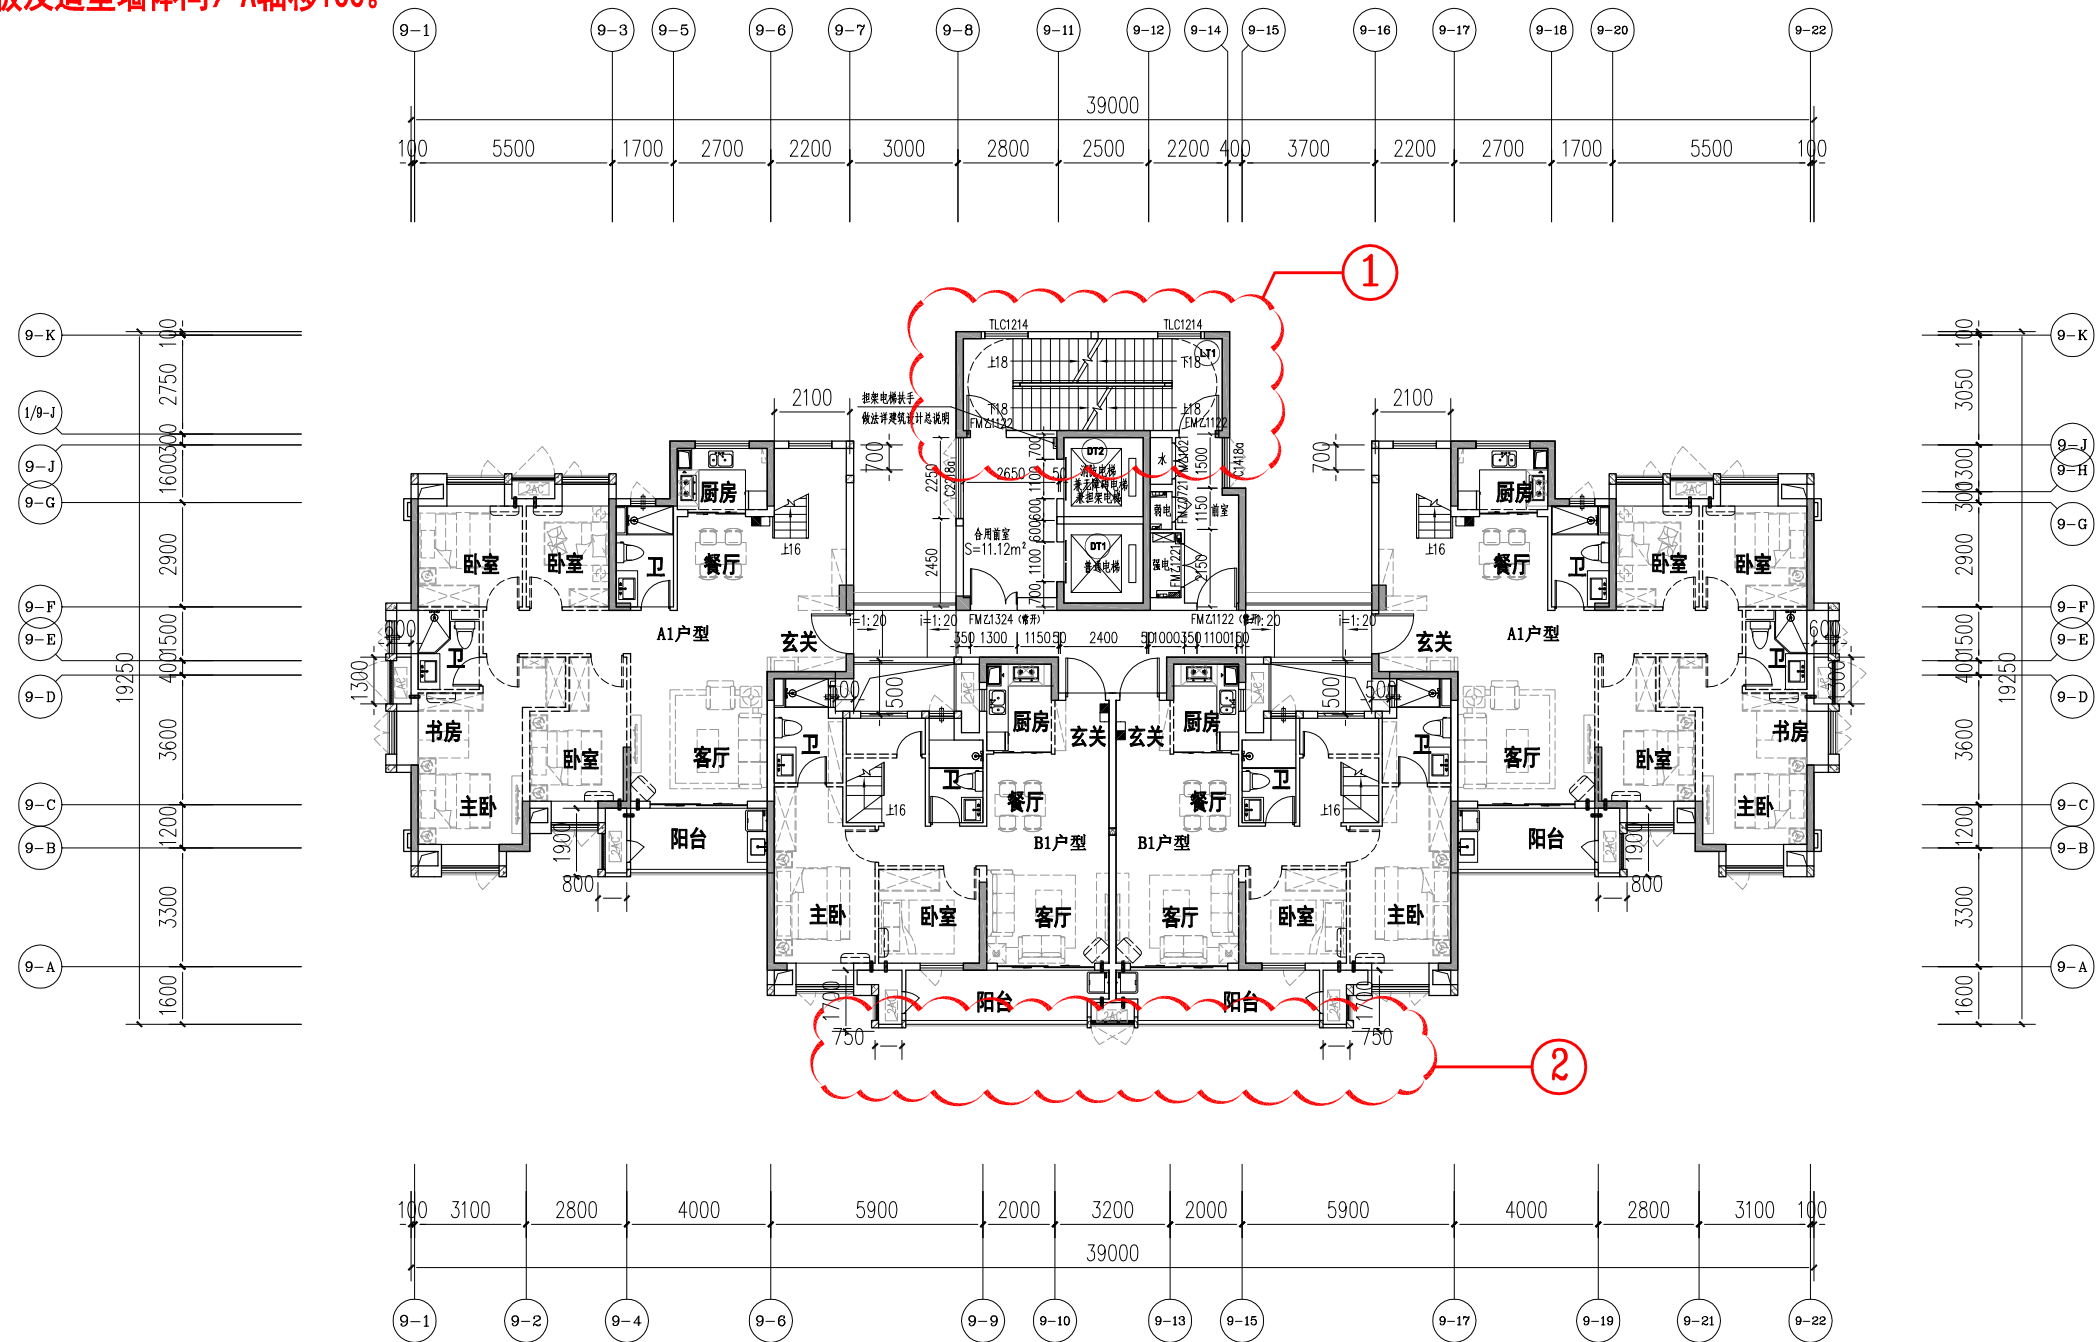

9#楼二十四层平面图 1:200

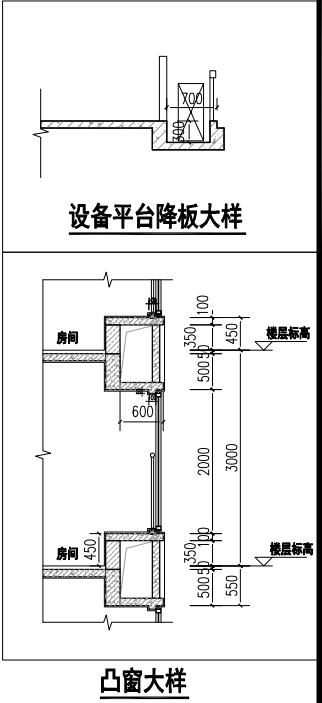


户型编号	户型	户型面积	户内面积	阳台水平投影面积	阳台面积	套内面积 (阳台+户内)	阳台占套内投影面积比例 (不含套内阳台)	公摊面积	公摊率	23+24层 面积(计容)
A1	4房3厅2卫	180.67	140.01	7.02	3.51	143.52	5.01%	37.15	20.56%	692.30
B1	2房3厅2卫	139.53	106.26	9.16	4.58	110.84	8.62%	28.69	20.56%	

9#楼二十五层平面图 变更后

变更内容:

- 1:层高由2.9m改为3.0m, 楼梯踏步相应修改。
- 2:此区域屋面底板向9-A轴移100。

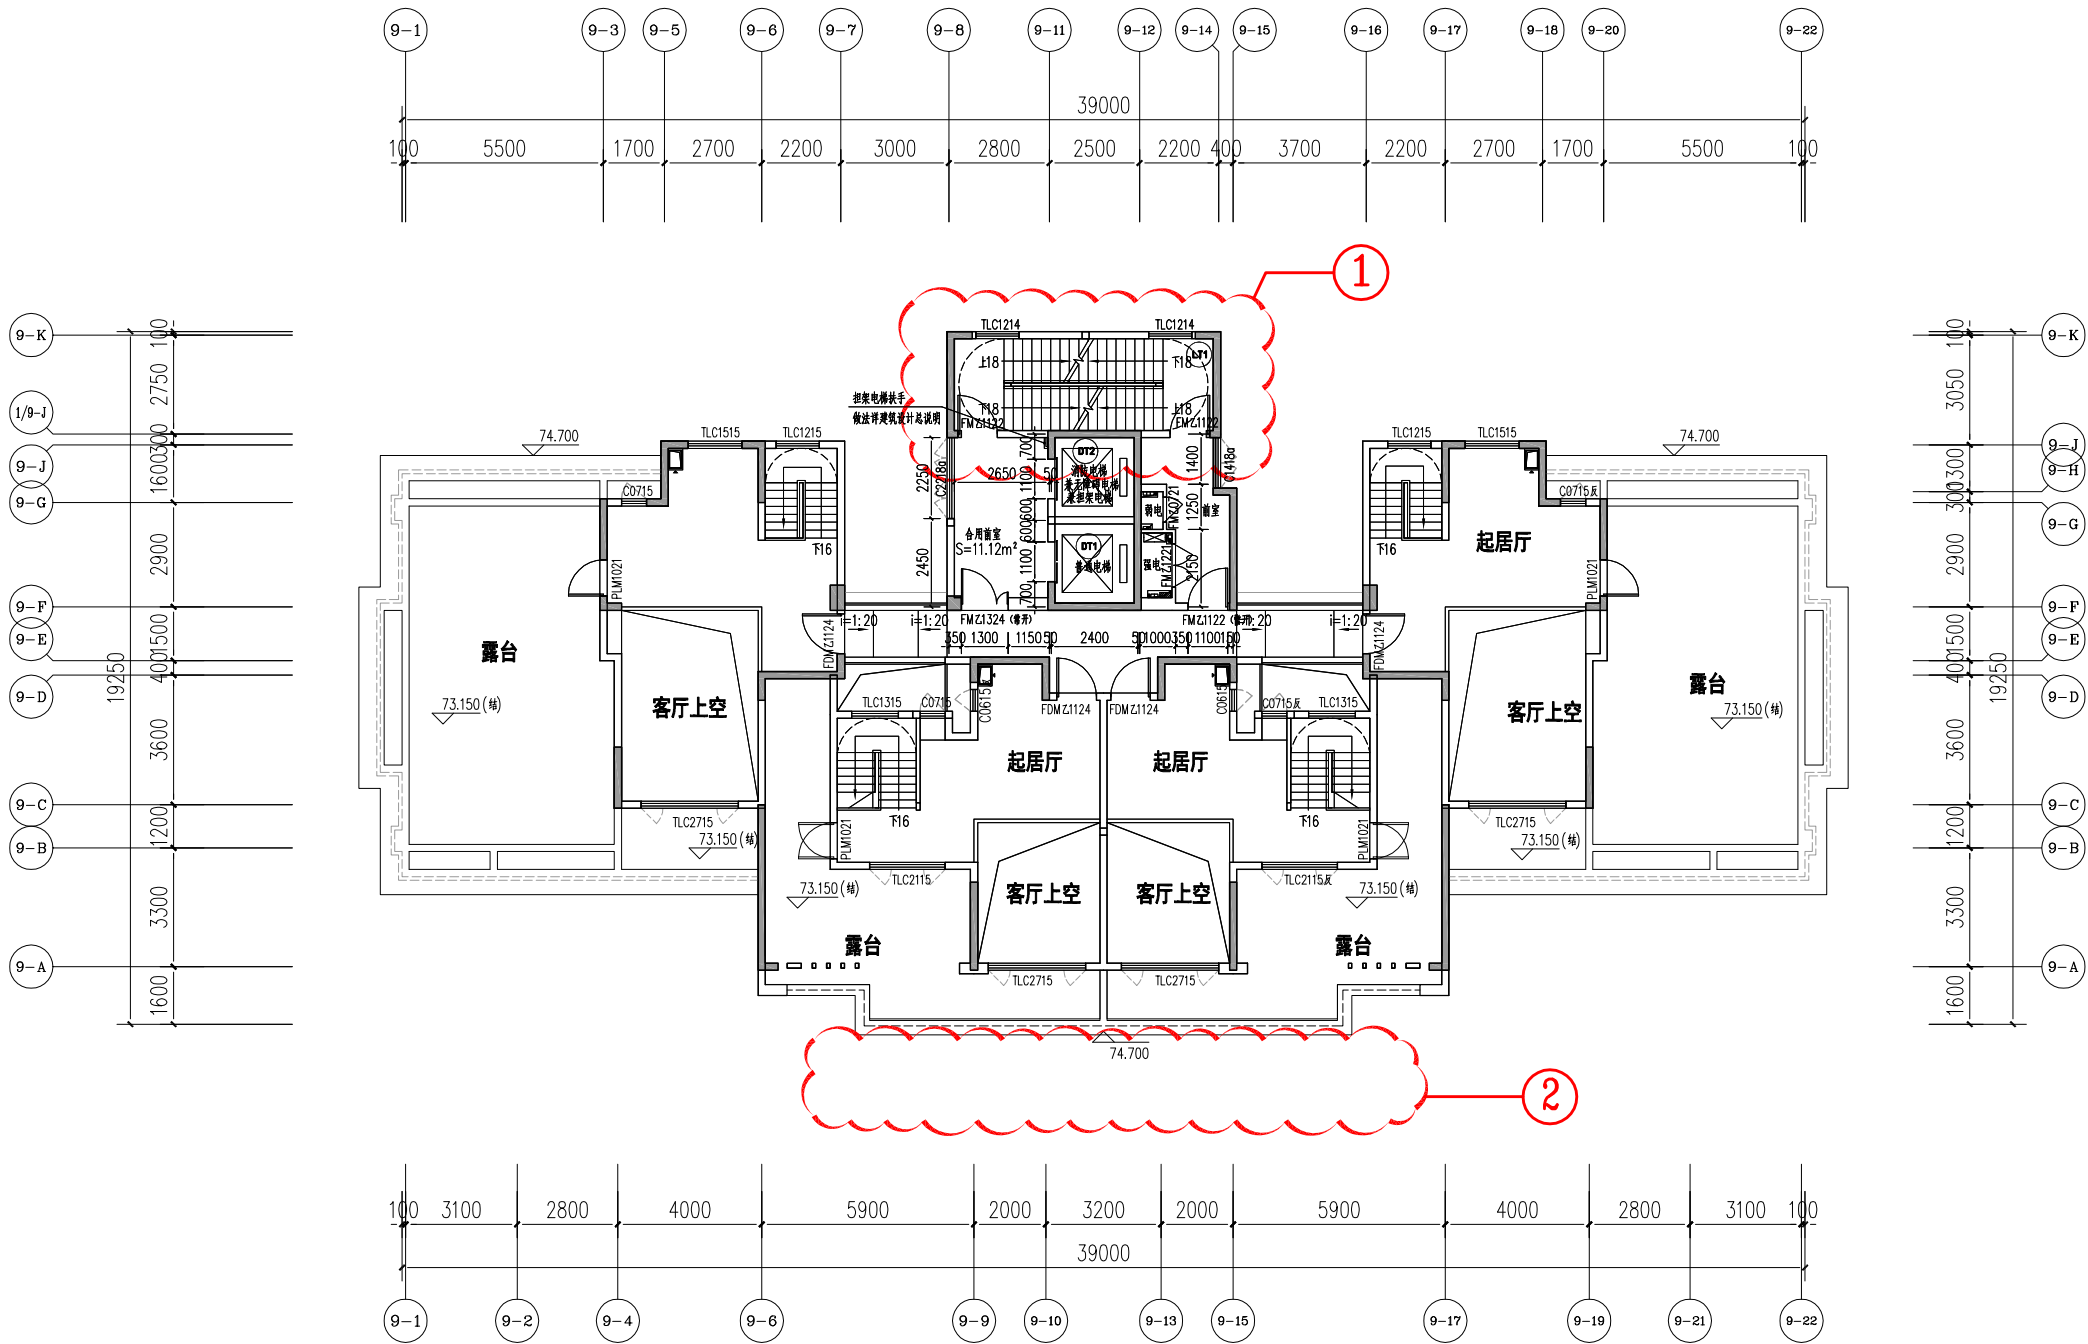


9#楼二十五层平面图 1:200

73.200

9#楼屋面层平面图 变更后

变更内容:

1:层高由2.9m改为3.0m, 楼梯踏步相应修改。

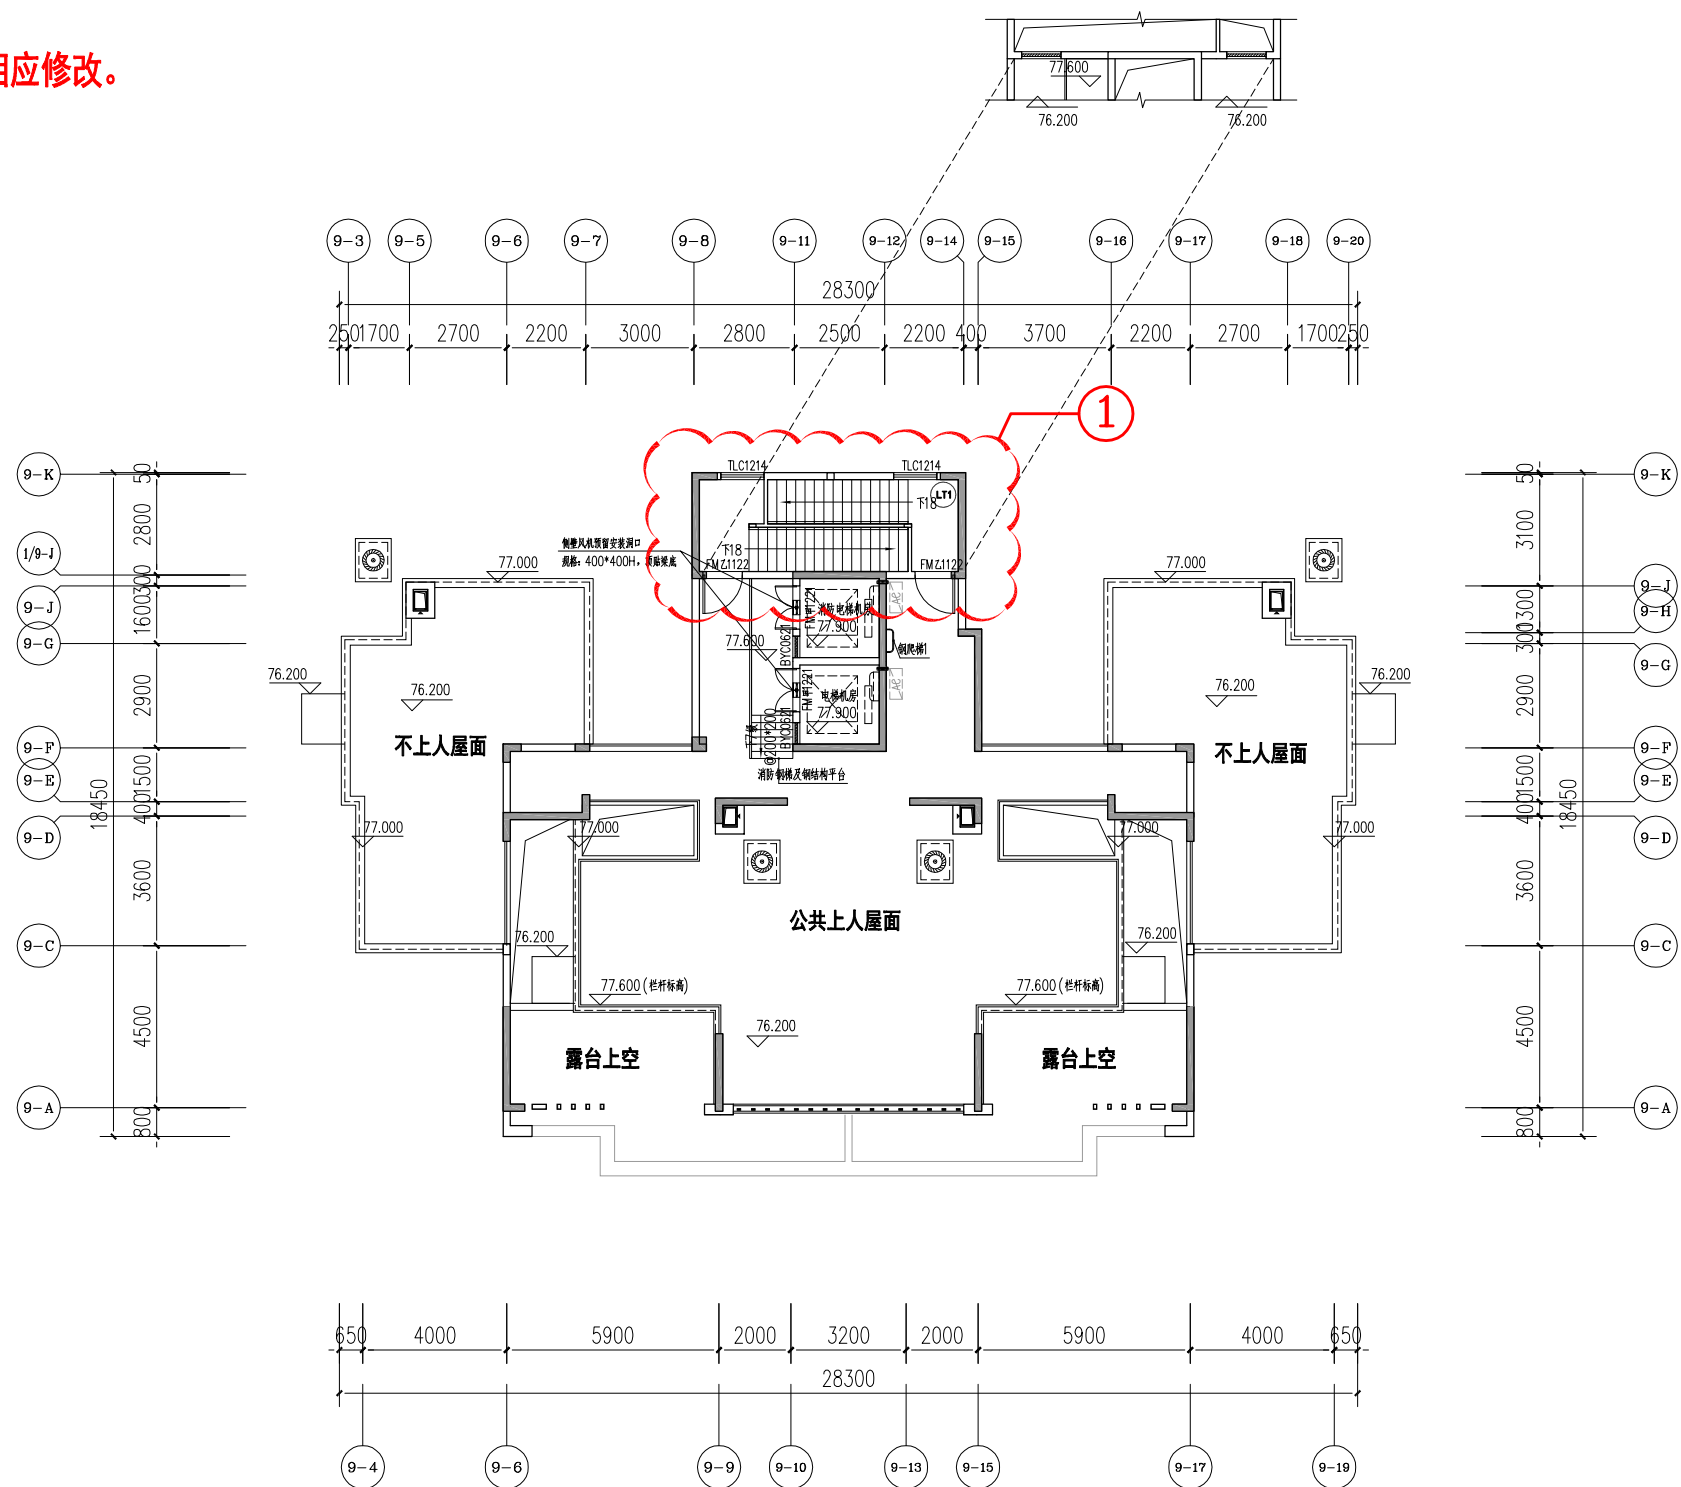

9#楼屋面层平面图 1:200


本层计容面积: 34.90m²

76.200

9#楼屋架层平面图 变更后

变更内容:

1:标准层层高由2.9m改为3.0m, 梯间层高由4.4m改为4.7m, 相应标高调整。

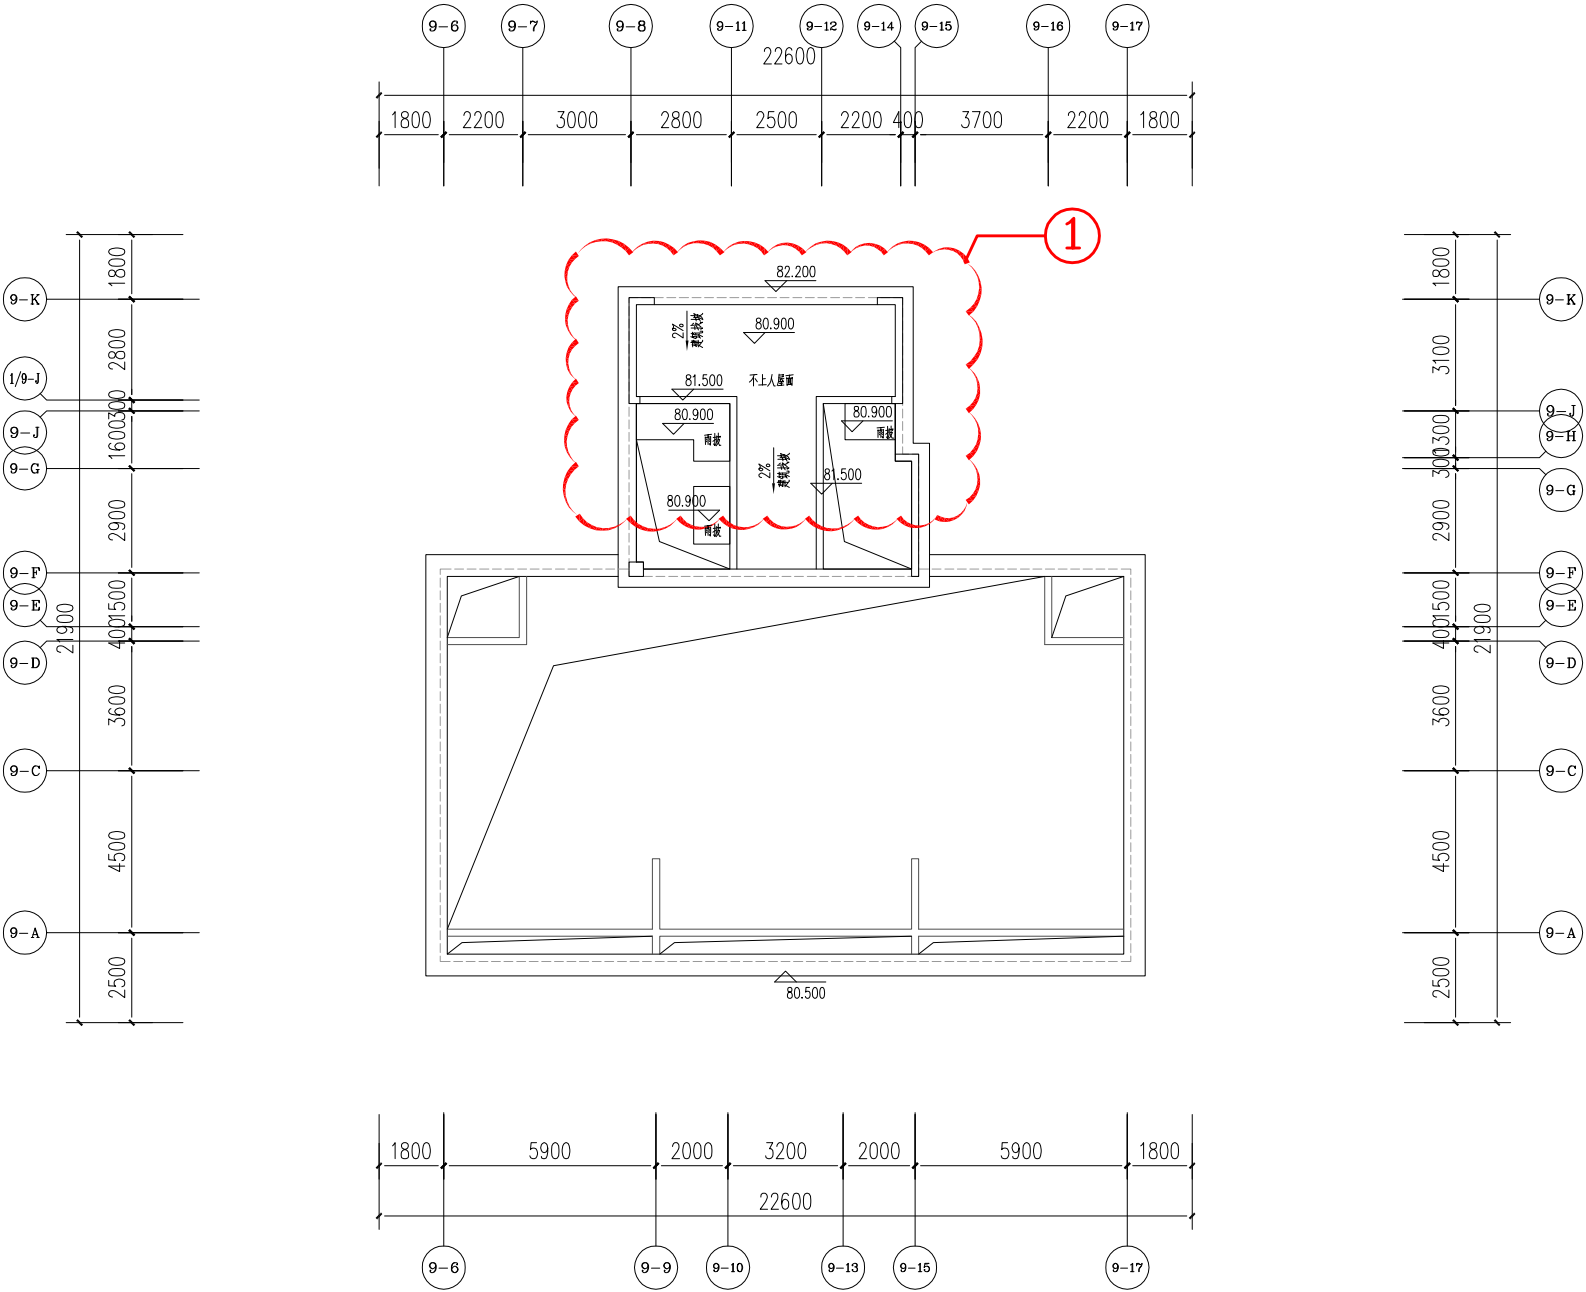


9#楼屋架层平面图 1:200

9#楼立面图变更后

变更内容:


1:一层层高由3.6米改为4.2米,二层至二十五层层高由2.9m改为3.0m,立面尺寸相应修改。

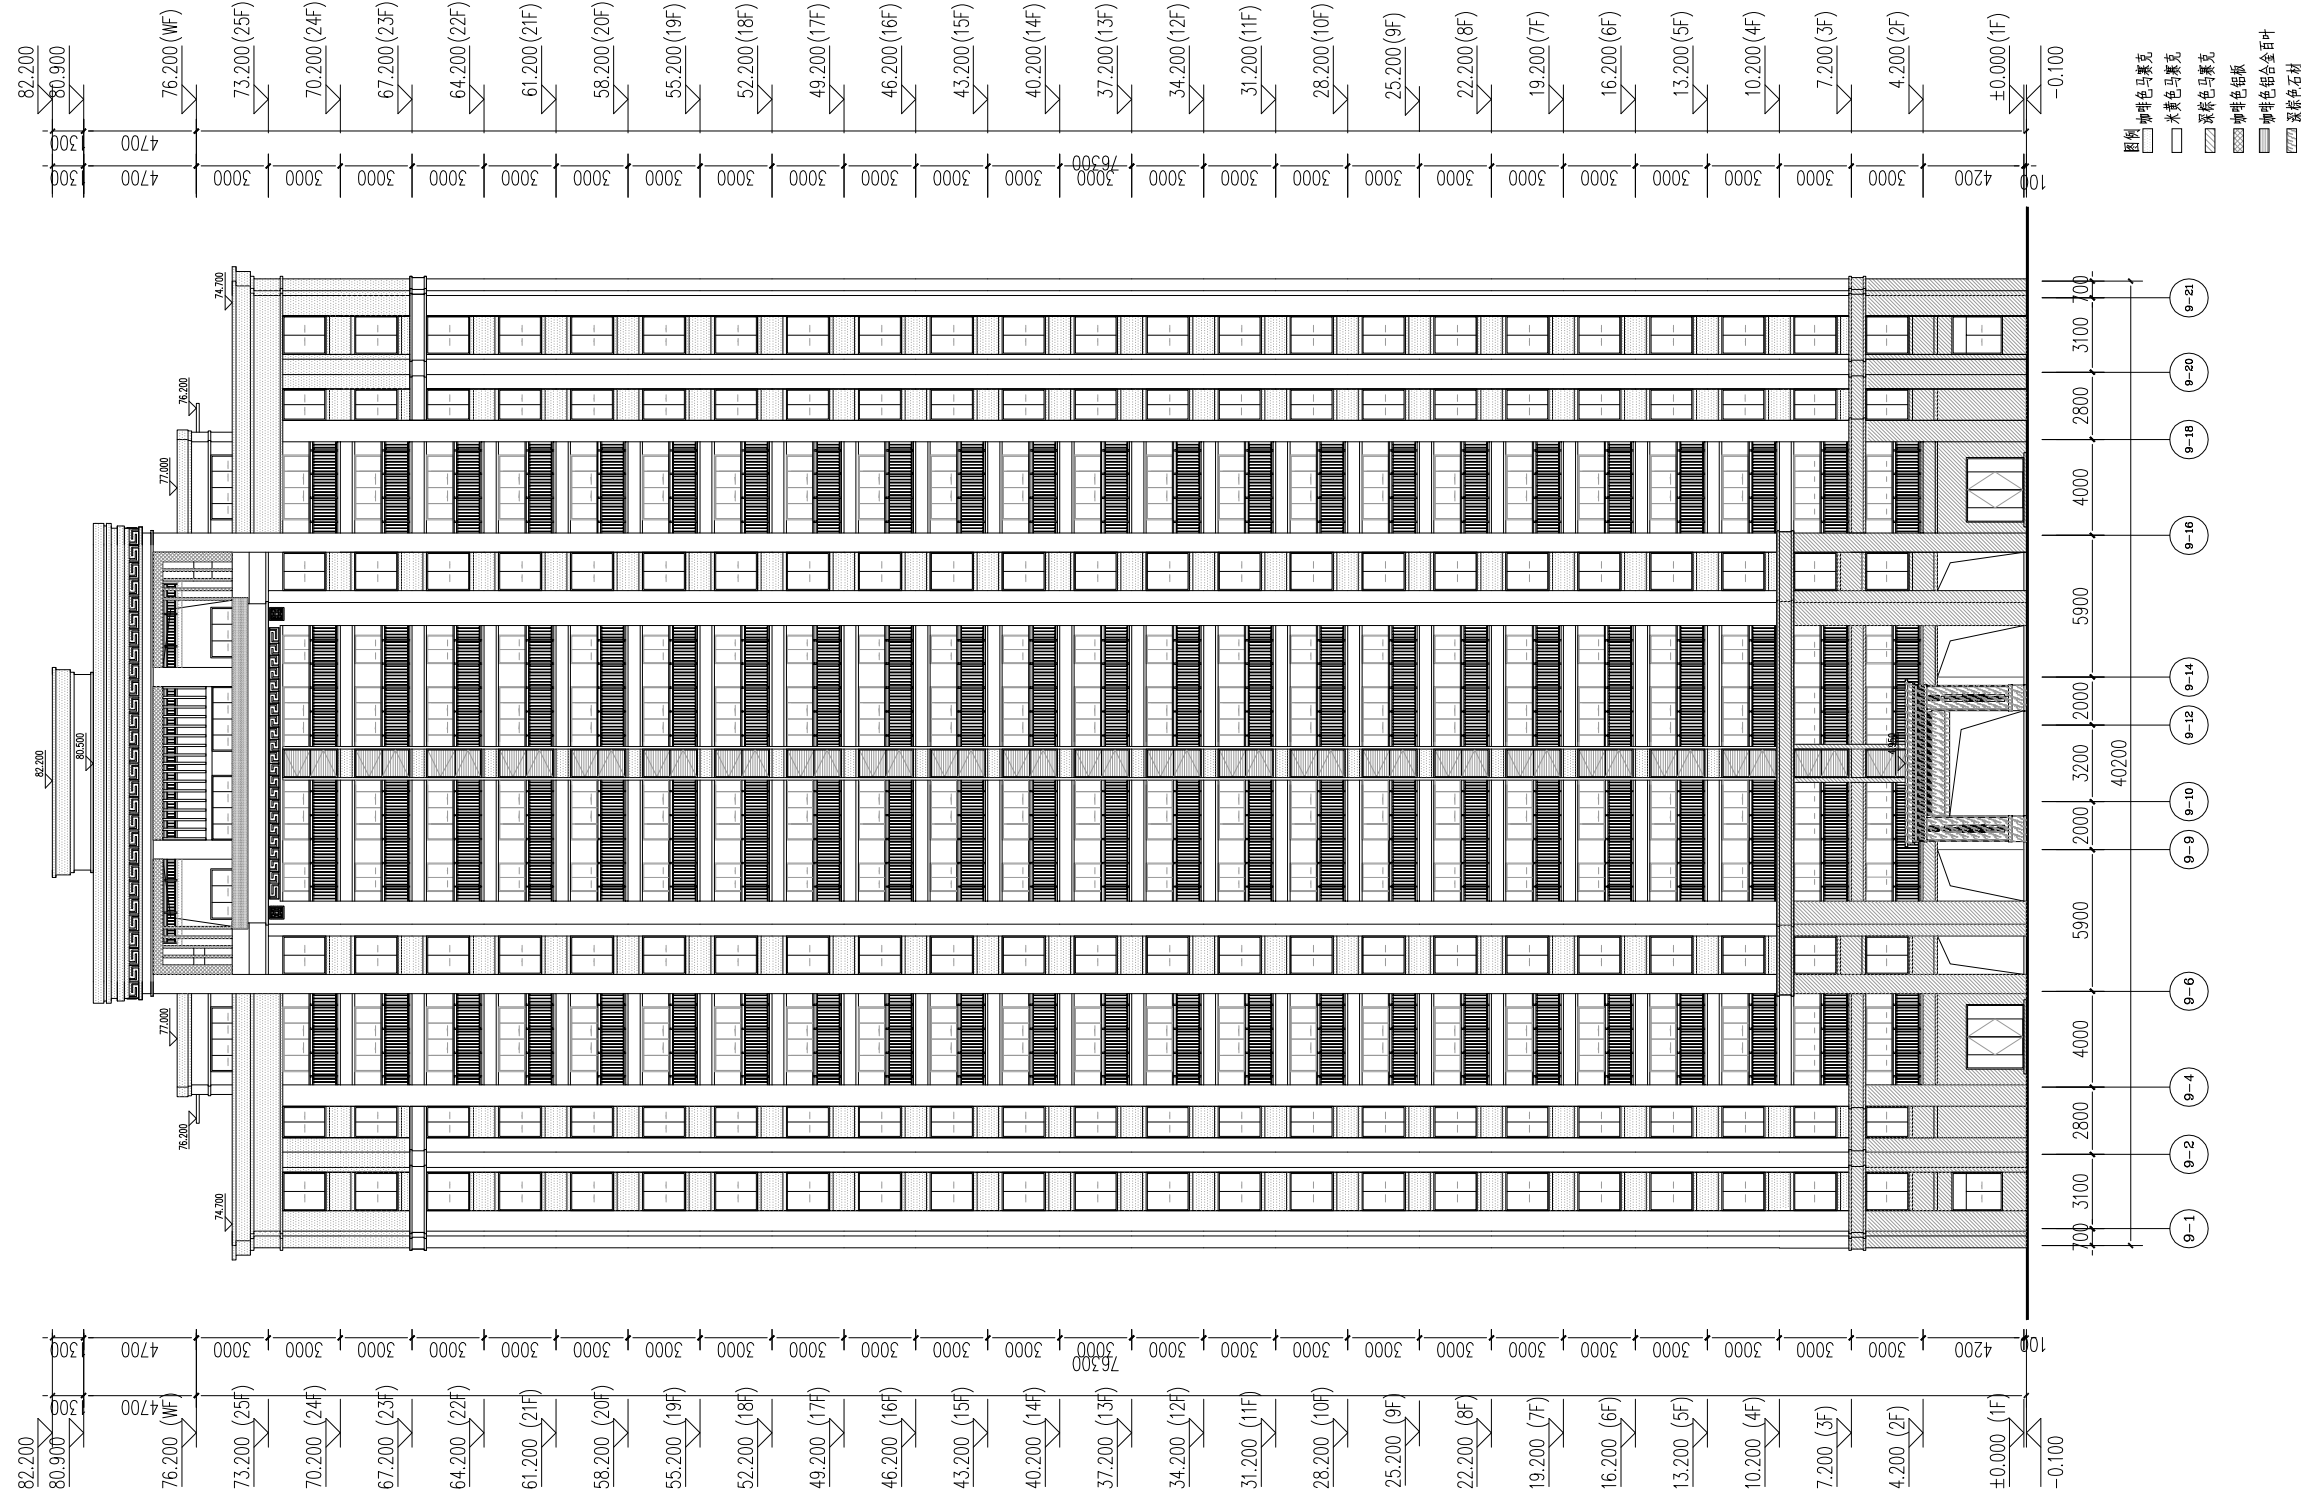

9#楼立面图 变更后

变更内容:

1:一层层高由3.6米改为4.2米，二层至二十五层层高由2.9m改为3.0m，立面尺寸相应修改。

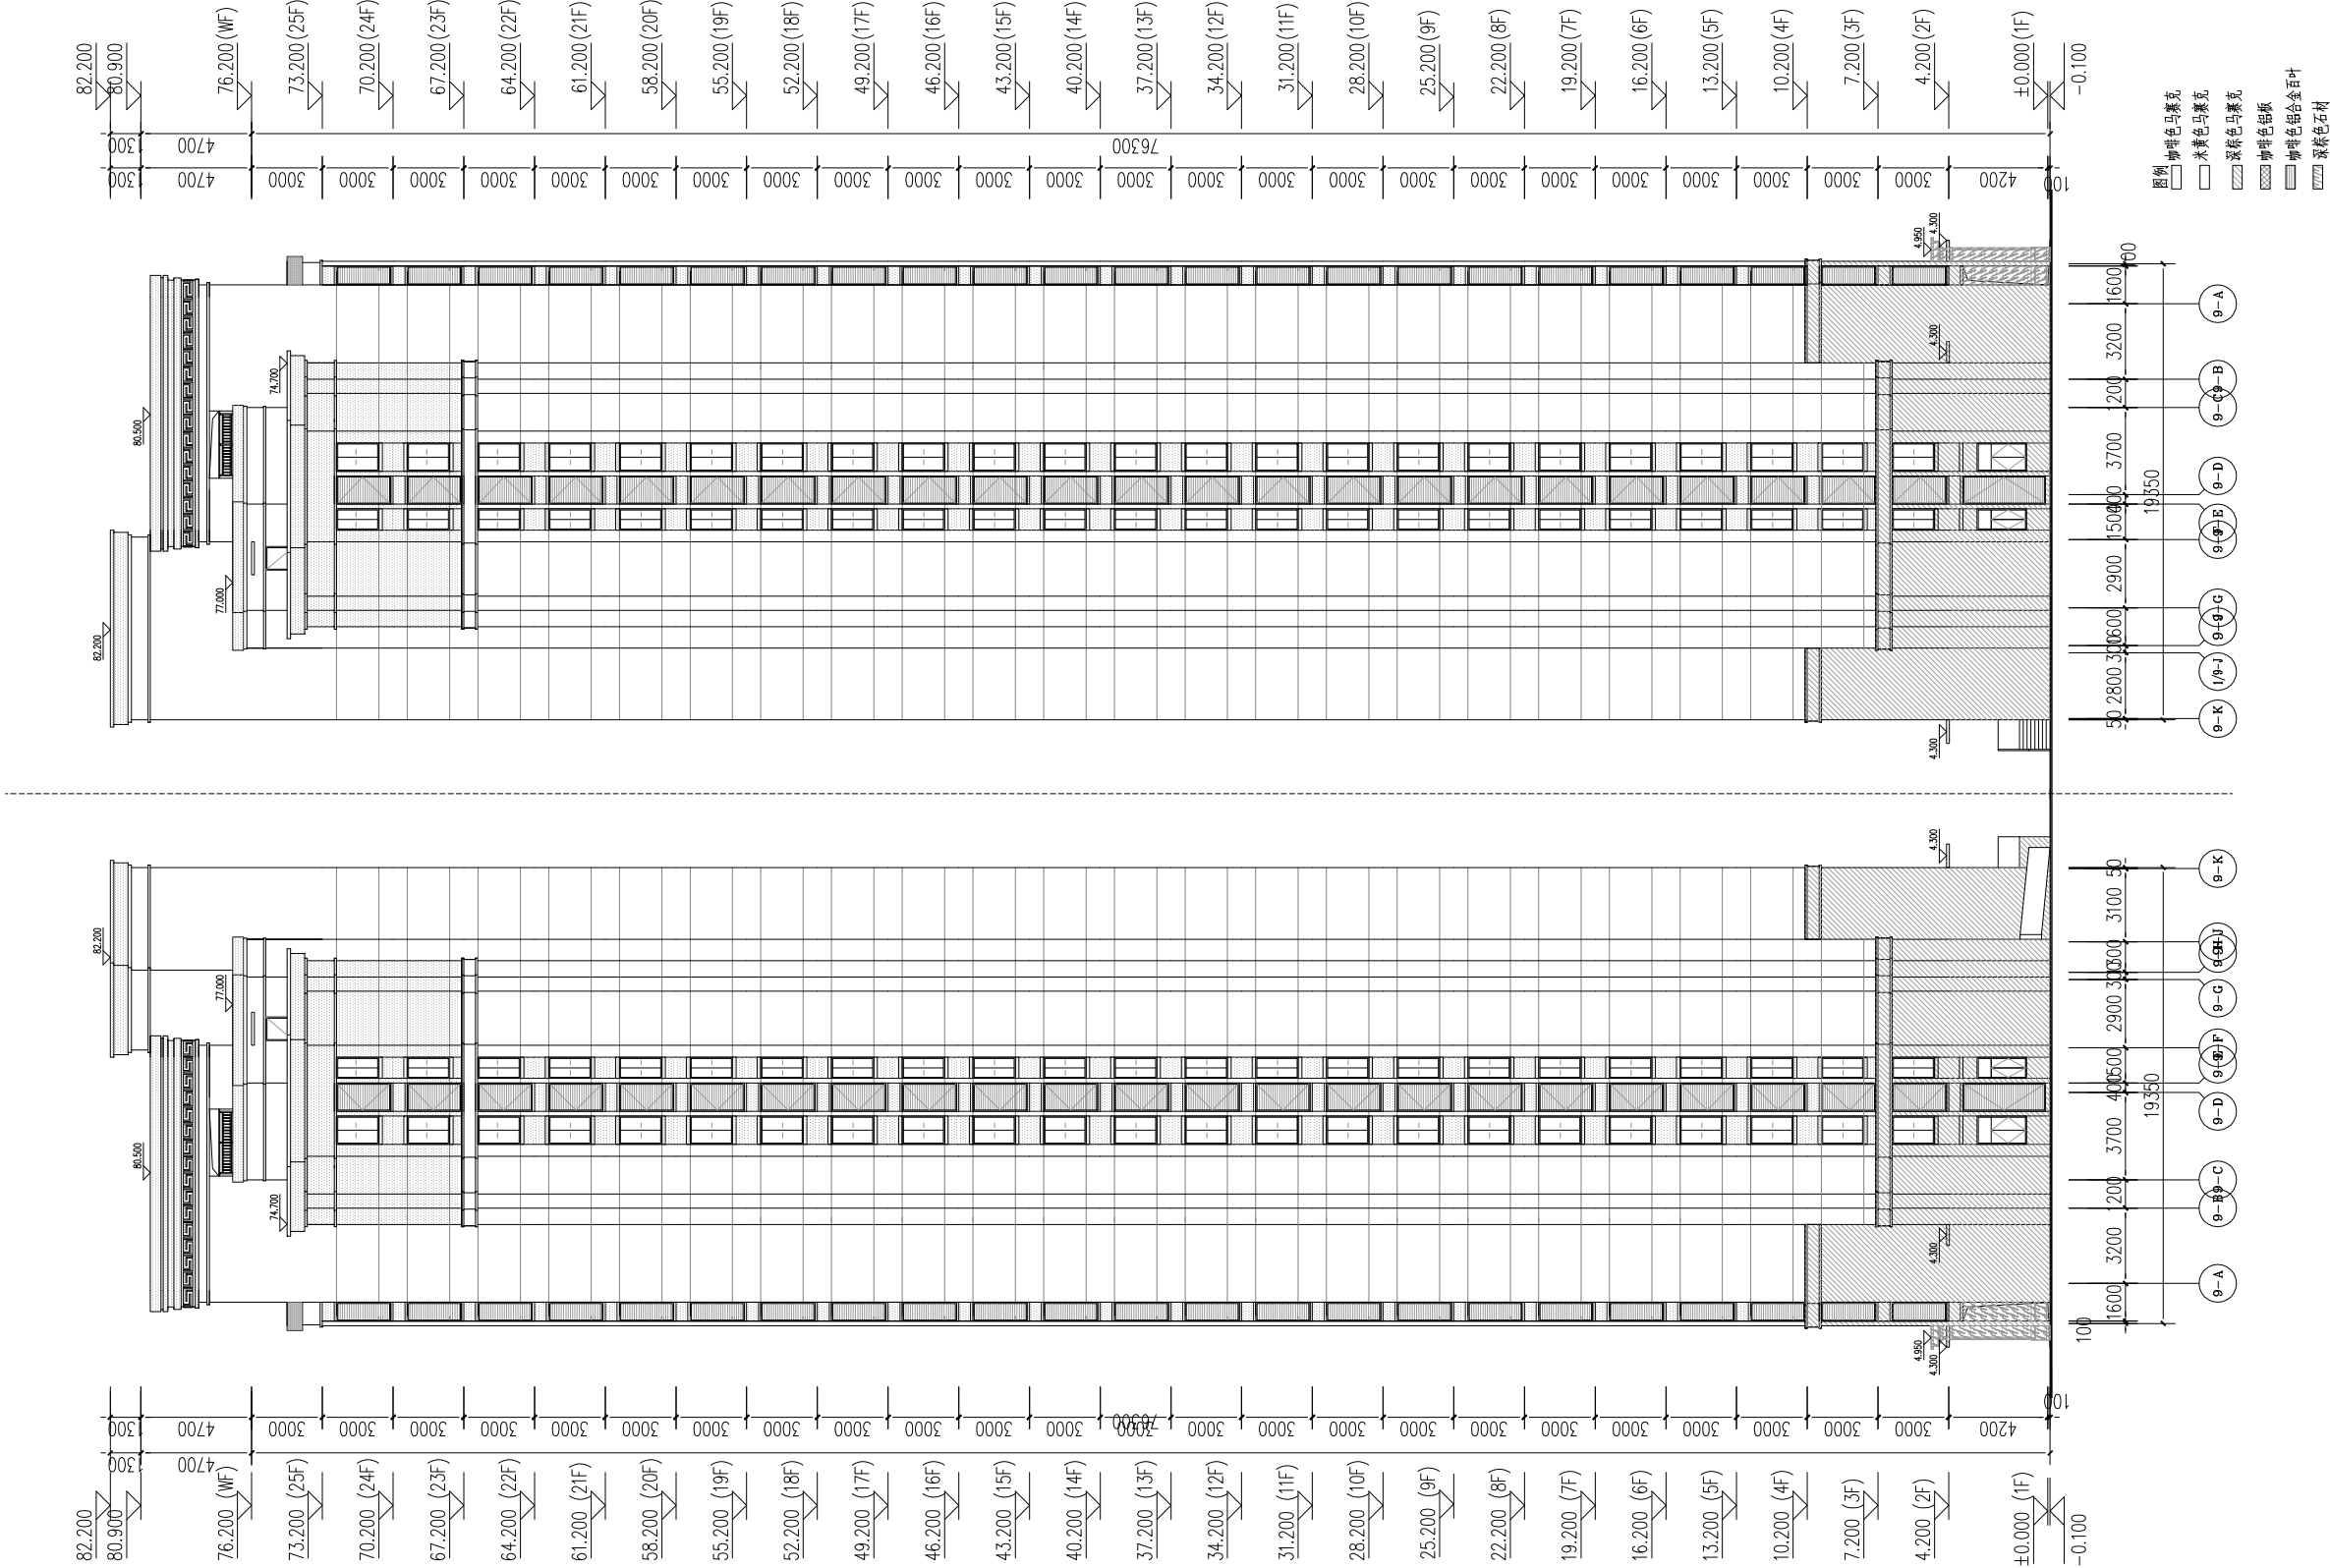


9-A ~ 9-K 轴立面图 1:300

9-A ~ 9-K 轴立面图 1:300



9#楼立面图 变更后

变更内容：
1:一层层高由3.6米改为4.2米，二层至二十五层层高由2.9m改为3.0m，剖面尺寸相应修改。

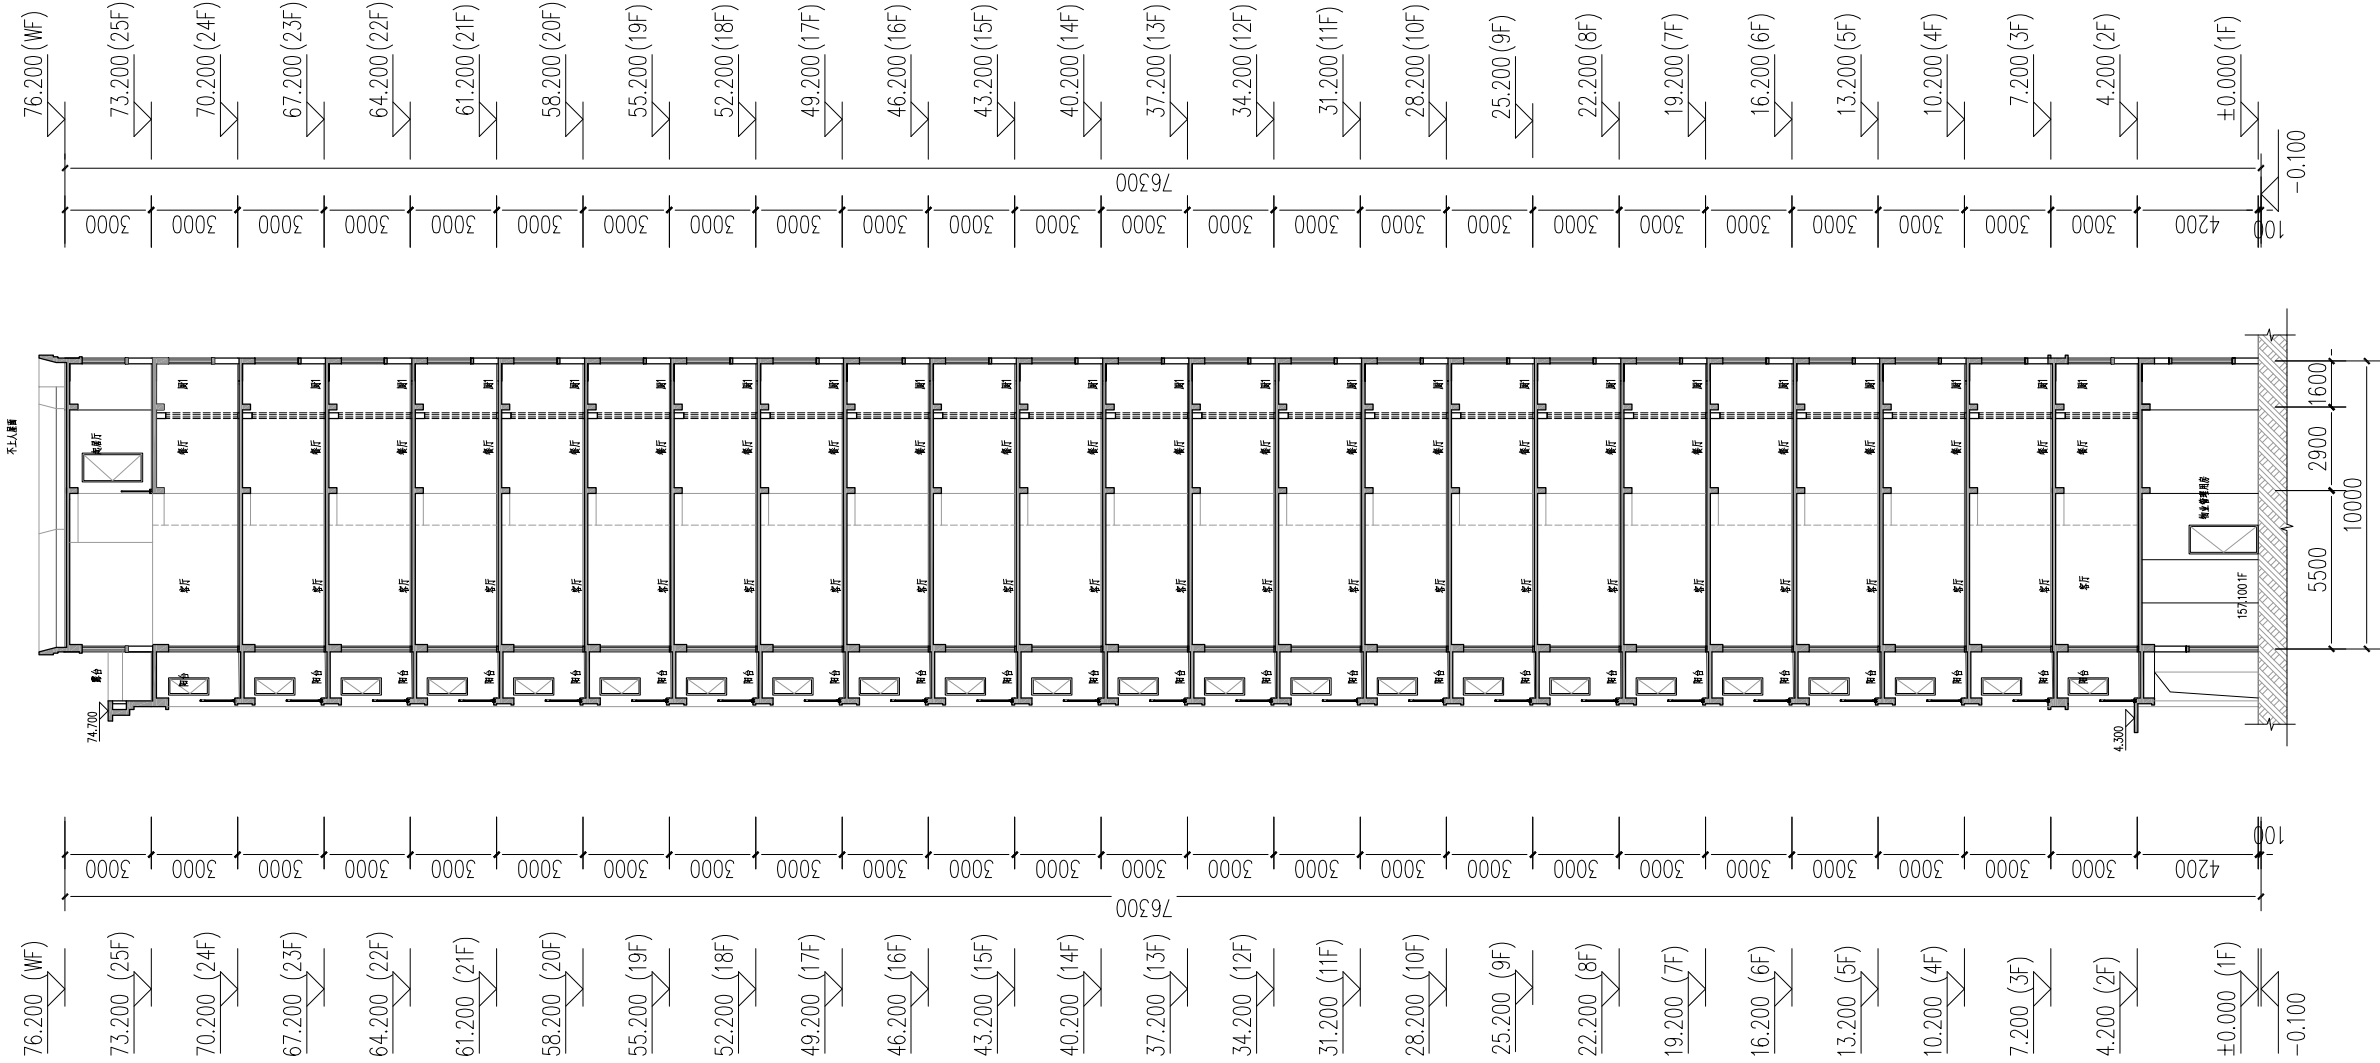

9#楼1-1剖面图 1:200



10#楼一层平面图 变更前

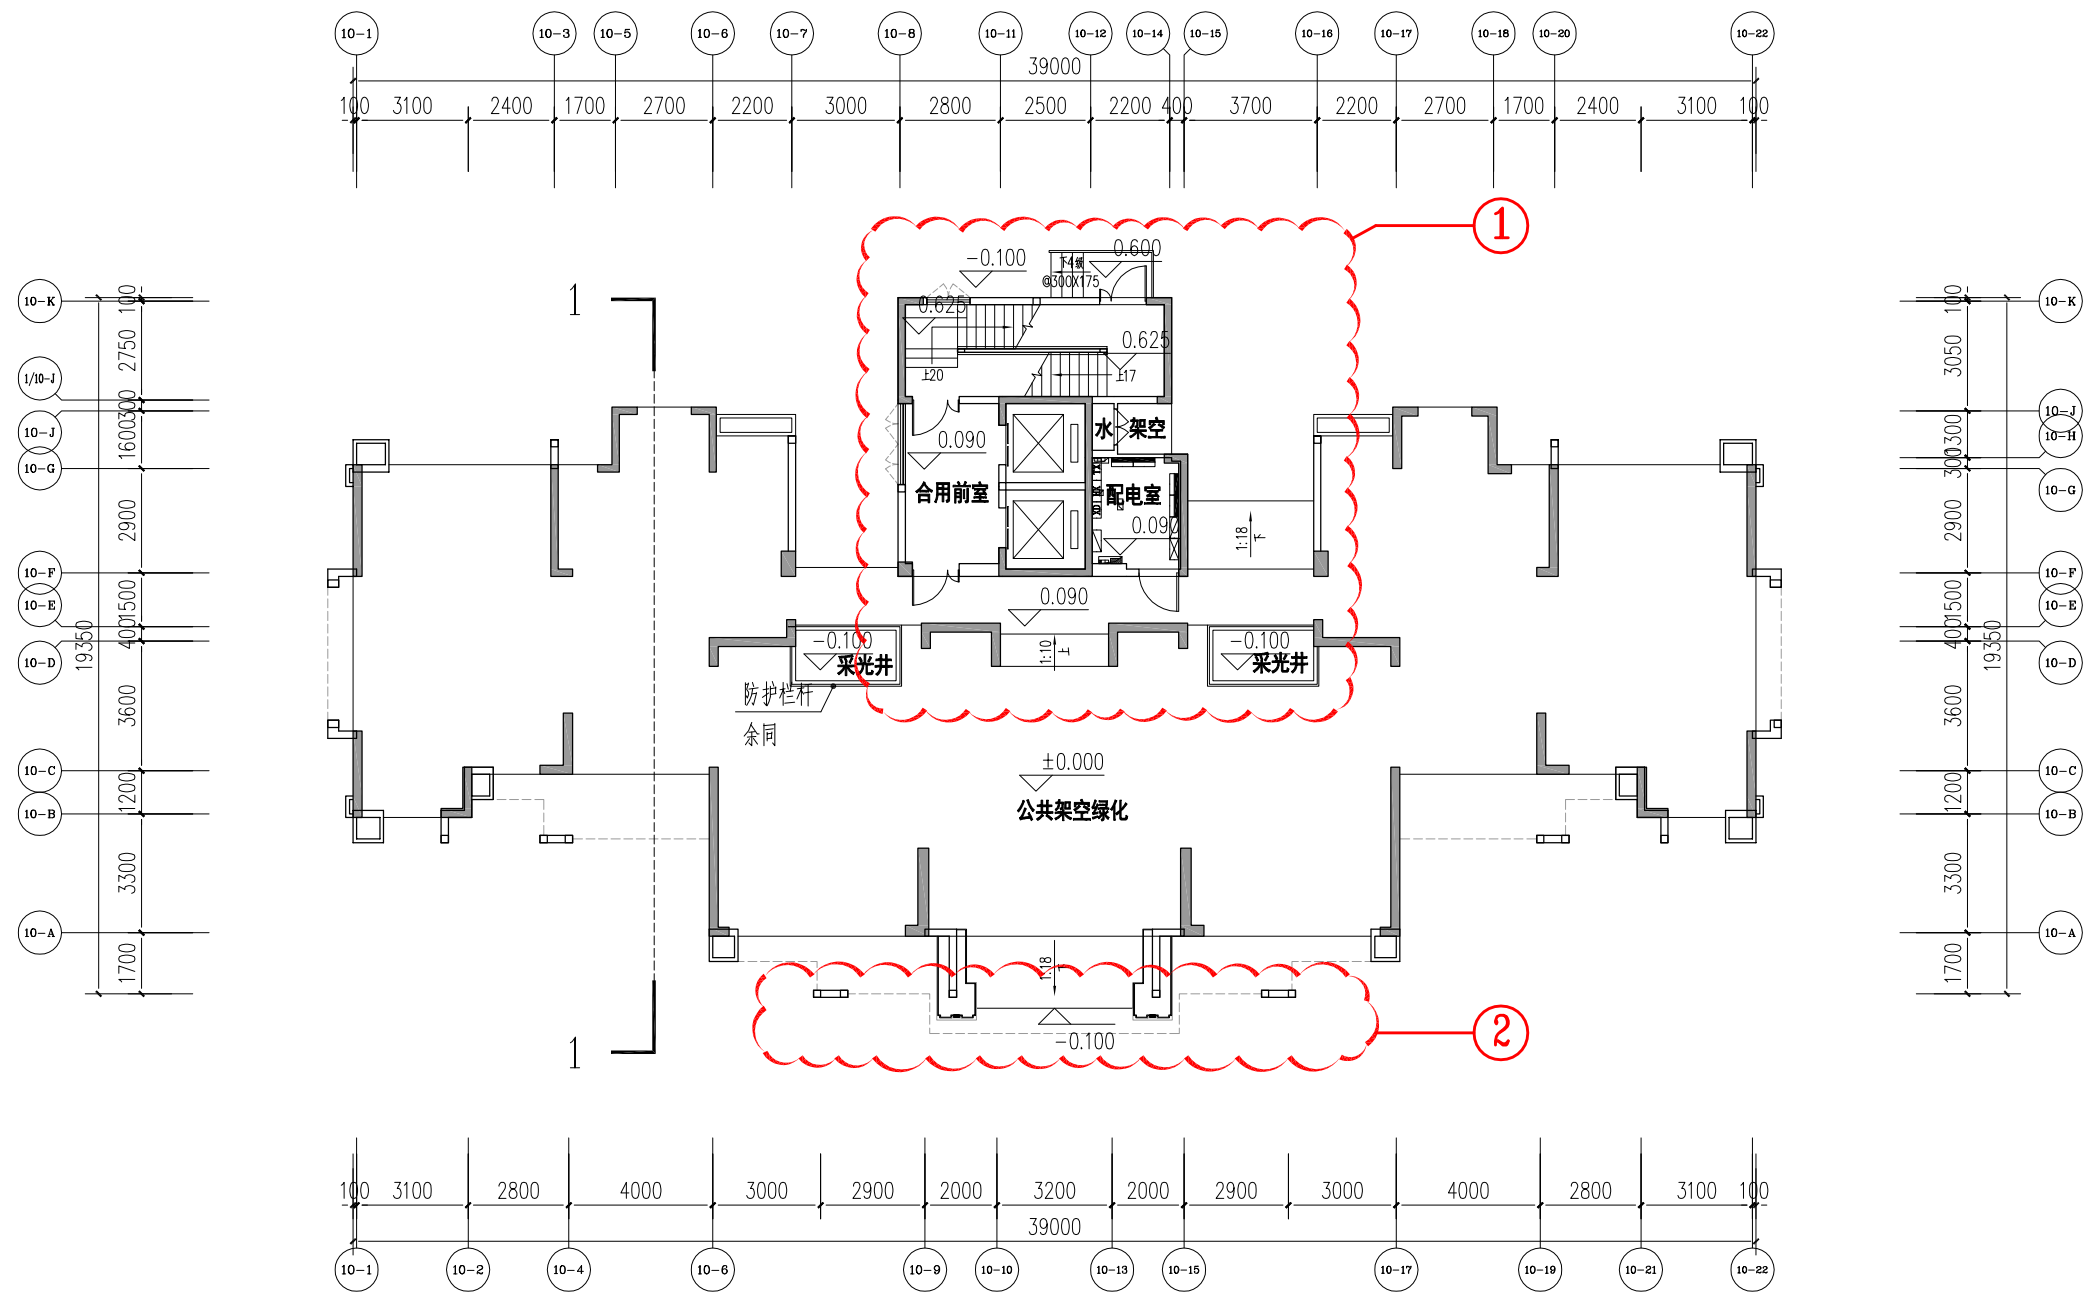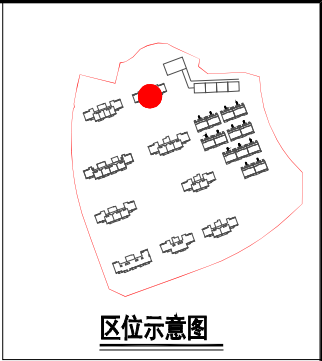

10#楼一层平面图 1:200 ±0.000 (158.00)

本栋计容面积: 10630.70m²
本层计容面积: 60.43m²
本层不计容架空面积: 400.97m²


10#楼二层平面图 变更前

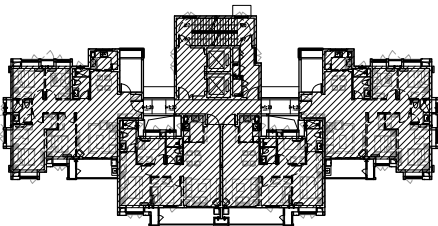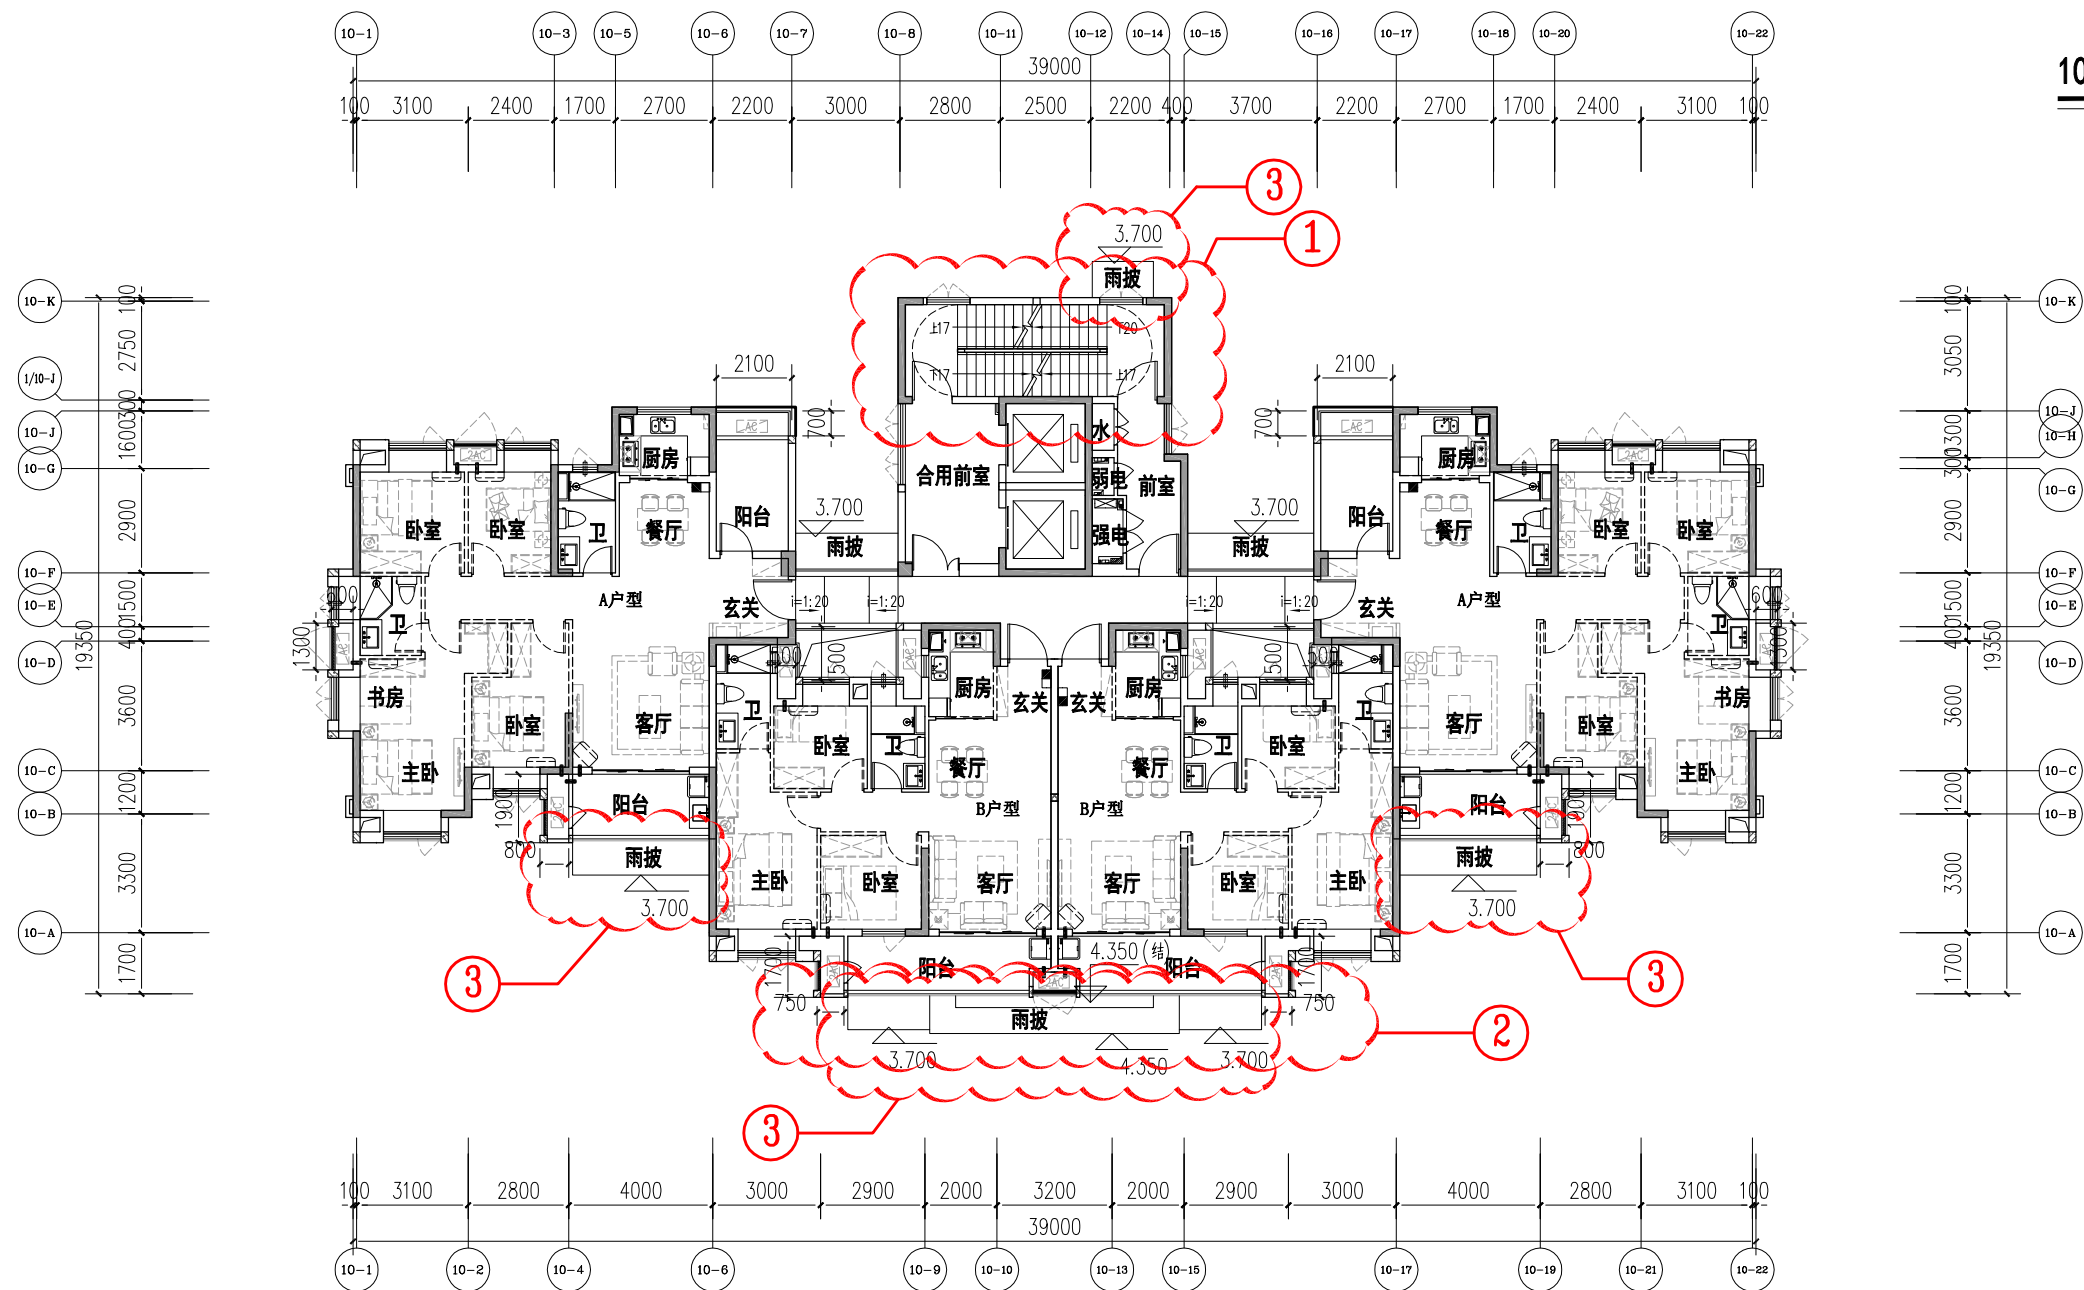


10#结构走向示意图

10#楼二层平面图 1:200

户型编号	户型	户型面积	户内面积	阳台水平投影面积	阳台面积	套内面积 (阳台+户内)	阳台占套内投影面积比例 (不含套内阳台)	公摊面积	公摊率	本层面积 (计容)
A	4房2厅2卫	128.39	98.01	14.00	7.00	105.01	14.28%	23.38	18.21%	446.12
B	3房2厅2卫	90.23	69.22	9.16	4.58	73.80	13.23%	16.43	18.21%	

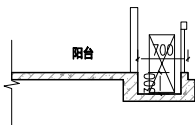


设备平台降板大样

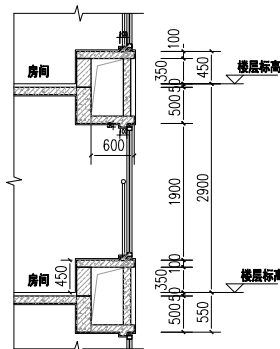


凸窗大样

10#楼三、四层平面图 变更前

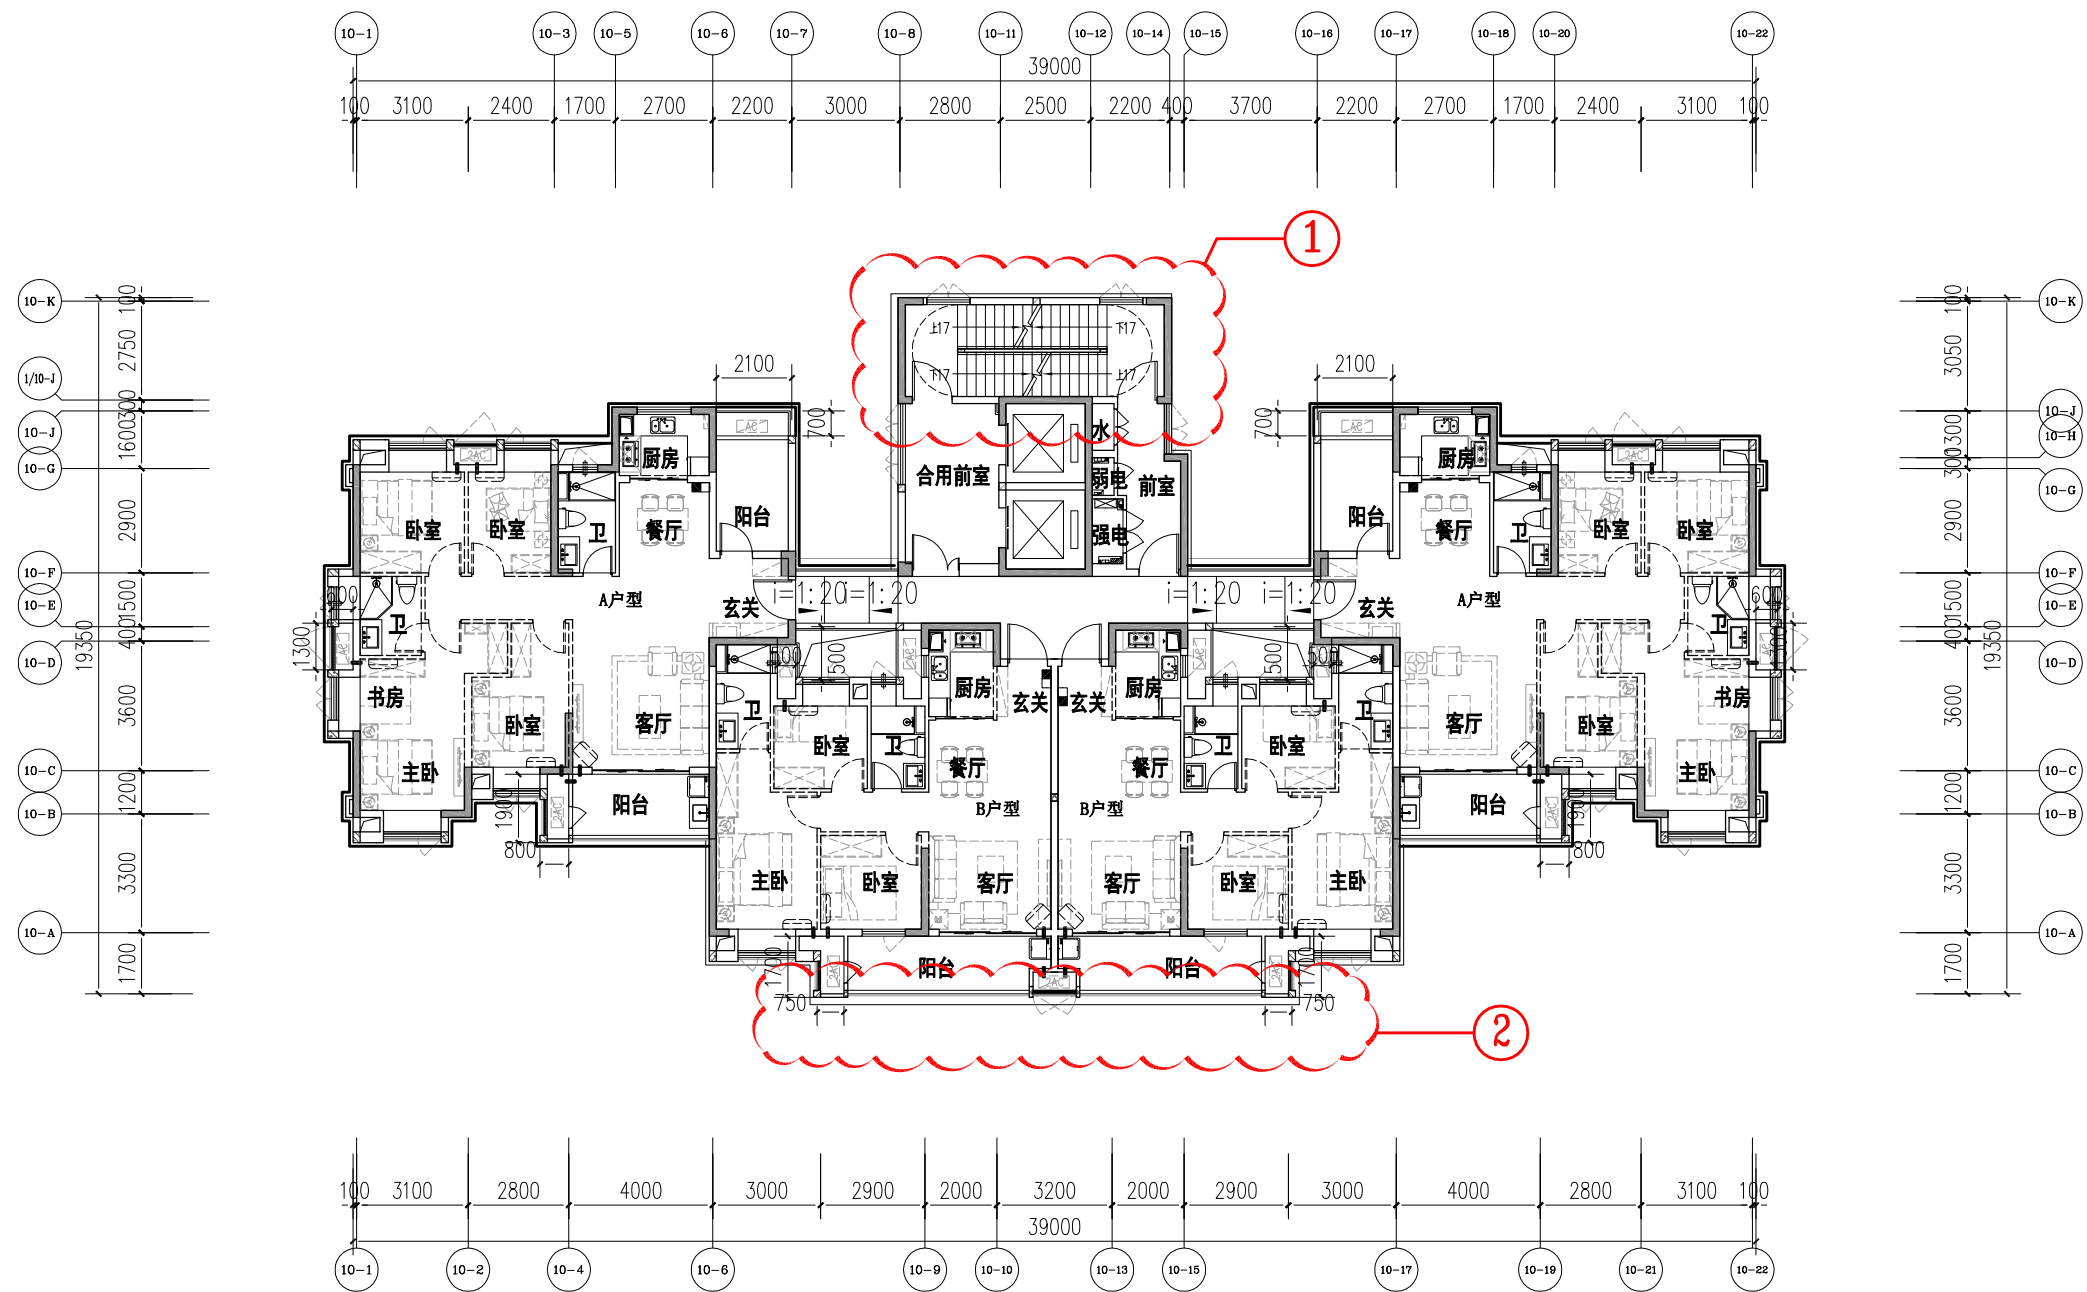


10#楼三、四层平面图 1:200 (9.400) 4F 6.500 3F

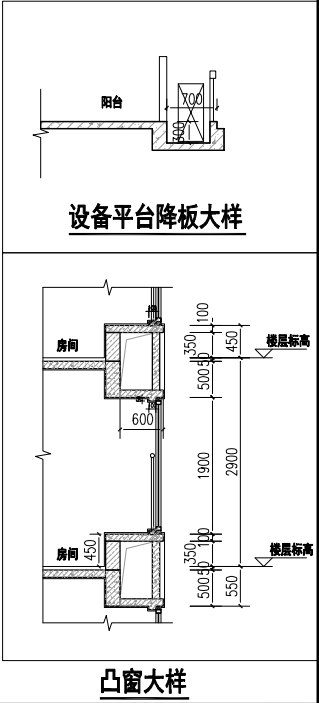

户型编号	户型	户型面积	户内面积	阳台水平投影面积	阳台面积	套内面积 (阳台+户内)	阳台占套内投影面积比例 (不含套内阳台)	公摊面积	公摊率	本层面积 (计容)
A	4房2厅2卫	128.39	98.01	14.00	7.00	105.01	14.28%	23.38	18.21%	446.12
B	3房2厅2卫	90.23	69.22	9.16	4.58	73.80	13.23%	16.43	18.21%	


10#楼五至二十三层平面图 变更前

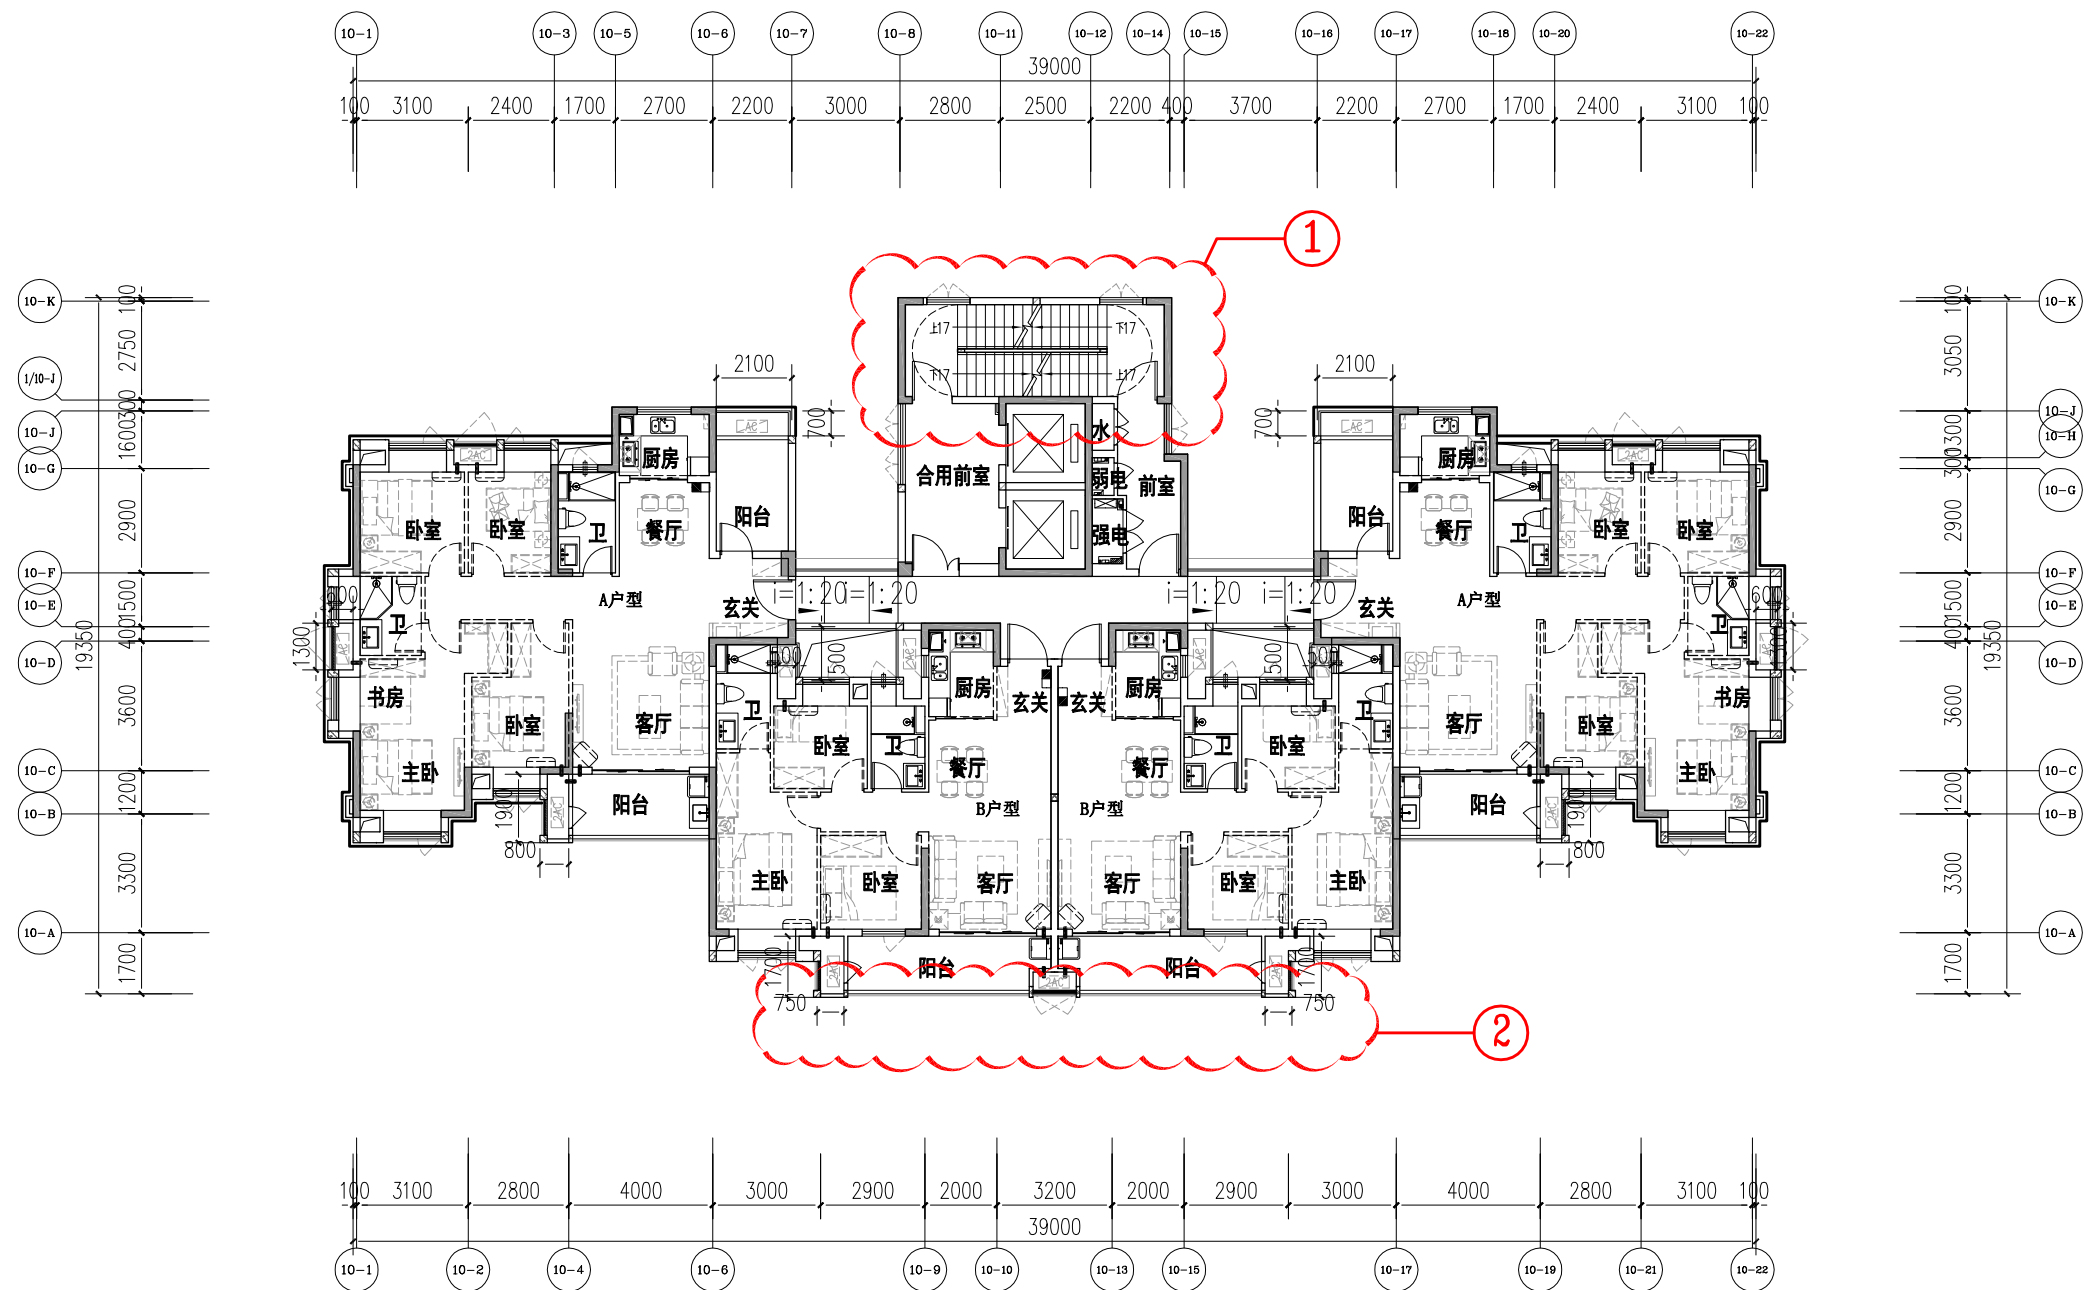


10#楼五至二十三层平面图 1:200

64.500 (23F)
~
12.300 (5F)


户型编号	户型	户型面积	户内面积	阳台水平投影面积	阳台面积	套内面积 (阳台+户内)	阳台占套内投影面积比例 (不含套内阳台)	公摊面积	公摊率	本层面积 (计容)
A	4房2厅2卫	128.39	98.01	14.00	7.00	105.01	14.28%	23.38	18.21%	446.12
B	3房2厅2卫	90.23	69.22	9.16	4.58	73.80	13.23%	16.43	18.21%	

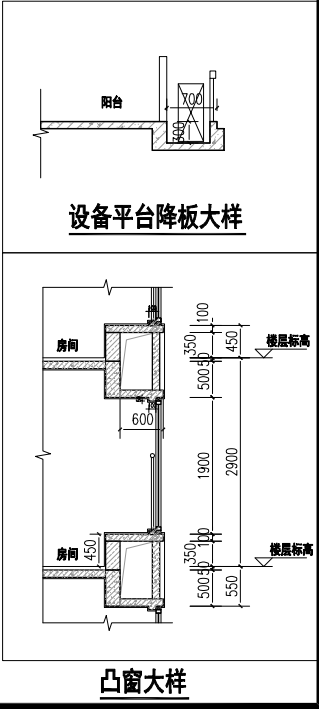

10#楼二十四层平面图 变更前

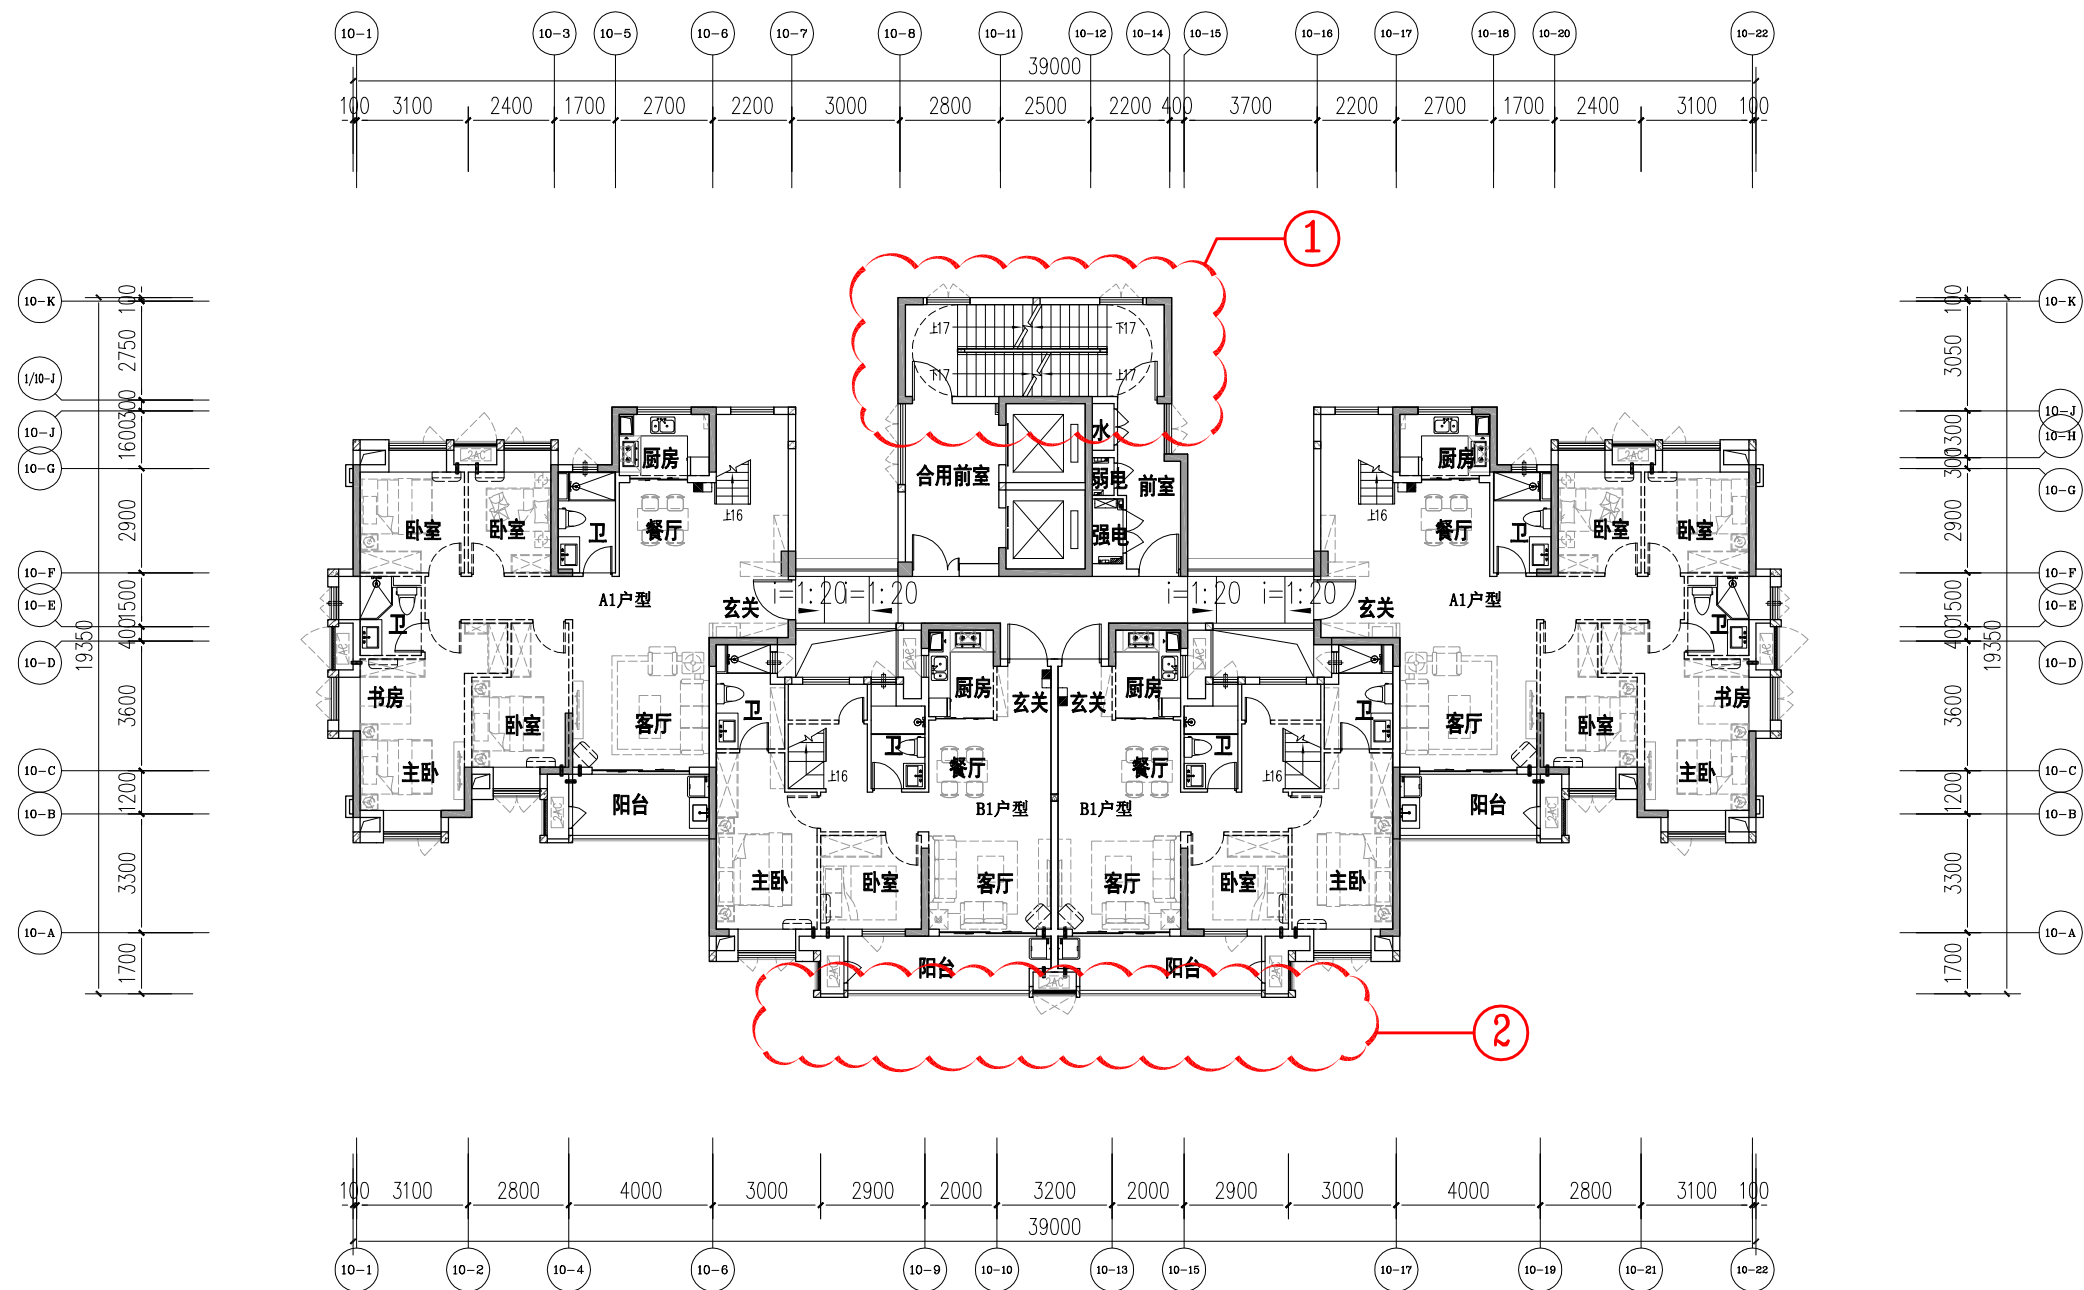


10#楼二十四层平面图 1:200 67.400

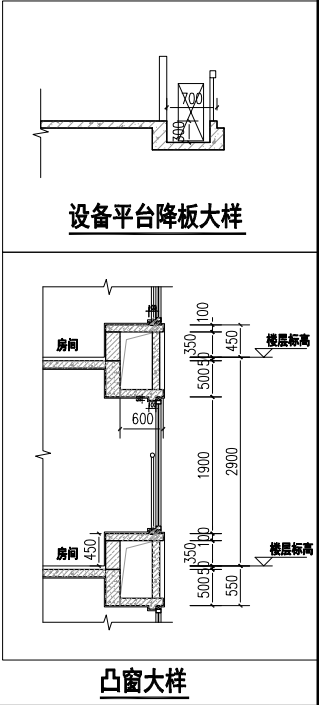

户型编号	户型	户型面积	户内面积	阳台水平投影面积	阳台面积	套内面积 (阳台+户内)	阳台占套内投影面积比例 (不含套内阳台)	公摊面积	公摊率	23+24层 面积(计容)
A1	4房3厅2卫	180.67	140.01	7.02	3.51	143.52	5.01%	37.15	20.56%	692.30
B1	2房3厅2卫	139.53	106.26	9.16	4.58	110.84	8.62%	28.69	20.56%	


10#楼二十五层平面图 变更前

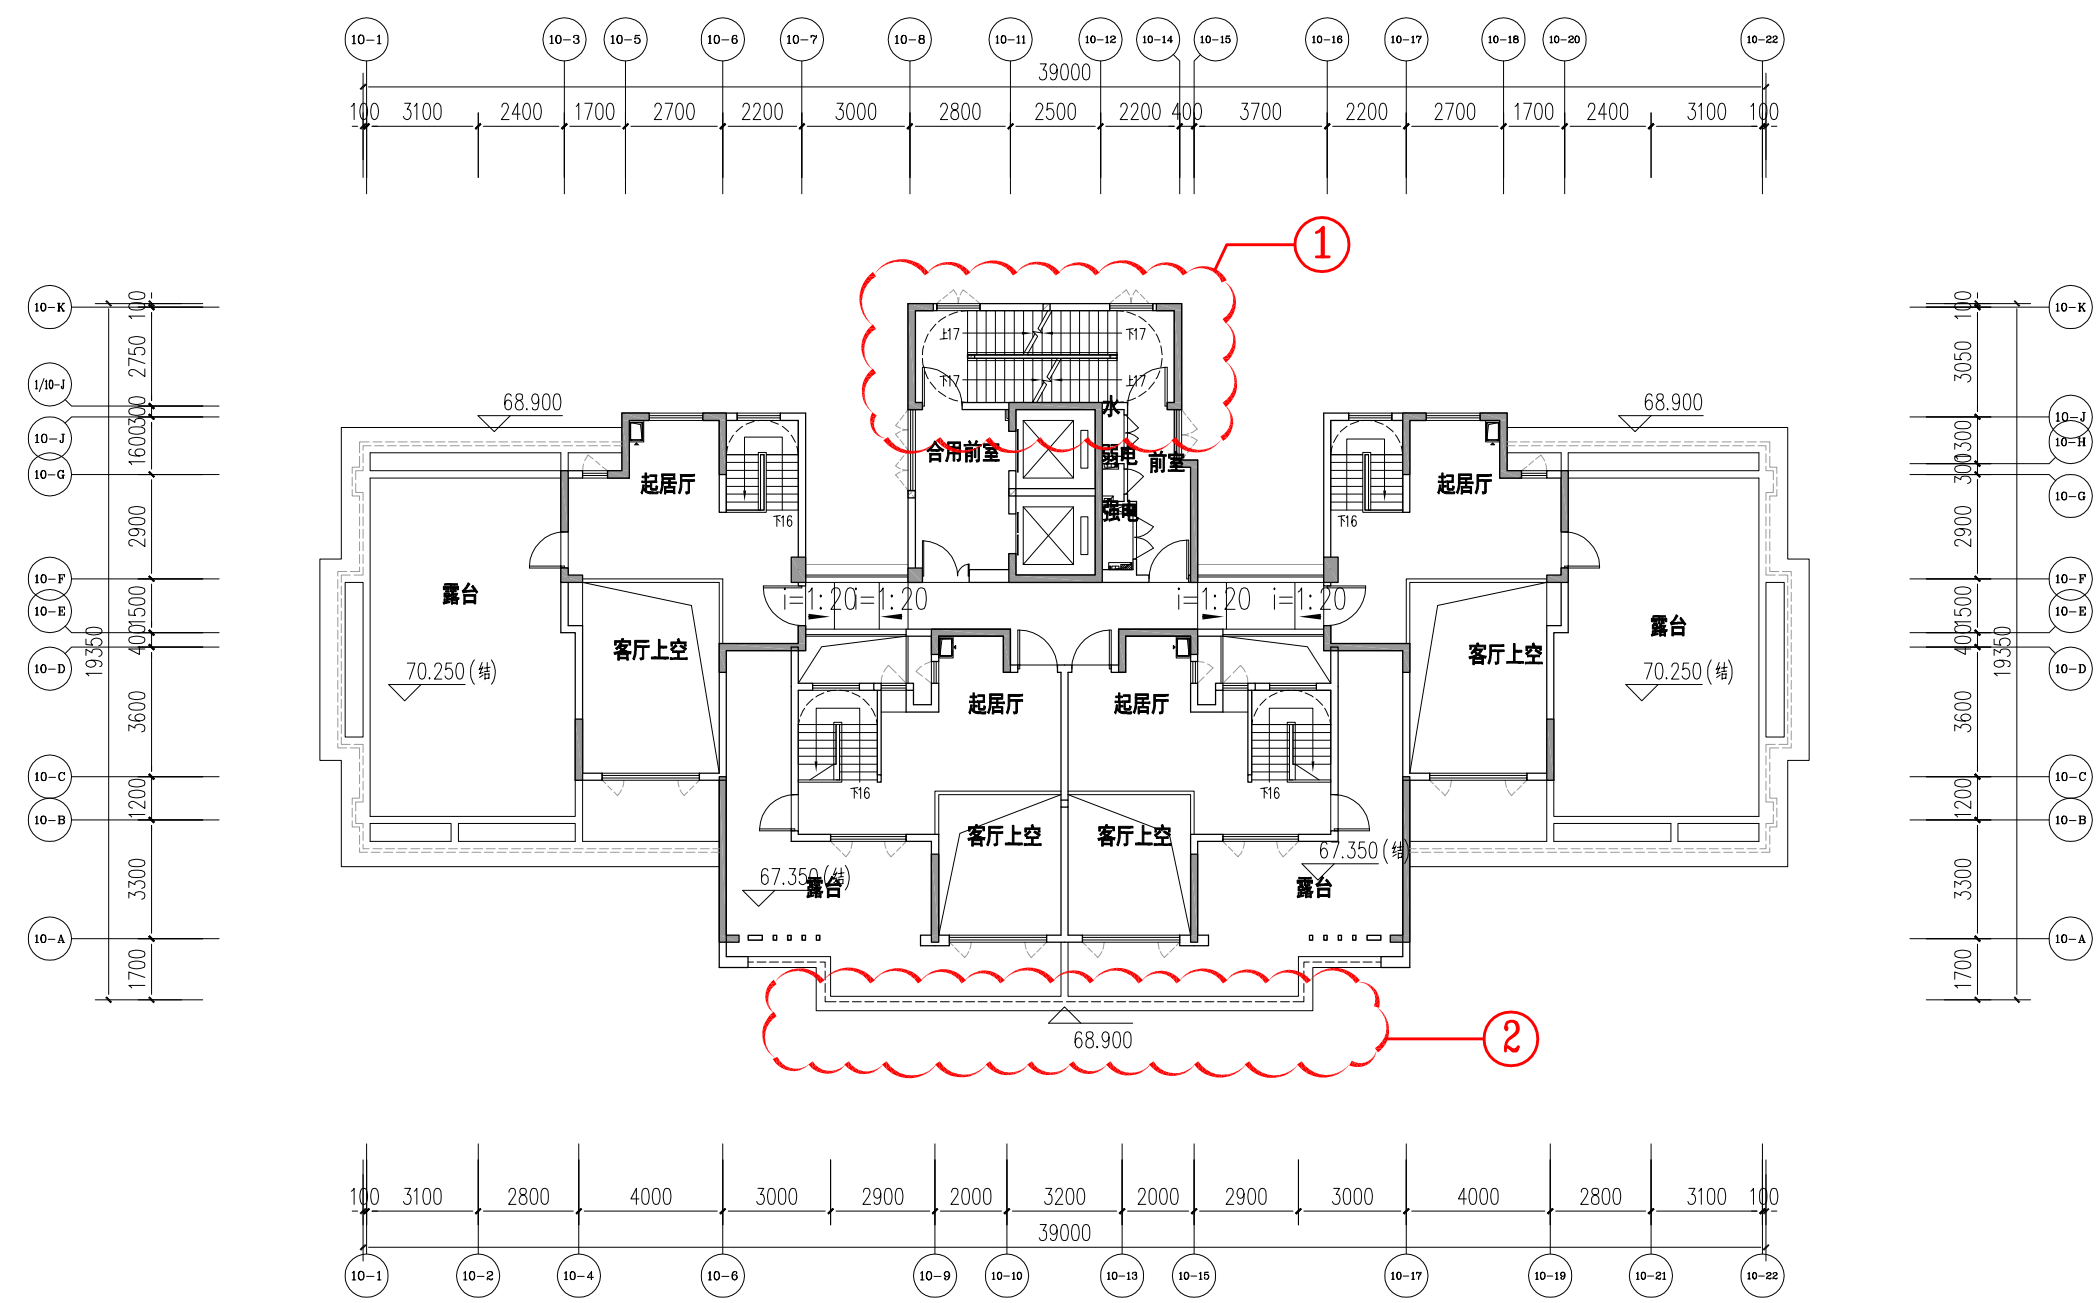

10#楼二十五层平面图 1:200

70.300


10#楼屋面层平面图 变更前

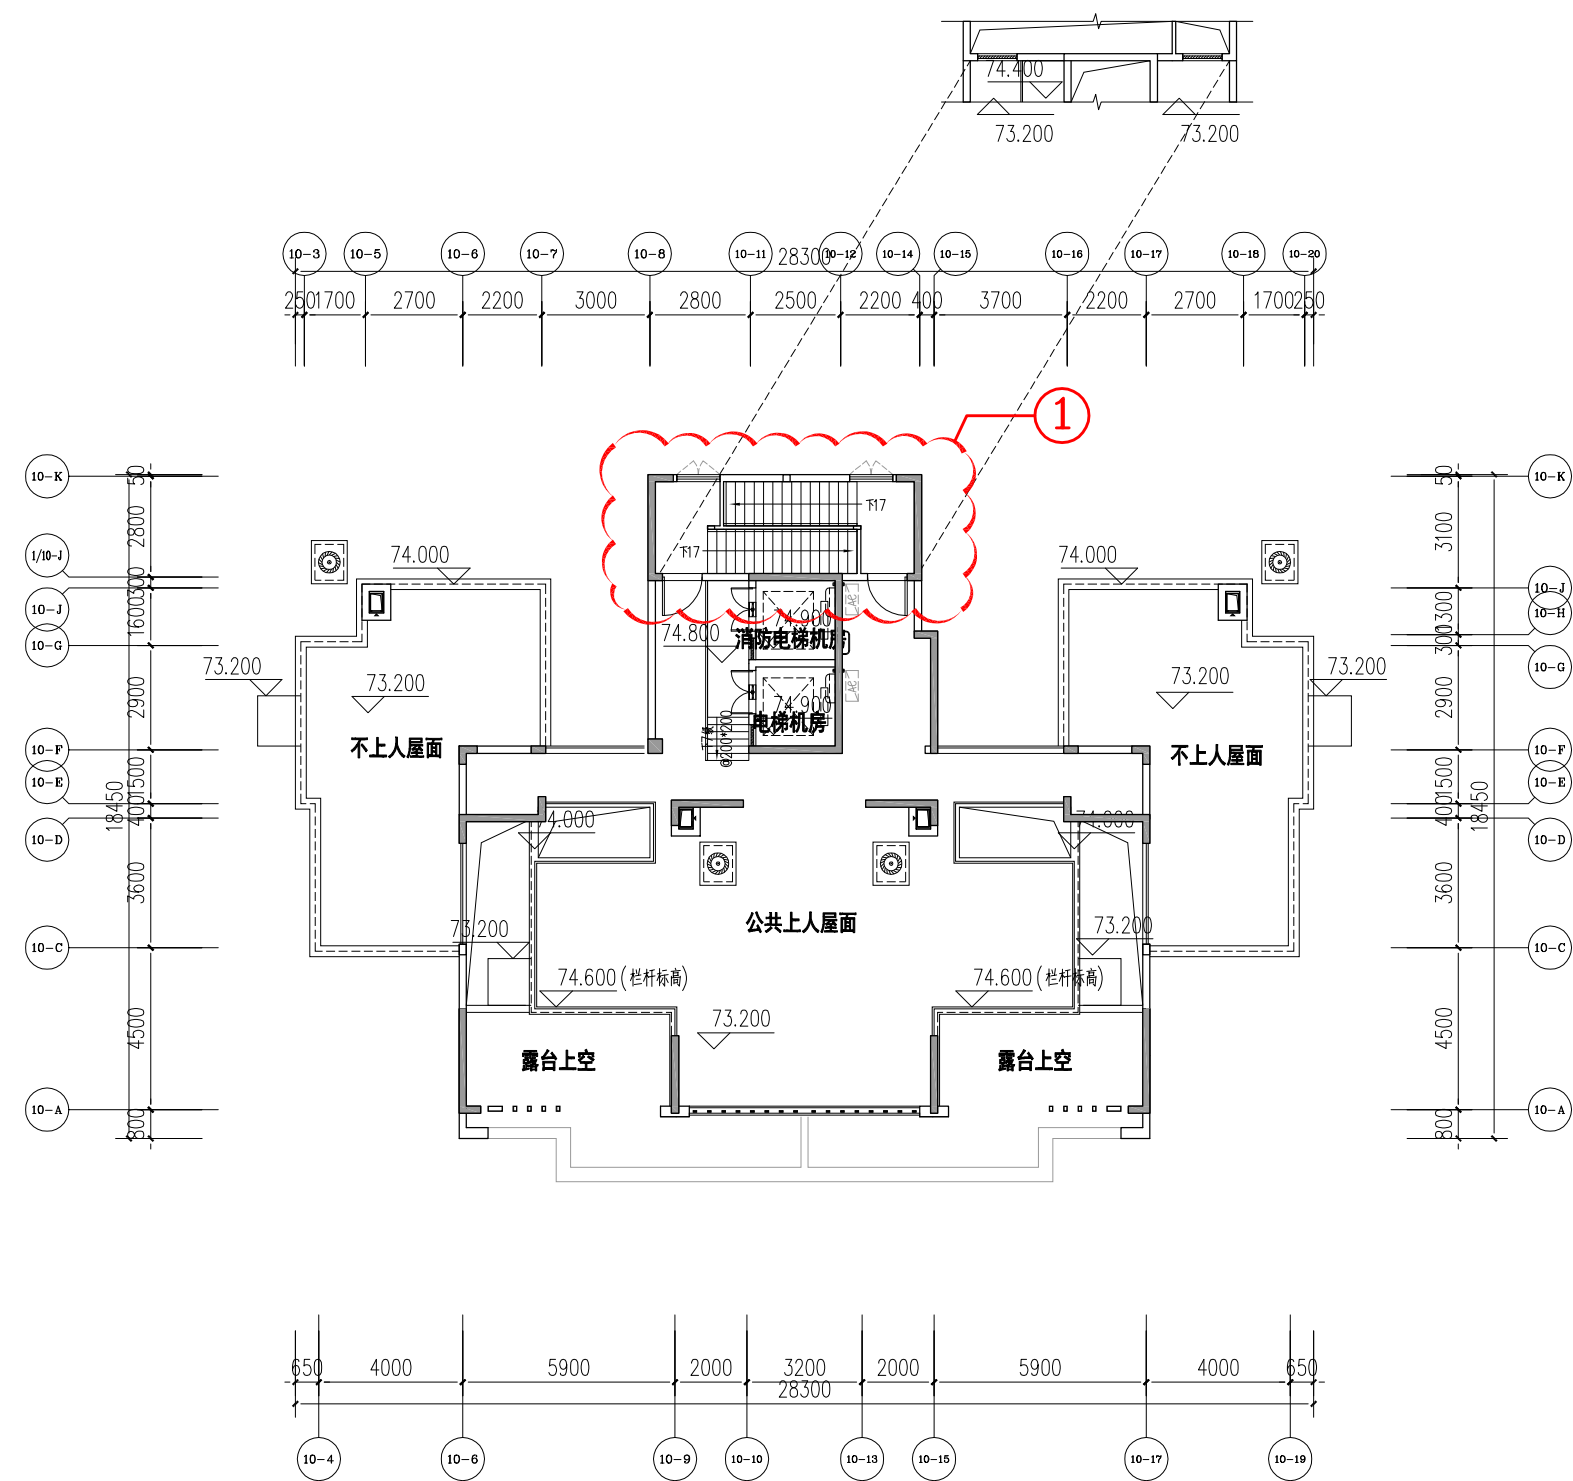

10#楼屋面层平面图 1:200


本层计容面积: 34.90m²

10#楼屋架层平面图 变更前

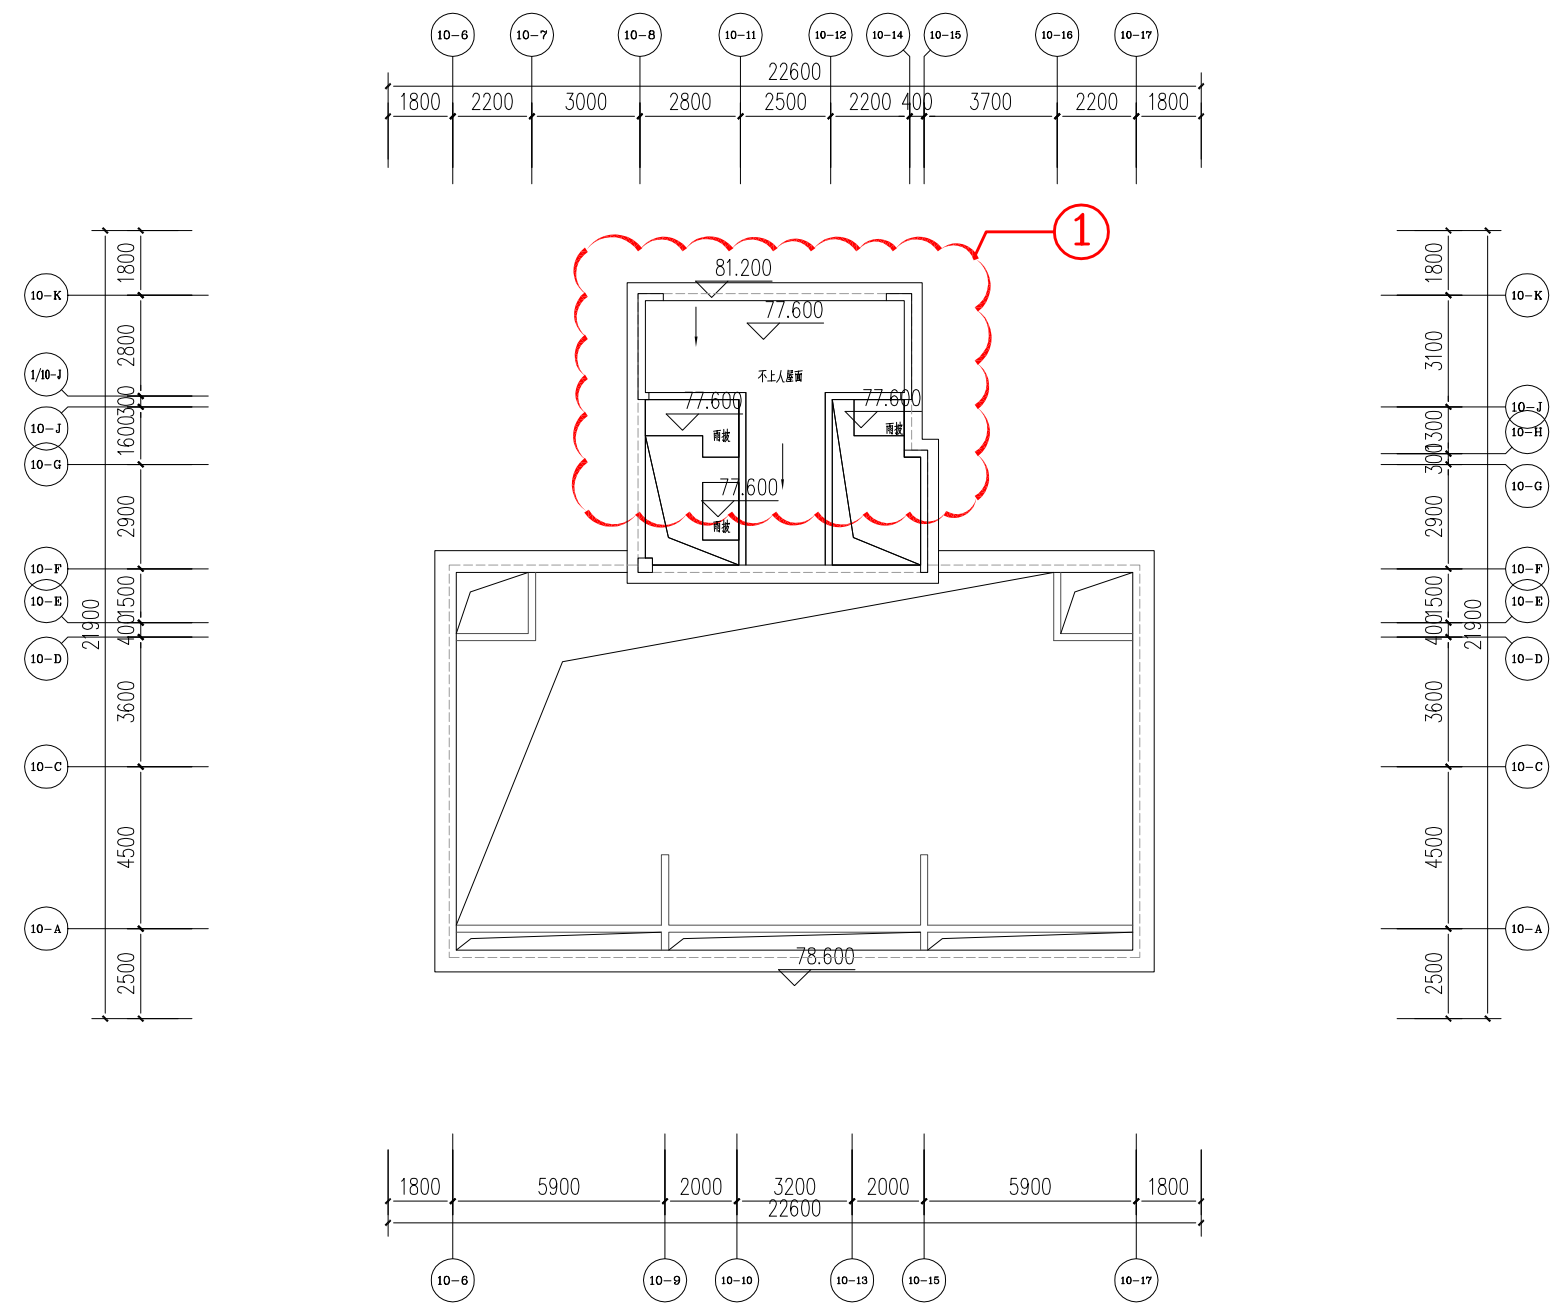


10#楼屋架层平面图 1:200

10#楼立面图 变更前

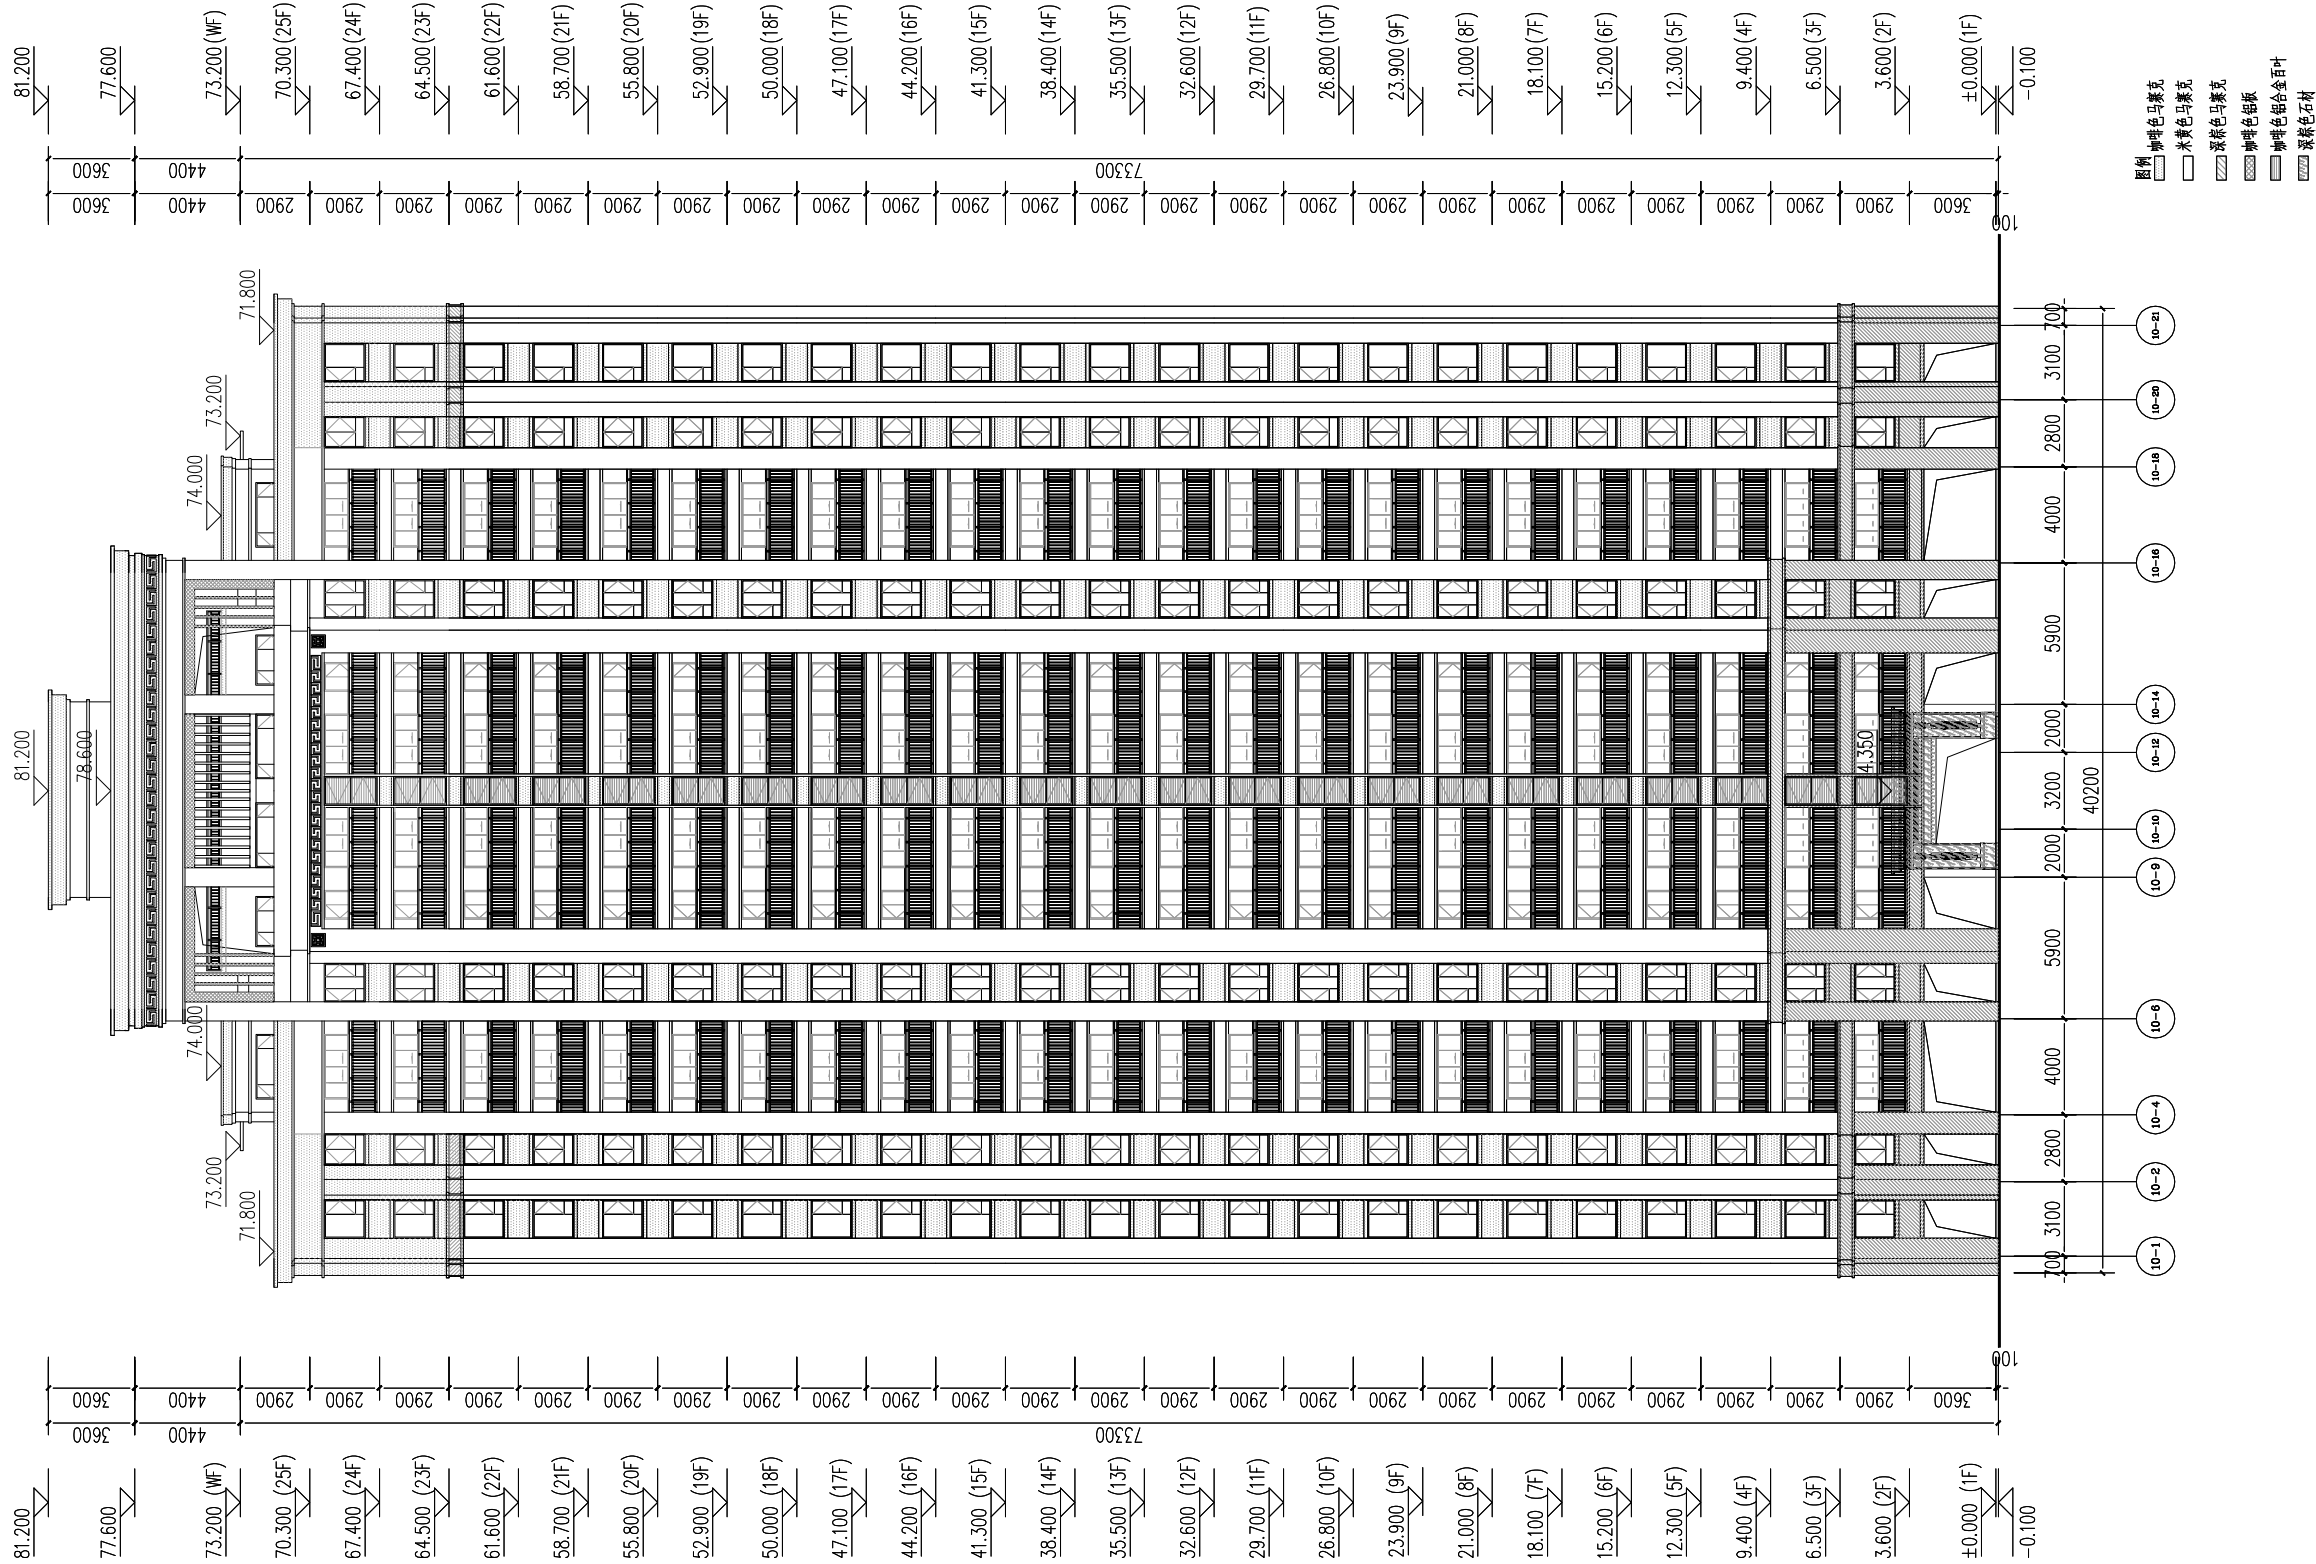


~ 10-1 10-21 轴立面图 1:300

10#楼立面图 变更前

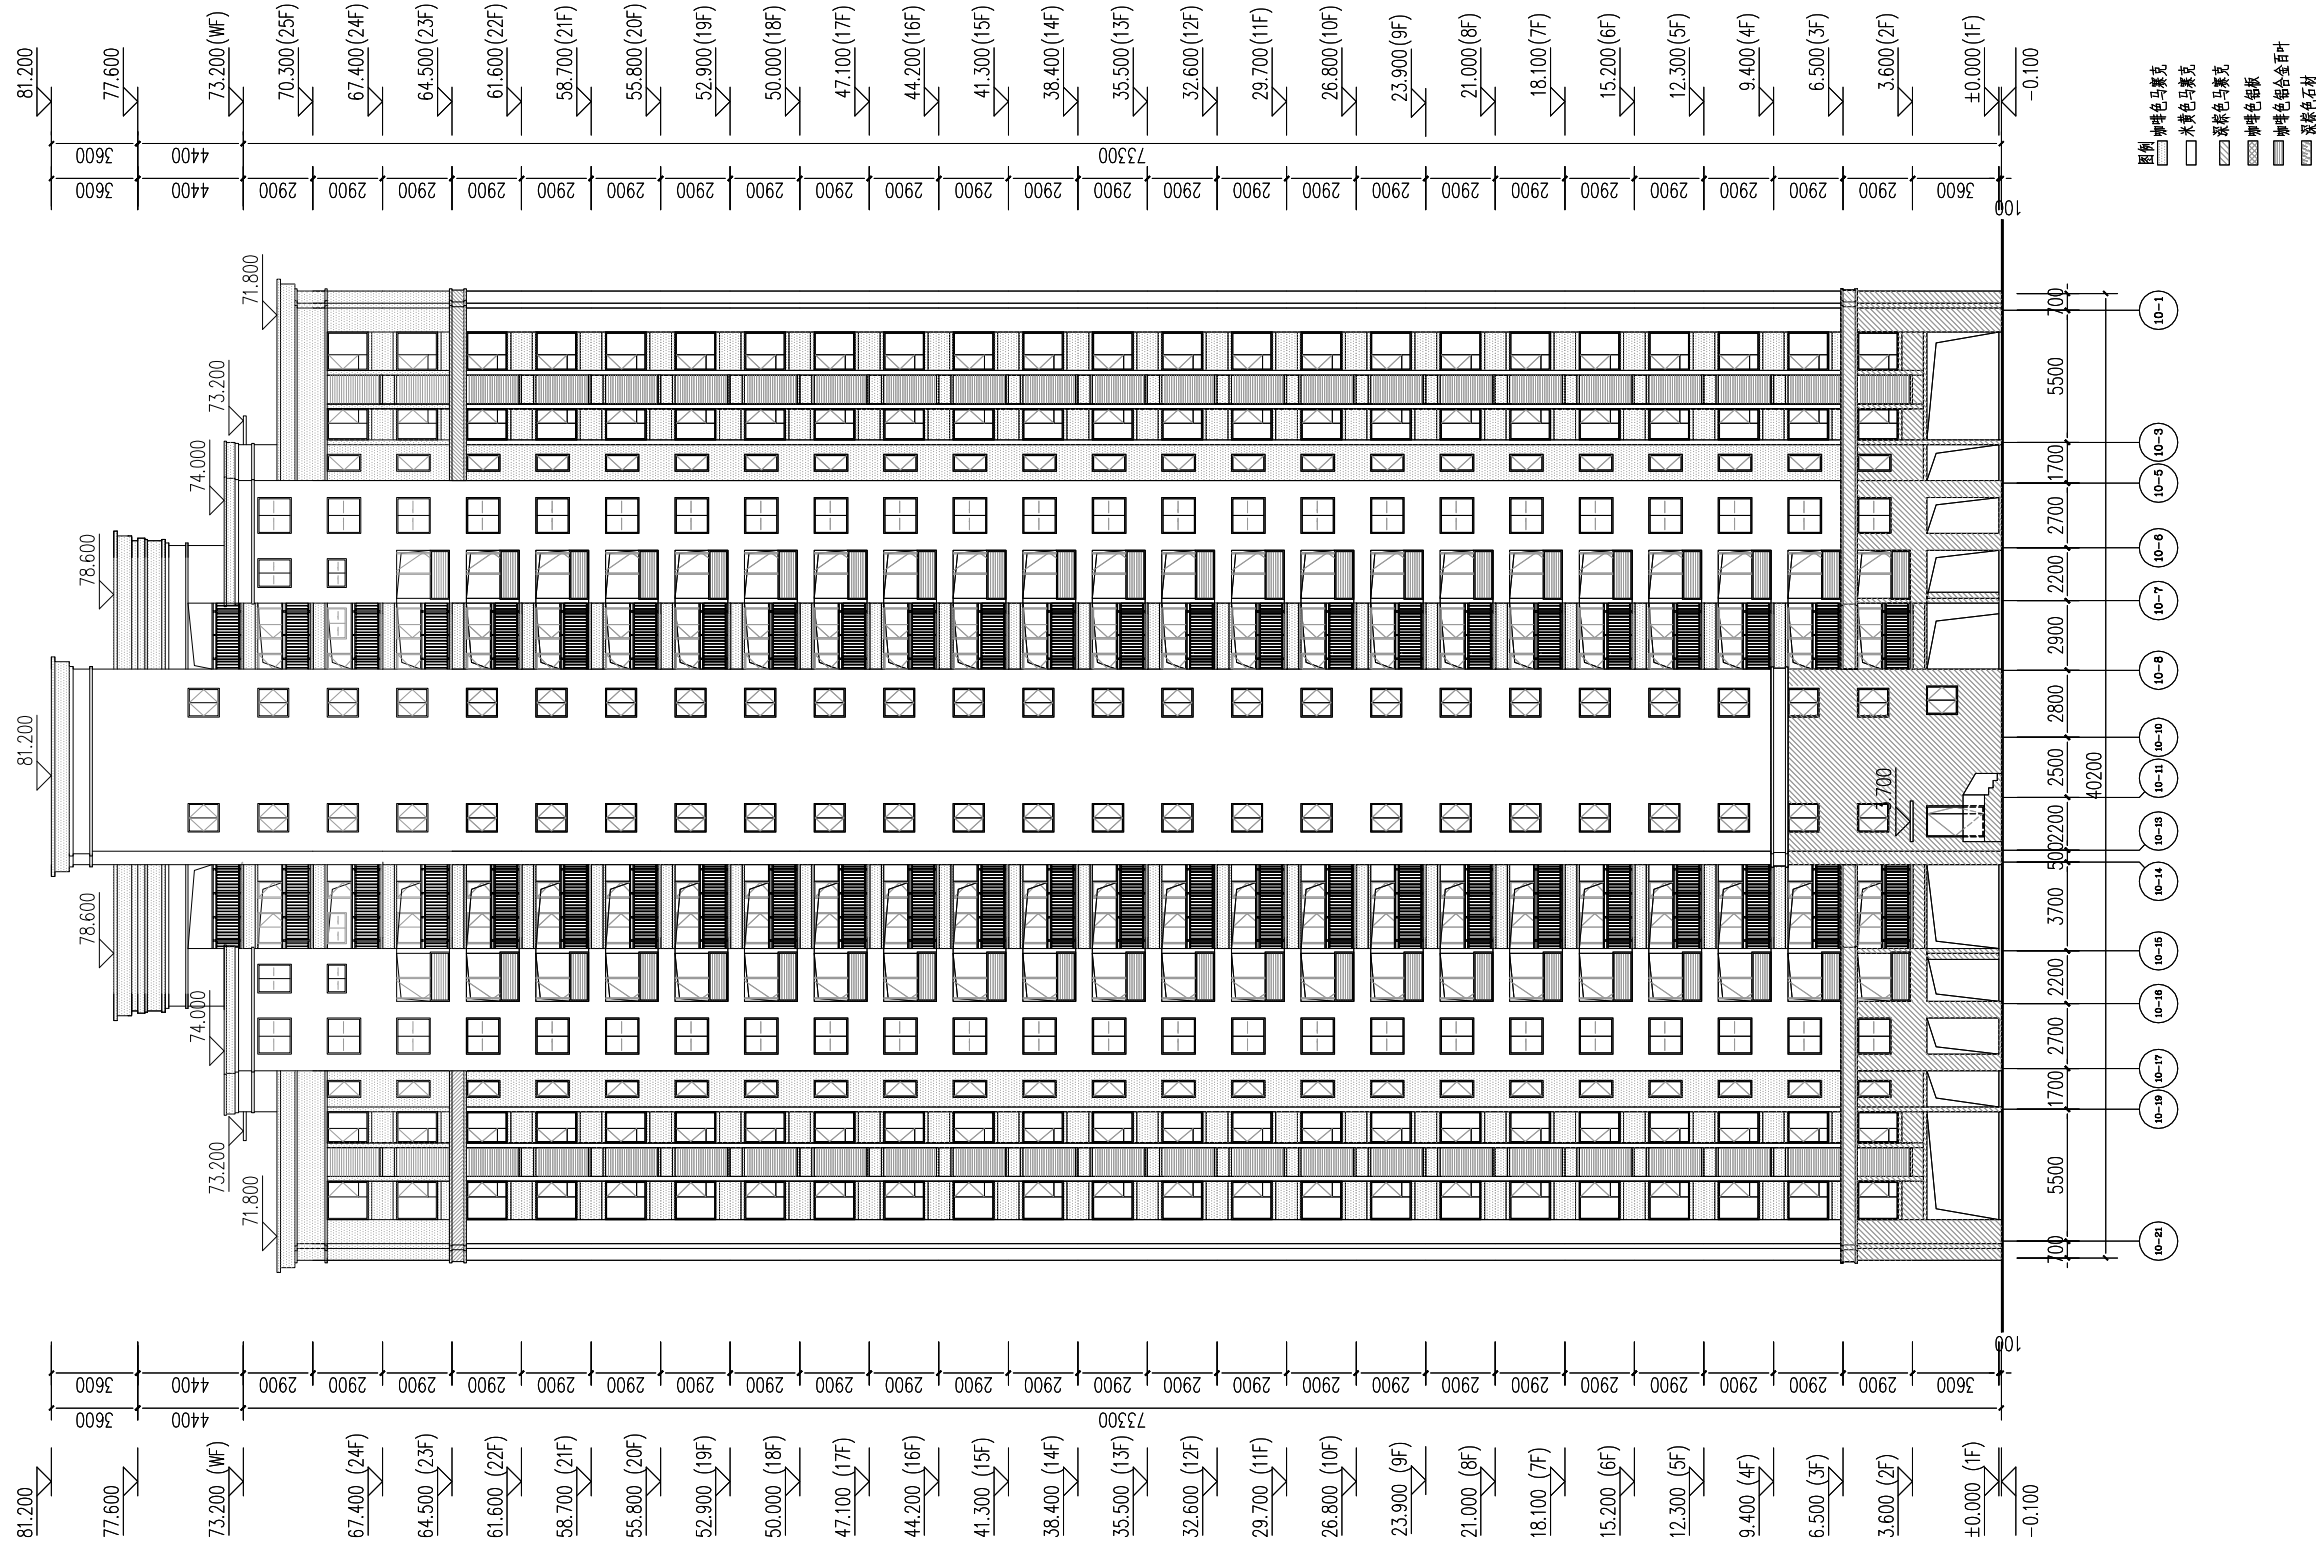


10-1 轴立面图 1:300

10#楼立面图 变更前

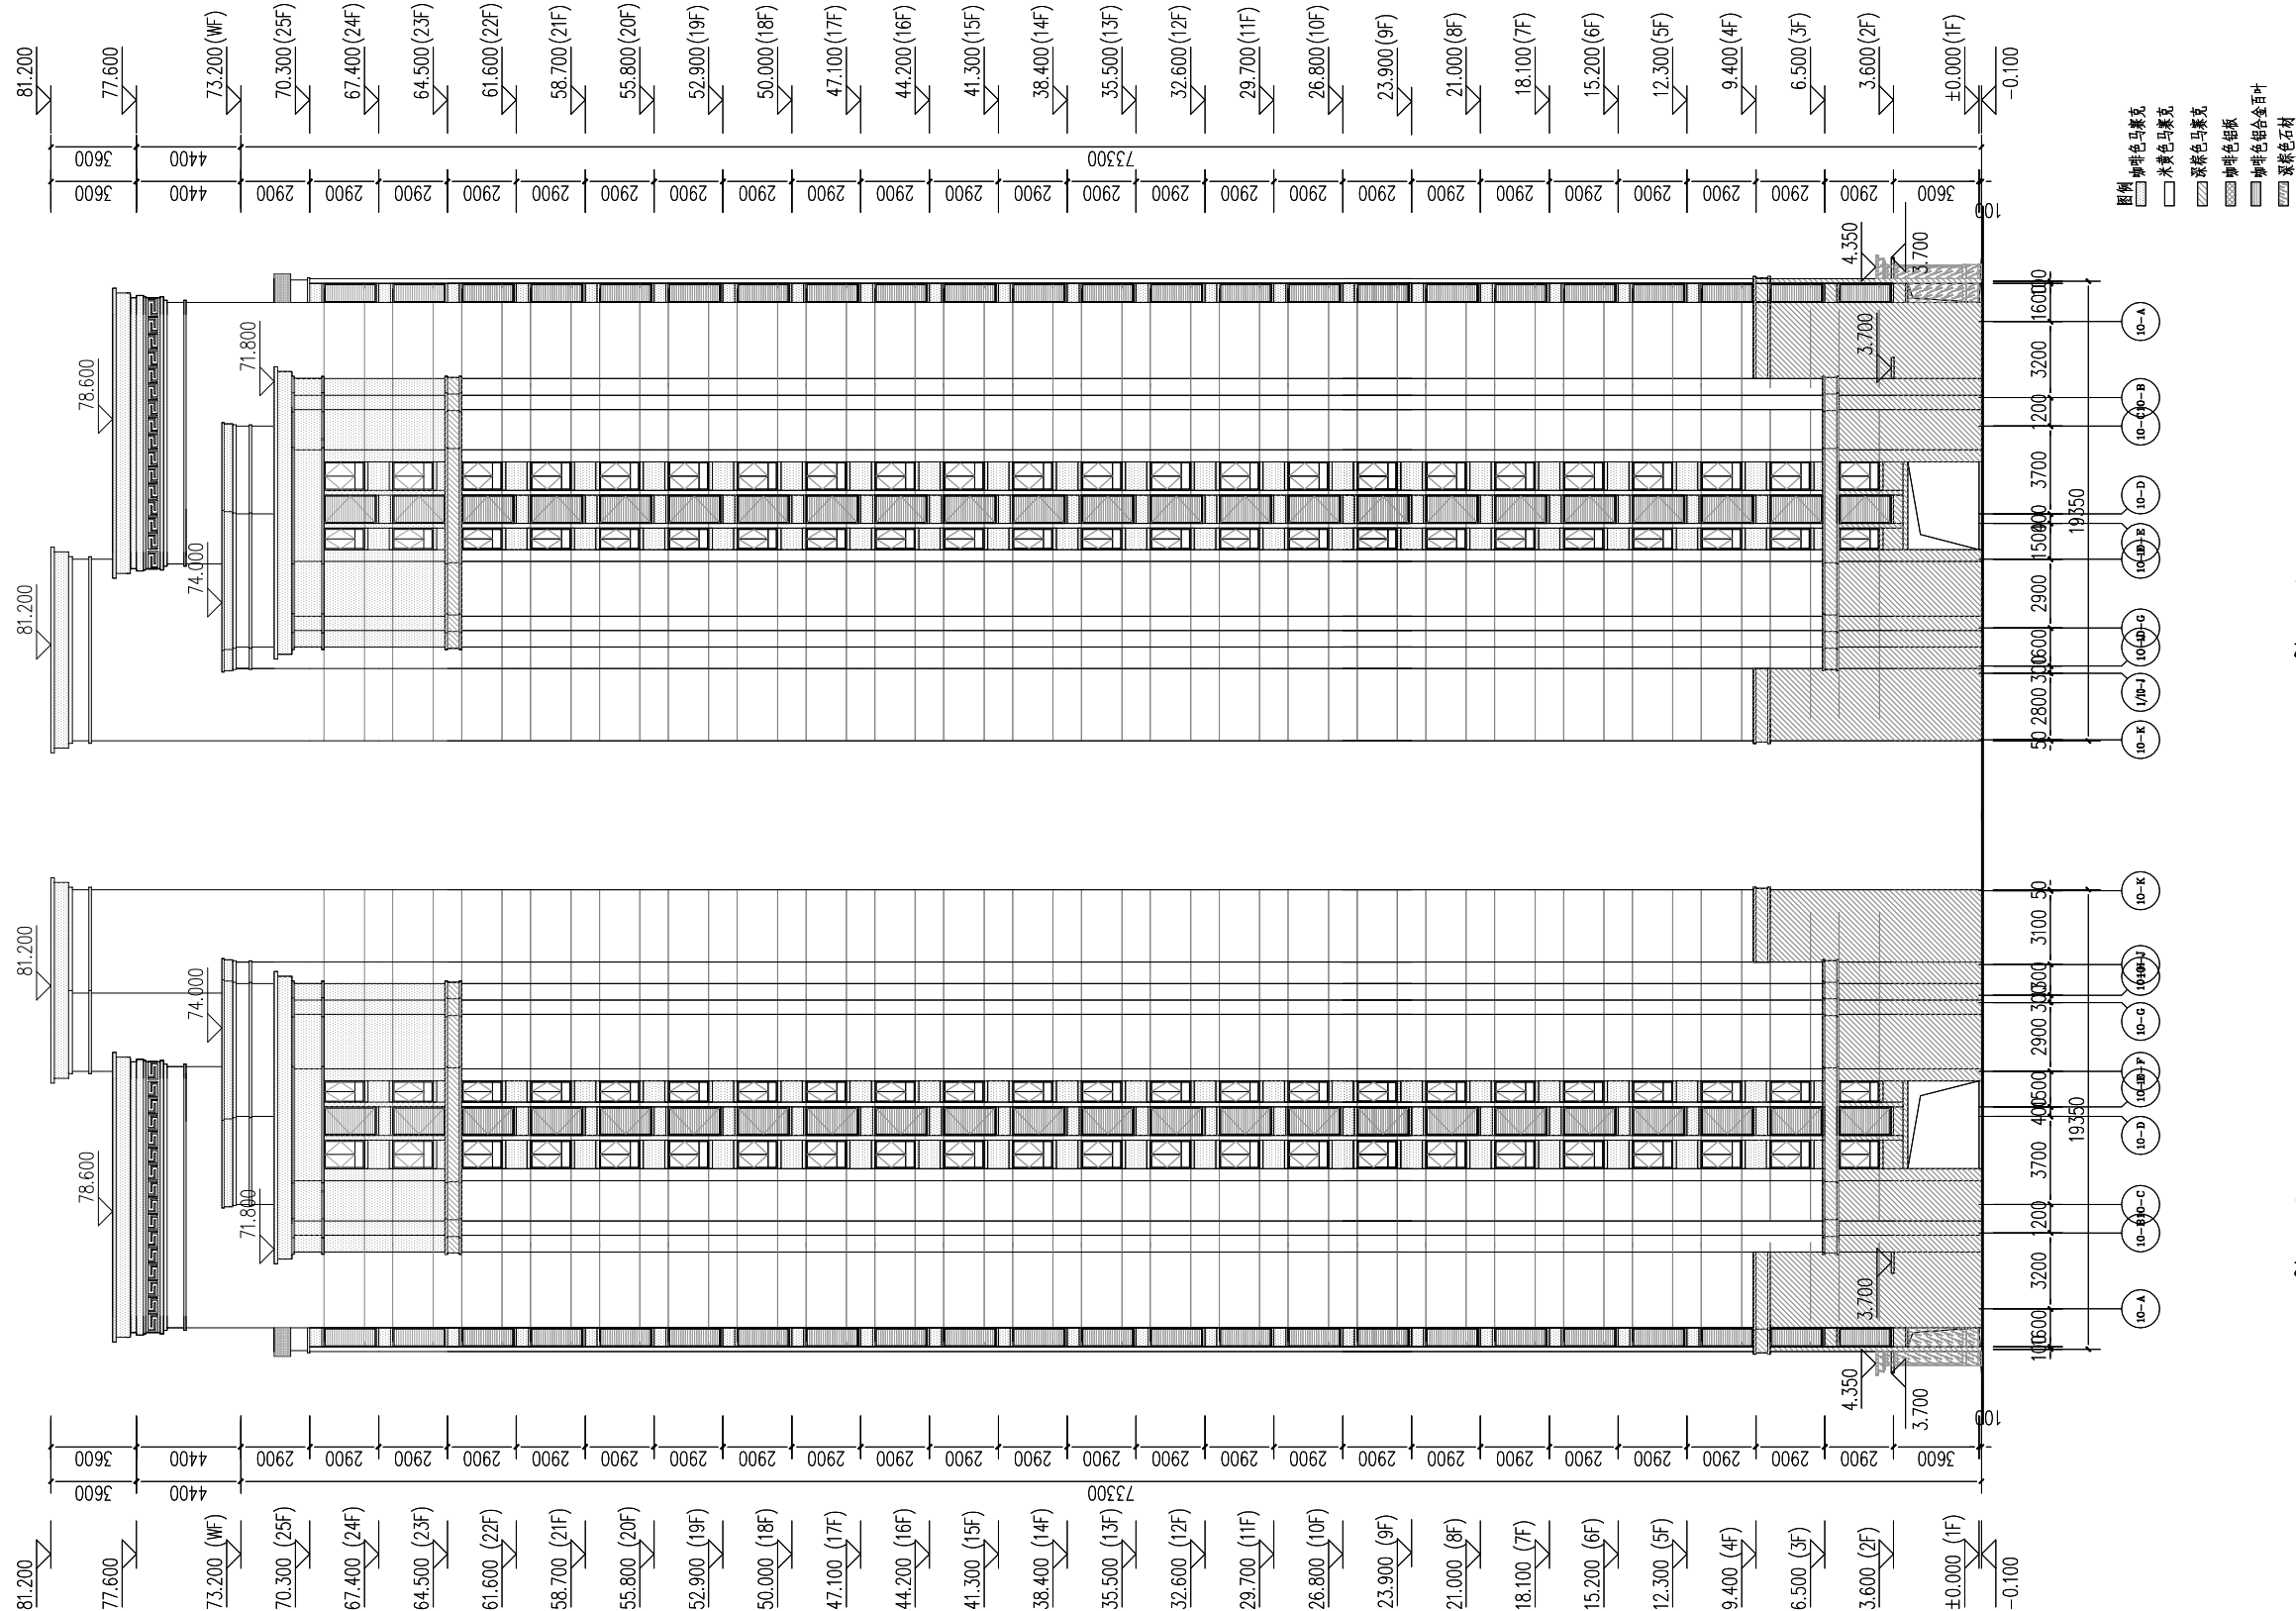

10#楼立面图 1:300

10#楼立面图 变更前

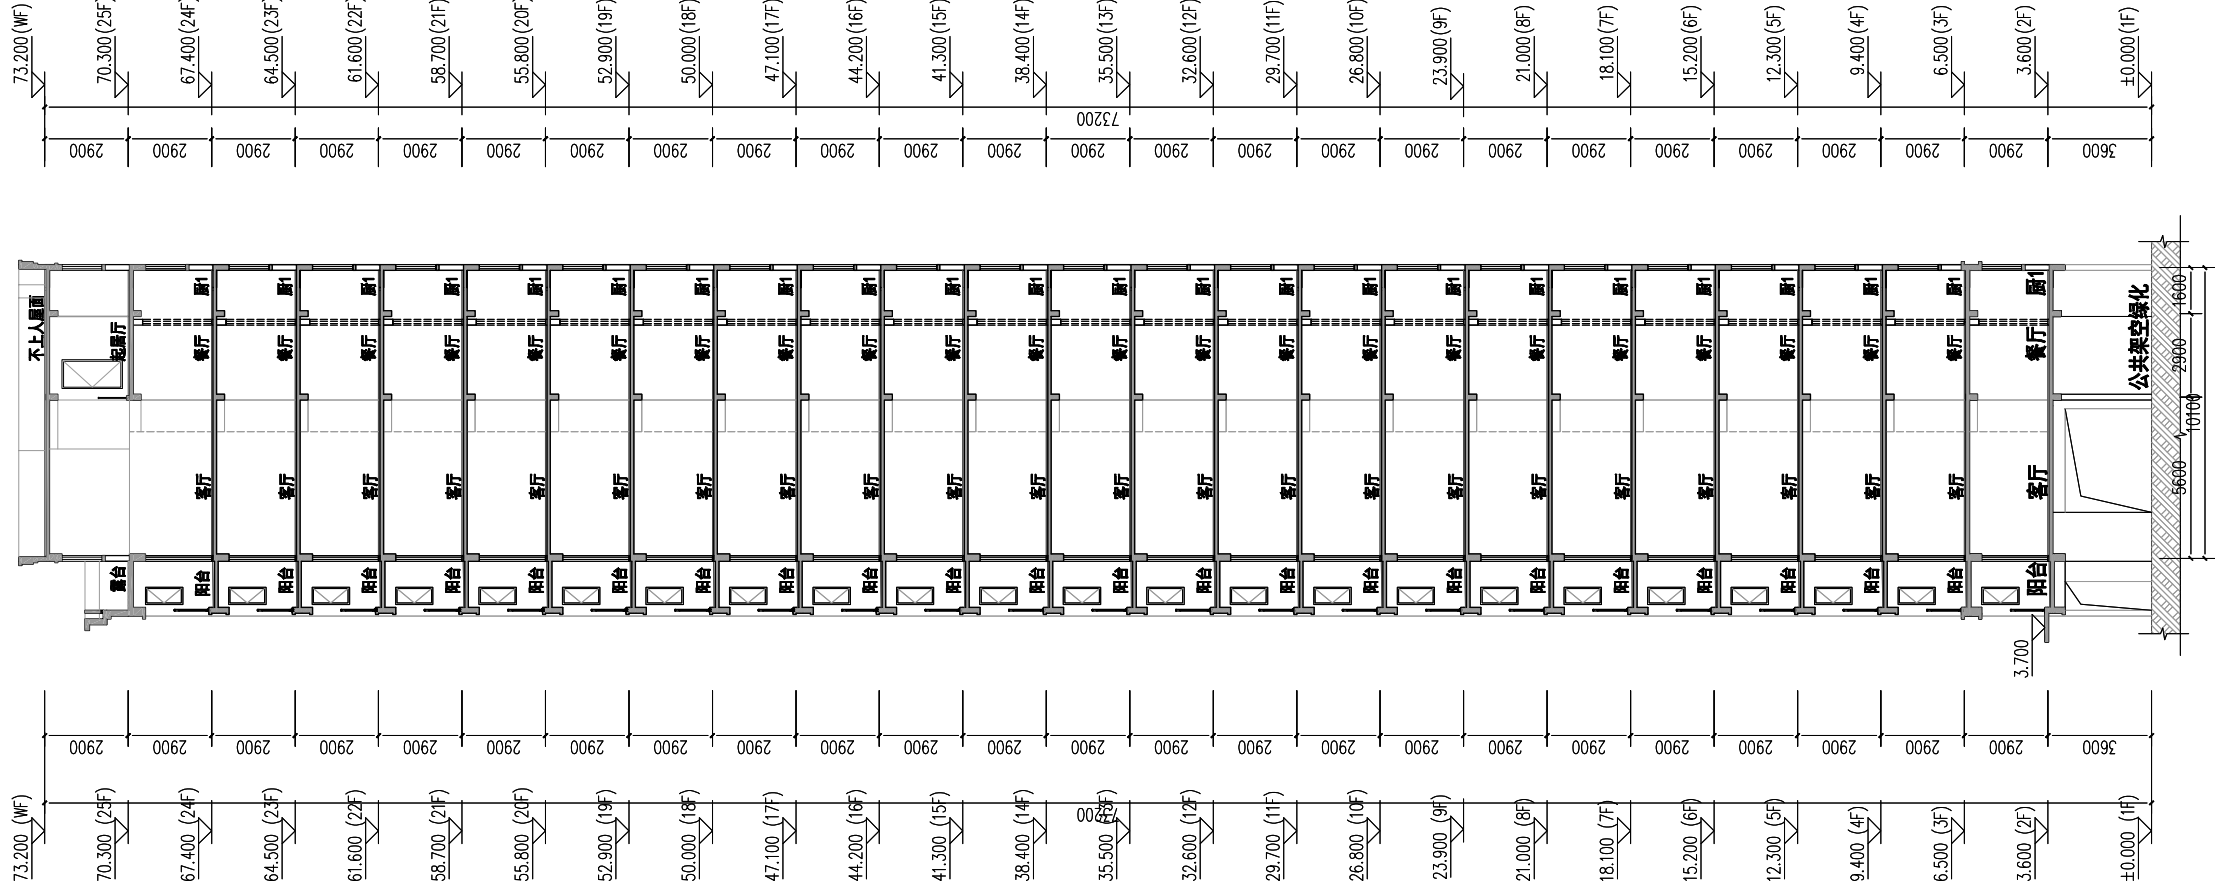


10#楼1-1剖面图 1:200

10#楼一层平面图 变更后


变更内容:

1:一层层高由3.6米改为4.2米, 楼梯踏步及无障碍坡道相应修改, 水井墙体外移至10-14轴处。

2: 此区域造型向10-A轴移100。

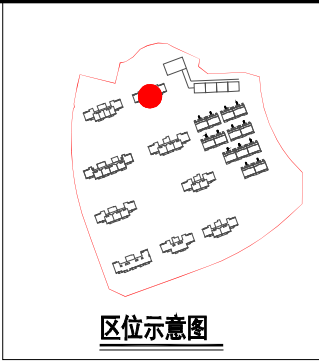

区位示意图

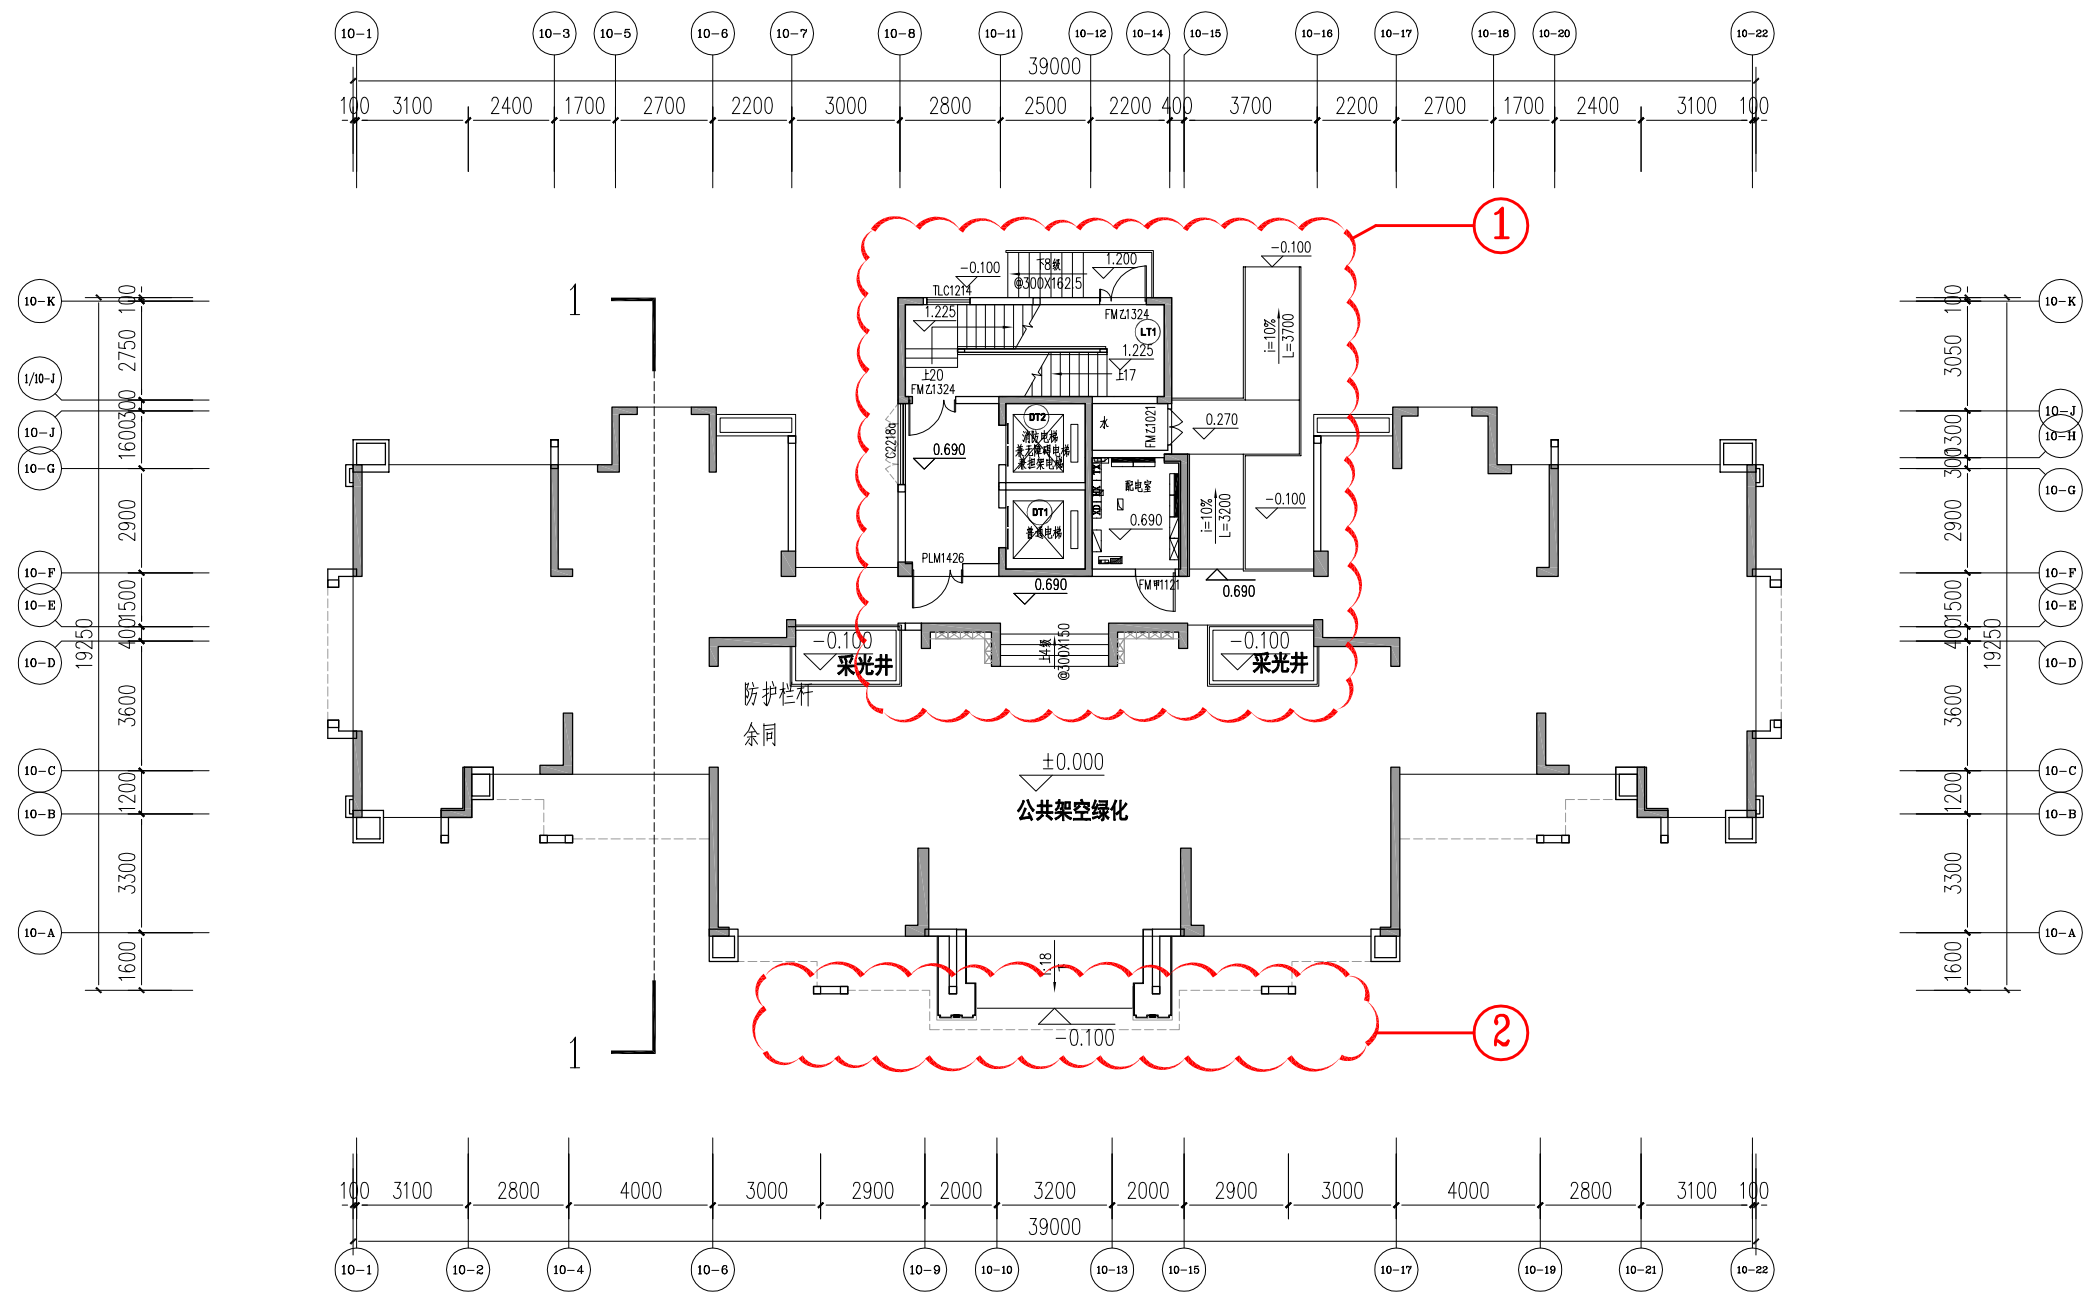

10#楼一层平面图 1:200

±0.000 (158.00)

本栋计容面积: 10630.70m²

本层计容面积: 60.43m²

本层不计容架空面积: 400.97m²


10#楼二层平面图 变更后

变更内容:


1:层高由2.9m改为3.0m, 楼梯踏步相应修改。

2:此区域阳台底板及造型墙体向10-A轴移100。

3:雨披标高相应调整。

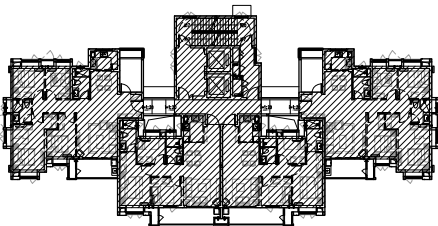


10#楼结构走向示意图

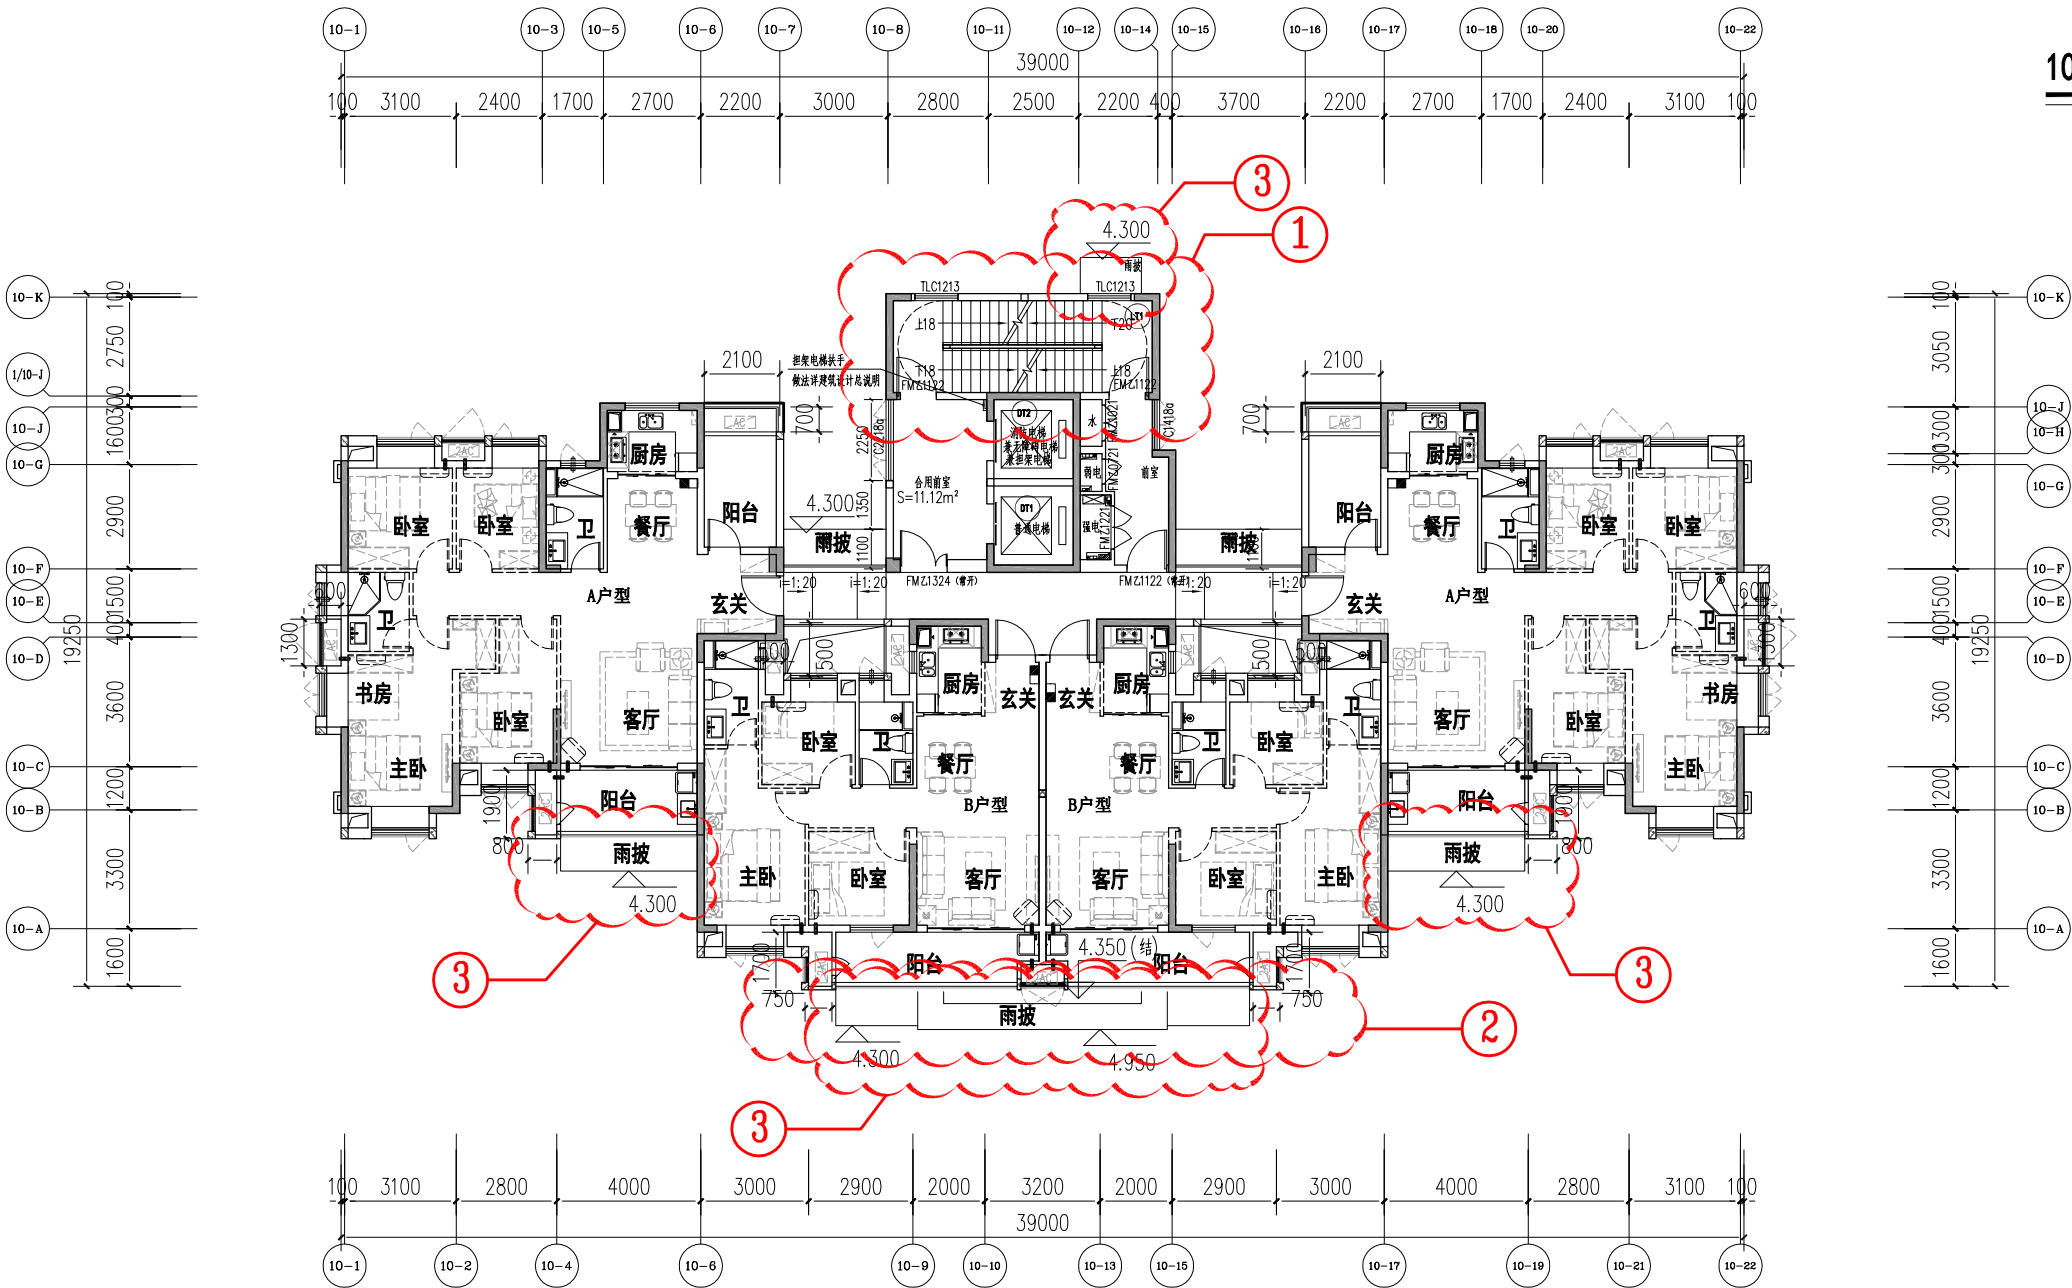


10#楼二层平面图 1:200

4.200

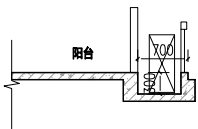

设备平台降板大样

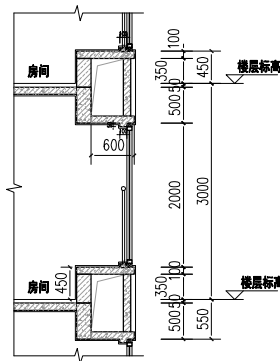

凸窗大样


户型编号	户型	户型面积	户内面积	阳台水平投影面积	阳台面积	套内面积 (阳台+户内)	阳台占套内投影面积比例 (不含套内阳台)	公摊面积	公摊率	本层面积 (计容)
A	4房2厅2卫	128.39	98.01	14.00	7.00	105.01	14.28%	23.38	18.21%	446.12
B	3房2厅2卫	90.23	69.22	9.16	4.58	73.80	13.23%	16.43	18.21%	

10#楼三、四层平面图 变更后

变更内容:

1:层高由2.9m改为3.0m, 楼梯踏步相应修改。


2:此区域阳台底板及造型墙体向10-A轴移100。

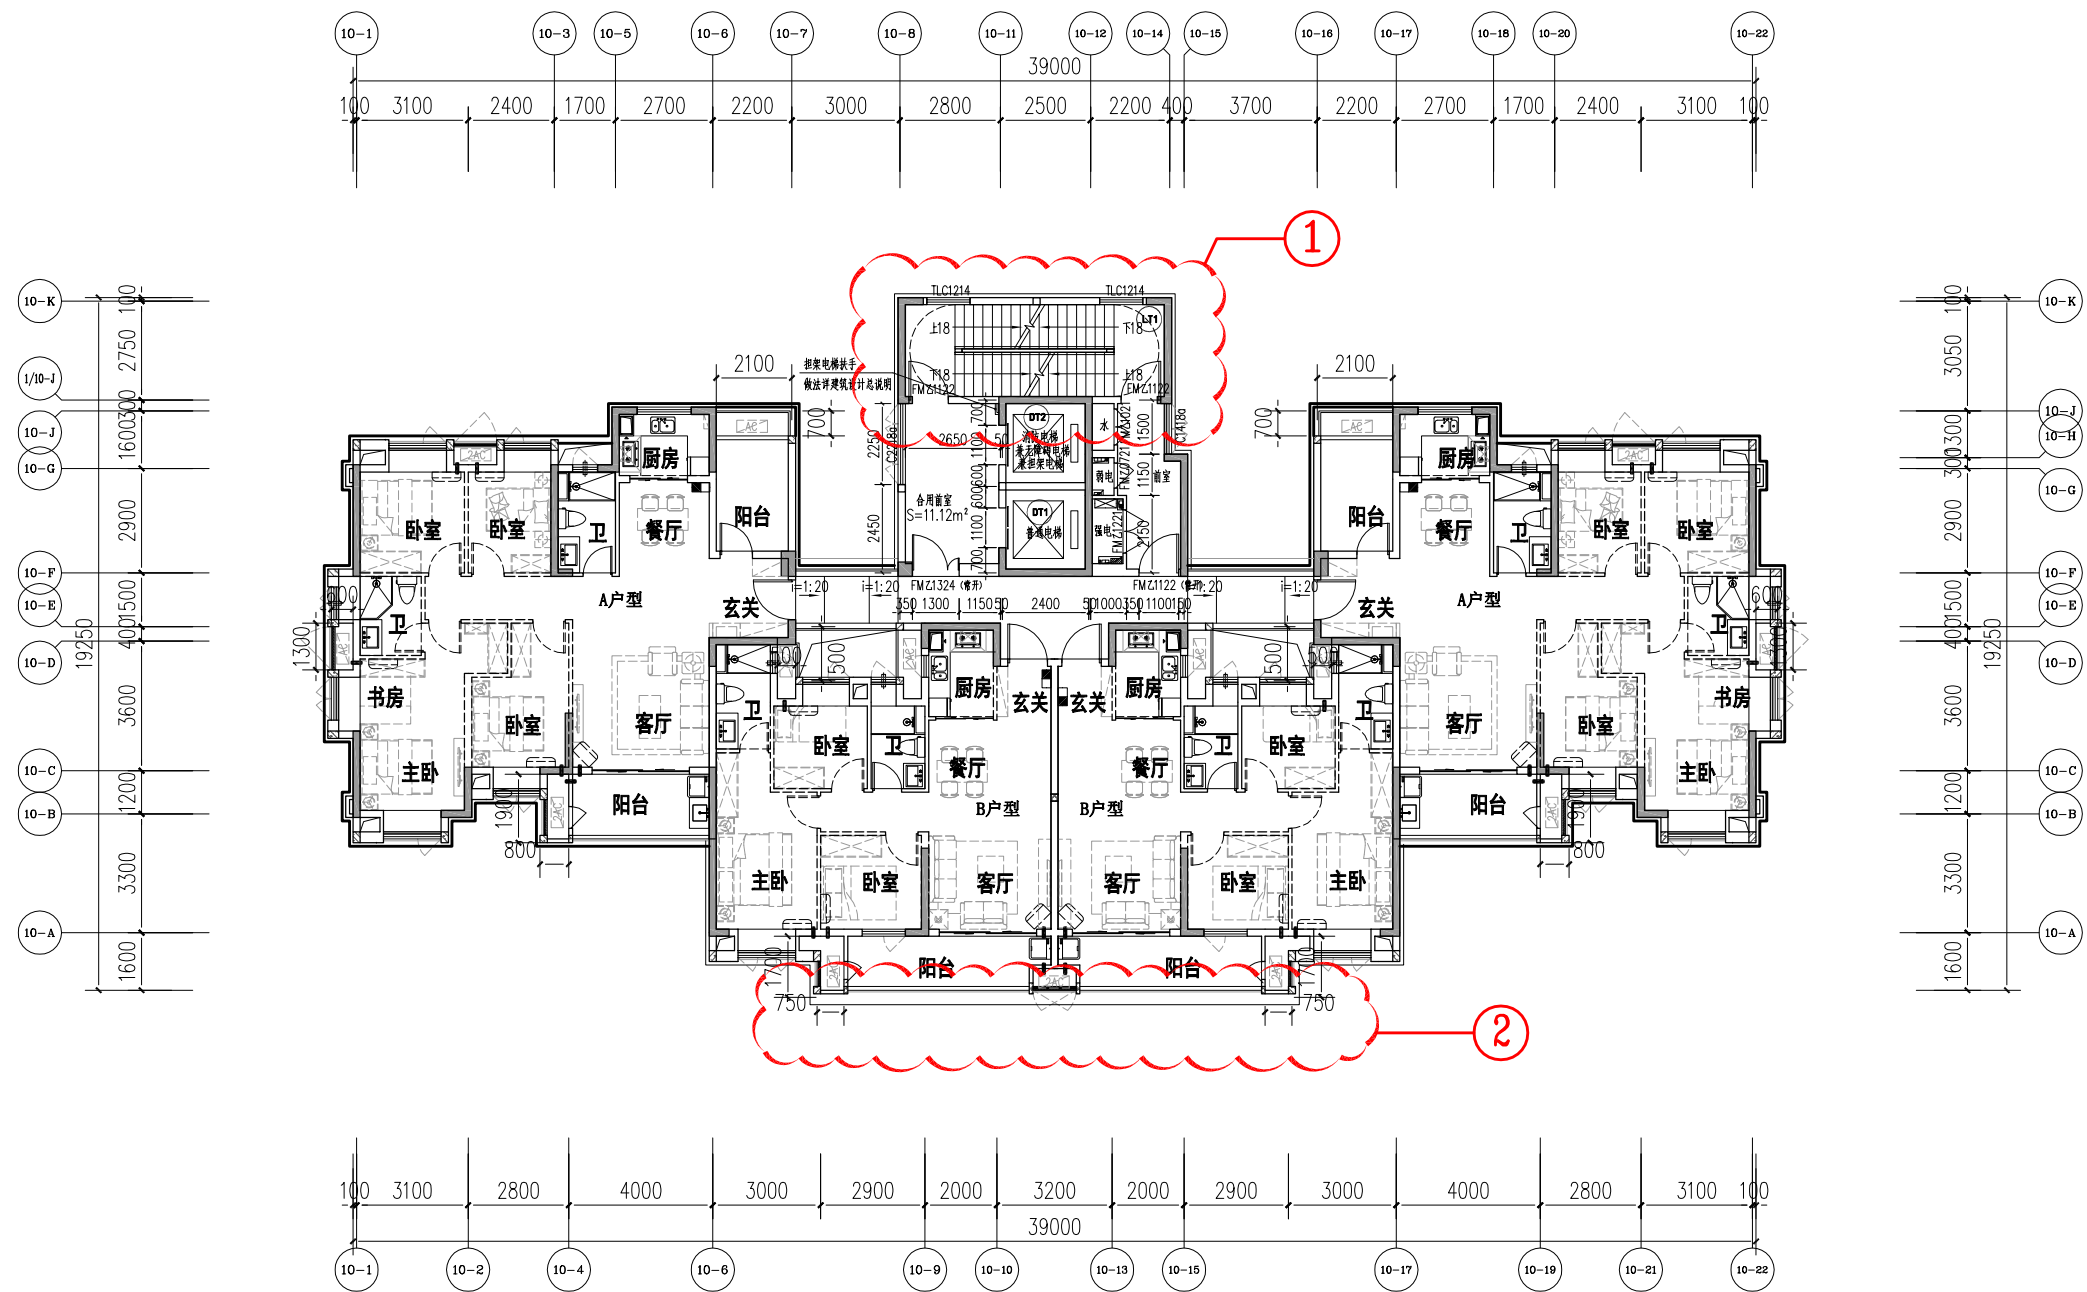

10#楼三、四层平面图 1:200

(10.200)4F
7.200 3F

户型编号	户型	户型面积	户内面积	阳台水平投影面积	阳台面积	套内面积 (阳台+户内)	阳台占套内投影面积比例 (不含套内阳台)	公摊面积	公摊率	本层面积 (计容)
A	4房2厅2卫	128.39	98.01	14.00	7.00	105.01	14.28%	23.38	18.21%	446.12
B	3房2厅2卫	90.23	69.22	9.16	4.58	73.80	13.23%	16.43	18.21%	

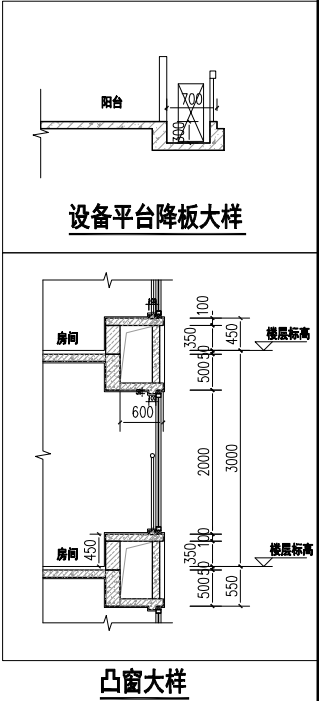


10#楼五至二十三层平面图 变更后

变更内容:

1:层高由2.9m改为3.0m, 楼梯踏步相应修改。


2:此区域阳台底板及造型墙体向10-A轴移100。

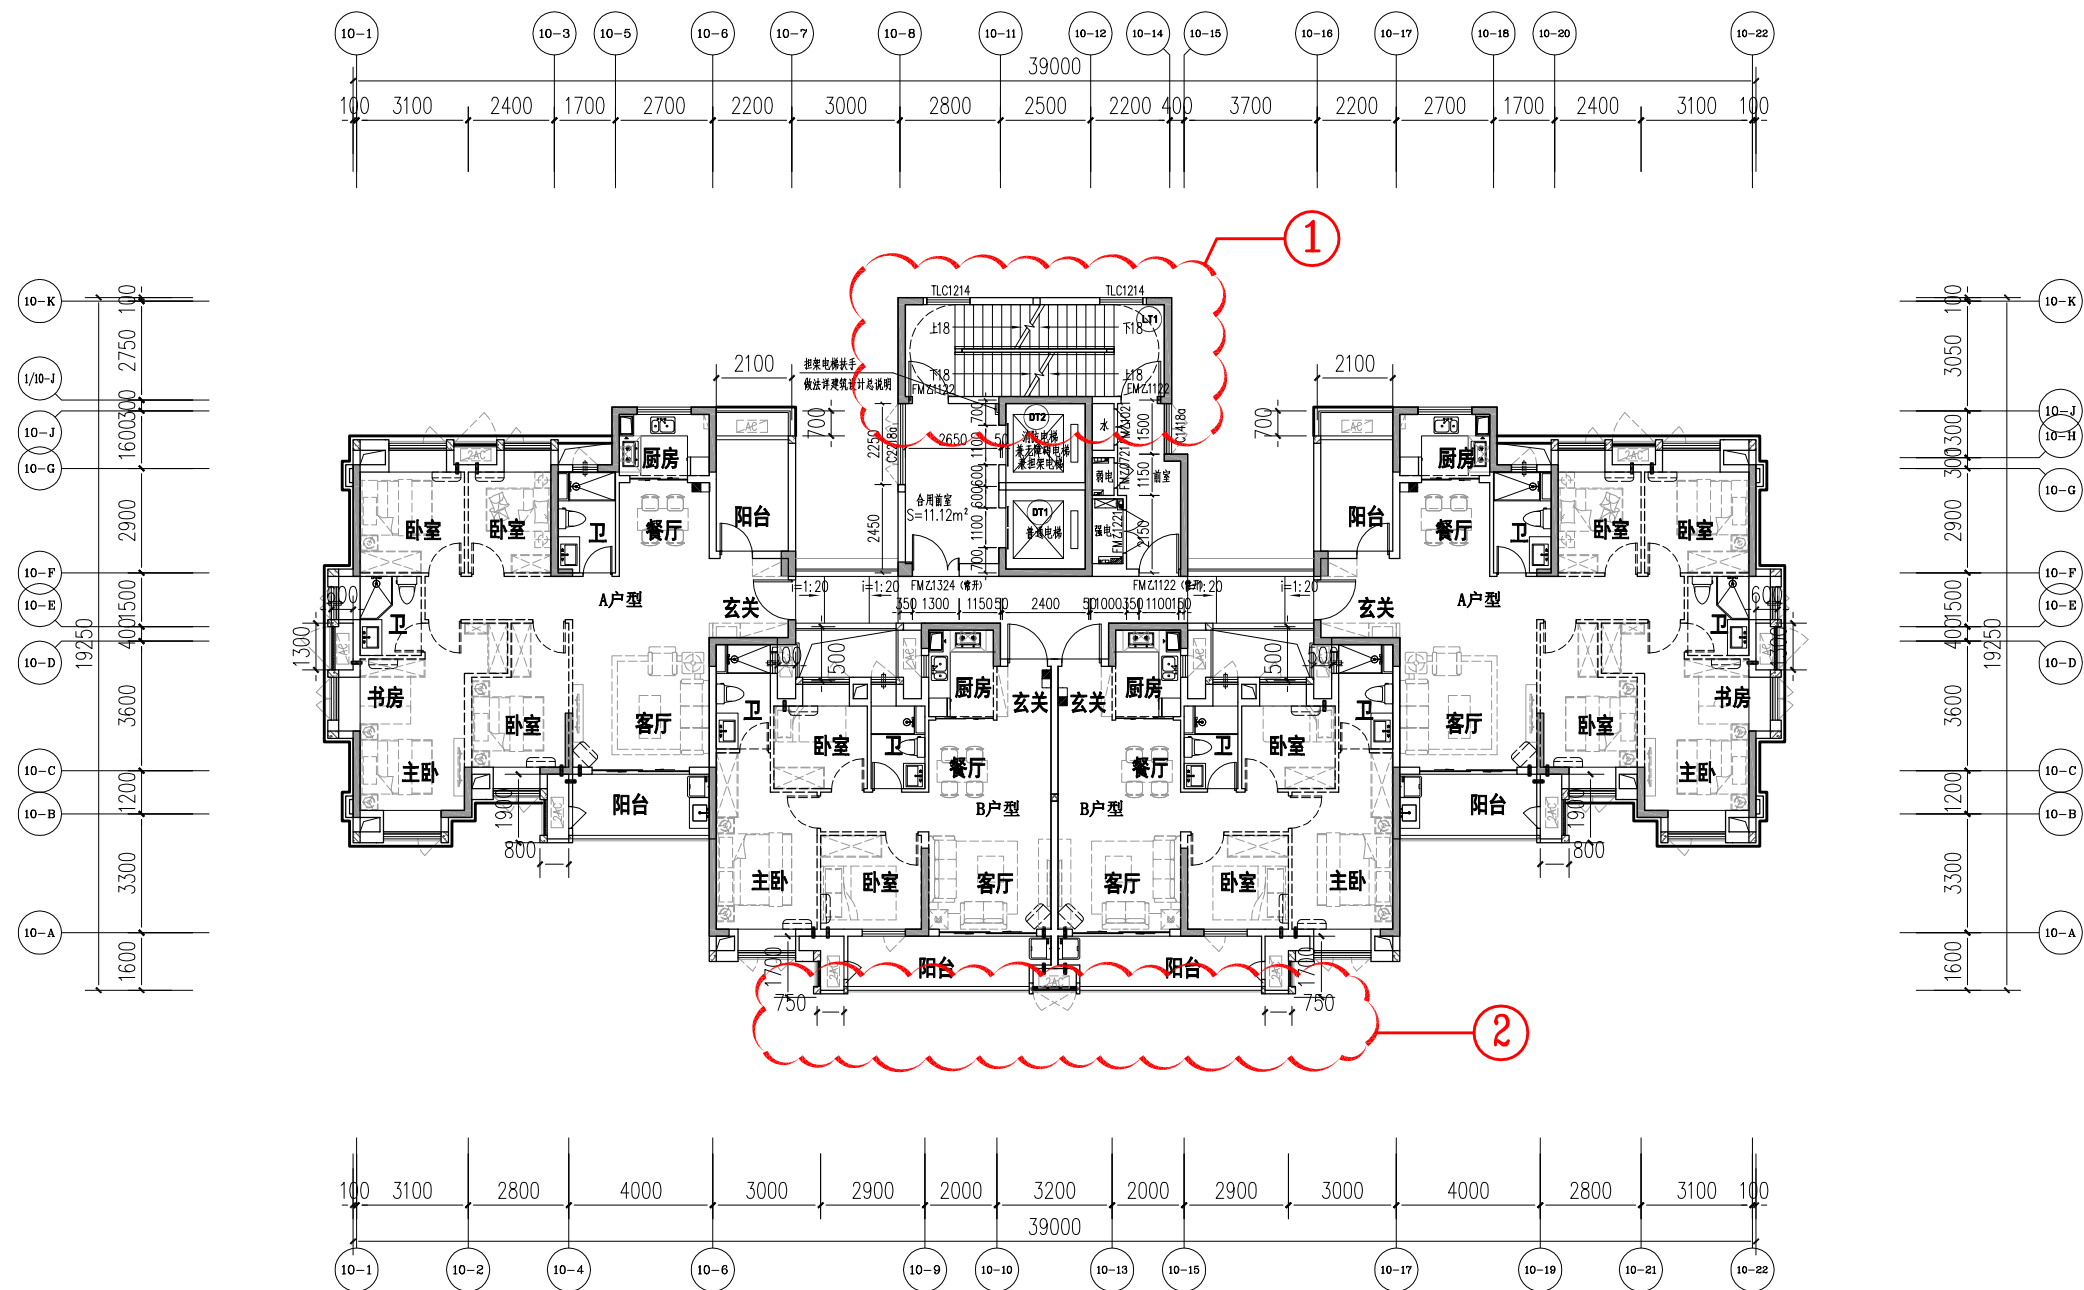

10#楼五至二十三层平面图 1:200

67.200 (23F)
~
13.200 (5F)

户型编号	户型	户型面积	户内面积	阳台水平投影面积	阳台面积	套内面积 (阳台+户内)	阳台占套内投影面积比例 (不含套内阳台)	公摊面积	公摊率	本层面积 (计容)
A	4房2厅2卫	128.39	98.01	14.00	7.00	105.01	14.28%	23.38	18.21%	446.12
B	3房2厅2卫	90.23	69.22	9.16	4.58	73.80	13.23%	16.43	18.21%	

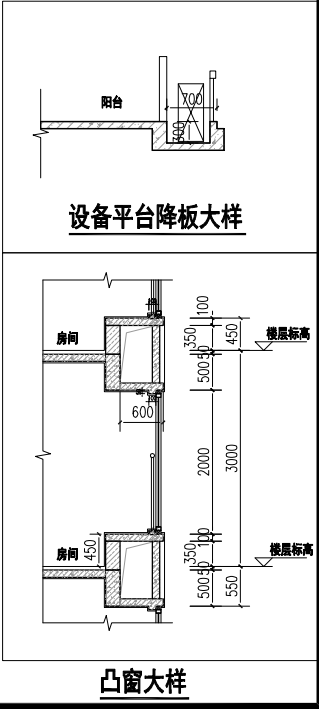


10#楼二十四层平面图 变更后


变更内容:

1:层高由2.9m改为3.0m, 楼梯踏步相应修改。

2:此区域阳台底板及造型墙体向10-A轴移100。

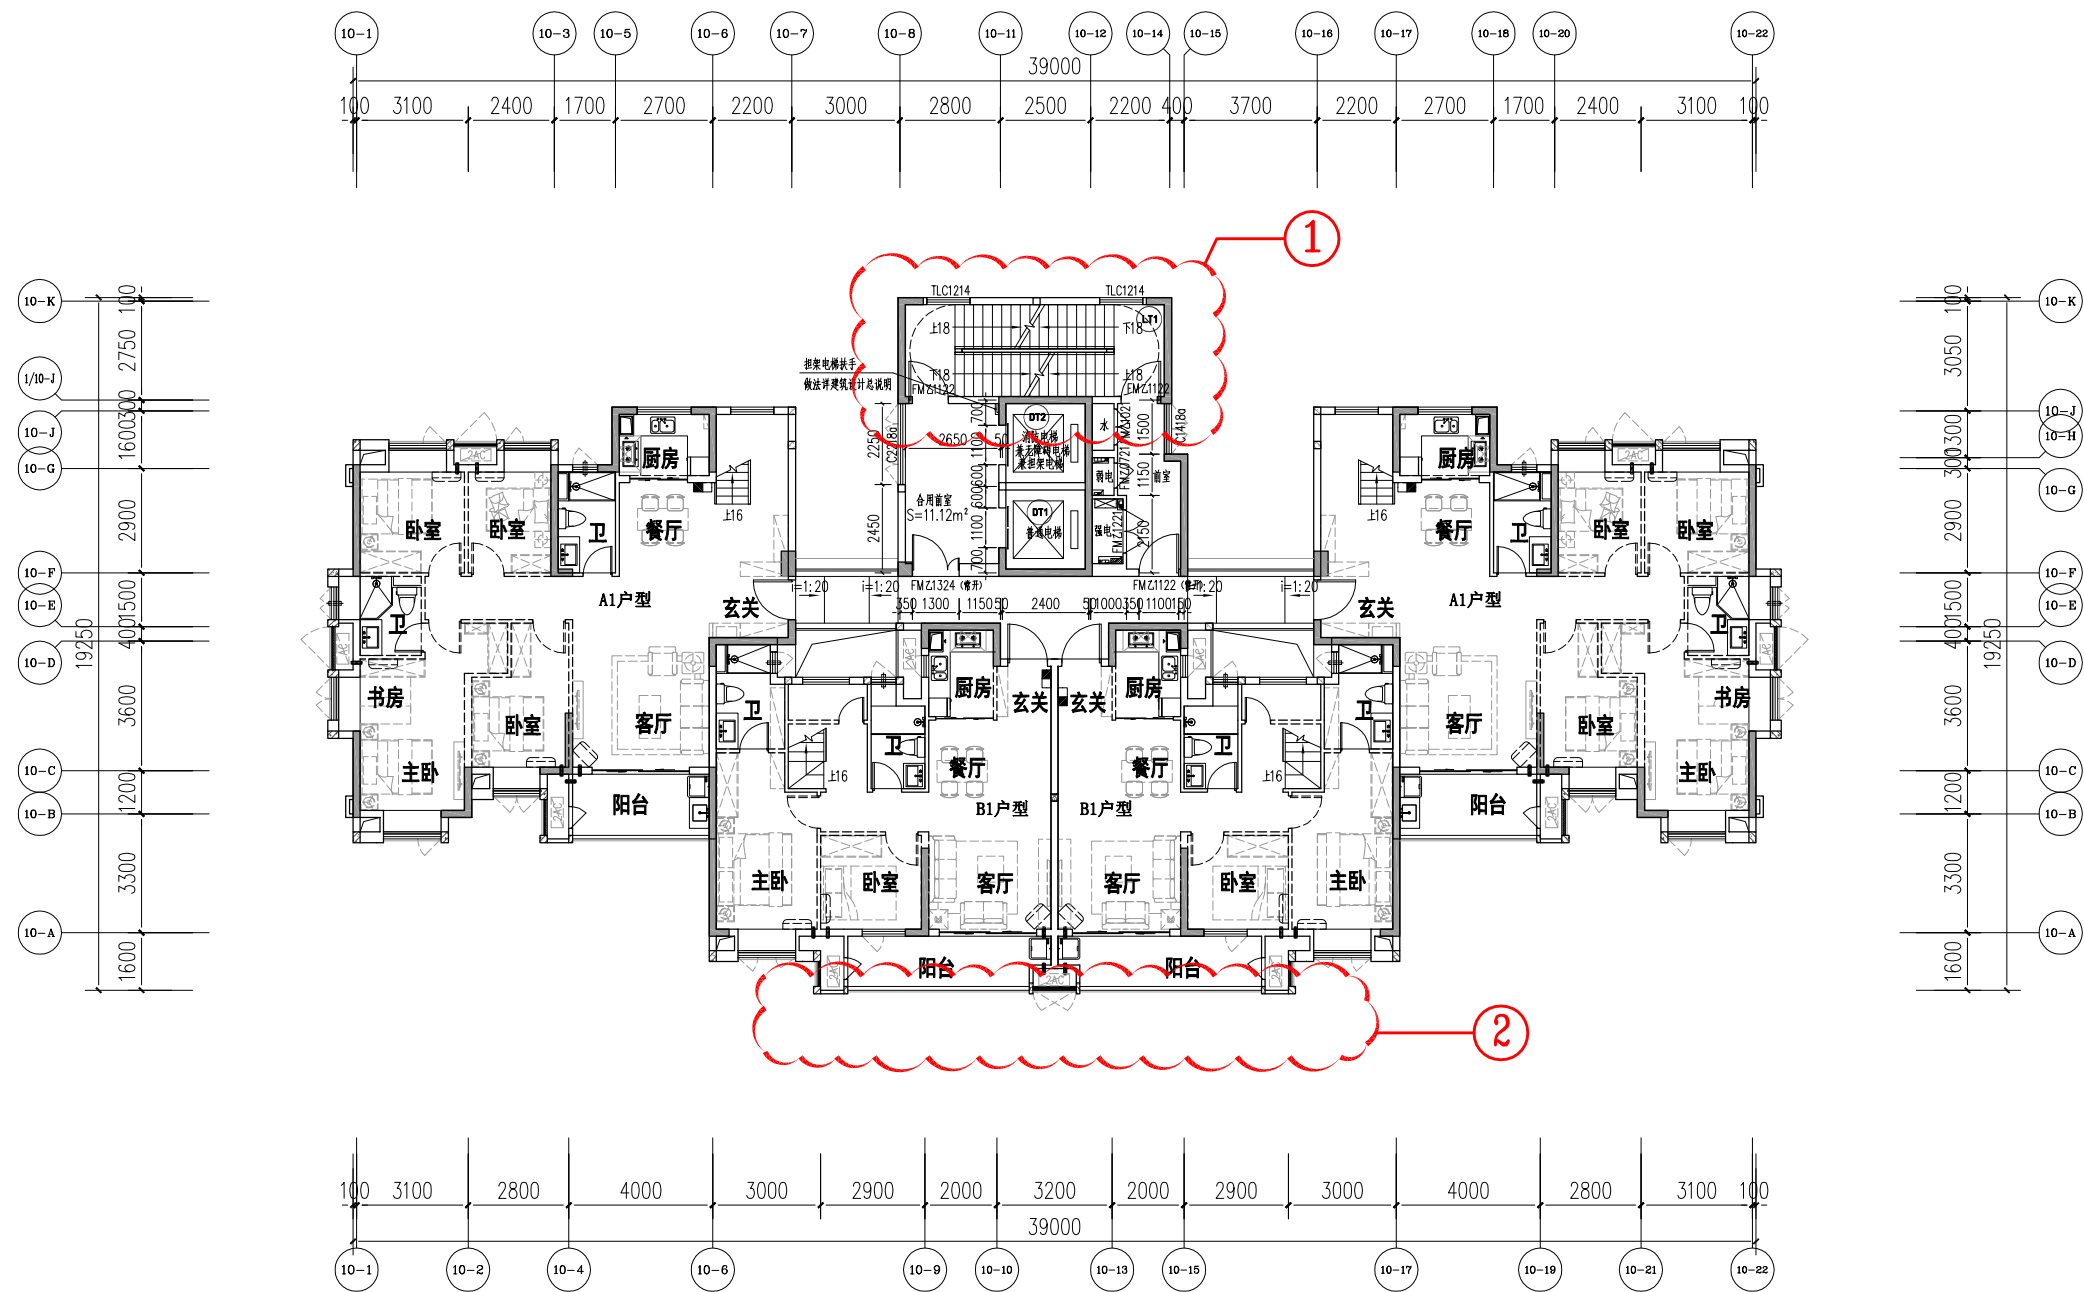

10#楼二十四层平面图 1:200 70.200

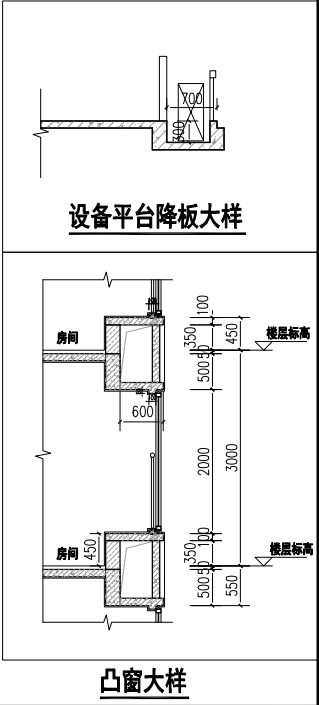


户型编号	户型	户型面积	户内面积	阳台水平投影面积	阳台面积	套内面积 (阳台+户内)	阳台占套内投影面积比例 (不含套内阳台)	公摊面积	公摊率	23+24层 面积(计容)
A1	4房3厅2卫	180.67	140.01	7.02	3.51	143.52	5.01%	37.15	20.56%	692.30
B1	2房3厅2卫	139.53	106.26	9.16	4.58	110.84	8.62%	28.69	20.56%	

10#楼二十五层平面图 变更后

变更内容:

- 1:层高由2.9m改为3.0m, 楼梯踏步相应修改。
- 2:此区域屋面底板向10-A轴移100。

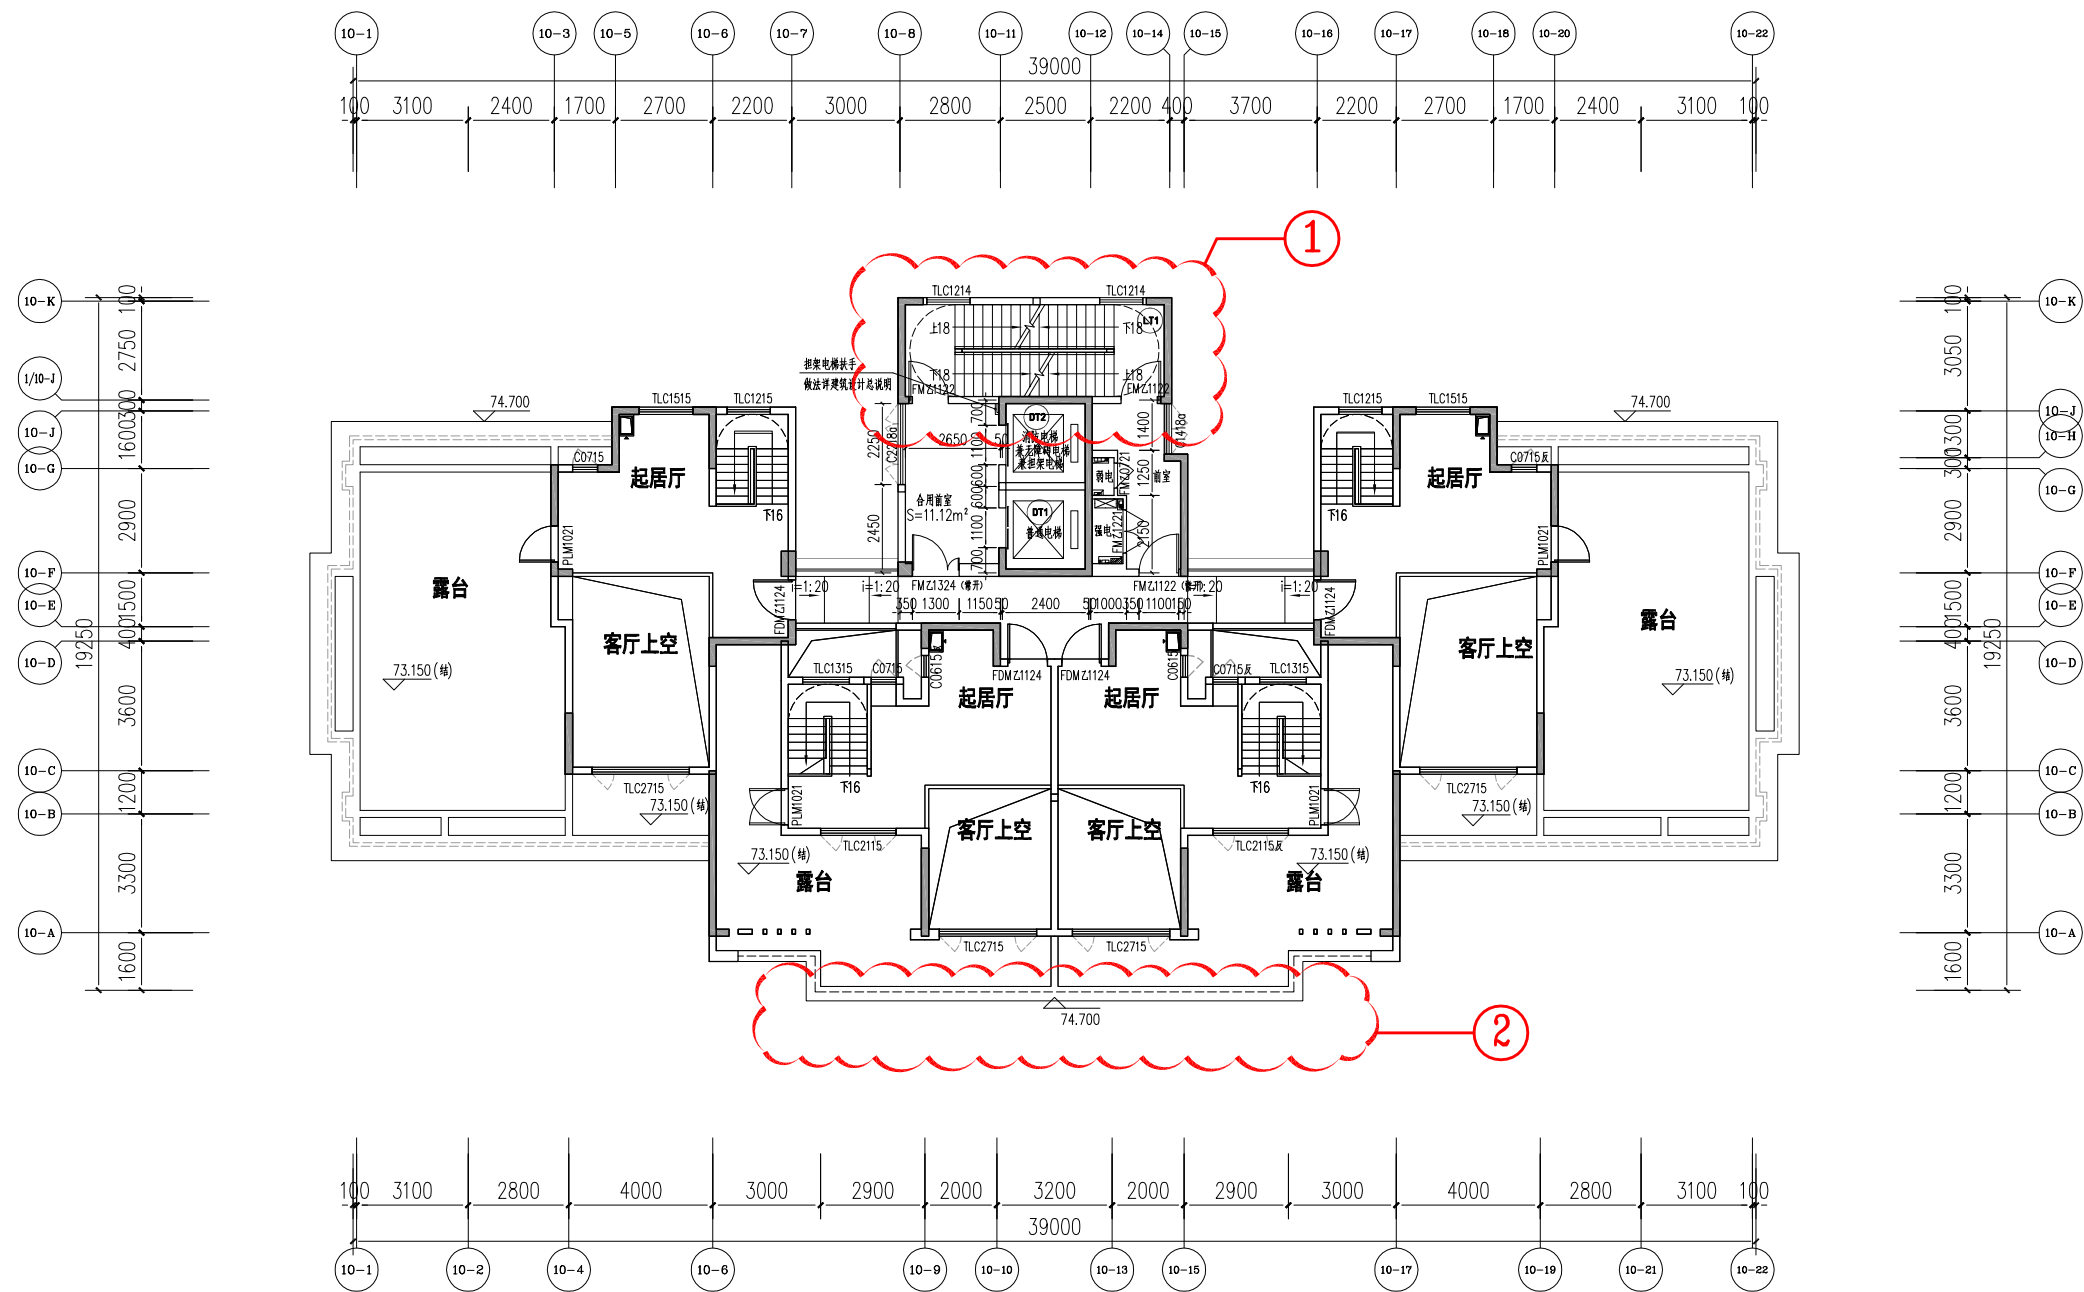


10#楼二十五层平面图 1:200

10#楼屋面层平面图 变更后

变更内容:

1:层高由2.9m改为3.0m, 楼梯踏步相应修改。

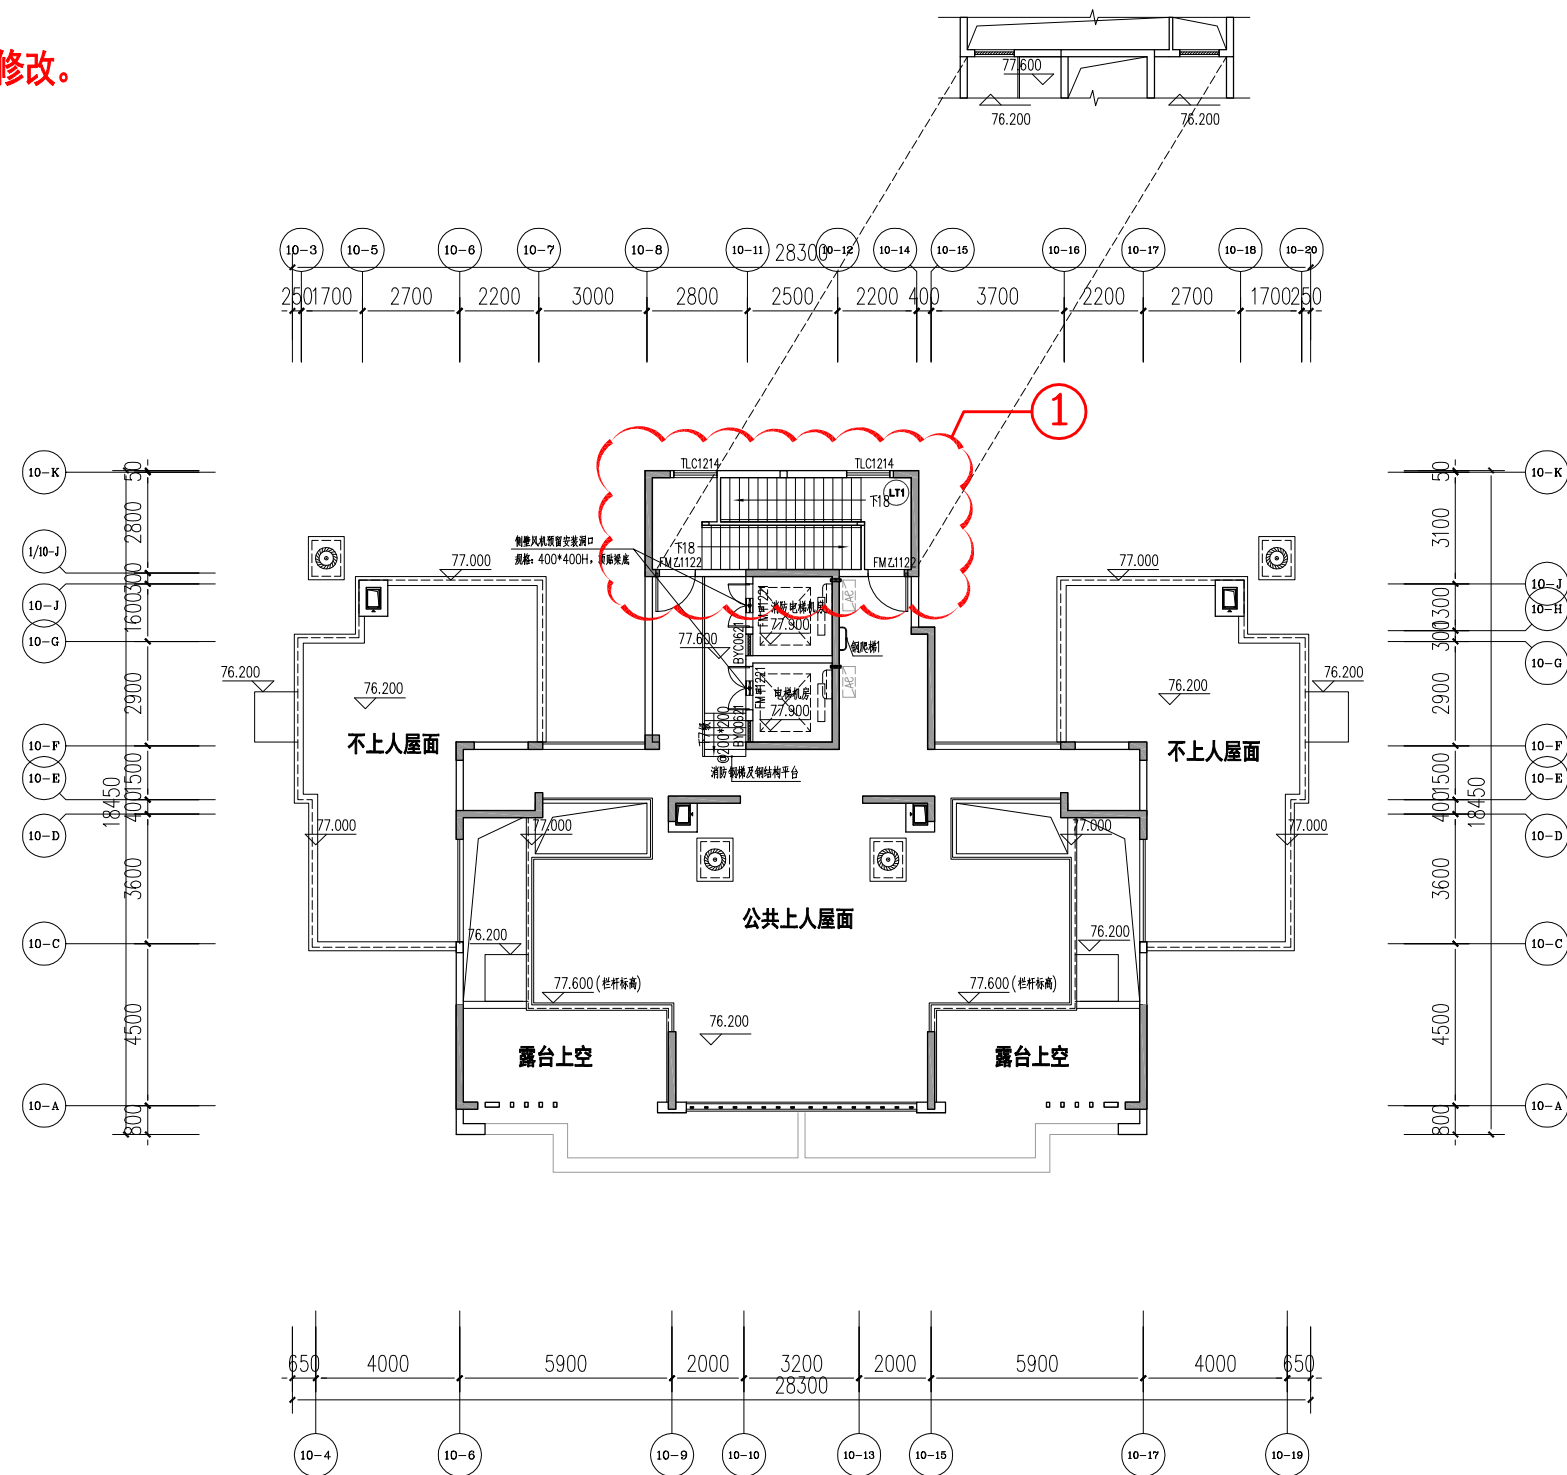


10#楼屋面层平面图 1:200

本层计容面积: 34.90m²

10#楼屋架层平面图 变更后

变更内容:

1:标准层层高由2.9m改为3.0m, 梯间层高由4.4m改为4.7m, 相应标高调整。

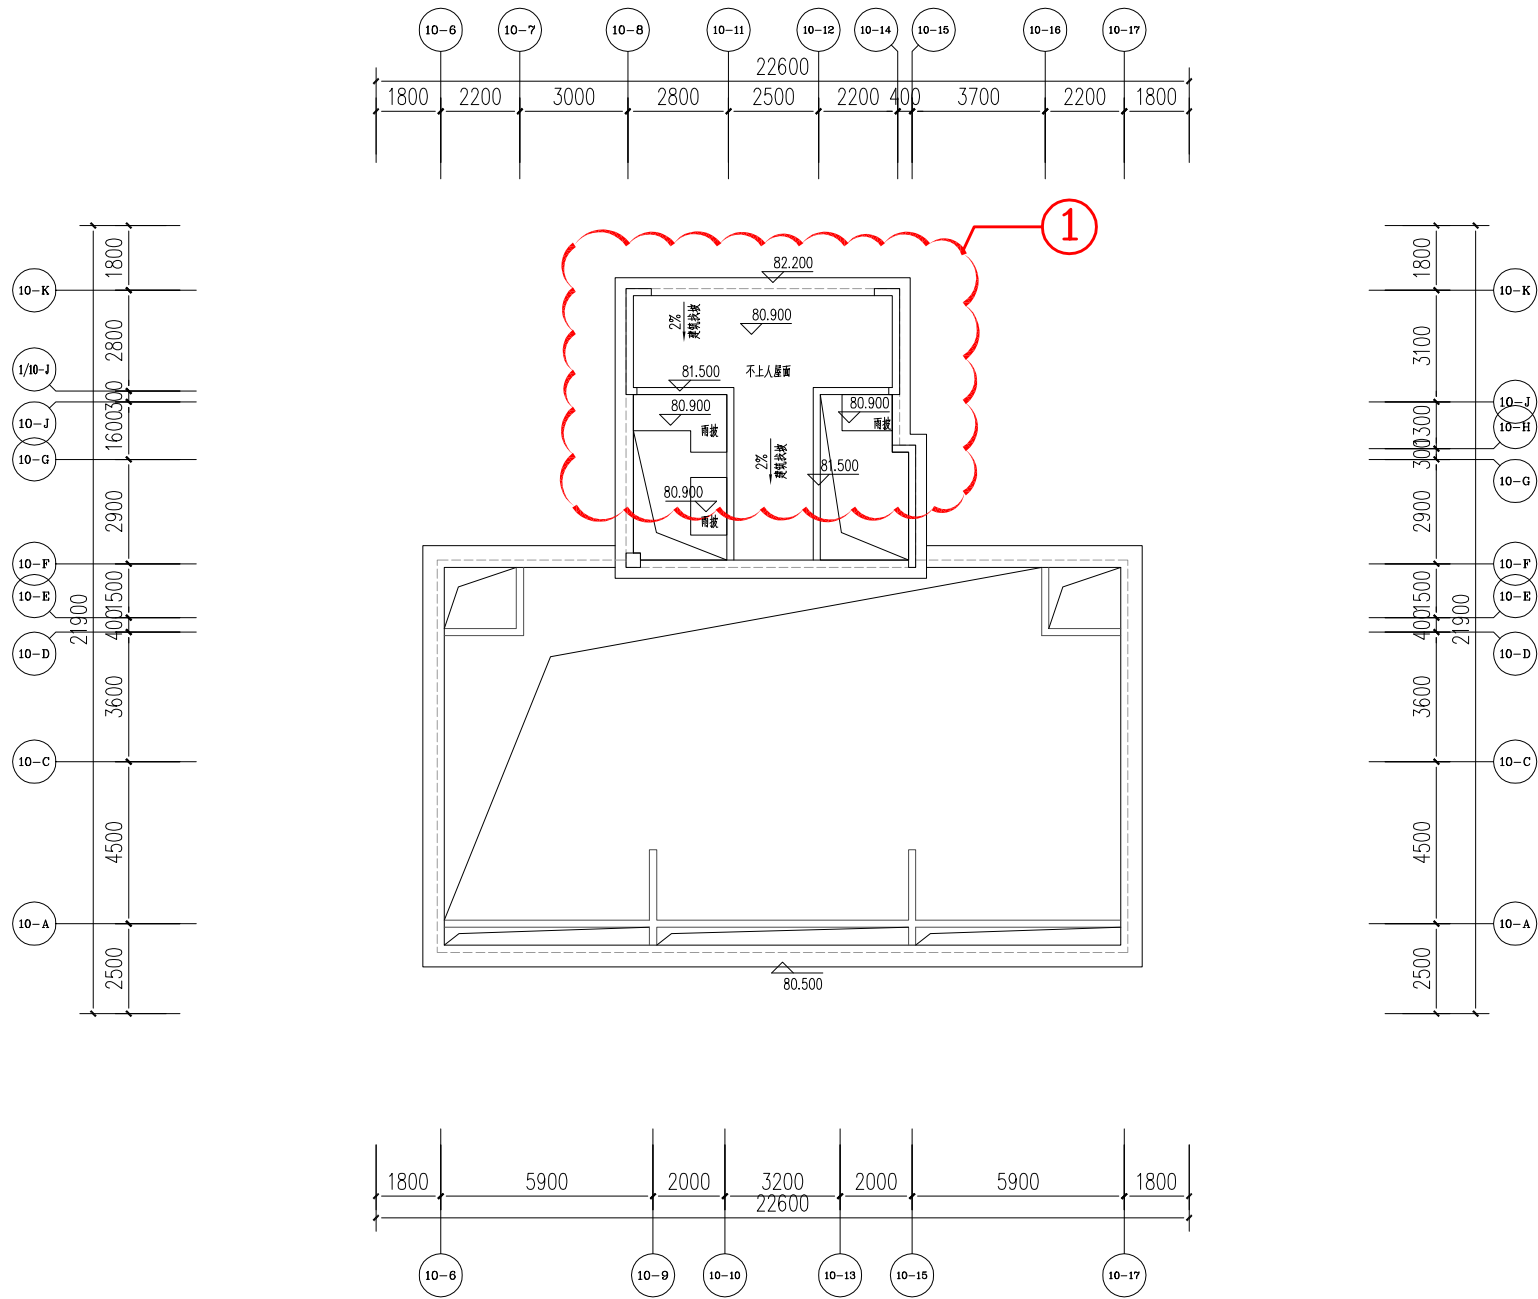


10#楼屋架层平面图 1:200

10#楼立面图 变更后

变更内容:

1:一层层高由3.6米改为4.2米，二层至二十五层层高由2.9m改为3.0m，立面尺寸相应修改。

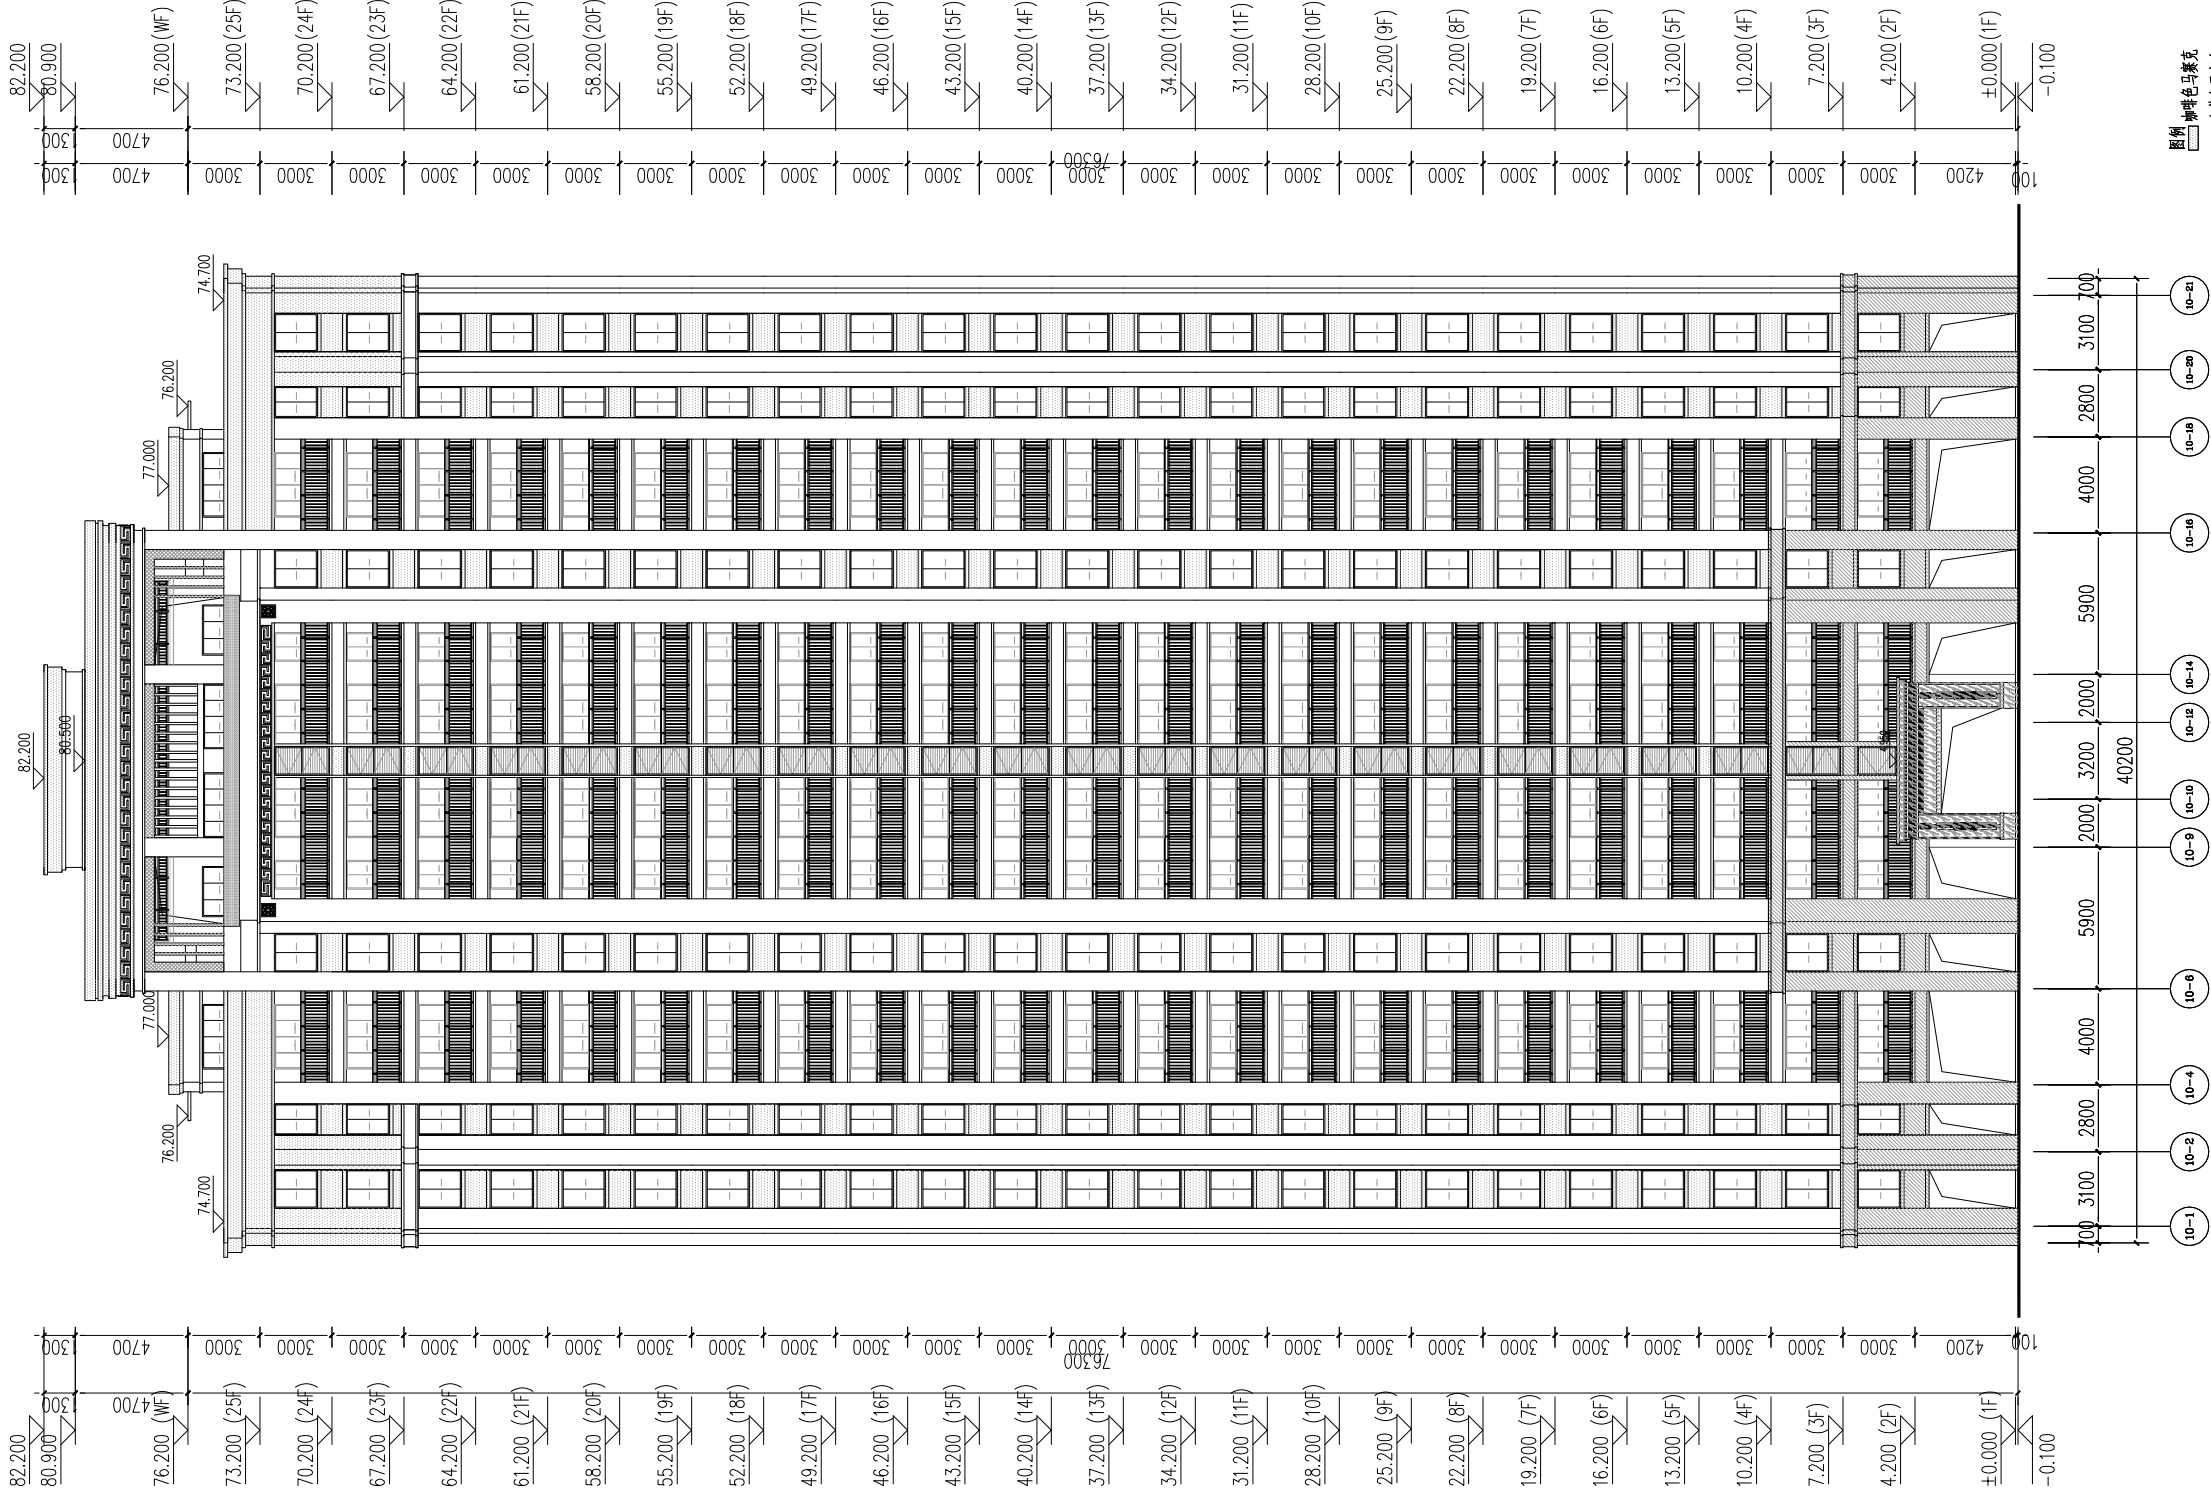


~ 10-21 轴立面图 1:300

10#楼立面图 变更后

变更内容:

1:一层层高由3.6米改为4.2米，二层至二十五层层高由2.9m改为3.0m，立面尺寸相应修改。

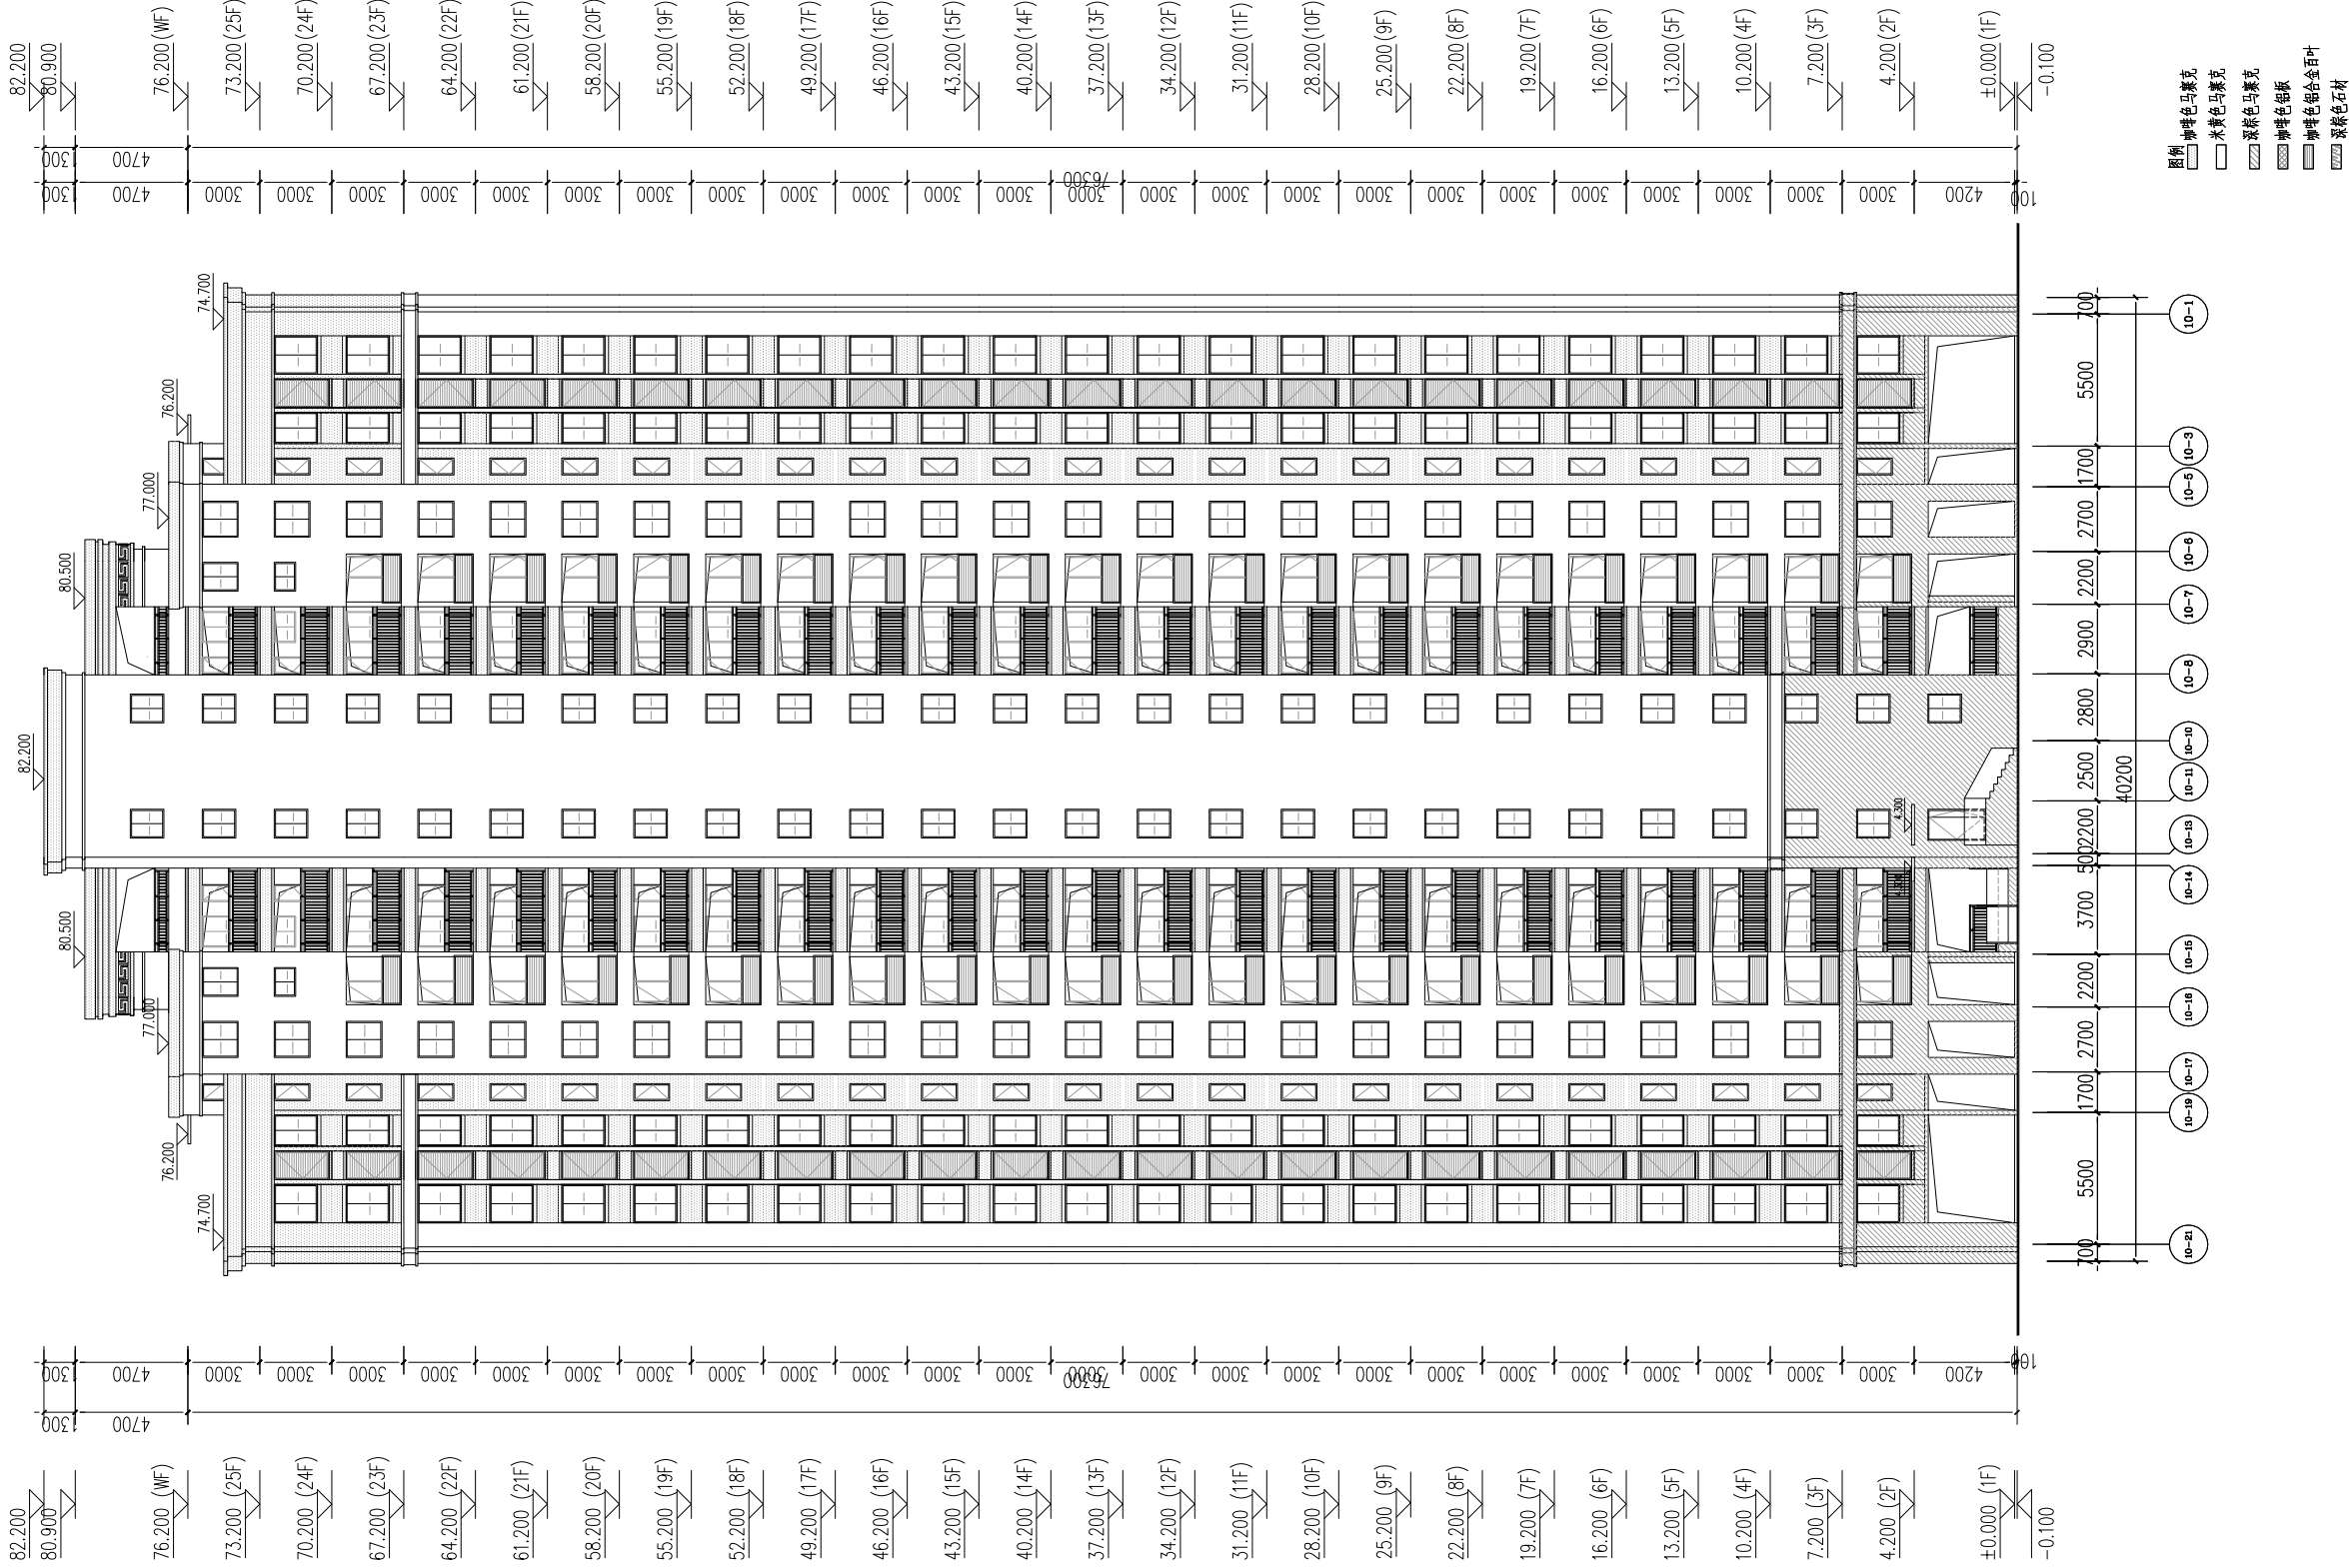


~ 10-1 轴立面图 1:300

10#楼立面图 变更后

变更内容:

1:一层层高由3.6米改为4.2米，二层至二十五层层高由2.9m改为3.0m，立面尺寸相应修改。

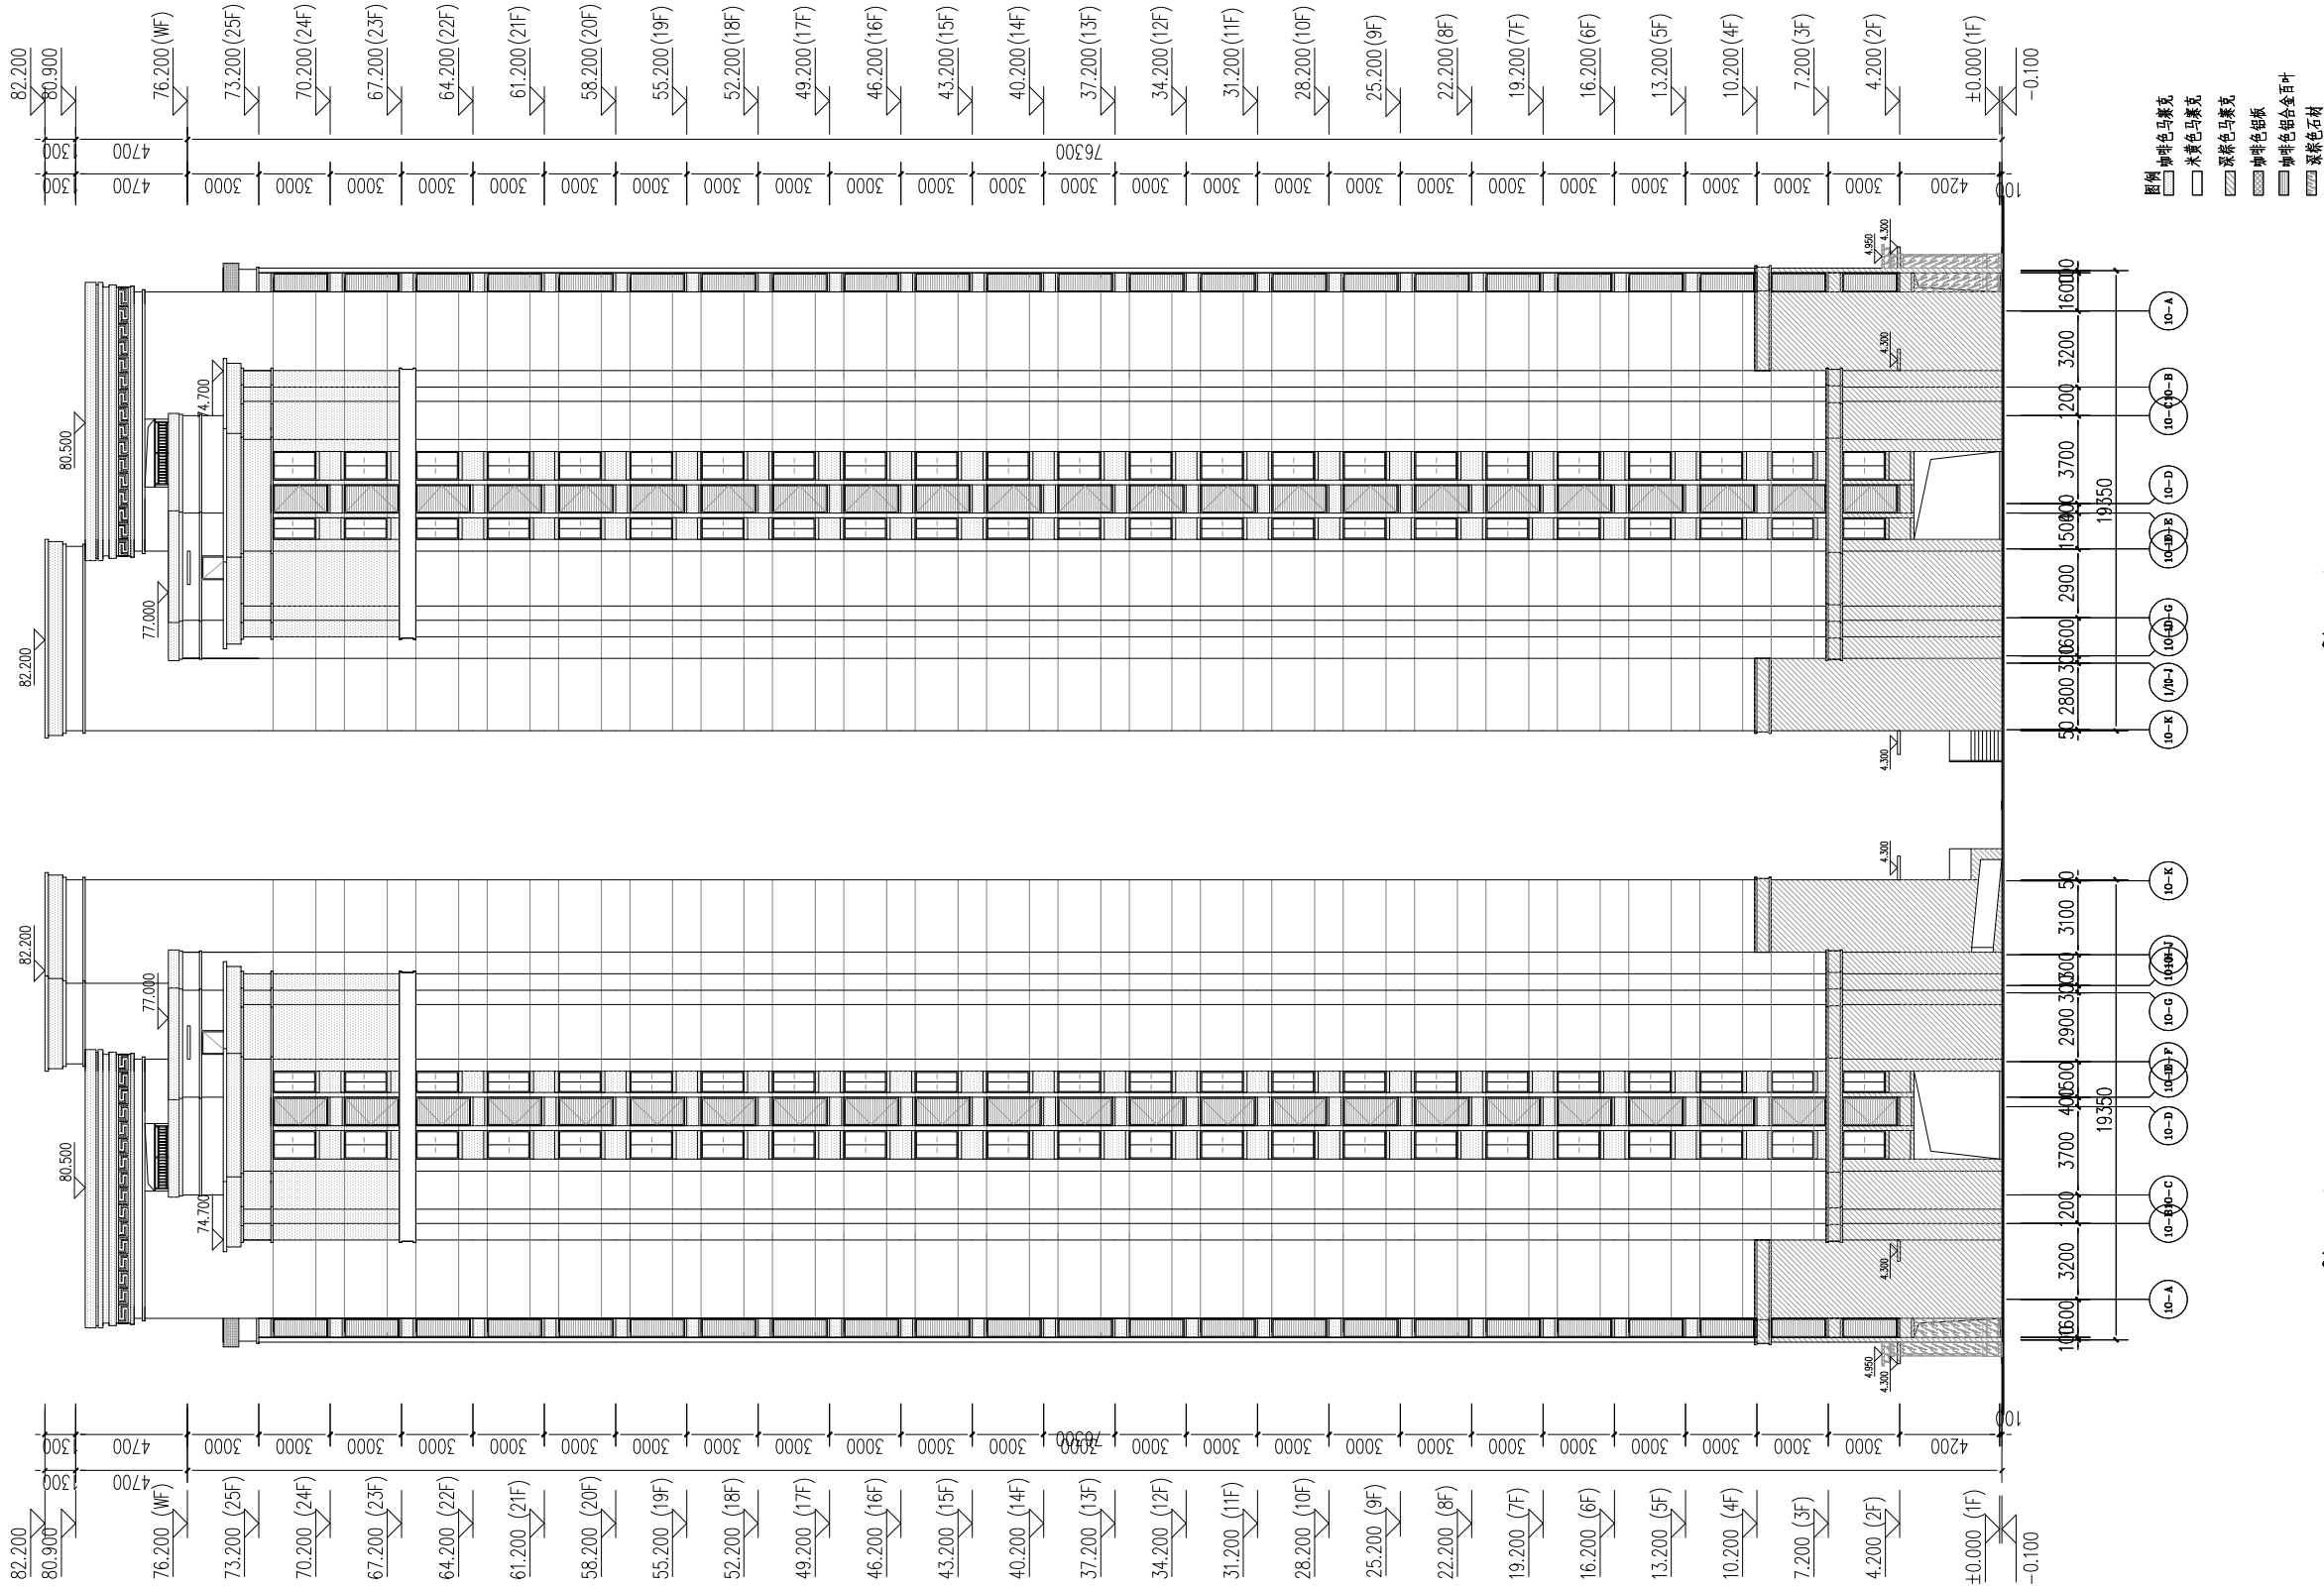


10-A ~ 10-K 轴立面图 1:300

10-K ~ 10-A 轴立面图 1:300

10#楼立面图 变更后

变更内容:

1:一层层高由3.6米改为4.2米，二层至二十五层层高由2.9m改为3.0m，剖面尺寸相应修改。

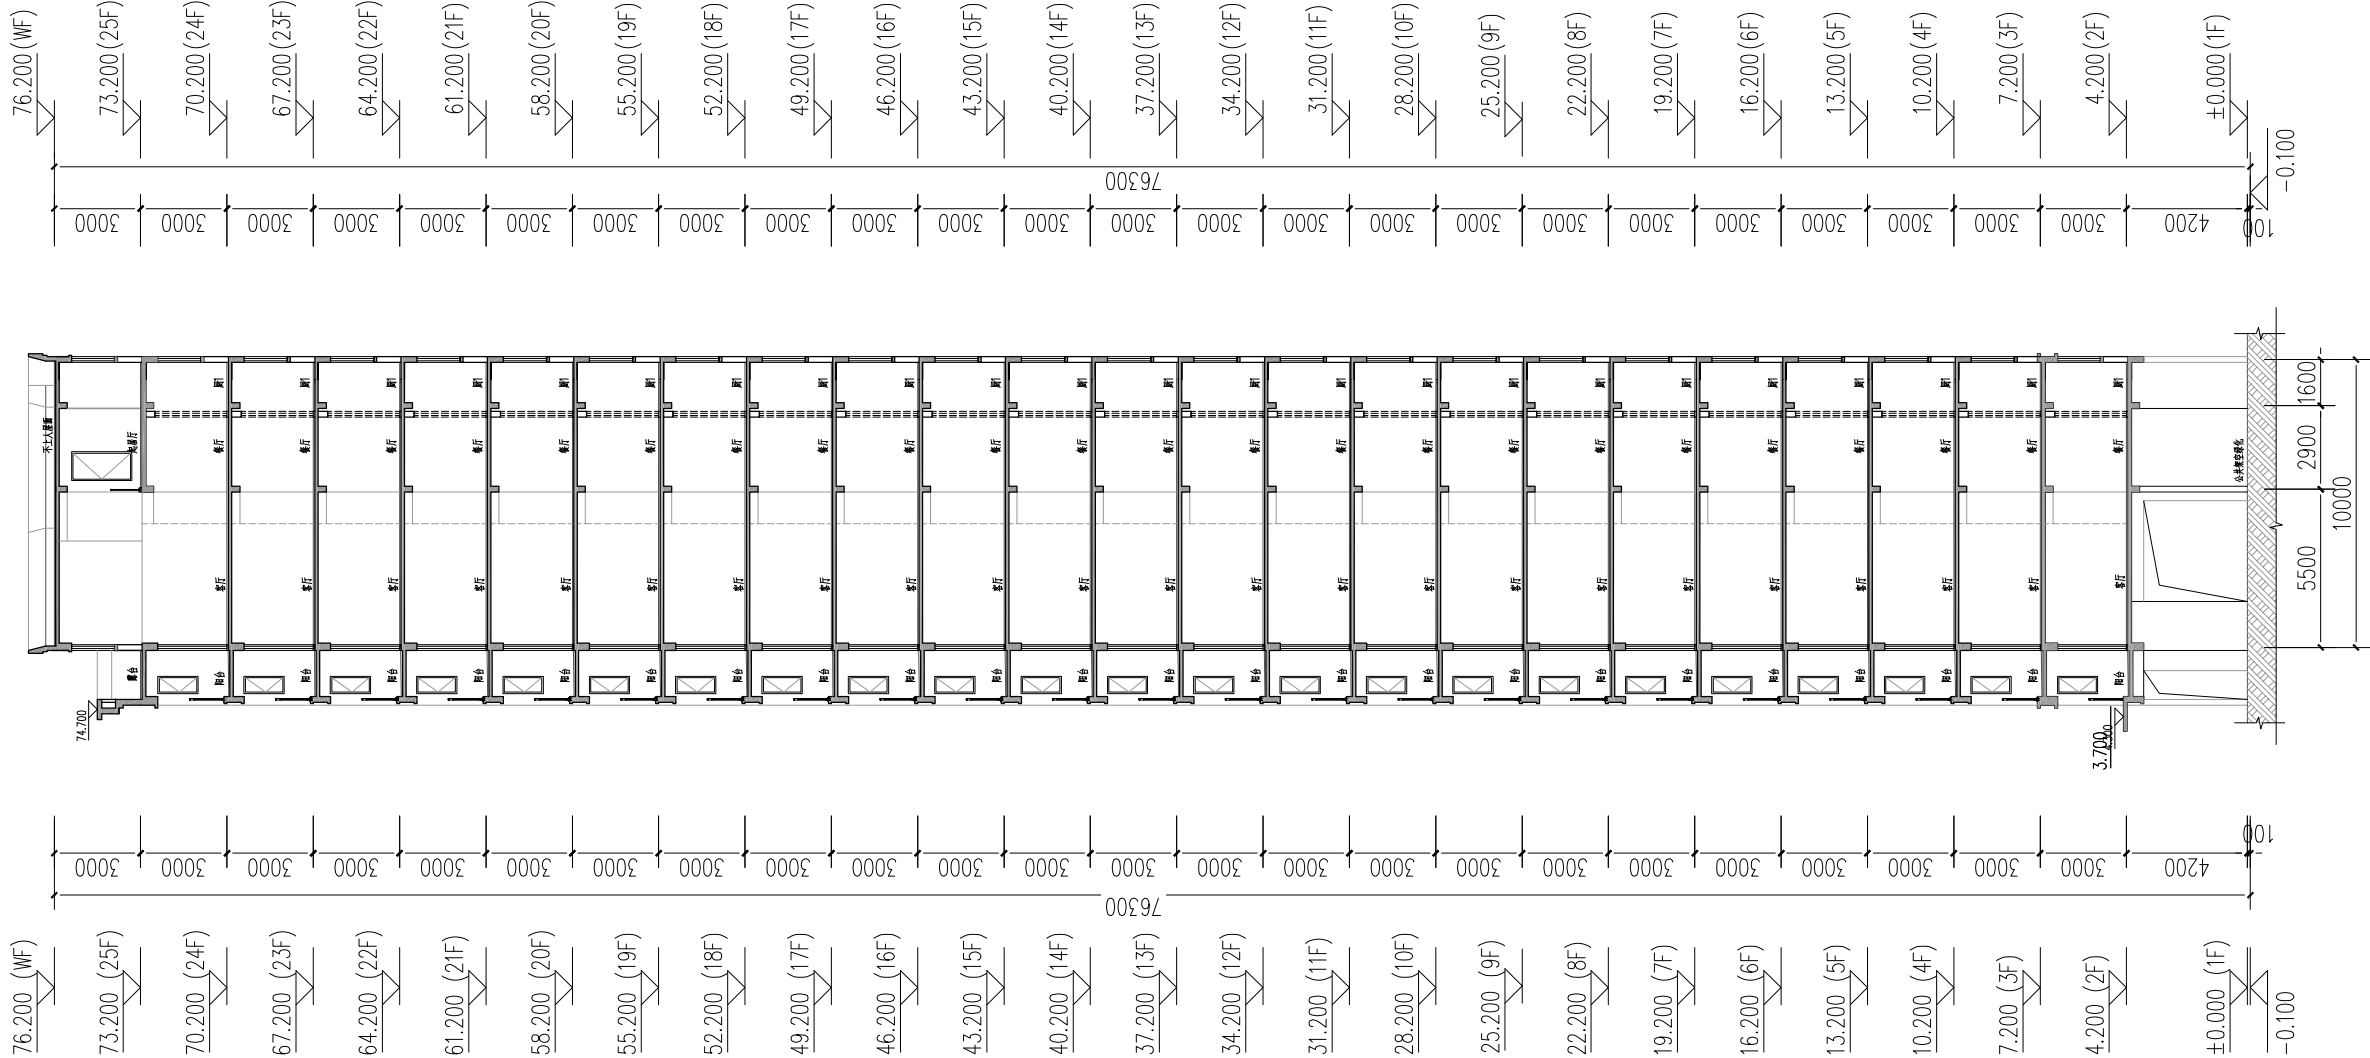

10#楼1-1剖面图 1:200