


瑞泉文苑二期方案变更


设计单位：广州博厦建筑设计研究院有限公司

变更前

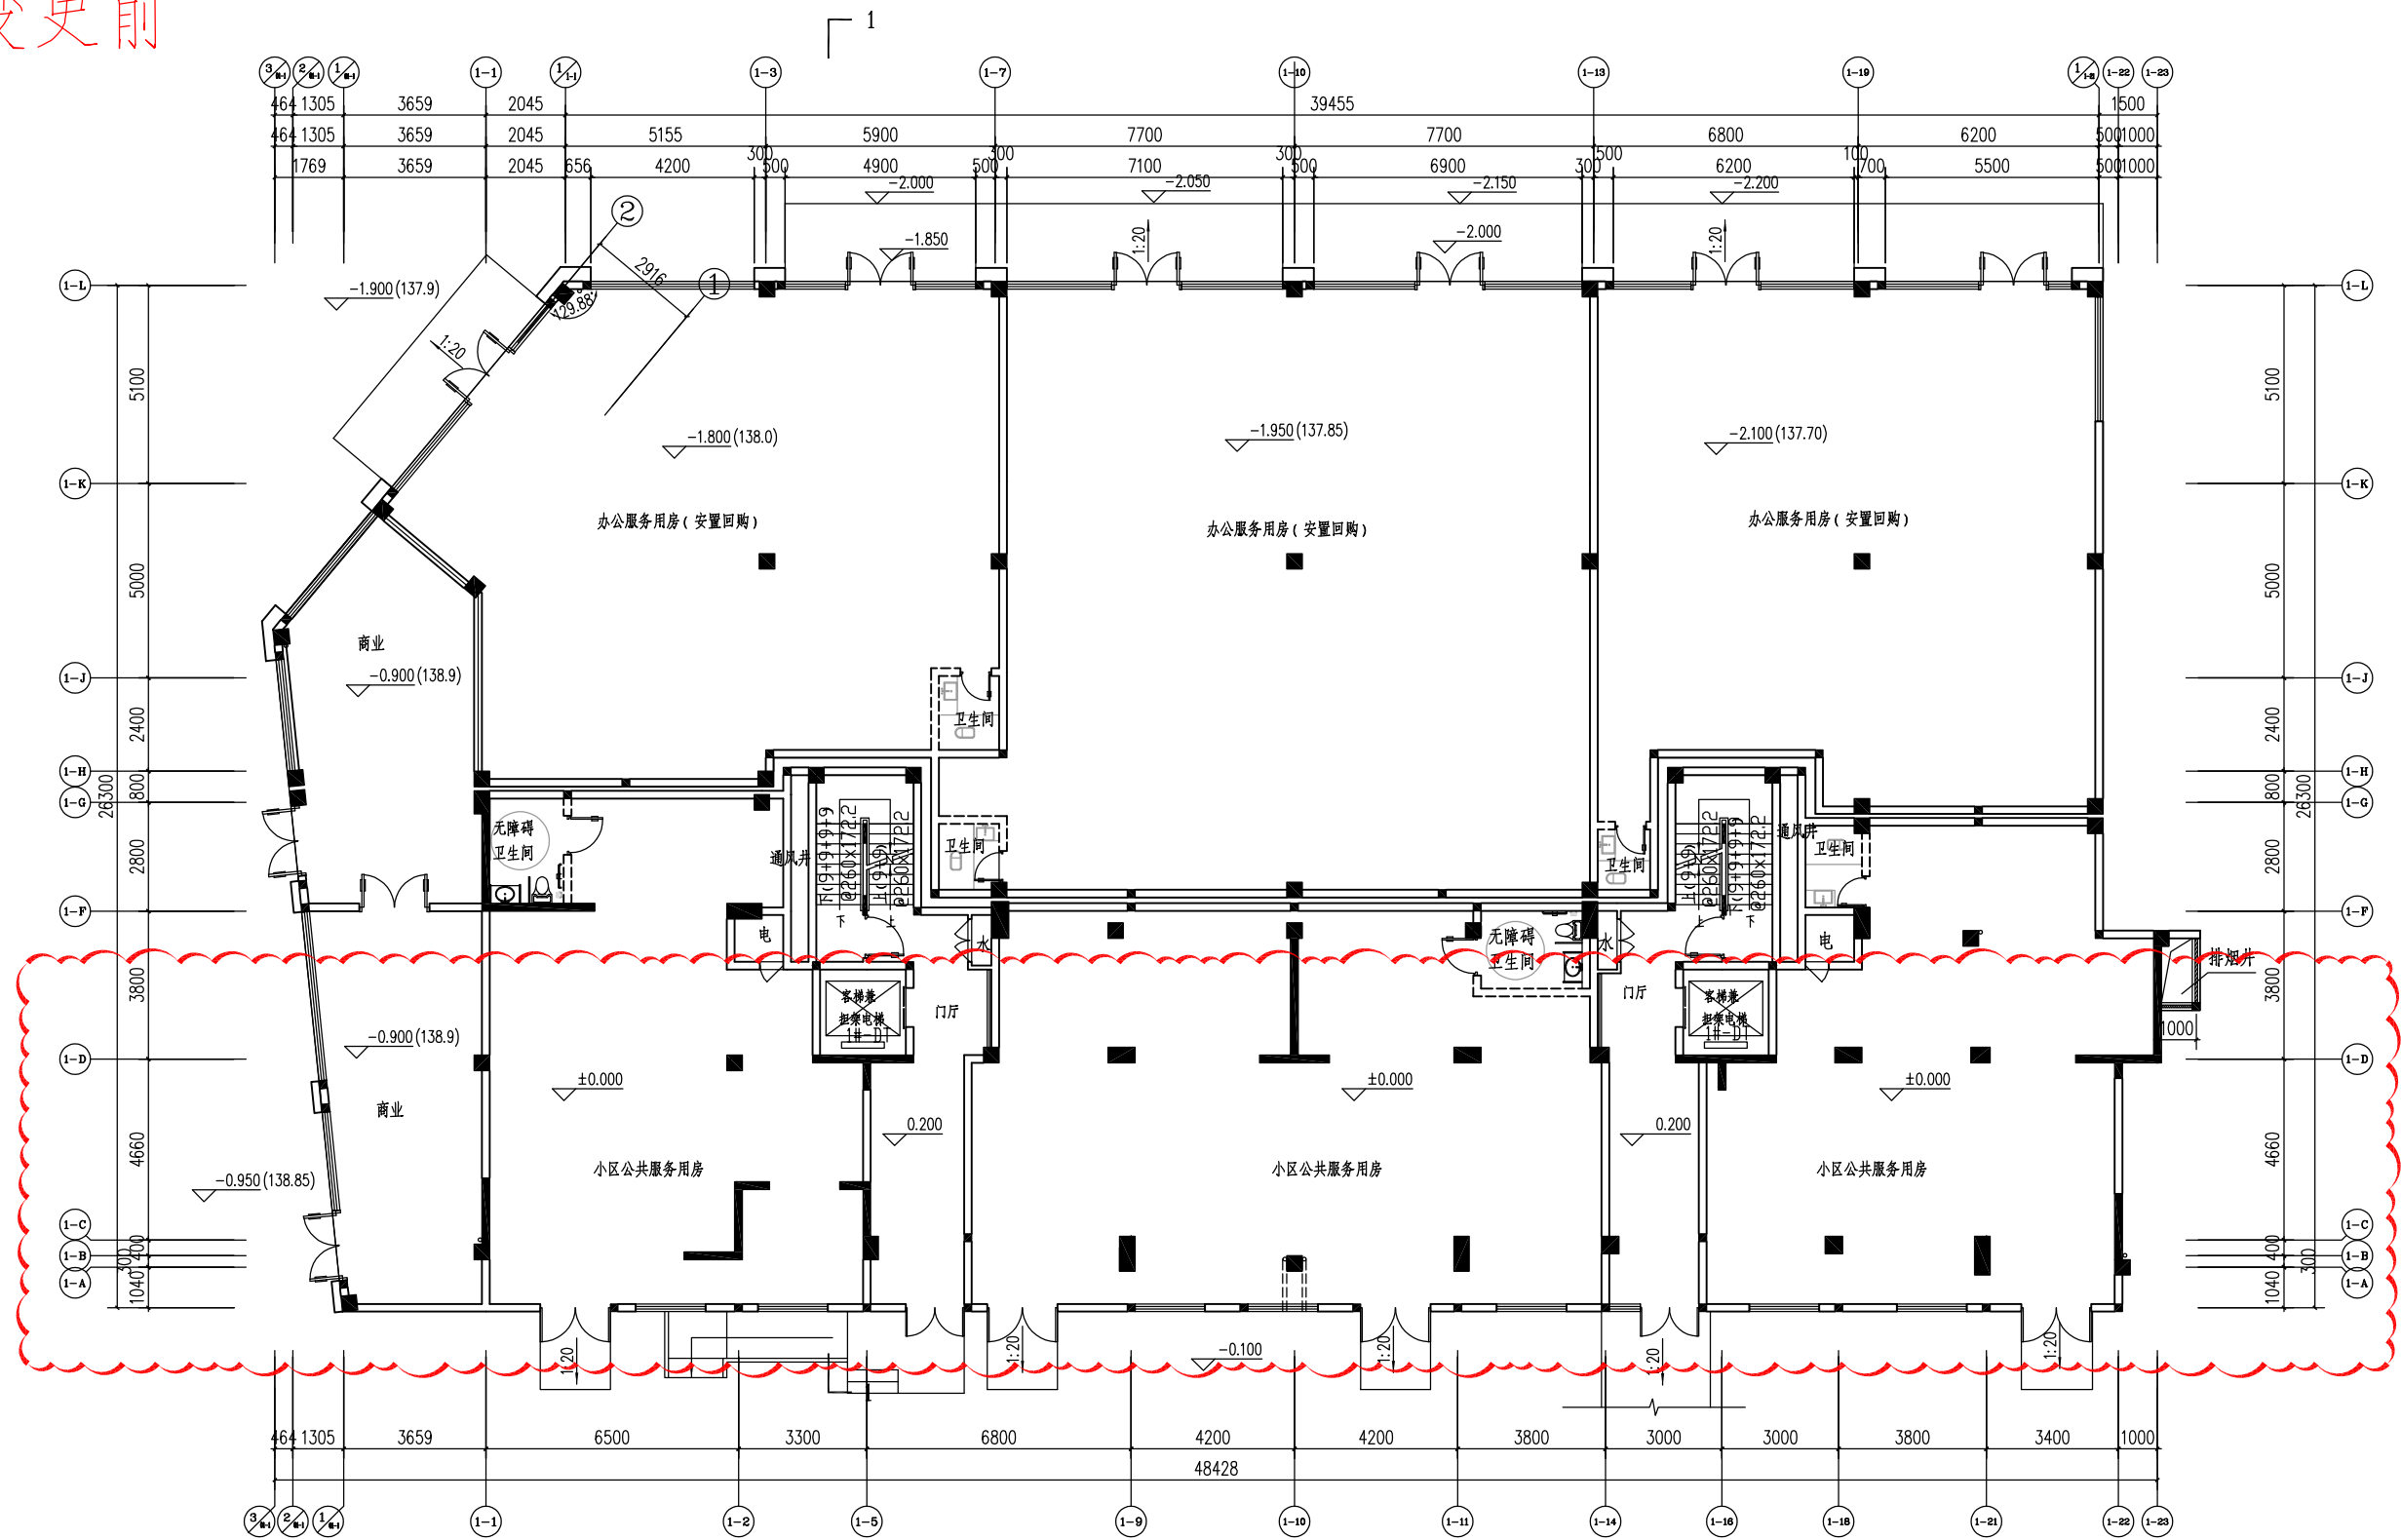

1#楼一层平面图

变更后

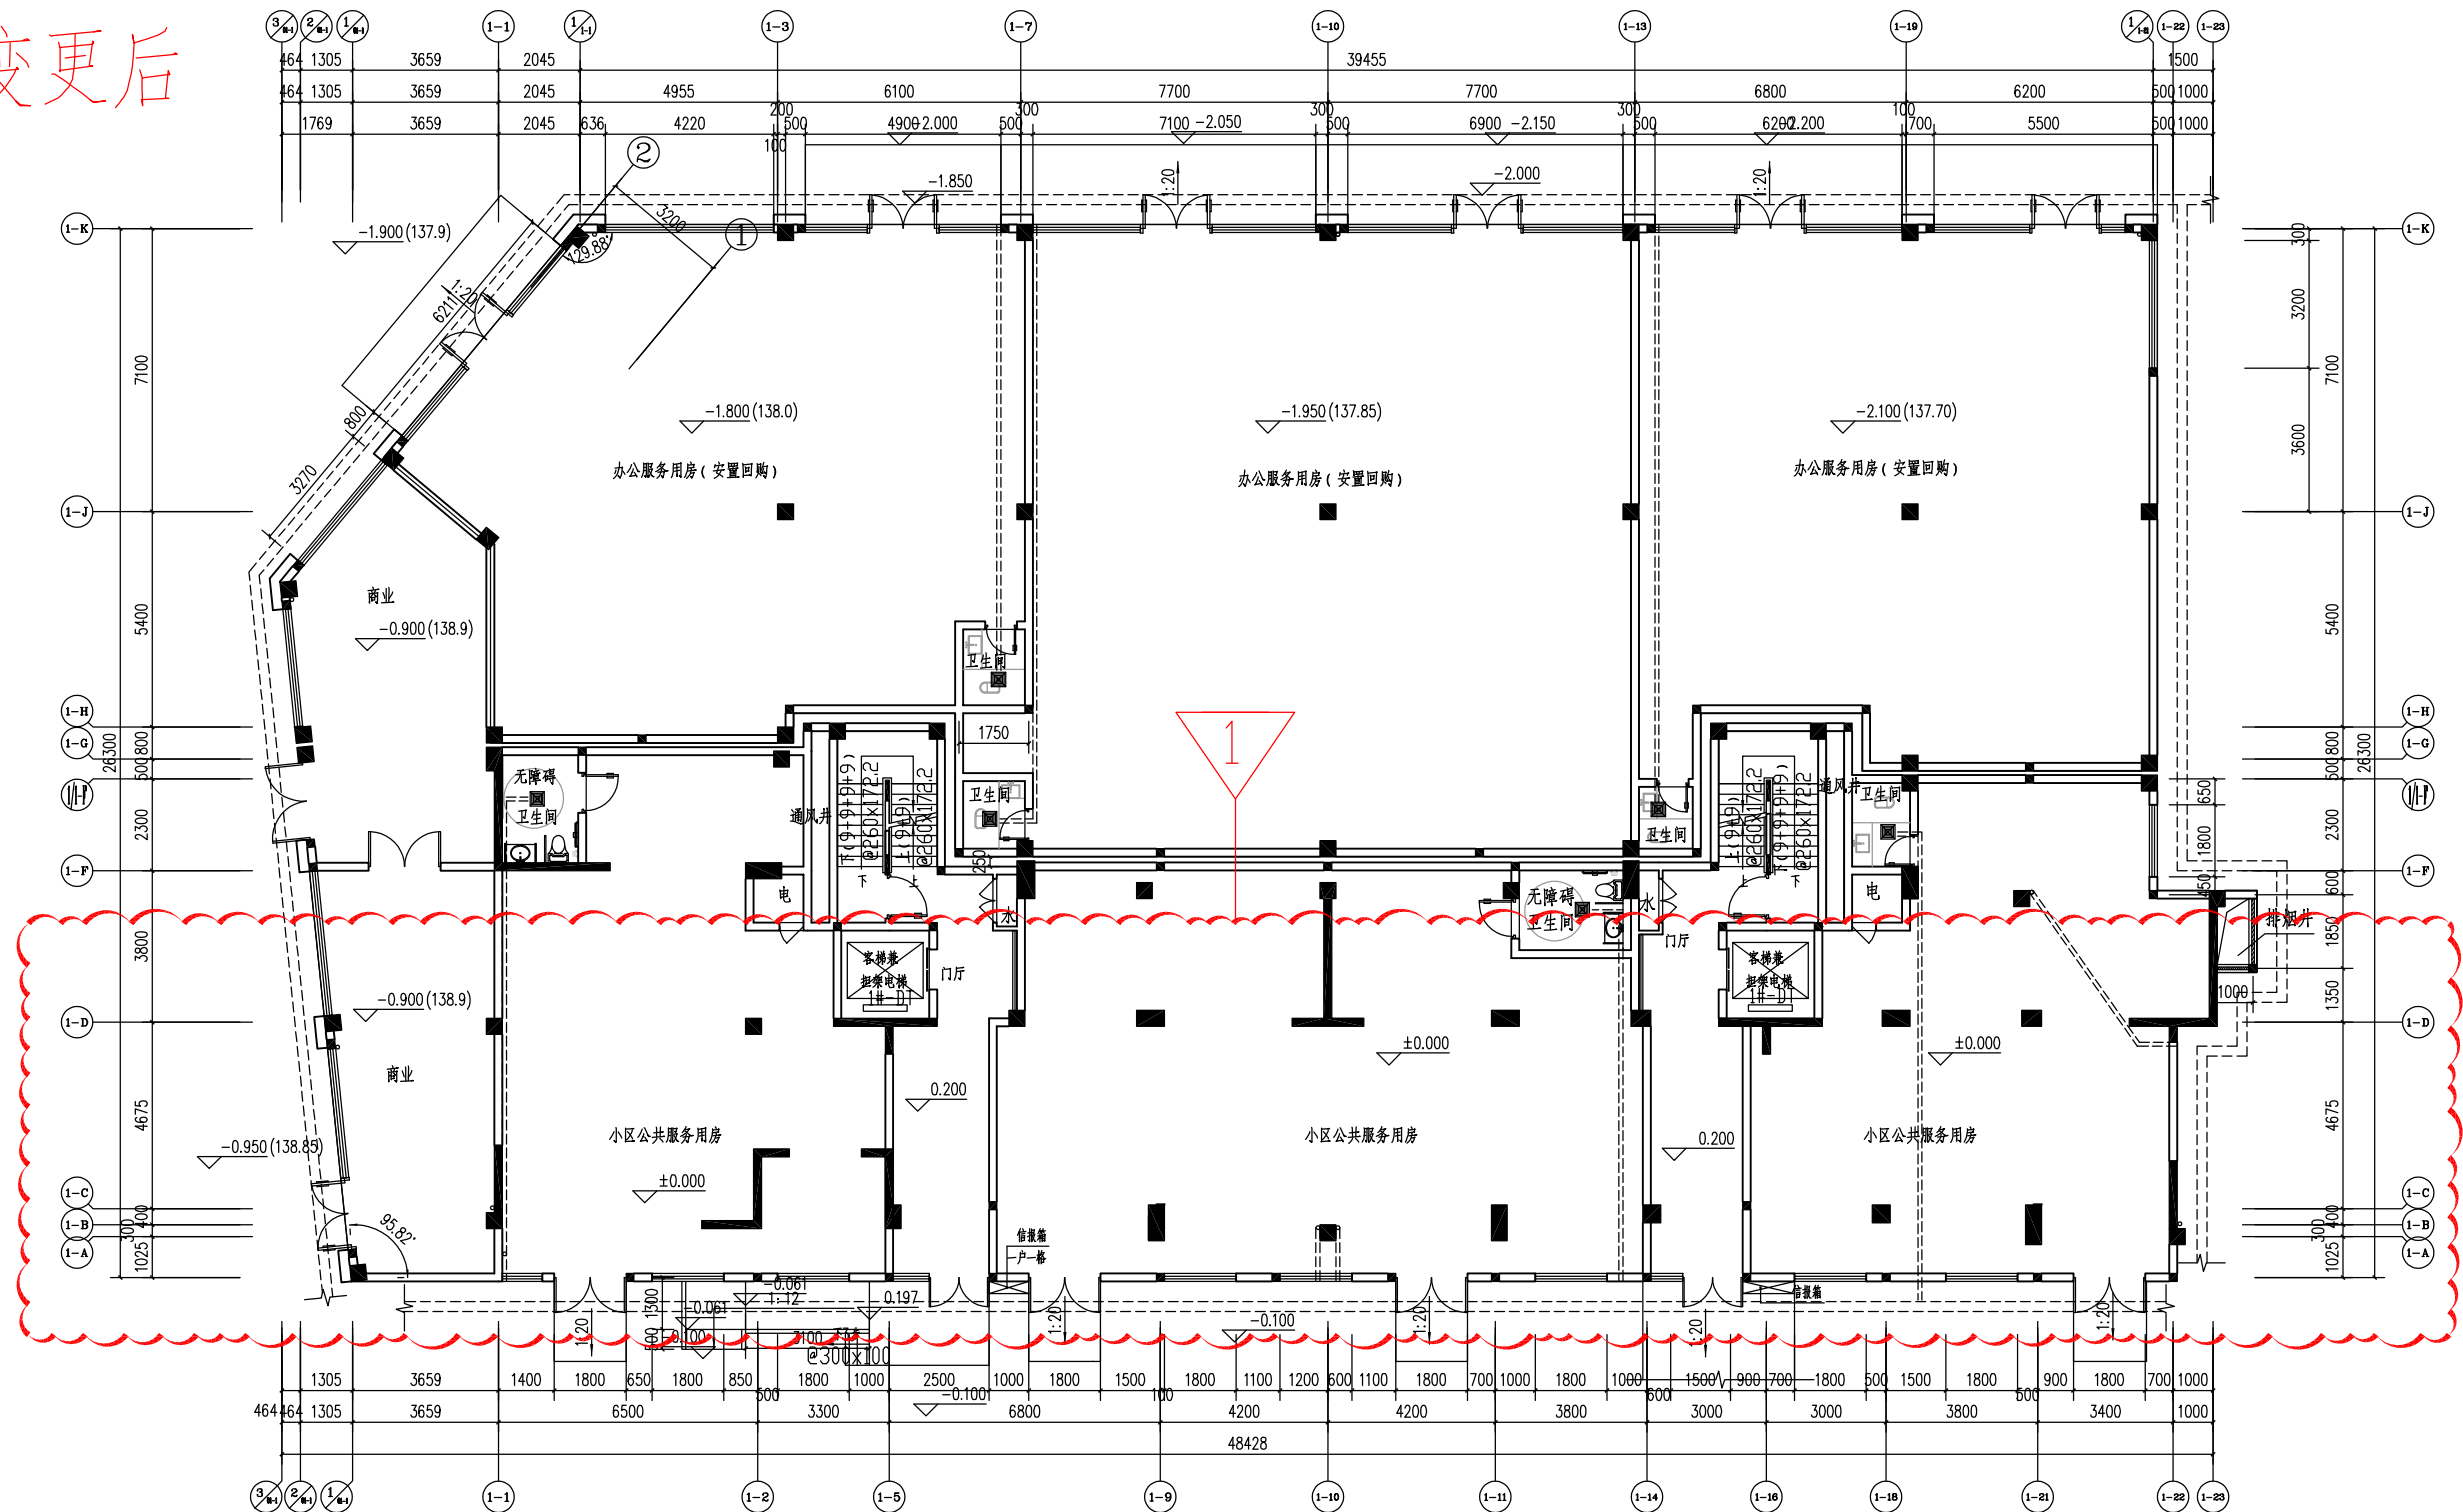

1#楼一层平面图

变更内容:


1. 图中①-D~①-B轴交①-B轴柱往下移15mm
图中①/0-①轴交①-D轴增加结构柱

变更前



1#楼二层平面图

变更后

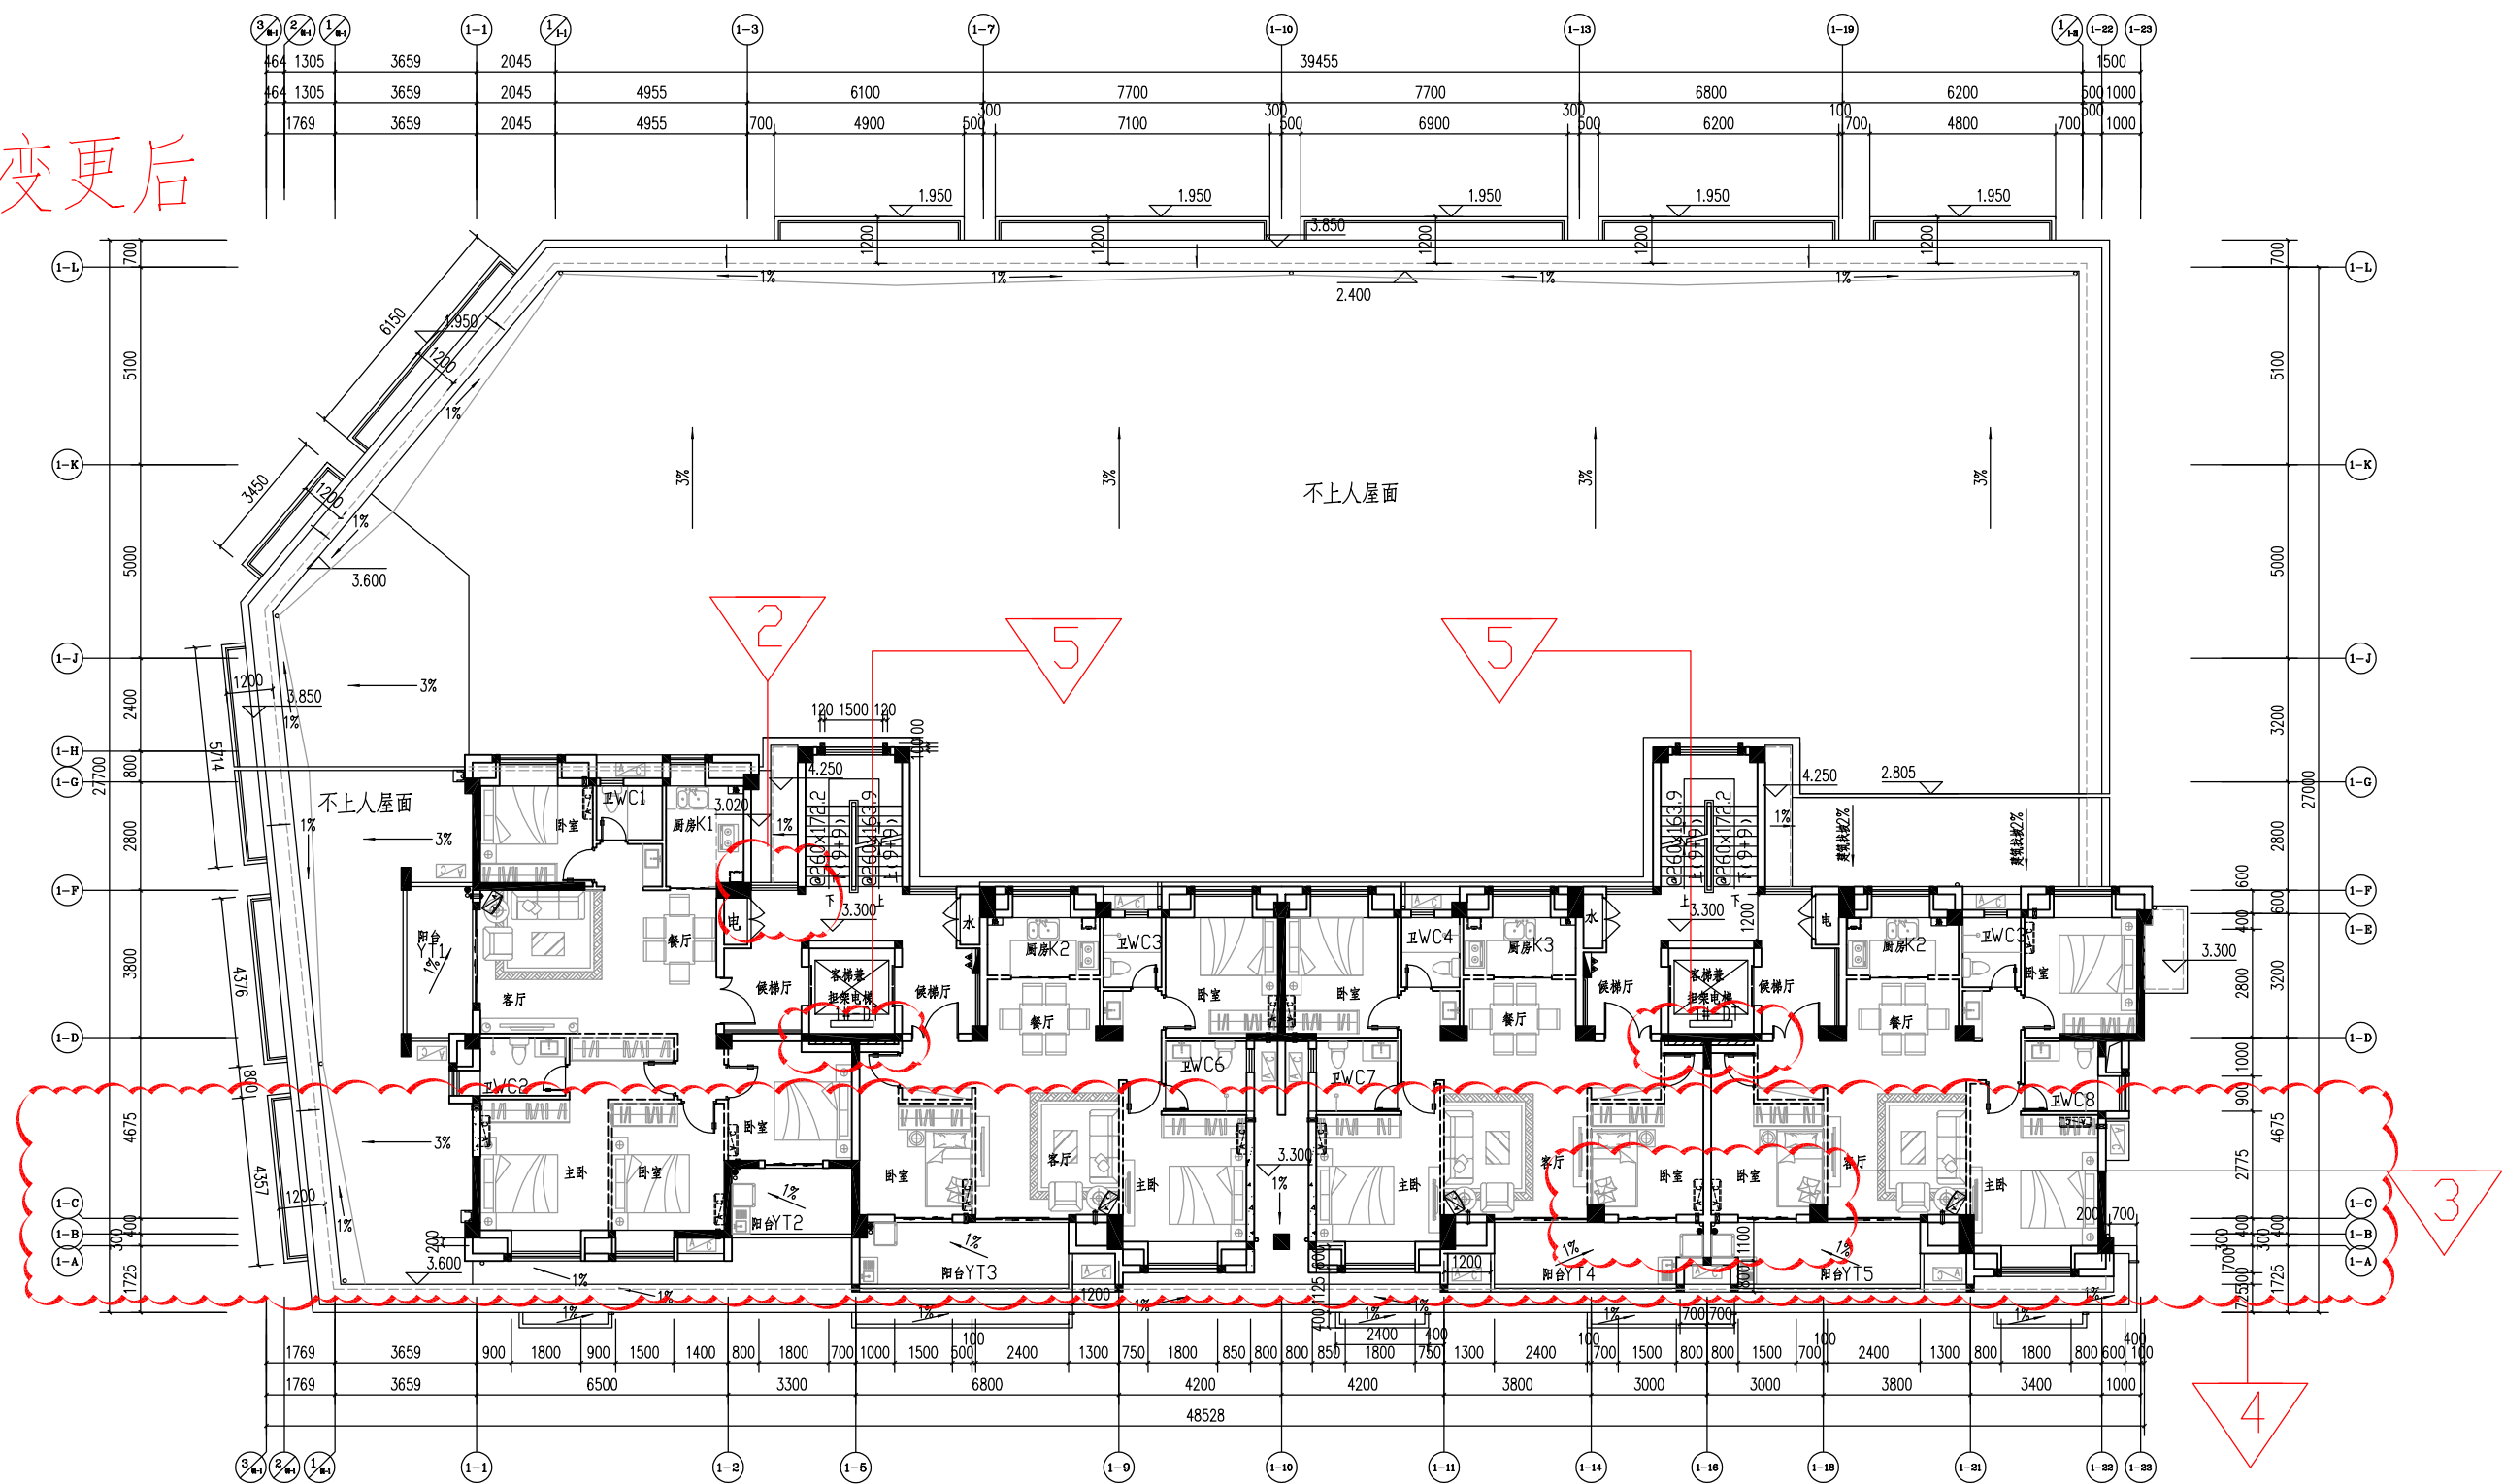


1#楼二层平面图

变更内容:


- 图中①~④轴交①-F轴外墙往①-G轴方向移100mm
- 图中①-G轴交①-14轴、①-18轴的柱子往①-D轴方向移250mm与外墙平
- 图中①-A~①-B轴交①-B轴柱往下移15mm,①-D~①-G轴尺寸由4660mm改为4675mm
- 图中①-D轴交①-5轴、①-16轴增设一段电梯隔音墙

变更前

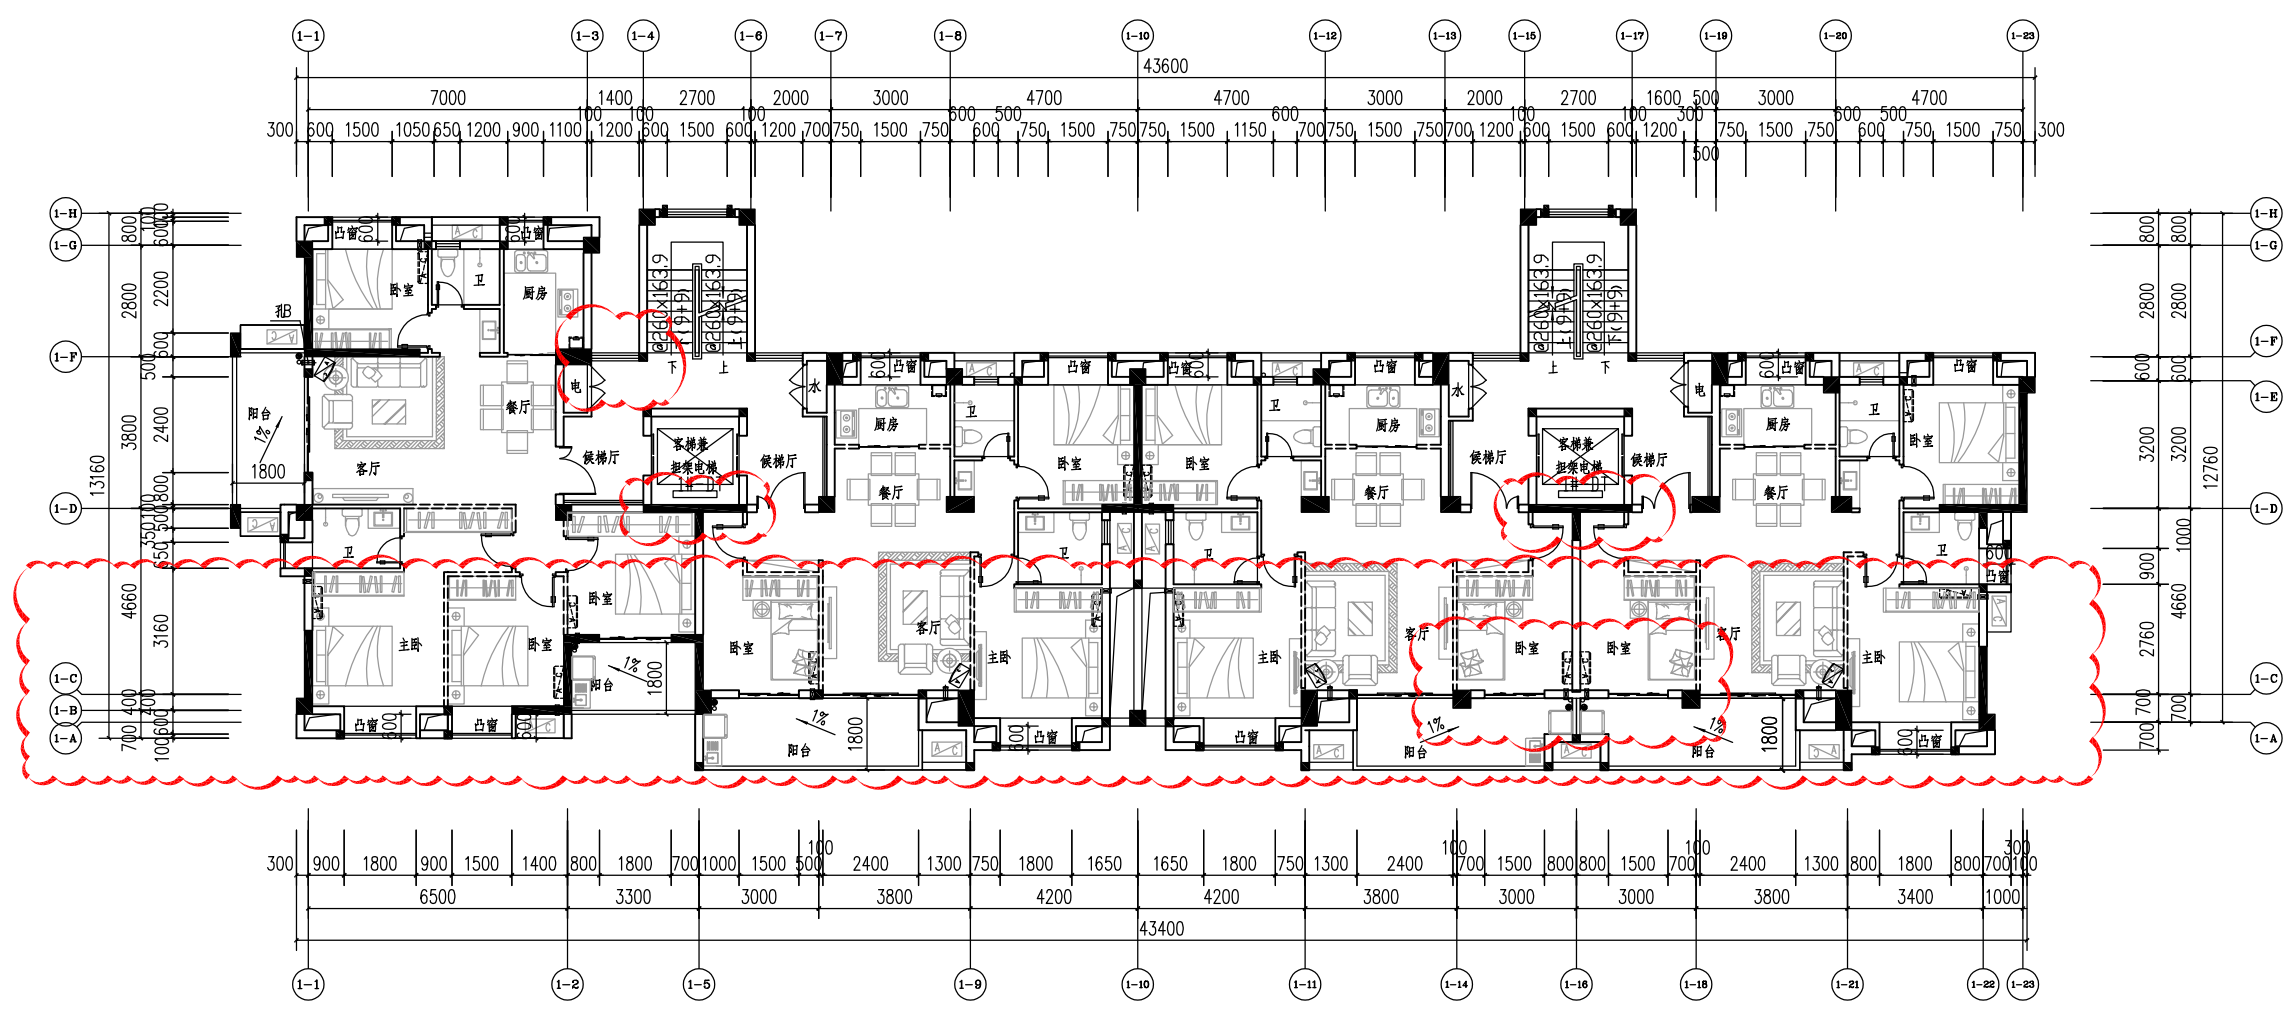

1#楼三~十层平面图

变更后

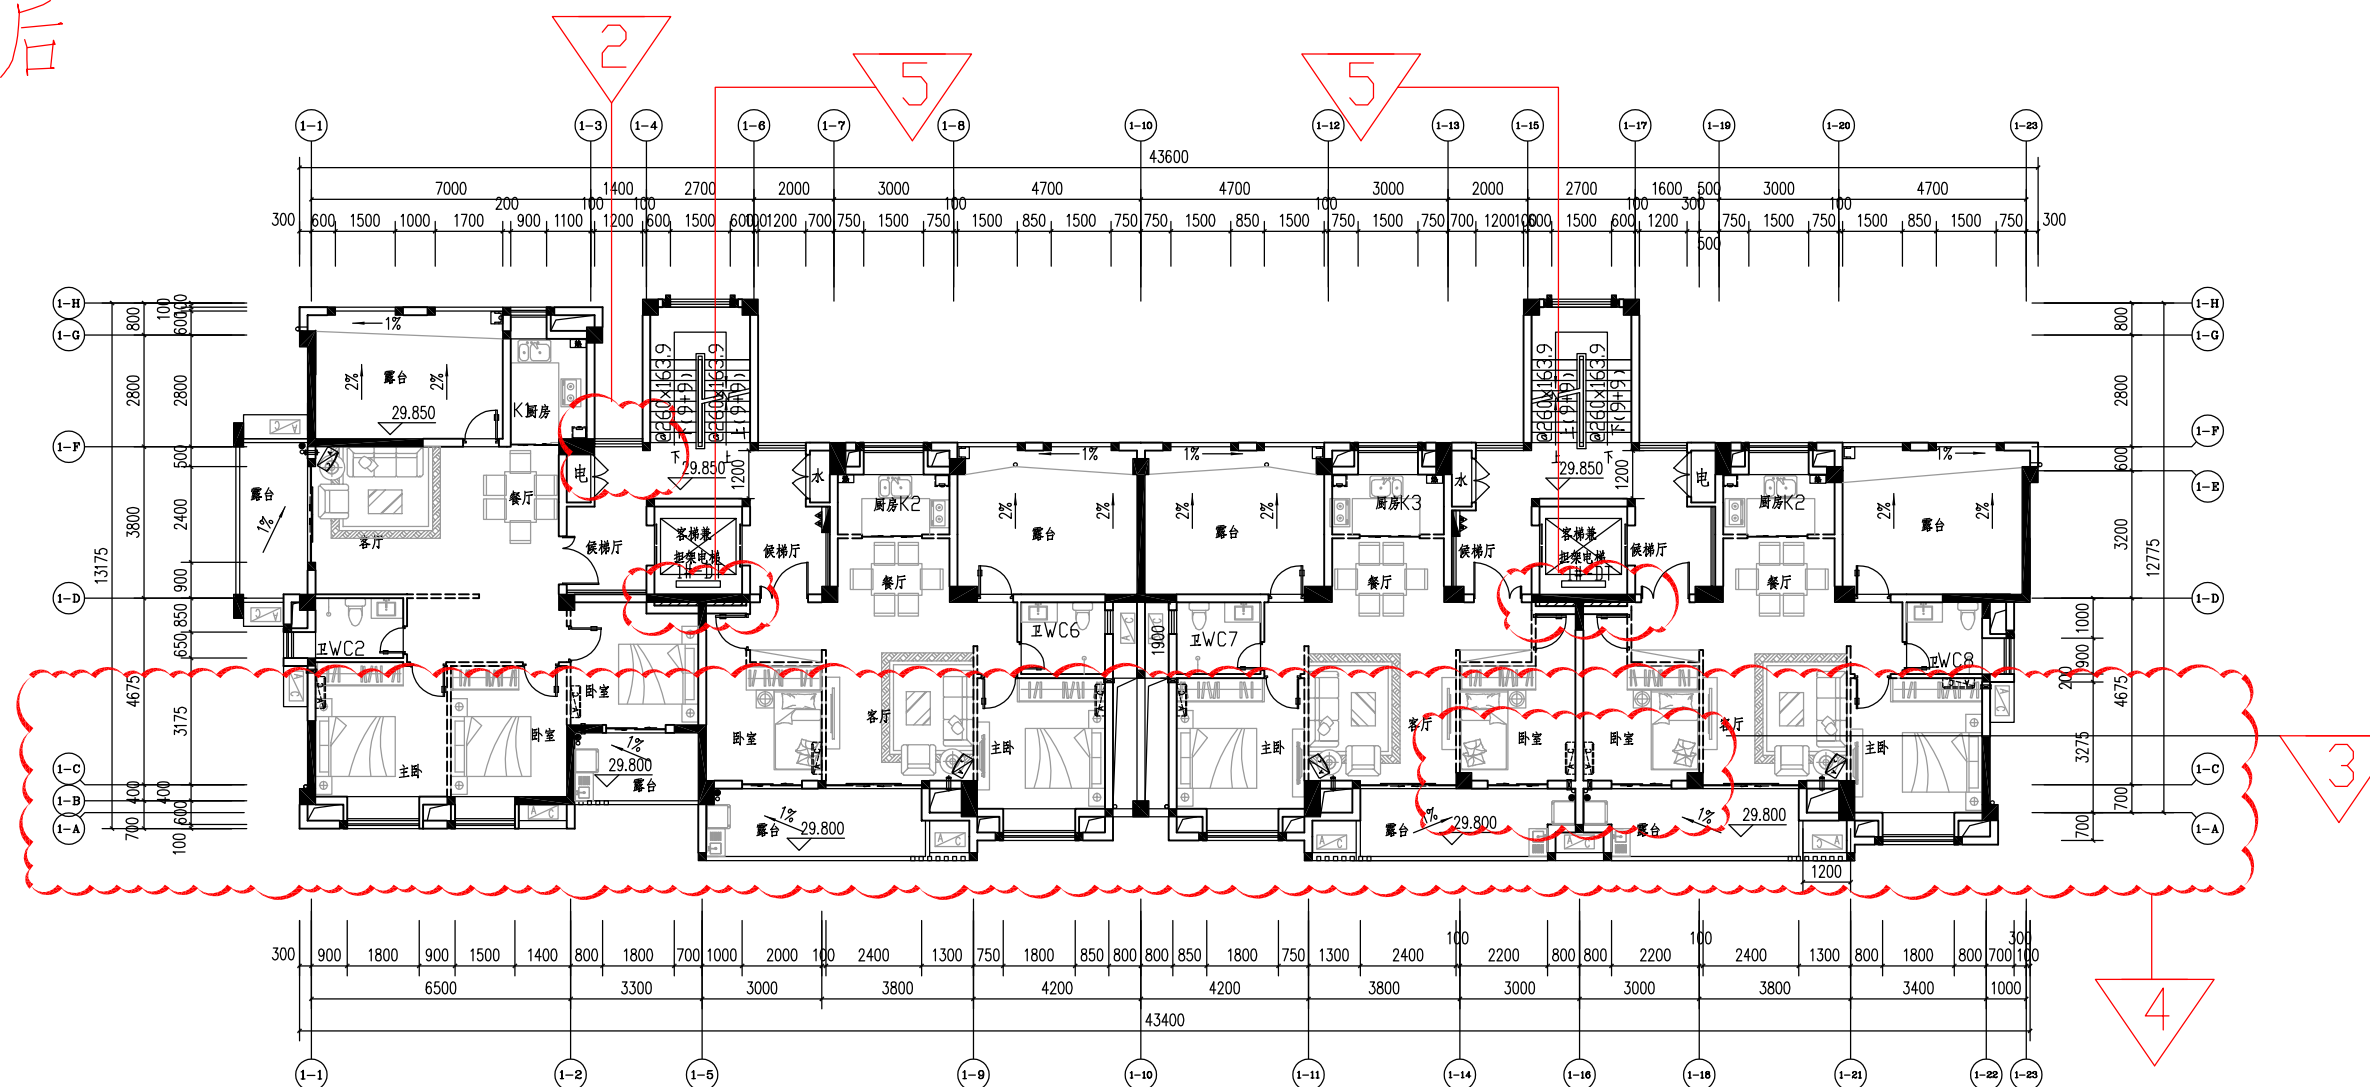


1#楼十一层平面图

变更内容:


2. 图中①~④轴交①轴外墙往①轴方向移100mm
3. 图中①~④轴交①~④轴的柱子往①轴方向移250mm 与外墙平
4. 图中①~④轴交①轴柱往下移15mm, ①~④轴尺寸由4660mm 改为4675mm
5. 图中①~④轴交①~④轴、①~④轴增设一段电梯隔音墙

变更前

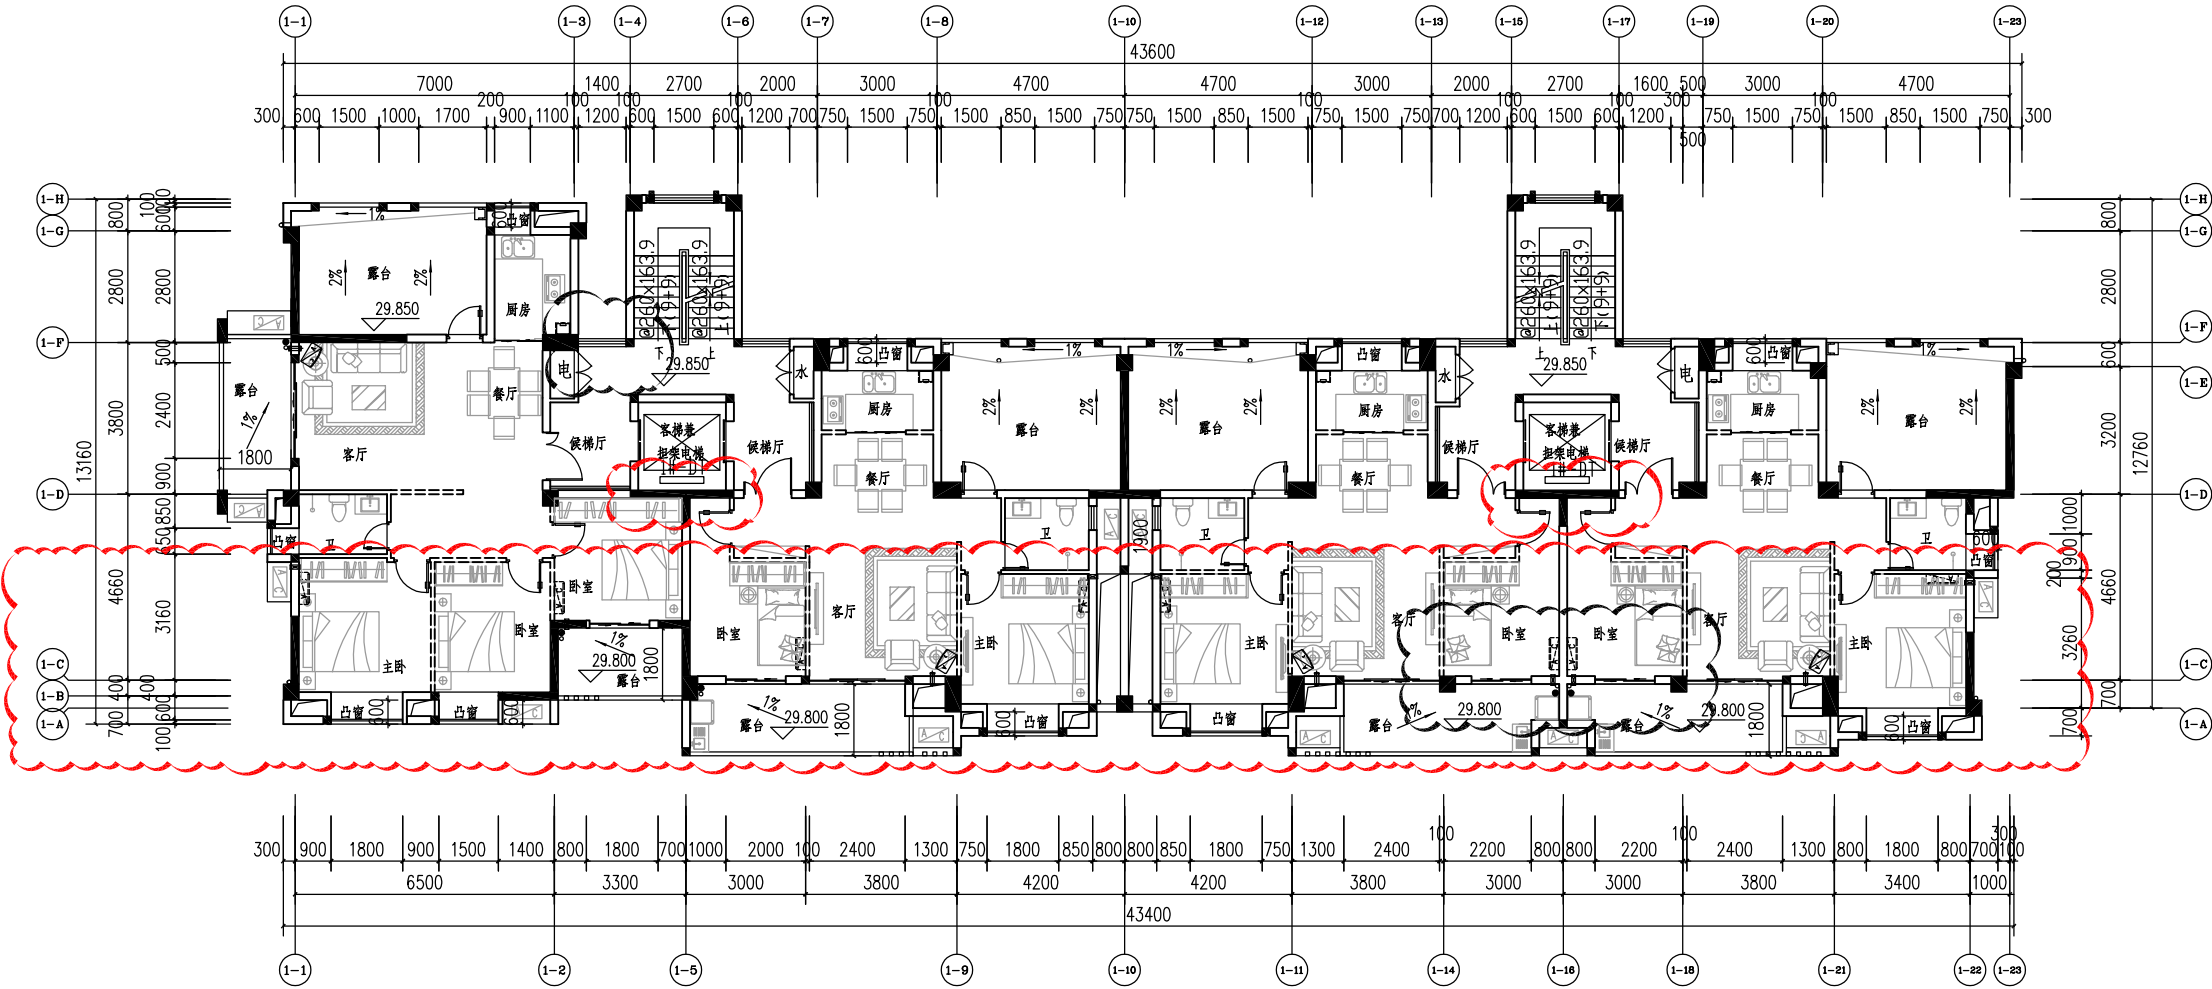

1#楼十一层平面图

变更后

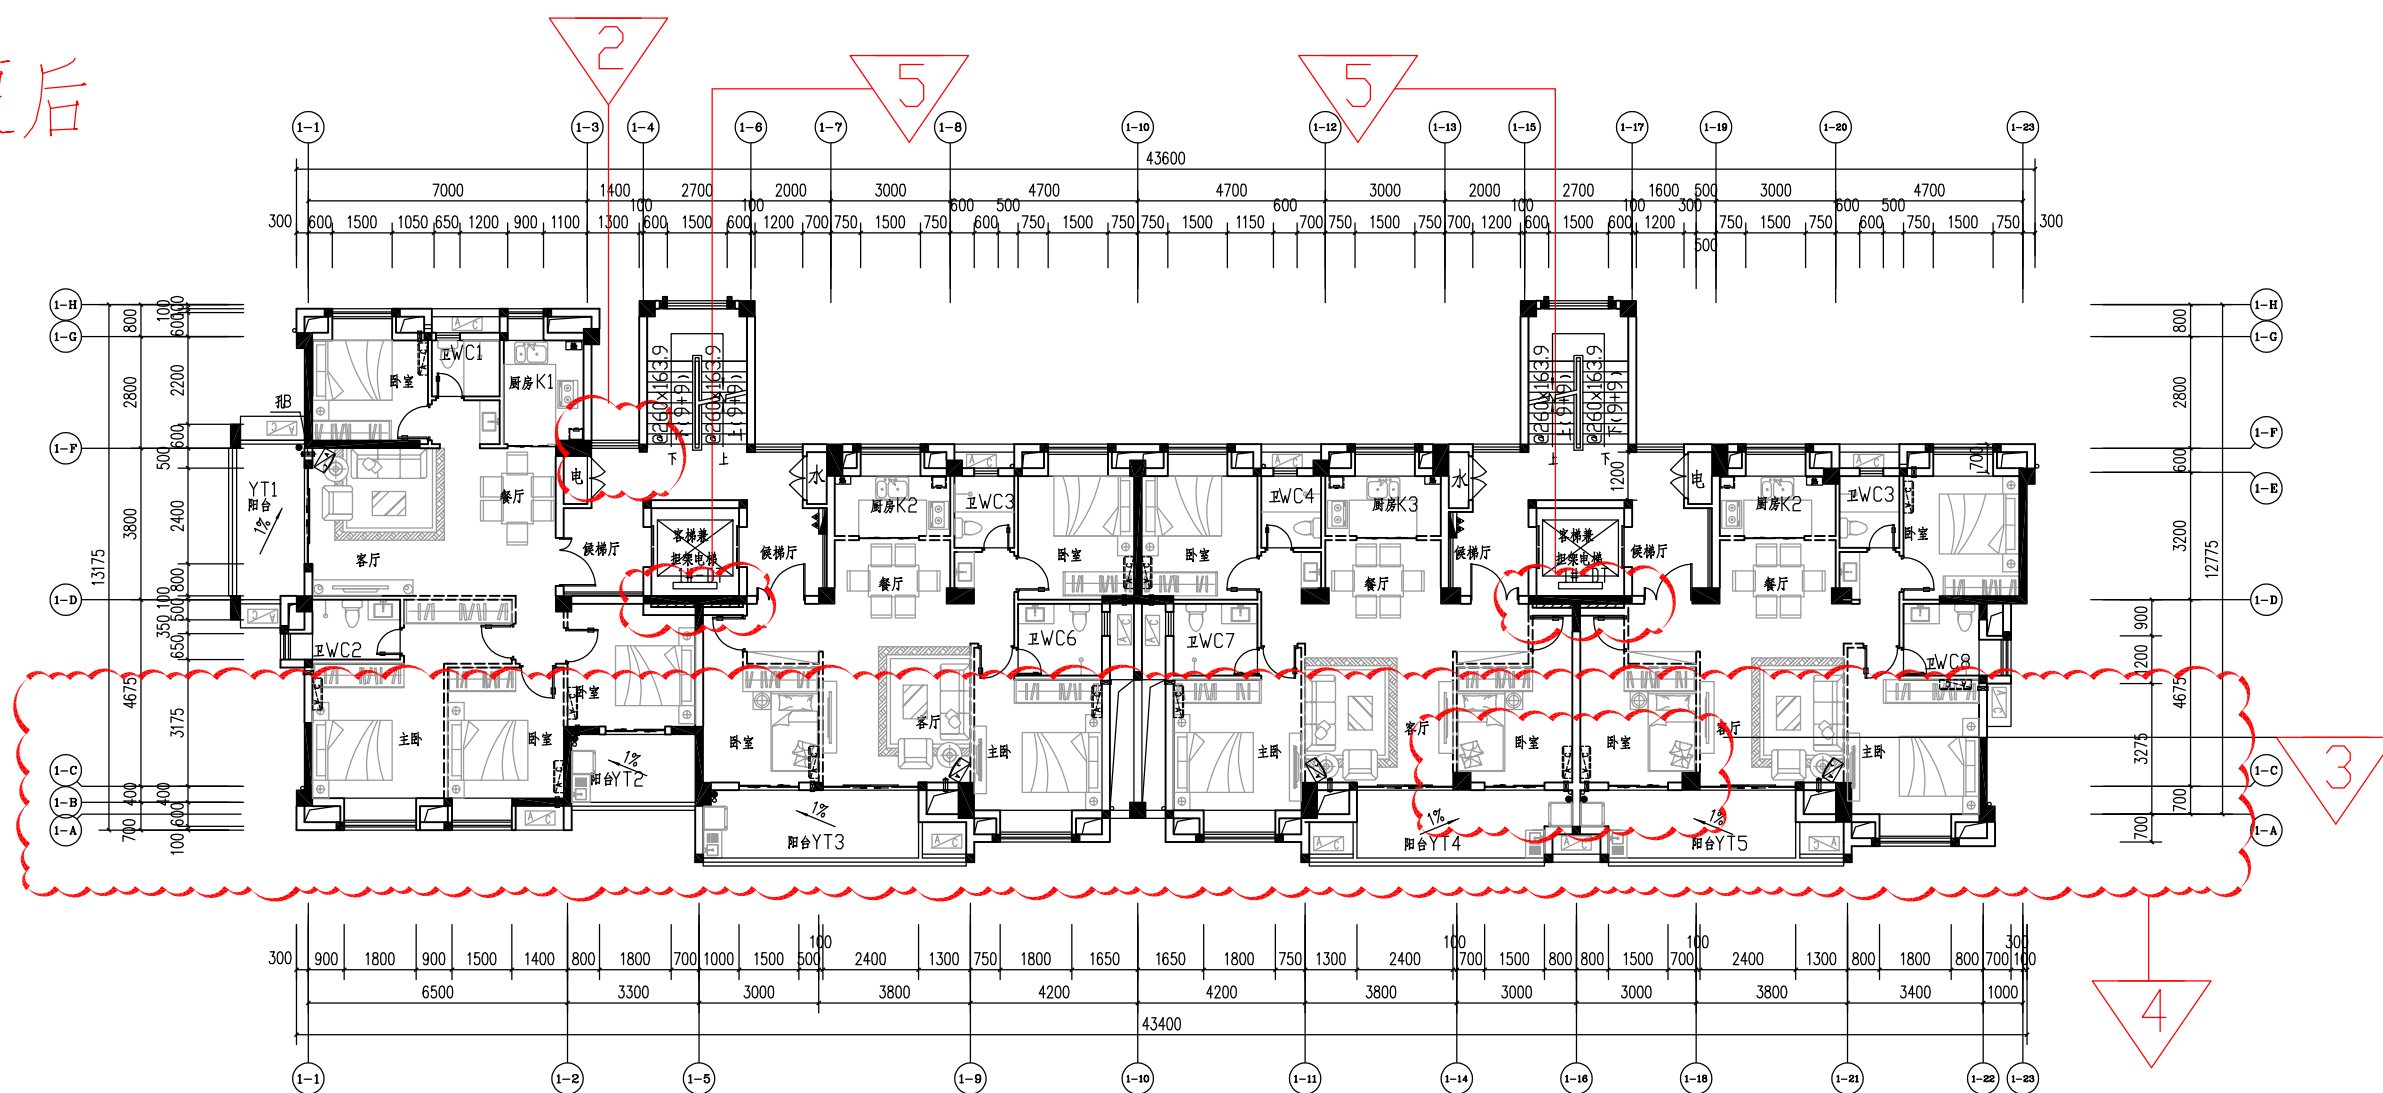


1#楼三~十层平面图

变更内容:


2. 图中①-3~①-4轴交①-F轴外墙往①-9轴方向移100mm
3. 图中①-10轴交①-14轴、①-18轴的柱子往①-D轴方向移250mm与外墙平
4. 图中①-D~①-B轴交①-B轴柱往下移15mm, ①-D~①-10轴尺寸由4660mm改为4675mm
5. 图中①-D轴交①-5轴、①-16轴增设一段电梯隔音墙

变更前

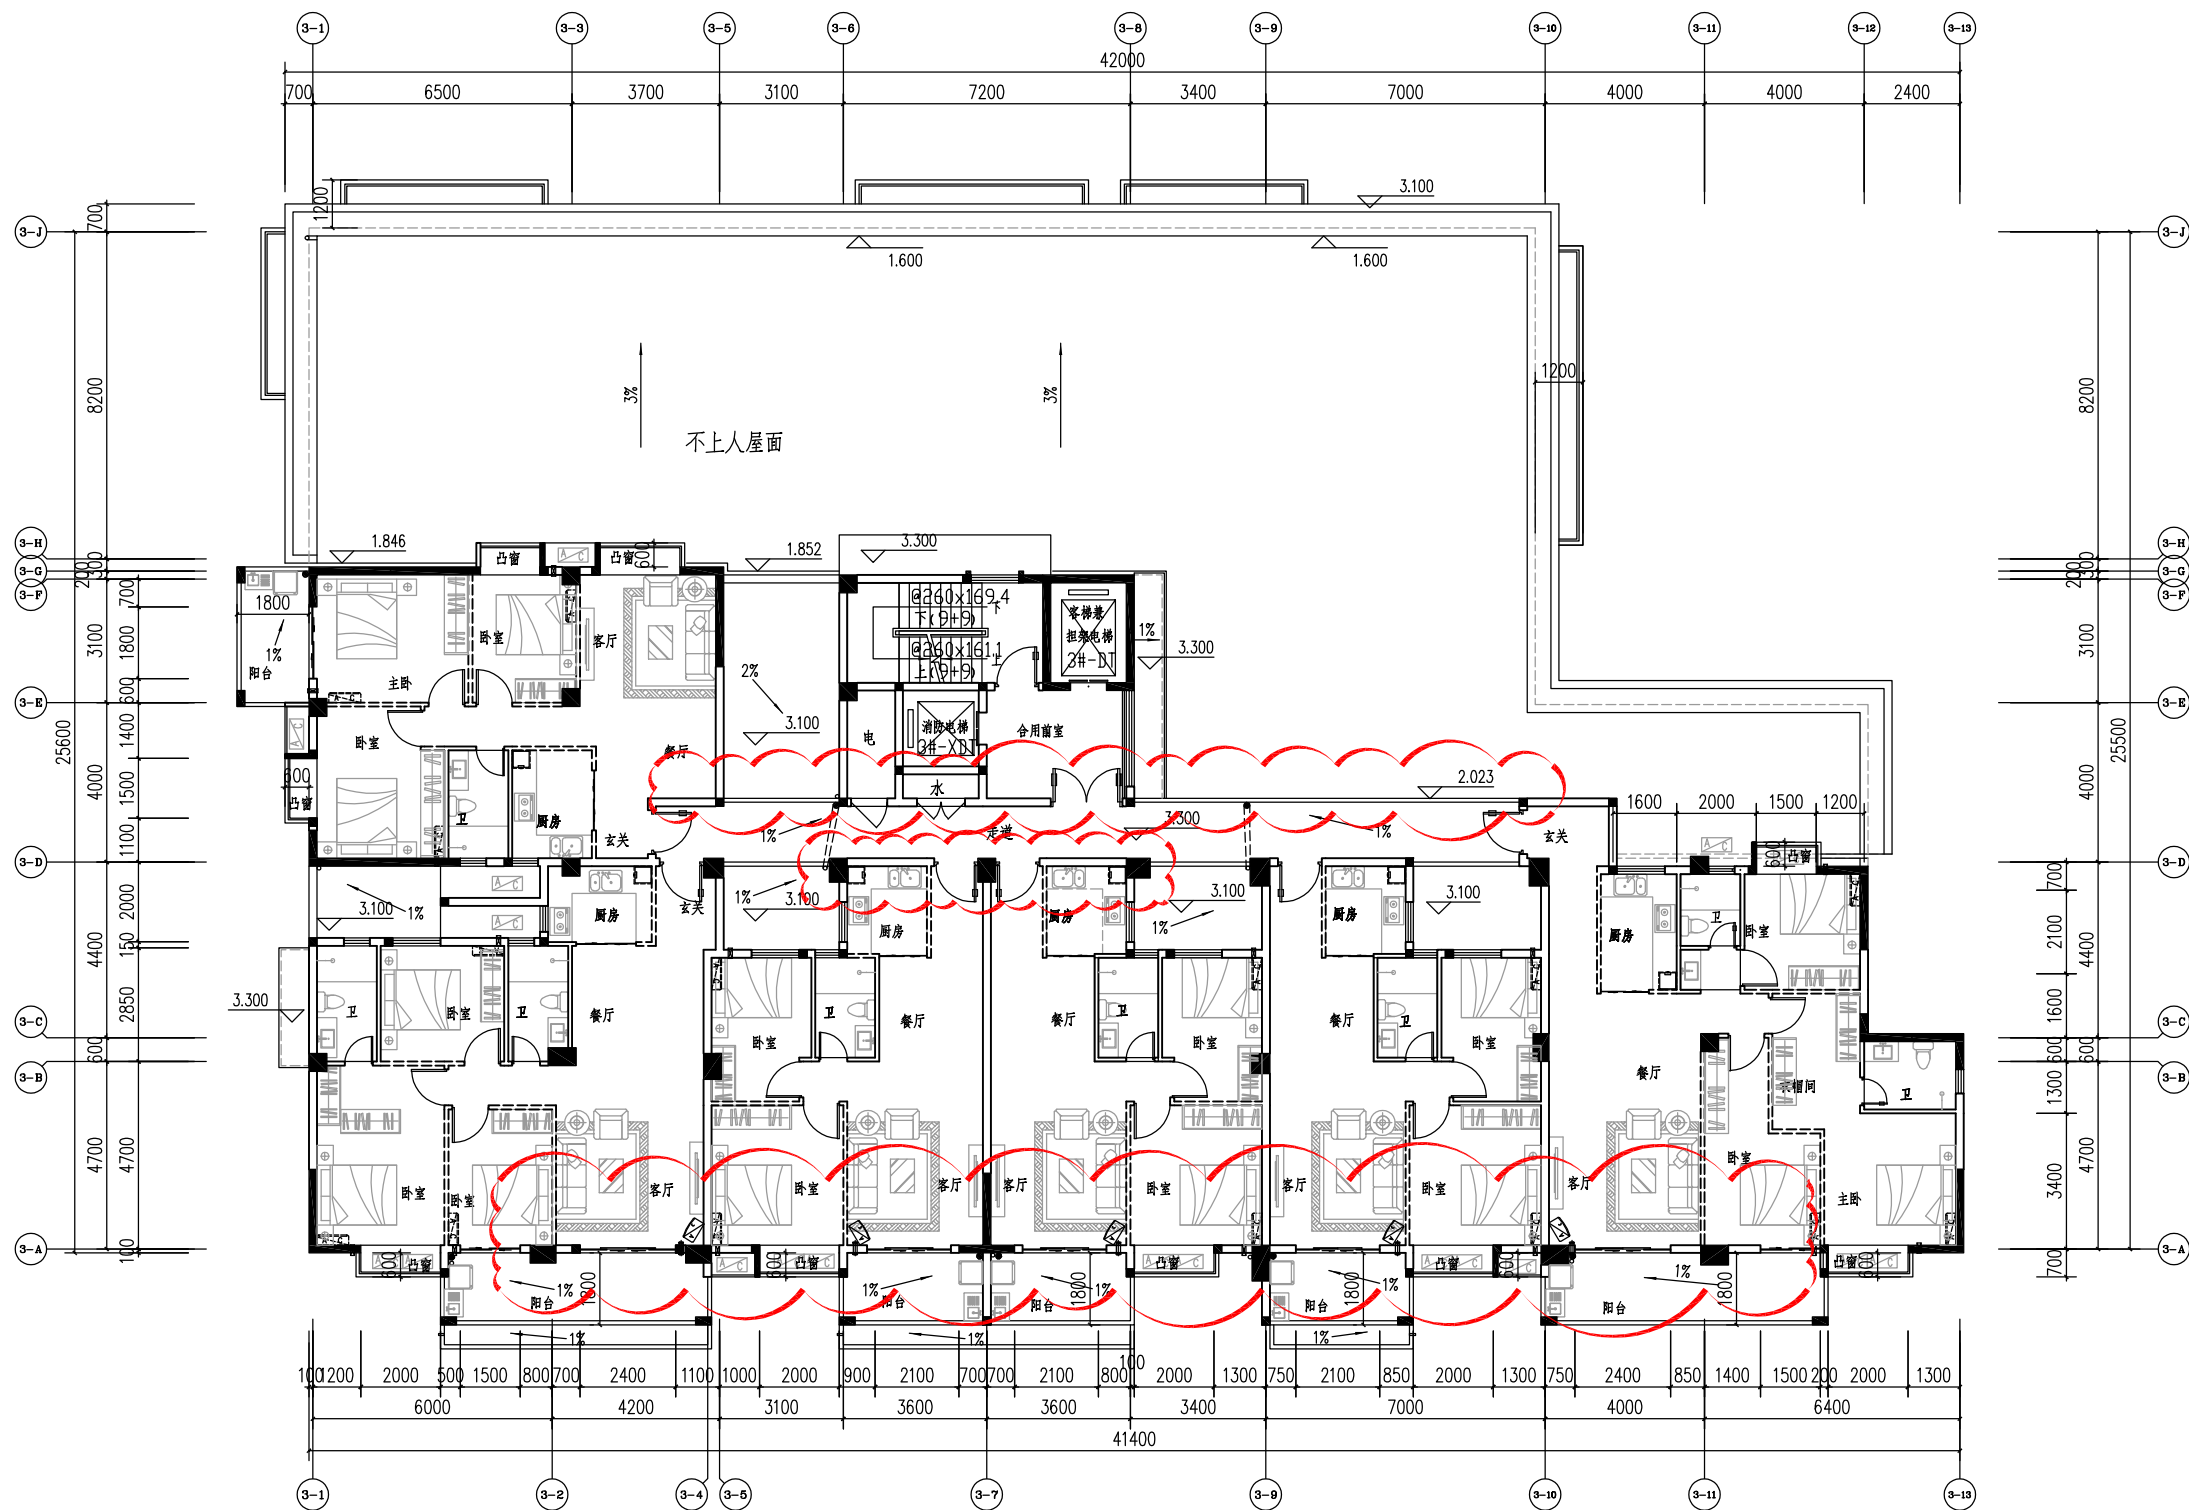

3#楼二层平面图

变更后

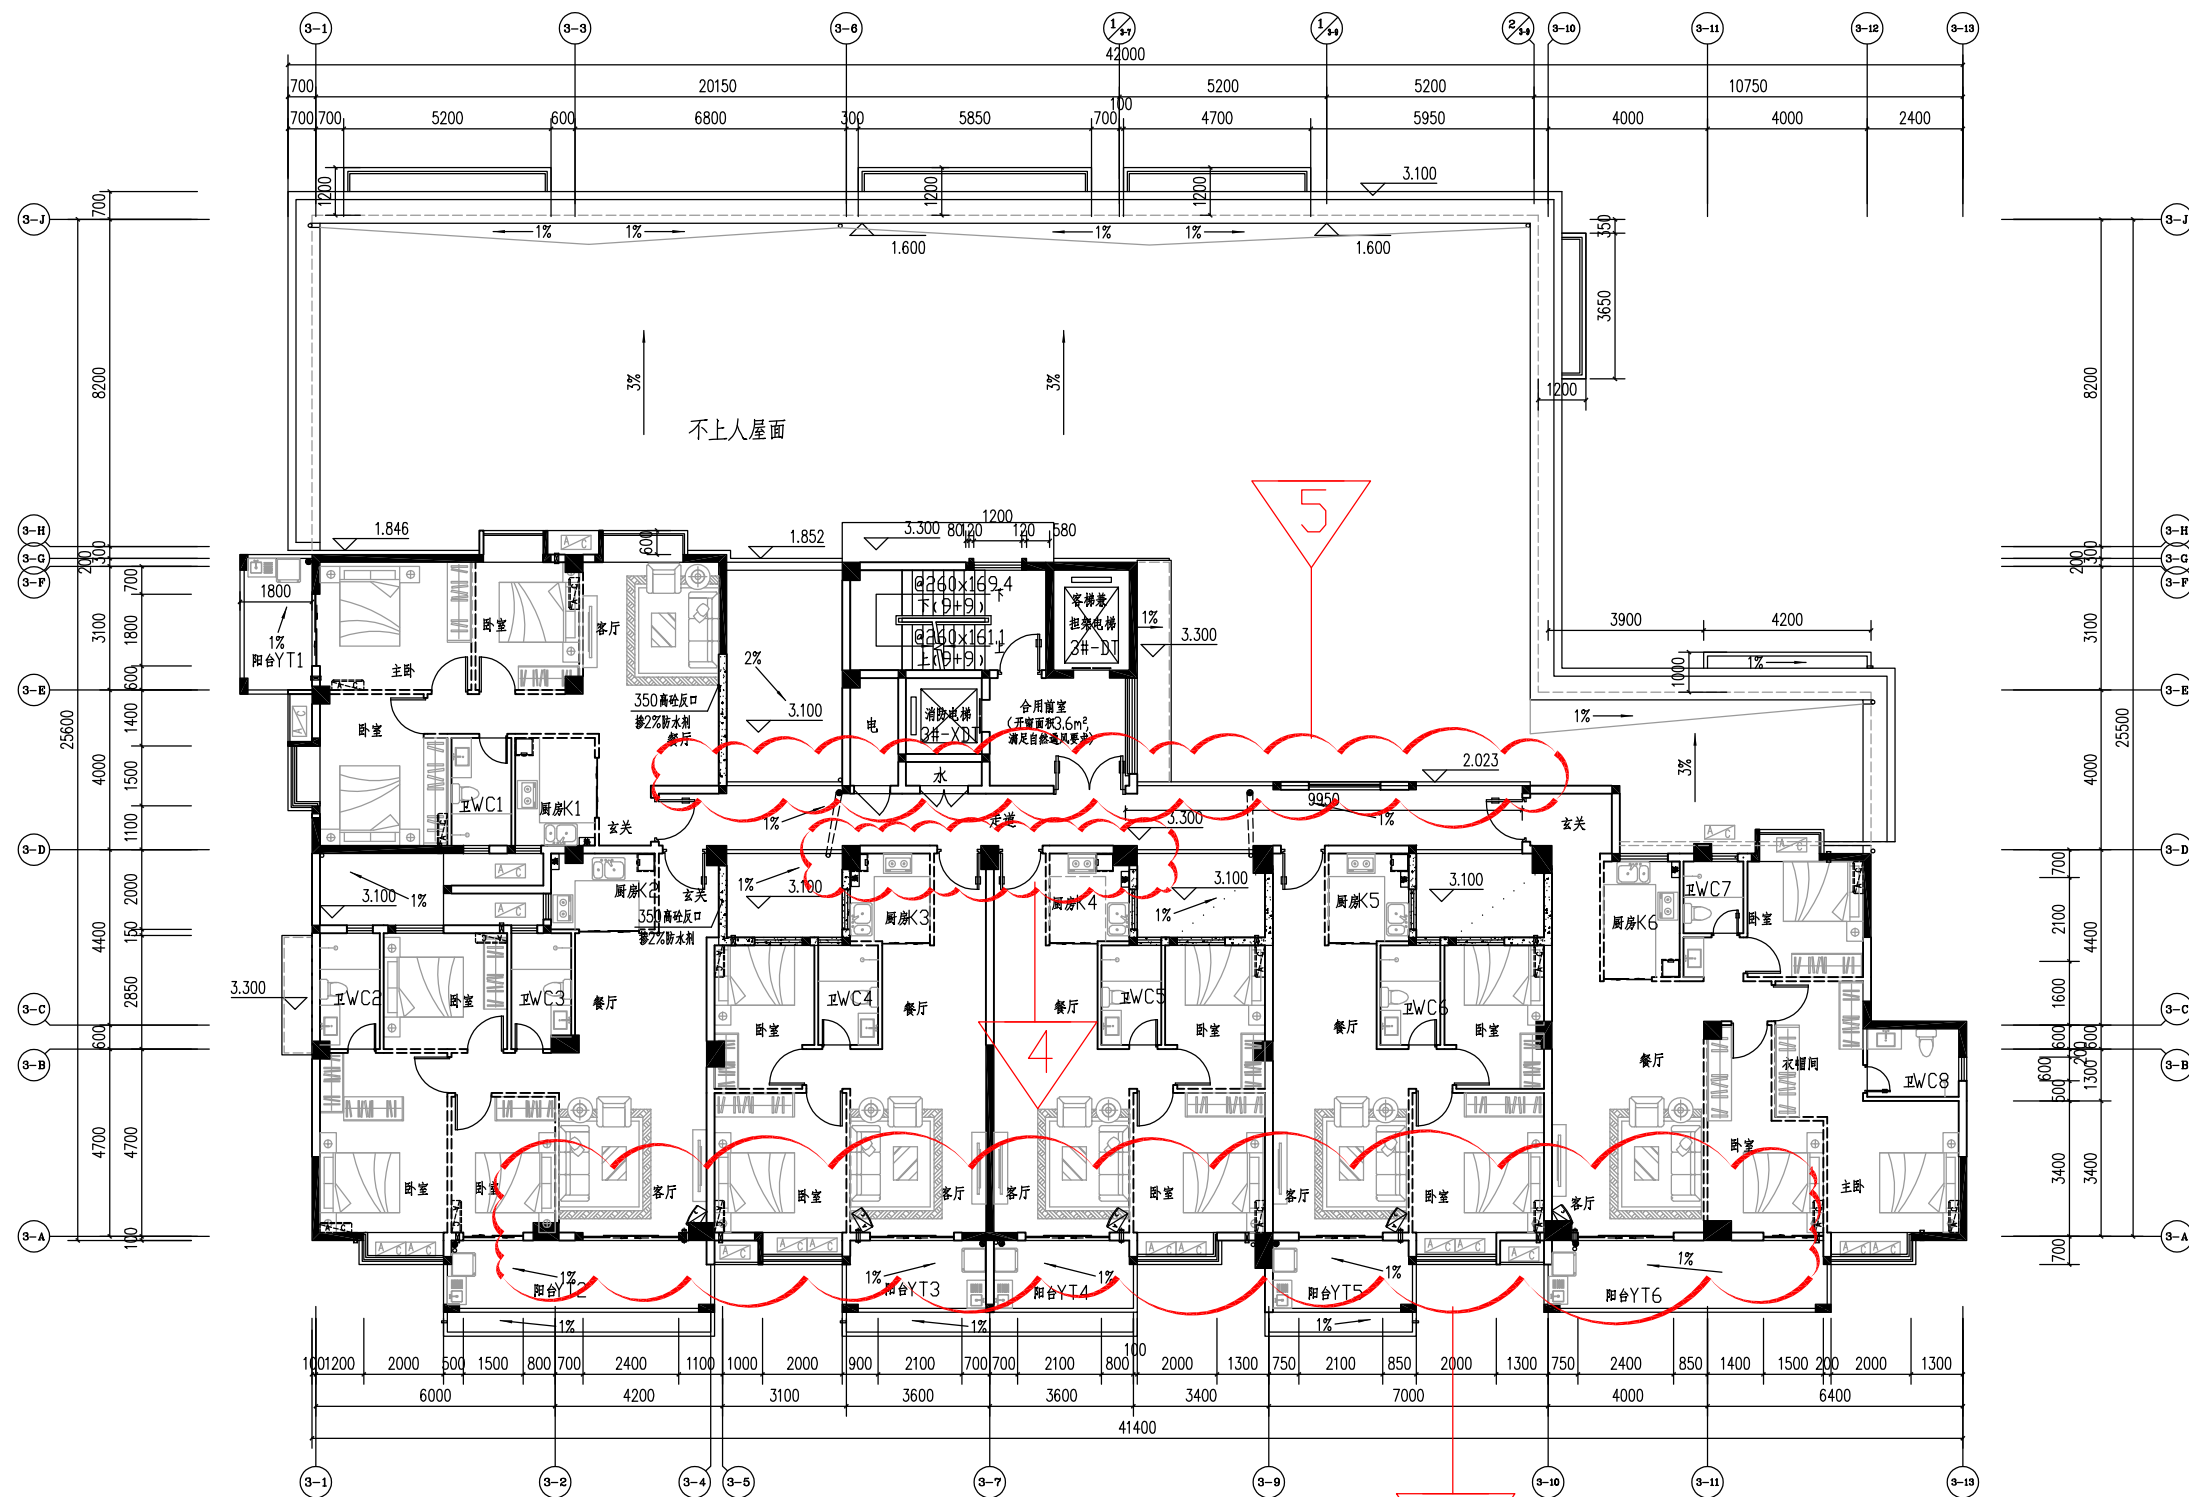


3#楼二层平面图

变更内容:


- 3.图中③-A轴交③-2轴、③-4轴、③-10轴、③-11轴的柱子往③-B方向移250mm与外墙平
- 4.图中③-D轴交③-6轴的柱子往③-9轴方向平移250mm与外墙平,图中③-D轴交③-8轴的柱子往③-5轴方向平移400mm与外墙平
- 5.图中③-8轴~③-10轴交③-D轴走道往③-9轴方向加宽100mm尺寸,由1700mm改为1800mm,③-9轴~③-6轴走道往③-B轴方向加宽100mm尺寸由1700mm改为1800mm,③-9轴~③-10轴间增加3.6米长墙,墙上升1.8米宽窗

变更前

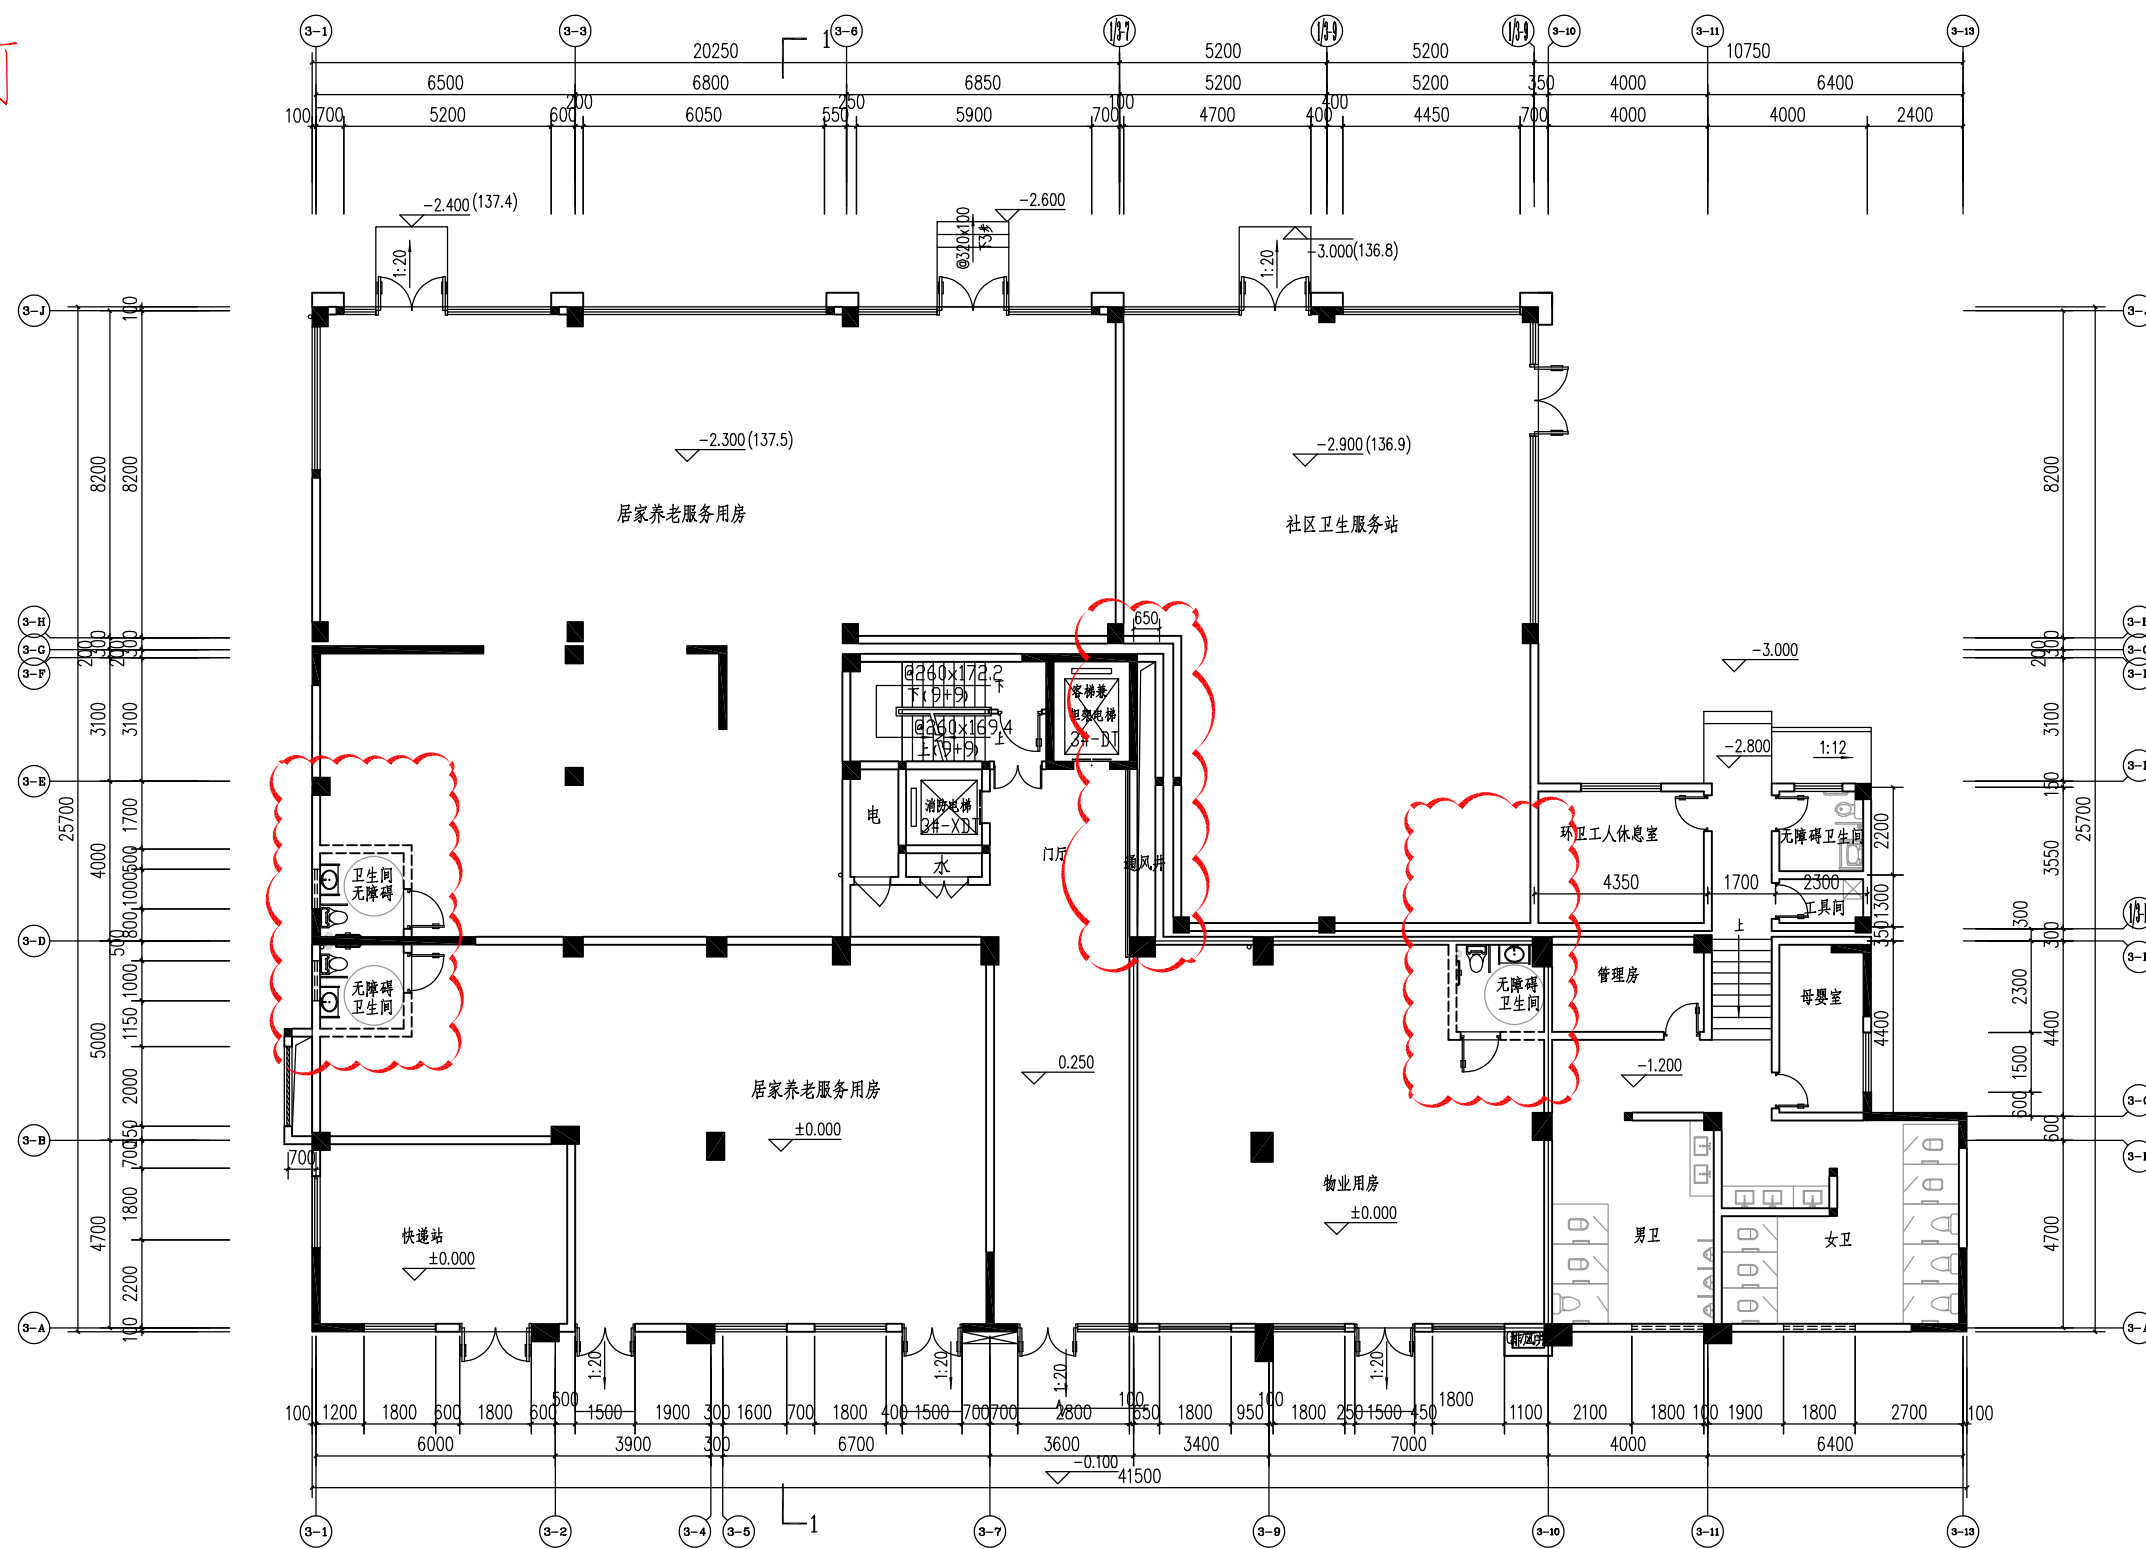

3#楼一层平面图

变更后

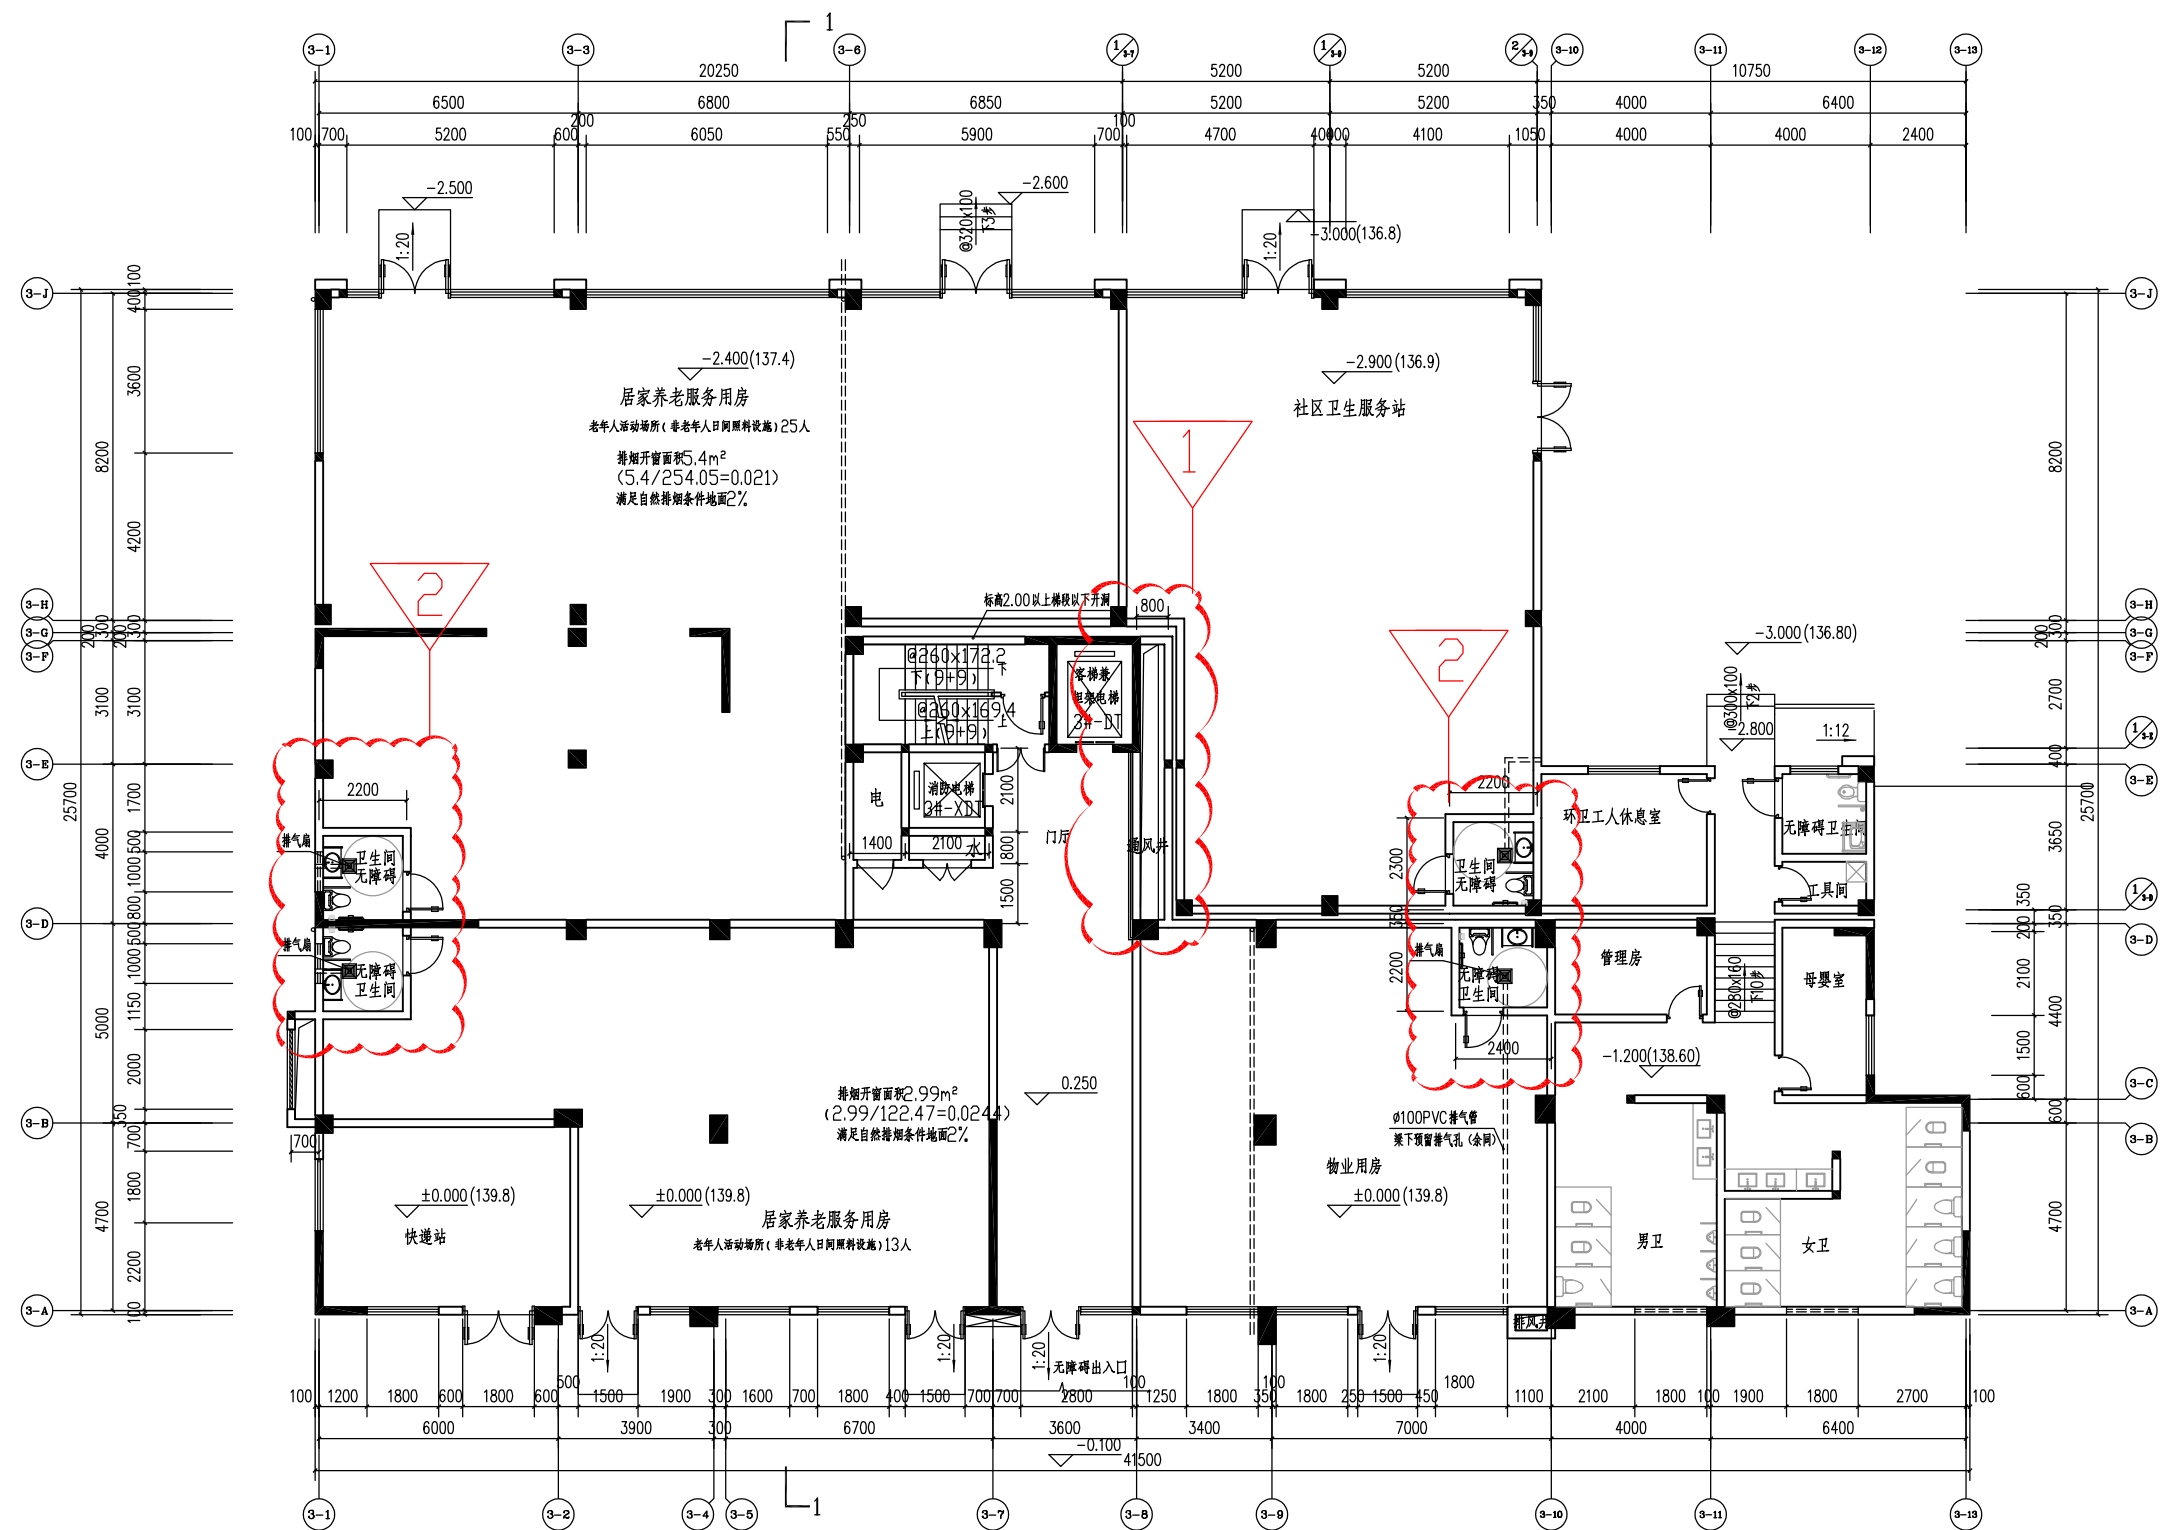


3#楼一层平面图

变更内容:


1. 图中 $\textcircled{1/3-7}$ 轴交 $\textcircled{3-F}$ 轴~ $\textcircled{3-D}$ 轴通风井尺寸由650mm改为800mm
2. 图中 $\textcircled{3-1}$ 轴交 $\textcircled{3-D}$ 轴、 $\textcircled{3-10}$ 轴交 $\textcircled{3-D}$ 轴卫生间虚线墙体改为实体墙体

变更前

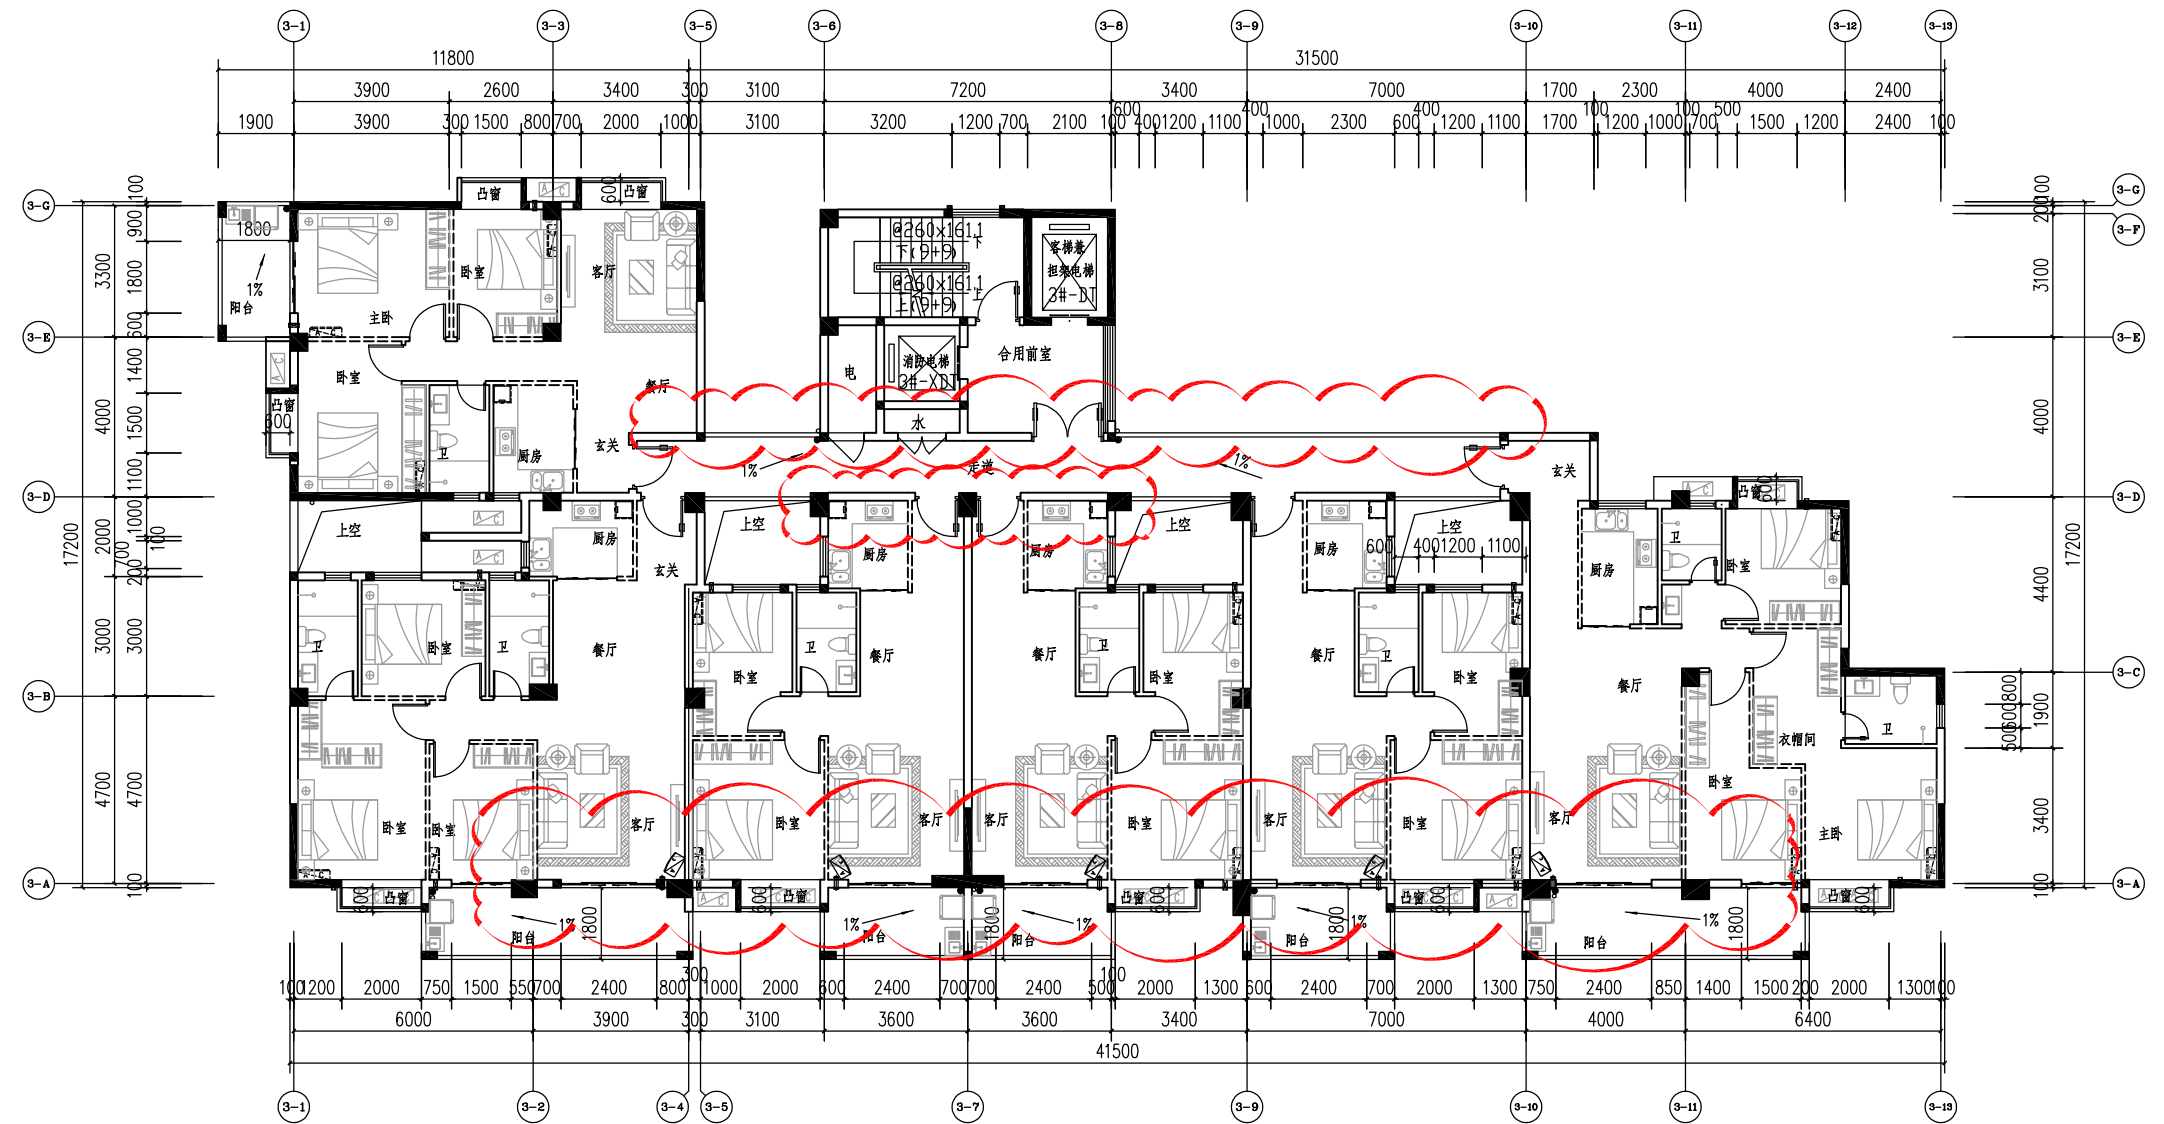

3#楼三~十八层平面图

变更后

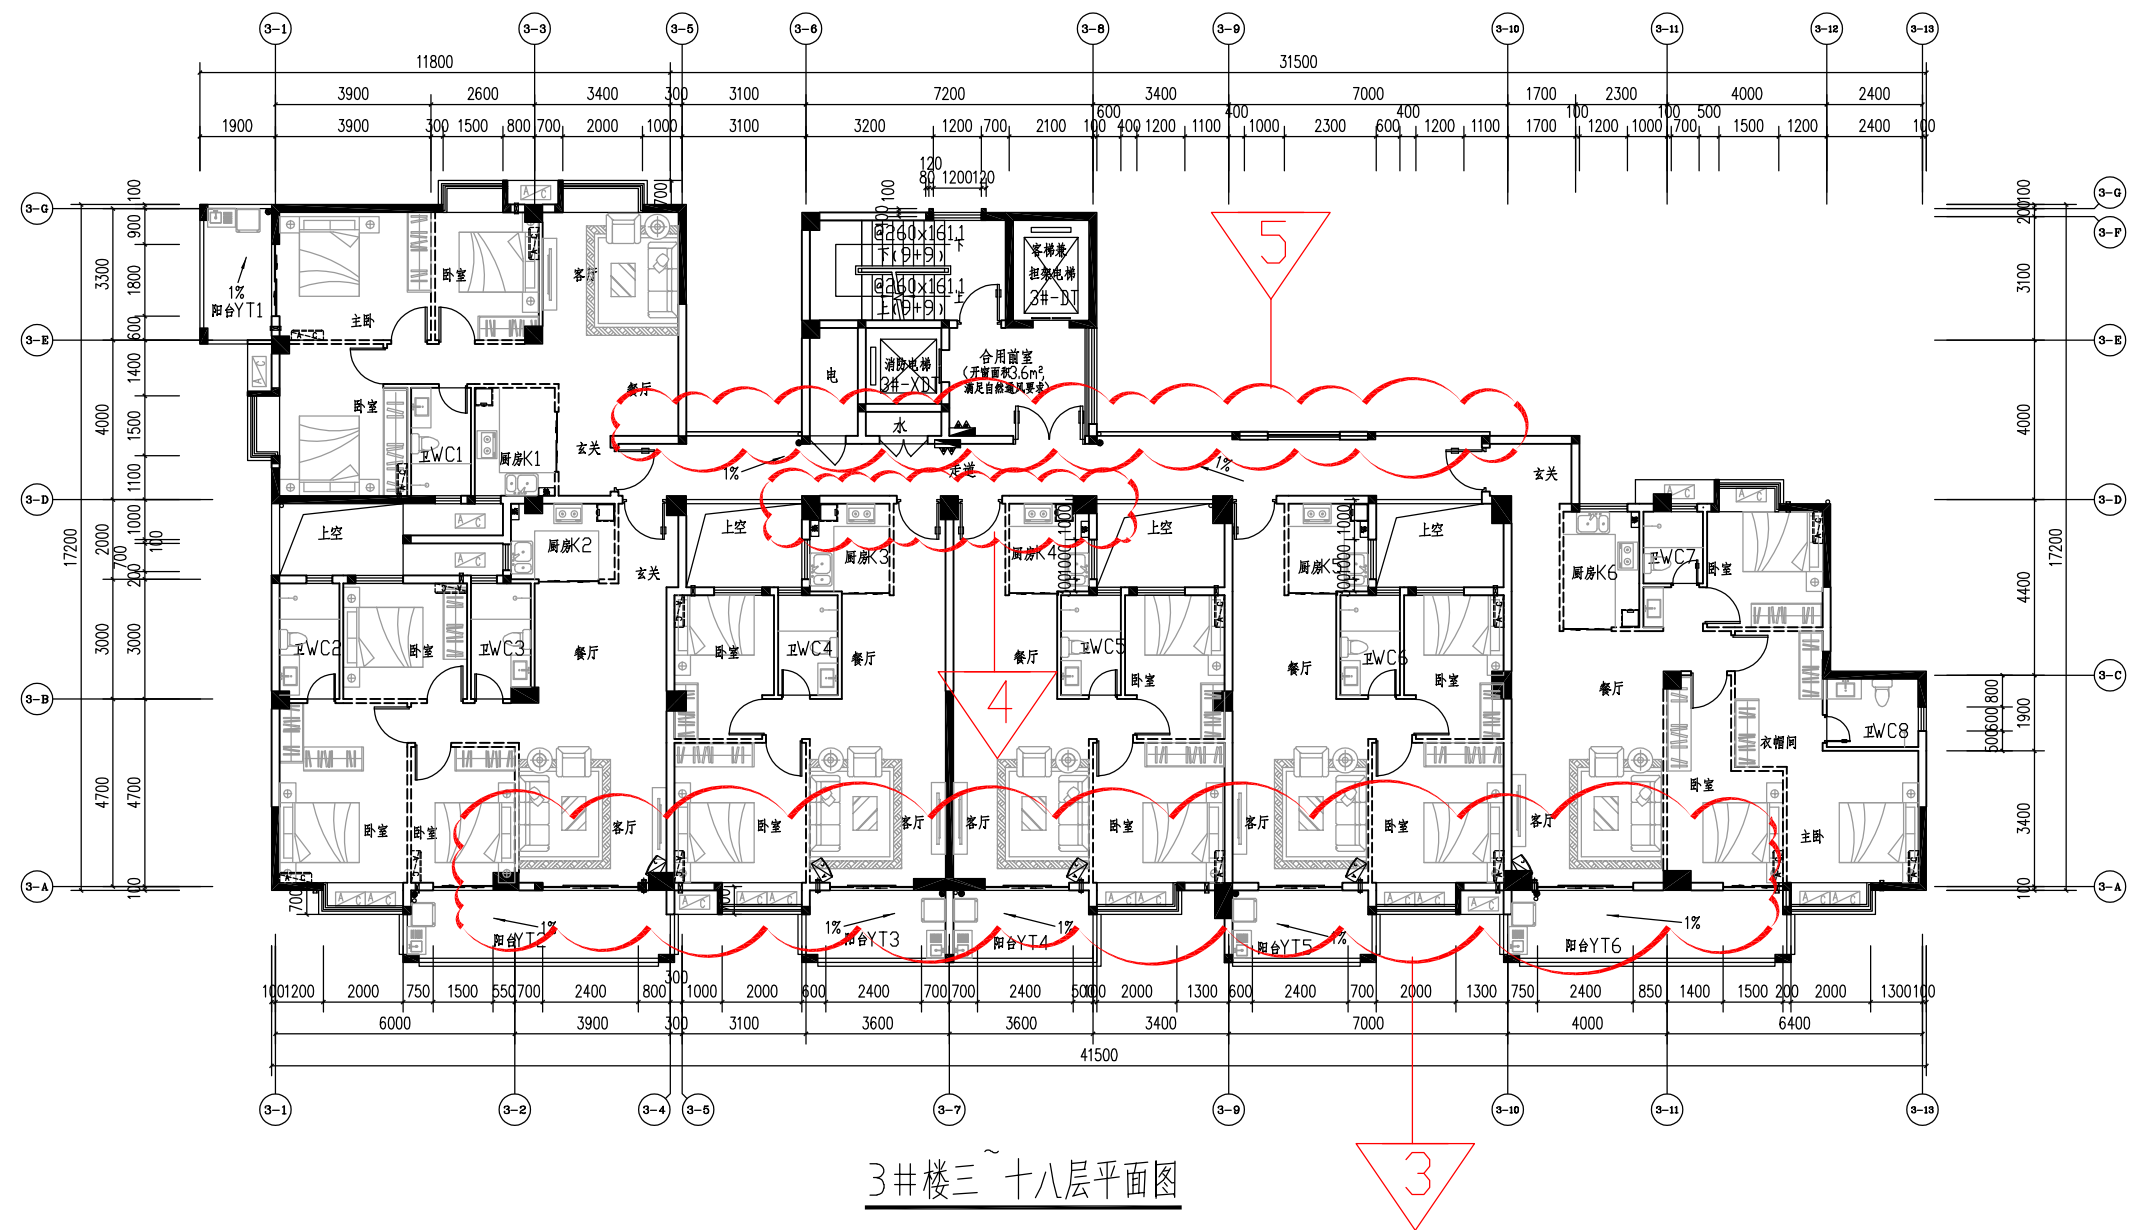


3#楼三~十八层平面图

变更内容:


- 3.图中③轴交③轴、③轴、③轴、③轴的柱子往③方向移250mm与外墙平
- 4.图中③轴交③的柱子往③轴方向平移250mm与外墙平,图中③轴交③的柱子往③轴方向平移400mm与外墙平
- 5.图中③轴~③轴交③轴走道往③轴方向加宽100mm尺寸,由1700mm改为1800mm,③轴~③轴走道往③轴方向加宽100mm尺寸由1700mm改为1800mm,③轴~③轴间增加3.6米长墙,墙上升1.8米宽窗

变更前

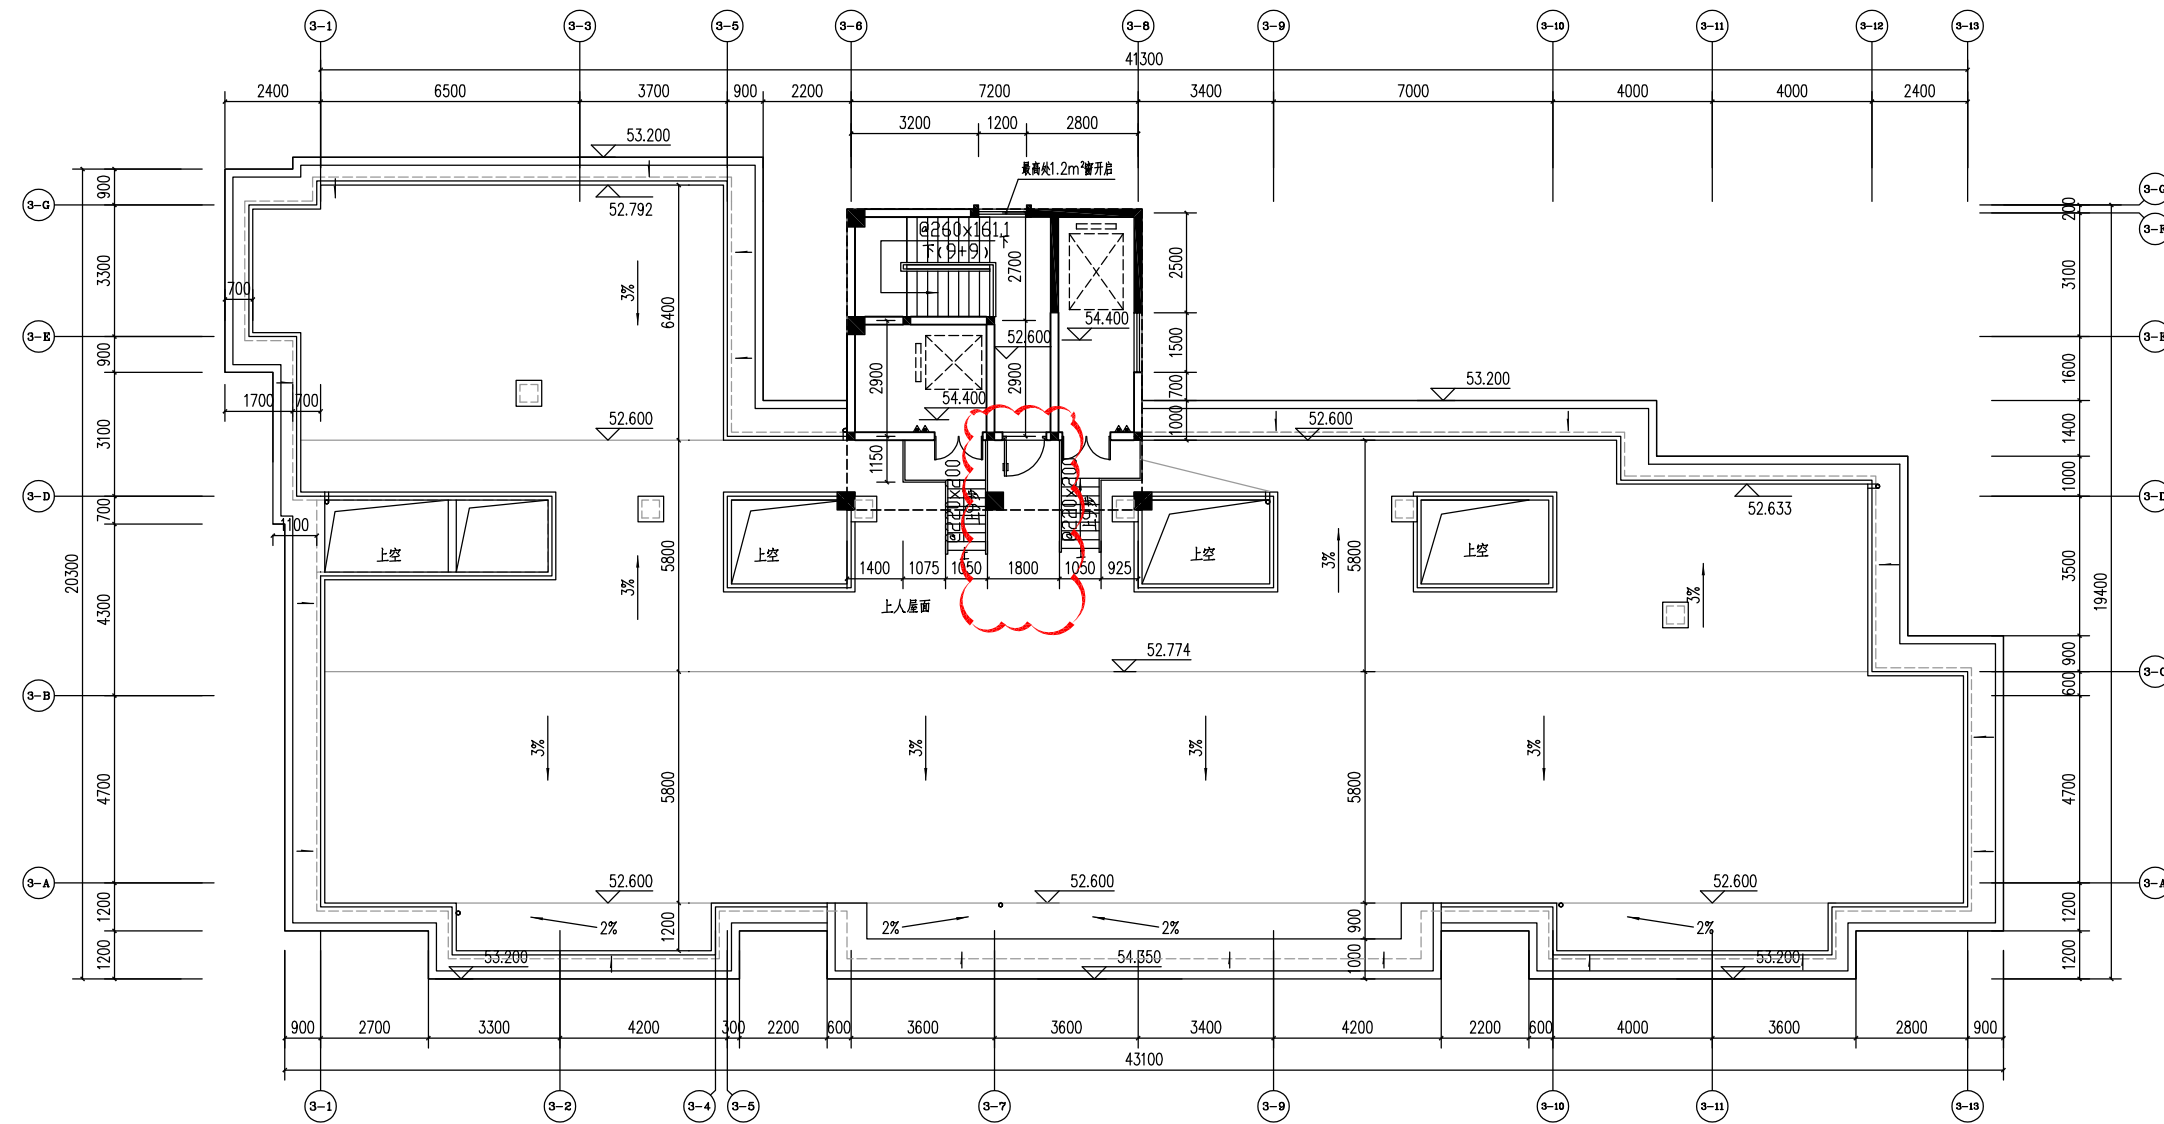


3#楼屋面平面图

变更后

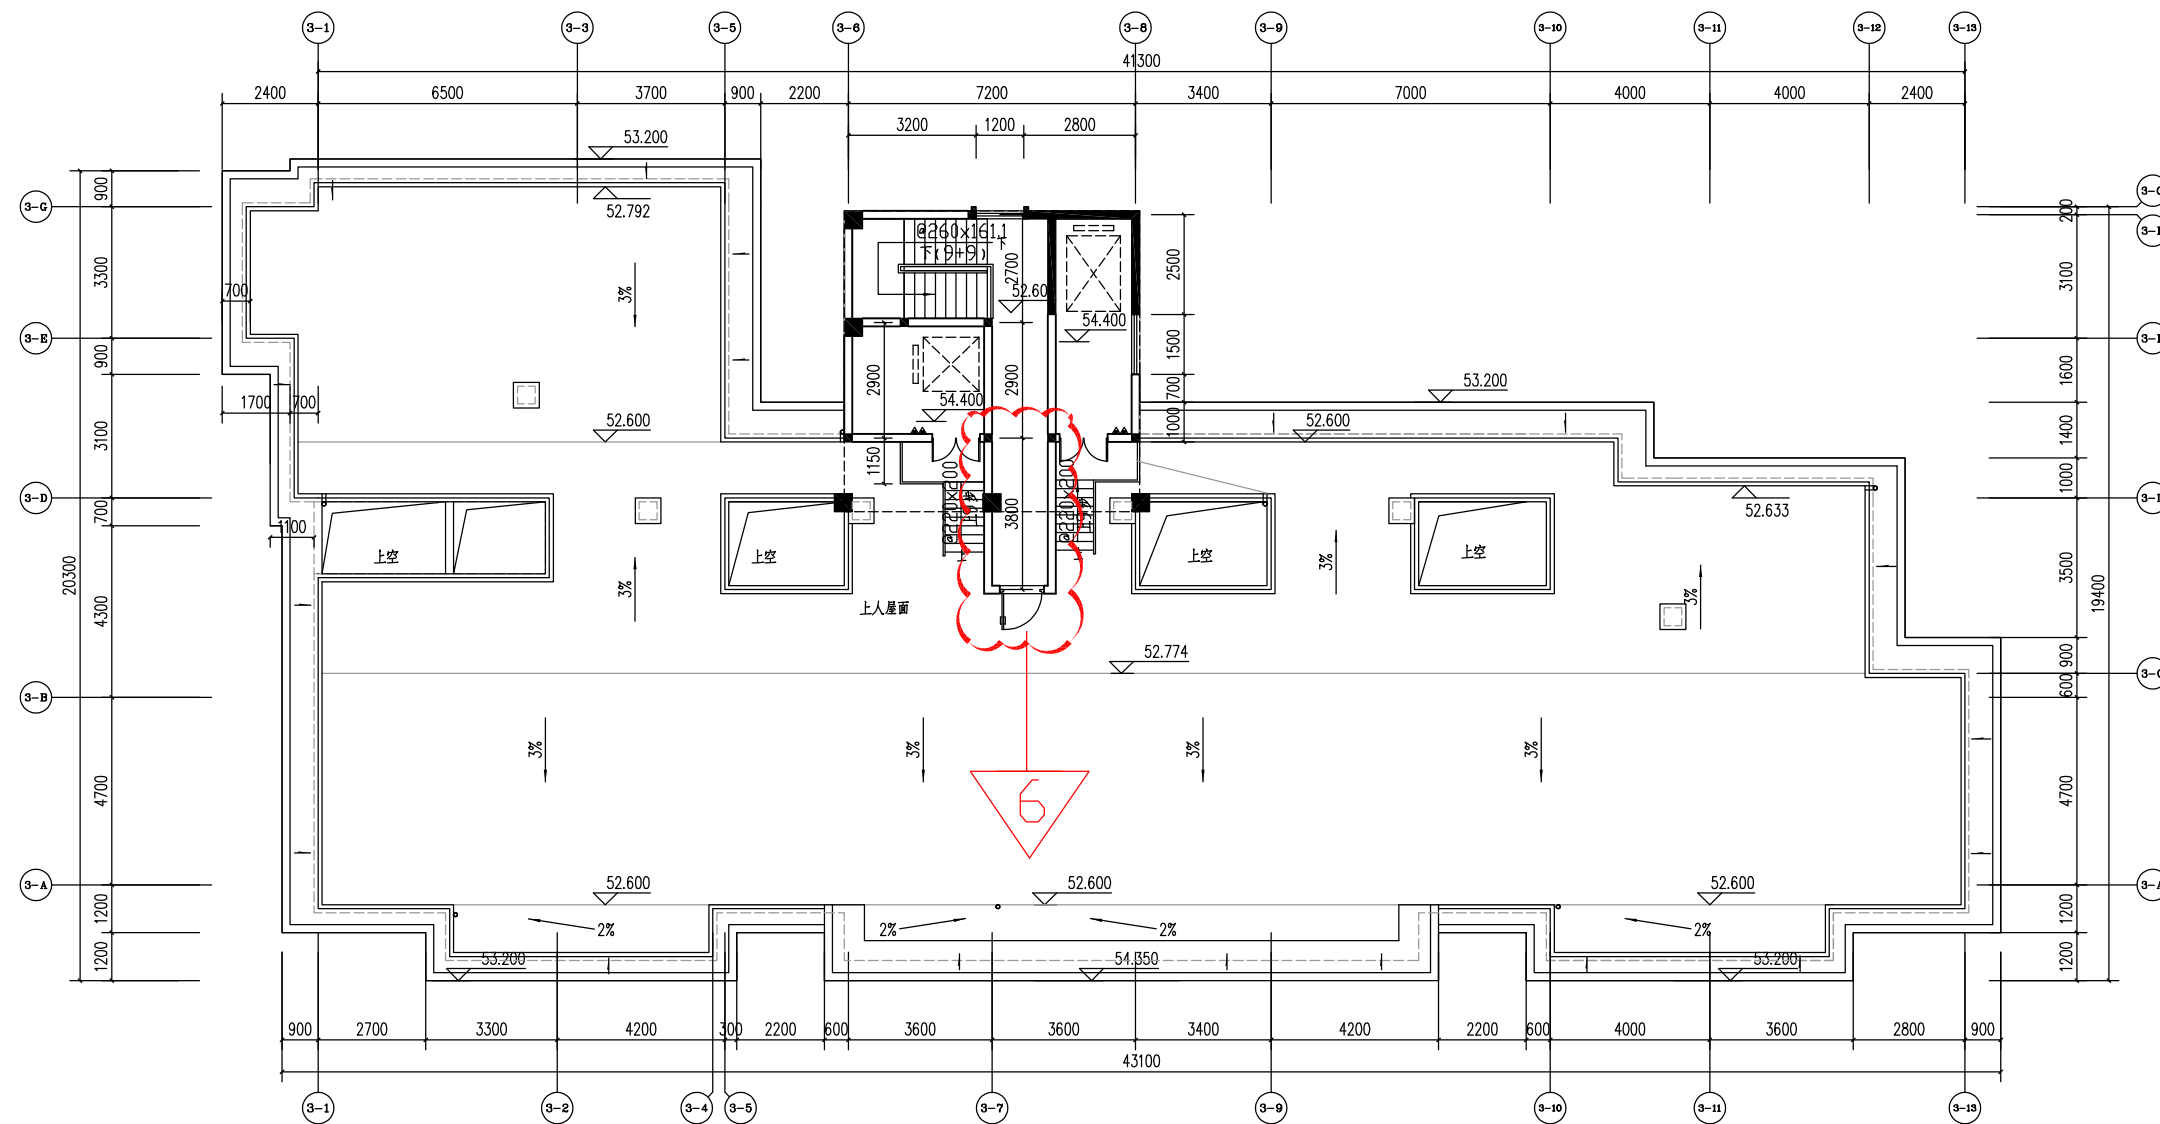


3#楼屋面平面图

变更内容：
6. 楼梯间过道墙及门向③-A轴方向移3800mm

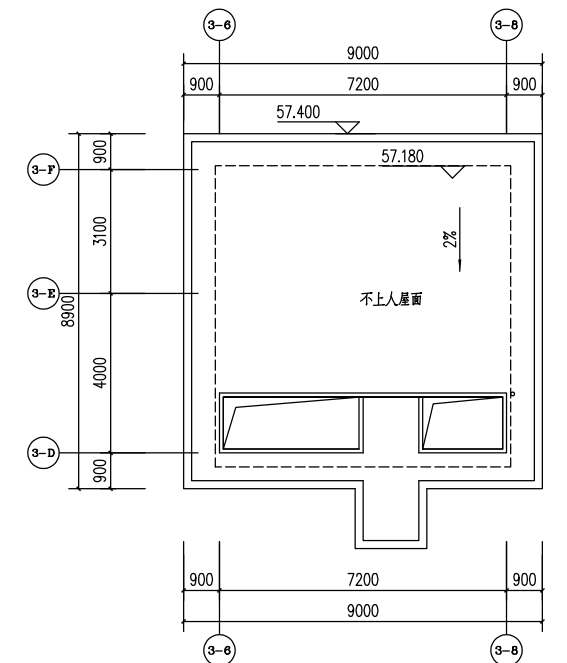


梯间屋面平面图 1:100

变更前

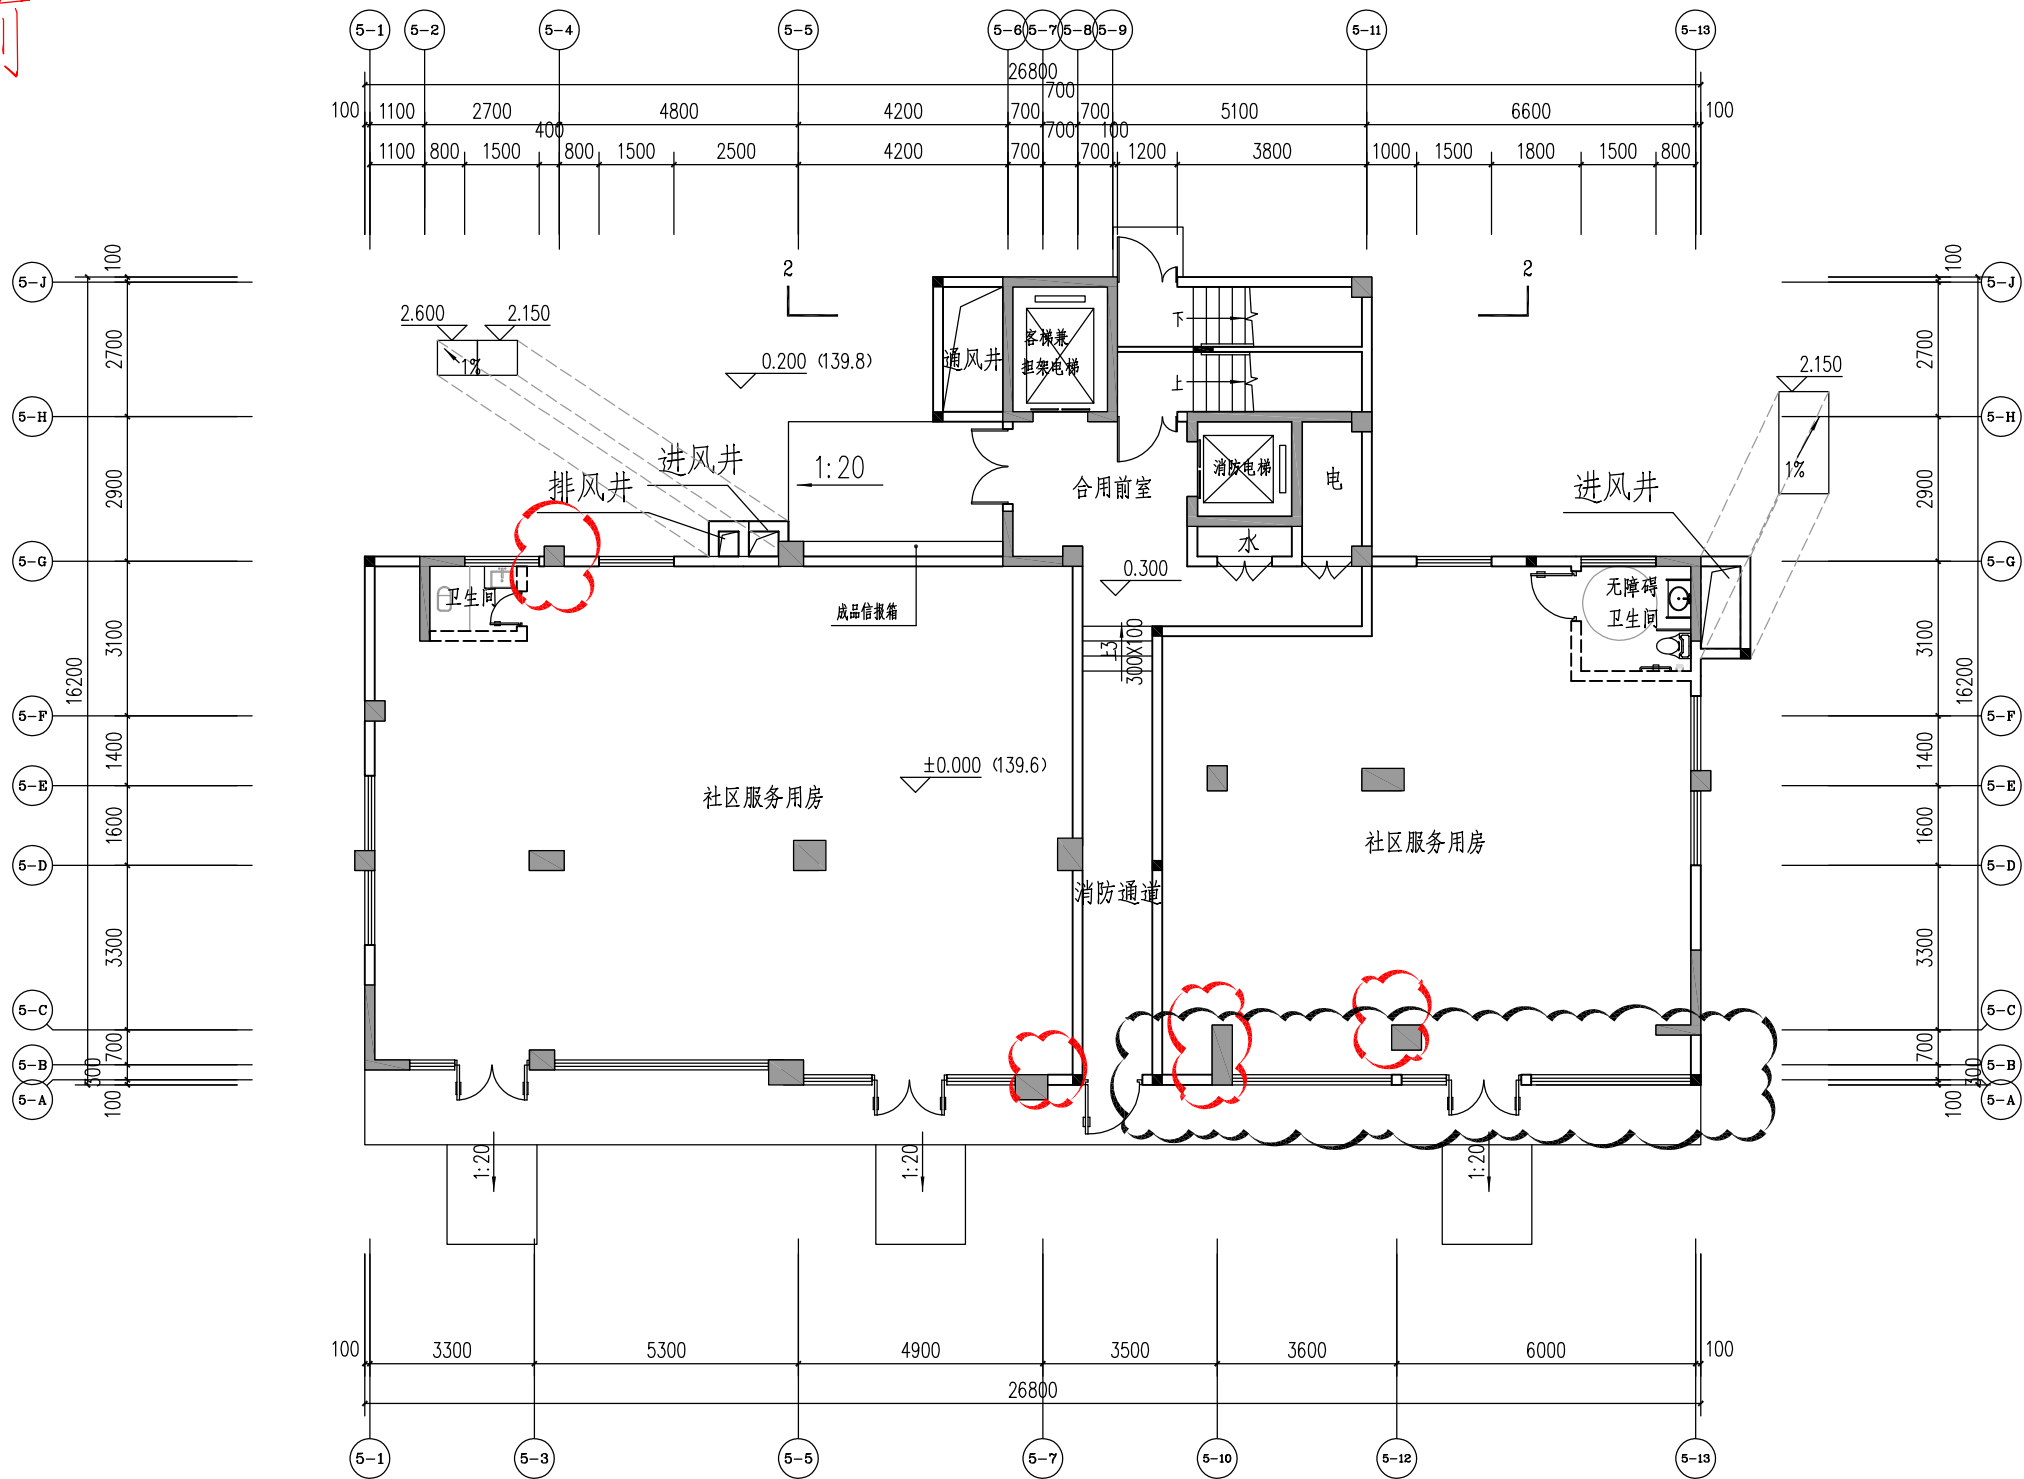

5#楼 一层平面图

变更后

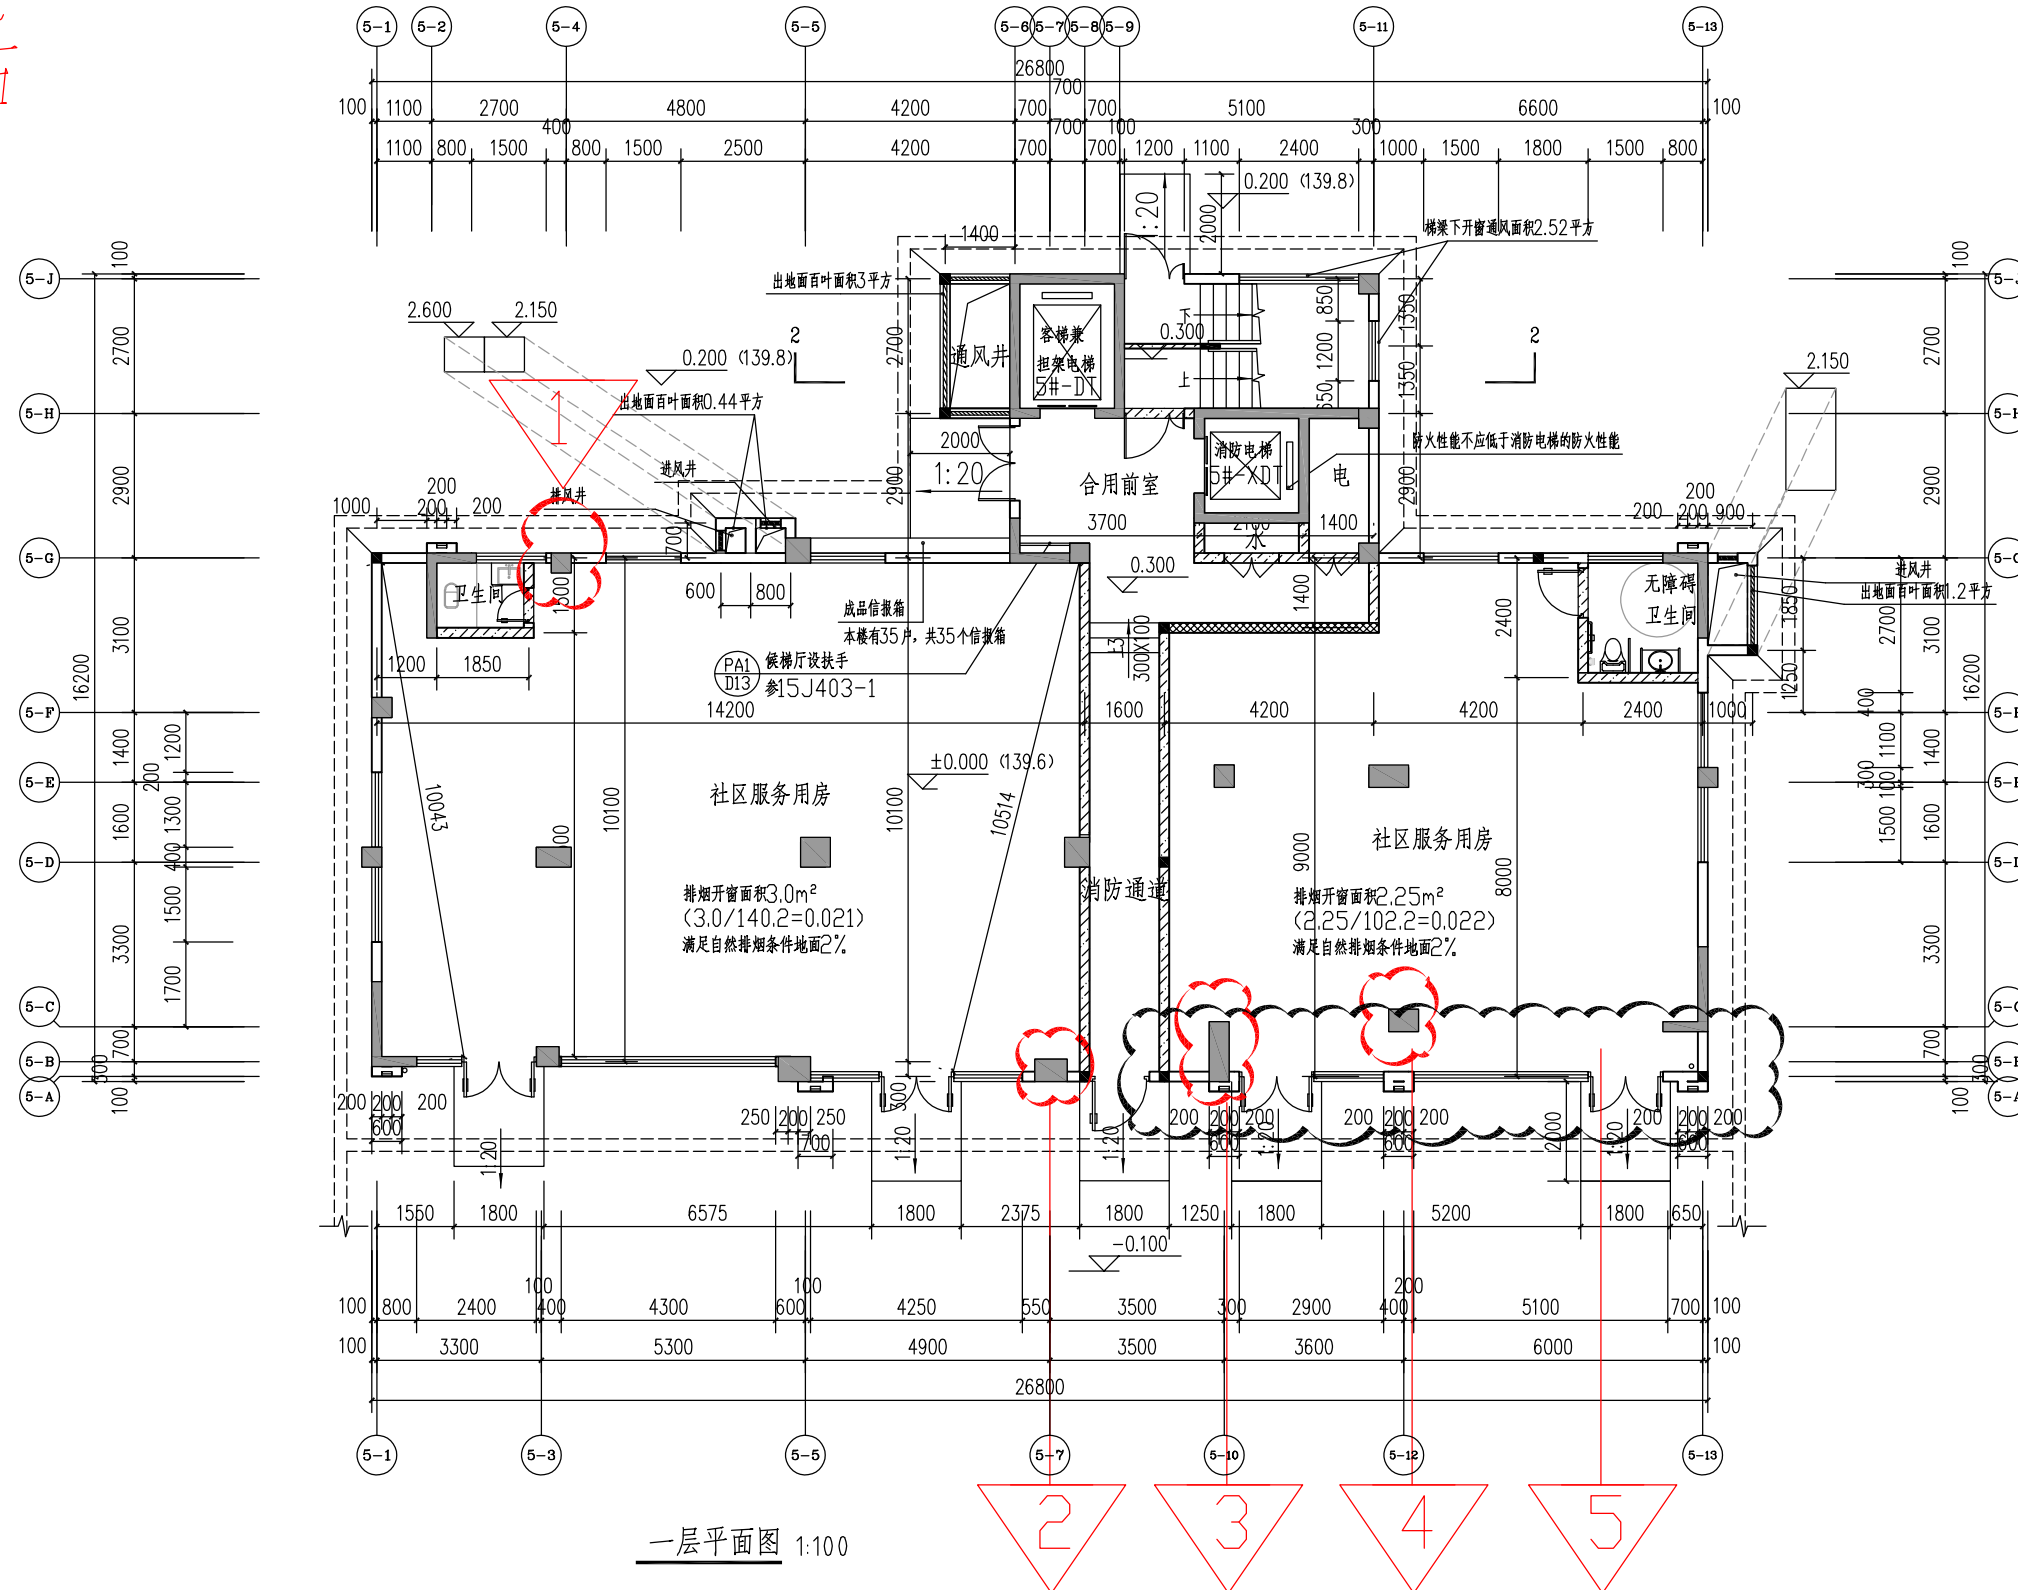


变更内容:


1. 图中⑤-G轴交⑤-1轴柱子往⑤-F方向移200mm 与外墙平
2. 图中⑤-A轴交⑤-7的柱子往⑤-B轴方向平移300mm 与外墙平

- 3.图中⊕₅₋₁₀轴交⊕_{5-A}轴柱子往⊕₅₋₇轴方向移200mm
- 4.图中⊕₅₋₁₂轴交⊕_{5-C}轴柱子往⊕_{5-D}轴方向移250mm
- 5.图中⊕₅₋₁₀轴~⊕₅₋₁₃轴交⊕_{5-A}轴右侧社区服务用房一个门改为两个门

变更前

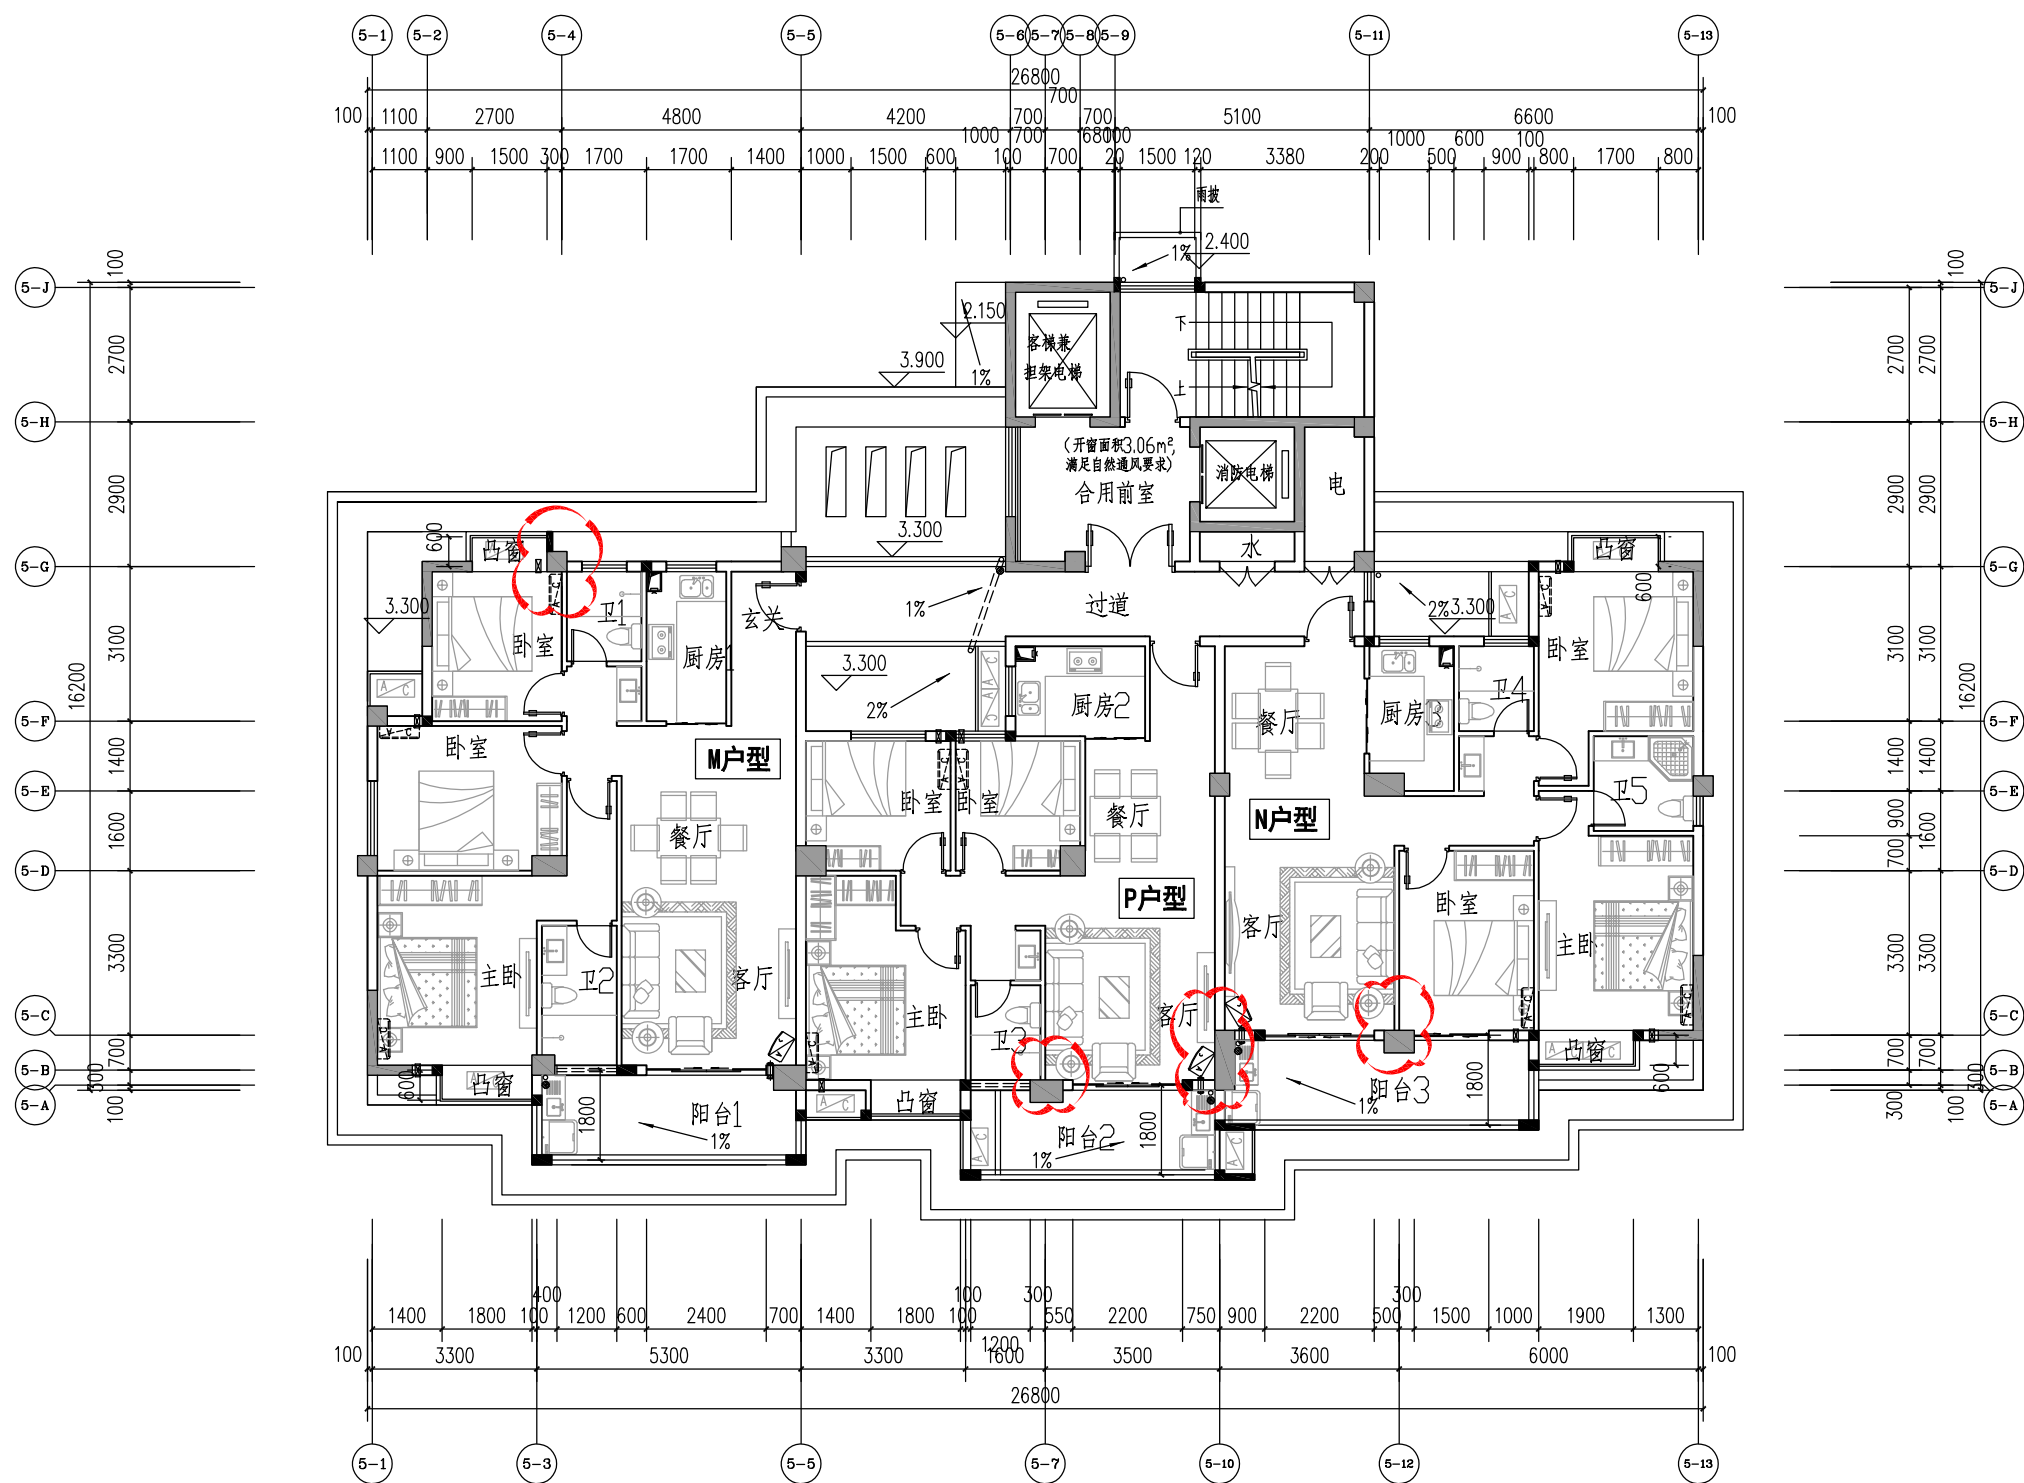


变更后

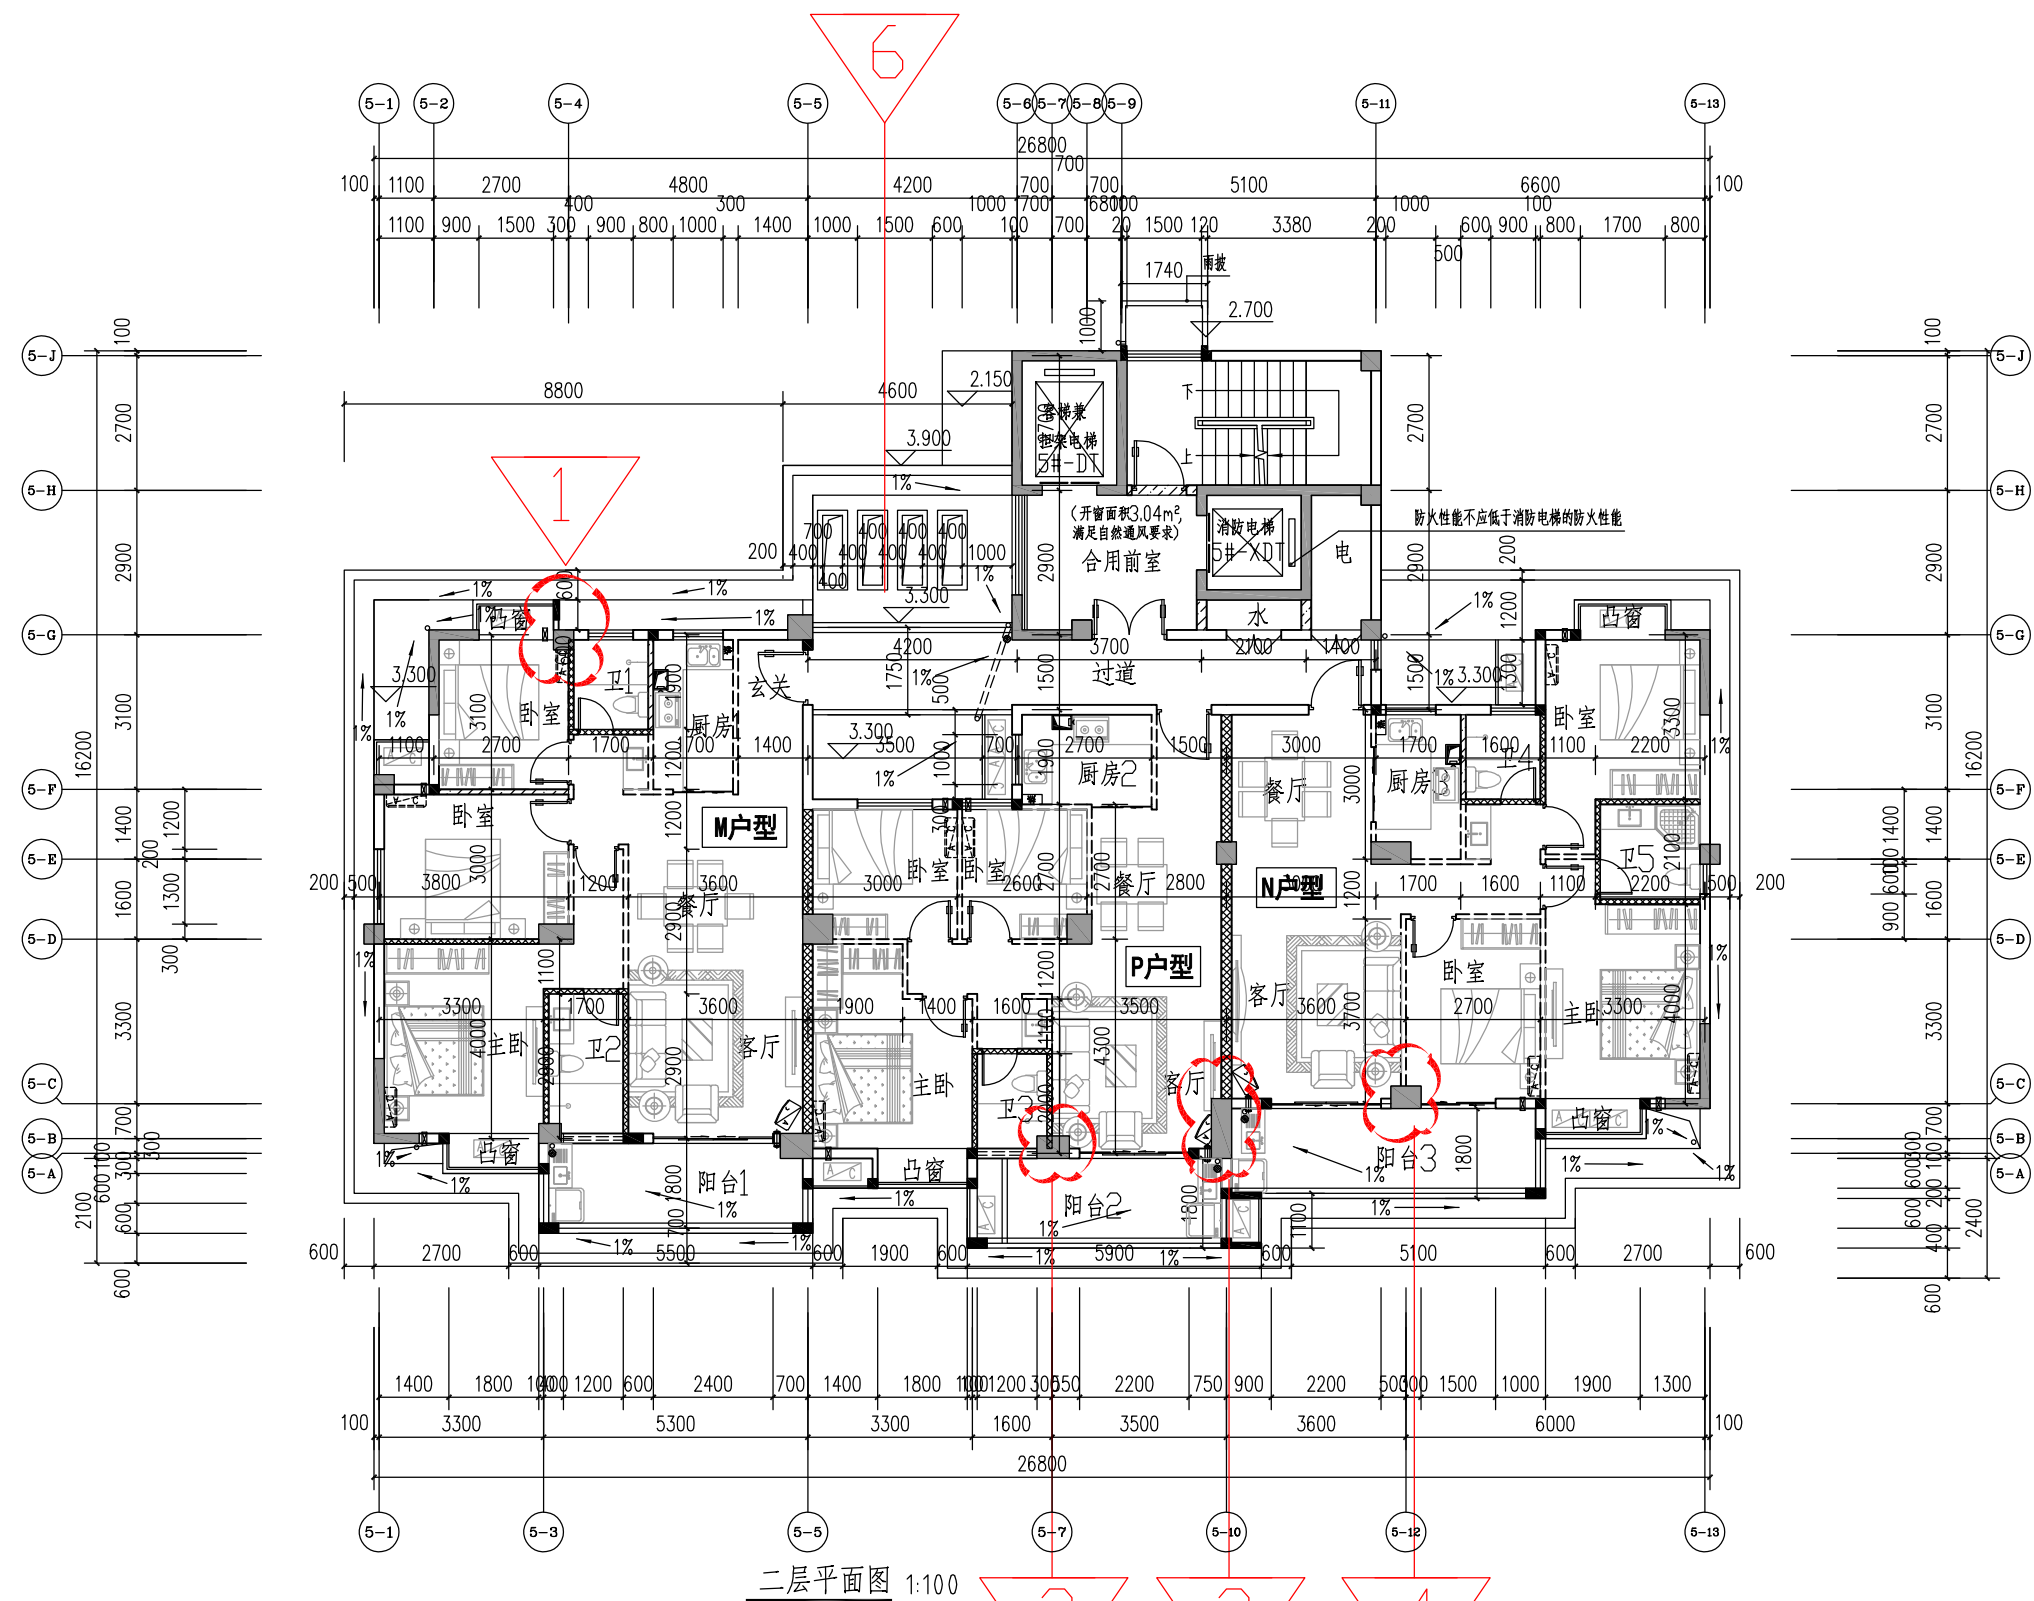

变更内容:


1. 图中⑤-G轴交⑤-1轴柱子往⑤-F方向移200mm与外墙平
2. 图中⑤-A轴交⑤-7的柱子往⑤-B轴方向平移300mm与外墙平
3. 图中⑤-10轴交⑤-A轴柱子往⑤-7轴方向移200mm
4. 图中⑤-12轴交⑤-C轴柱子往⑤-D轴方向移250mm
6. 图中⑤-5轴~⑤-6轴交⑤-G轴走道往⑤-H轴方向加宽50mm尺寸由1700mm改为1750mm

变更前

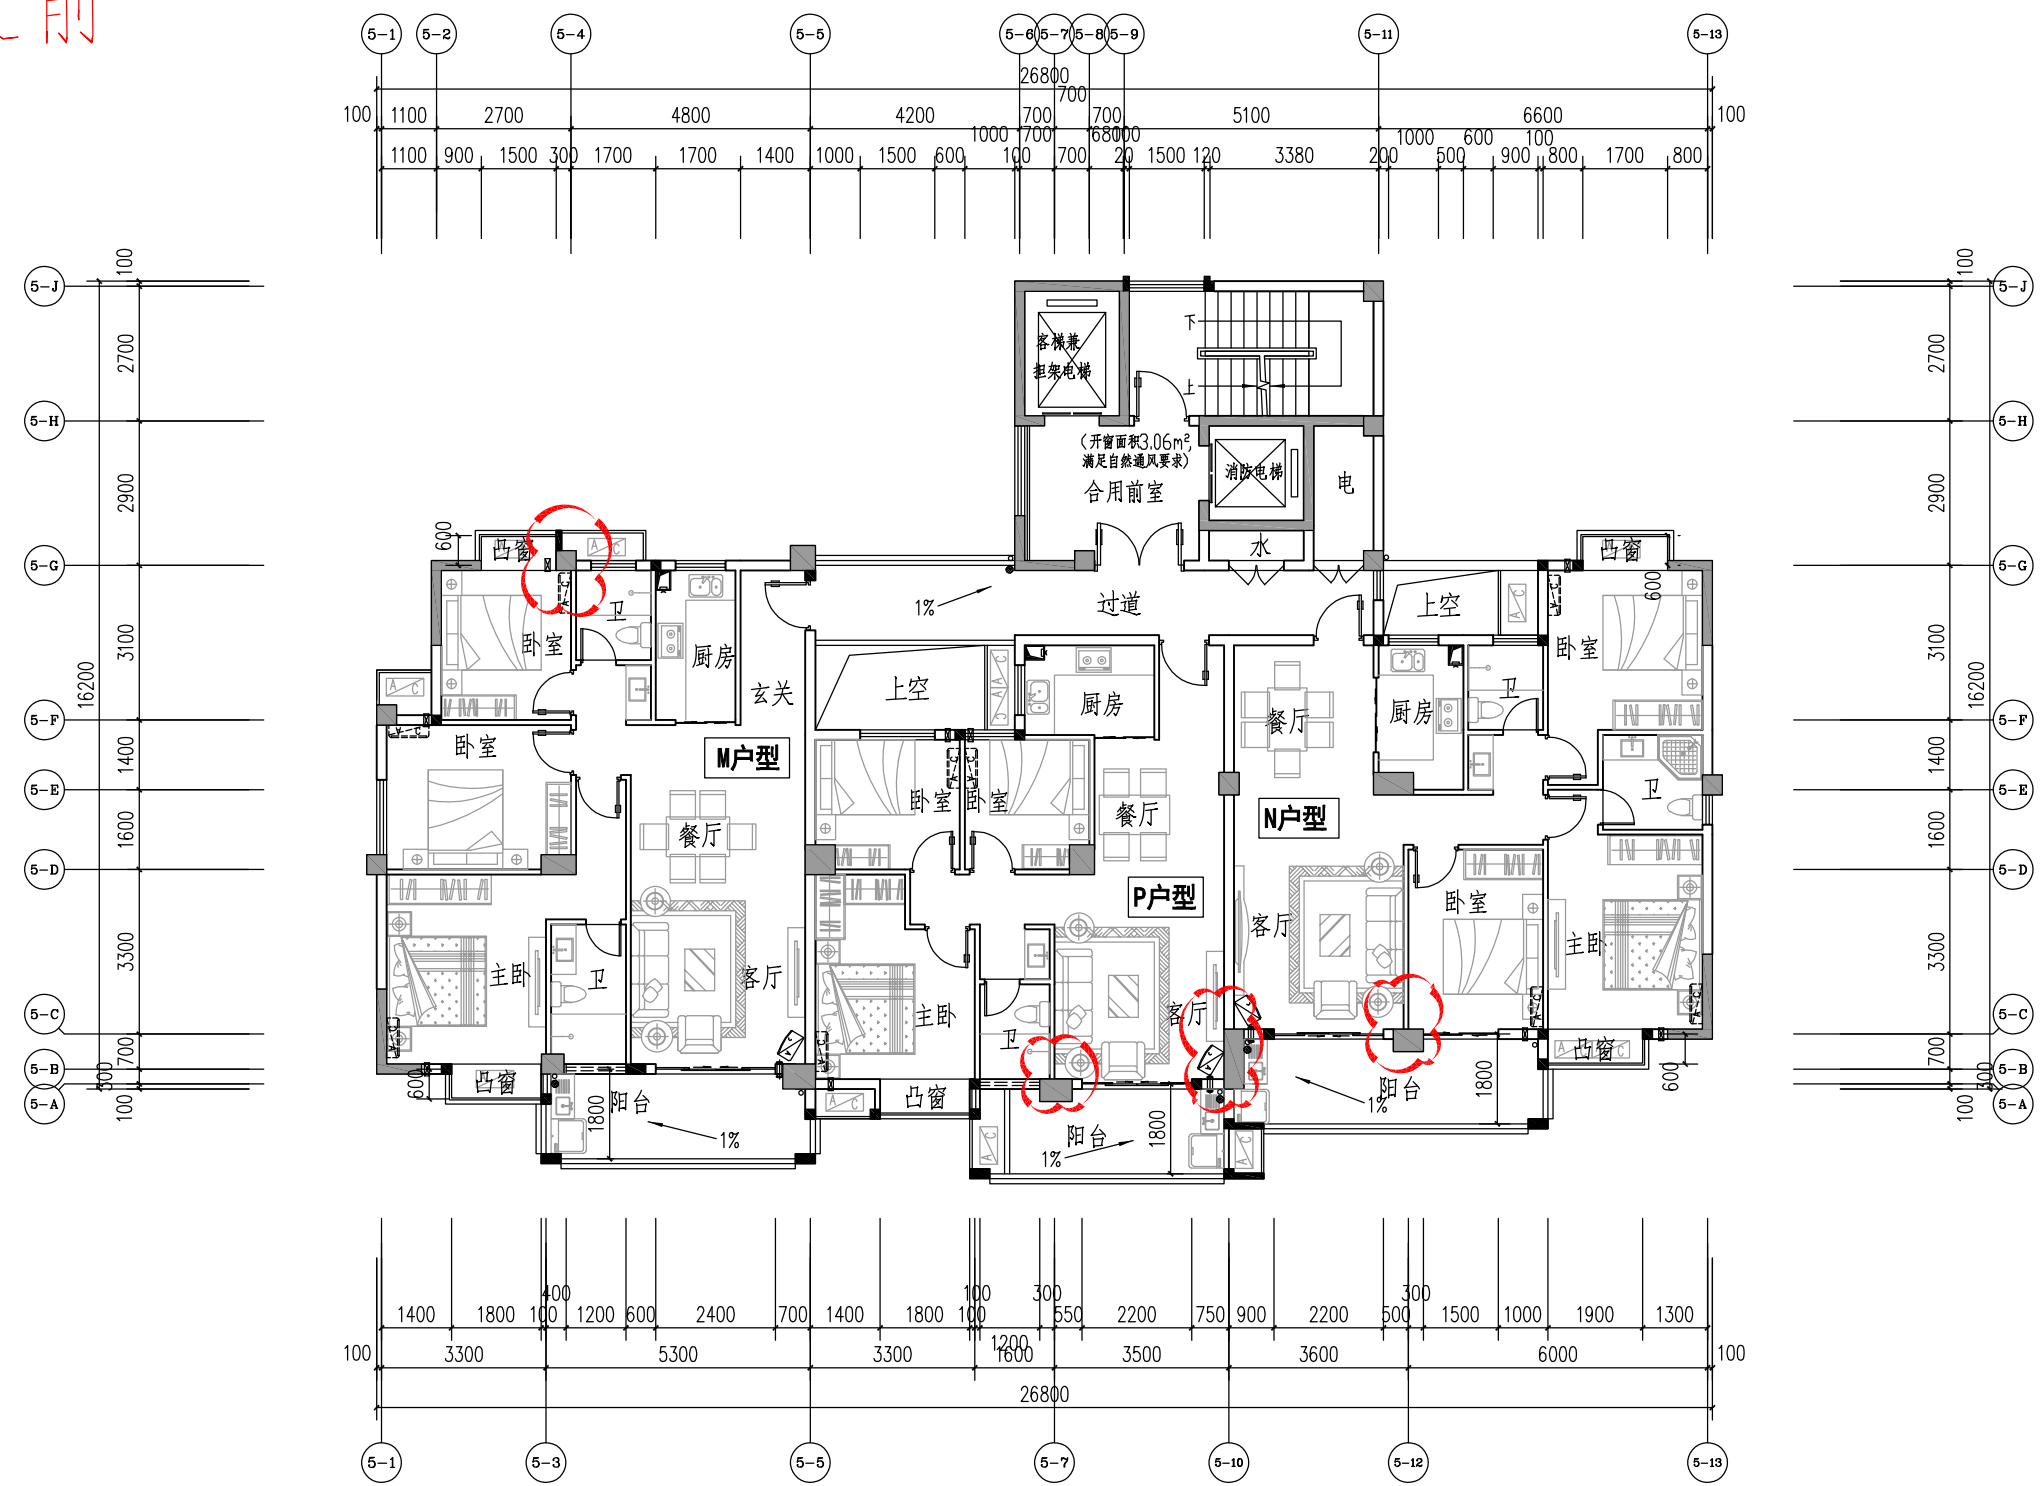

5#楼 三~十八层平面图

变更后

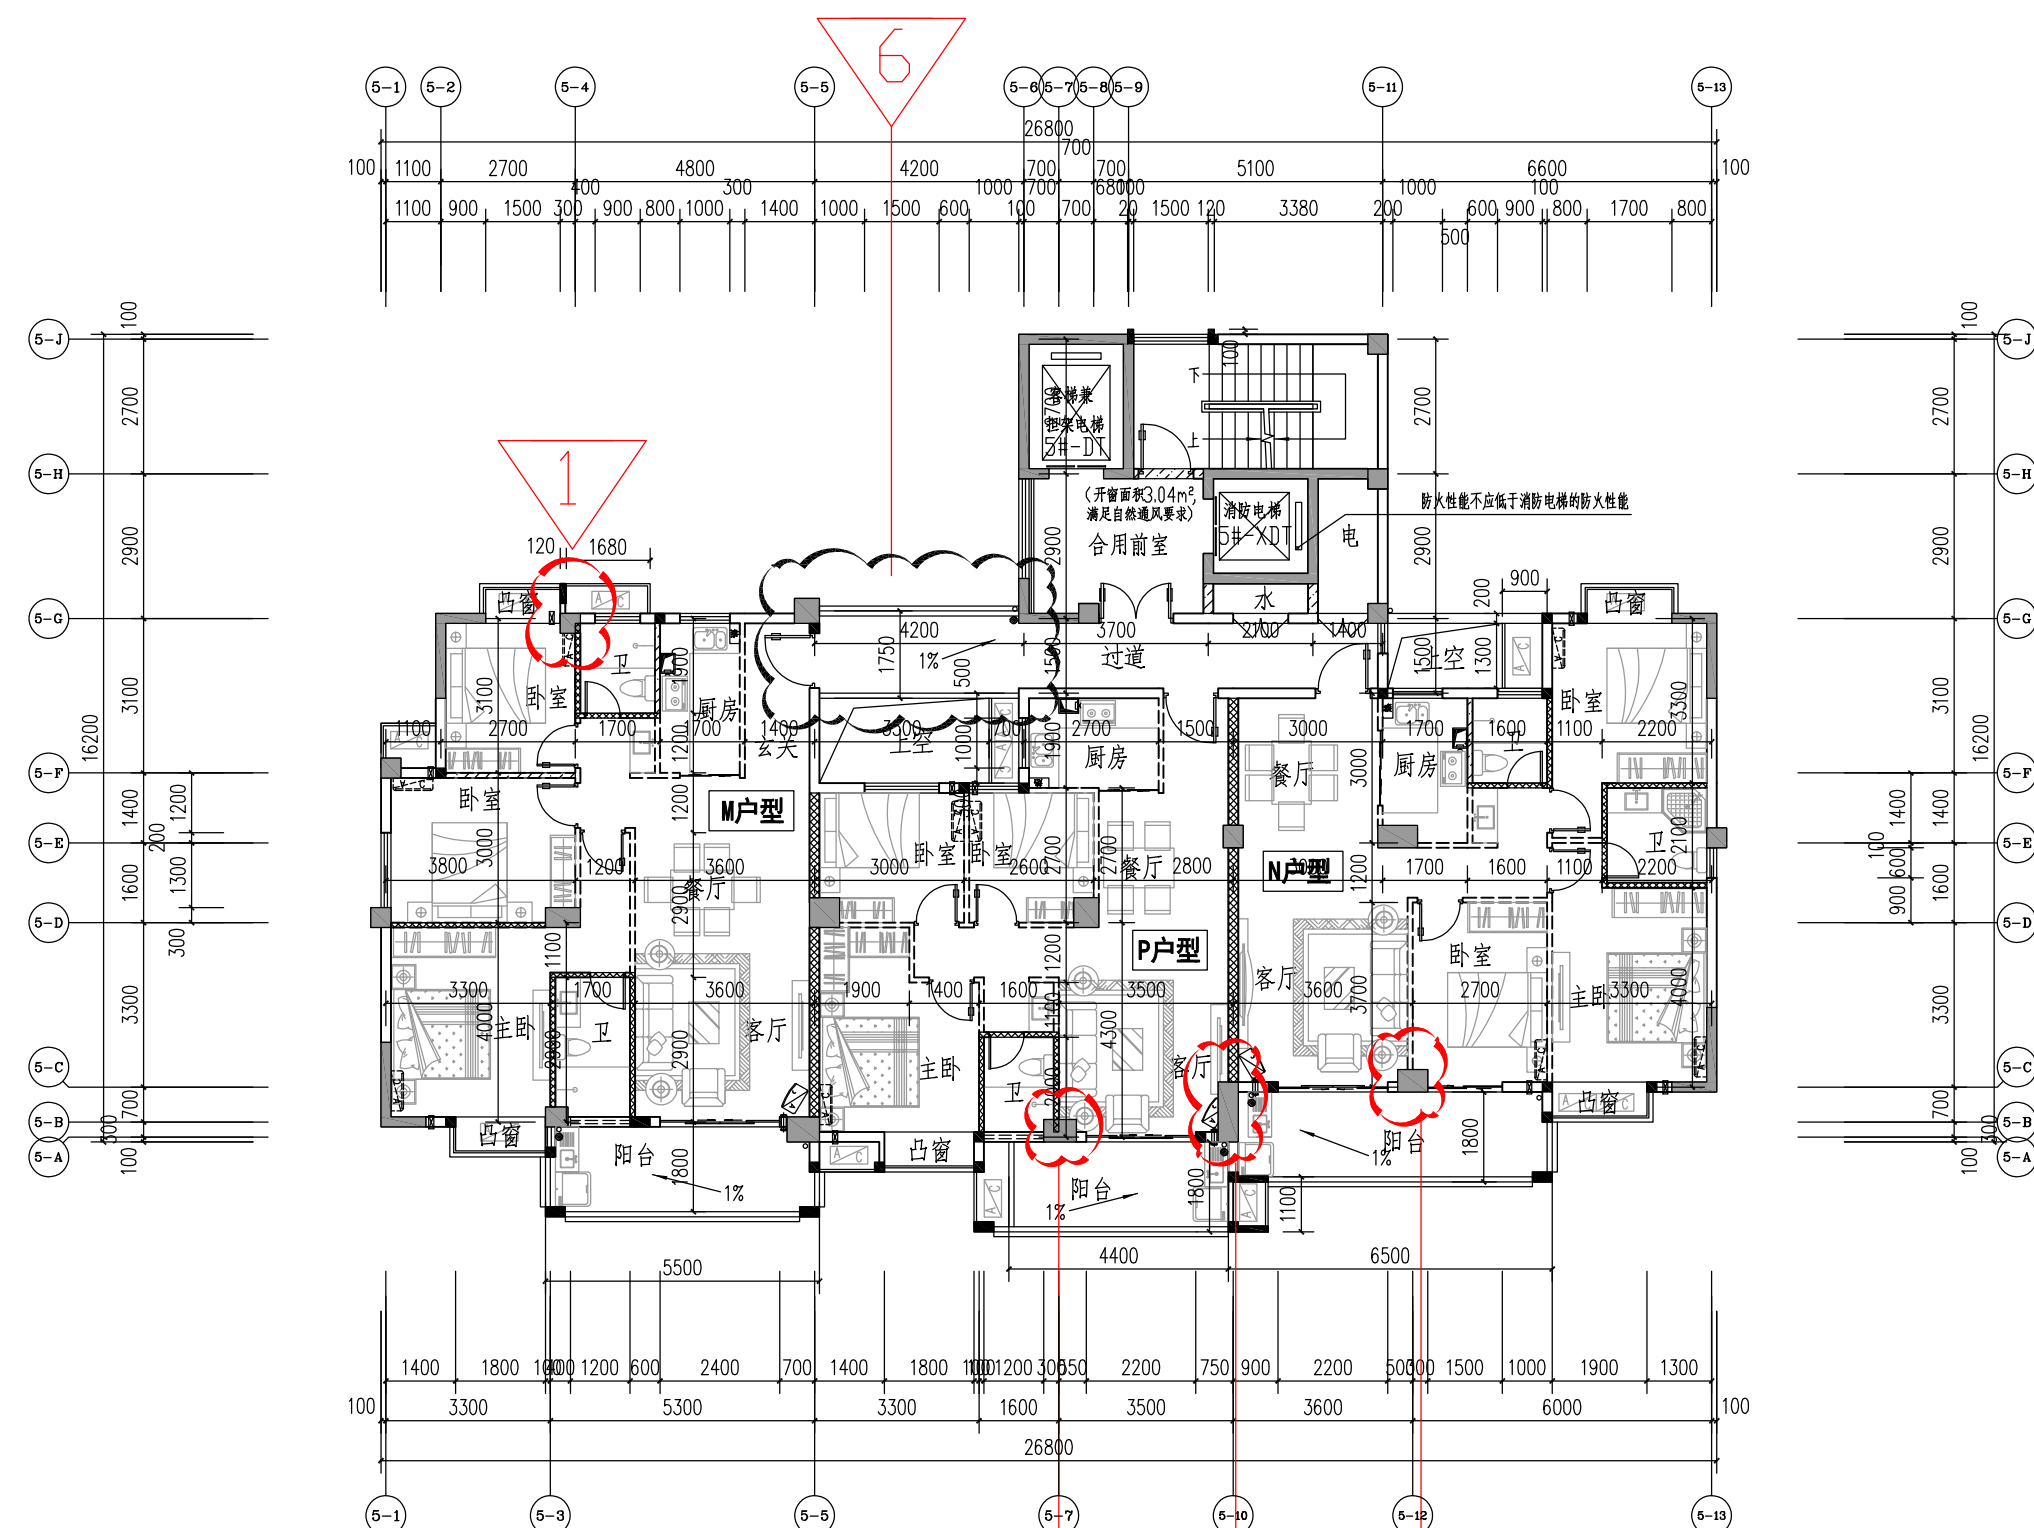


三~十八层平面图 1:100

变更内容:


1. 图中⑤-9轴交⑤-1轴柱子往⑤-F方向移200mm与外墙平
2. 图中⑤-A轴交⑤-7的柱子往⑤-B轴方向平移300mm与外墙平
3. 图中⑤-10轴交⑤-A轴柱子往⑤-7轴方向移200mm
4. 图中⑤-12轴交⑤-C轴柱子往⑤-D轴方向移250mm
6. 图中⑤-5轴~⑤-6轴交⑤-G轴走道往⑤-H轴方向加宽50mm尺寸由1700mm改为1750mm

变更前

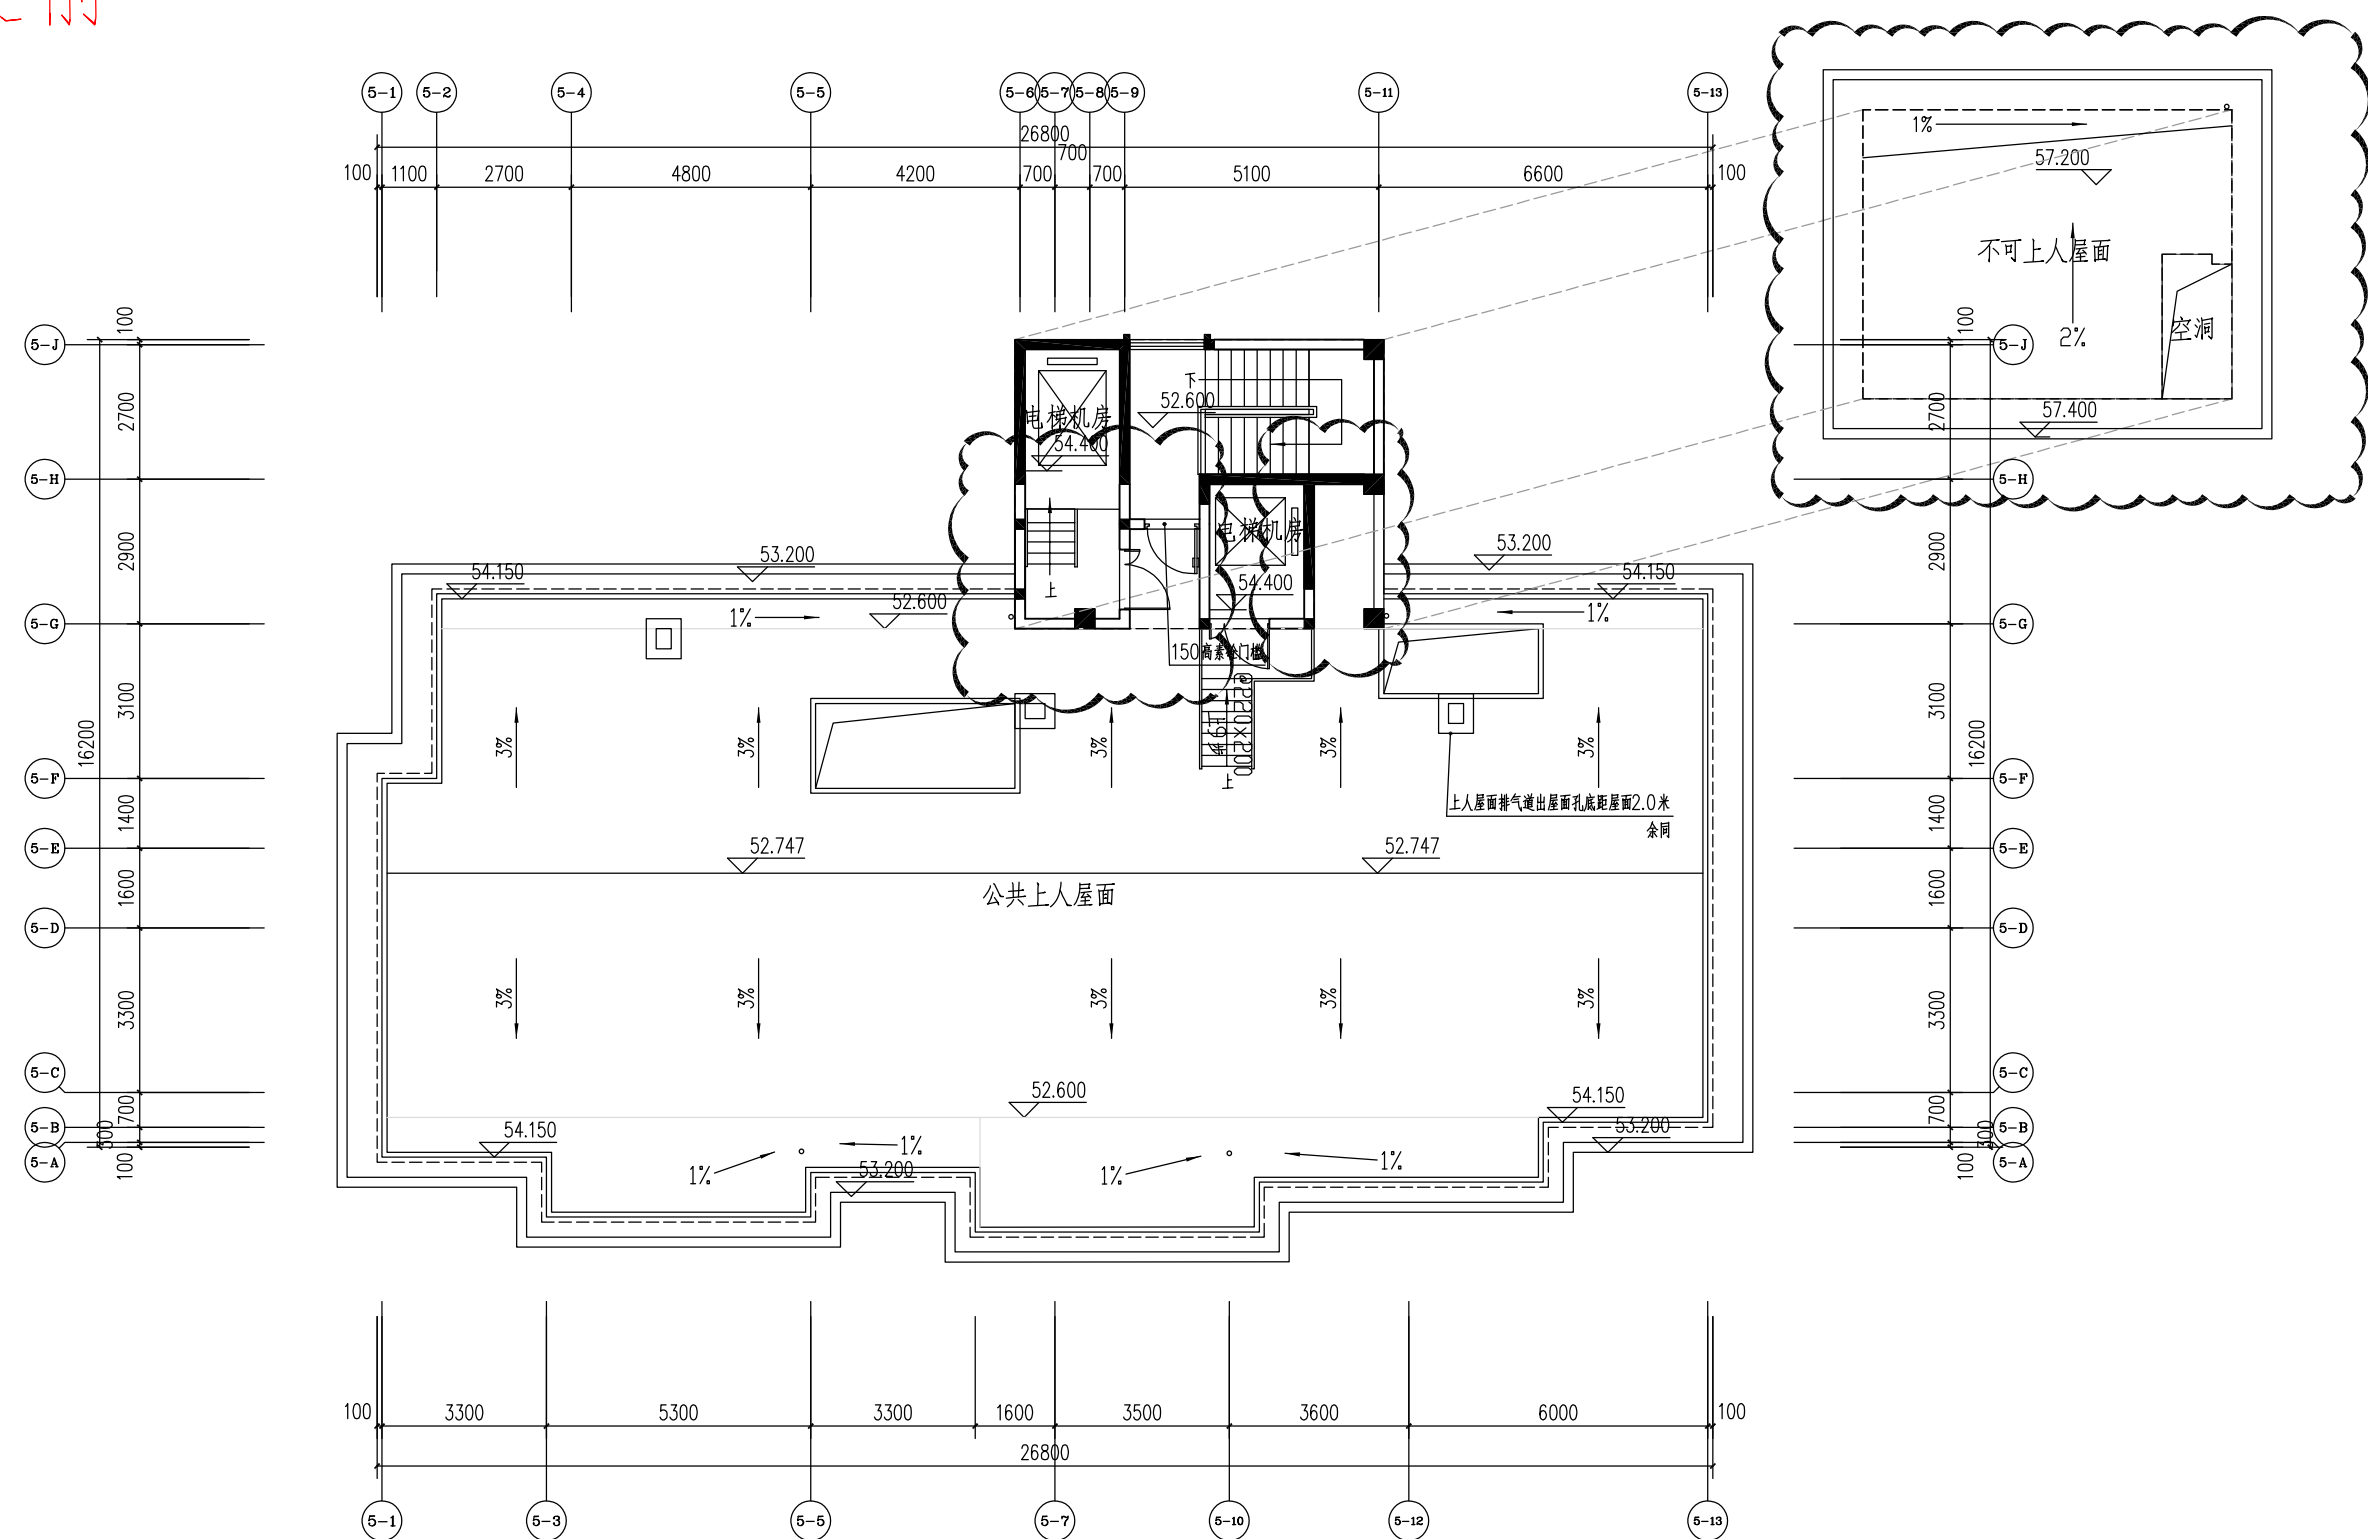

5#楼 屋面层平面图

变更后

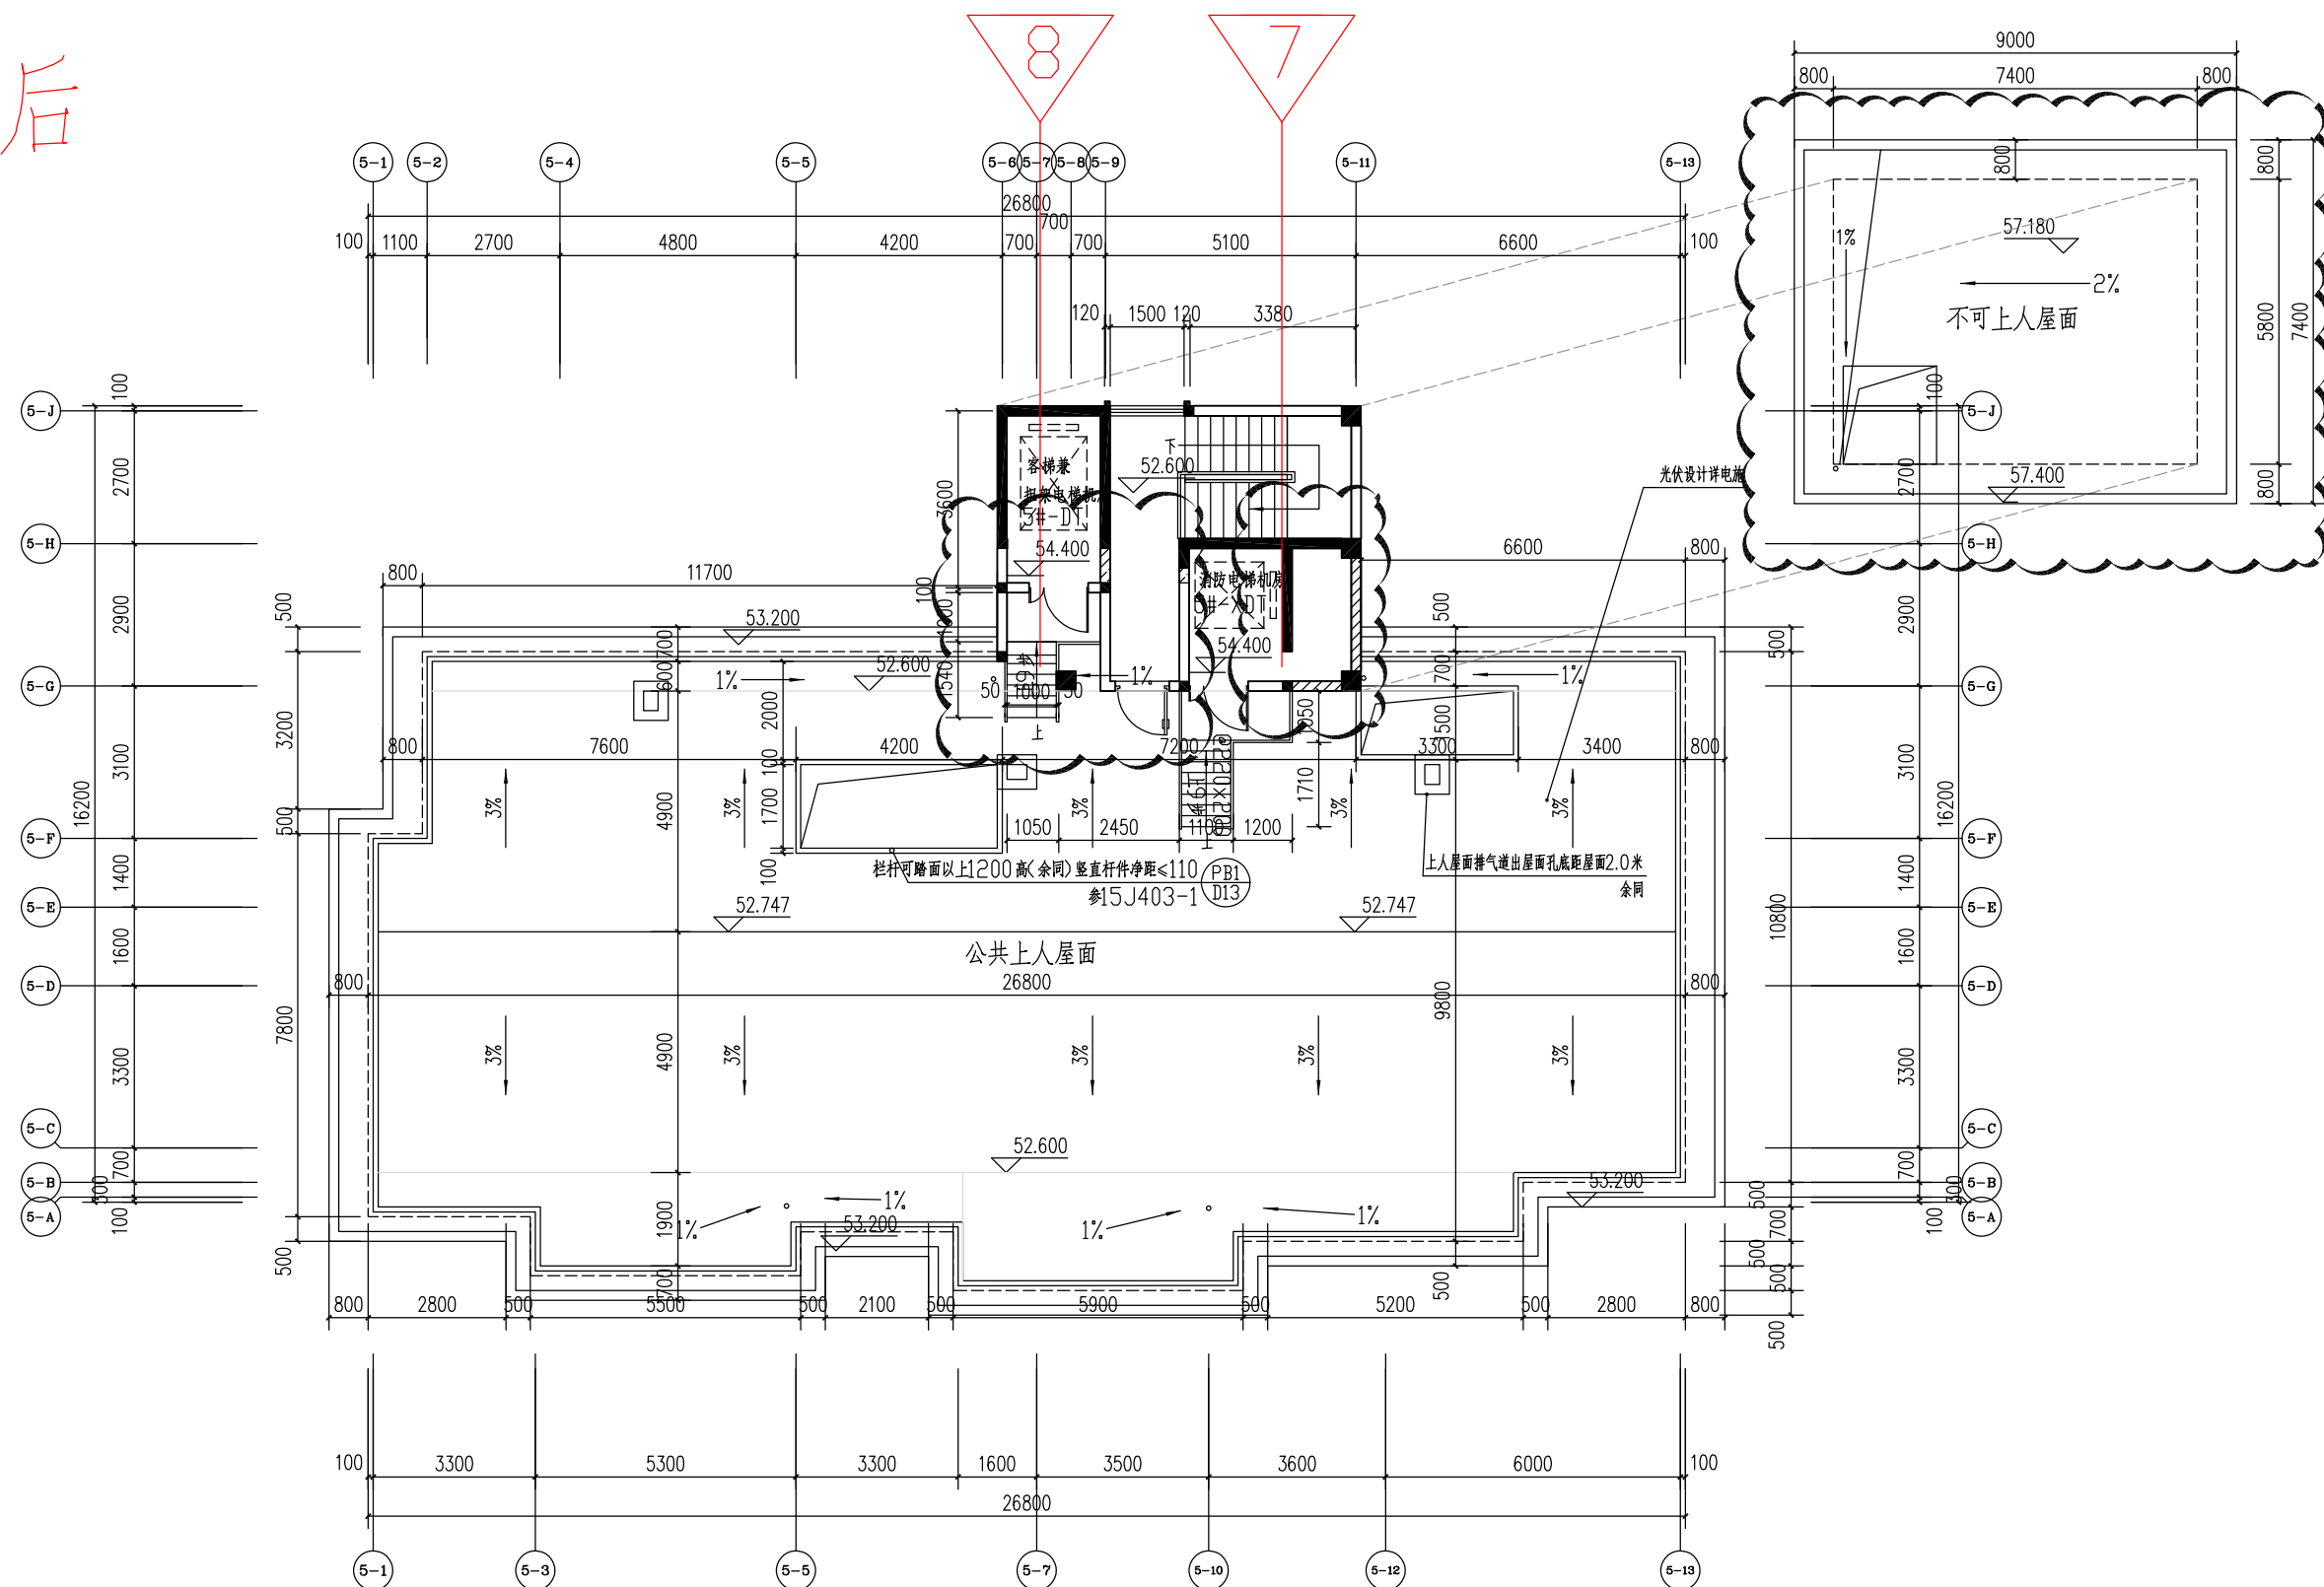

变更内容:


屋面层平面图 1:100

7.图中⑤-⑥轴交⑤-⑪轴电梯机房屋面空洞取消,增设屋面板及新增墙体(墙体阴影部分)

8.图中⑤-⑥轴交⑤-⑥~⑤-⑨轴客梯机房墙体往上移2000mm,墙体及开门位置调整


图中⑤-⑥轴交⑤-⑥~⑤-⑨轴电梯机房屋面设空洞,楼梯间出屋面门及墙往下移2000mm至⑤-⑥轴

变更前

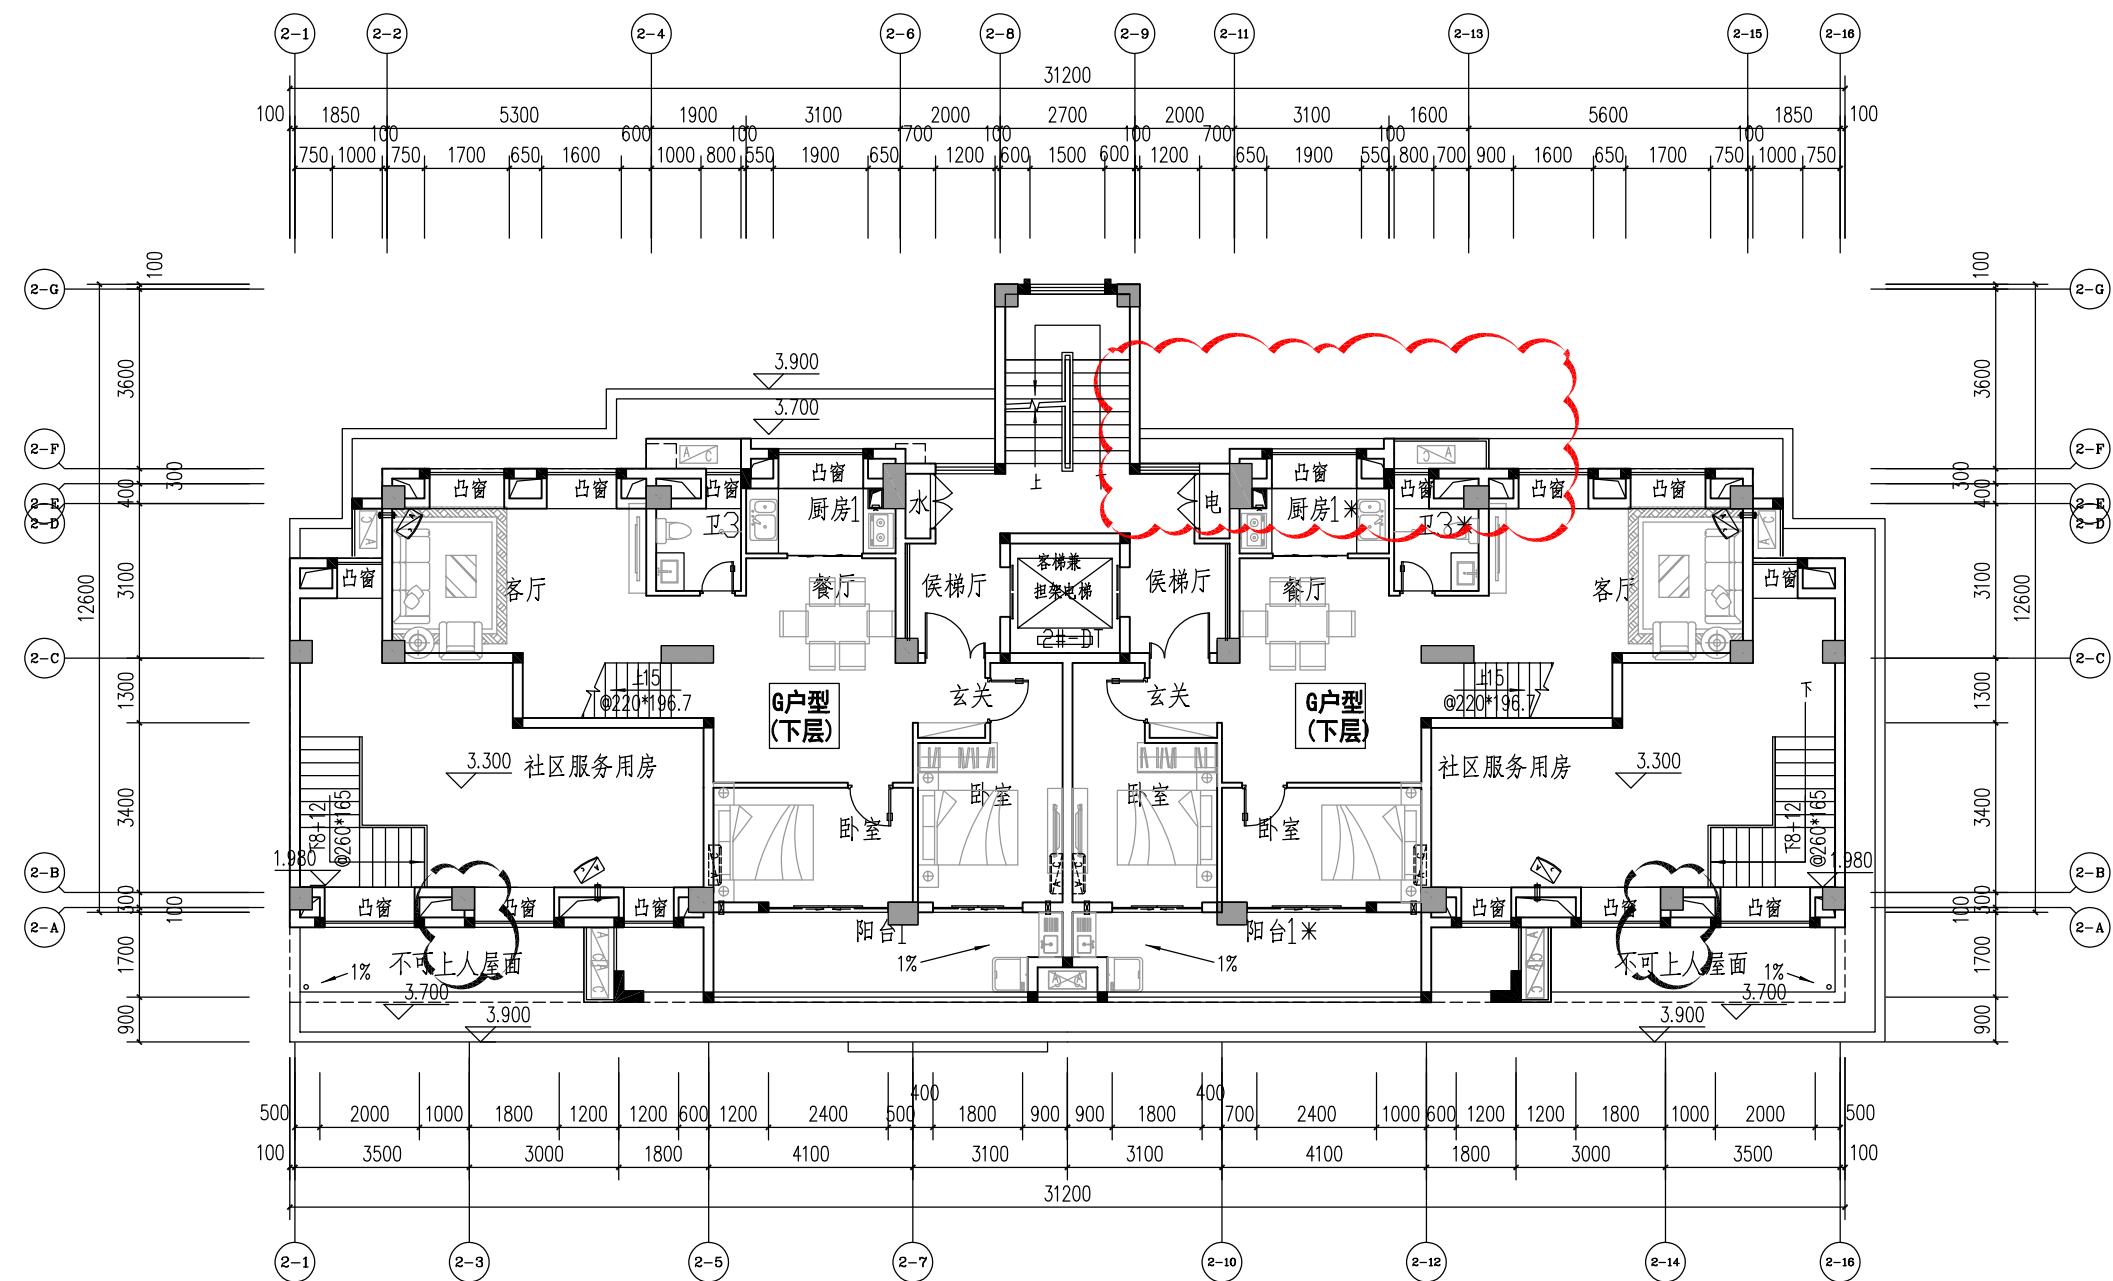

2#楼 二层平面图

变更后

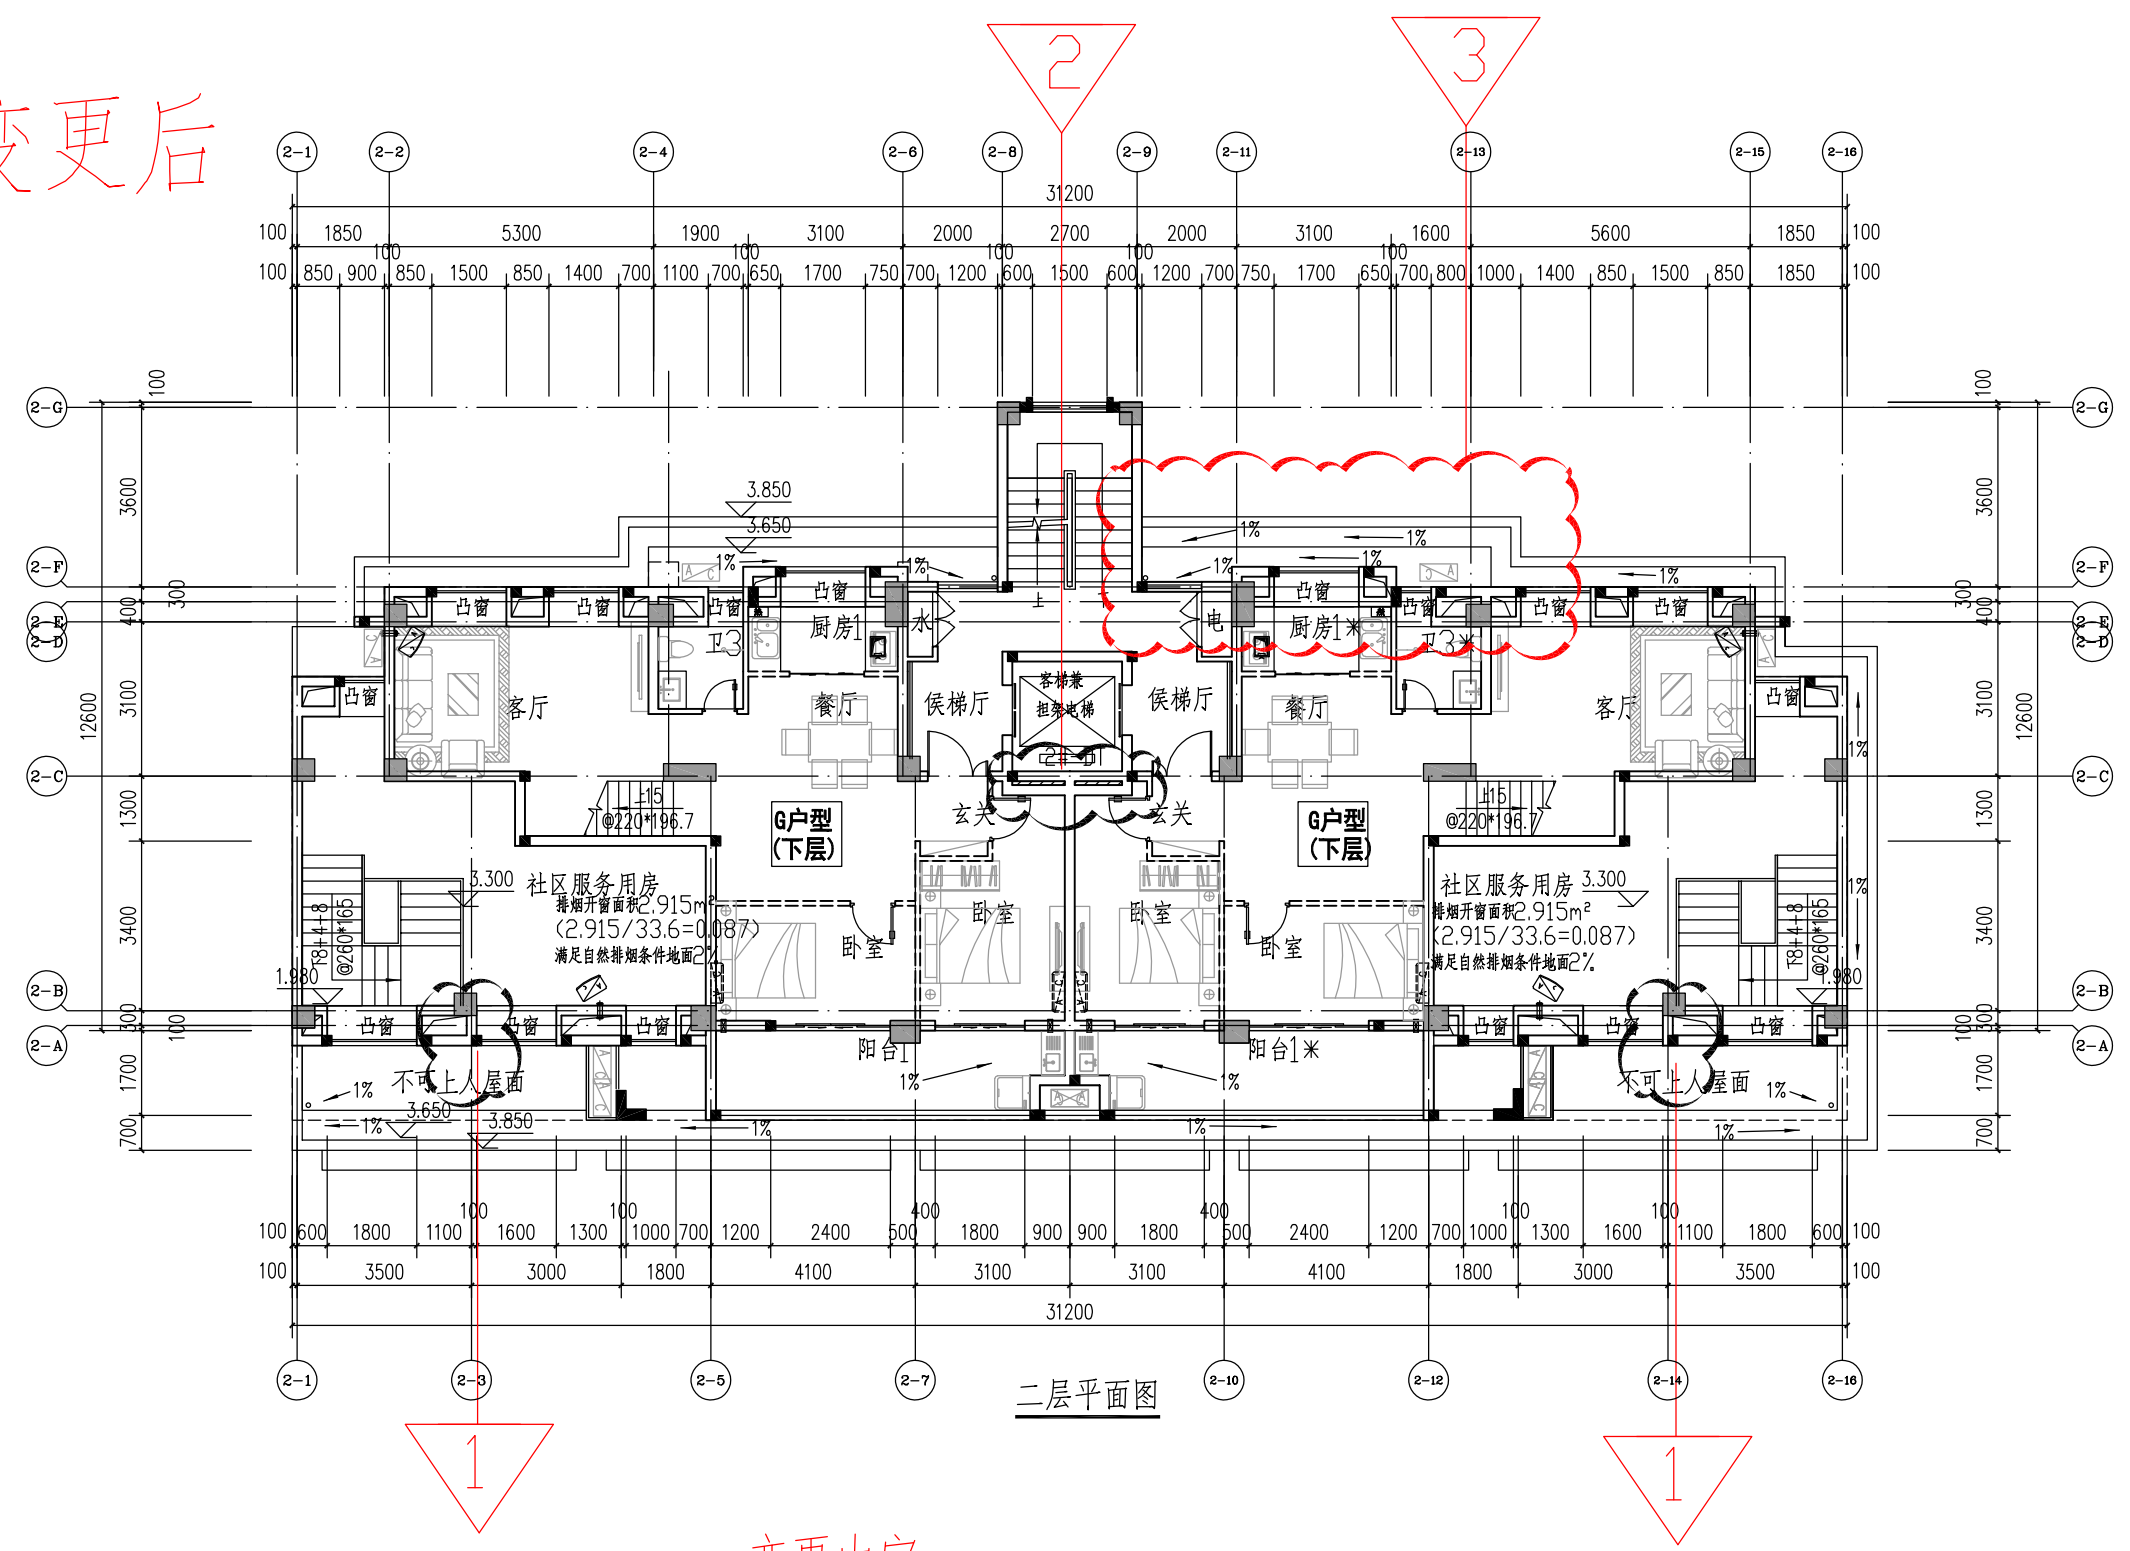


二层平面图

变更内容:


1. 图中②-A轴交②-3及②-14轴柱子往②-B方向移250mm 与外墙平
2. 图中②-C轴交②-8轴、②-9轴增设一段电梯隔音墙
3. 图中②-F轴交②-9轴~②-13轴（楼梯右侧）处挑檐增加800mm

变更前

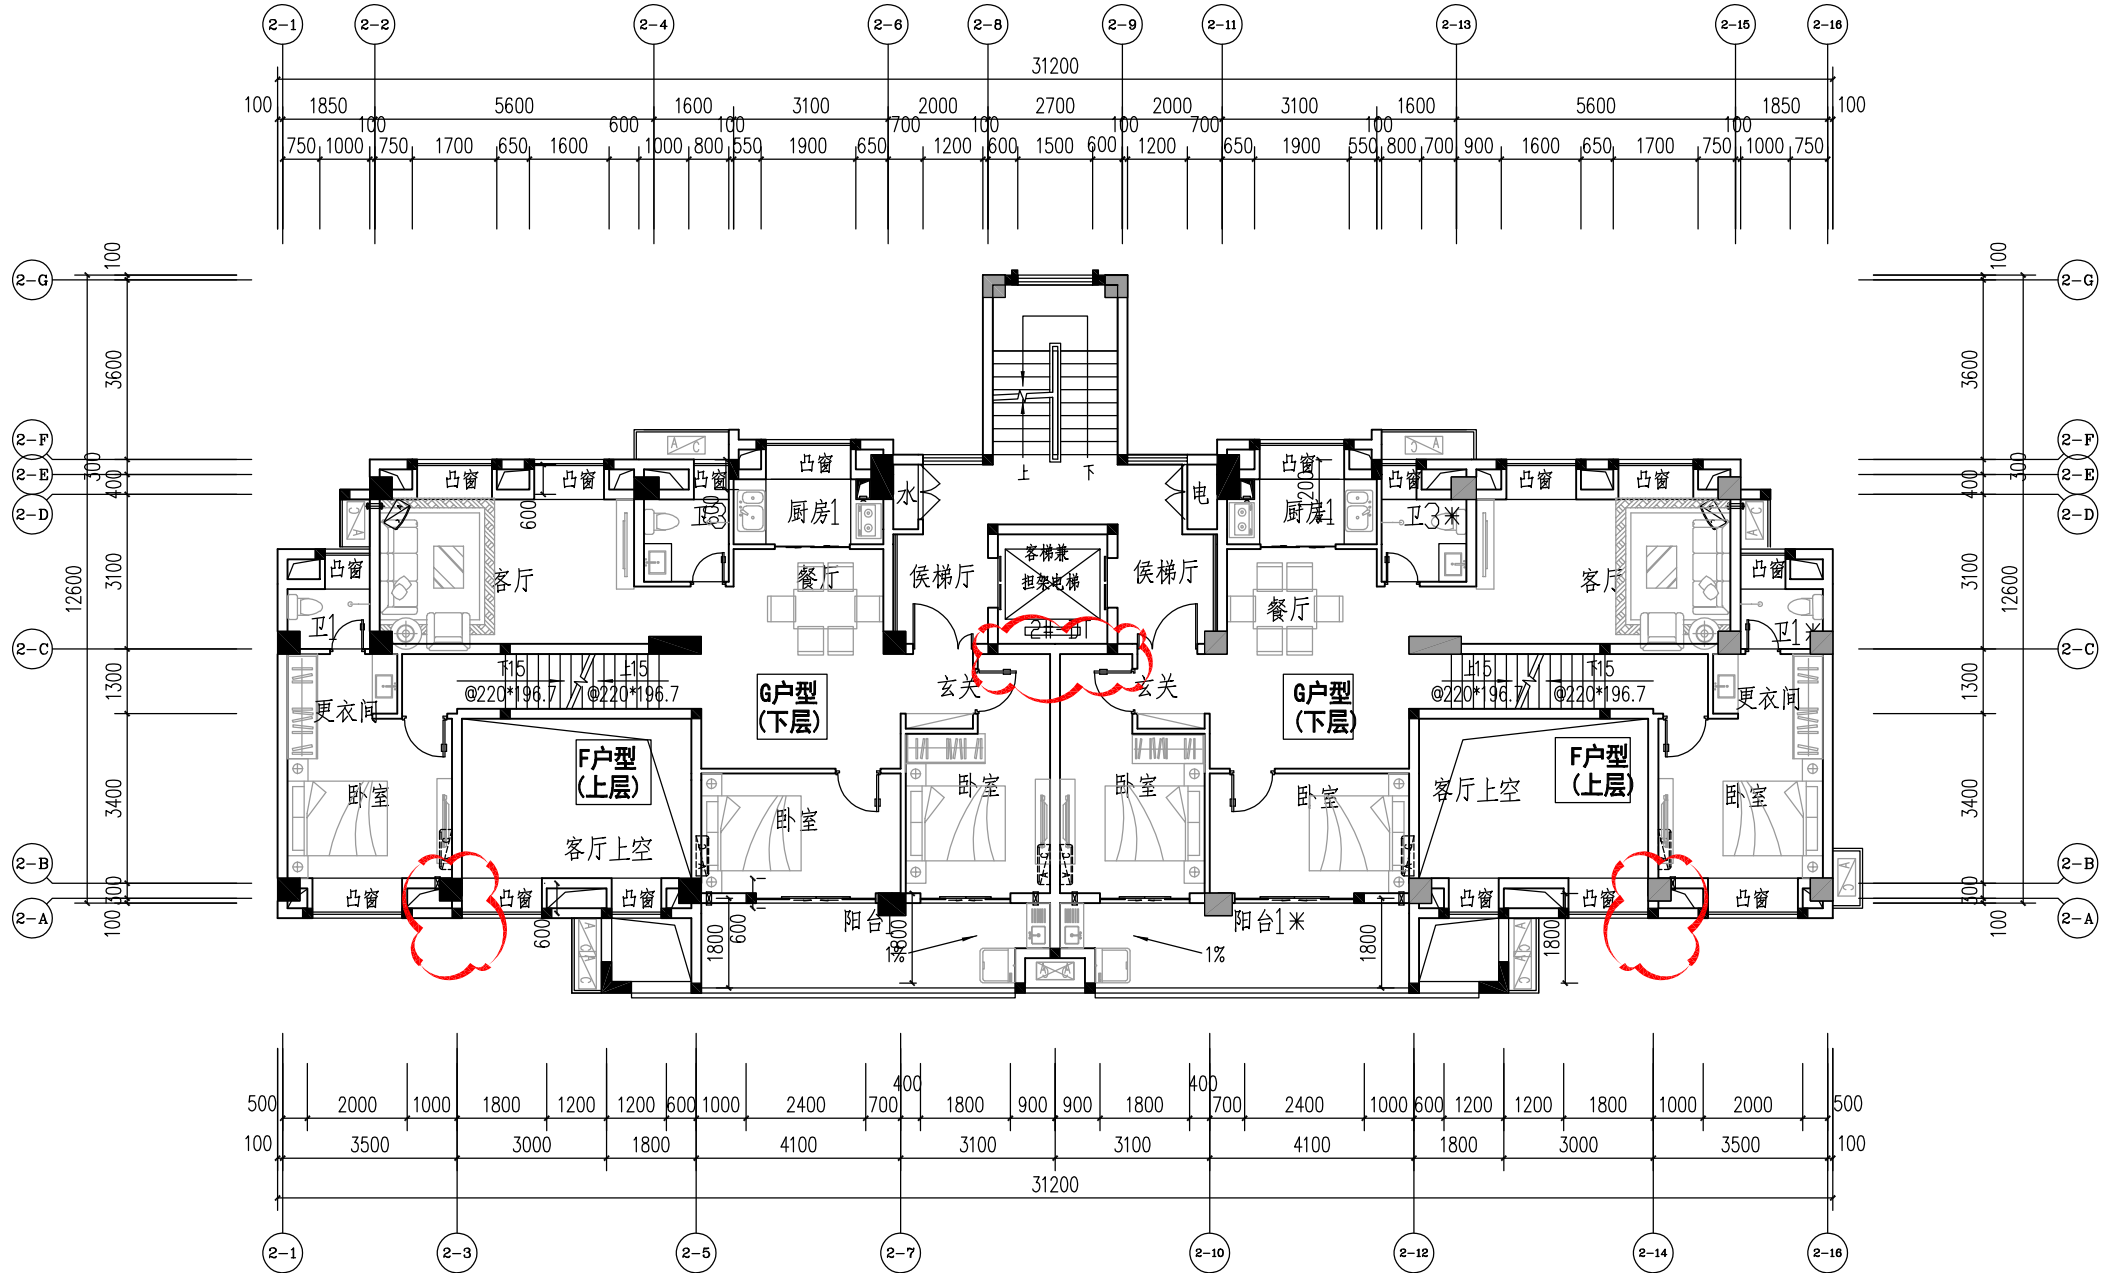

2#楼 四、六、八、十层平面图

变更后

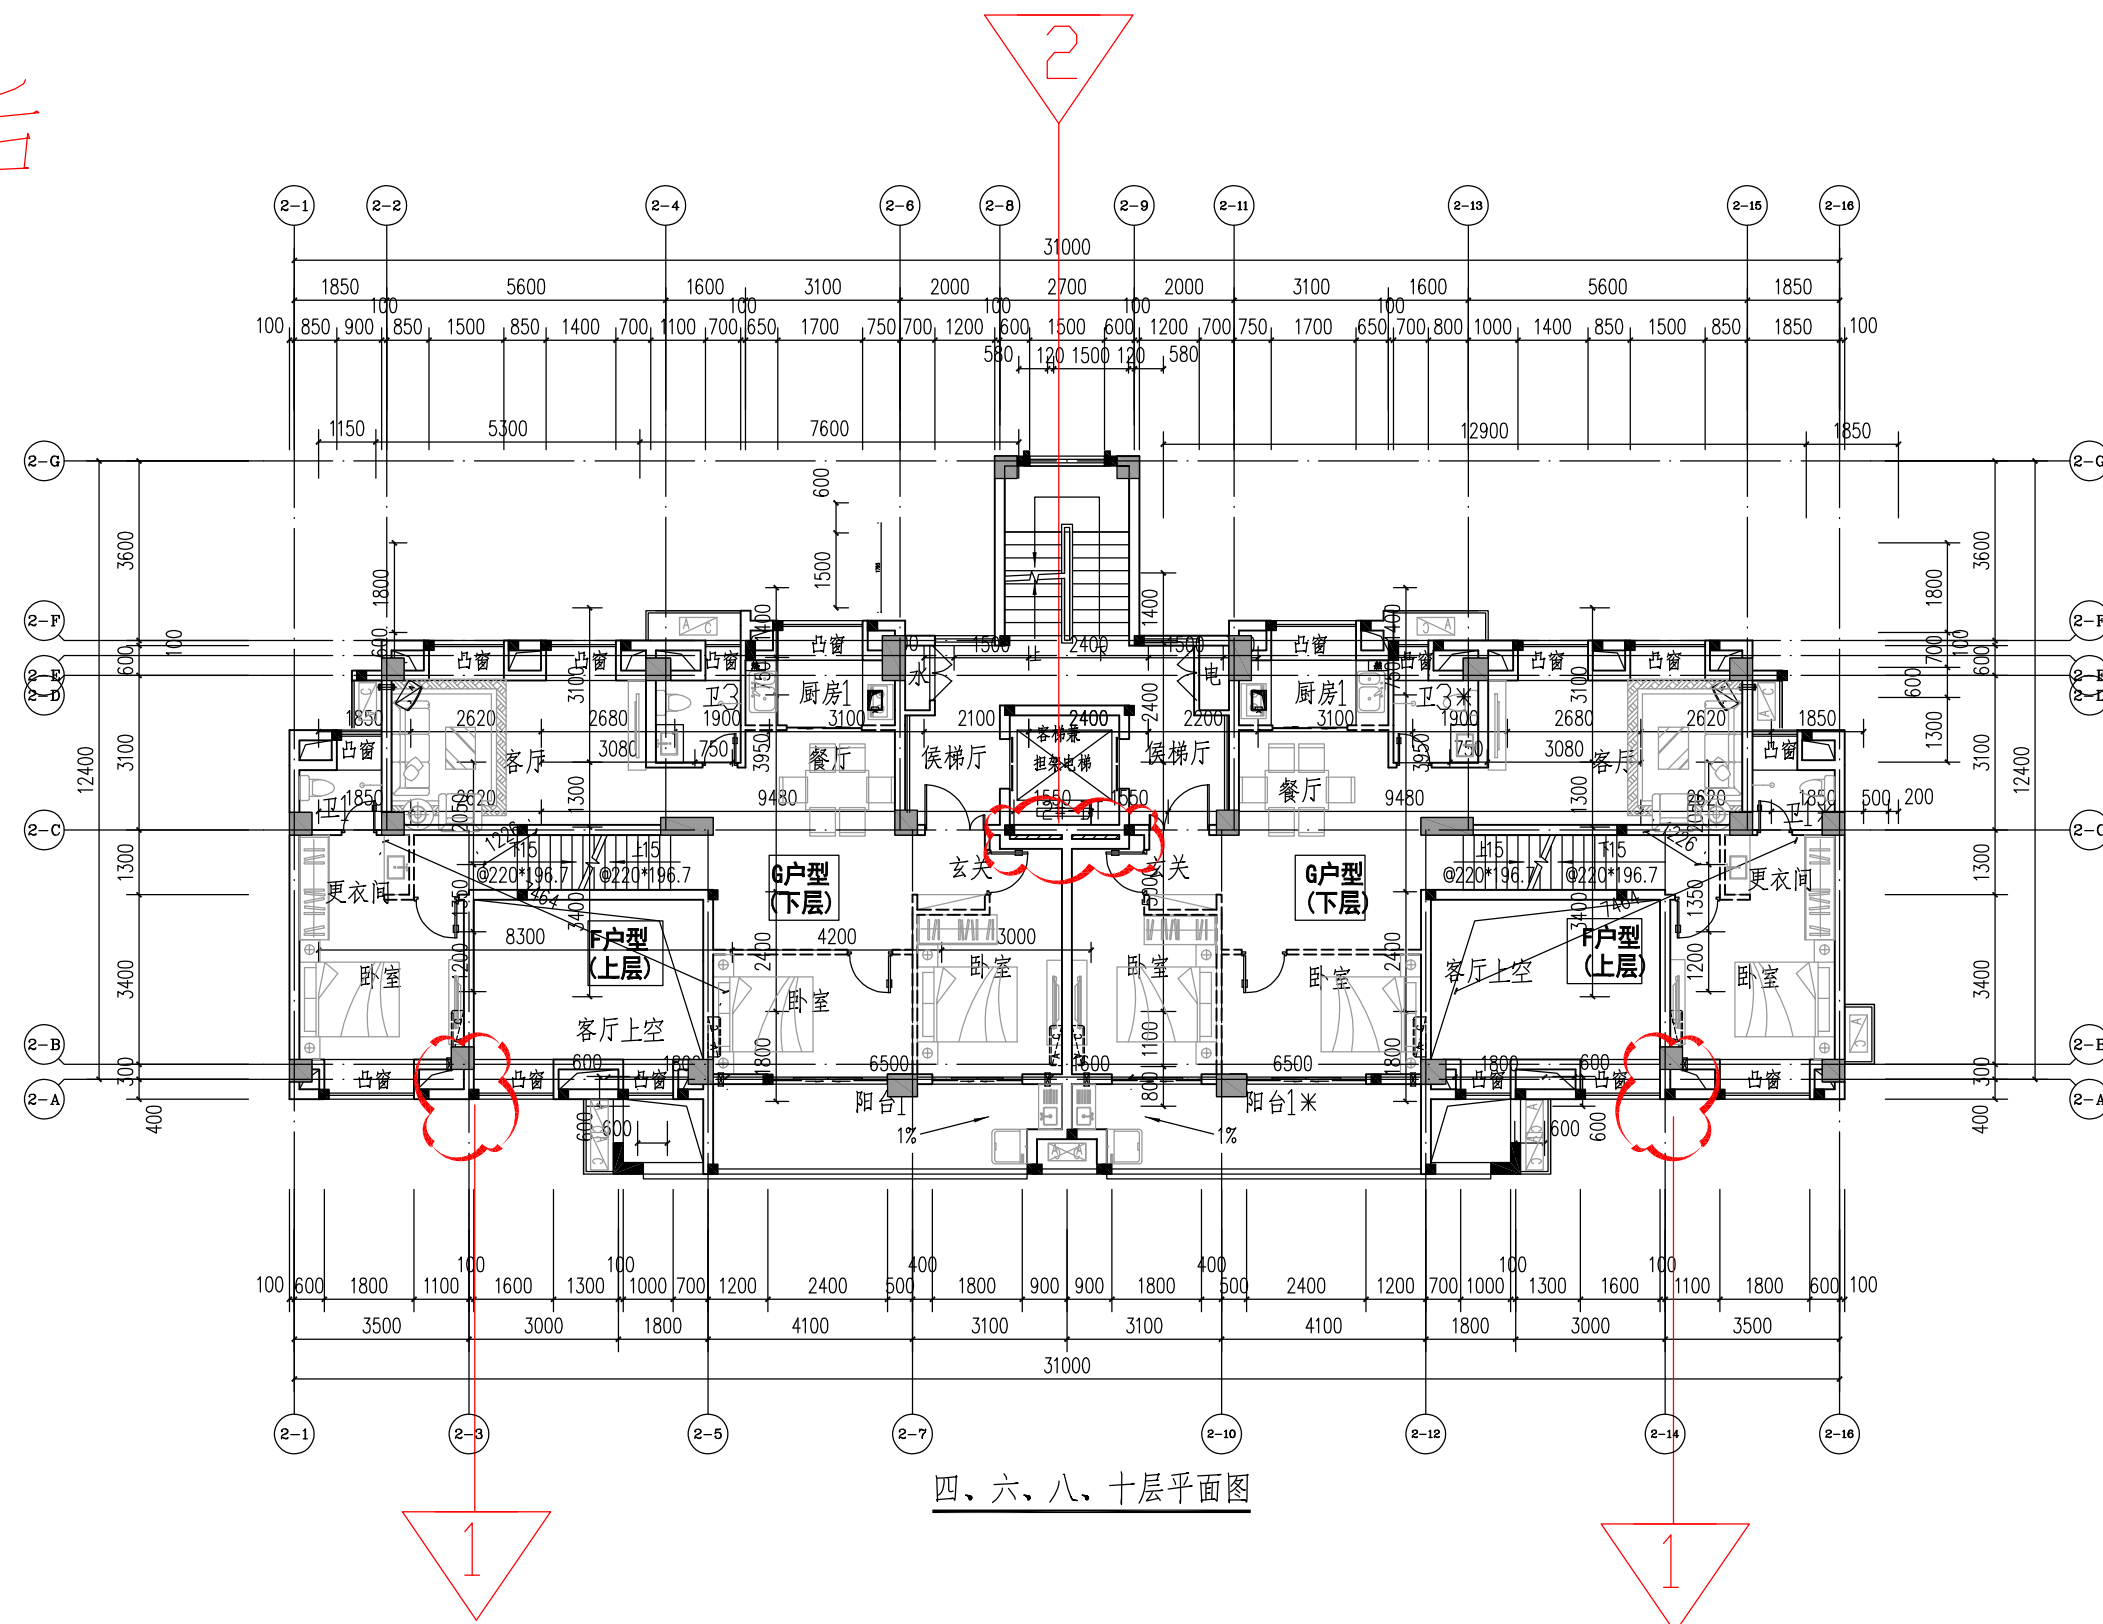


四、六、八、十层平面图

变更内容:


1. 图中②-A轴交②-3及②-14轴柱子往②-B方向移250mm 与外墙平
2. 图中②-C轴交②-8轴、②-9轴增设一段电梯隔音墙

变更前

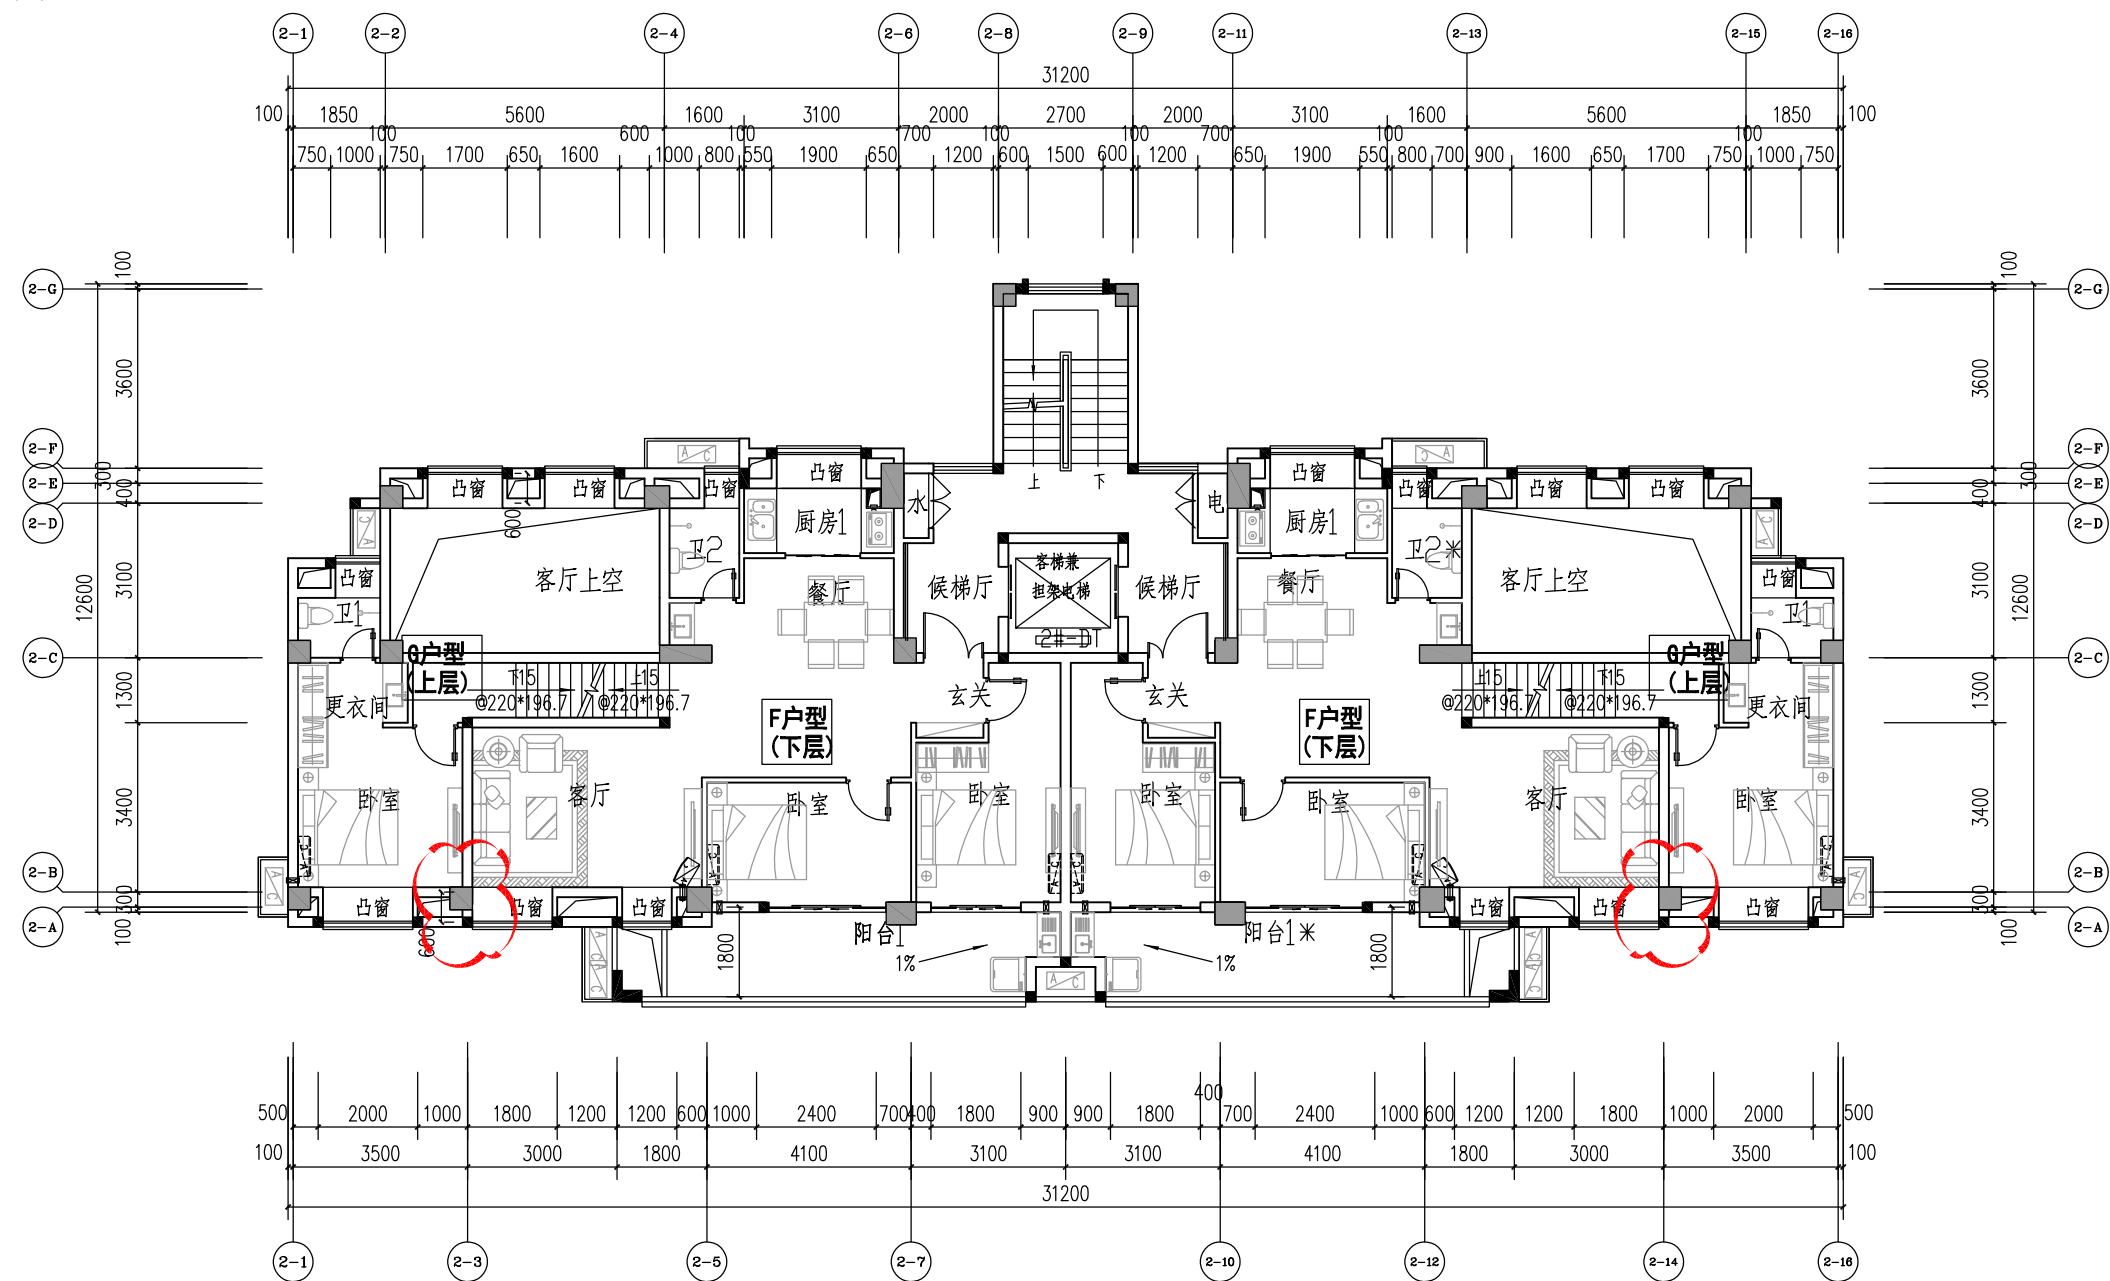

2#楼 三、五、七、九层平面图

变更后

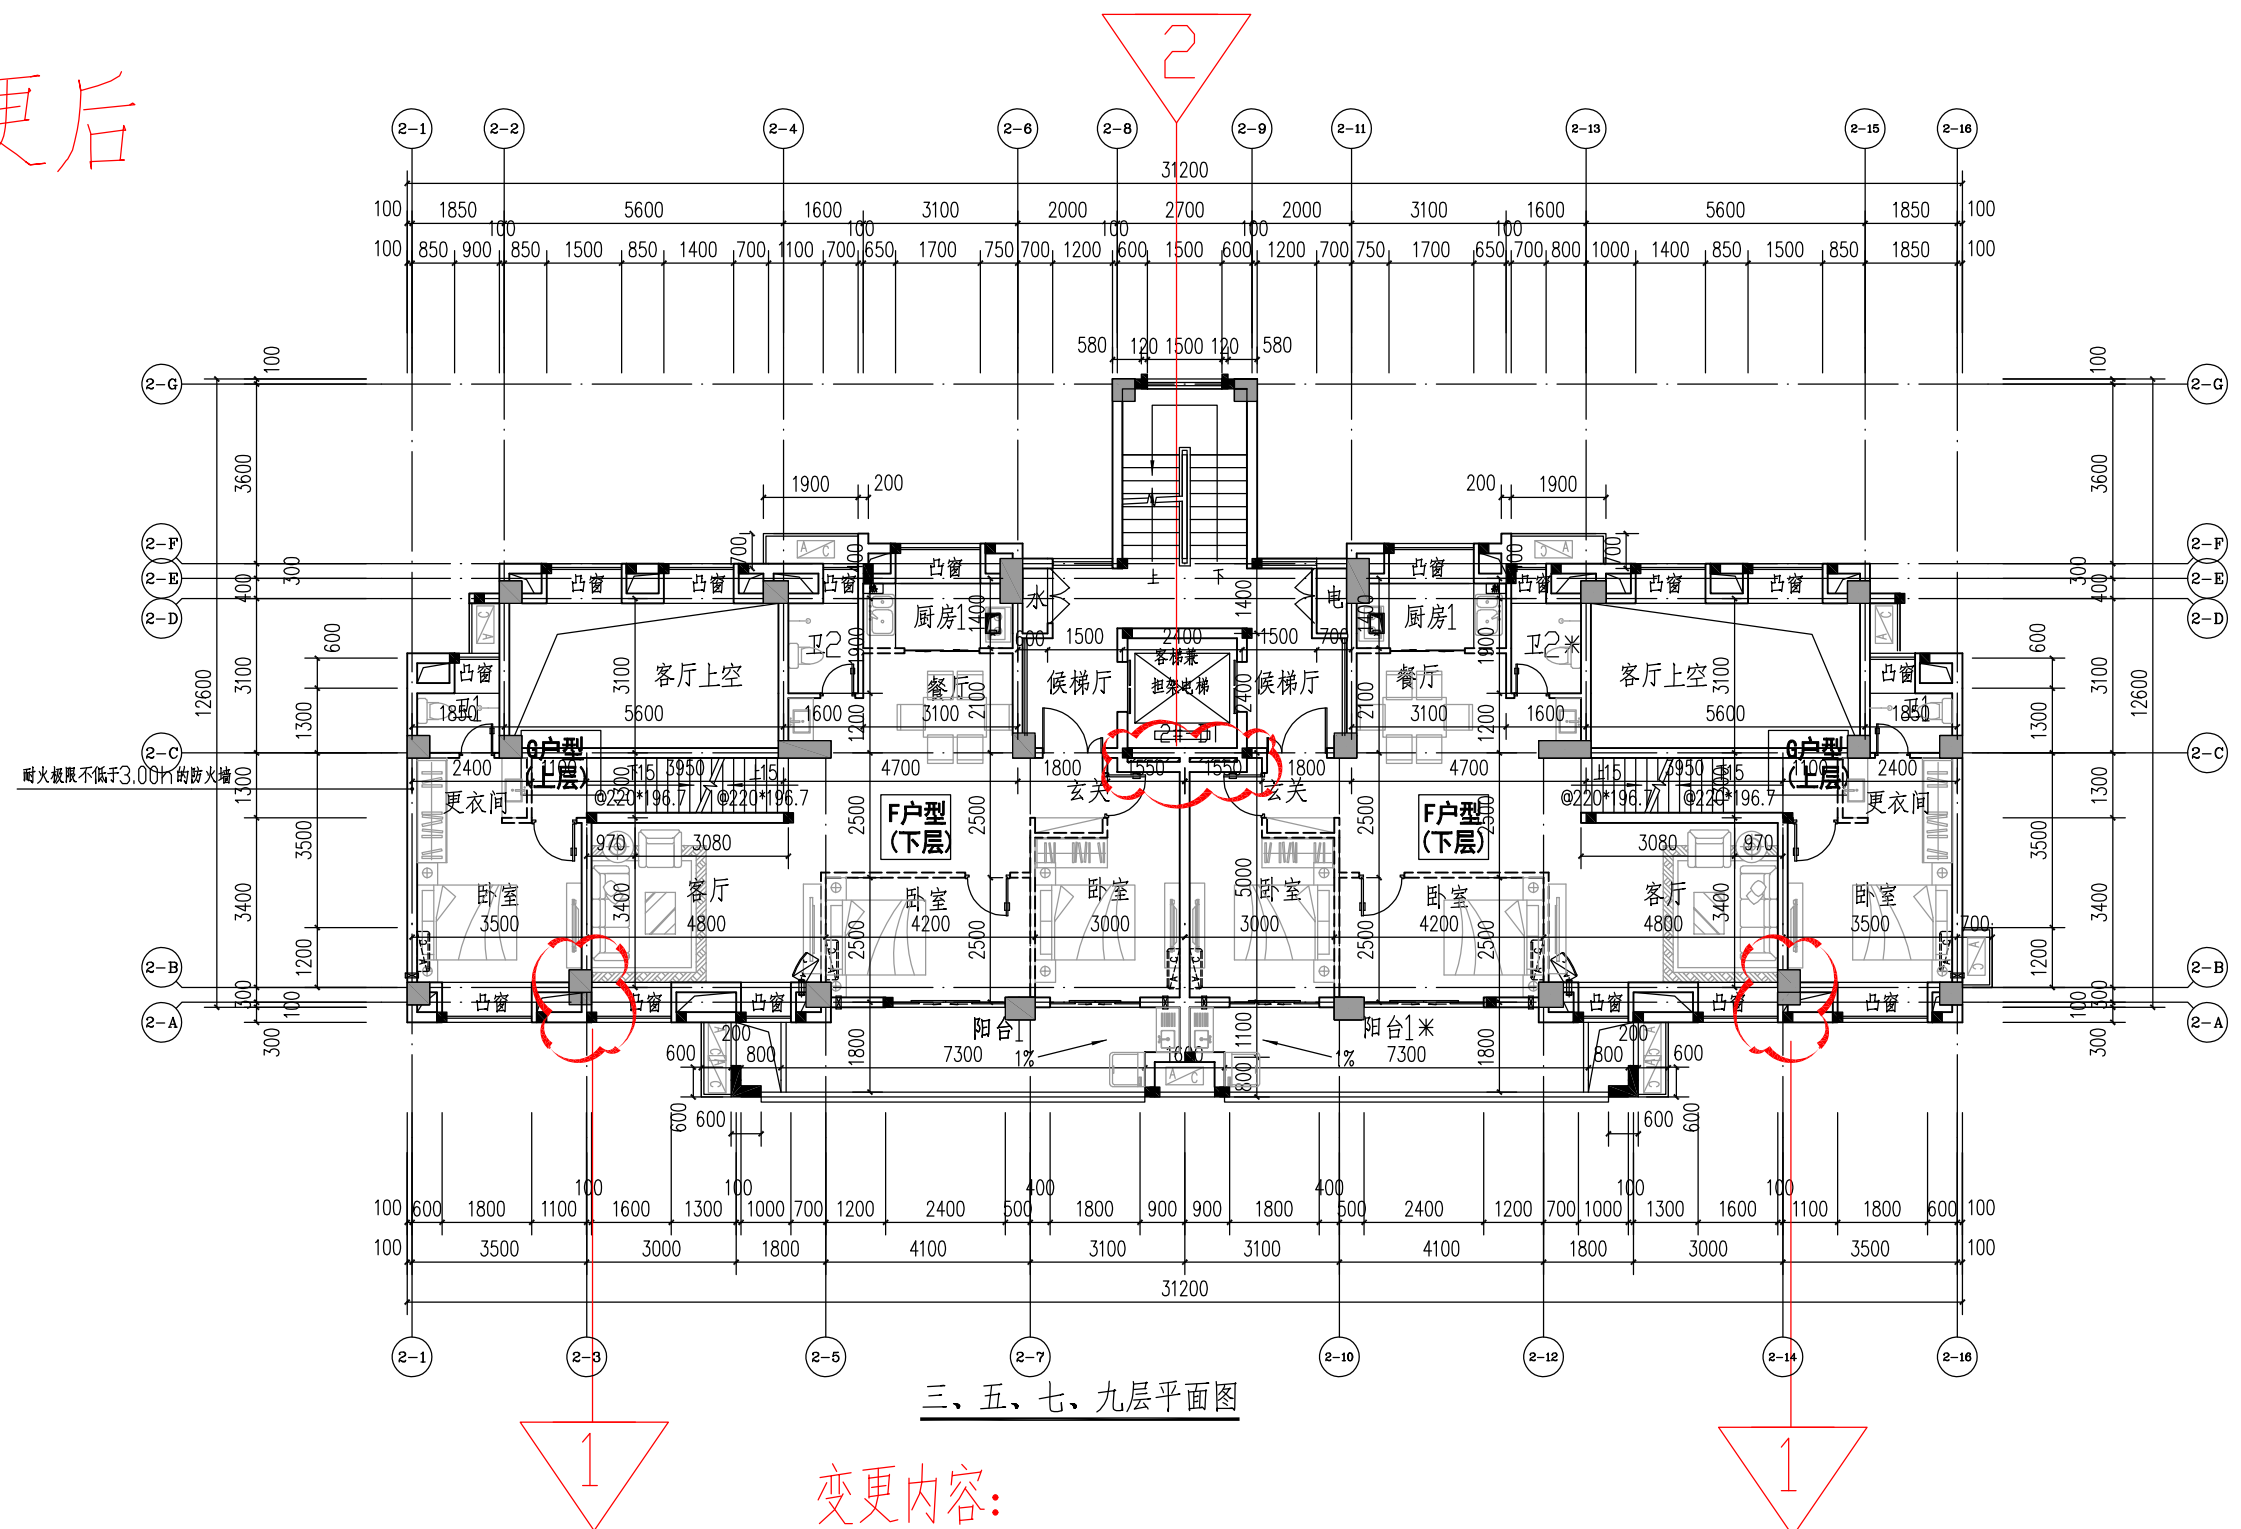


三、五、七、九层平面图

变更内容:


- 1.图中②-A轴交②-3及②-14轴柱子往②-B方向移250mm与外墙平
- 2.图中②-C轴交②-8轴、②-9轴增设一段电梯隔音墙

变更前

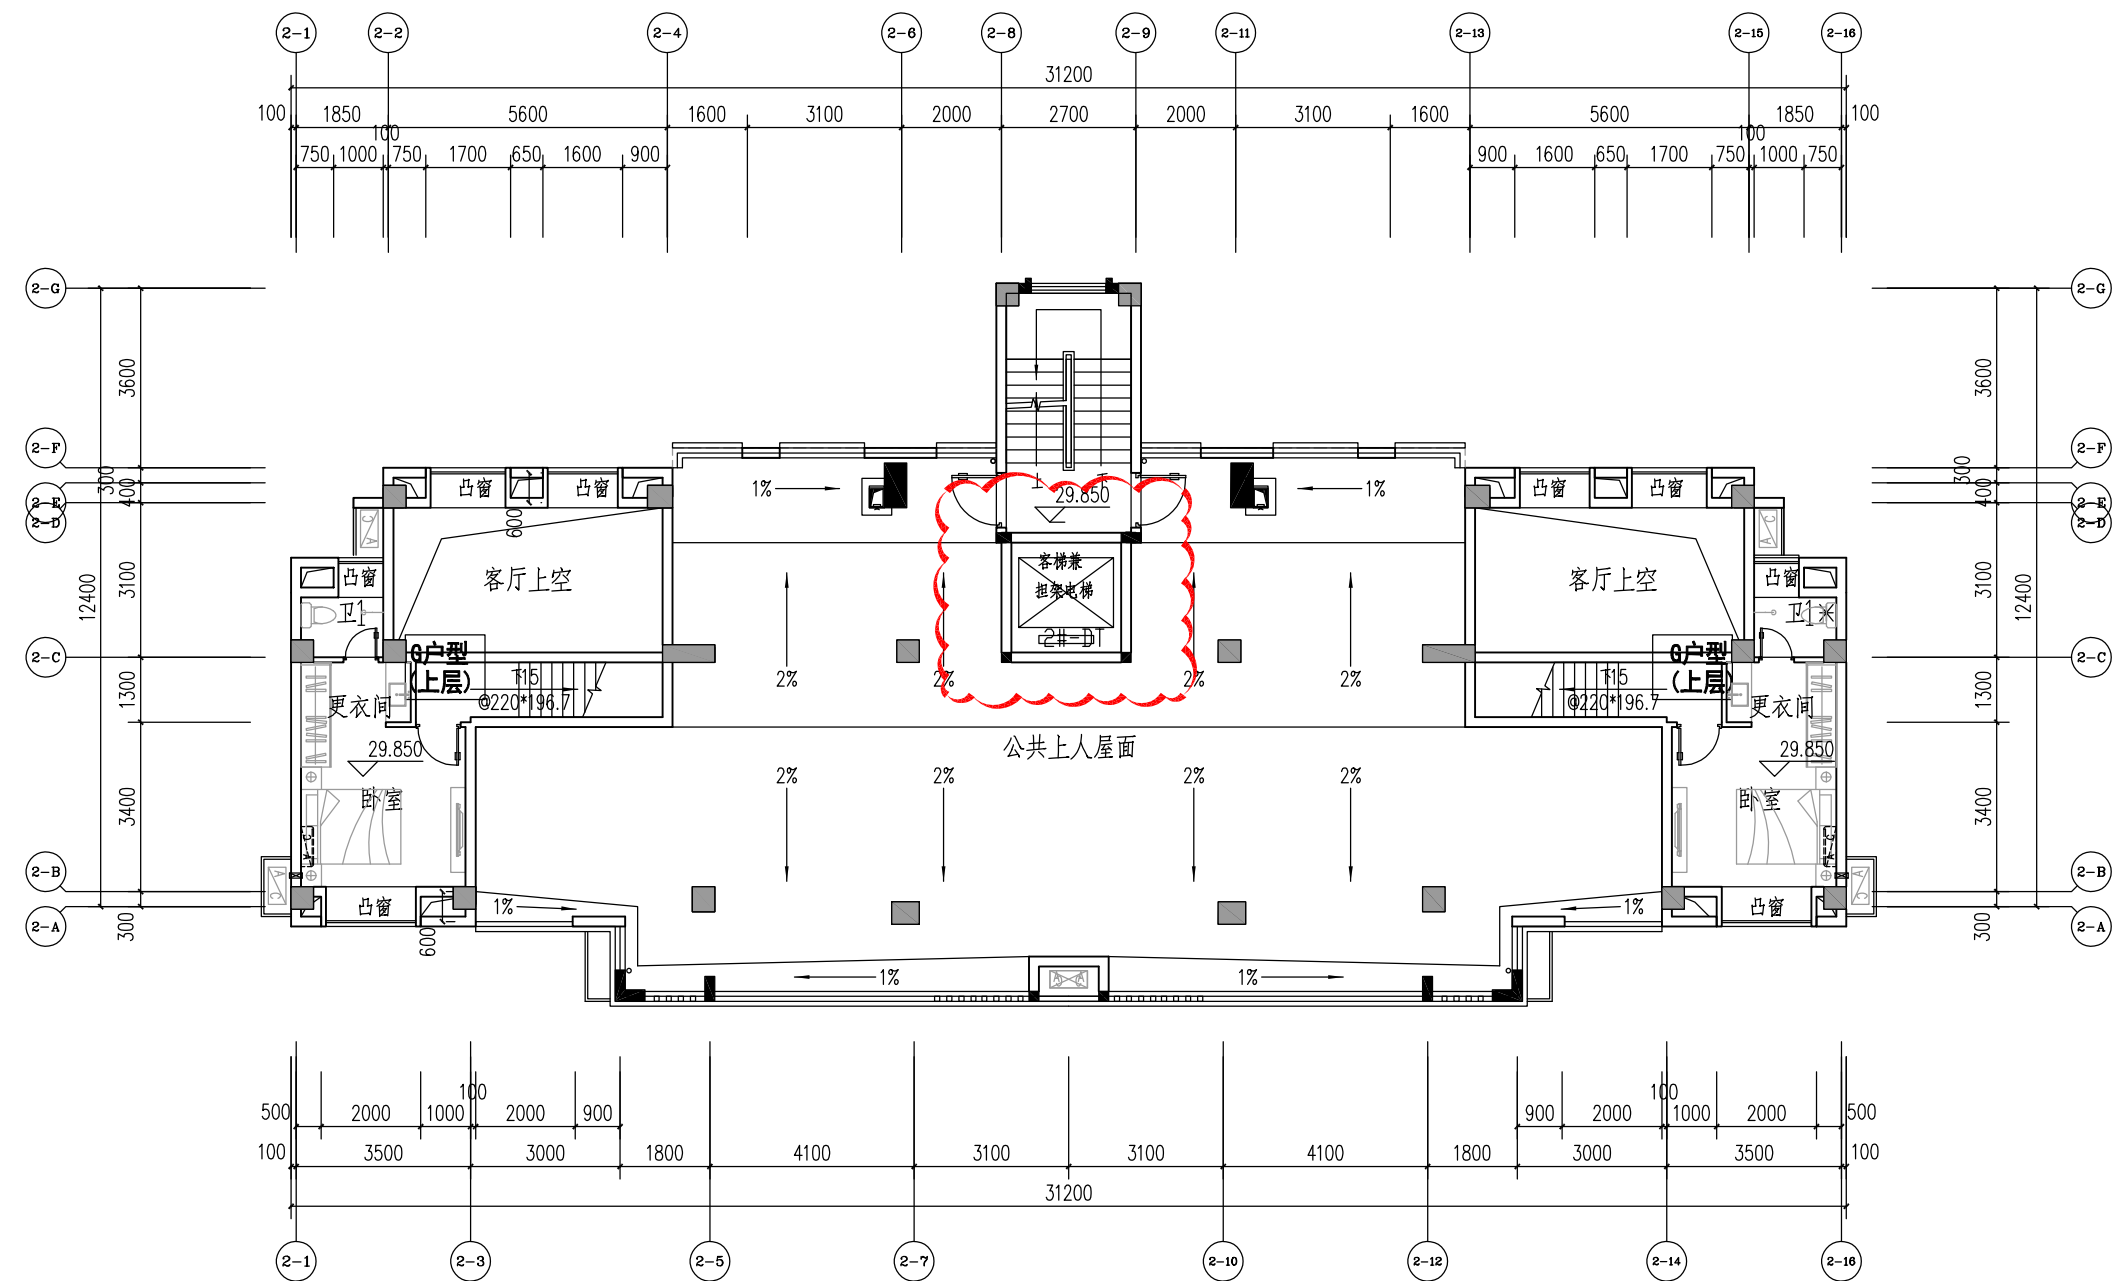

2#楼 十一层平面图

变更后

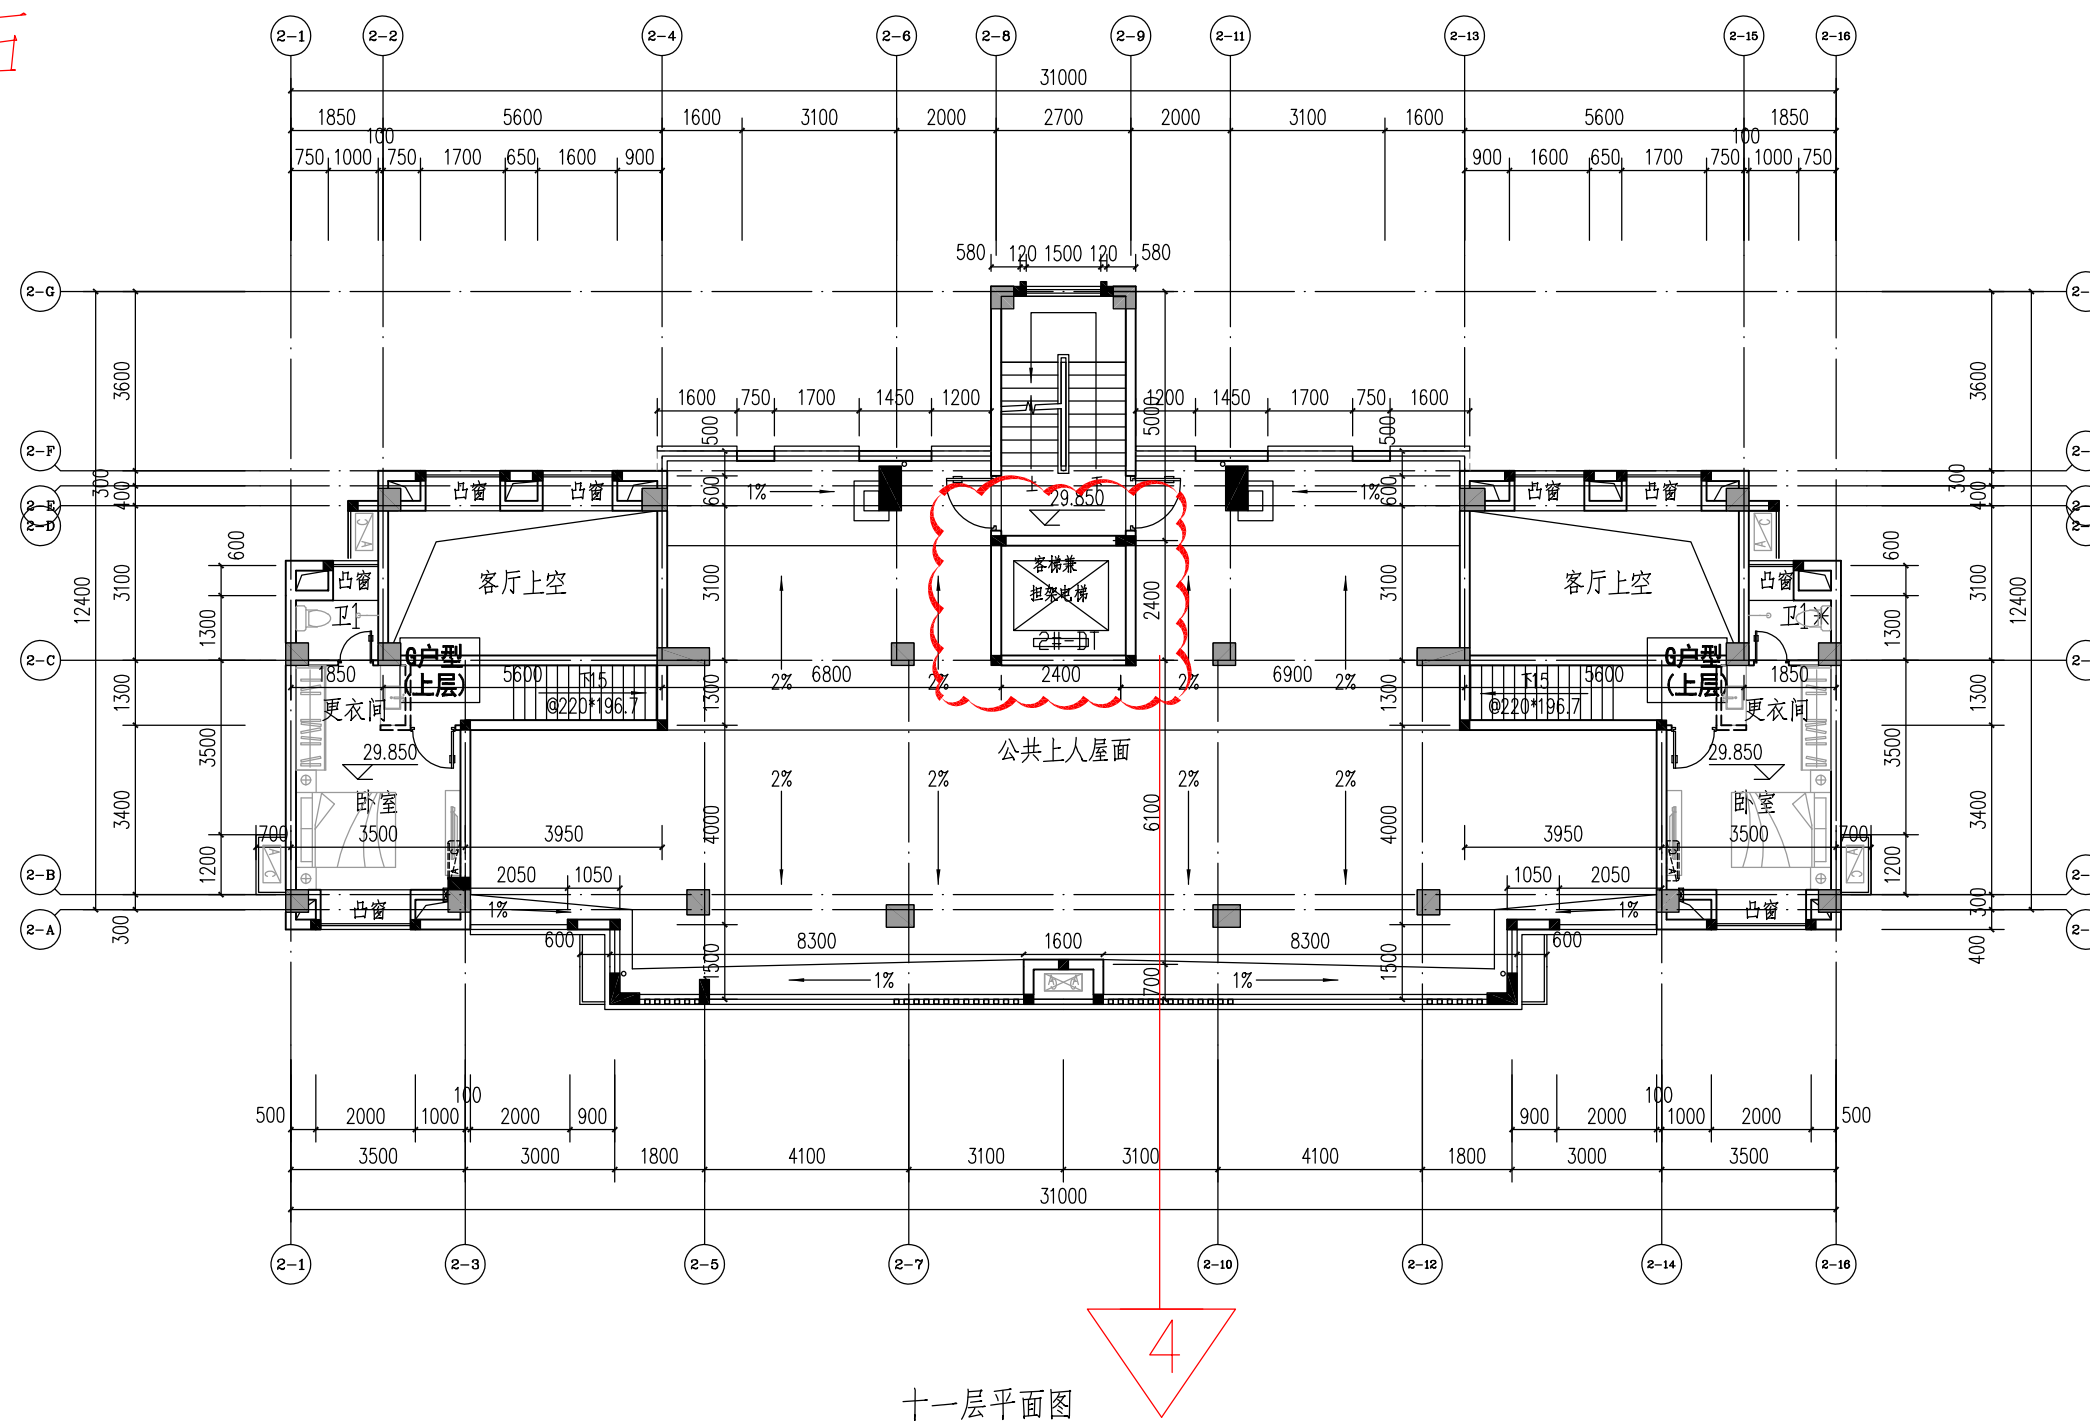


十一层平面图

变更内容:


4.图中②-8及②-9轴电梯机房外墙平

变更前

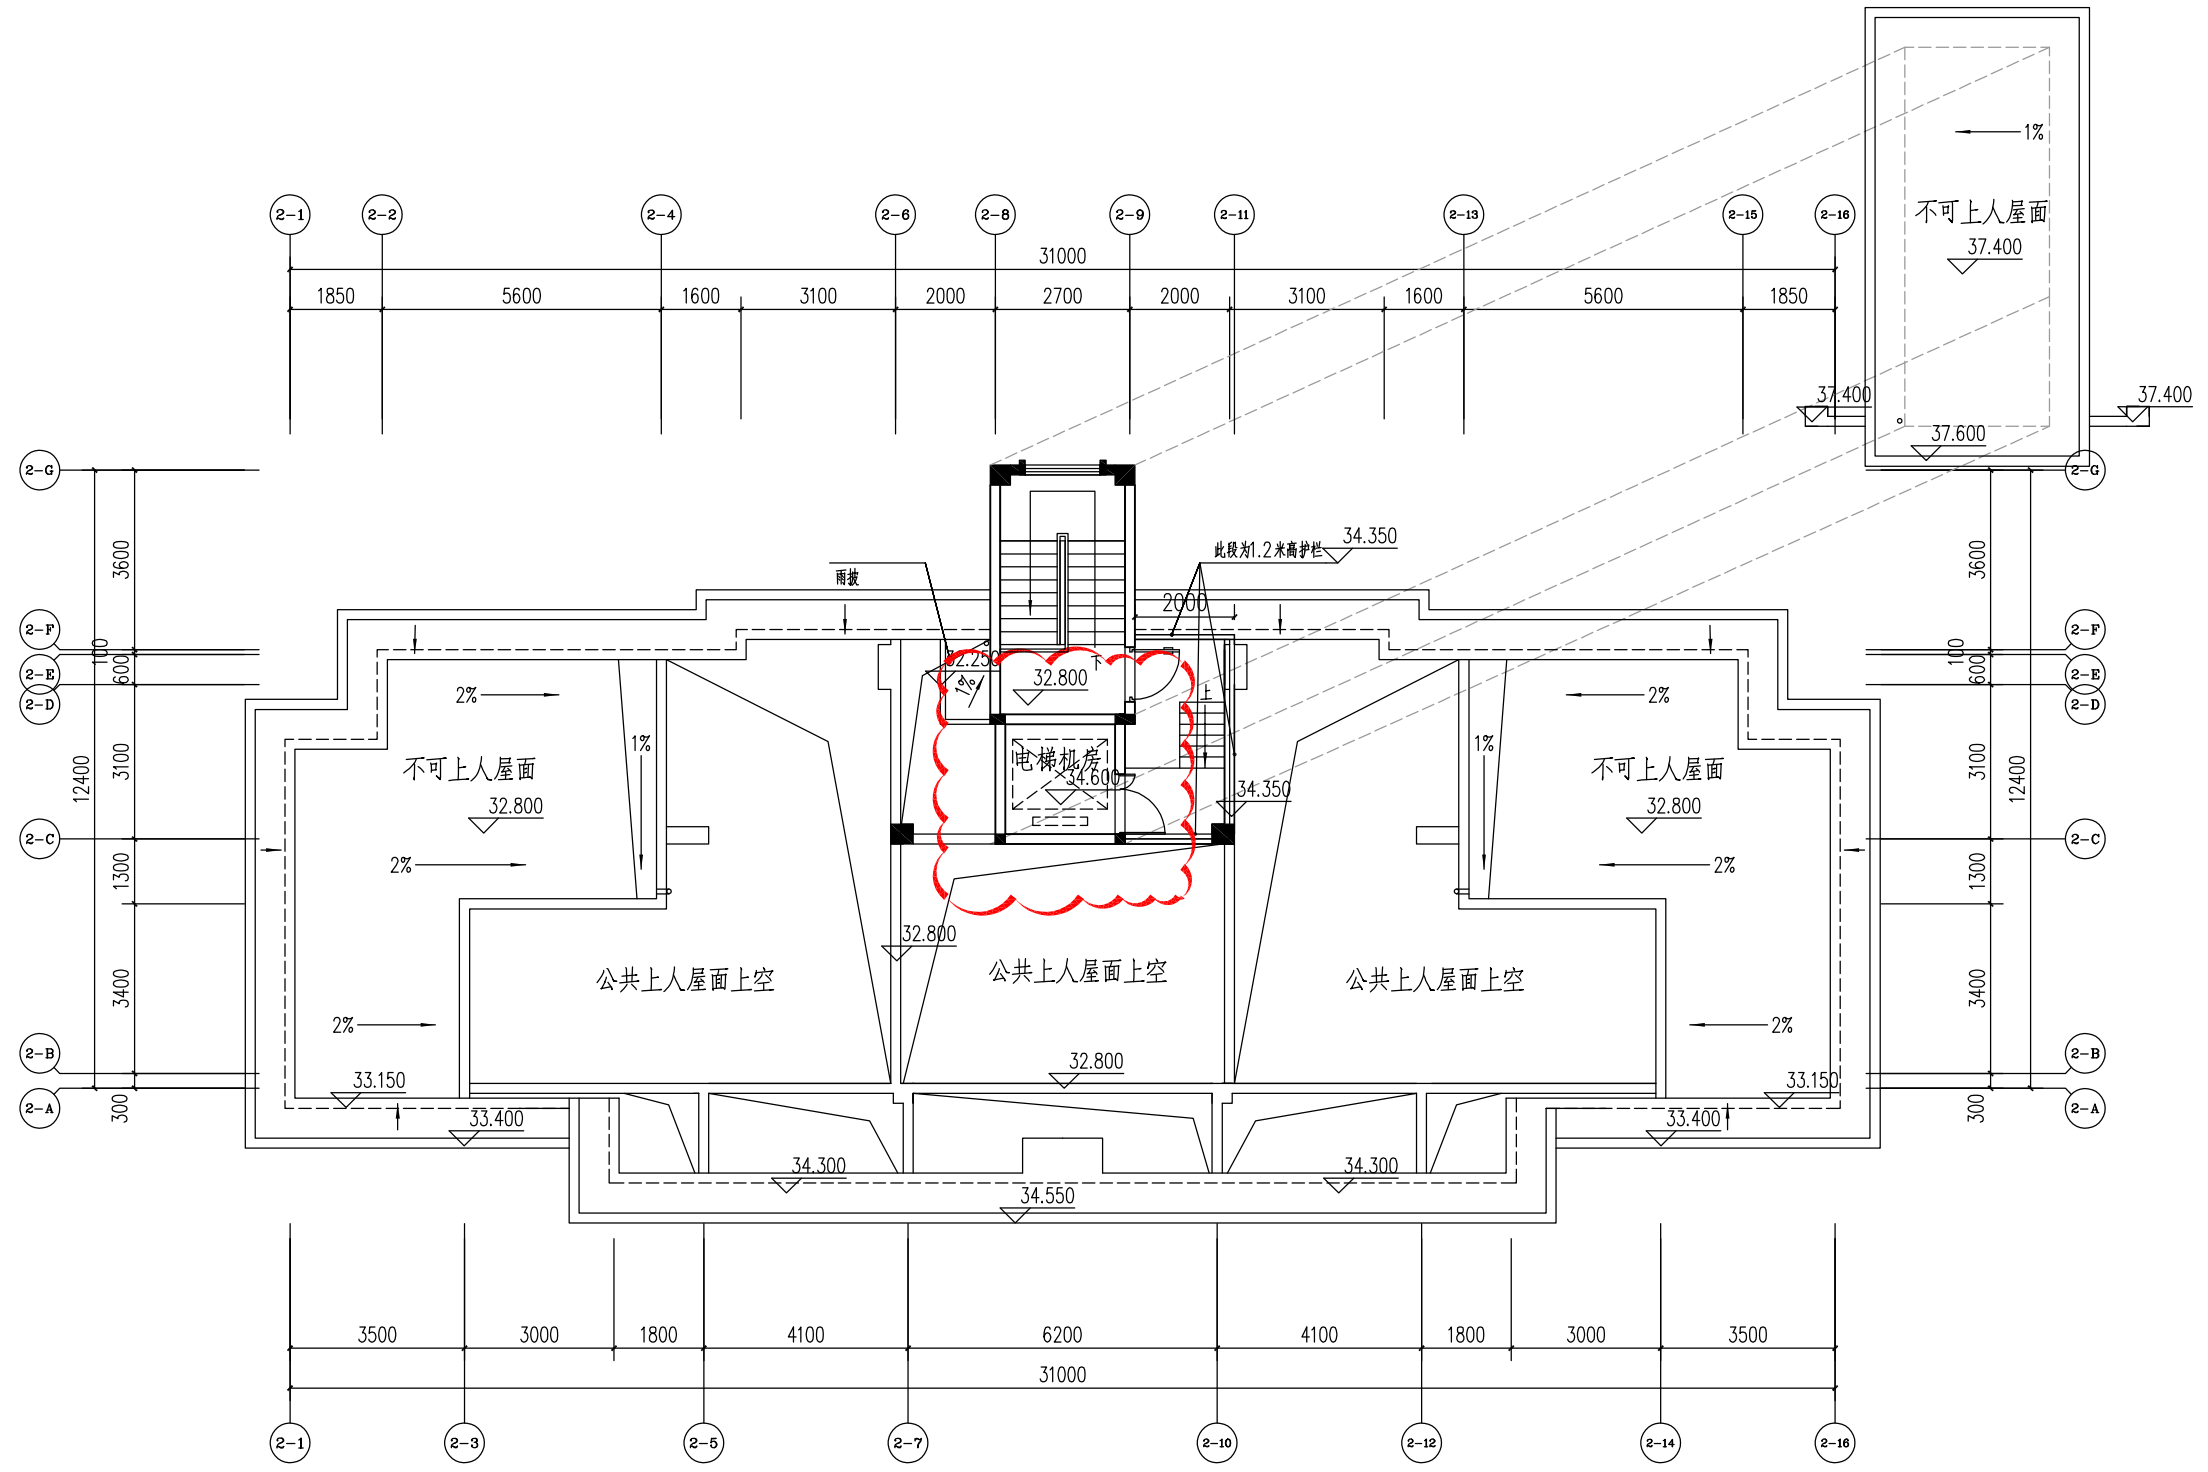

2#楼 屋面层平面图

变更后

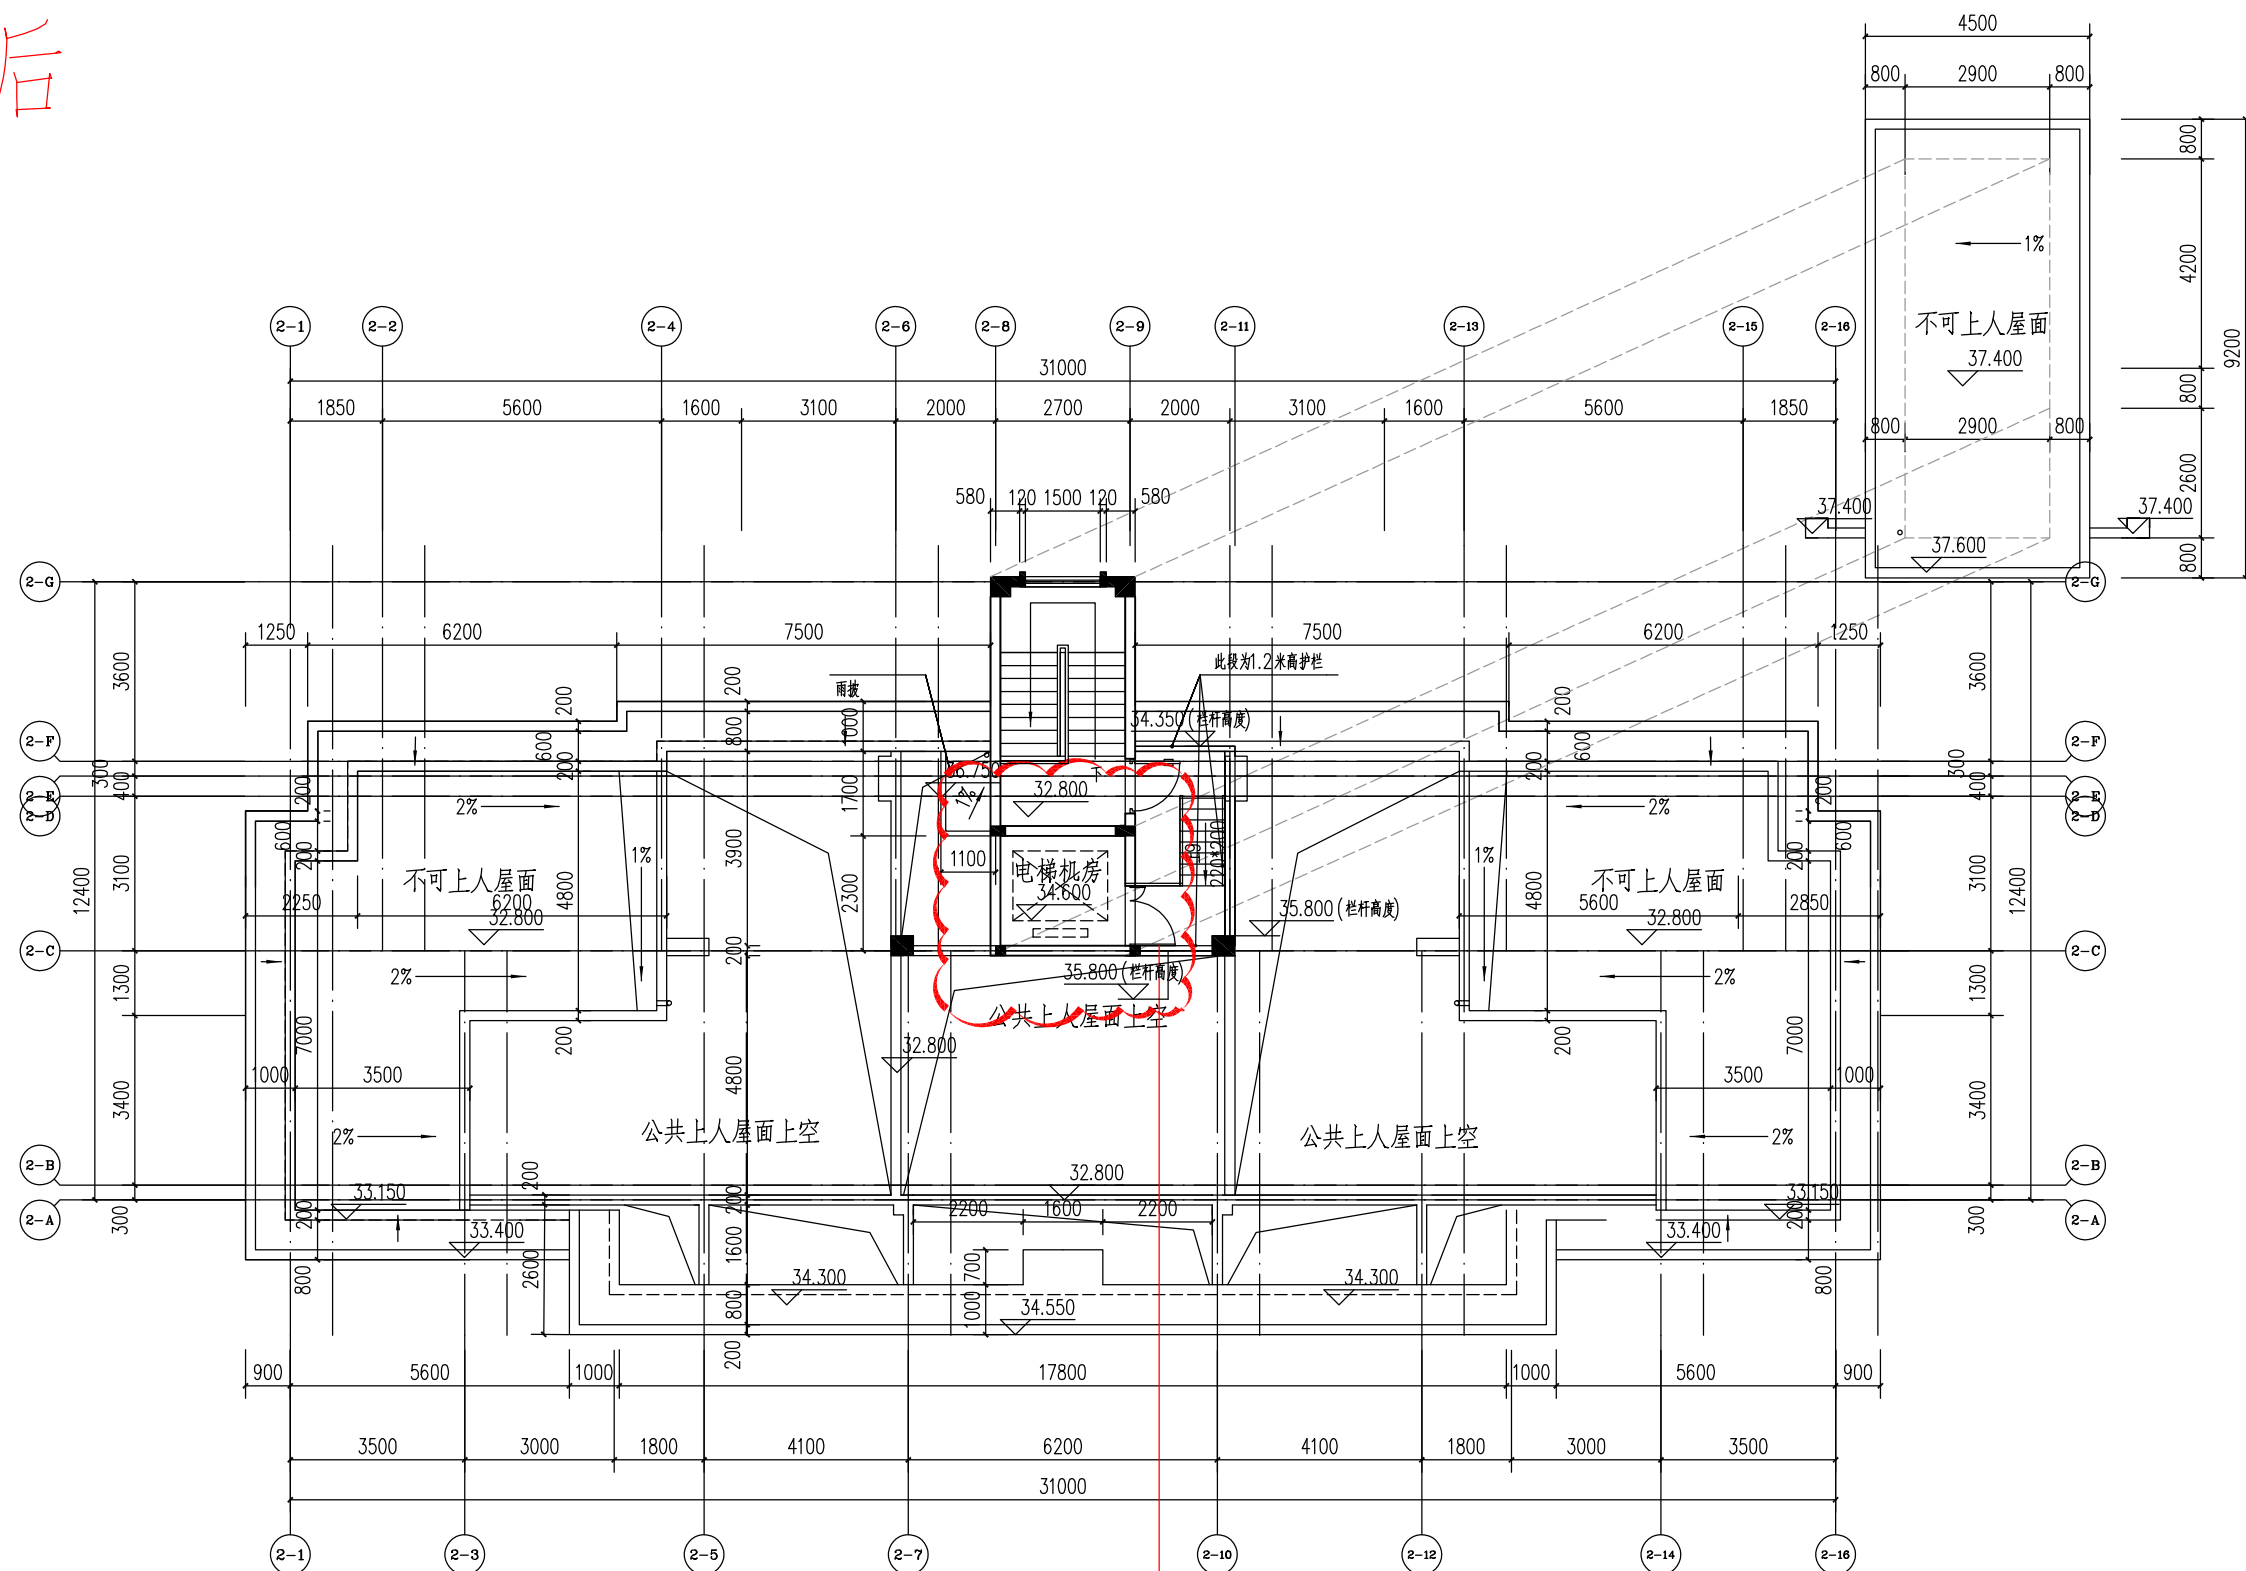

屋面层平面图

变更内容:

4.图中②-8及②-9轴电梯机房外墙平