

荆东安置房及周边附属配套工程项目（学生街）

规划建筑方案设计(方案变更)

三明 福建




福建一建集团有限公司

2020.10


 福建一建集团有限公司 FuJian First Construction Group Co., Ltd.		福建一建集团有限公司 设计资质： 甲级 证书编号： A135004919		建设单位		三明市三元区城市建设投资有限责任公司	
				工程名称		荆东安置房及周边附属配套工程项目（学生街）	
方案设计				专业负责			
建筑设计		王海帆、方毓荣、罗裘华、洪烨、谢雨歆		建筑专业负责		周成才	
结构设计		谢煜辉		结构专业负责		王锦星	
电气设计		李镇鸿		电气专业负责		李镇鸿	
给排水设计		郑伯辉		给排水专业负责		郑伯辉	
暖通设计		元平华		暖通专业负责		林忠东	
图纸专用章：				建筑师注册章：			

变更前

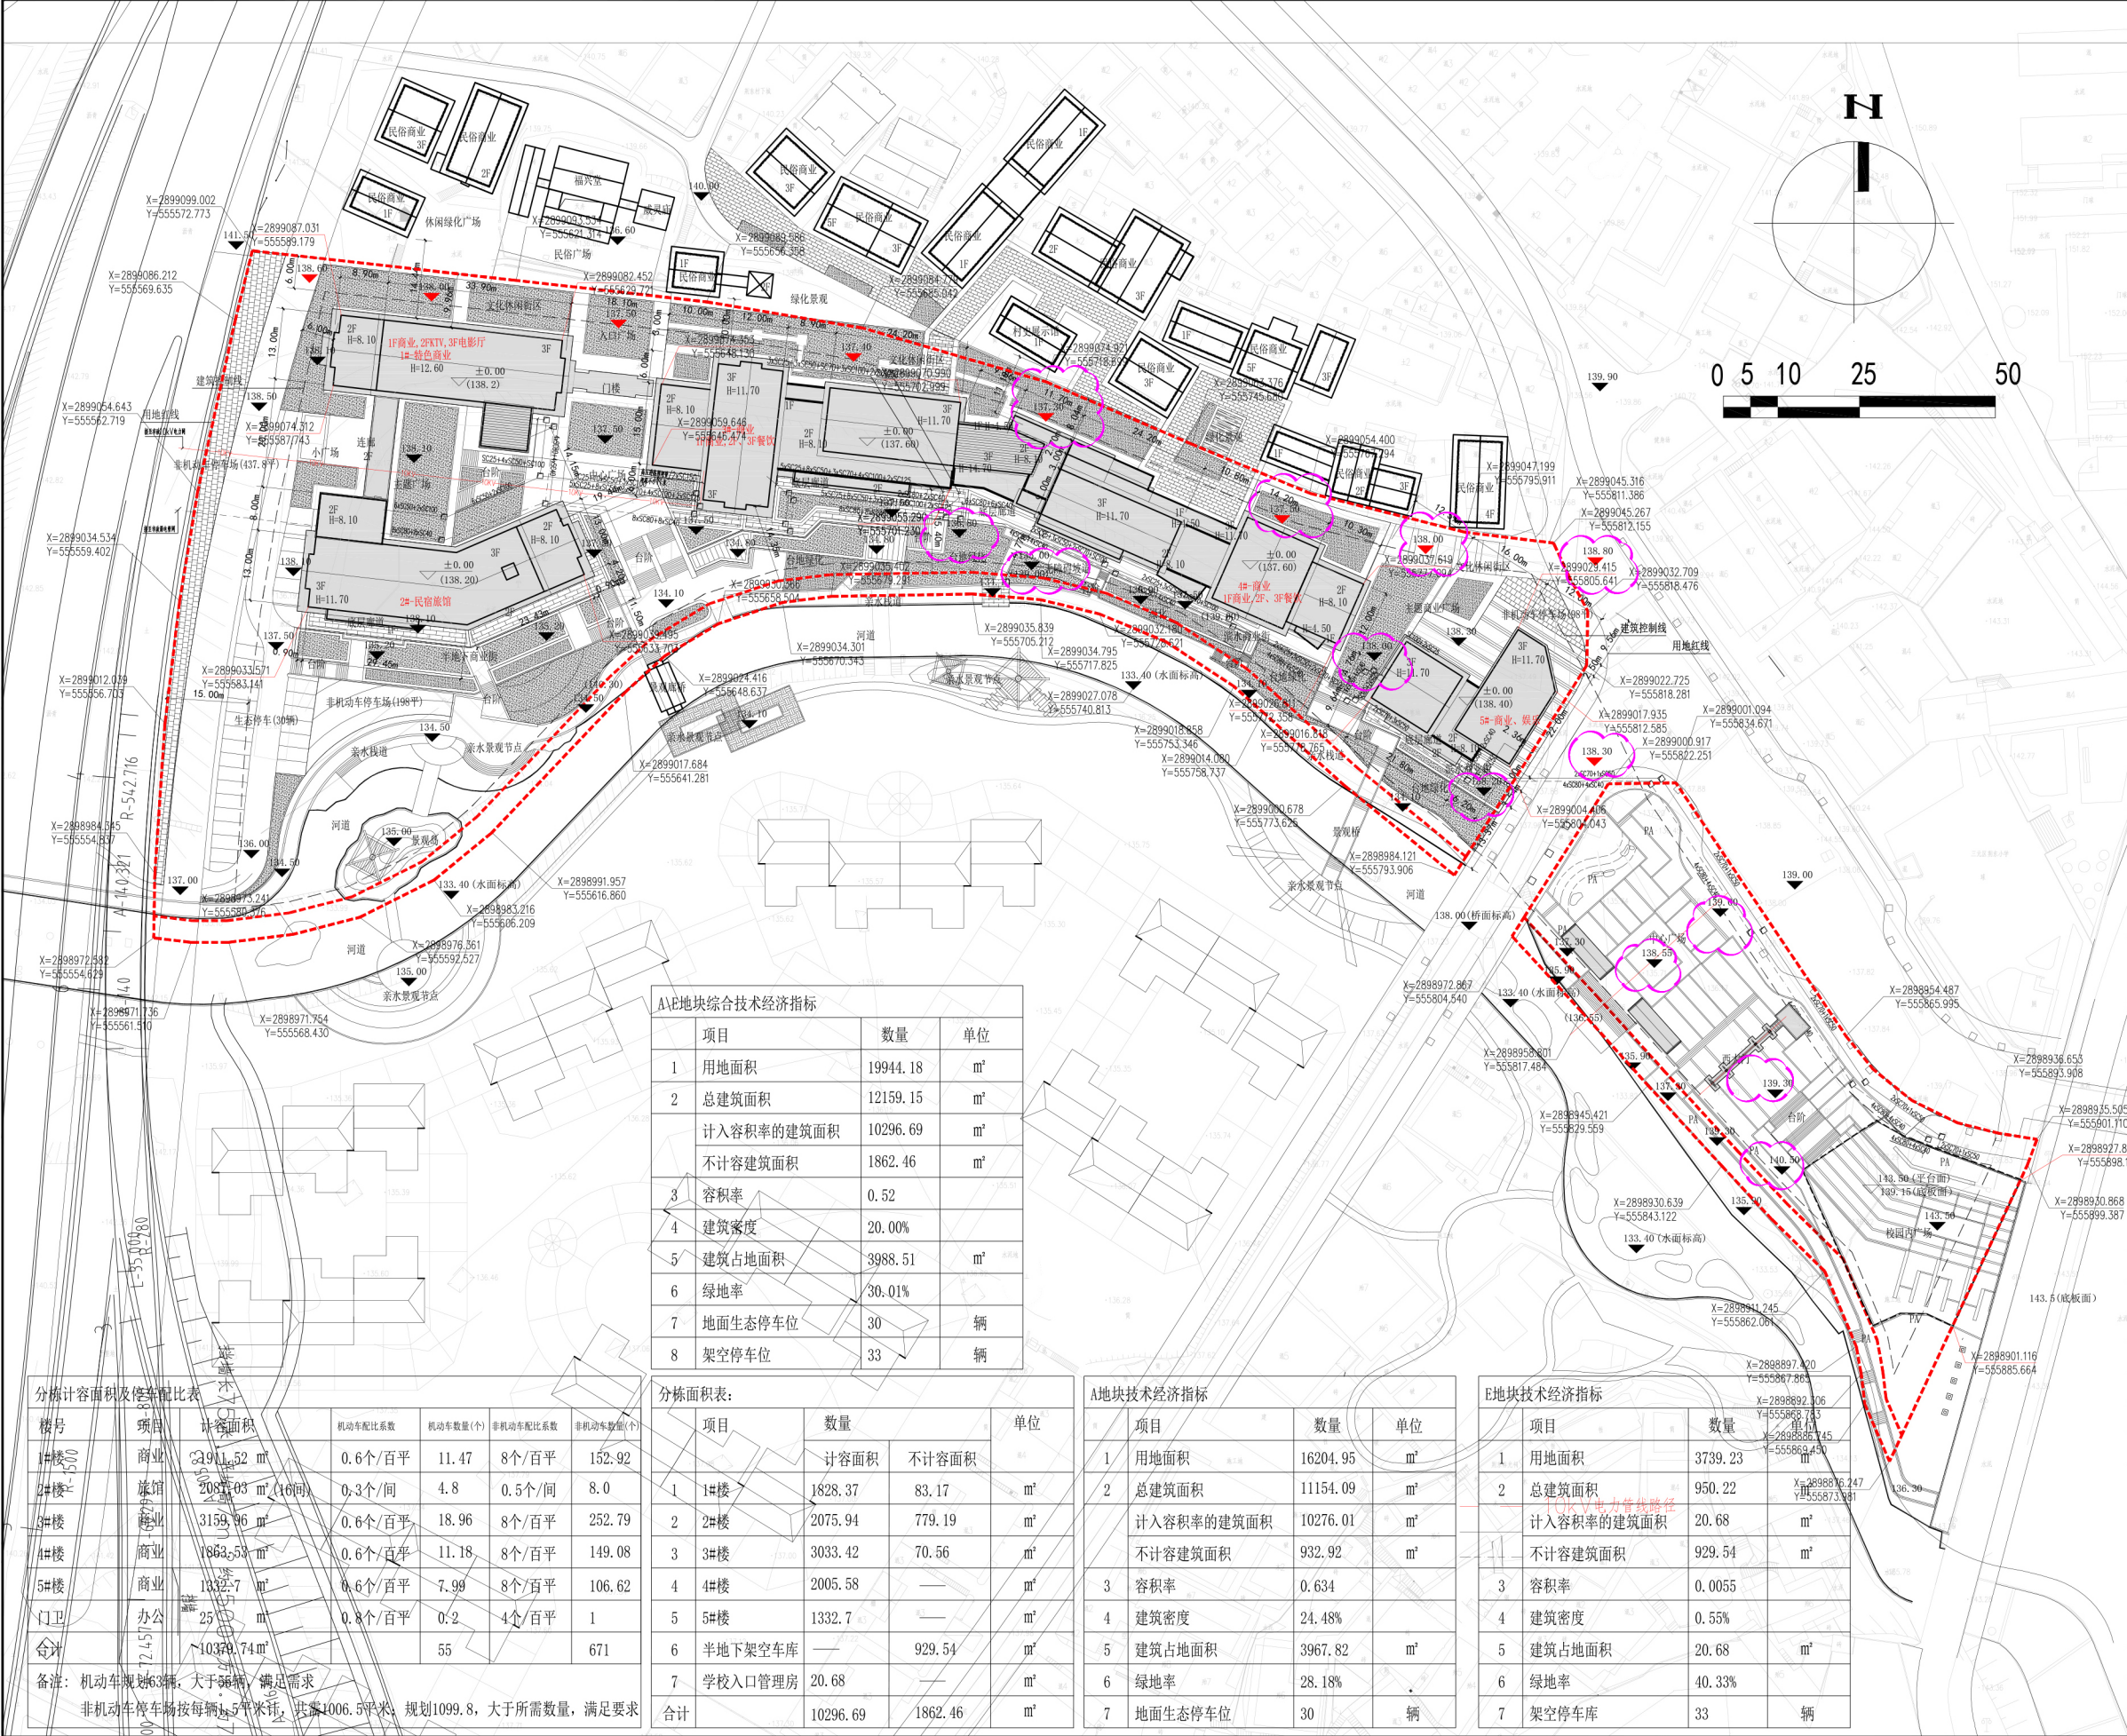


变更后

1、室外标高局部调整

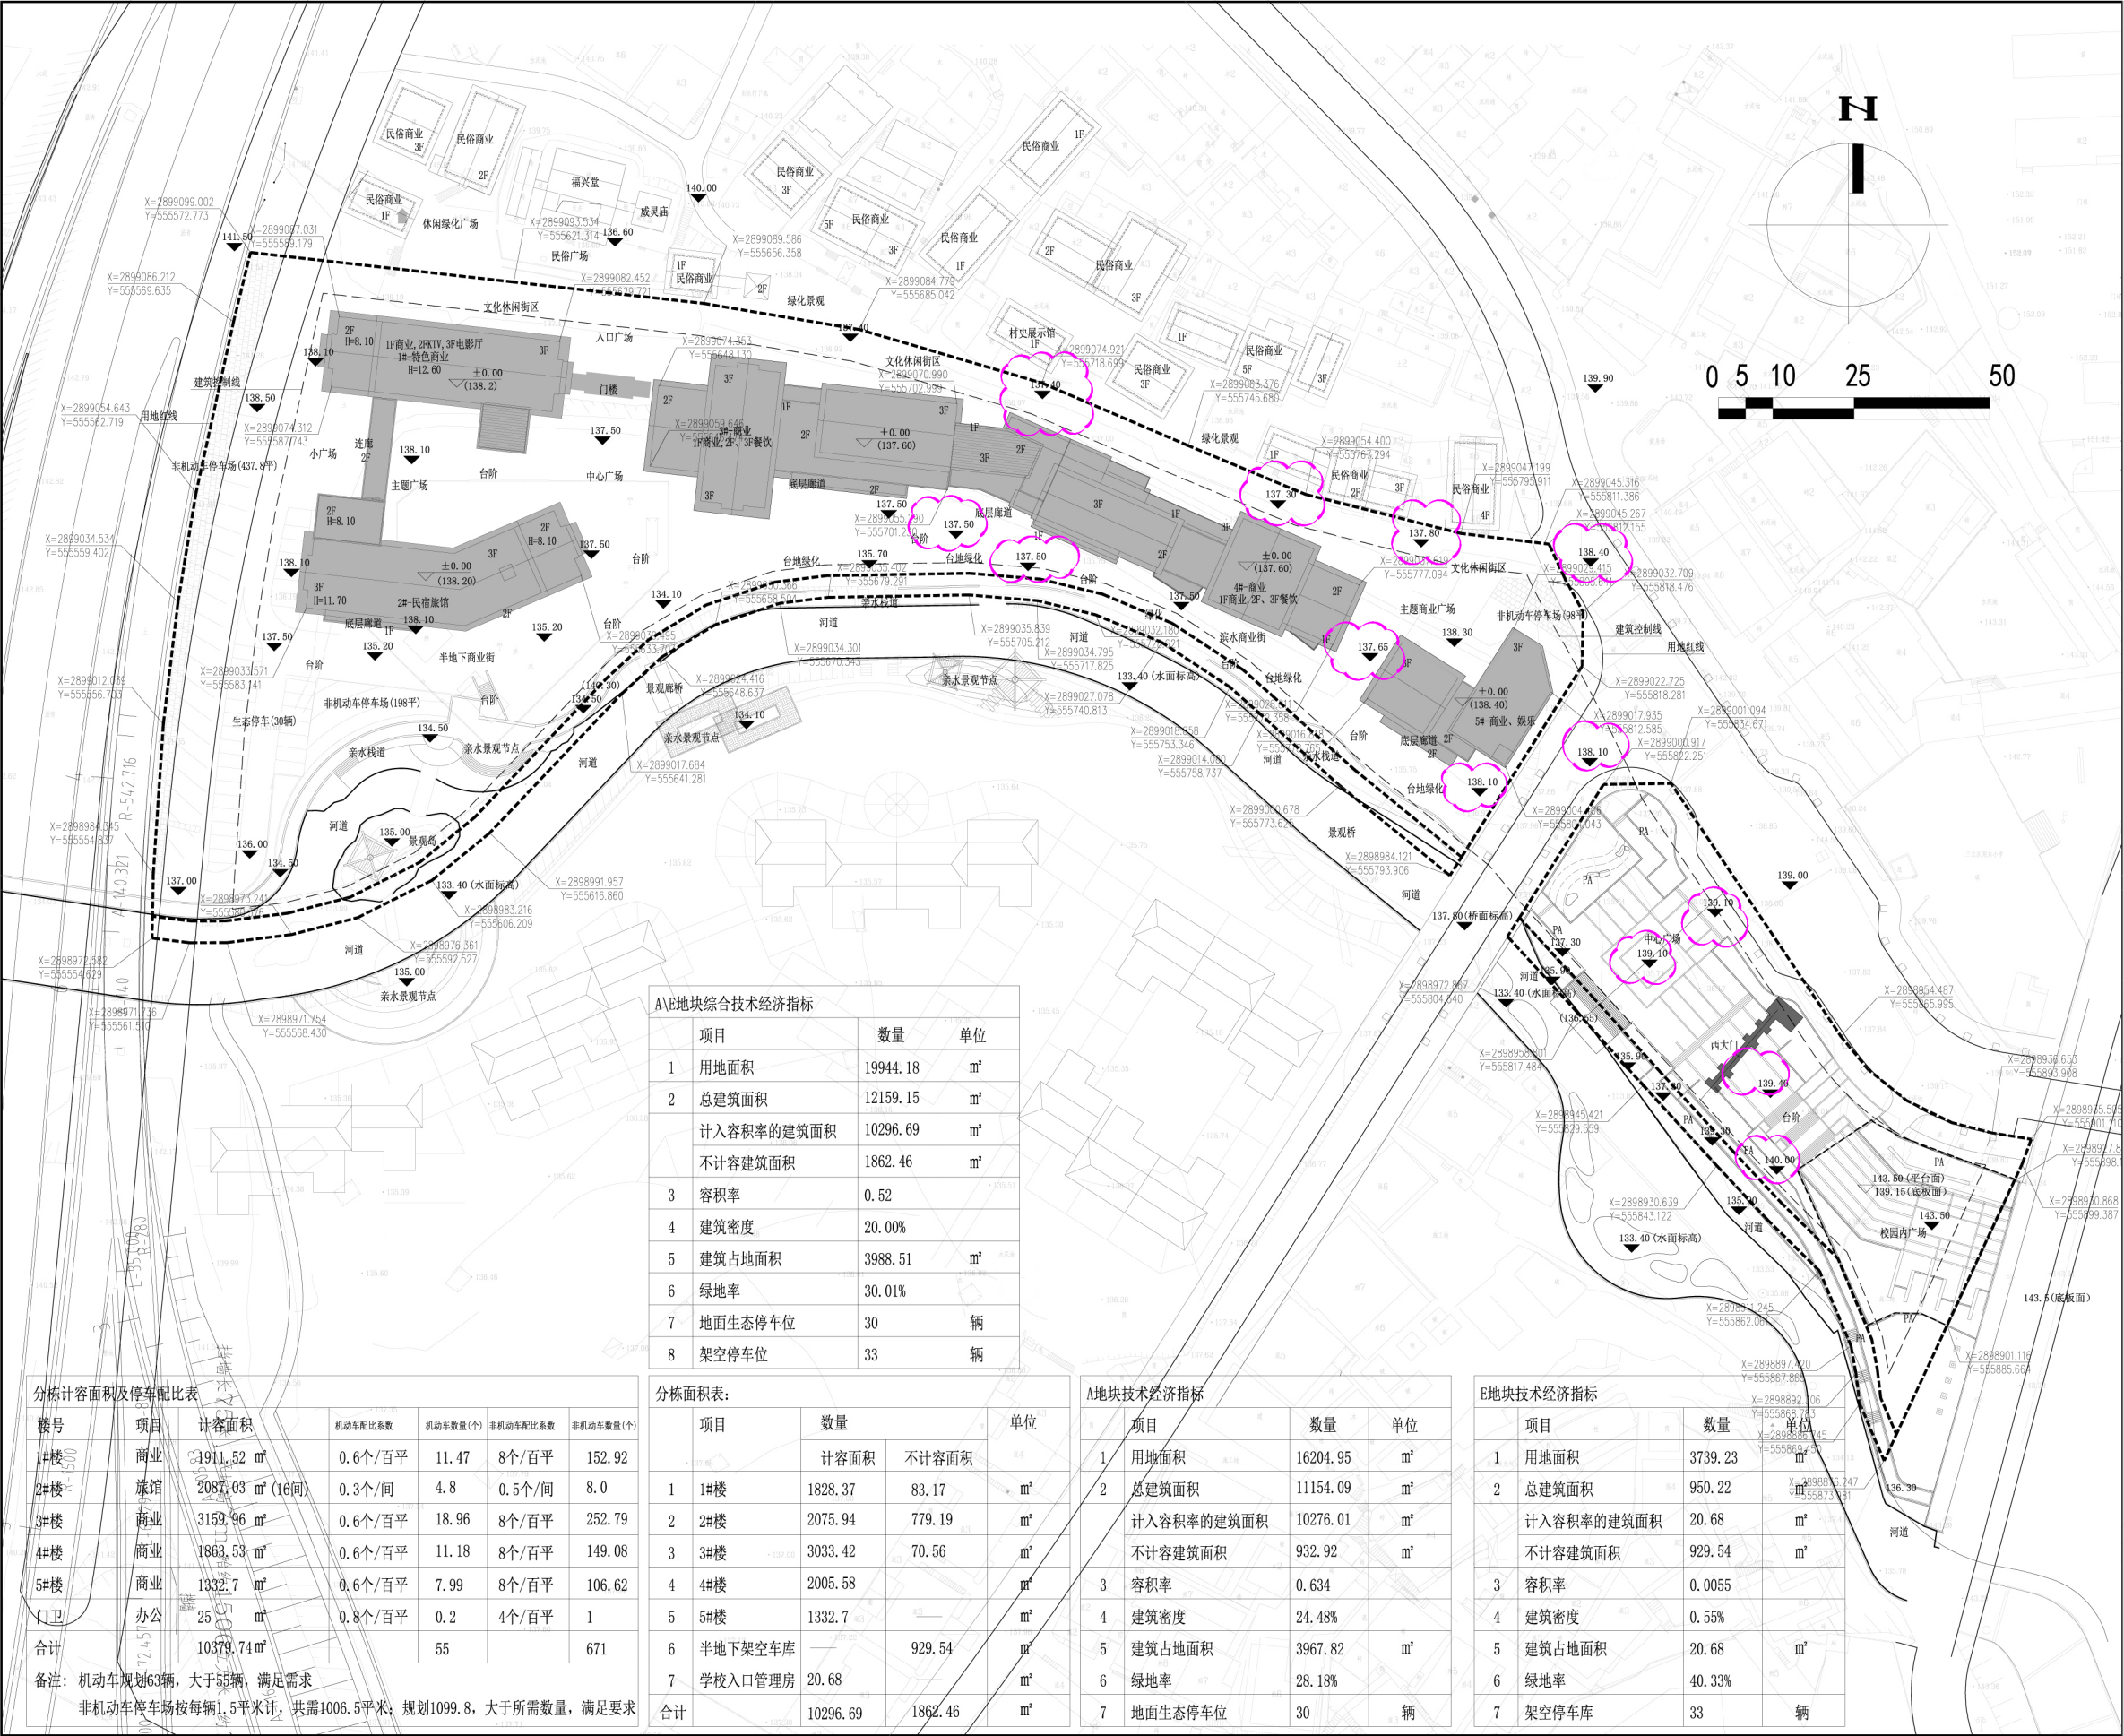


变更前

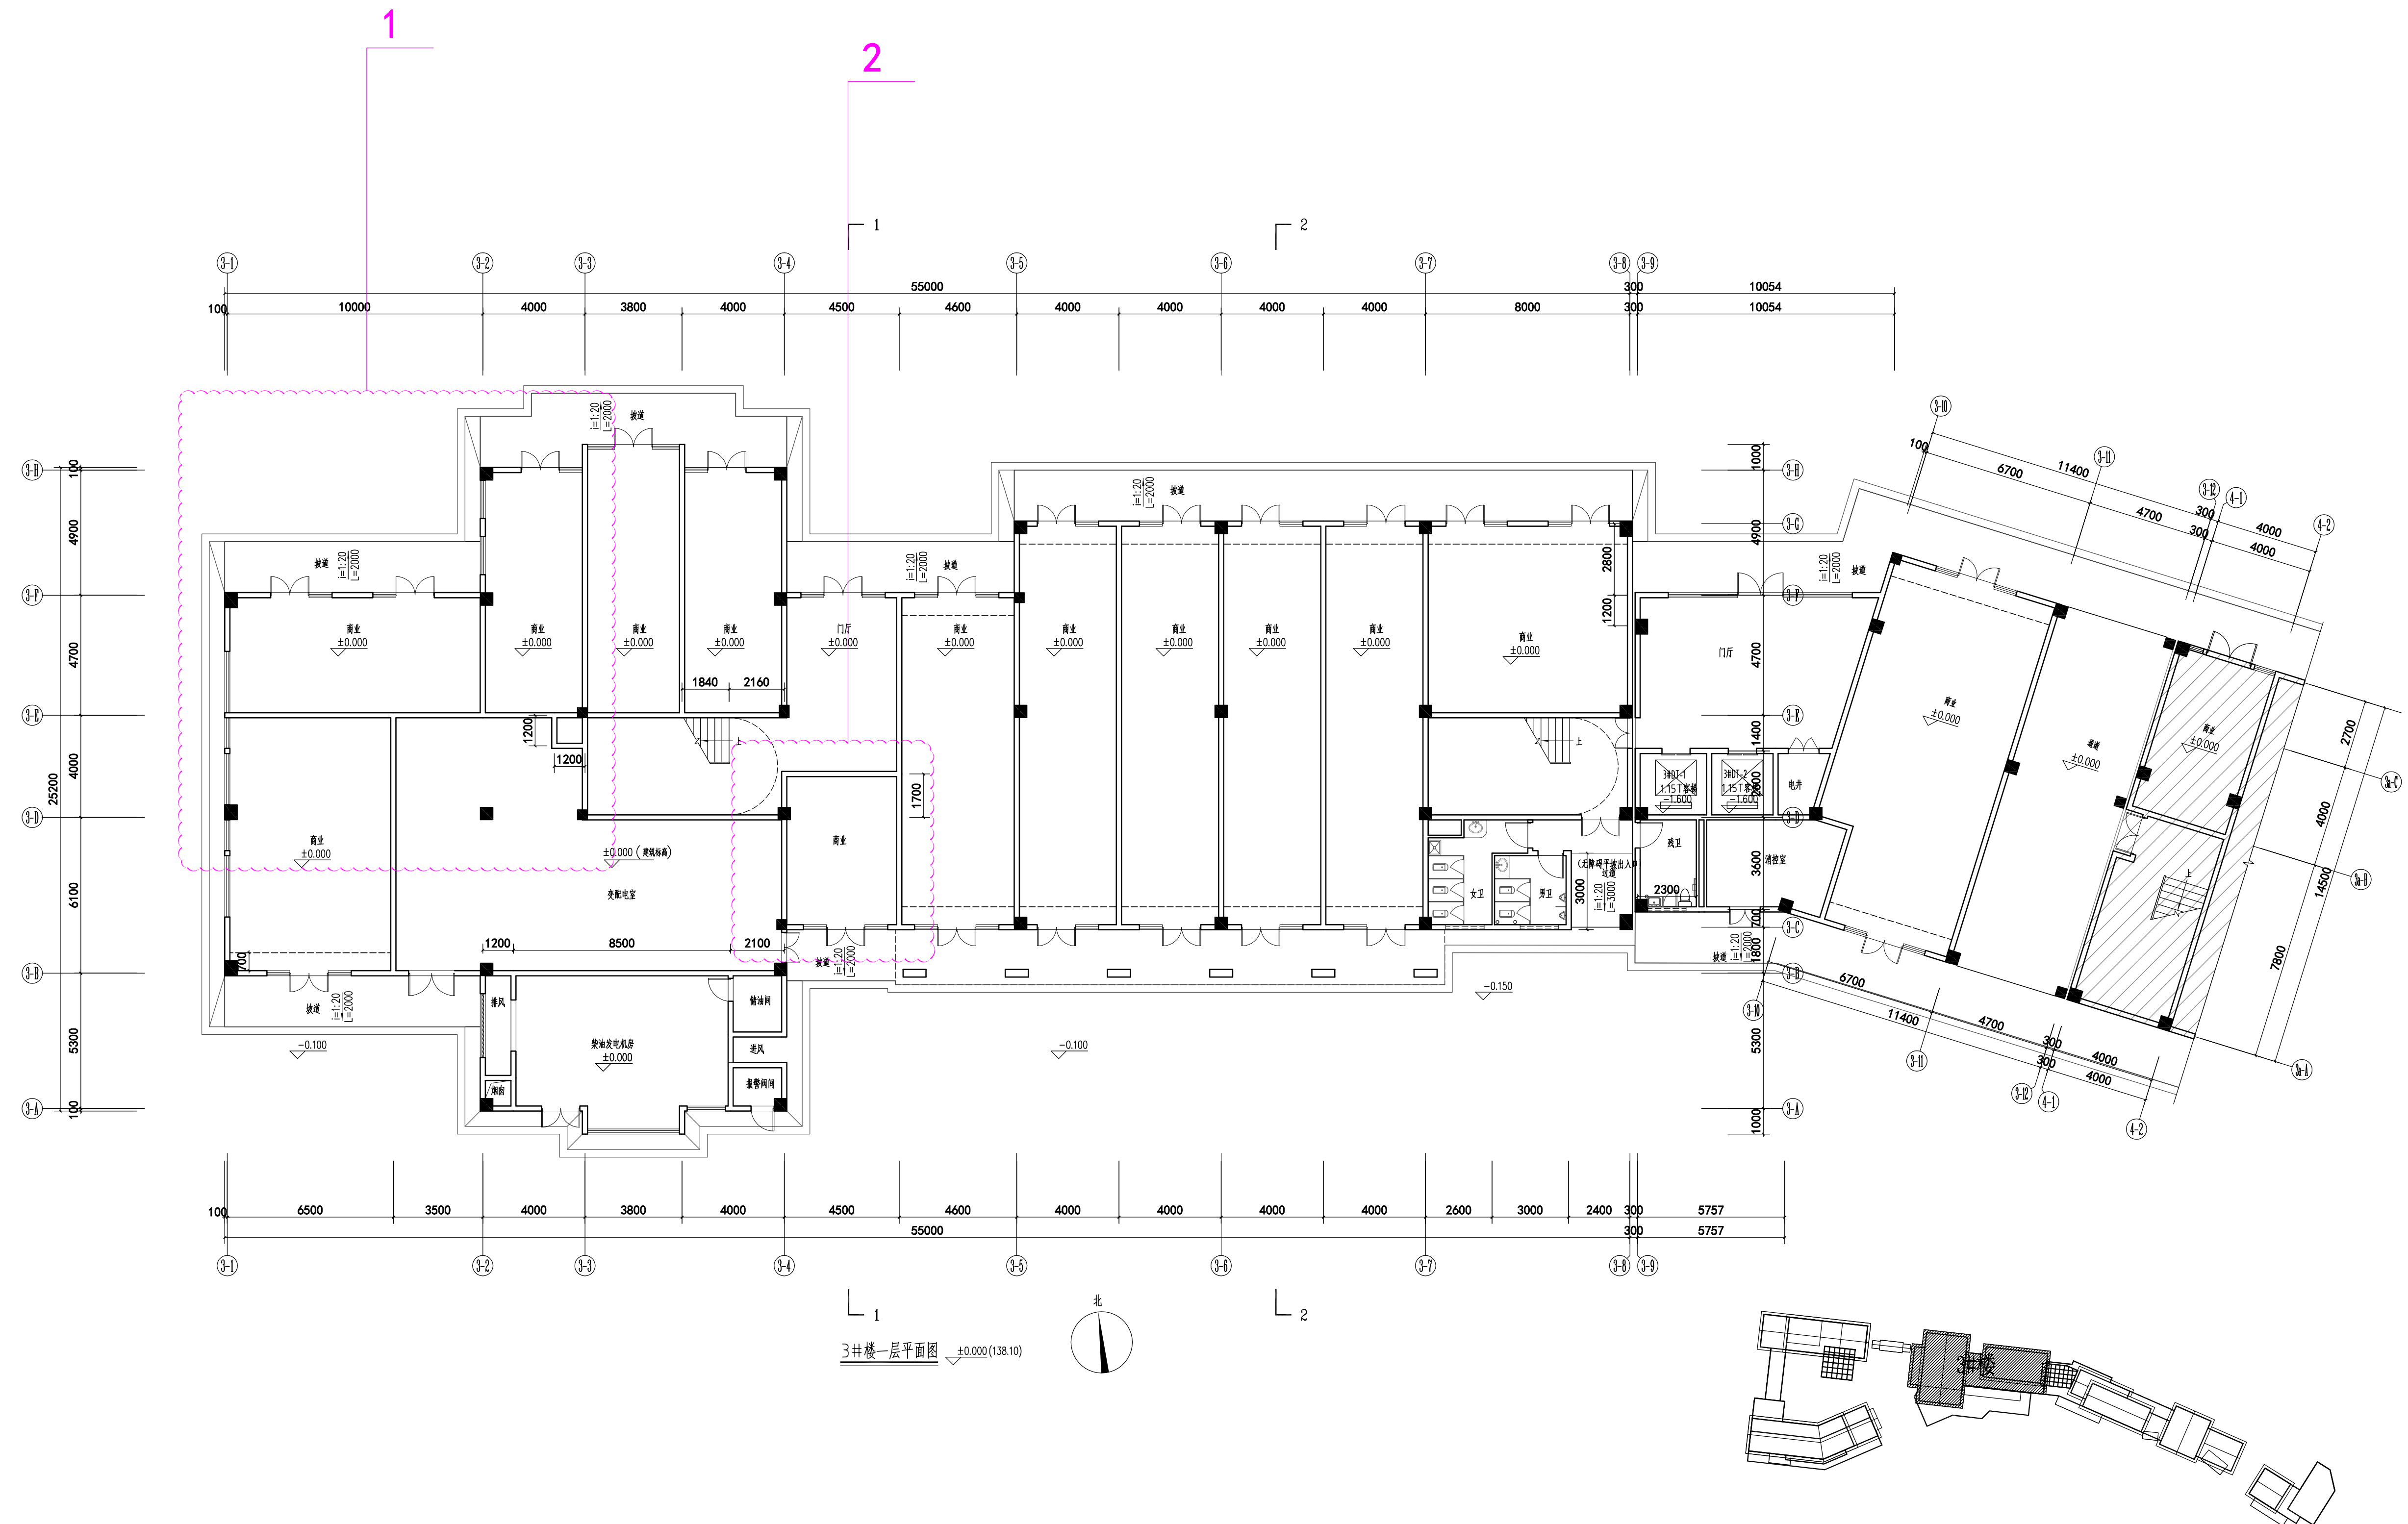

设计单位	福建一建集团有限公司	工程名称	荆东安置房及周边附属配套工程项目（学生街）	图 名	3#楼一层平面图	图 别	方 案
						日 期	2020. 10


变更后

1. 商业隔间调整
2. 门厅及商业隔墙取消，原设计商业部分变更为门厅

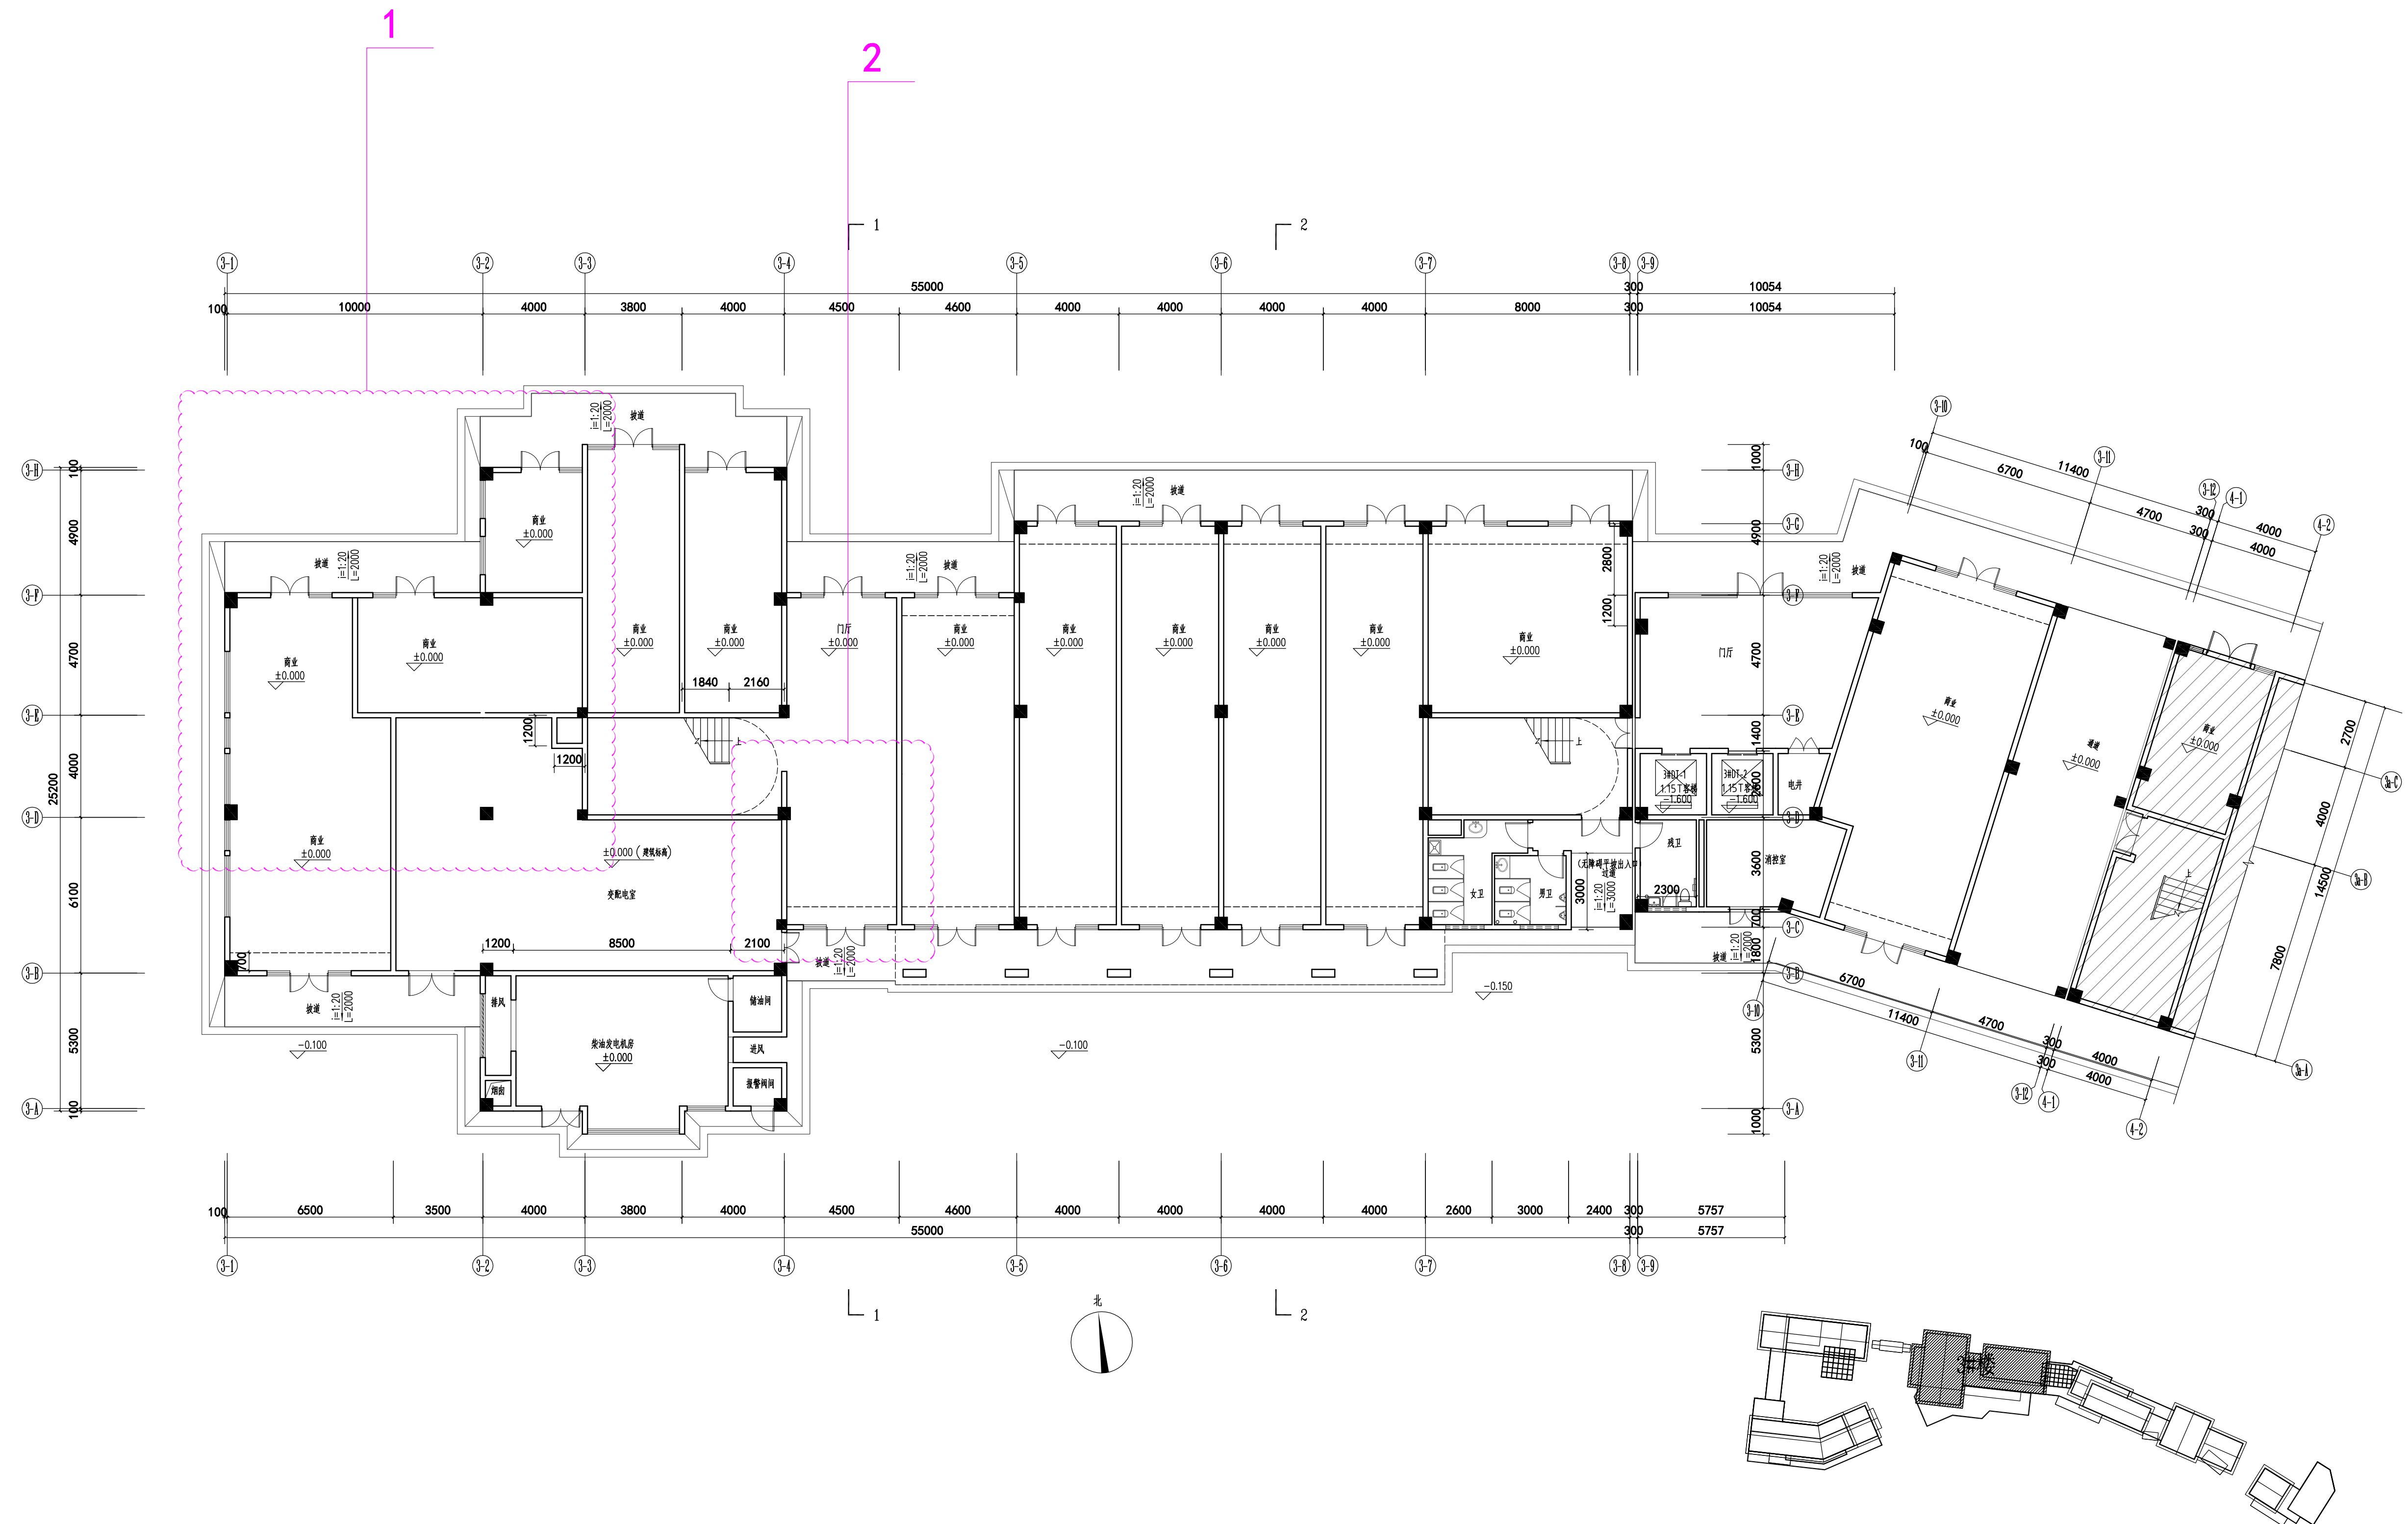

设计单位	福建一建集团有限公司	工程名称	荆东安置房及周边附属配套工程项目（学生街）	图 名	3#楼一层平面图	图 别	方 案
						日 期	2024. 01


变更前

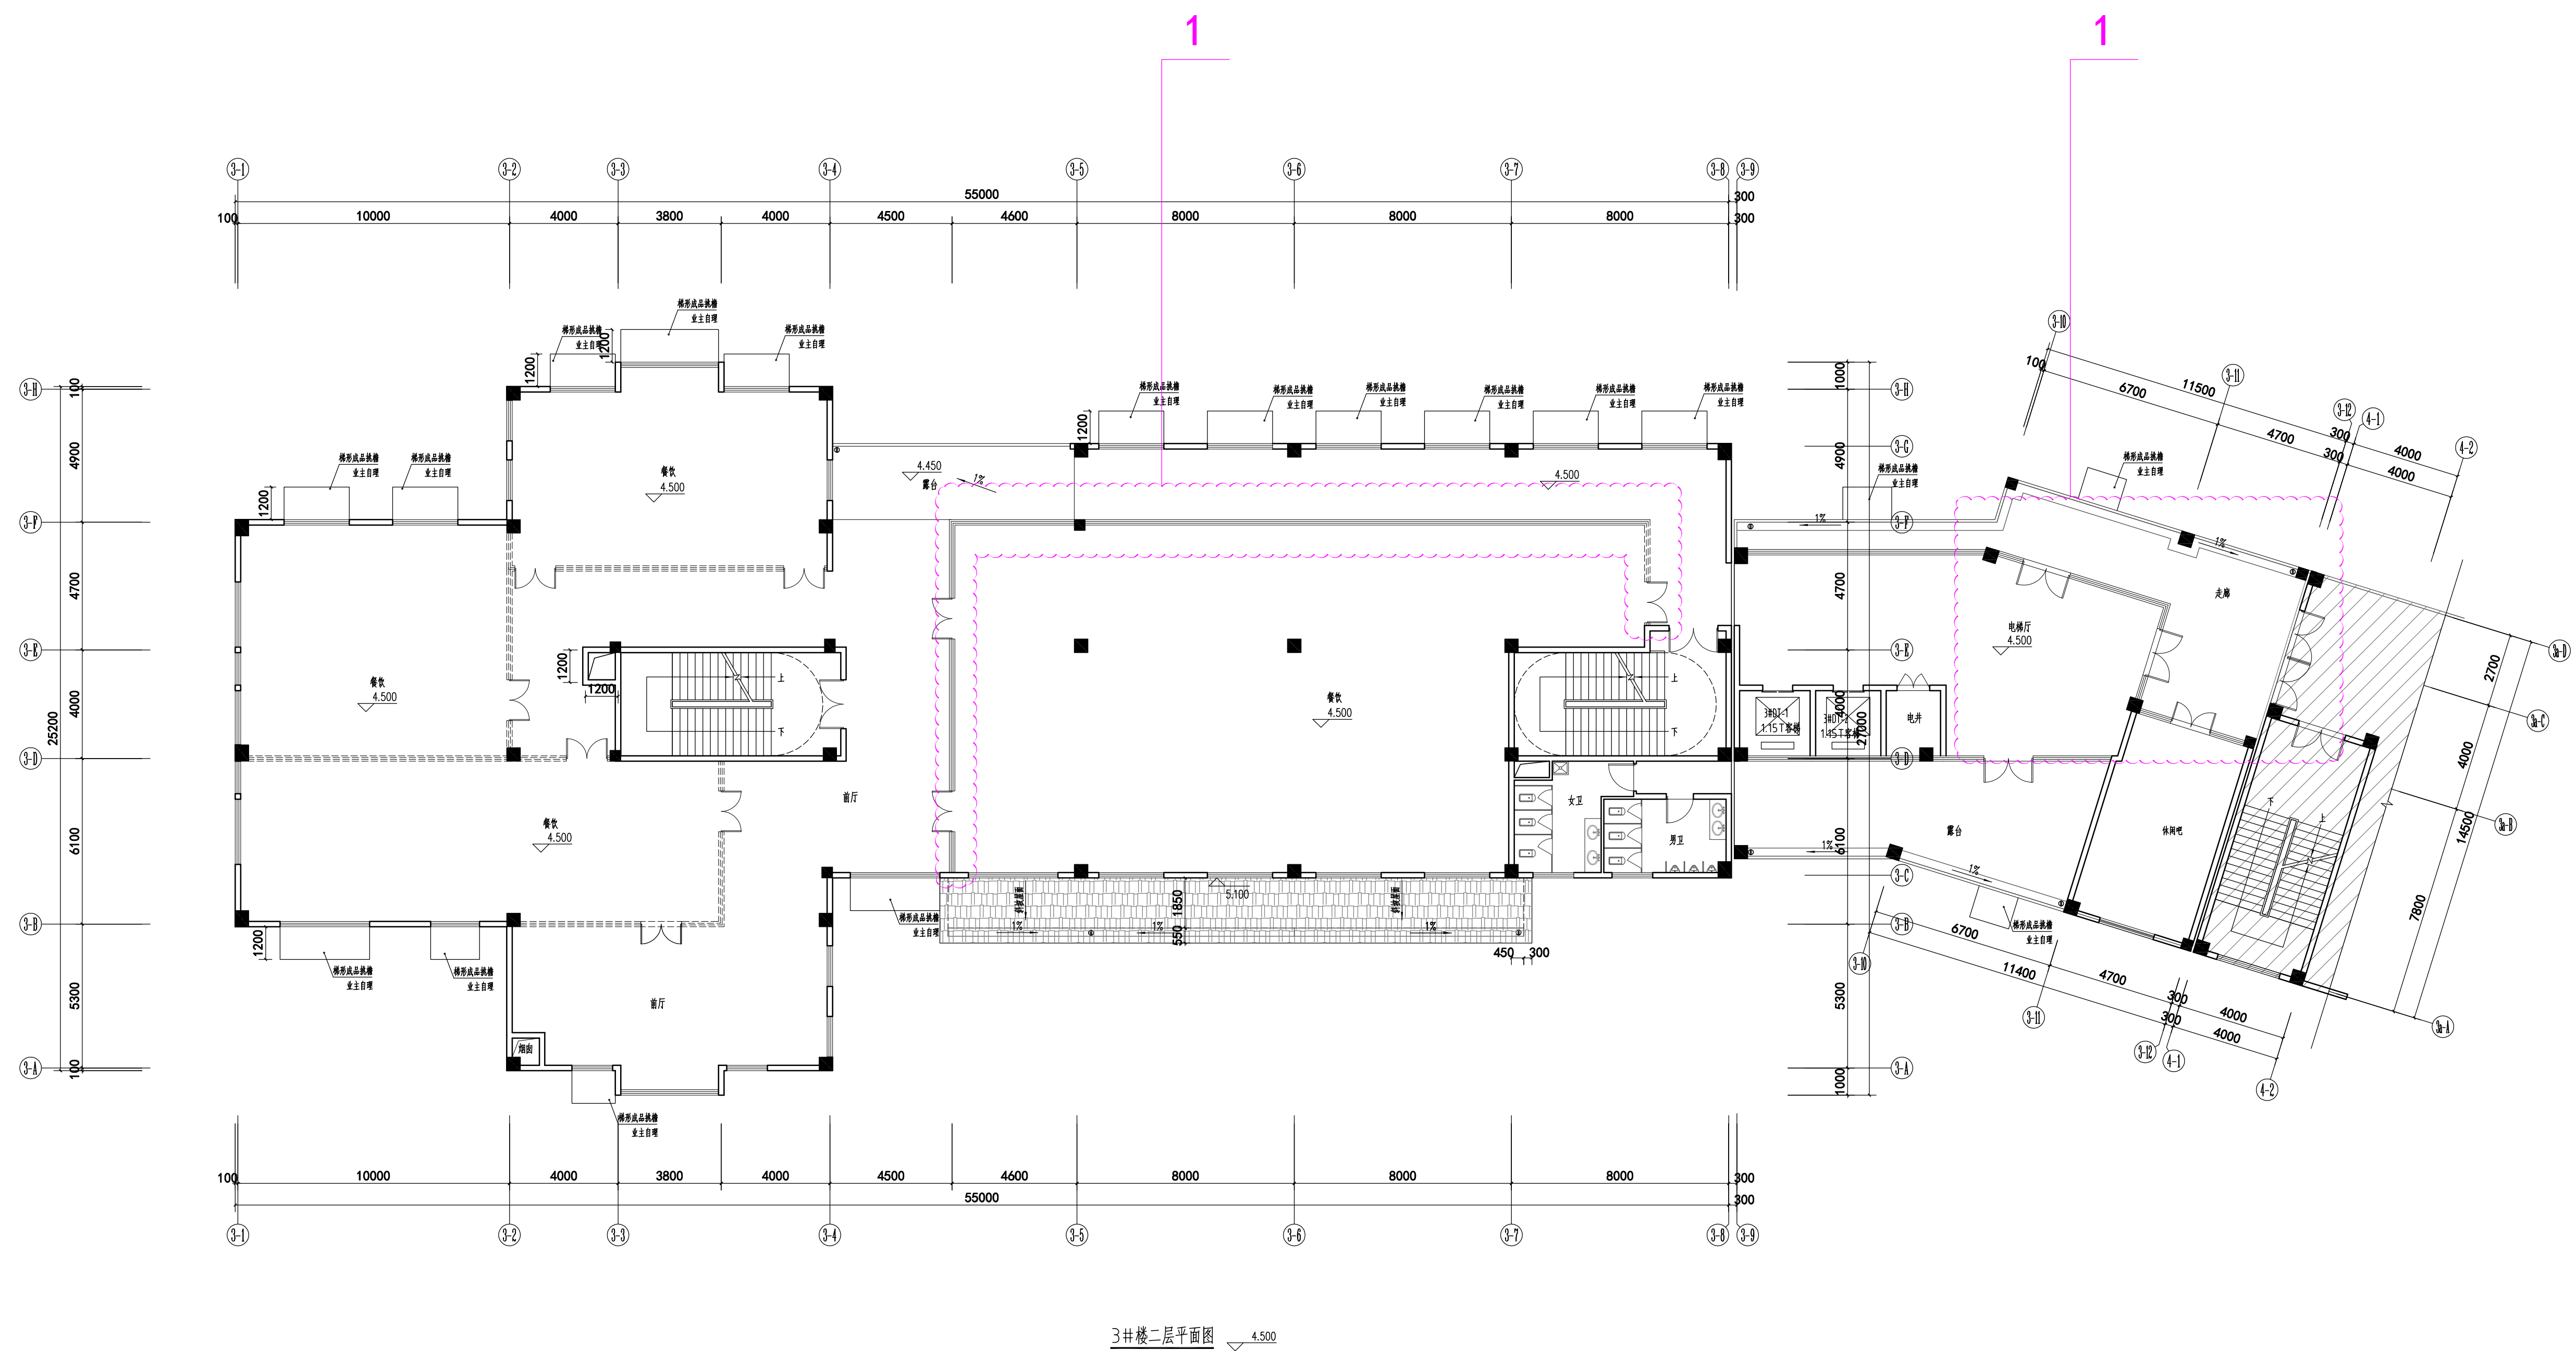

设计单位	福建一建集团有限公司	工程名称	荆东安置房及周边附属配套工程项目（学生街）	图 名	3#楼二层平面图	图 别	方 案
						日 期	2020. 10

变更后

1. 玻璃幕墙和门取消

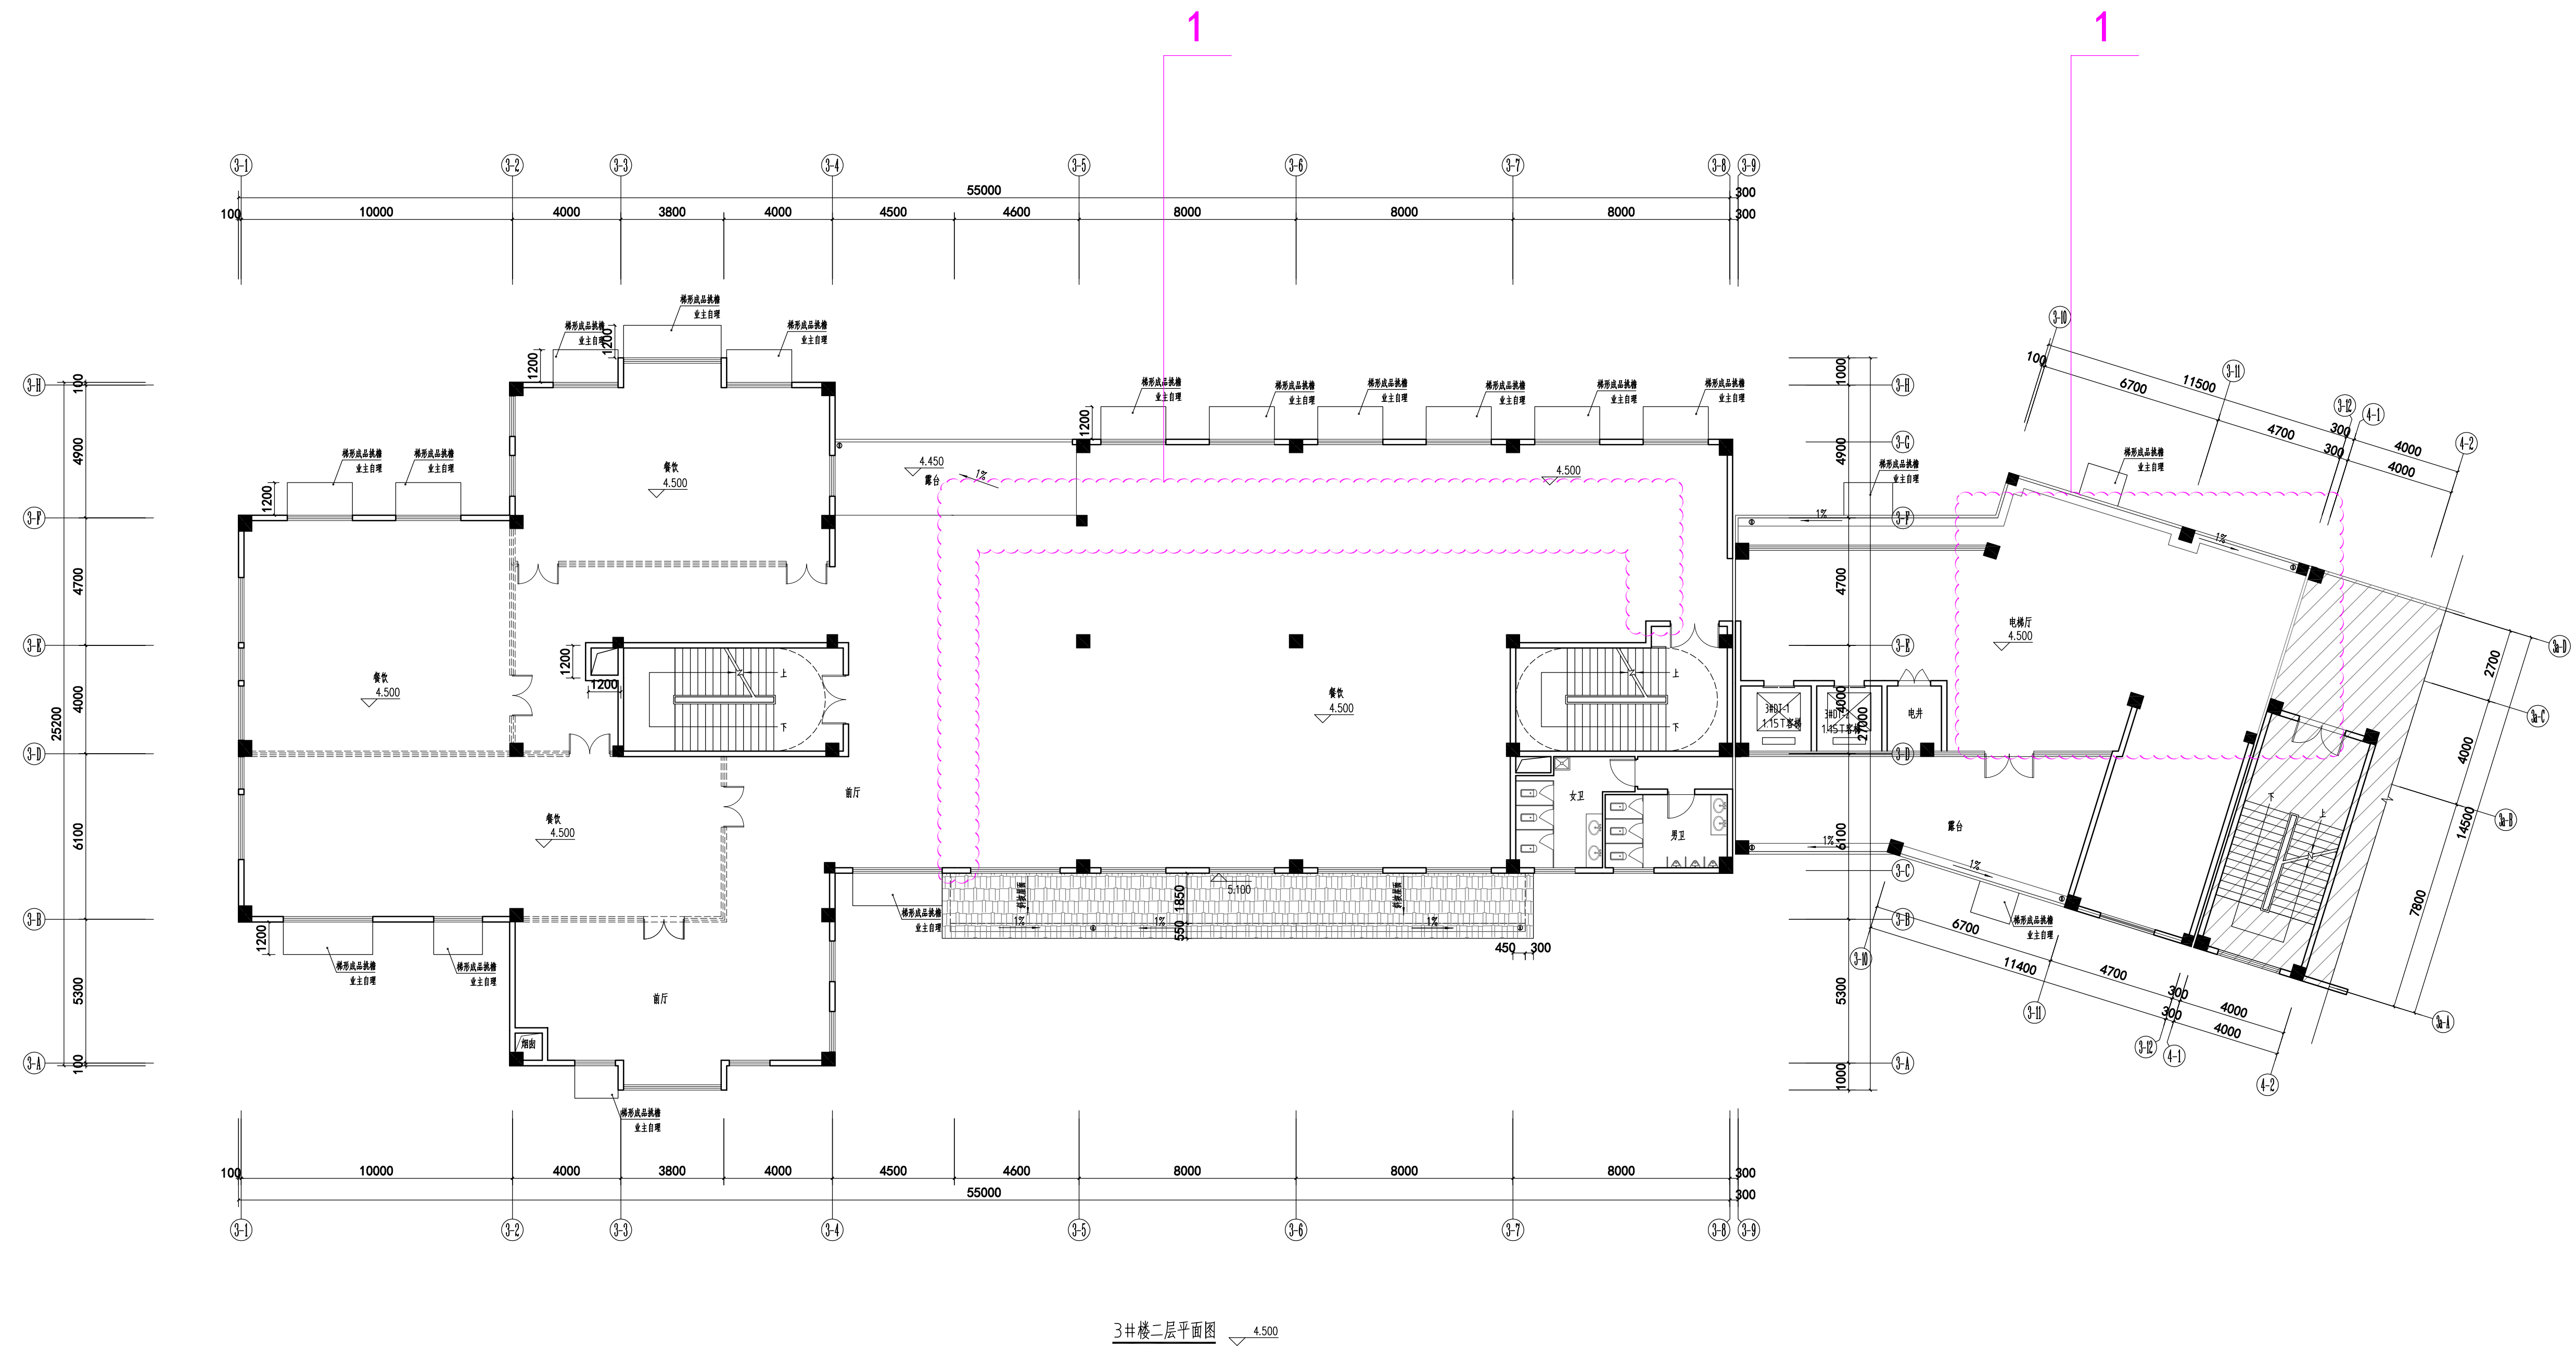

设计单位	福建一建集团有限公司	工程名称	荆东安置房及周边附属配套工程项目（学生街）	图 名	3#楼二层平面图	图 别	方 案
						日 期	2024. 01


变更前



设计单位	福建一建集团有限公司	工程名称	荆东安置房及周边附属配套工程项目（学生街）	图 名	3#楼三层平面图	图 别	方 案
						日 期	2020. 10


变更后

1. 墙体取消

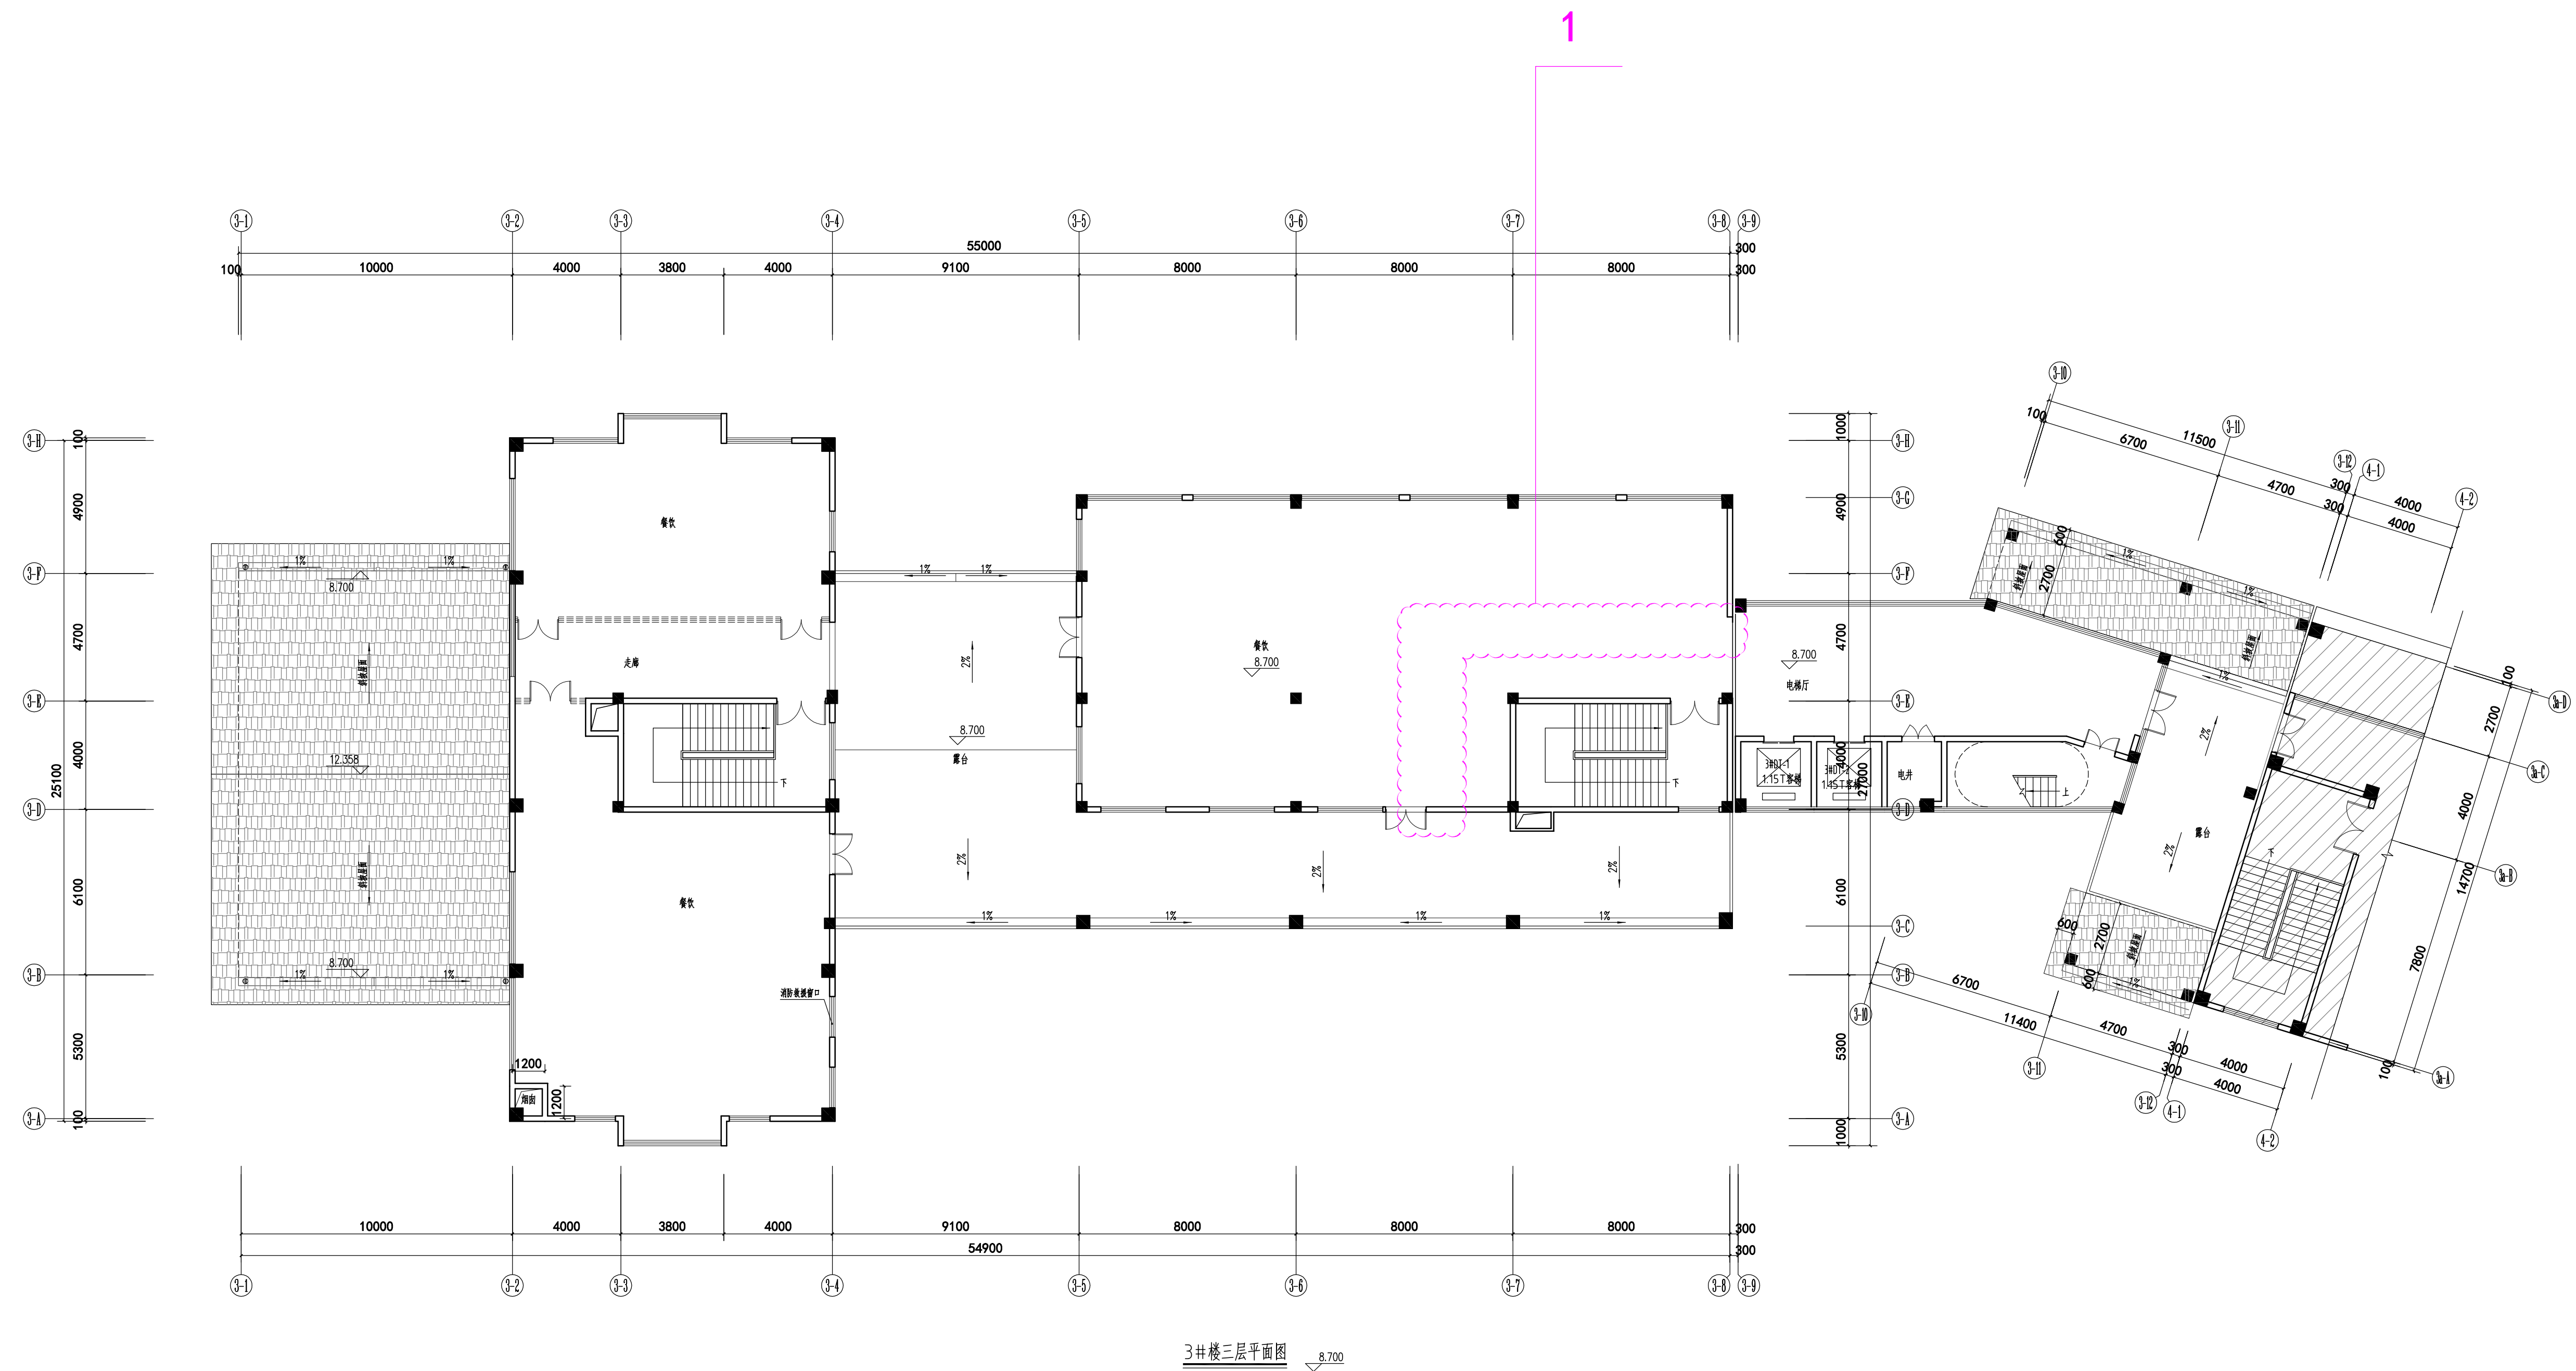

设计单位	福建一建集团有限公司	工程名称	荆东安置房及周边附属配套工程项目（学生街）	图 名	3#楼三层平面图	图 别	方 案
						日 期	2024. 01


变更前

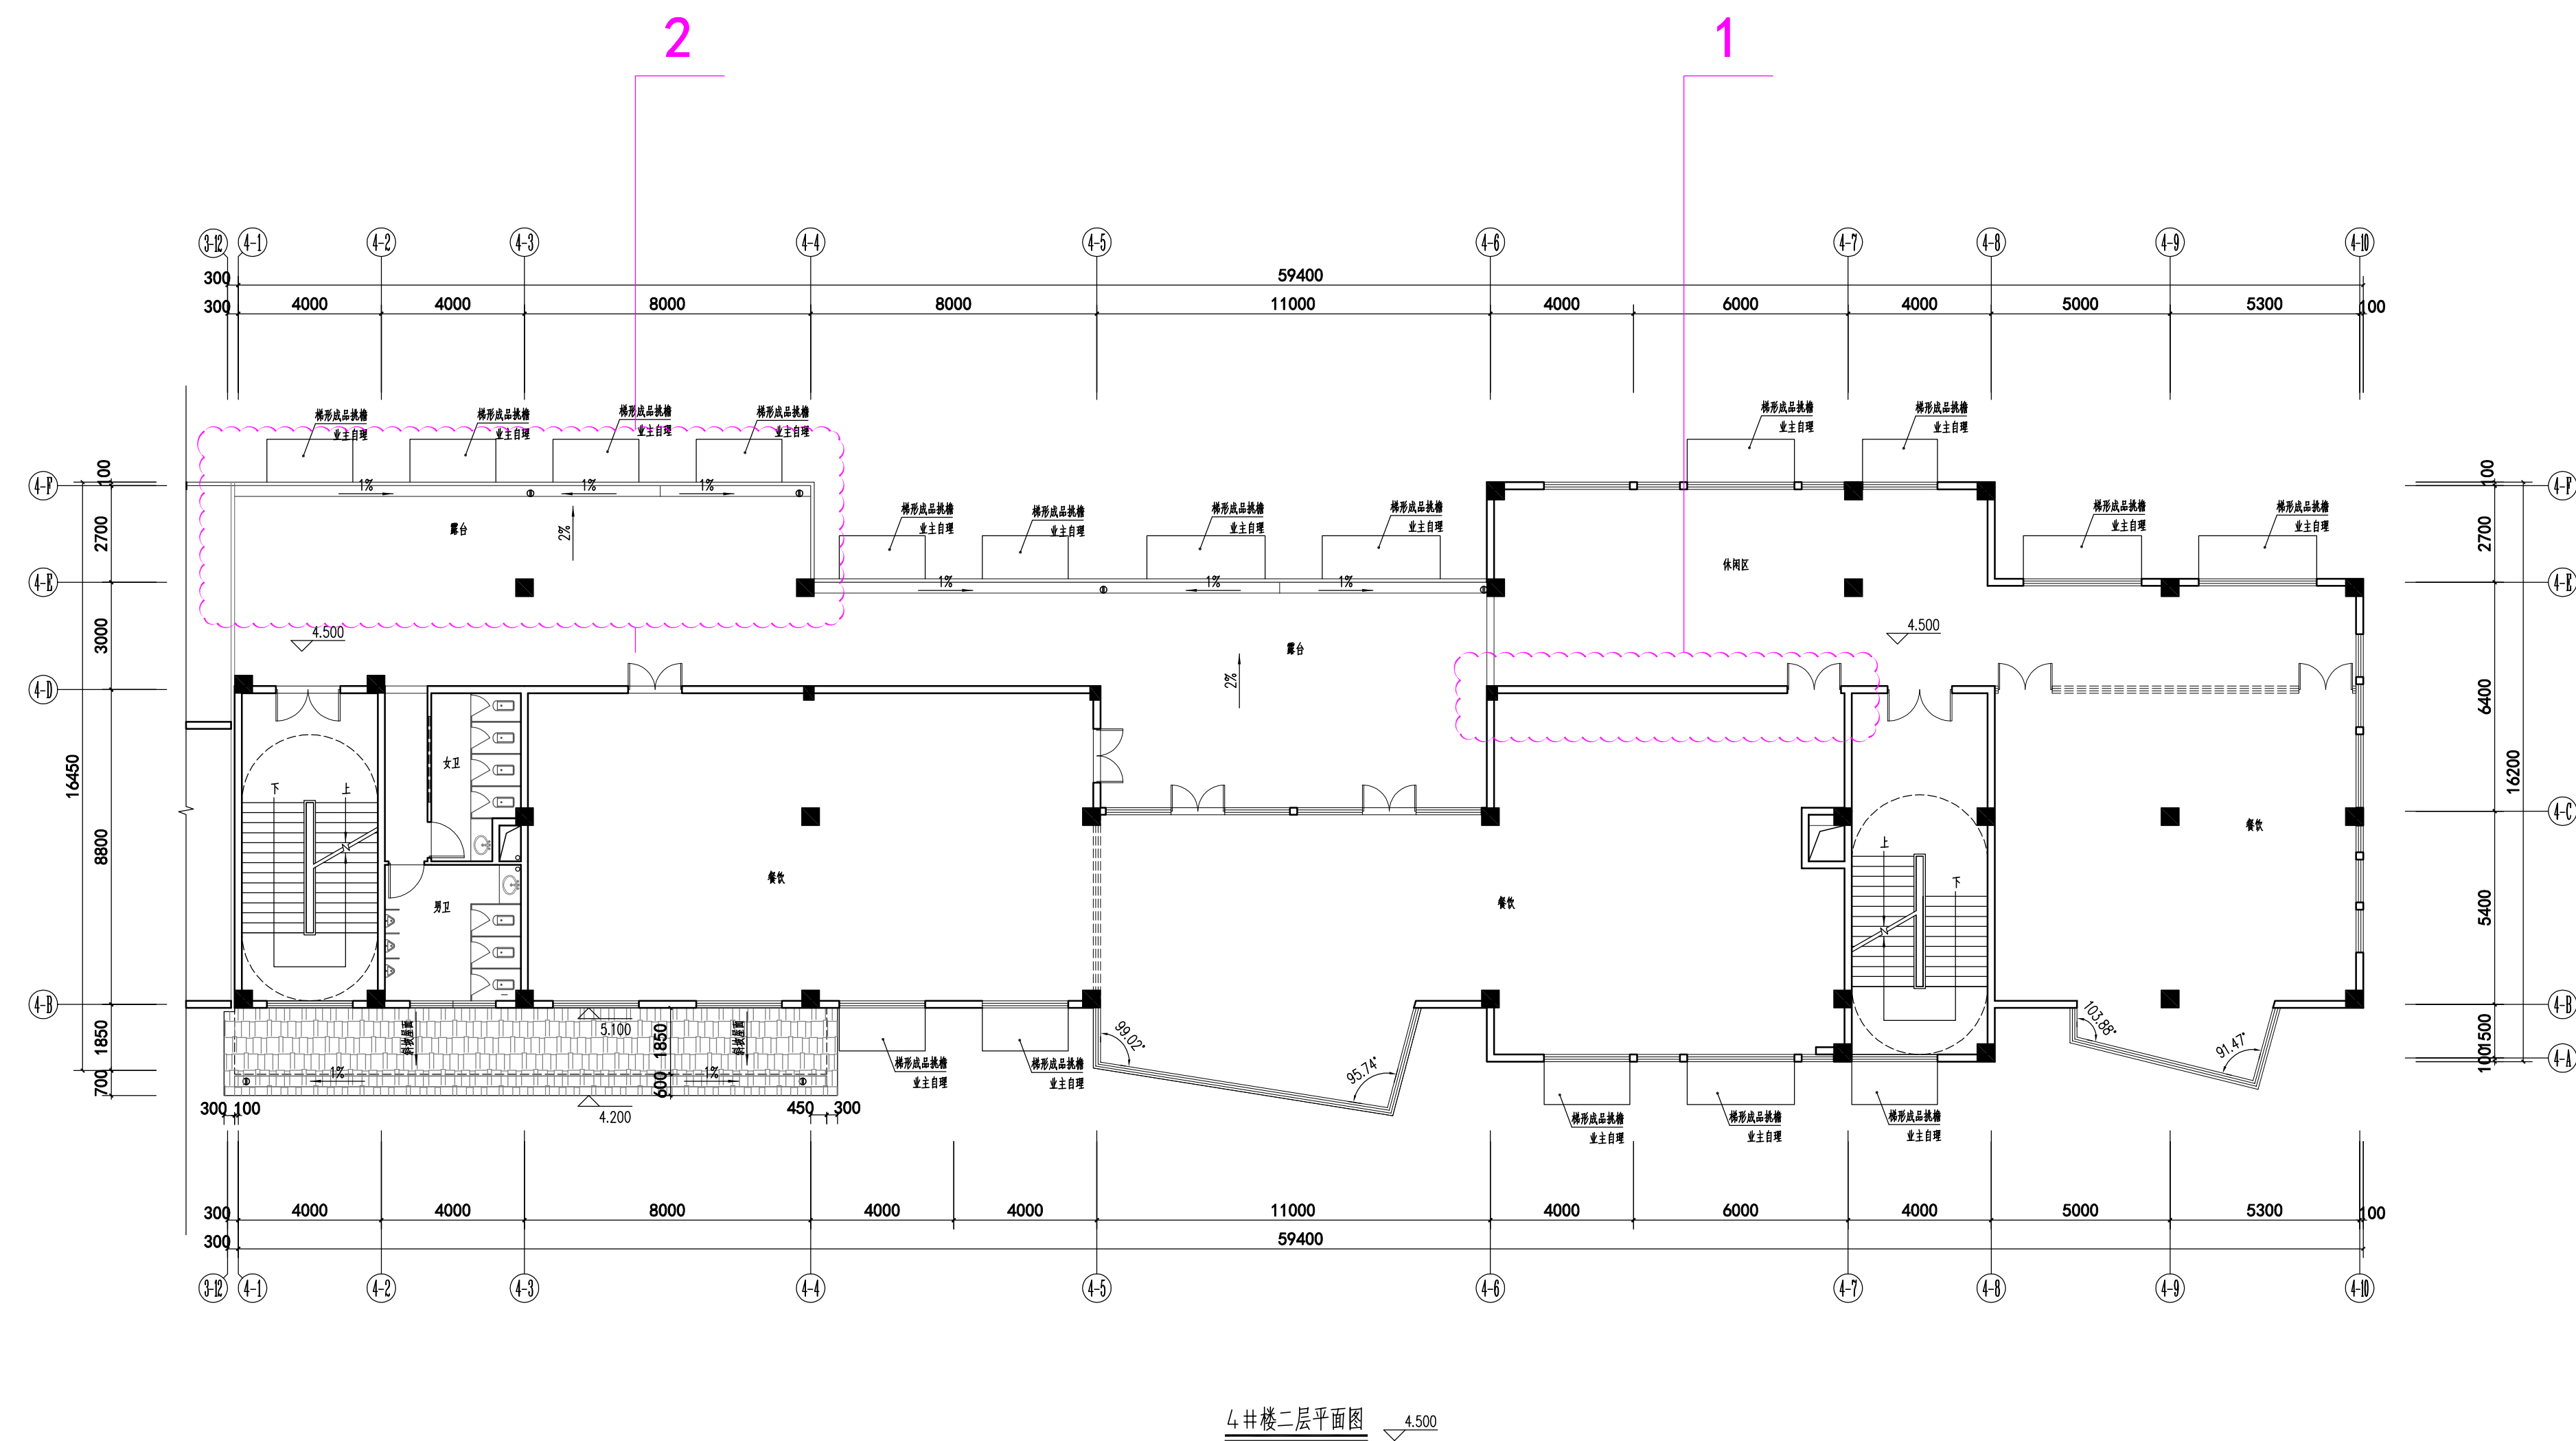

设计单位	福建一建集团有限公司	工程名称	荆东安置房及周边附属配套工程项目（学生街）	图 名	4#楼二层平面图	图 别	方 案
						日 期	2020. 10


变更后

1. 墙体和门取消
2. 新增结构柱，1-4轴审批功能为露台部分改为局部走廊

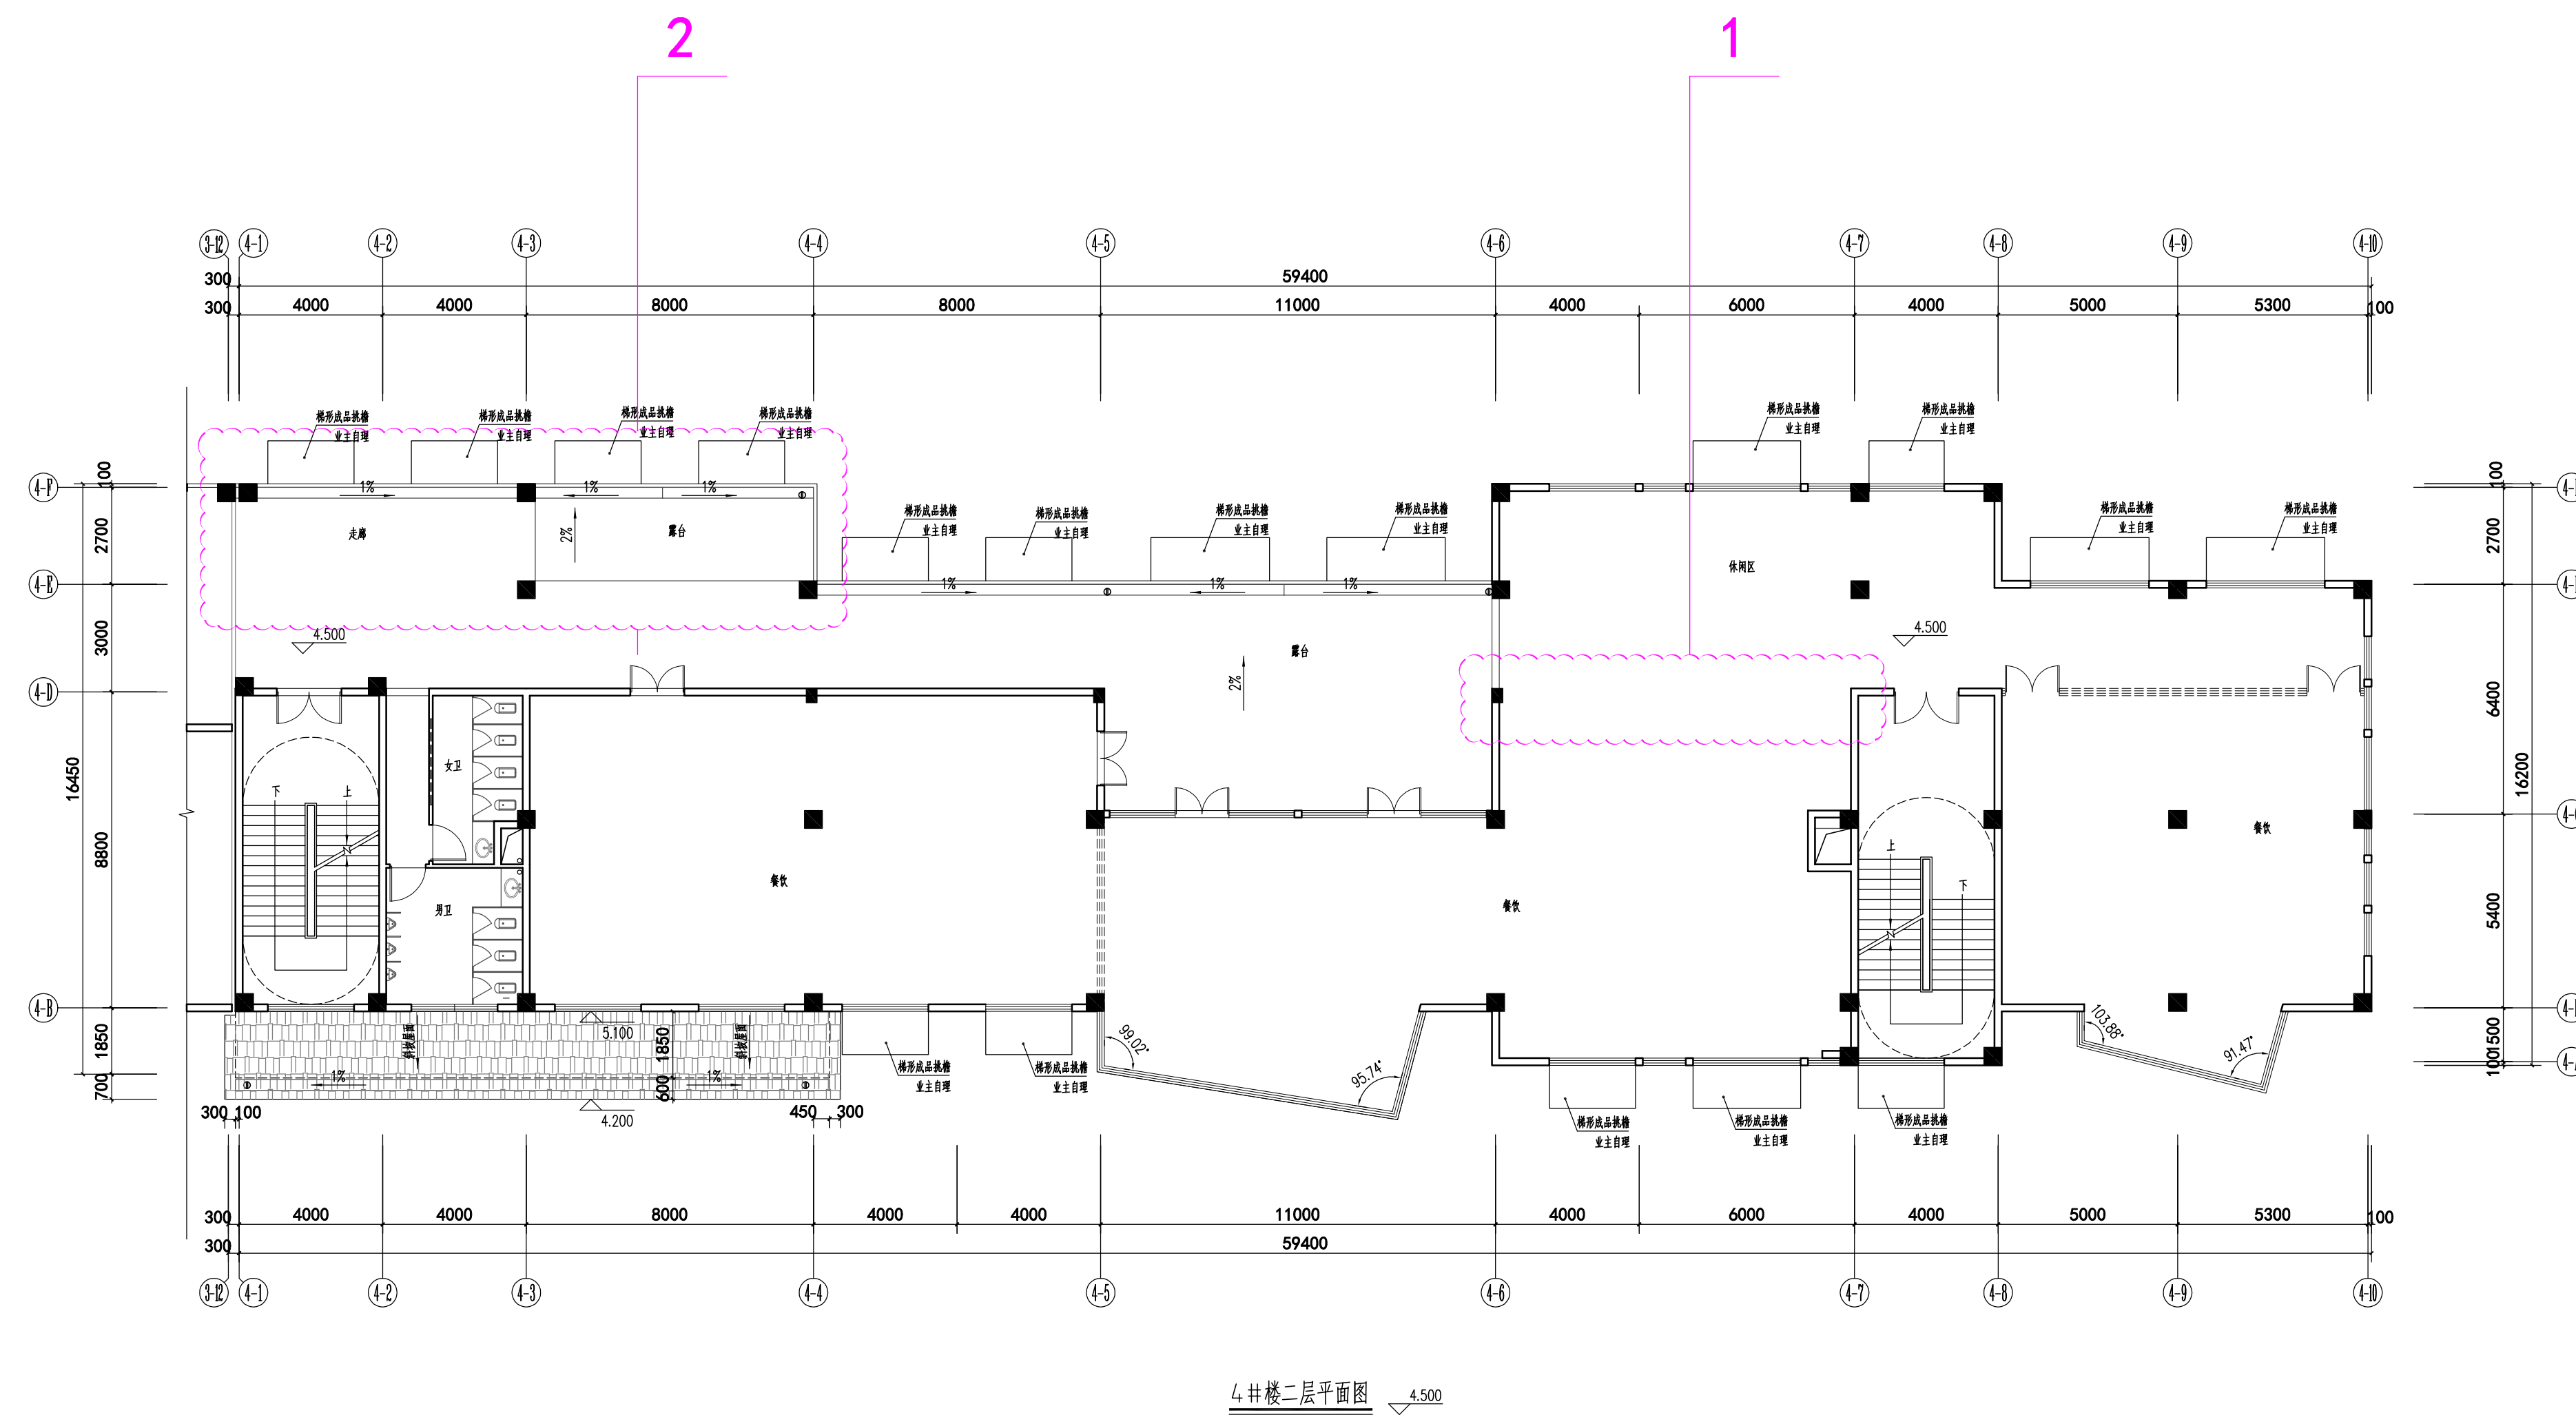

设计单位	福建一建集团有限公司	工程名称	荆东安置房及周边附属配套工程项目（学生街）	图 名	4#楼二层平面图	图 别	方 案
						日 期	2024. 01

变更前

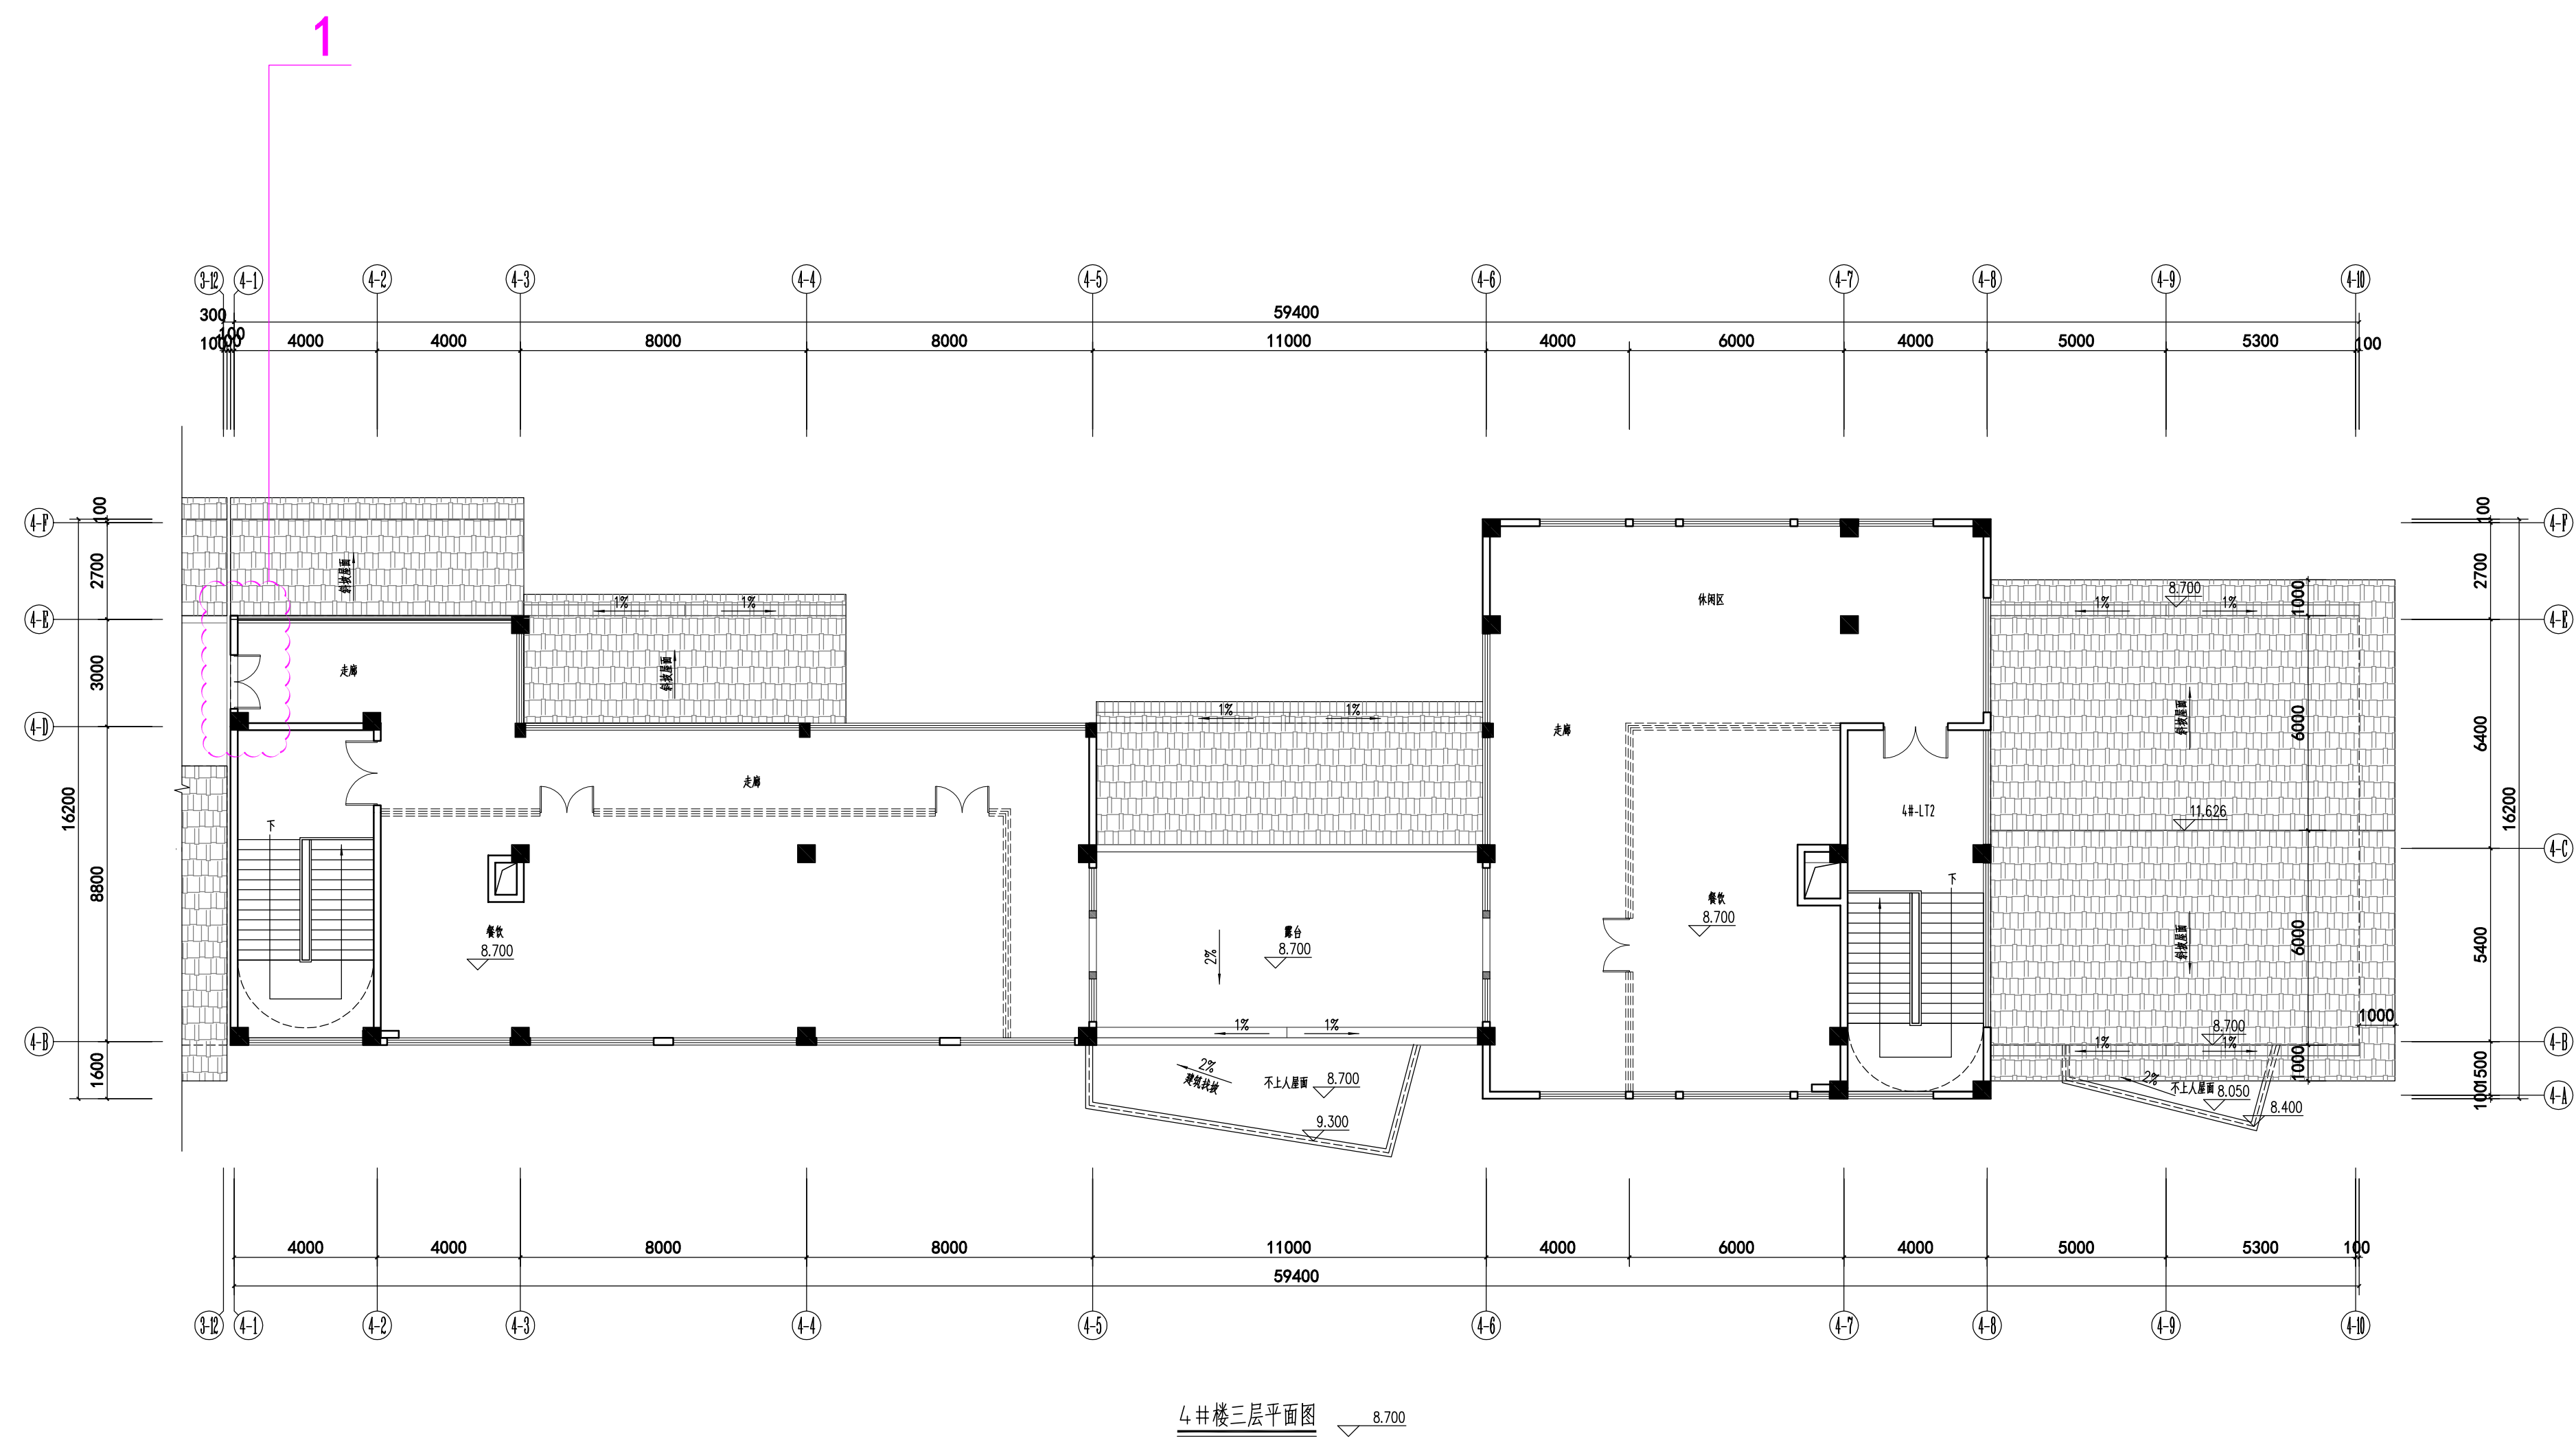

设计单位

福建一建集团有限公司

工程名称

荆东安置房及周边附属配套工程项目（学生街）

图 名

4#楼三层平面图

图 别


方 案

日 期

2020. 10


变更后

1. 墙体和门取消，走廊改为露天走廊。

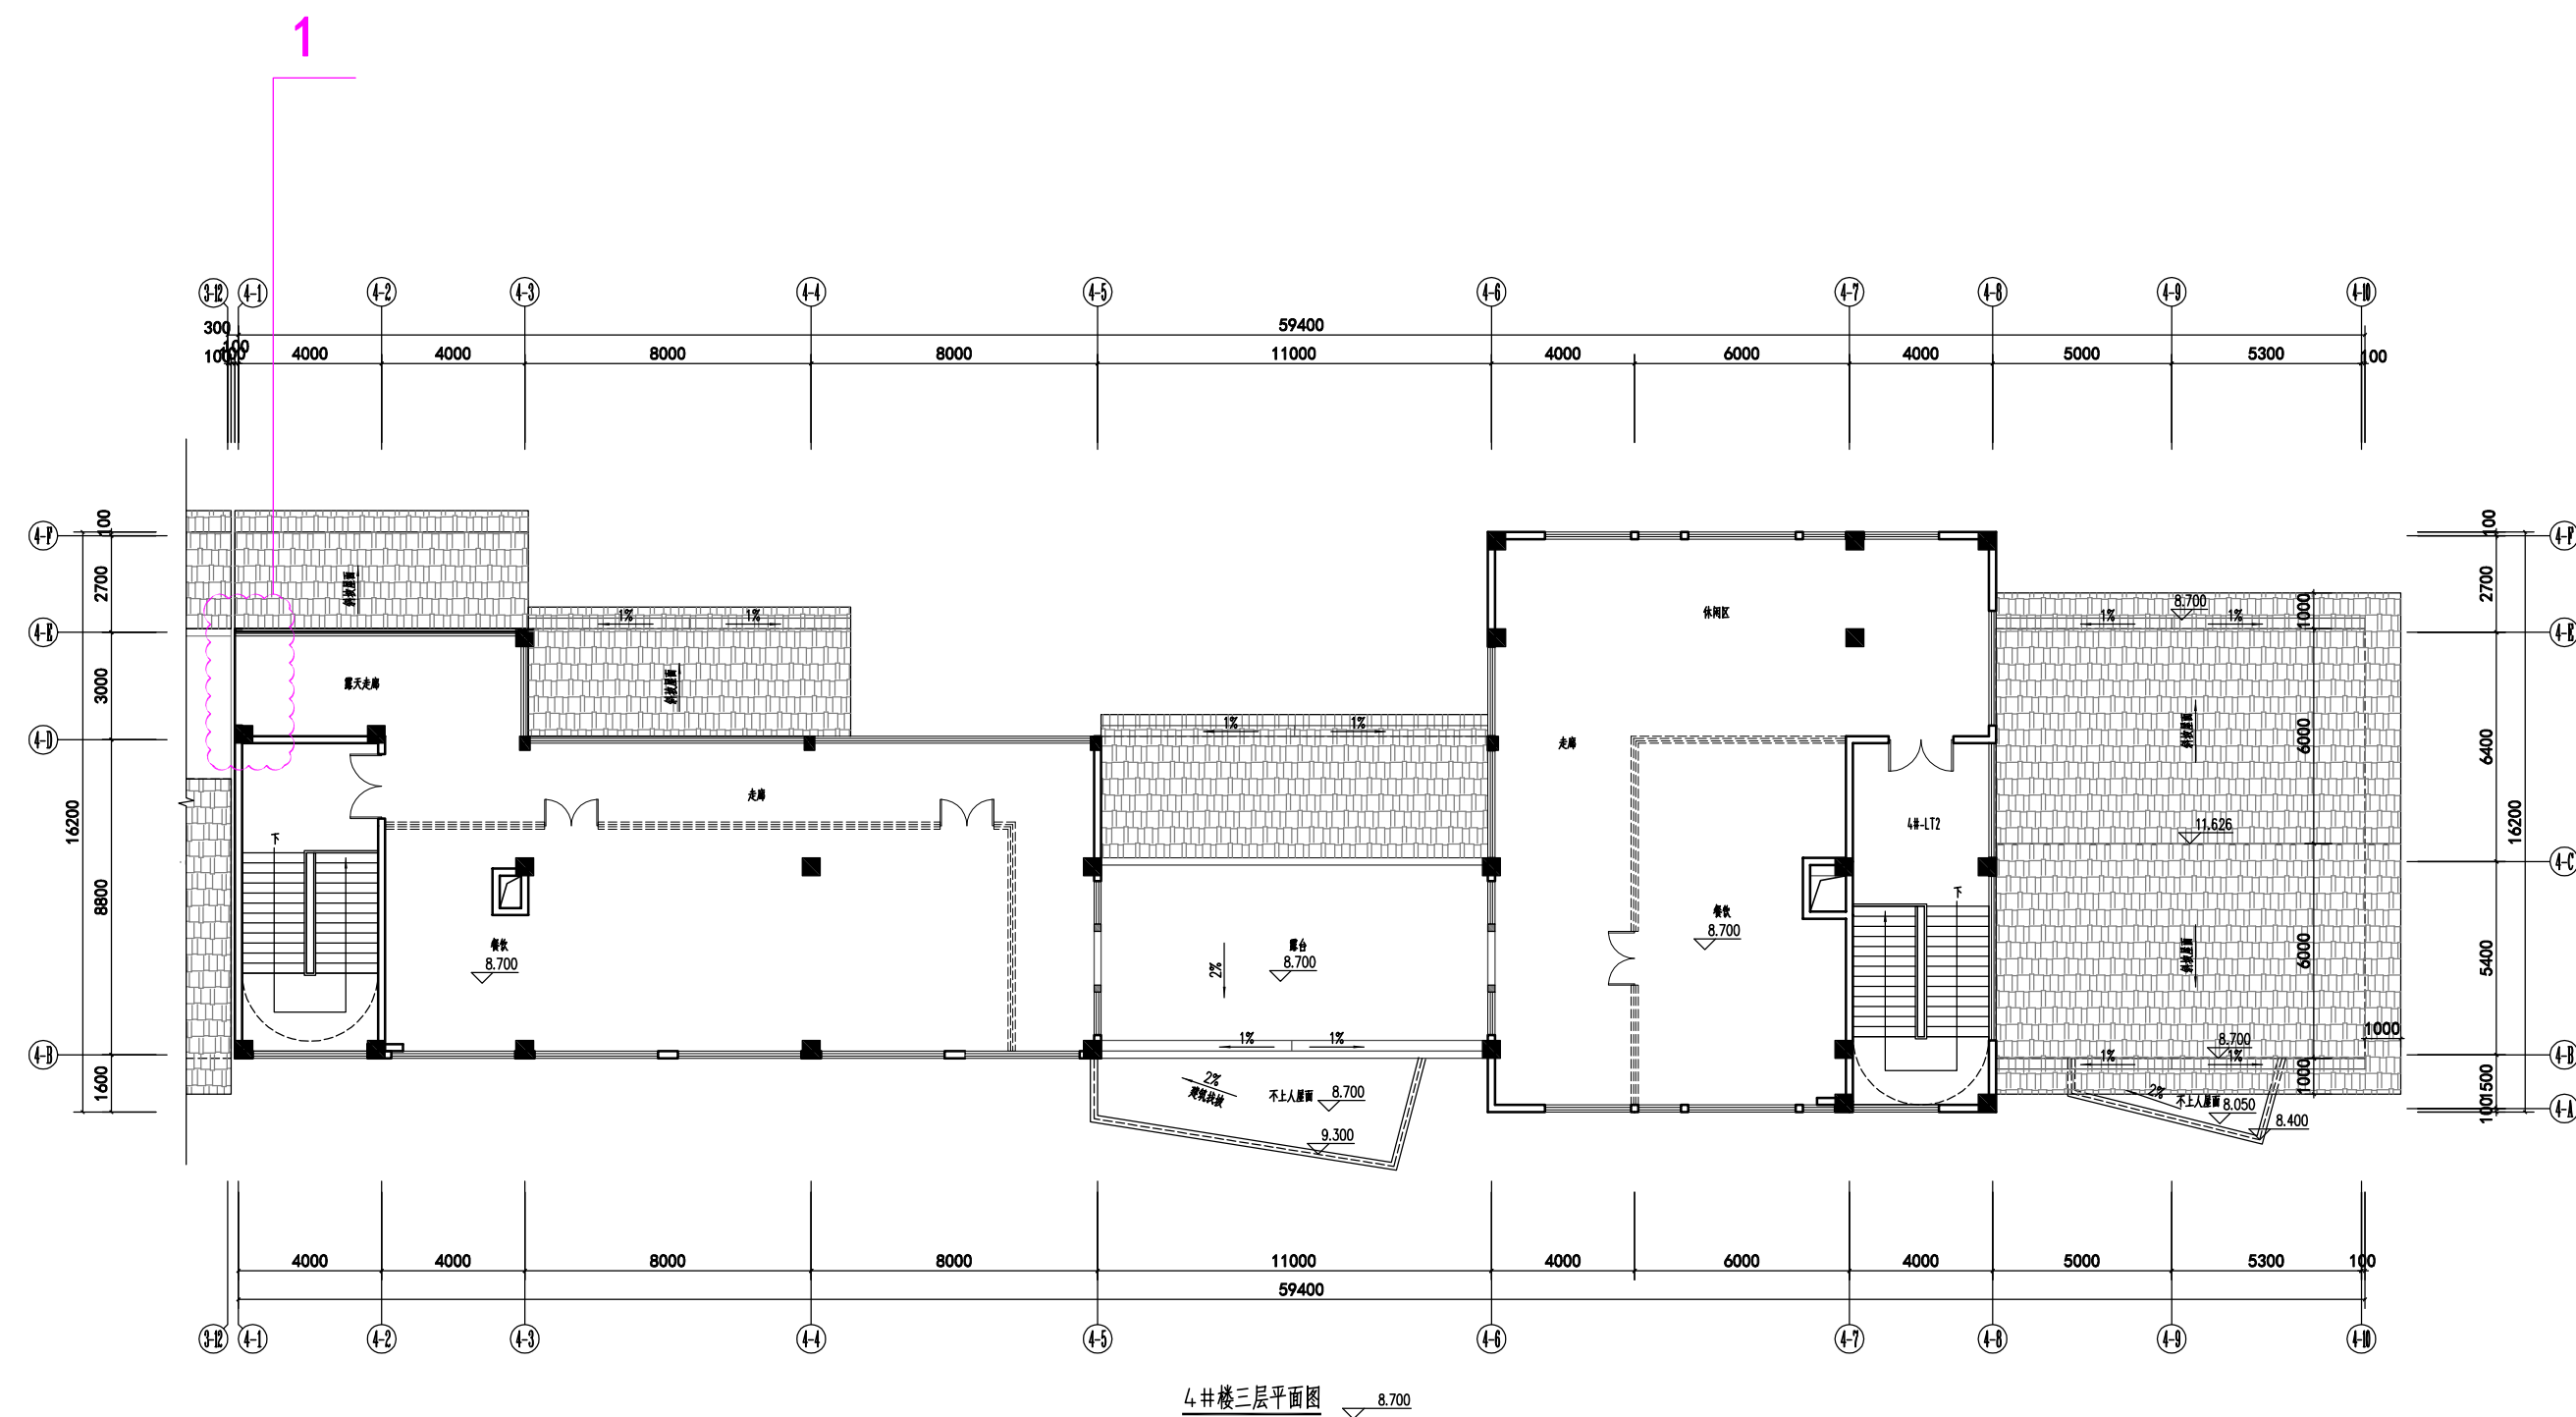

设计单位	福建一建集团有限公司	工程名称	荆东安置房及周边附属配套工程项目（学生街）	图 名	4#楼三层平面图	图 别	方 案
						日 期	2024. 02


变更前

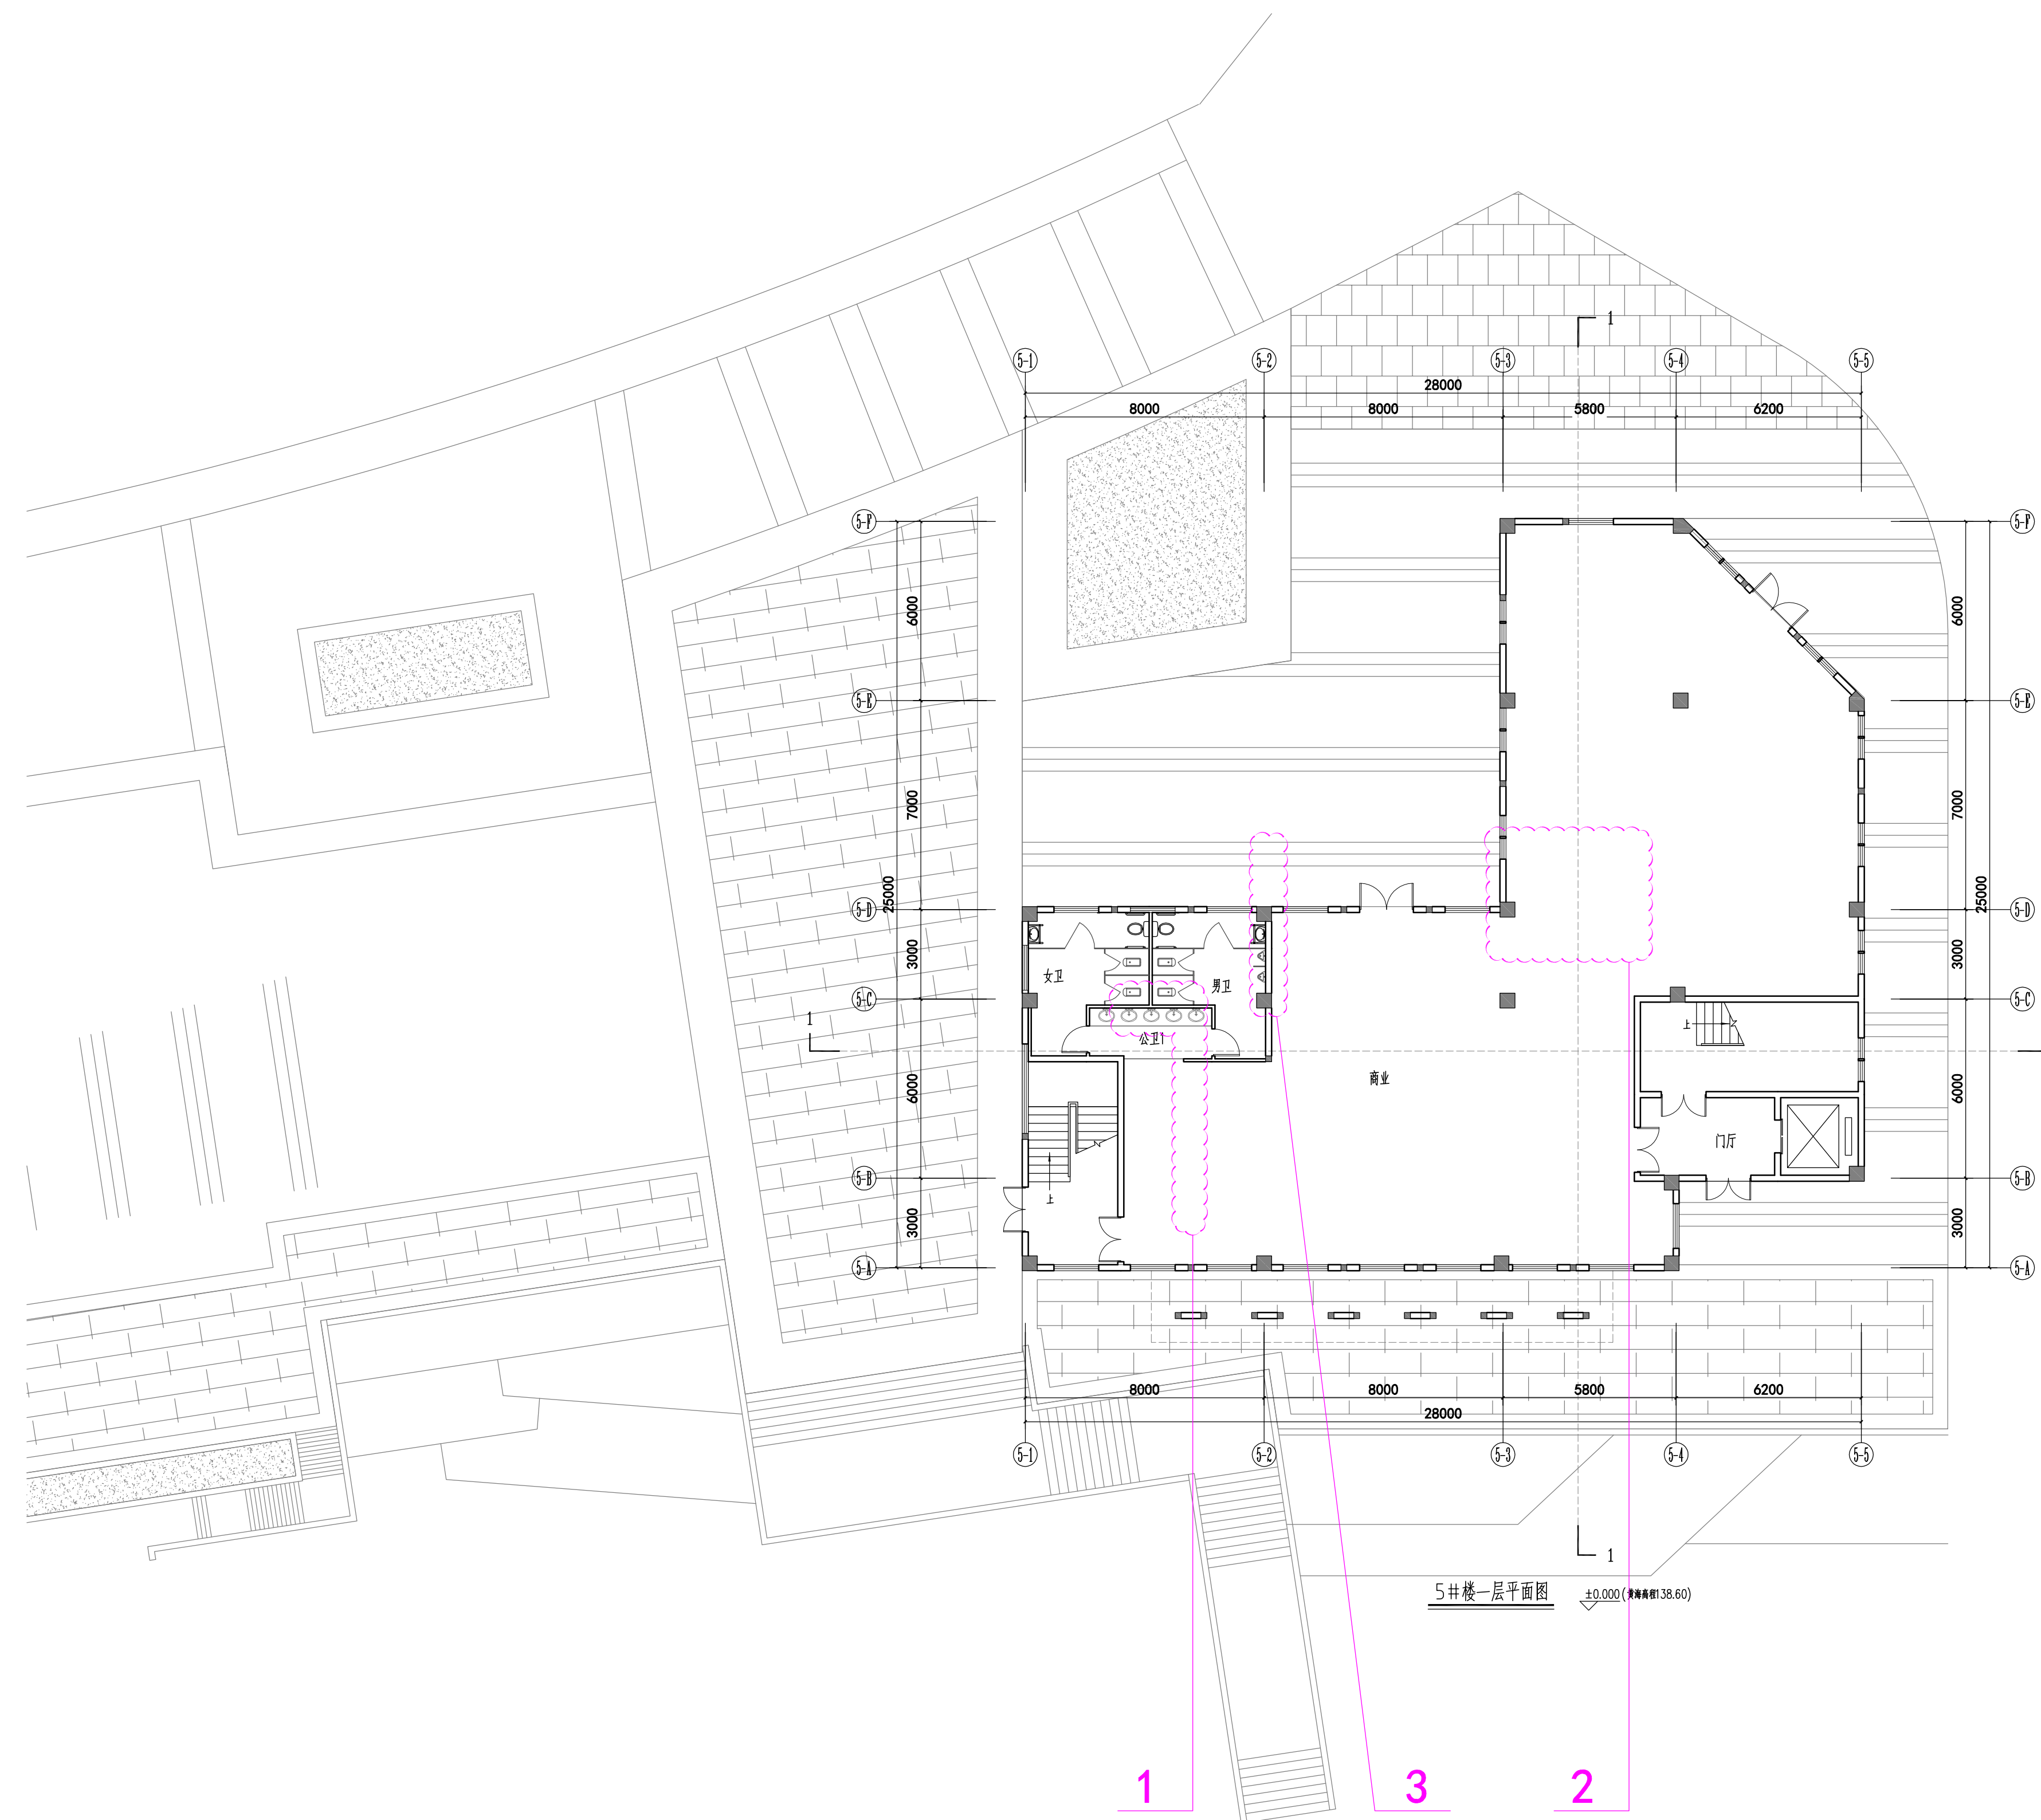

设计单位	福建一建集团有限公司	工程名称	荆东安置房及周边附属配套工程项目（学生街）	图 名	5#楼一层平面图	图 别	方 案
						日 期	2020. 10


变更后

1. 新增墙体和门
2. 商业增加隔墙
3. 卫生间与商业之间隔墙左移动0.15m

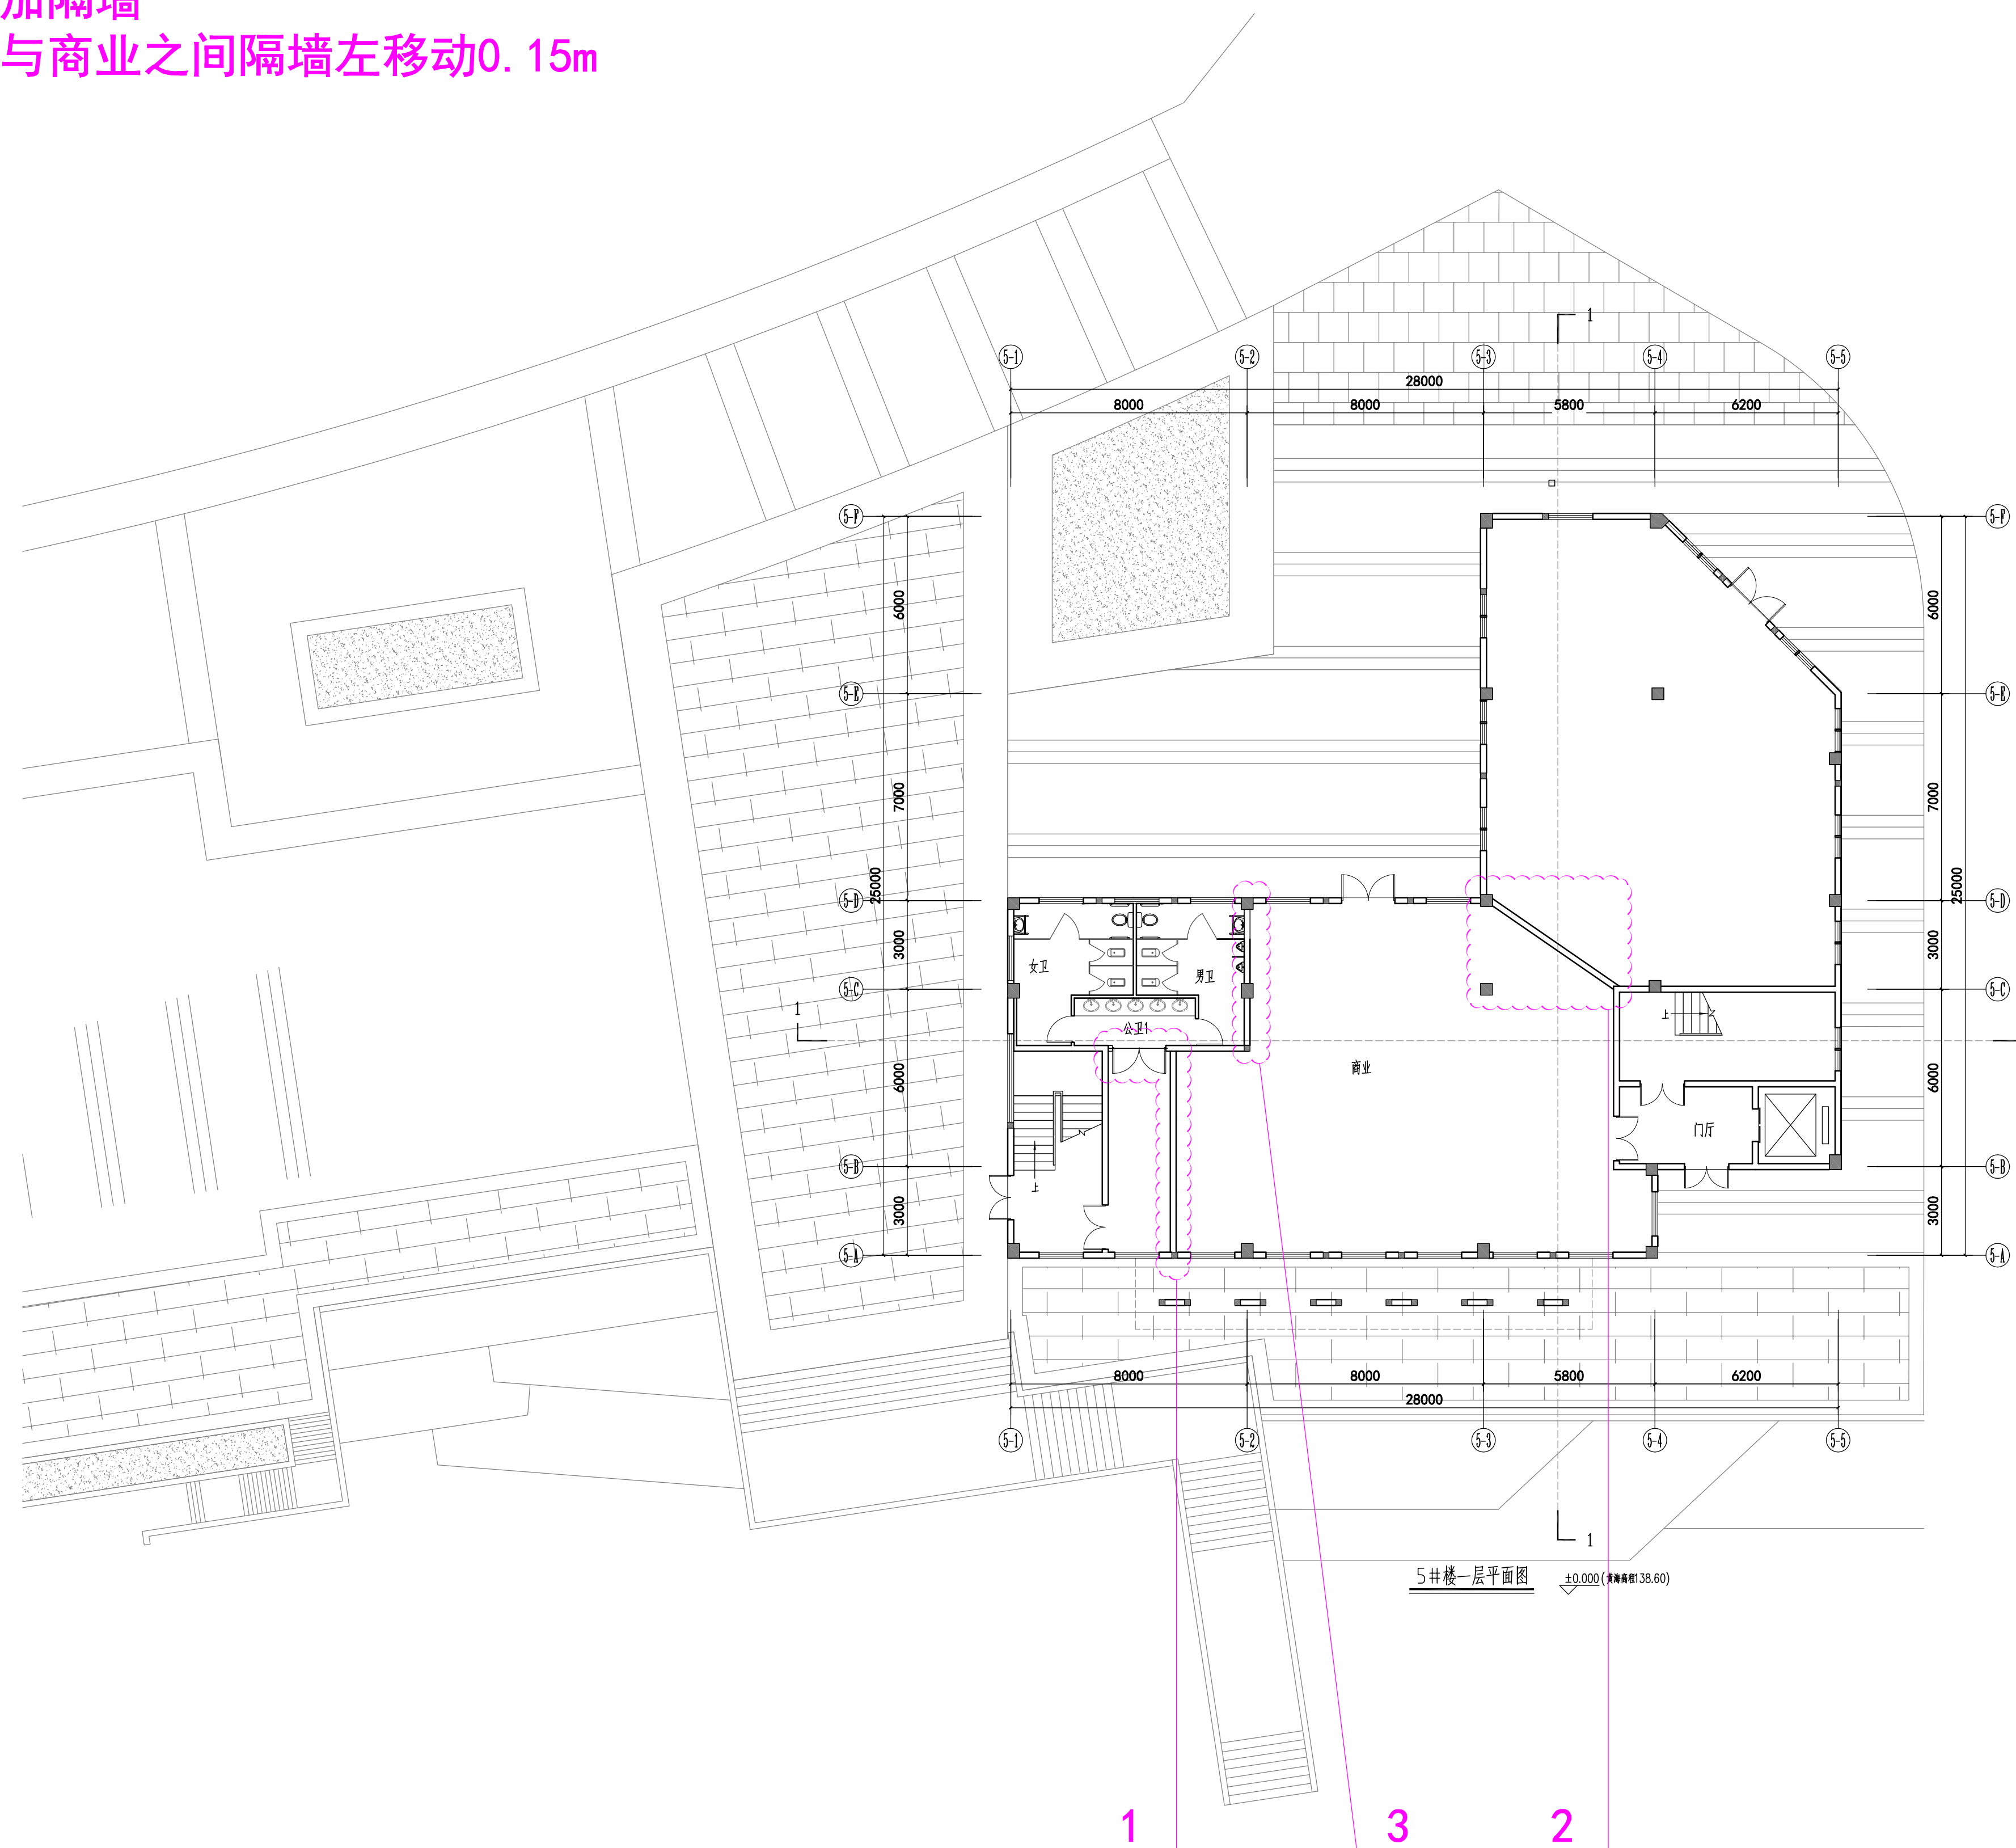

设计单位	福建一建集团有限公司	工程名称	荆东安置房及周边附属配套工程项目（学生街）	图 名	5#楼一层平面图	图 别	方 案
						日 期	2024. 02


变更前

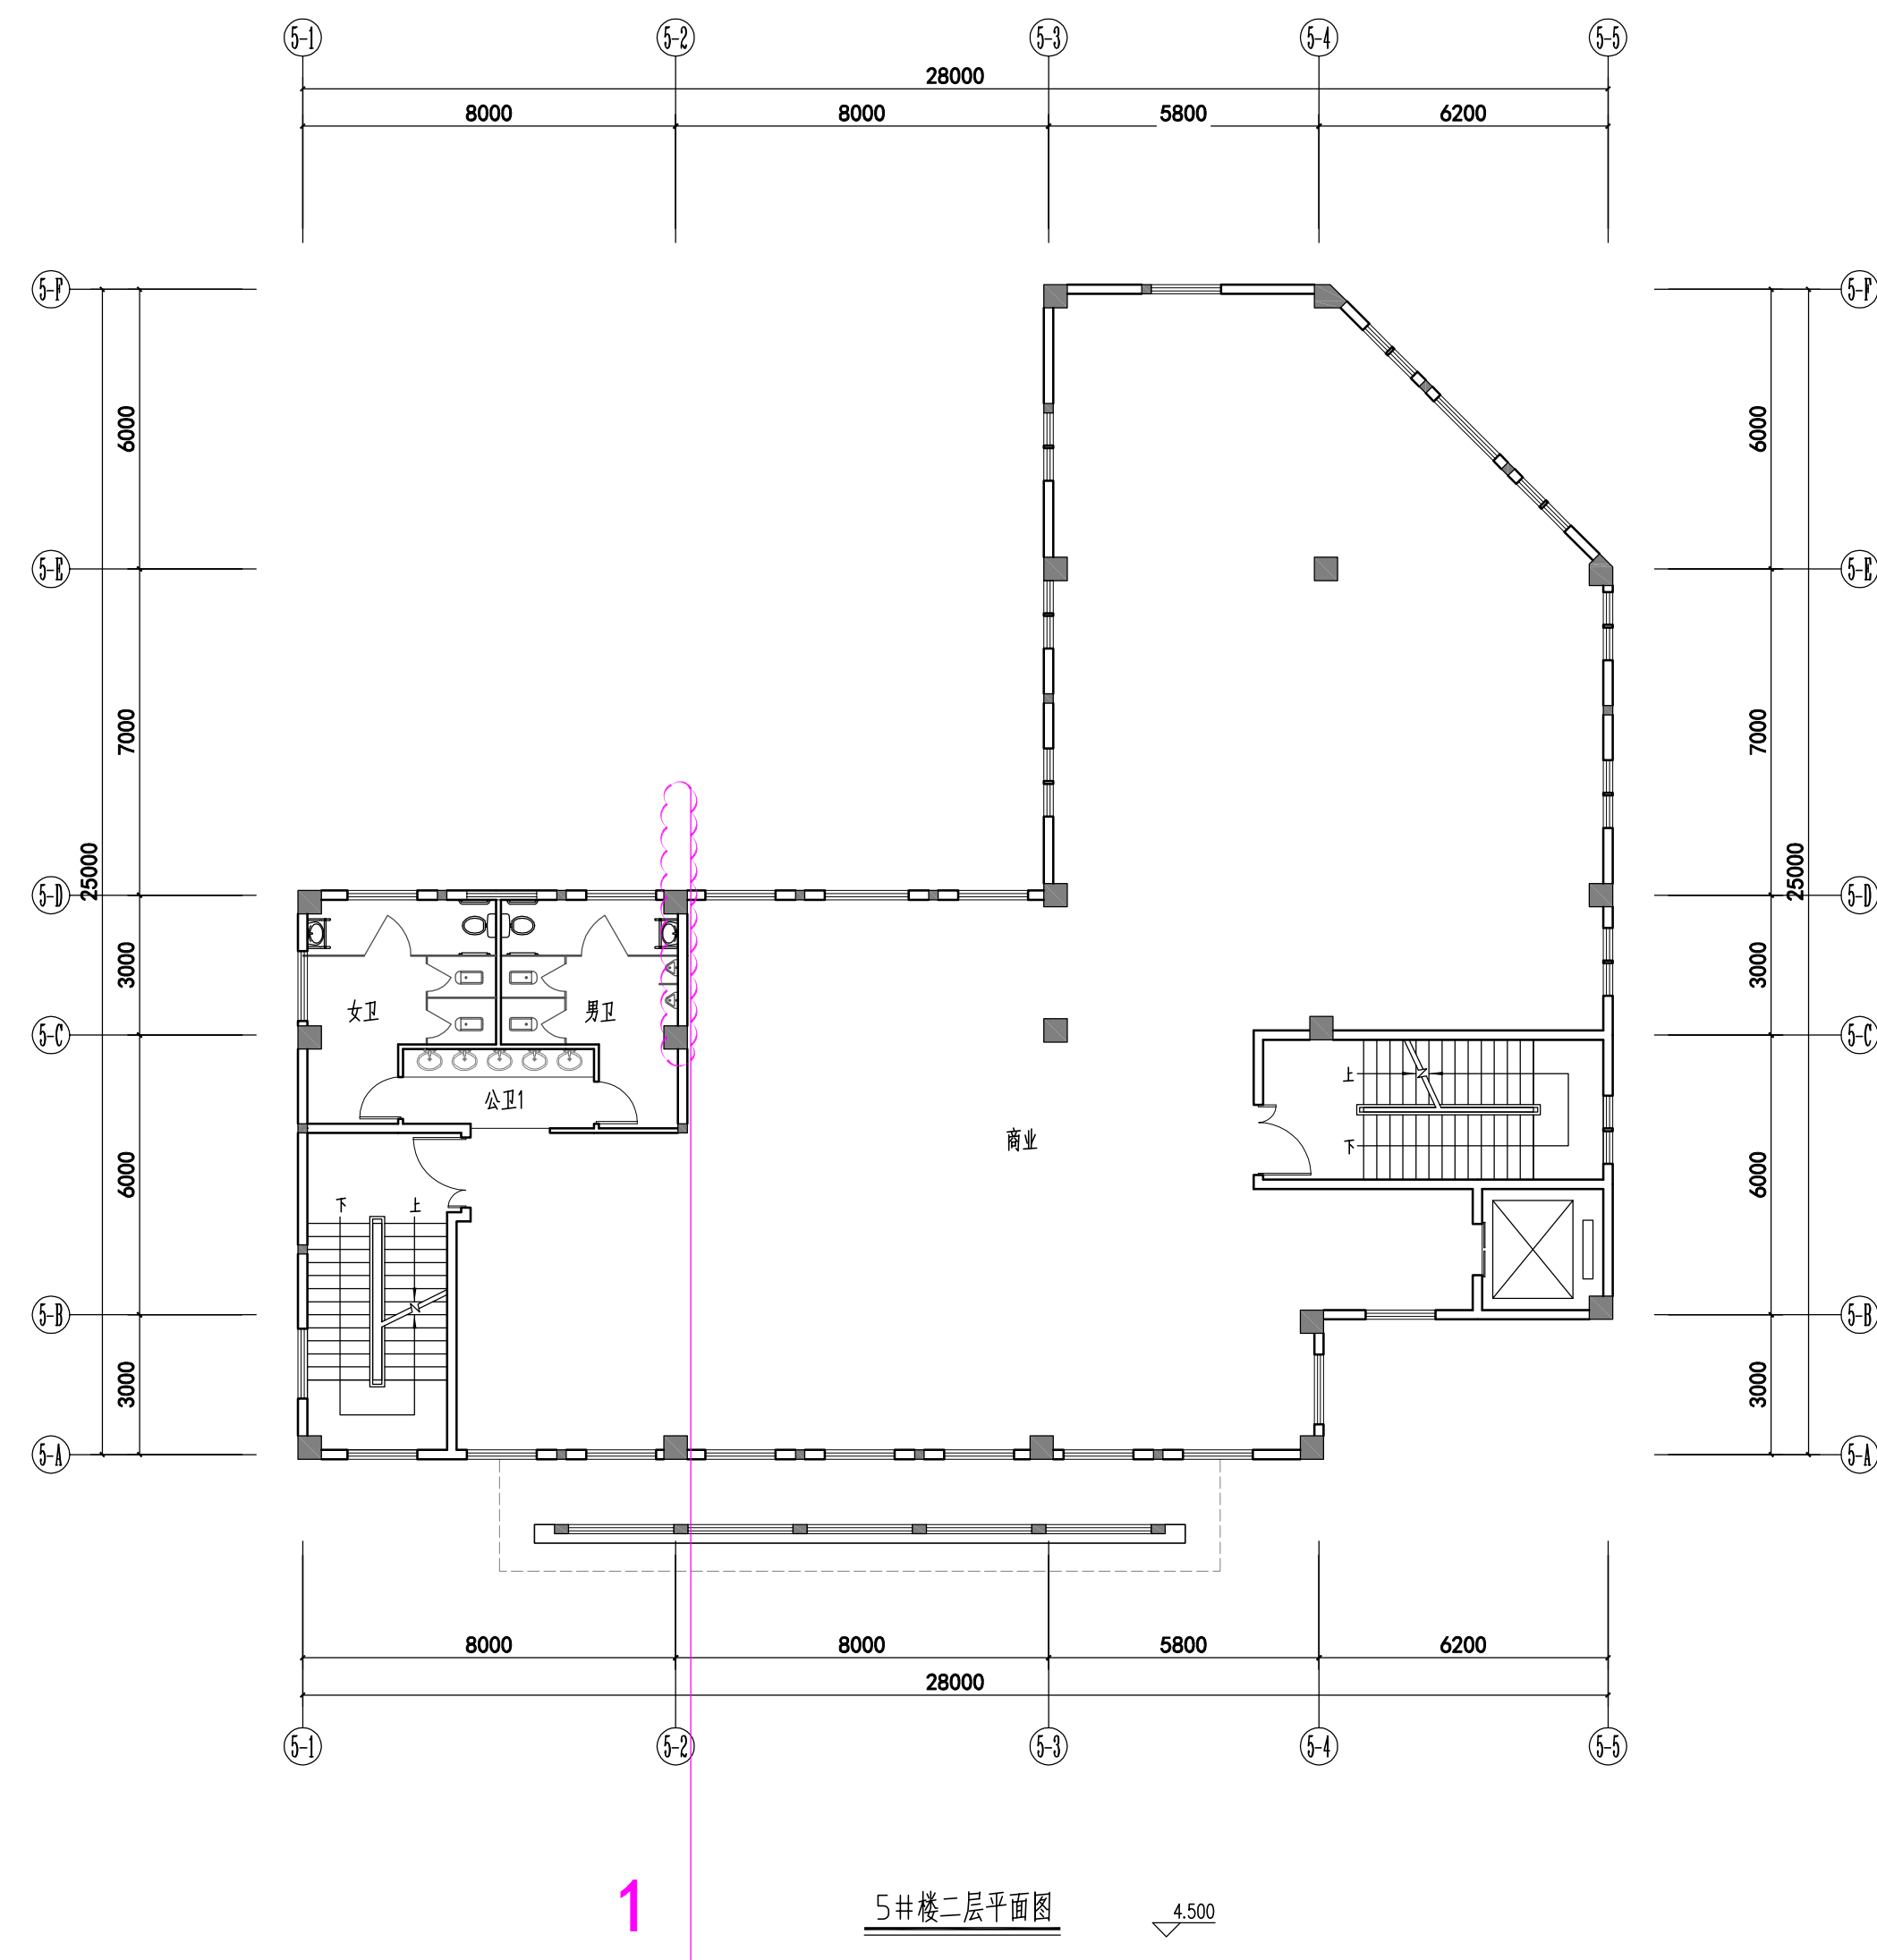

设计单位	福建一建集团有限公司	工程名称	荆东安置房及周边附属配套工程项目（学生街）	图 名	5#楼二层平面图	图 别	方 案
						日 期	2020. 10


变更后

1. 卫生间与商业之间隔墙左移动0.15m

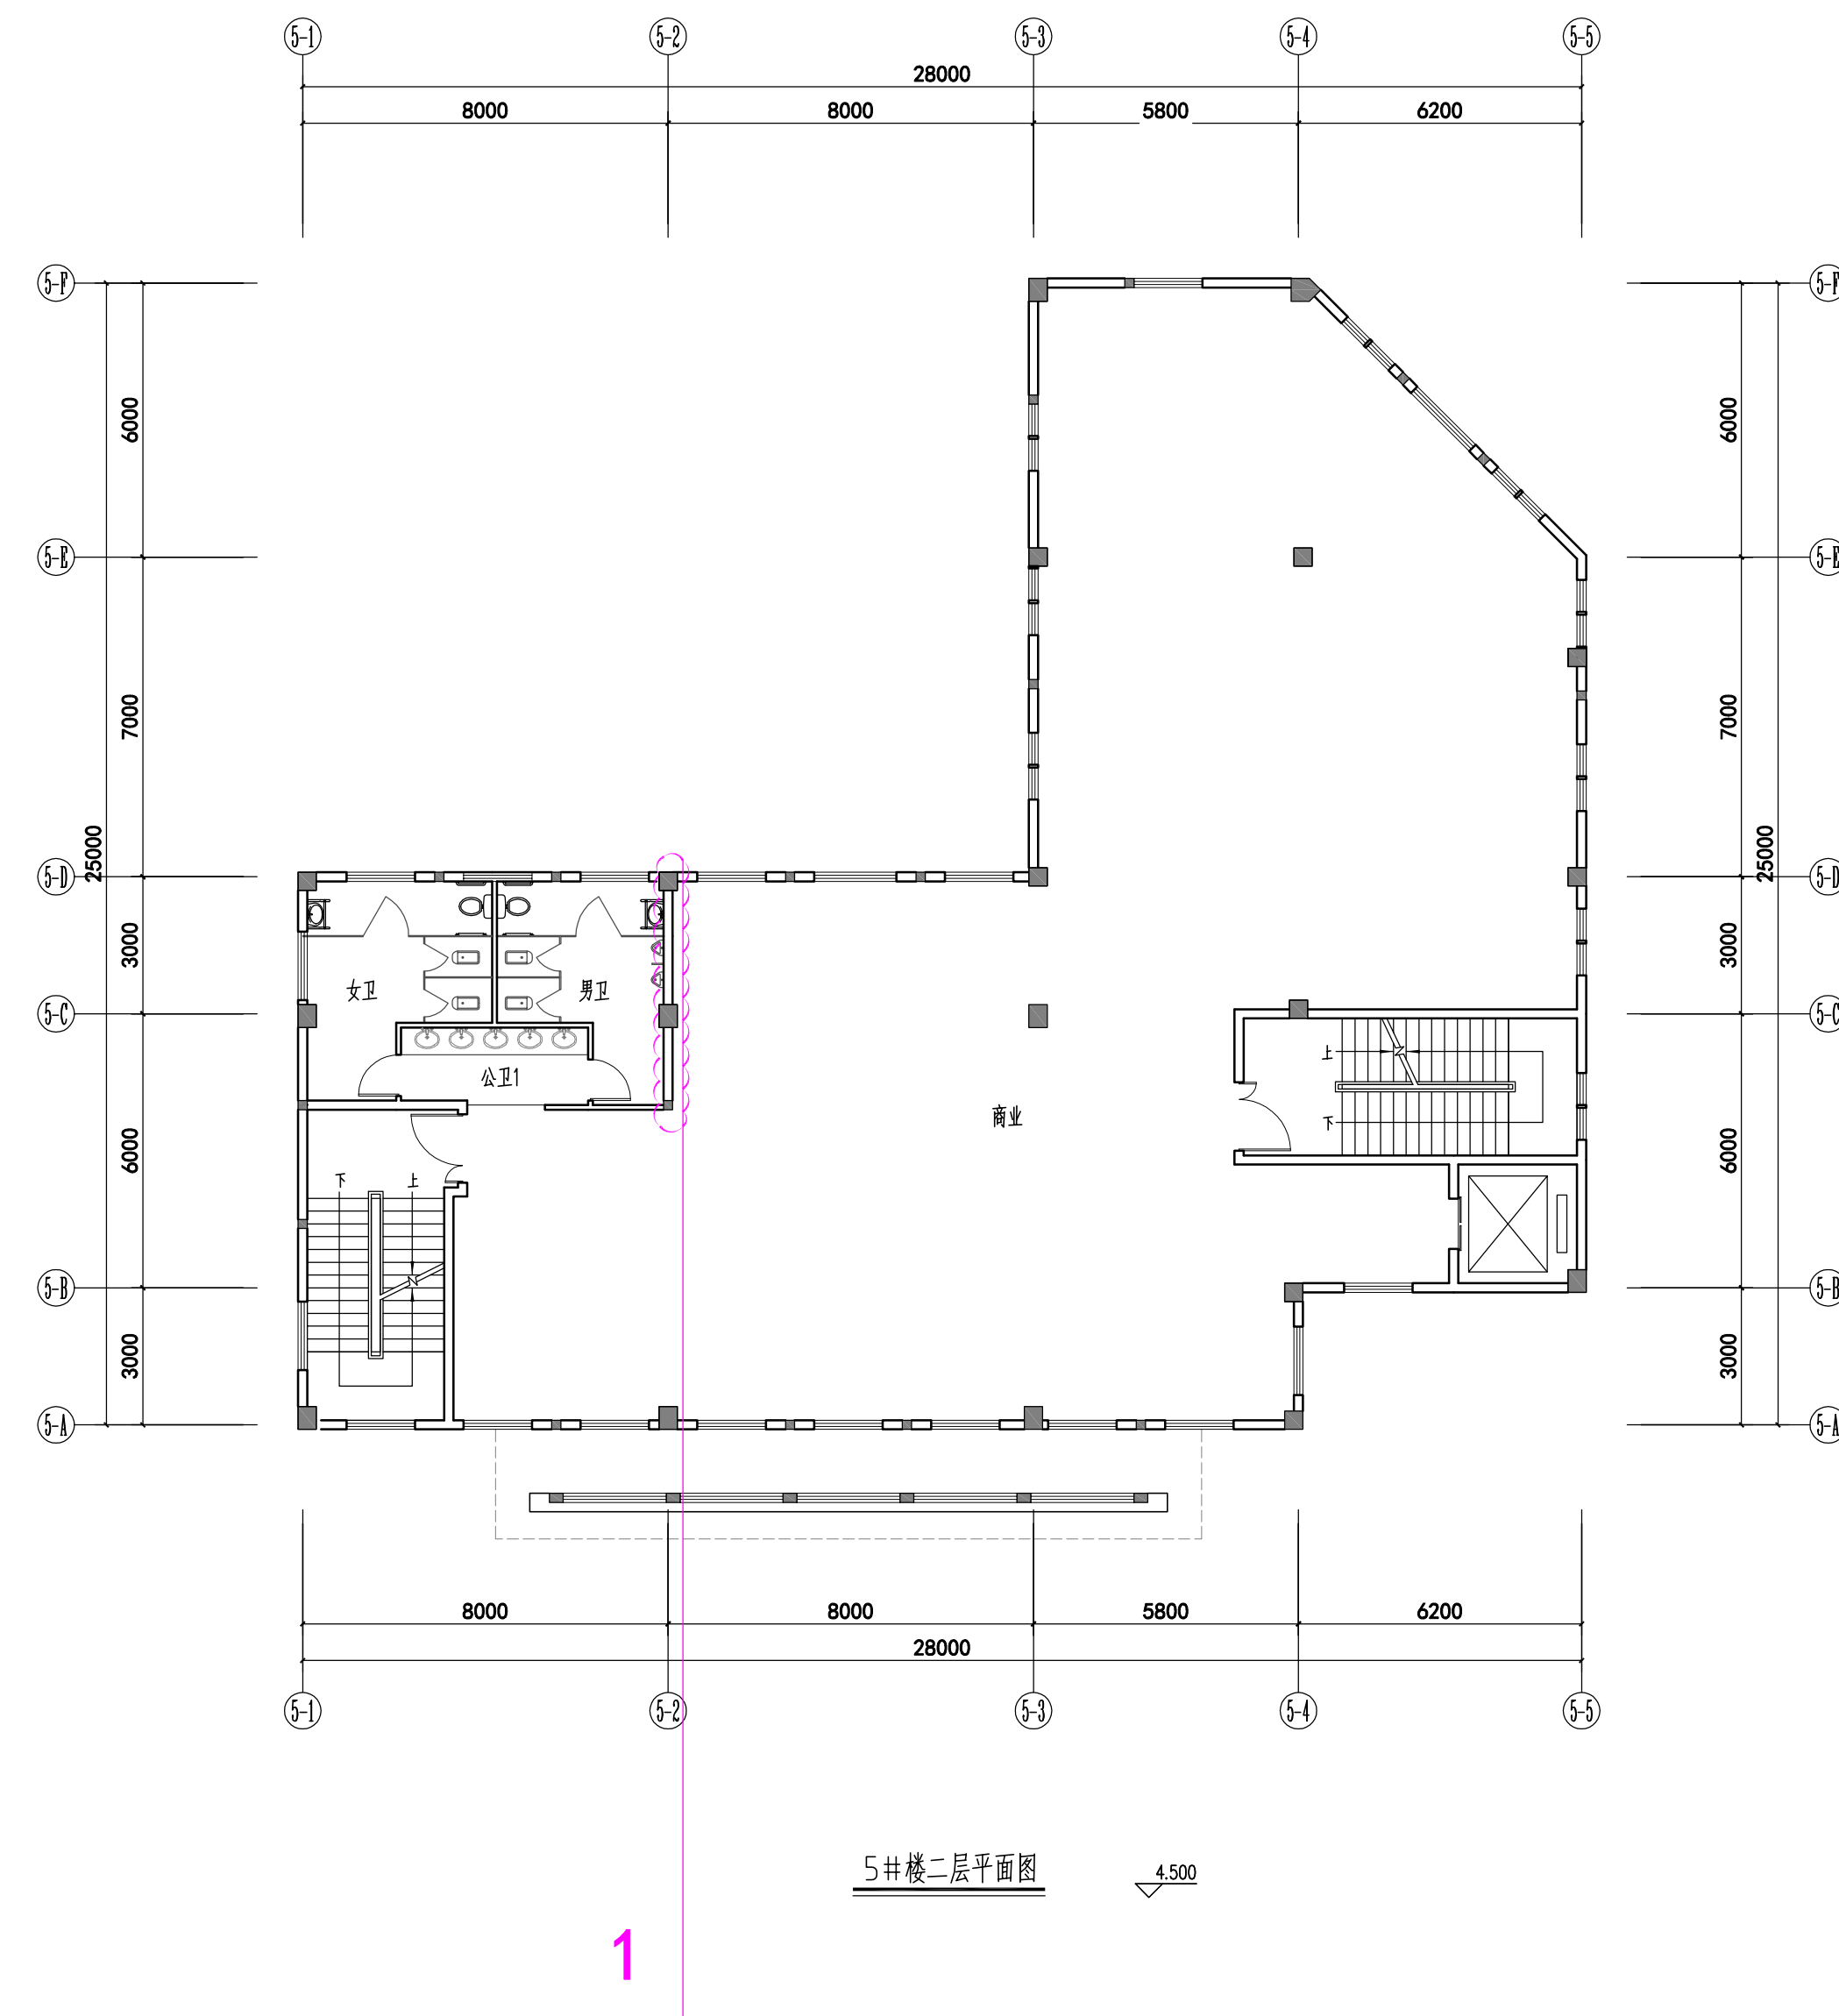

设计单位	福建一建集团有限公司	工程名称	荆东安置房及周边附属配套工程项目（学生街）	图 名	5#楼二层平面图	图 别	方 案
						日 期	2024. 02


变更前

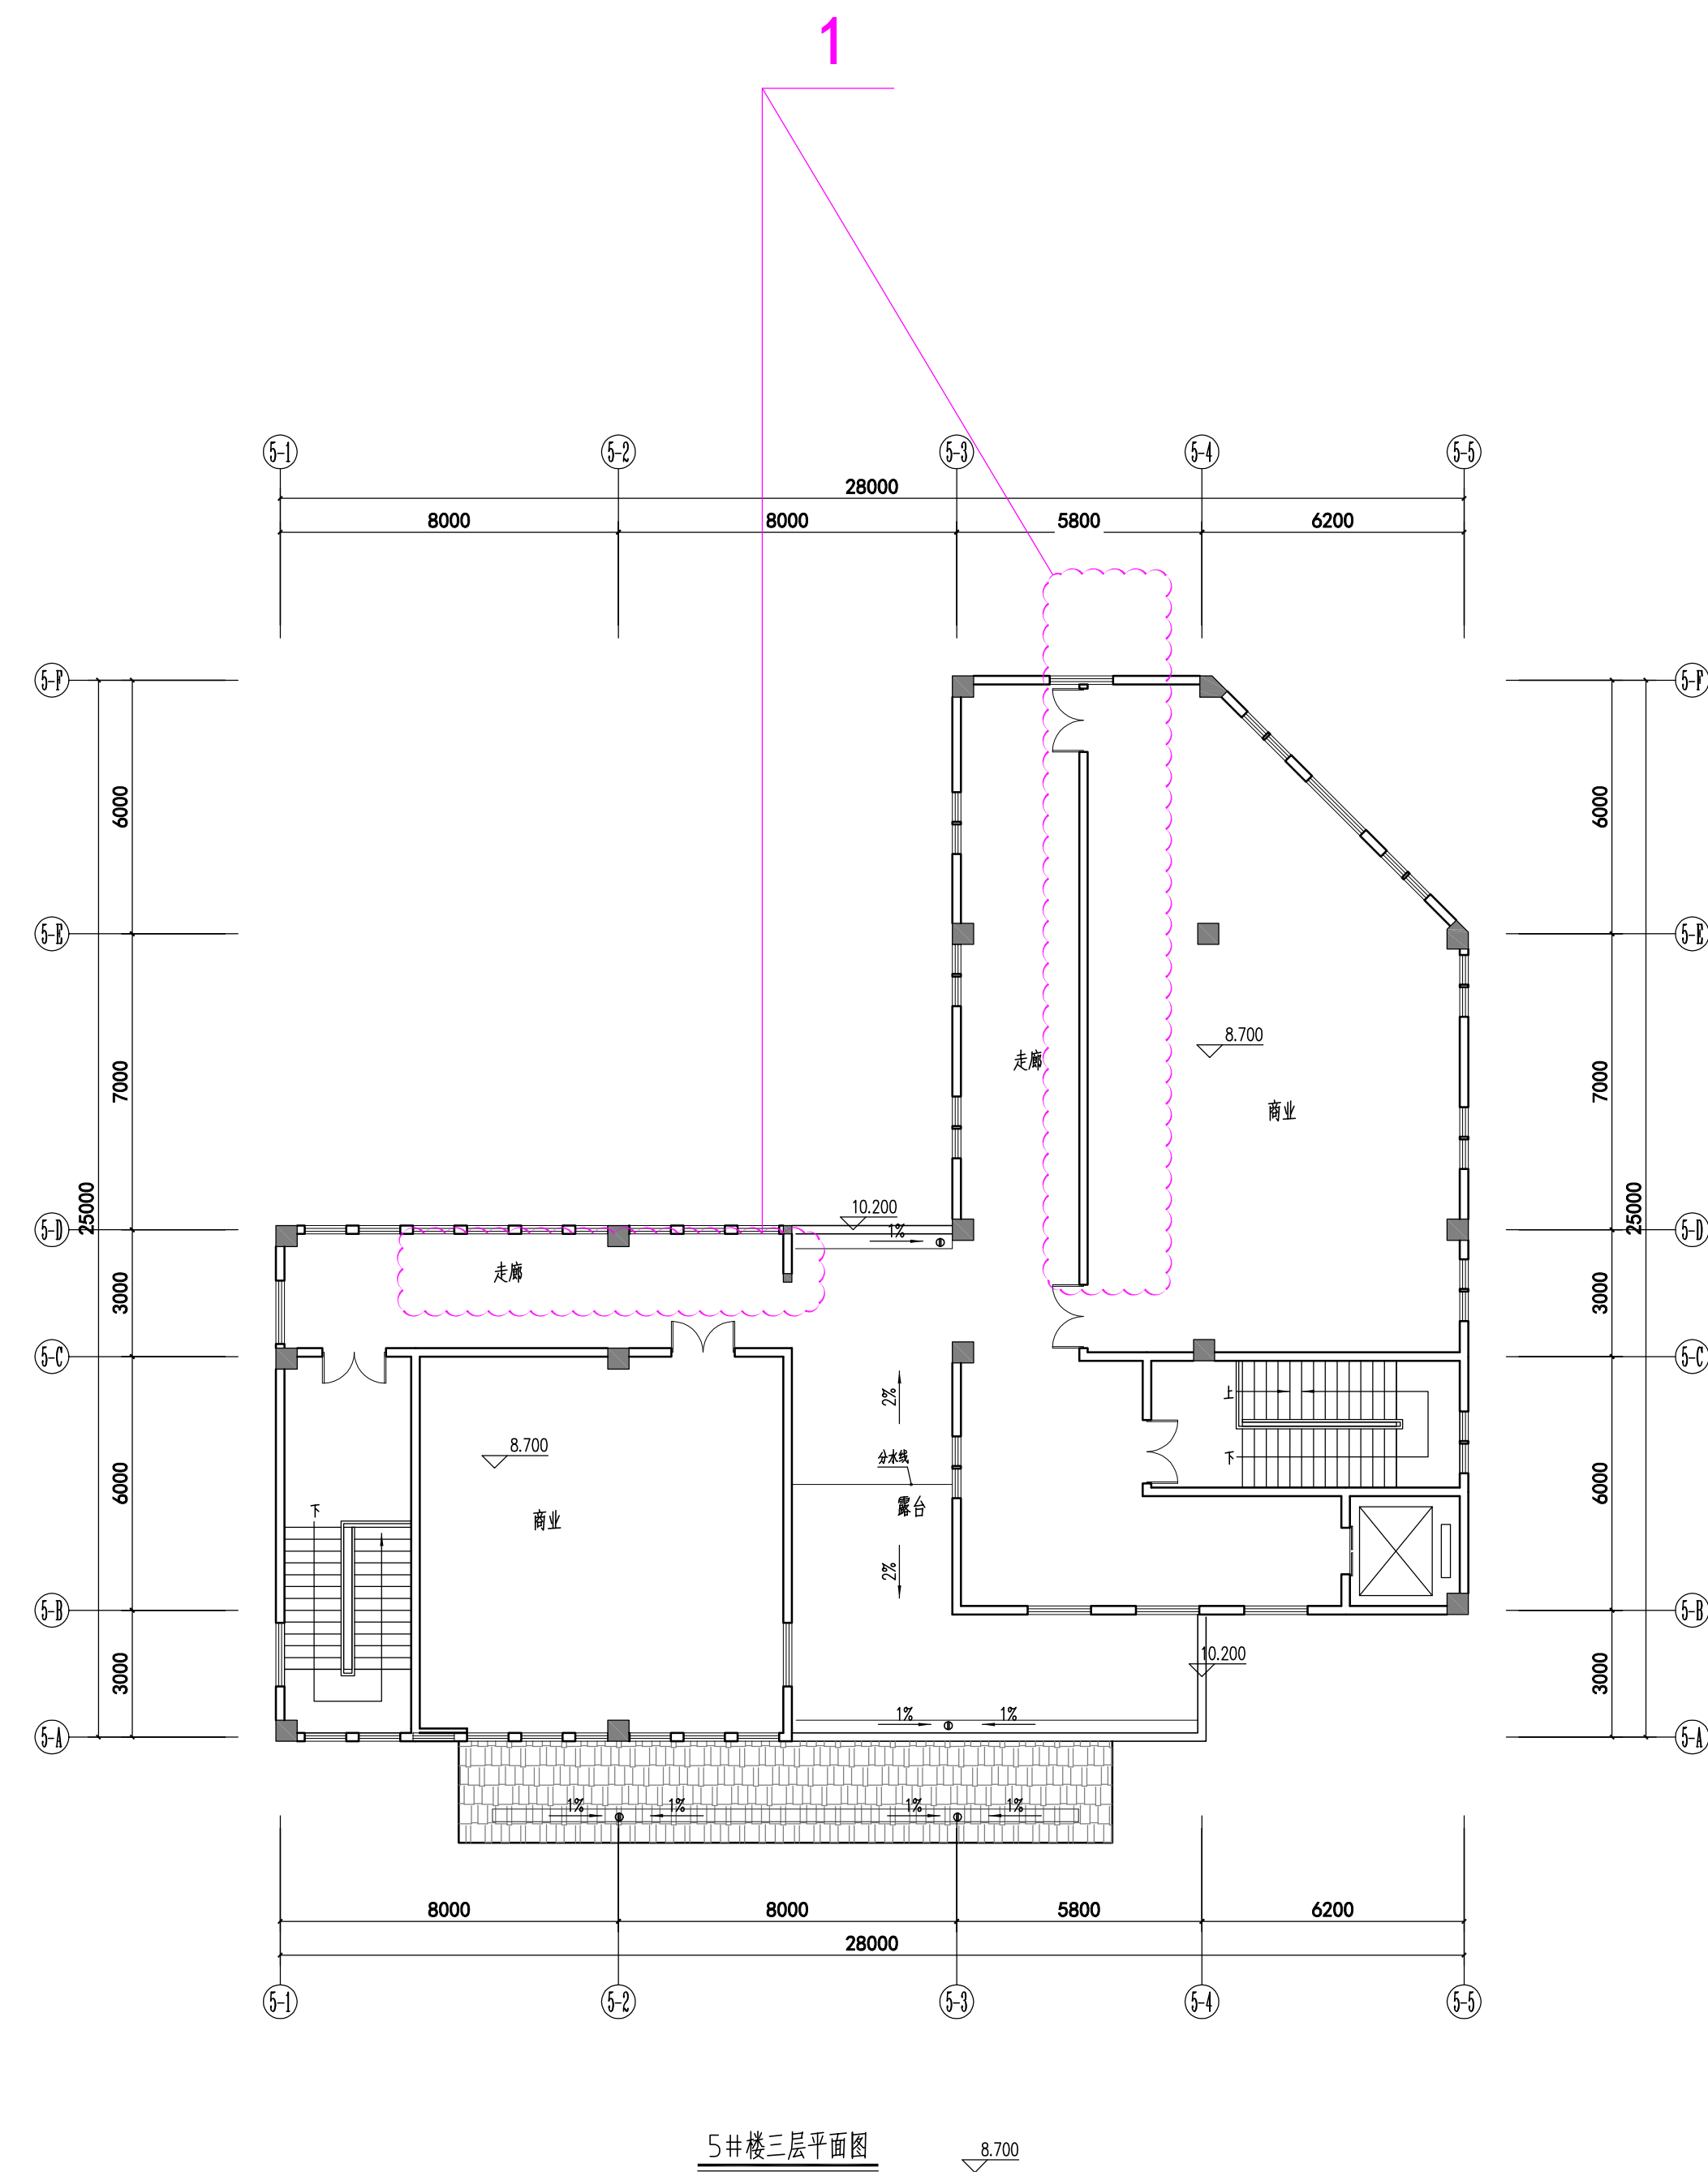

设计单位	福建一建集团有限公司	工程名称	荆东安置房及周边附属配套工程项目（学生街）	图 名	5#楼三层平面图	图 别	方 案
						日 期	2020. 10


变更后

1. 取消分隔墙体 and 门

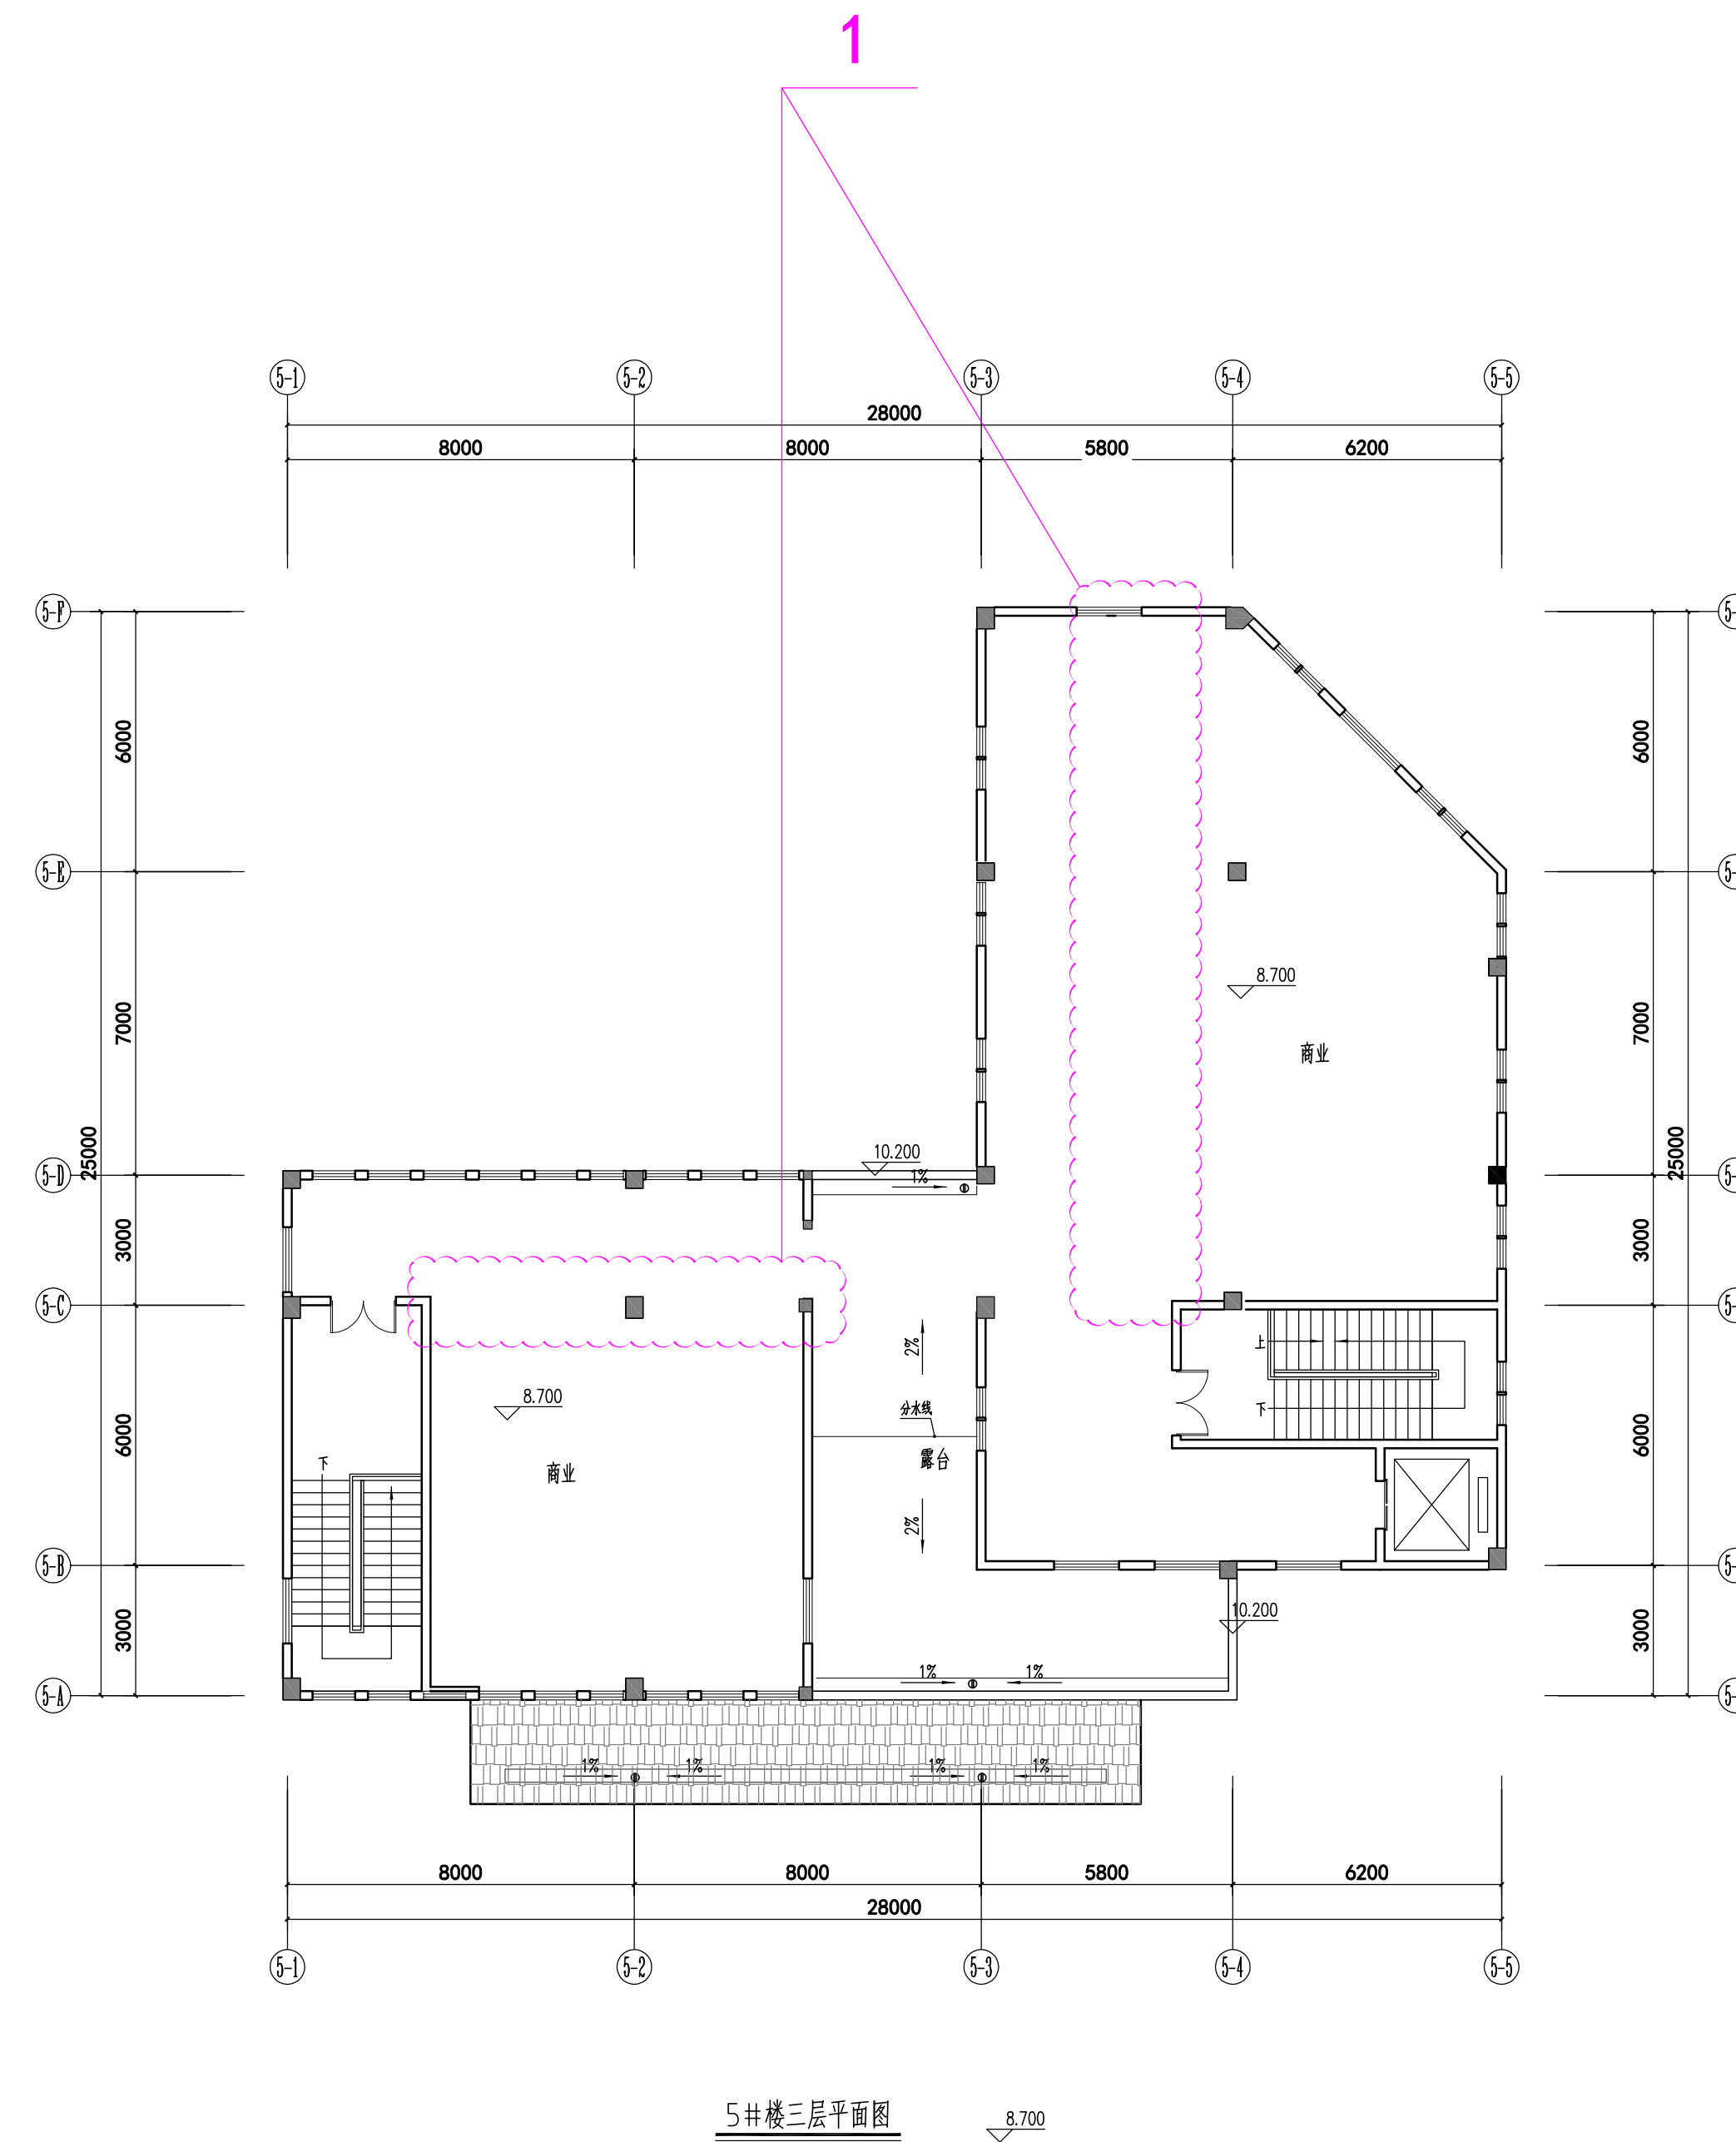

设计单位	福建一建集团有限公司	工程名称	荆东安置房及周边附属配套工程项目（学生街）	图 名	5#楼三层平面图	图 别	方 案
						日 期	2024. 02

变更前

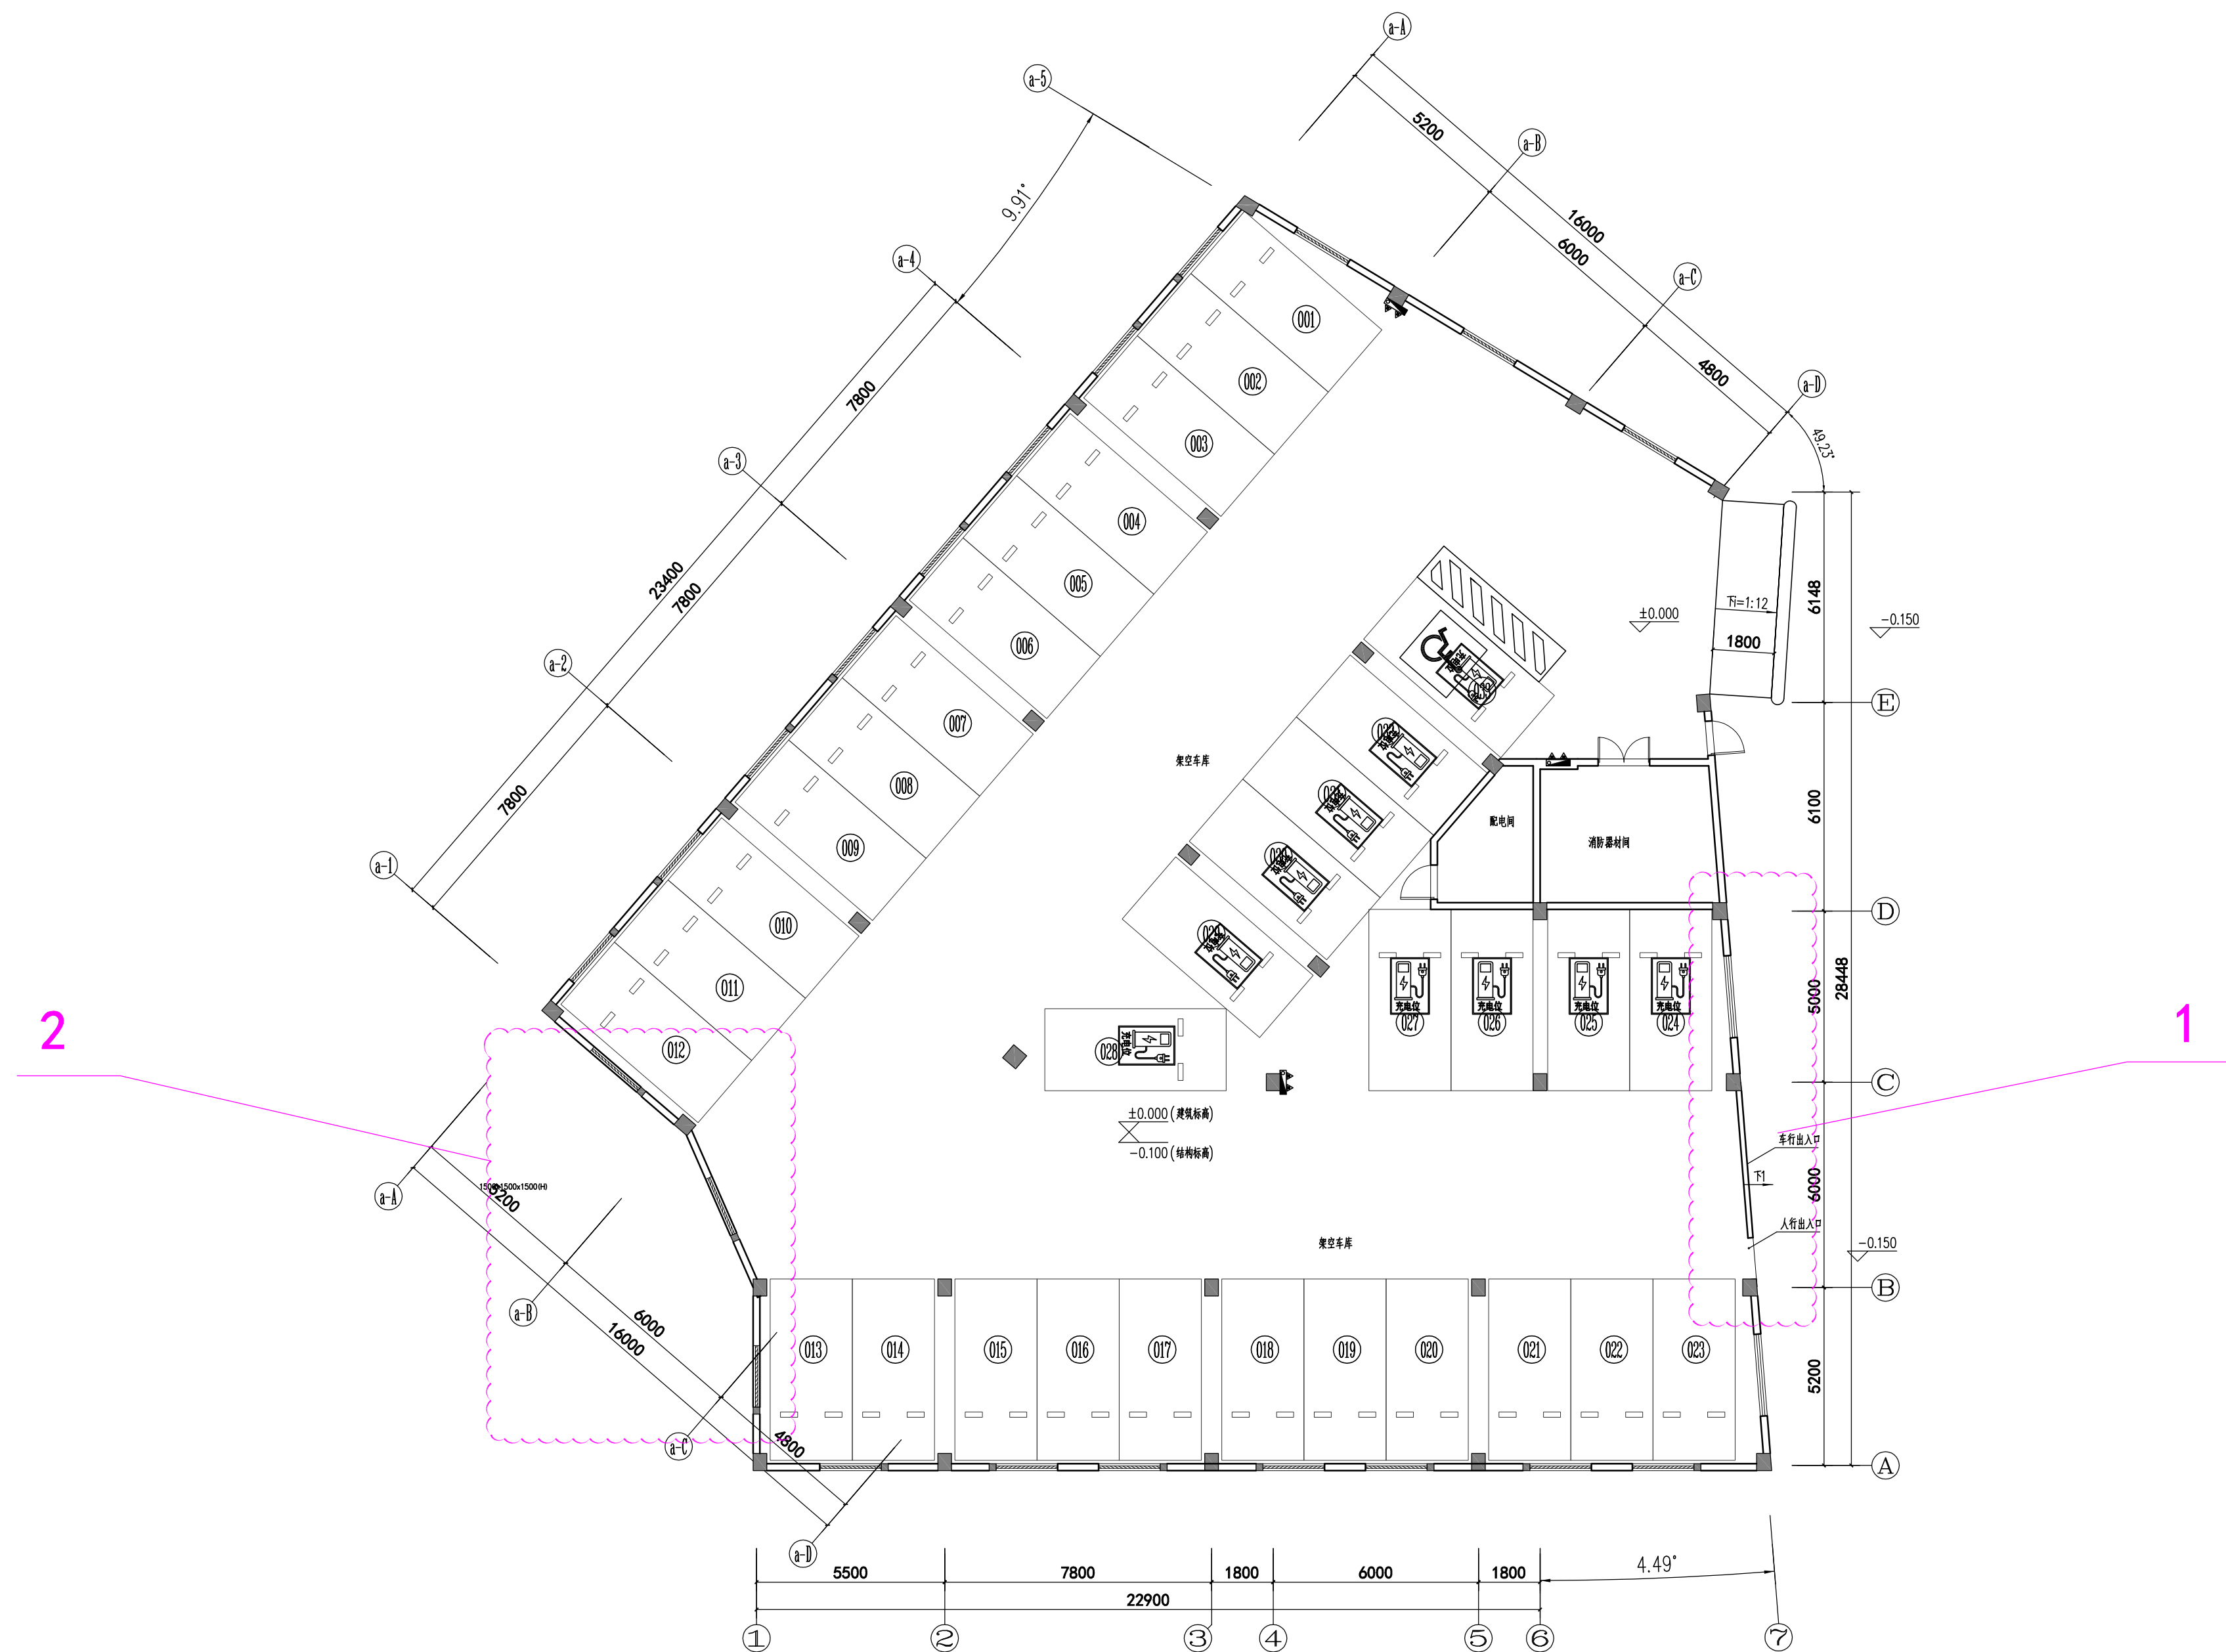


架空车库平面图 ± 0.000 (黄海高程139.05)

设计单位	福建一建集团有限公司	工程名称	荆东安置房及周边附属配套工程项目（学生街）	图 名	架空车库平面图	图 别	方 案
						日 期	2020. 10

变更后

1. 人行出入口改为车行出入口
2. a-A~a-D轴交a-1轴, 3处百叶窗取消

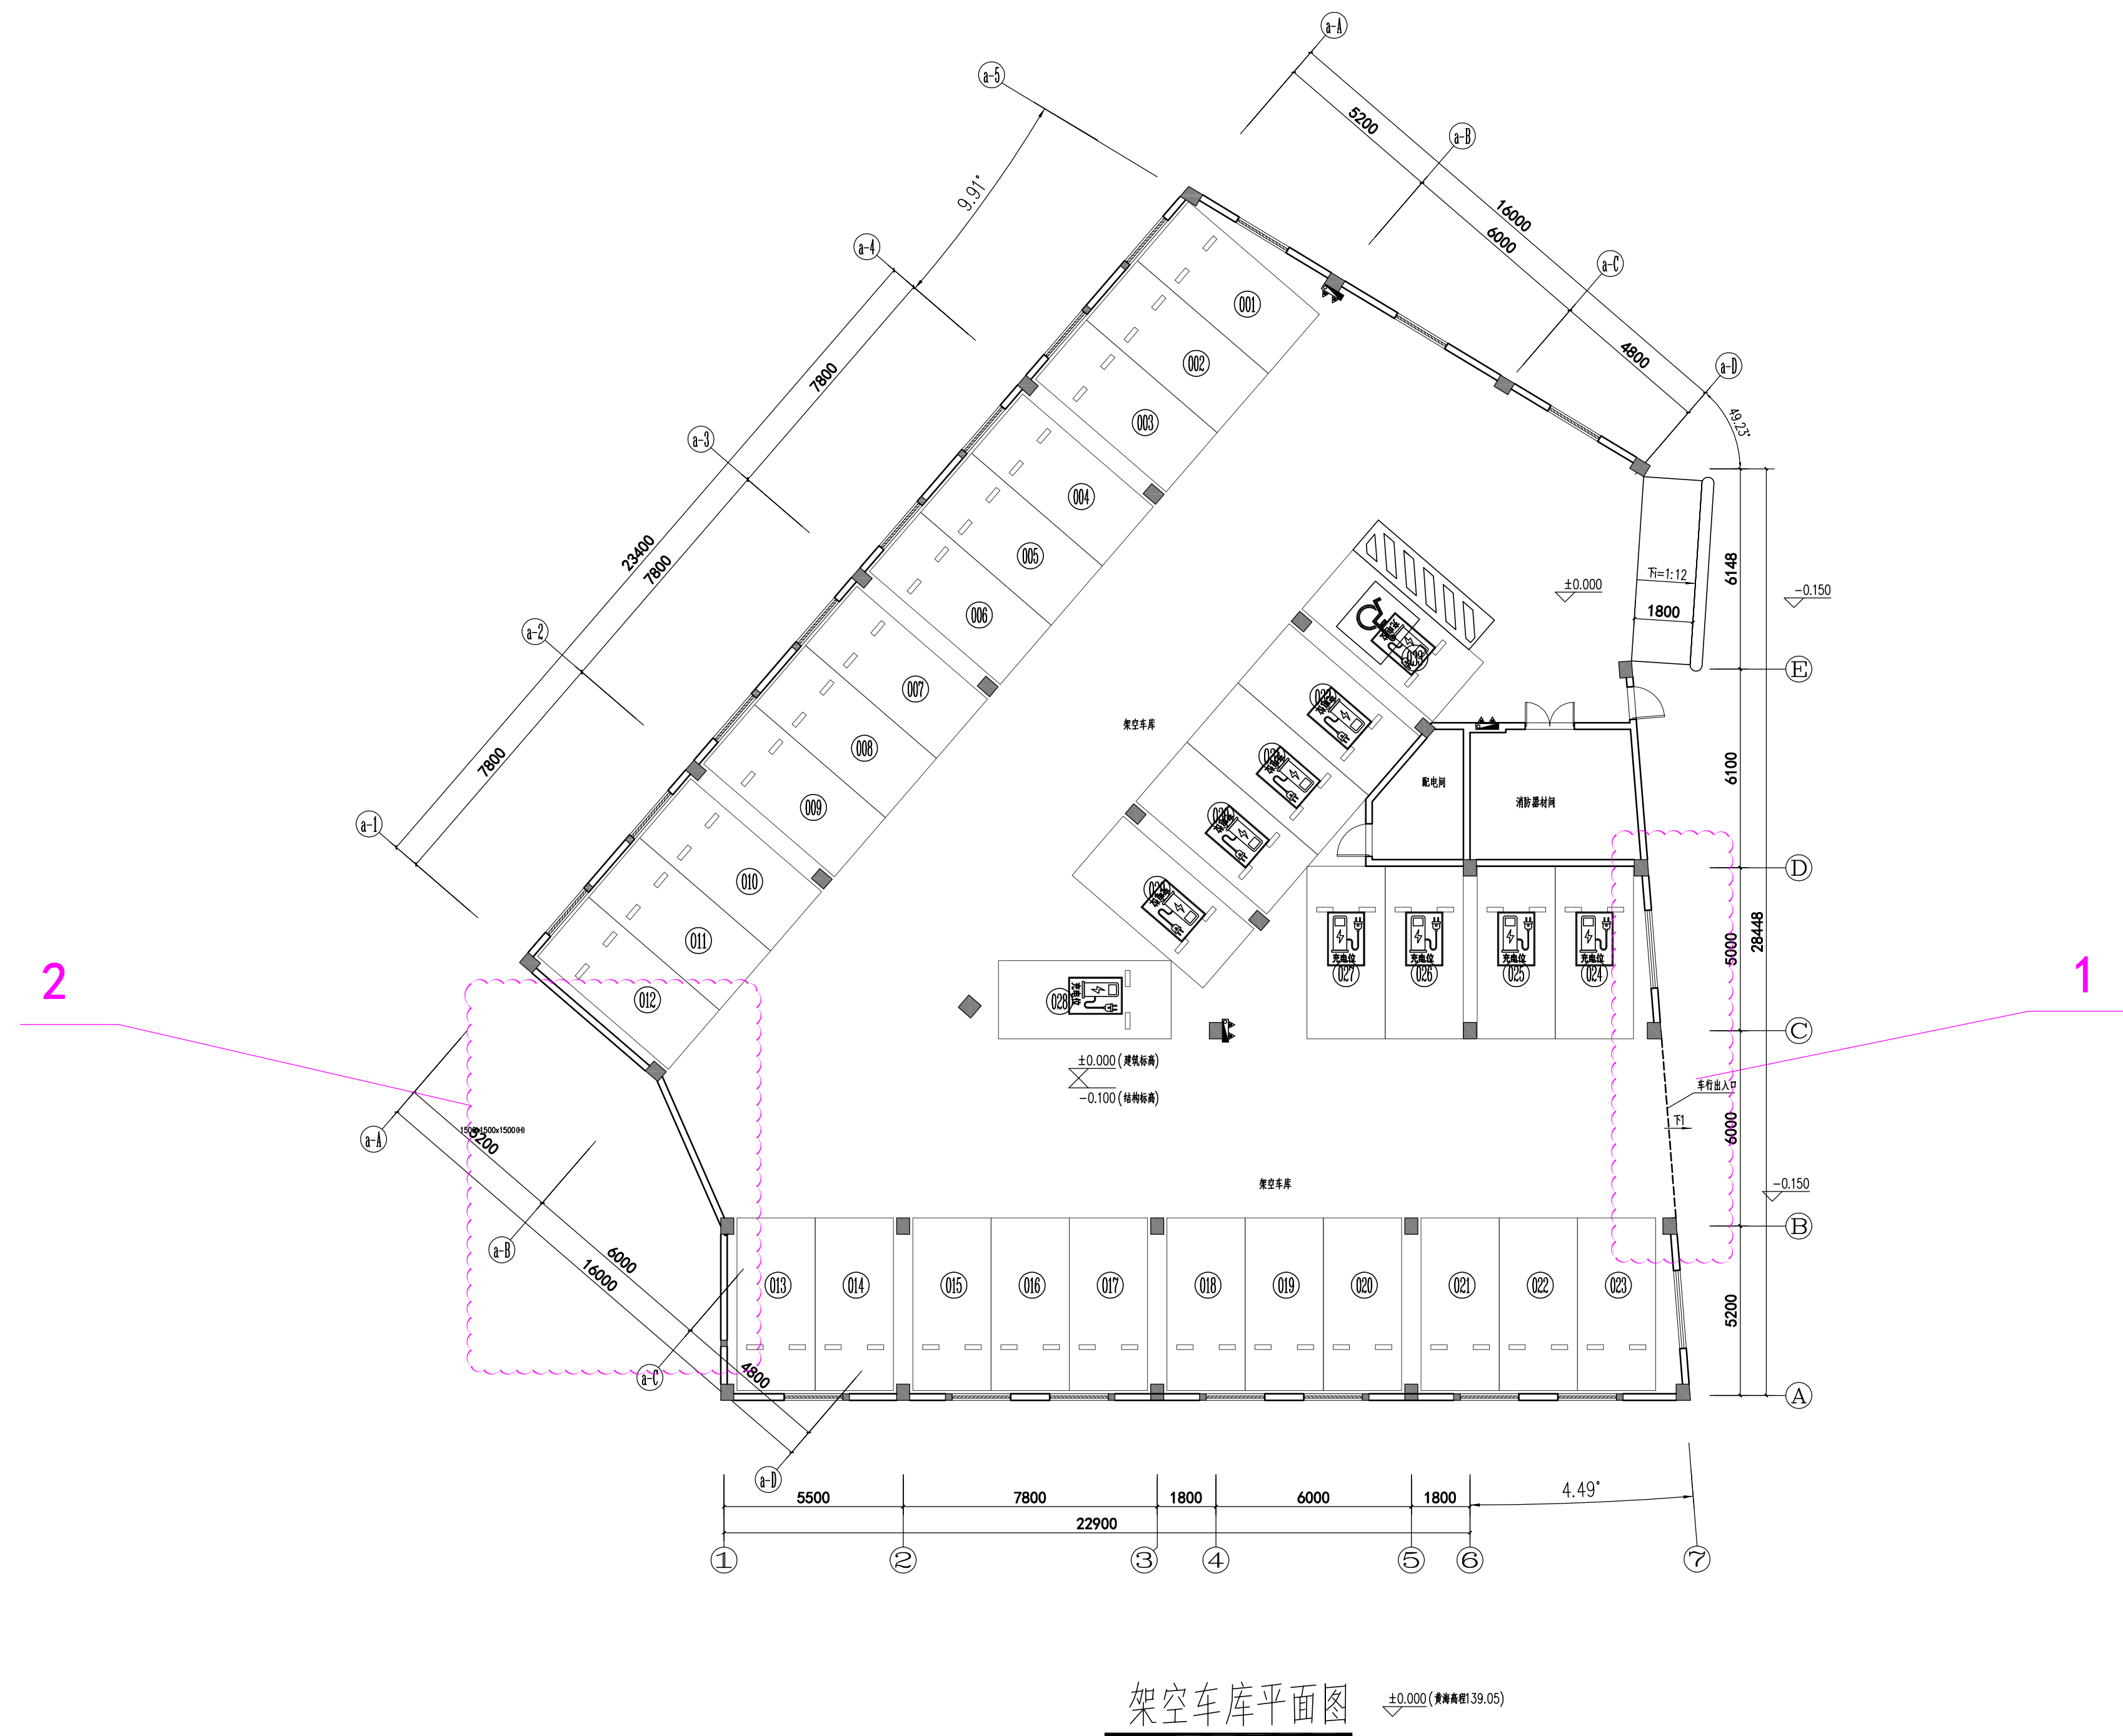

设计单位	福建一建集团有限公司	工程名称	荆东安置房及周边附属配套工程项目（学生街）	图 名	架空车库平面图	图 别	方 案
						日 期	2024. 01