


设计修改变更通知

建设单位	三明市沙县区虬江街道金泉村股份经济合作社	主送单位	建设单位						
工程名称	沙县如意苑商务中心建设项目	抄送单位	质检 监理 施工单位						
工程编号	2022-05	发文日期	2023 年 02 月 15 日						
更改理由	1 . 原设计图纸错、漏、碰、缺的更正。 √ 6 . 建设单位要求更改。 2 . 原设计计算的更正。 7 . 施工单位要求更改。 √ 3 . 原构造设计的改进或完善。 8 . 施工条件变化。 4 . 其它工种设计人员要求配合更改。 √ 9 . 施工图审查意见。 5 . 地质条件与原资料有出入造成的修改。 10 . 规划部门审查意见。								
	应建设单位要求, 变更如下: 1 A栋、B栋、C栋地下室③轴~⑤轴交 ① 轴~⑧轴增设一个机动车位, 地下室机动车位63个改为64个。 2 A栋、B栋、C栋地下室⑩轴~⑪轴交 ① 轴~⑧轴车位改排烟机房及排烟竖井, 满足地下室自然机械排烟要求。 3 A栋、B栋、C栋地下室⑩轴~⑪轴交 ① 轴~⑧轴电梯出口增设电梯候梯厅, 满足地下室电梯出口要求。 4 A栋、B栋、C栋地下室⑦轴~⑪轴交 ① 轴~⑧轴电梯出口增设电梯候梯厅和通道, 满足地下室电梯出口要求。 5 A栋、B栋、C栋地下室水泵房右移, 增设控制室, 满足地下室设备房独立防火分区要求。 6 A栋、B栋、C栋地下室⑧轴交 ⑧轴 轴风机房取消, 增设排烟竖井, 满足地下室机械排烟要求。 7 A栋、B栋、C栋地下室消防水池加大, ⑧轴~⑨轴交 ⑧轴~⑨轴为加大部位 , 满足消防水池的用水容量要求。 8 A栋一层大堂增设残卫, 男女厕所做相应调整。 9 A栋一层增设发电机房, 配电房加大。消控室调整到B栋一层。 10 A栋一层 ⑧轴处增设砖墙, 一间商铺改为两间商铺。 11 A栋二层厕所改为管理用房, 包间改为客房, 餐厅改为客房, 厨房、包间改为管理用房。 12 A栋二~五层弱电井左边功能房取消, 满足本层走道自然通风、排烟要求。 13 B栋、C栋一层 ④轴~⑥轴交 ① 轴~⑧轴和 ②①轴~②②轴交 ① 轴~⑧轴商铺内卫生间移位, 满足电井与用水房间不能相邻要求。门厅内增设残卫, 满足残疾人无障碍规范要求。 14 B栋、C栋一层 ②④轴~②⑤轴交 ① 轴~⑧轴商铺改为消控室。 15 B栋、C栋三~五层南立面两侧边跨挑出部分缩短, 边跨中间竖向构造柱取消。 16 B栋、C栋三~五层侧立面窗户右移, 中间竖向构造柱取消, 两扇窗户改为一扇窗户, 窗户两侧增设百页空调位。 17 总平面右上脚小区道路做调整, 满足通行更顺畅的要求。 18 建筑北面到红线范围, 小区道路调整到中部, 两侧设绿化。 19 红线北侧接北面小区的铺地取消。 20 总平面东南角绿地改铺砌地砖。 21 绿地面积增加15. 27平方米, 绿地率由21. 37%增加为21. 68%。 22 本次变更后, 项目建筑面积增加: 48. 17平方米, 其中计容面积增减: 0. 00平方米, 不计容面积增加: 48. 17平方米。								
 福建境景建筑设计有限公司		审 定		项目负责		设 计		工程编号	2022-05
		审 核		专业负责		校 对		出图日期	2023. 02

图	号	01
图	名	负一层平面图
图	比	1:100
图	日	2022.05
图	人	张青军
图	审	张青军
图	校	张青军
图	核	张青军
图	设	张青军
图	制	张青军

负一层平面图 变更前

 

单位名称：

福建境景

建筑设计有限公司

图例乙类：A235005080

备 注：

施工图审查单位：

施工图审查合格书编号：

图纸专用章：

注册建筑师执业章：

注册结构师执业章：

工程名称：

沙县知意苑商务中心B栋、C栋

建设单位：三明市沙县区吴江街道金泉村股份经济合作社

审 定 张青军
工程负责人 郑功农
专业负责人 郑功农
审 核 张青军
校 对 张青军
设 计 徐思楠
制 图 徐思楠


图名：

负一层平面图

工程编号	2022-05
图 别	建 施
图 号	01
日 期	2022.02

姓名	姓	名	日期	专业	姓名	日期
魏 强	魏	强		给排水	罗香城	
梁 洲	梁	洲		电气	李斌	

负一层平面图 变更后

 

负一层平面图 1:100

单位名称:

 福建境景
建筑设计有限公司

建筑乙级: A235005080

备注:	
-----	--

施工图审查单位:

施工图审查合格书编号:

图纸专用章:

注册建筑师执业章

注册结构师执业章

工程名称:

沙县如意苑商务中心B栋、C栋

建设单位：三明市沙县区虬江街道金泉村
股份经济合作社

工程负责人	郑功农	郑功农
-------	-----	-----

三、四、五、六、七、八、九、十、十一、十二、十三、十四、十五、十六、十七、十八、十九、二十、二十一、二十二、二十三、二十四、二十五、二十六、二十七、二十八、二十九、三十、三十一、三十二、三十三、三十四、三十五、三十六、三十七、三十八、三十九、四十、四十一、四十二、四十三、四十四、四十五、四十六、四十七、四十八、四十九、五十、五十一、五十二、五十三、五十四、五十五、五十六、五十七、五十八、五十九、六十、六十一、六十二、六十三、六十四、六十五、六十六、六十七、六十八、六十九、七十、七十一、七十二、七十三、七十四、七十五、七十六、七十七、七十八、七十九、八十、八十一、八十二、八十三、八十四、八十五、八十六、八十七、八十八、八十九、九十、九十一、九十二、九十三、九十四、九十五、九十六、九十七、九十八、九十九、一百	郑功成	郑功成
由业负责人	郑功成	郑功成

2. 王興興人	鄭功秋	2008
宋 楠	劉 傑	2008

甲 核	张 通 京	
核 对	李 林 洲	

校 对	张 善 军	
		11月10日

设计	徐恩辉	徐恩辉


图名:

负一层平面图

工程编号	2022-06
图 别	建 施
图 号	02
日 期	2023.02

专业	建筑	姓名	张善军	职称	注册建筑师
专业	结构	姓名	张善军	职称	注册结构师
专业	给排水	姓名	张善军	职称	注册给排水工程师
专业	暖通	姓名	张善军	职称	注册暖通工程师
专业	电气	姓名	张善军	职称	注册电气工程师
专业	其他	姓名	张善军	职称	注册其他工程师

A栋一层平面图 变更前

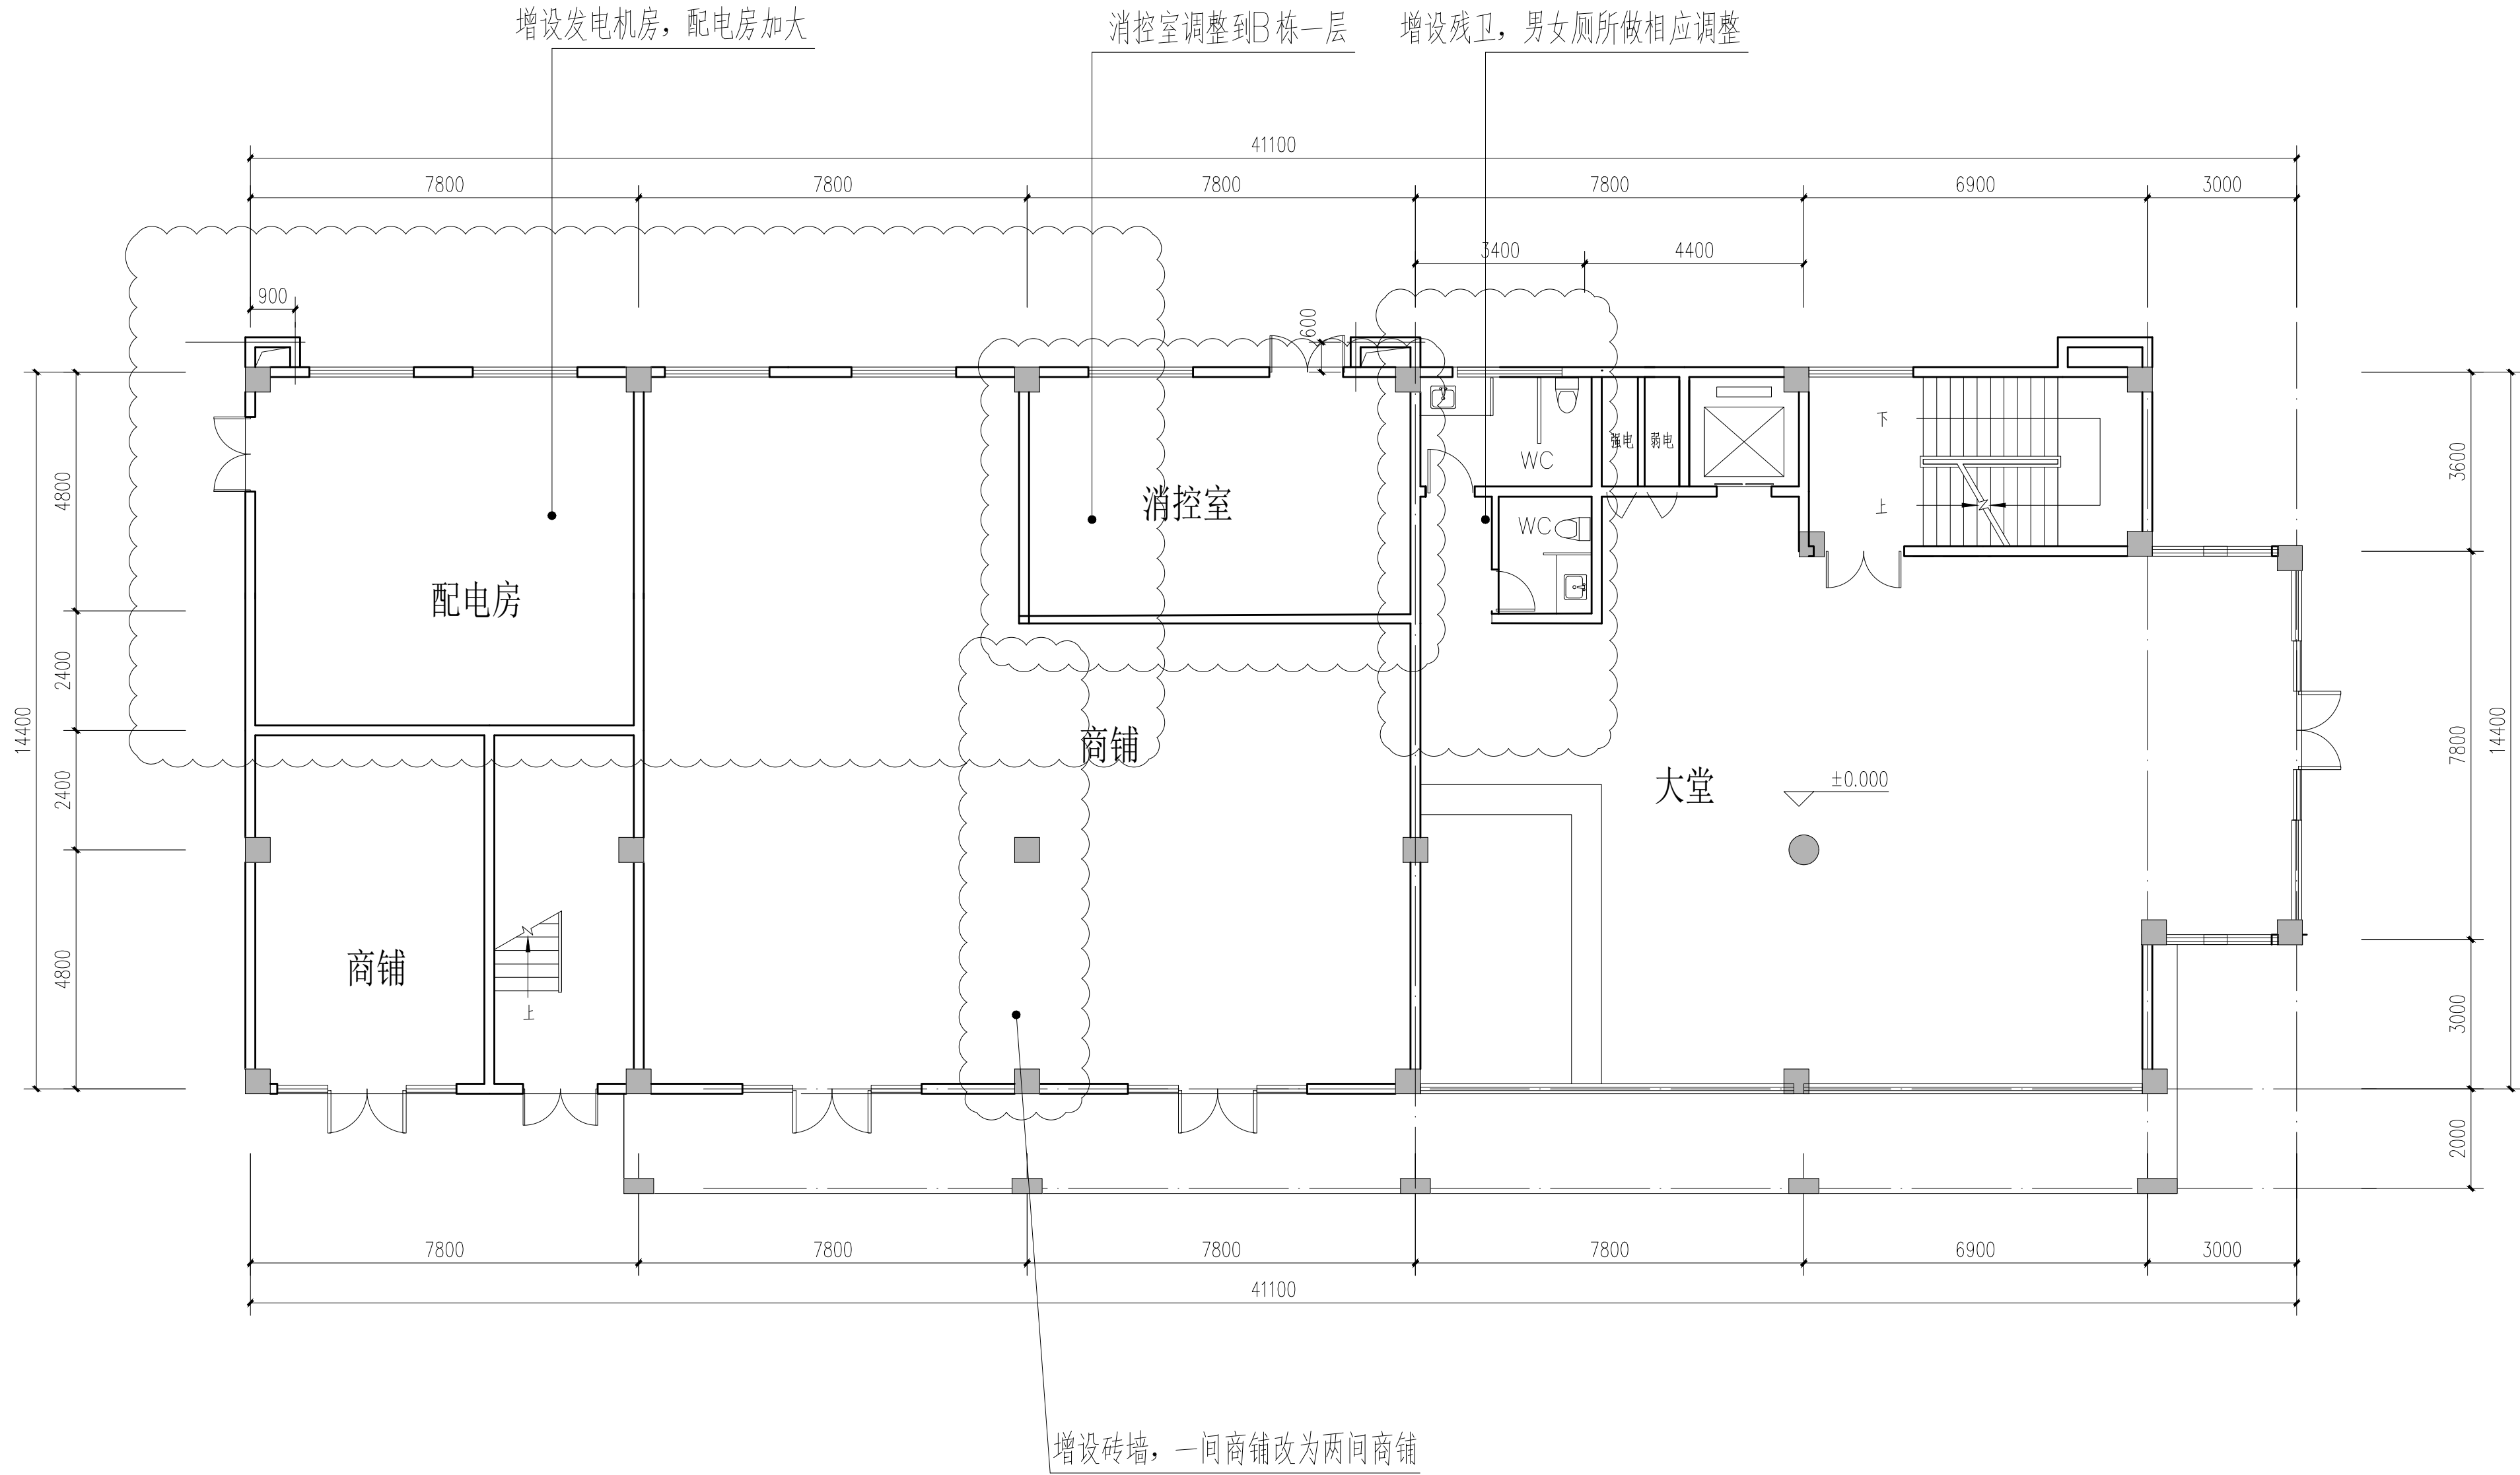

一层平面图（33井幢）


单位名称： 福建境景 建筑设计有限公司 建筑乙级：A235005080	
备 注：	
施工图审查单位：	
施工图审查合格书编号：	
图纸专用章：	
注册建筑师执业章：	
注册结构师执业章：	
工程名称： 沙县如意苑商务中心A栋	
建设单位：三明市沙县区虬江街道金泉村 股份经济合作社	
审 定	张 善 军
工程负责人	郑功农
专业负责人	郑功农
审 核	张 绳 景
校 对	张 善 军
设 计	徐 恩 辉
制 图	徐 恩 辉
图名： 一层平面图	
工程编号	2022-05
图 别	建 施
图 号	03
日 期	2023.02

[illegible]

建筑设计有限公司

备 注:


工程编号	2022-05
图 别	建 施
图 号	04
日 期	2023.02

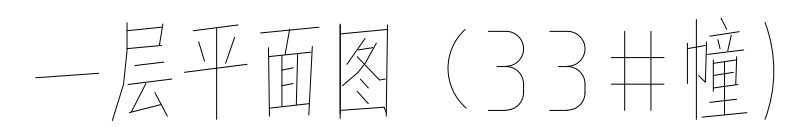


[illegible]

建筑乙级: A235005080

工程编号	2022-05
图 别	建 施
图 号	05
日 期	2023.02

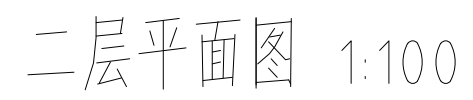

A栋二层平面图 变更后

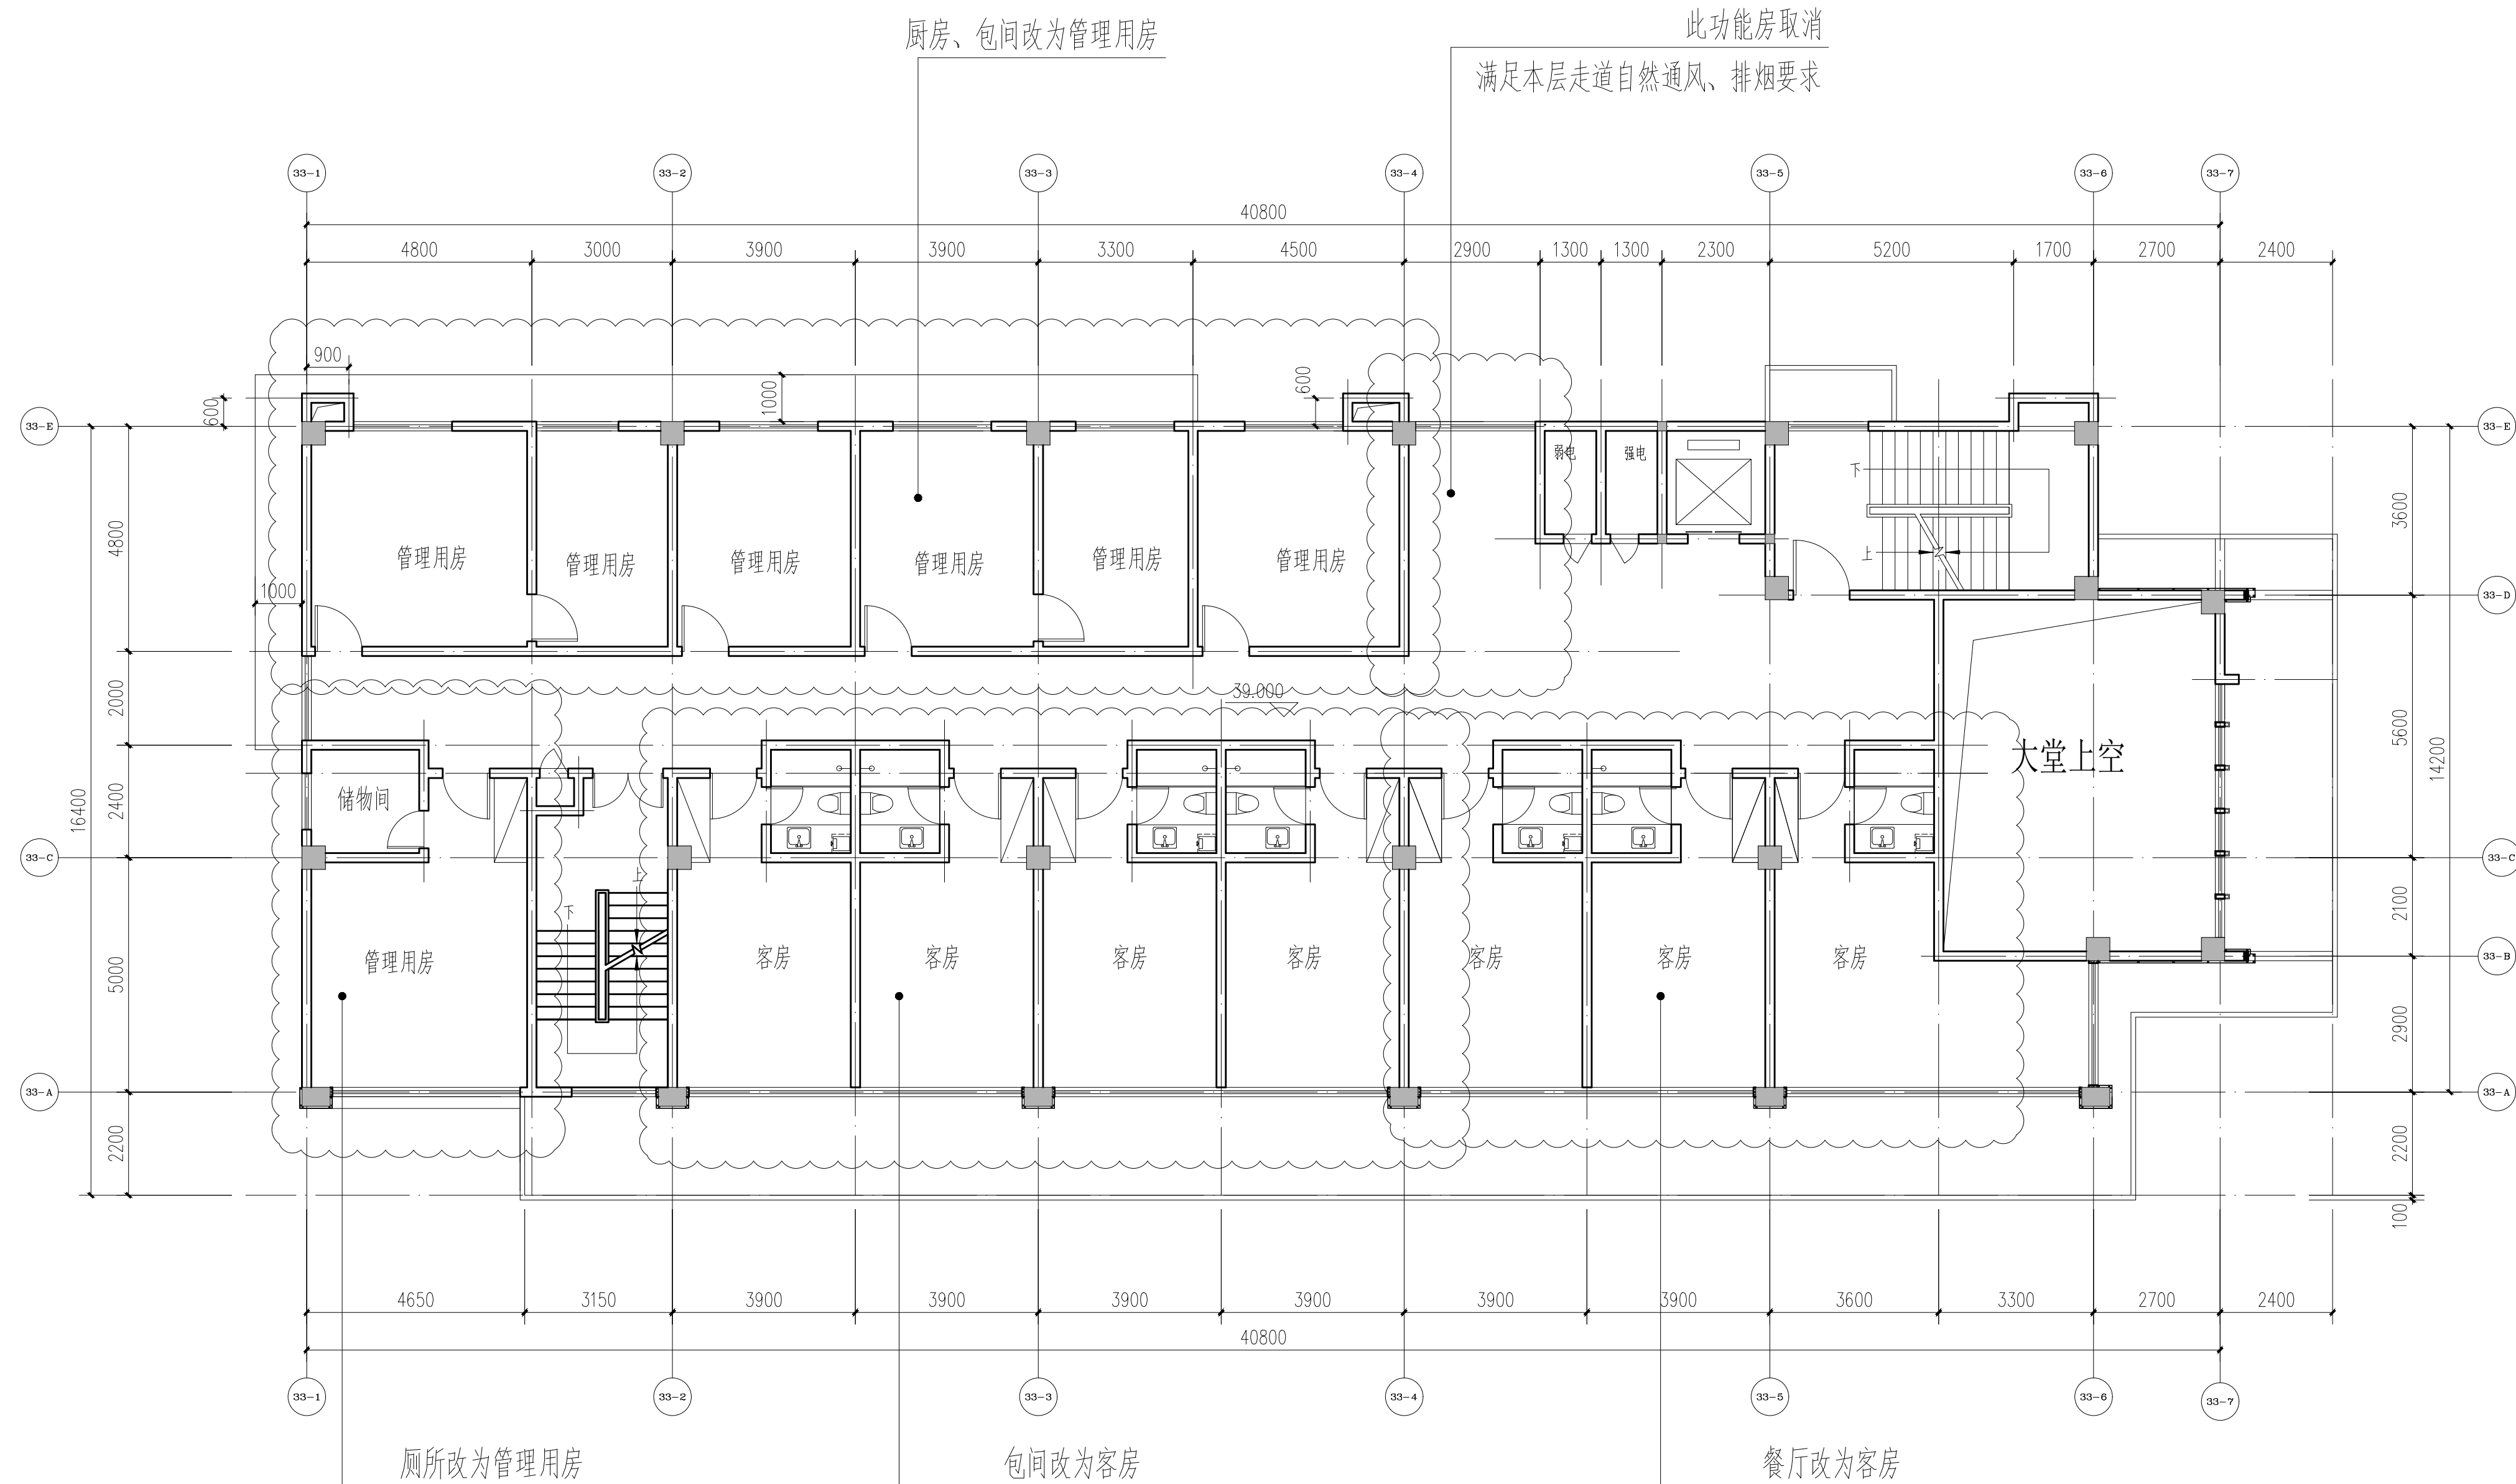

二层平面图 1:100

单位名称:

福建境景
建筑设计有限公司

建筑乙级: A235005080

备注:

施工图审查单位:

施工图审查合格书编号:

图纸专用章:

注册建筑师执业章:

注册结构师执业章:

工程名称:

沙县如意苑商务中心A栋

建设单位: 三明市沙县区虬江街道金泉村
股份经济合作社

审 定	张 善 军	张善军
工程负责人	郑功农	郑功农
专业负责人	郑功农	郑功农
审 核	张 绳 景	张绳景
校 对	张 善 军	张善军
设 计	徐 恩 辉	徐恩辉
制 图	徐 恩 辉	徐恩辉


图名:

二层平面图

工程编号	2022-05
图 别	建 施
图 号	06
日 期	2023.02

姓名	张永福
性别	男
出生日期	1980-06-17
籍贯	安徽六安
民族	汉族
学历	本科
学位	学士
专业名称	电气工程及其自动化
毕业院校	安徽工程大学
联系电话	13956610000
电子邮箱	zhangyongfu@ahut.edu.cn
联系地址	安徽省芜湖市弋江区南陵县经济开发区
邮政编码	241000

工程编号	2022-05
图 别	建 施
图 号	07
日 期	2023.02

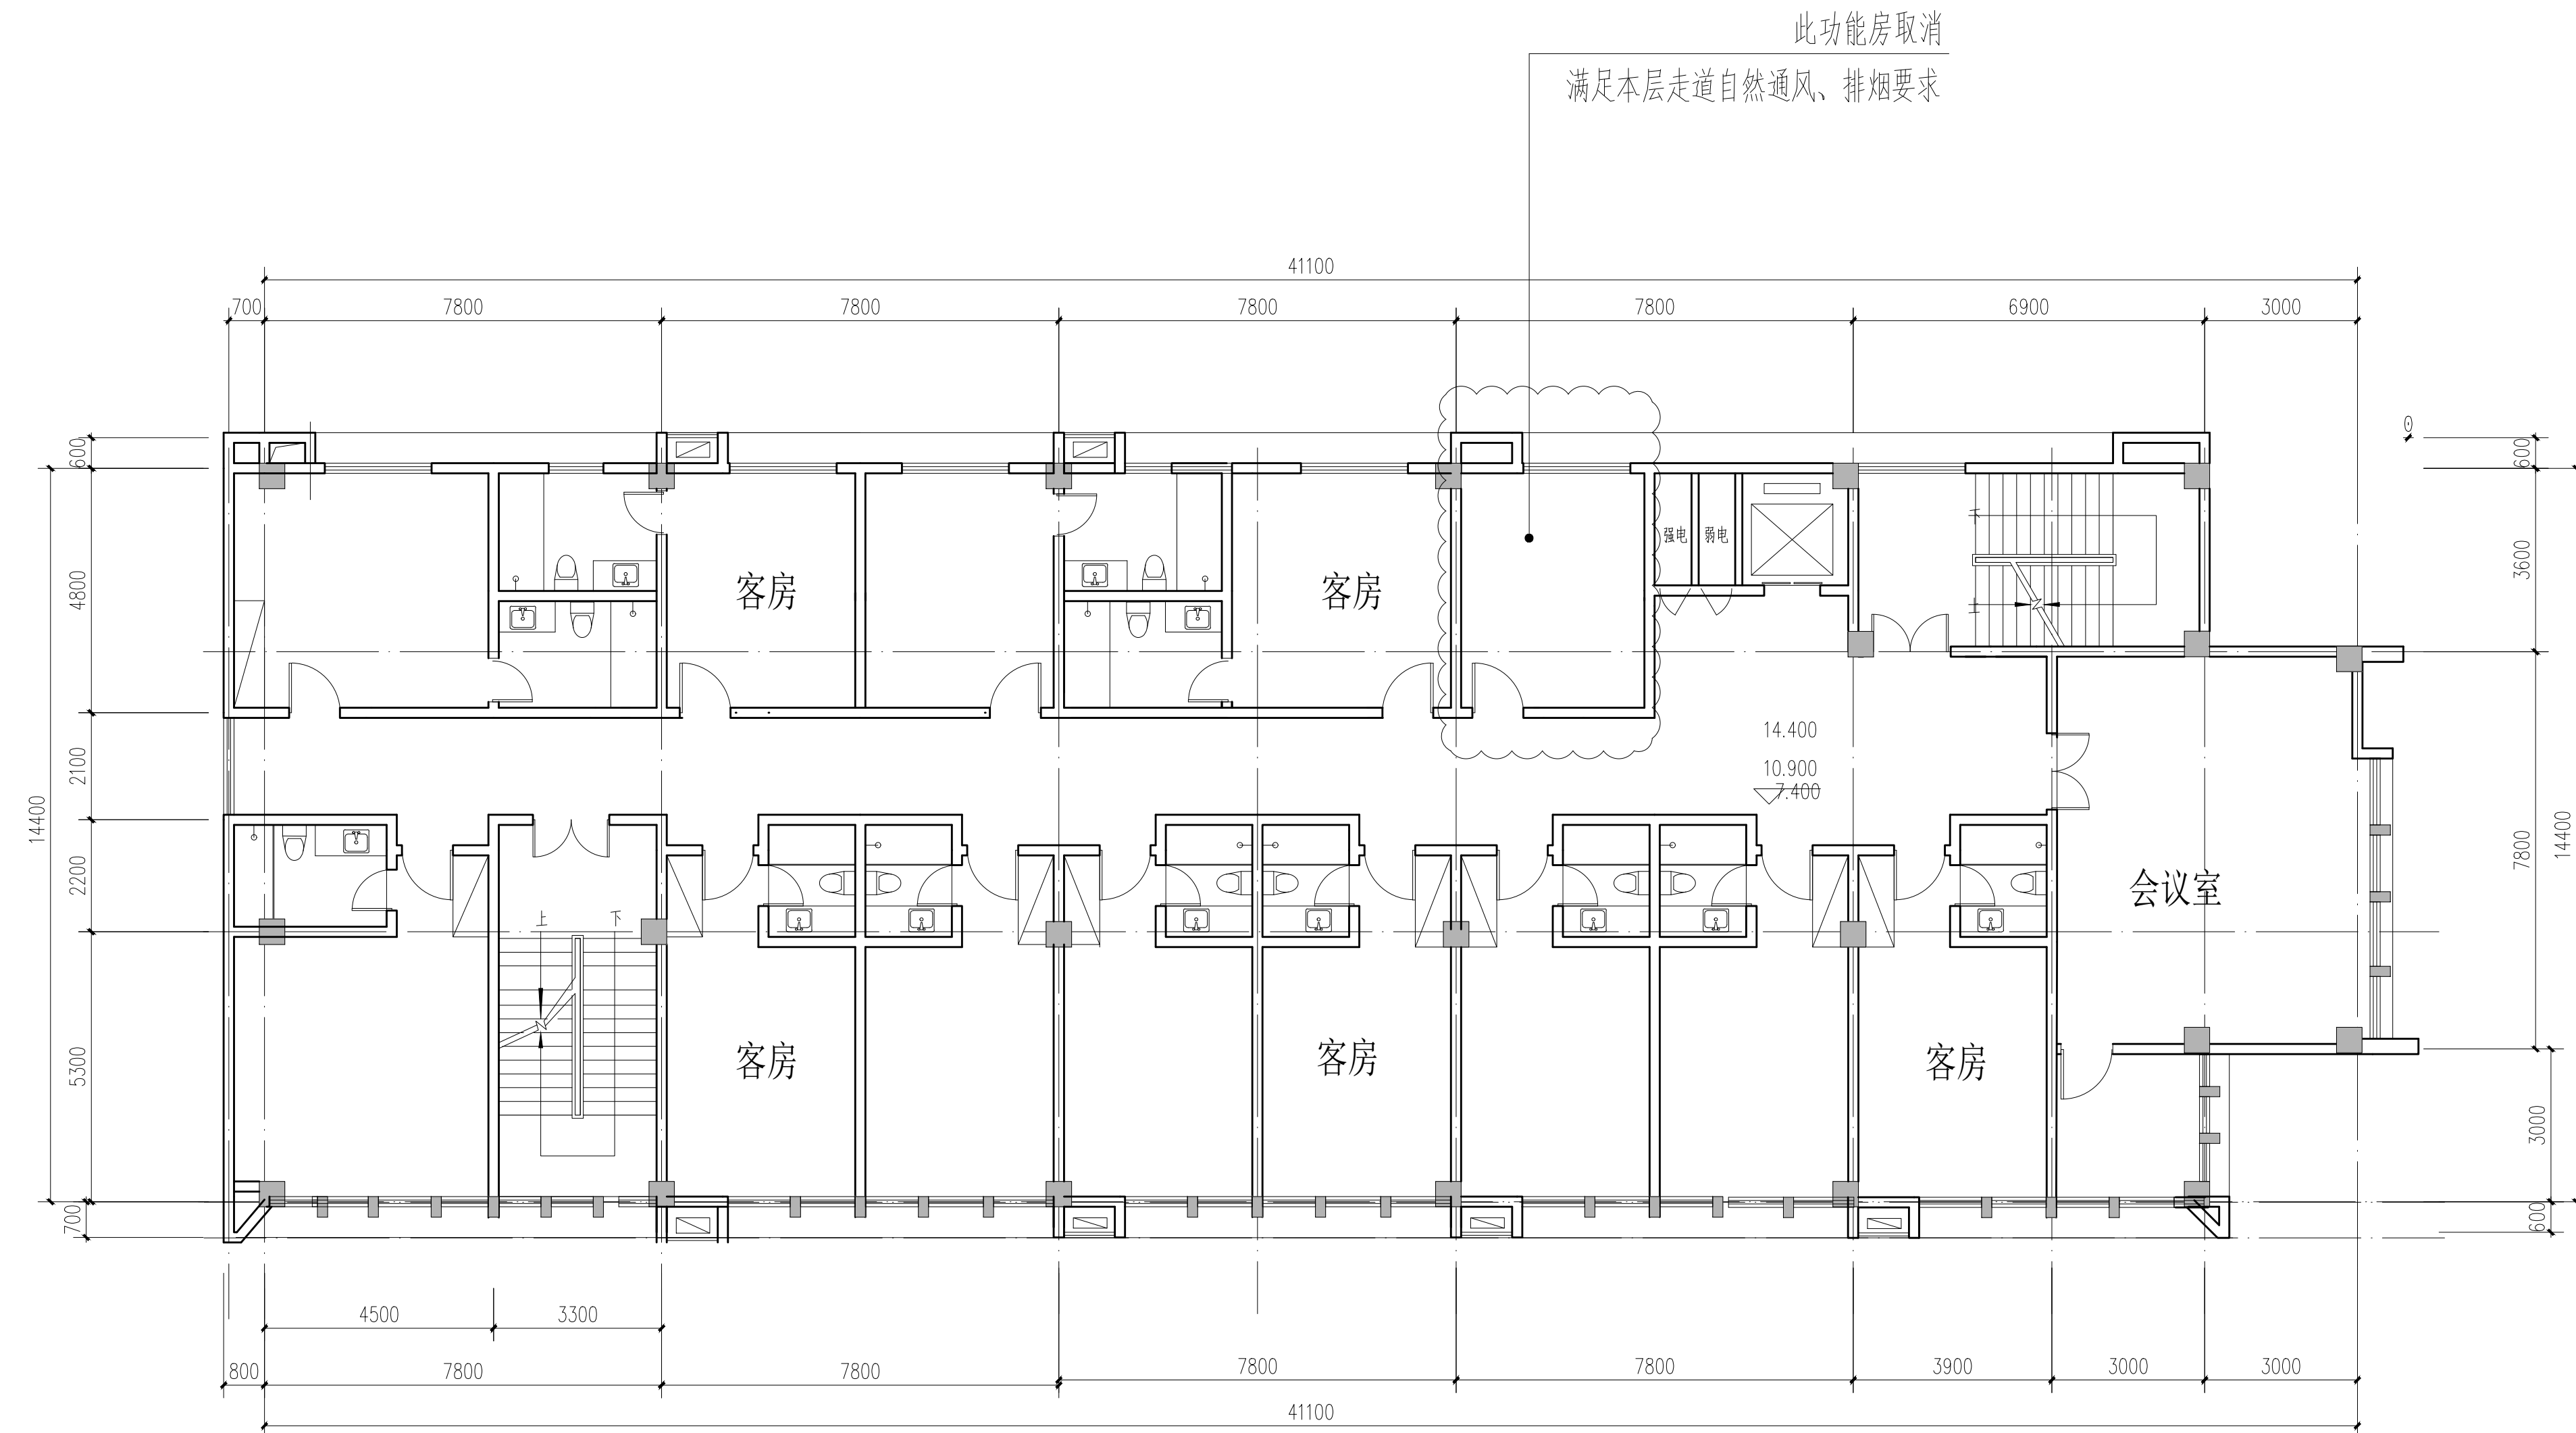


三~五层平面图 1:100

姓名	张永福
性别	男
出生日期	1980年1月1日
籍贯	河北省石家庄市
民族	汉族
学历	本科
专业名称	电气工程及其自动化
毕业院校	河北工业大学
学位等级	学士学位
毕业时间	2003年7月
工作单位	国家电网公司
工作岗位	变电运行值班员
入职日期	2003年8月
职称等级	助理工程师
取得日期	2006年12月
备注	

筑乙级: A235005080


工程编号	2022-05
图 别	建 施
图 号	08
日 期	2023.02

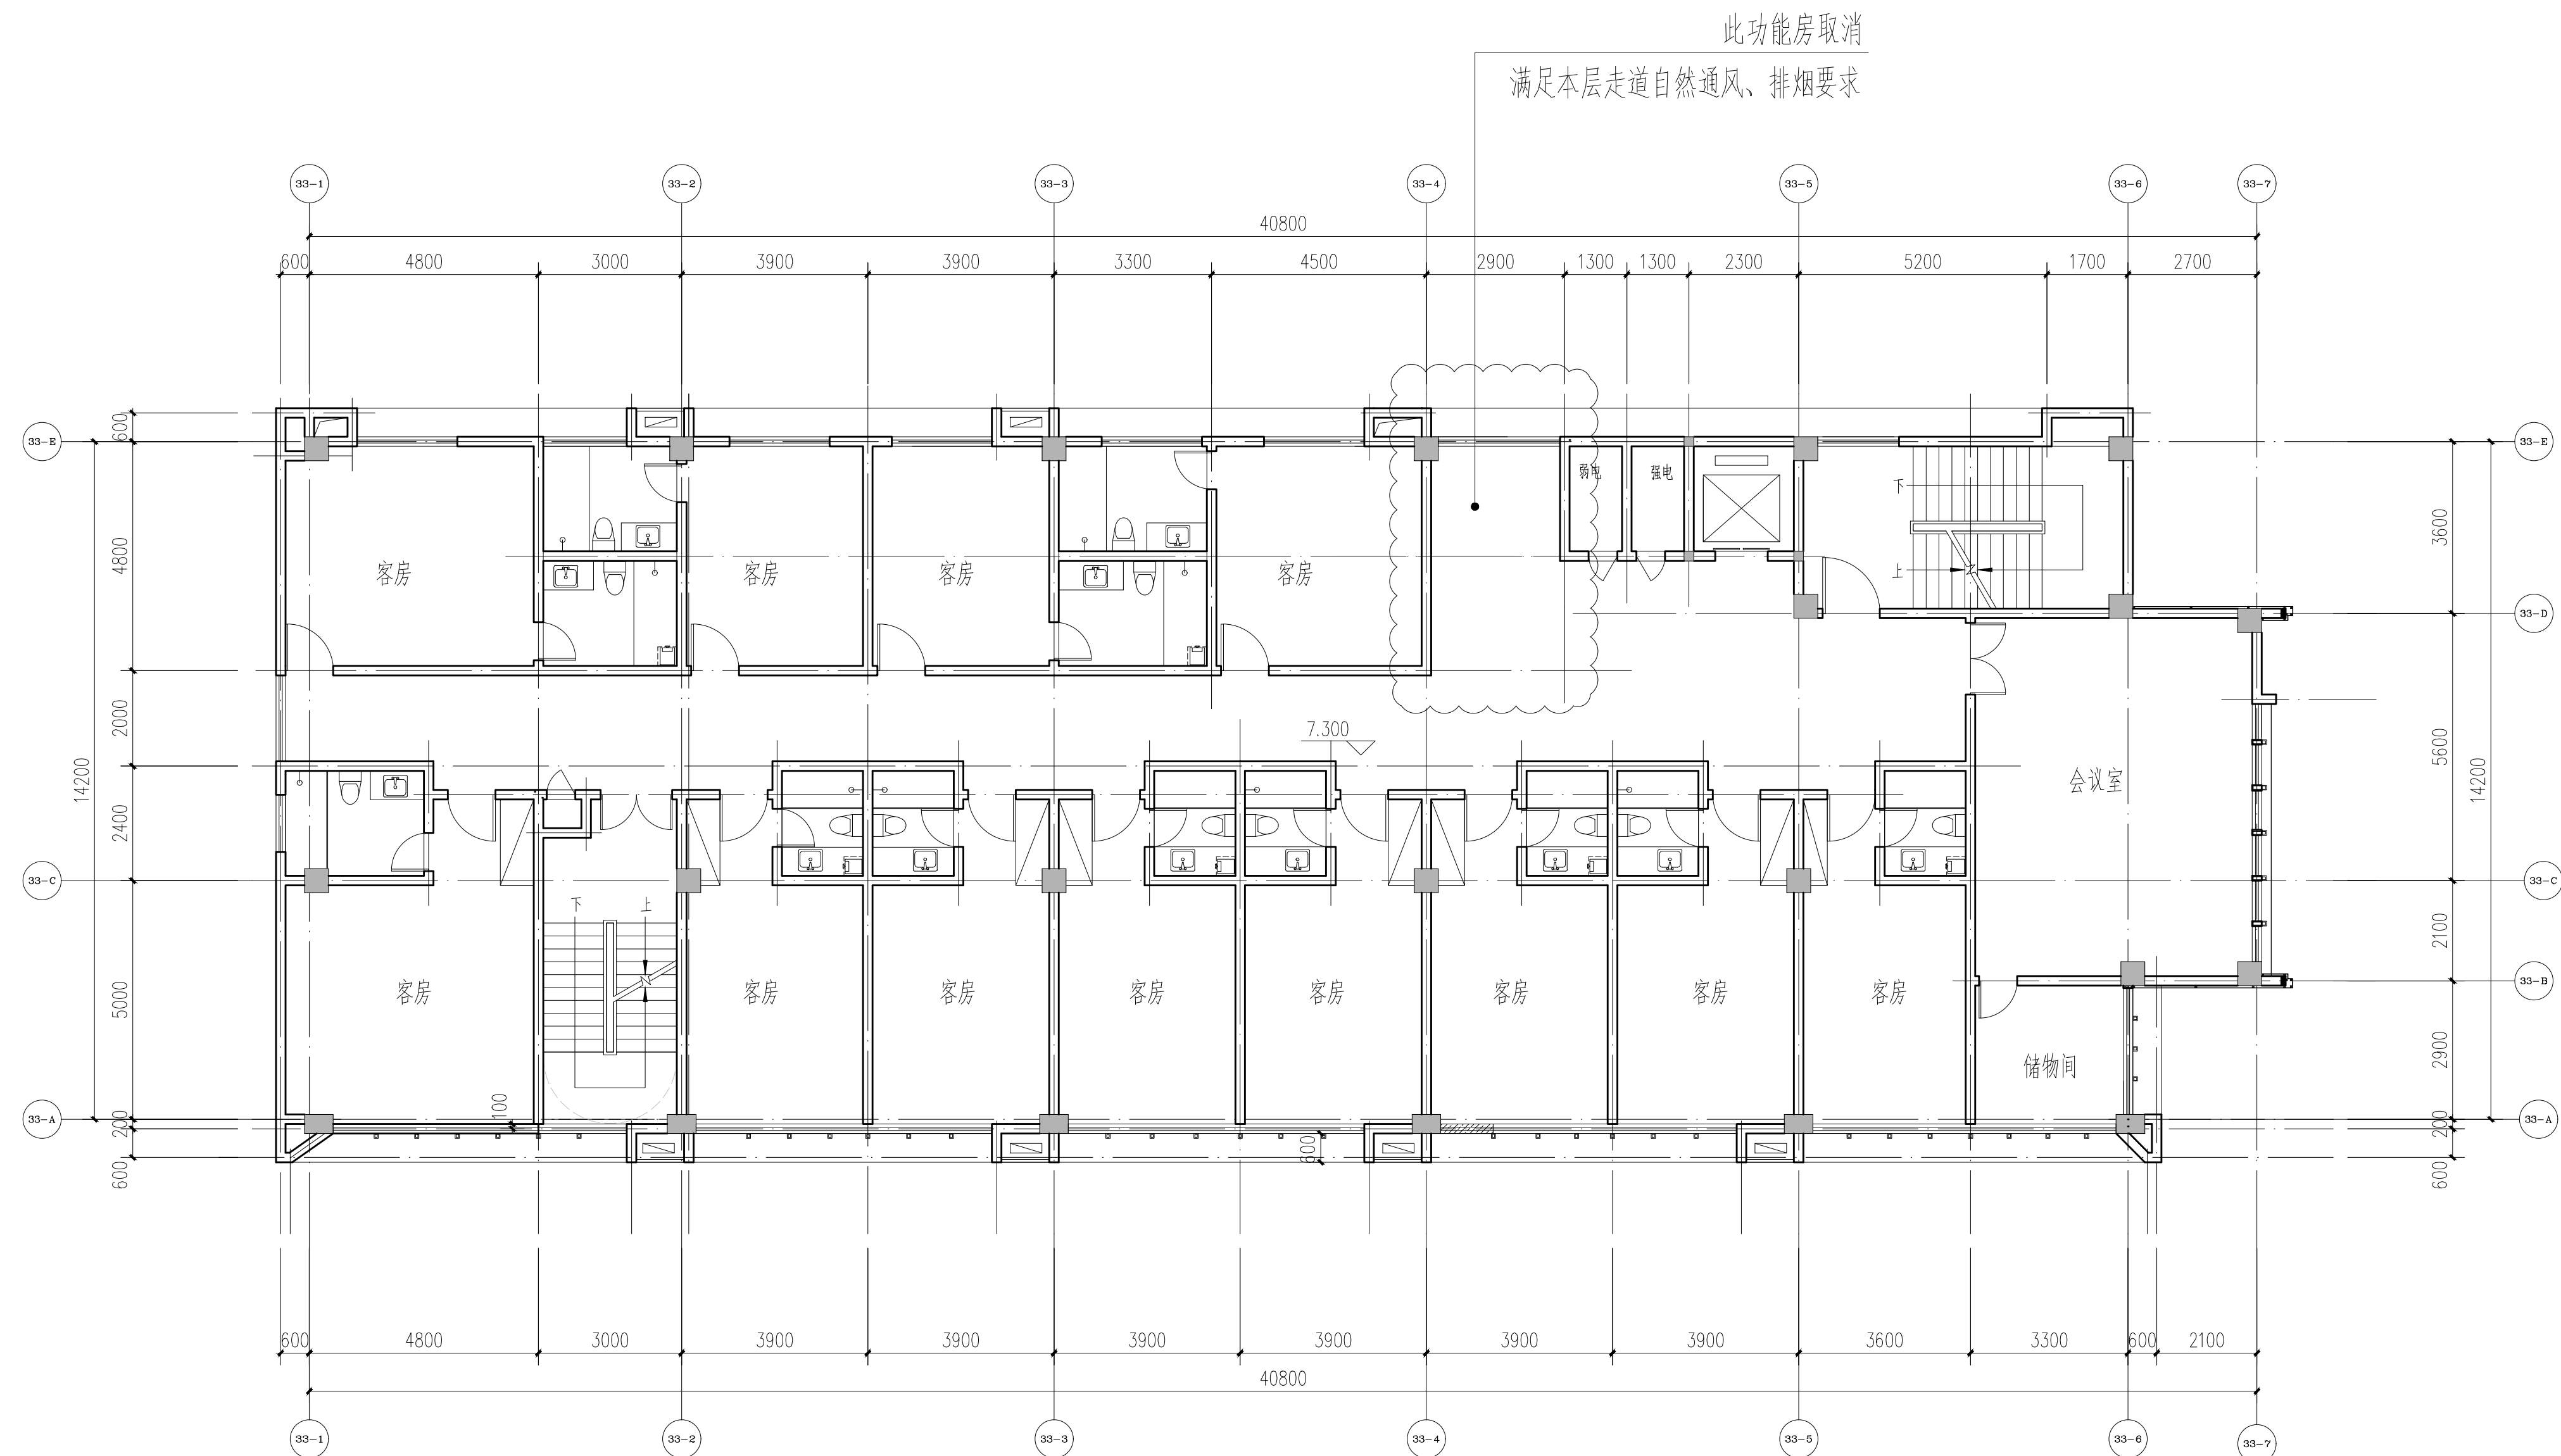

三~五层平面图 1:100

设计人	张善军
审核人	郑功农
专业负责人	郑功农
校对人	张善军
制图人	徐恩辉
日期	2023.02
图名	B栋、C栋一层平面图

B栋、C栋一层平面图 变更前

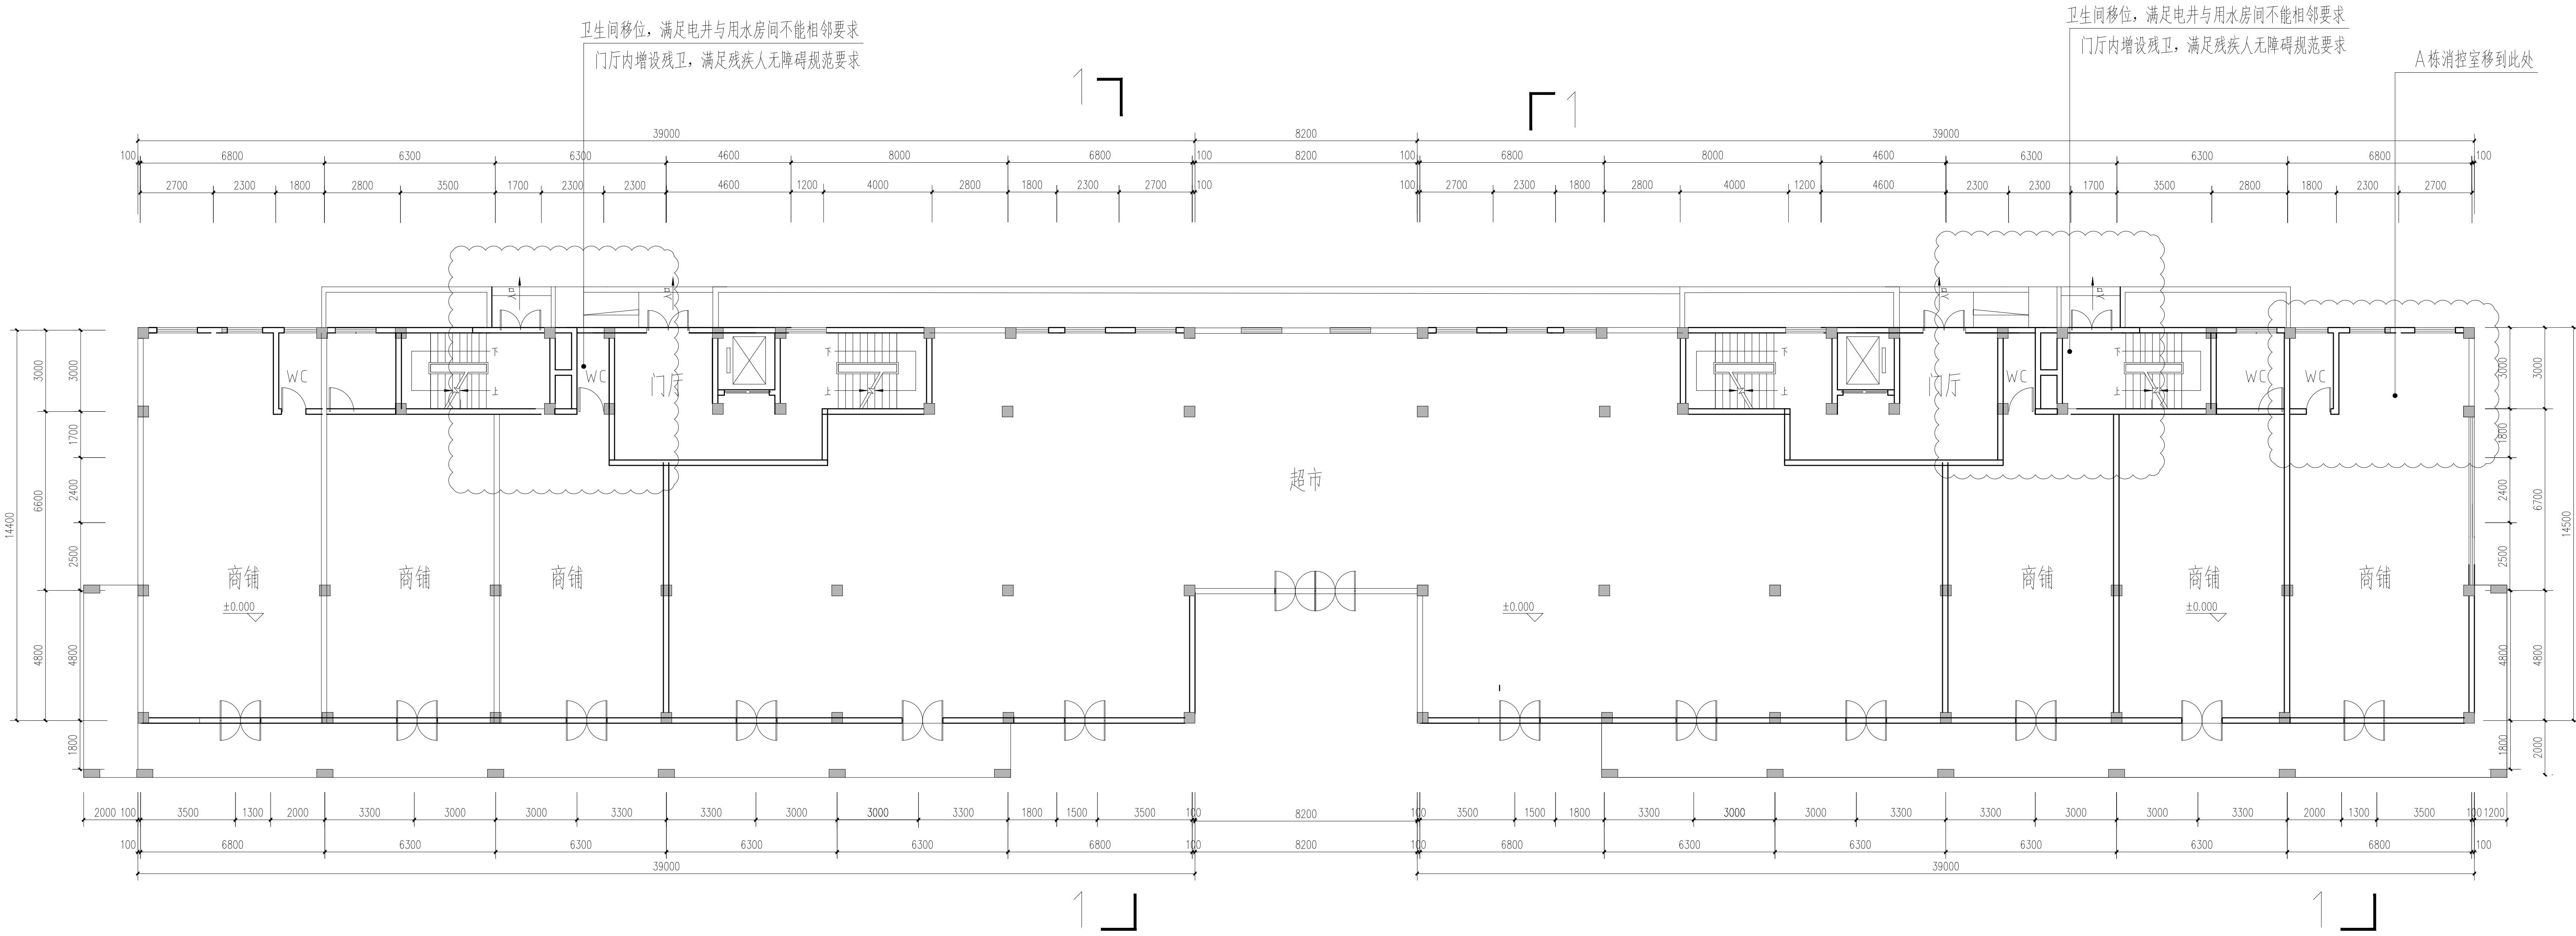

一层平面图

单位名称：
福建境景
建筑设计有限公司
建筑乙级：A235005080

备注：

施工图审查单位：

施工图审查合格书编号：

图章专用章：

注册建筑师执业章：

注册结构师执业章：

工程名称：

沙县如意苑商务中心B栋、C栋

建设单位：三明市沙县区虬江街道金泉村
股份经济合作社

审定	张善军	张善军
工程负责人	郑功农	郑功农
专业负责人	郑功农	郑功农
审核	张绳景	张绳景
校对	张善军	张善军
设计	徐恩辉	徐恩辉
制图	徐恩辉	徐恩辉

图名：

一层平面图

工程编号	2022-05
图别	建筑
图号	09
日期	2023.02


工程名称	沙县如意苑商务中心B栋、C栋
建设单位	三明市沙县区虬江街道金泉村股份经济合作社
设计单位	福建境景建筑设计有限公司
项目负责人	张善军
专业负责人	郑功农
审核人	张绳景
校对	张善军
设计	徐恩辉
制图	徐恩辉

B栋、C栋一层平面图 变更后

卫生间移位，满足电井与用水房间不能相邻要求
门厅内增设残卫，满足残疾人无障碍规范要求

卫生间移位，满足电井与用水房间不能相邻要求
门厅内增设残卫，满足残疾人无障碍规范要求

A栋消控室移到此处

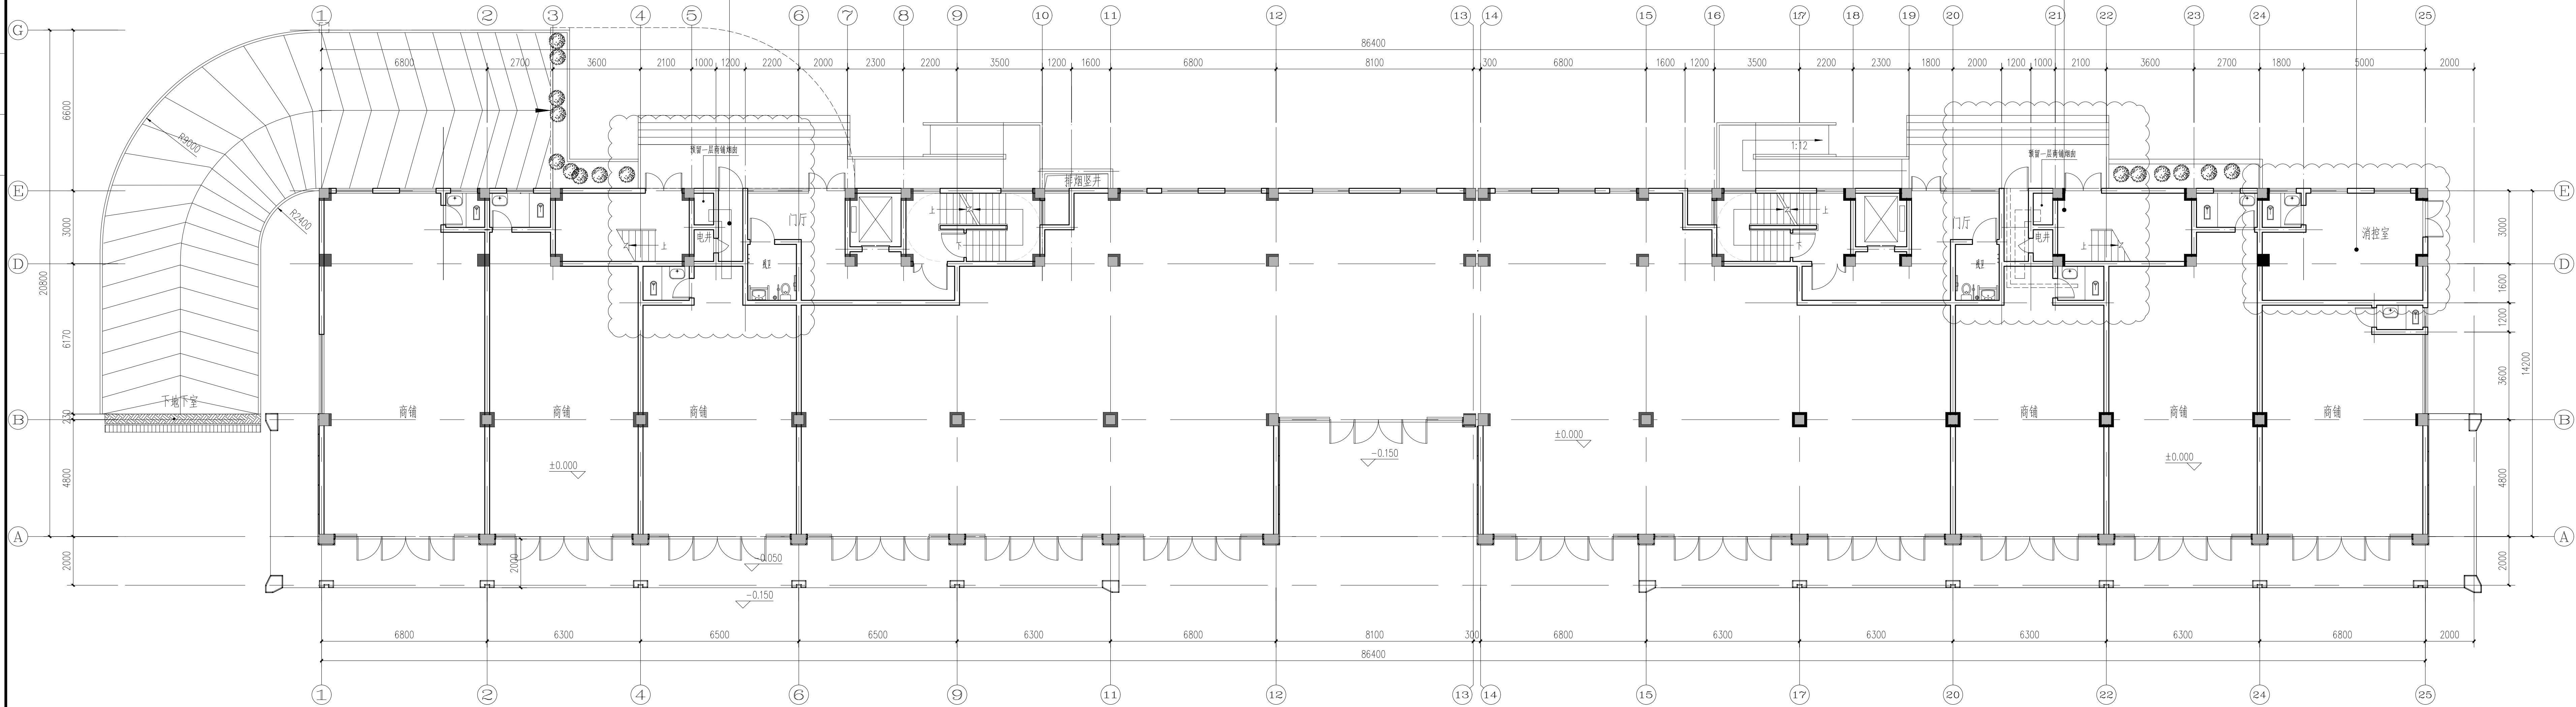

一层平面图 1:100

单位名称:

福建境景
建筑设计有限公司

建筑乙级: A235005080

备注:

施工图审查单位:

施工图审查合格书编号:

图纸专用章:

注册建筑师执业章:

注册结构师执业章:

工程名称:

沙县如意苑商务中心B栋、C栋

建设单位: 三明市沙县区虬江街道金泉村
股份经济合作社

审定	张善军	张善军
工程负责人	郑功农	郑功农
专业负责人	郑功农	郑功农
审核	张绳景	张绳景
校对	张善军	张善军
设计	徐恩辉	徐恩辉
制图	徐恩辉	徐恩辉

图名:

一层平面图

工程编号	2022-05
图别	建筑
图号	10
日期	2023.02

B栋、C栋南立面两端三~五层立面 变更后



南立面图 1:100

单位名称:

 福建境景
建筑设计有限公司

建筑乙级: A235005080

备注:

施工图审查单位:

施工图审查合格书编号:

图纸专用章:

注册建筑师执业章:

注册结构师执业章:

工程名称:

沙县如意苑商务中心B栋、C栋

建设单位： 三明市沙县区虬江街道金泉村
股份经济合作社

审 定 张 善 军

工程负责人	郑 功 农	郑功农
-------	-------	-----

专业负责人	郑功农	郑功农
-------	-----	-----

编制人	陈功根	审核人	张通景
-----	-----	-----	-----

中 微	米 純 米	15808
檢 封	米 前 經	25808

校 刘	张 善 车	
温 林		张团山

设计	徐恩辉	徐恩辉
----	-----	-----

制 图	徐 恩 辉	徐恩辉
-----	-------	-----

图名:

南立面图

用立国图

工程编号	2022-06
------	---------

工 程 名 称	2012 年
图 号	建 施

日 期	建 施
国 号	12

图 5	12
-----	----


专业	建筑	姓名	张善军	职称	注册建筑师
专业	结构	姓名	徐恩辉	职称	注册结构师
专业	给排水	姓名		职称	
专业	电气	姓名		职称	
专业	暖通	姓名		职称	
专业	其他	姓名		职称	

B栋、C栋三~五层侧面变更



侧立面图 1:100

B栋、C栋三~五层侧面变更后

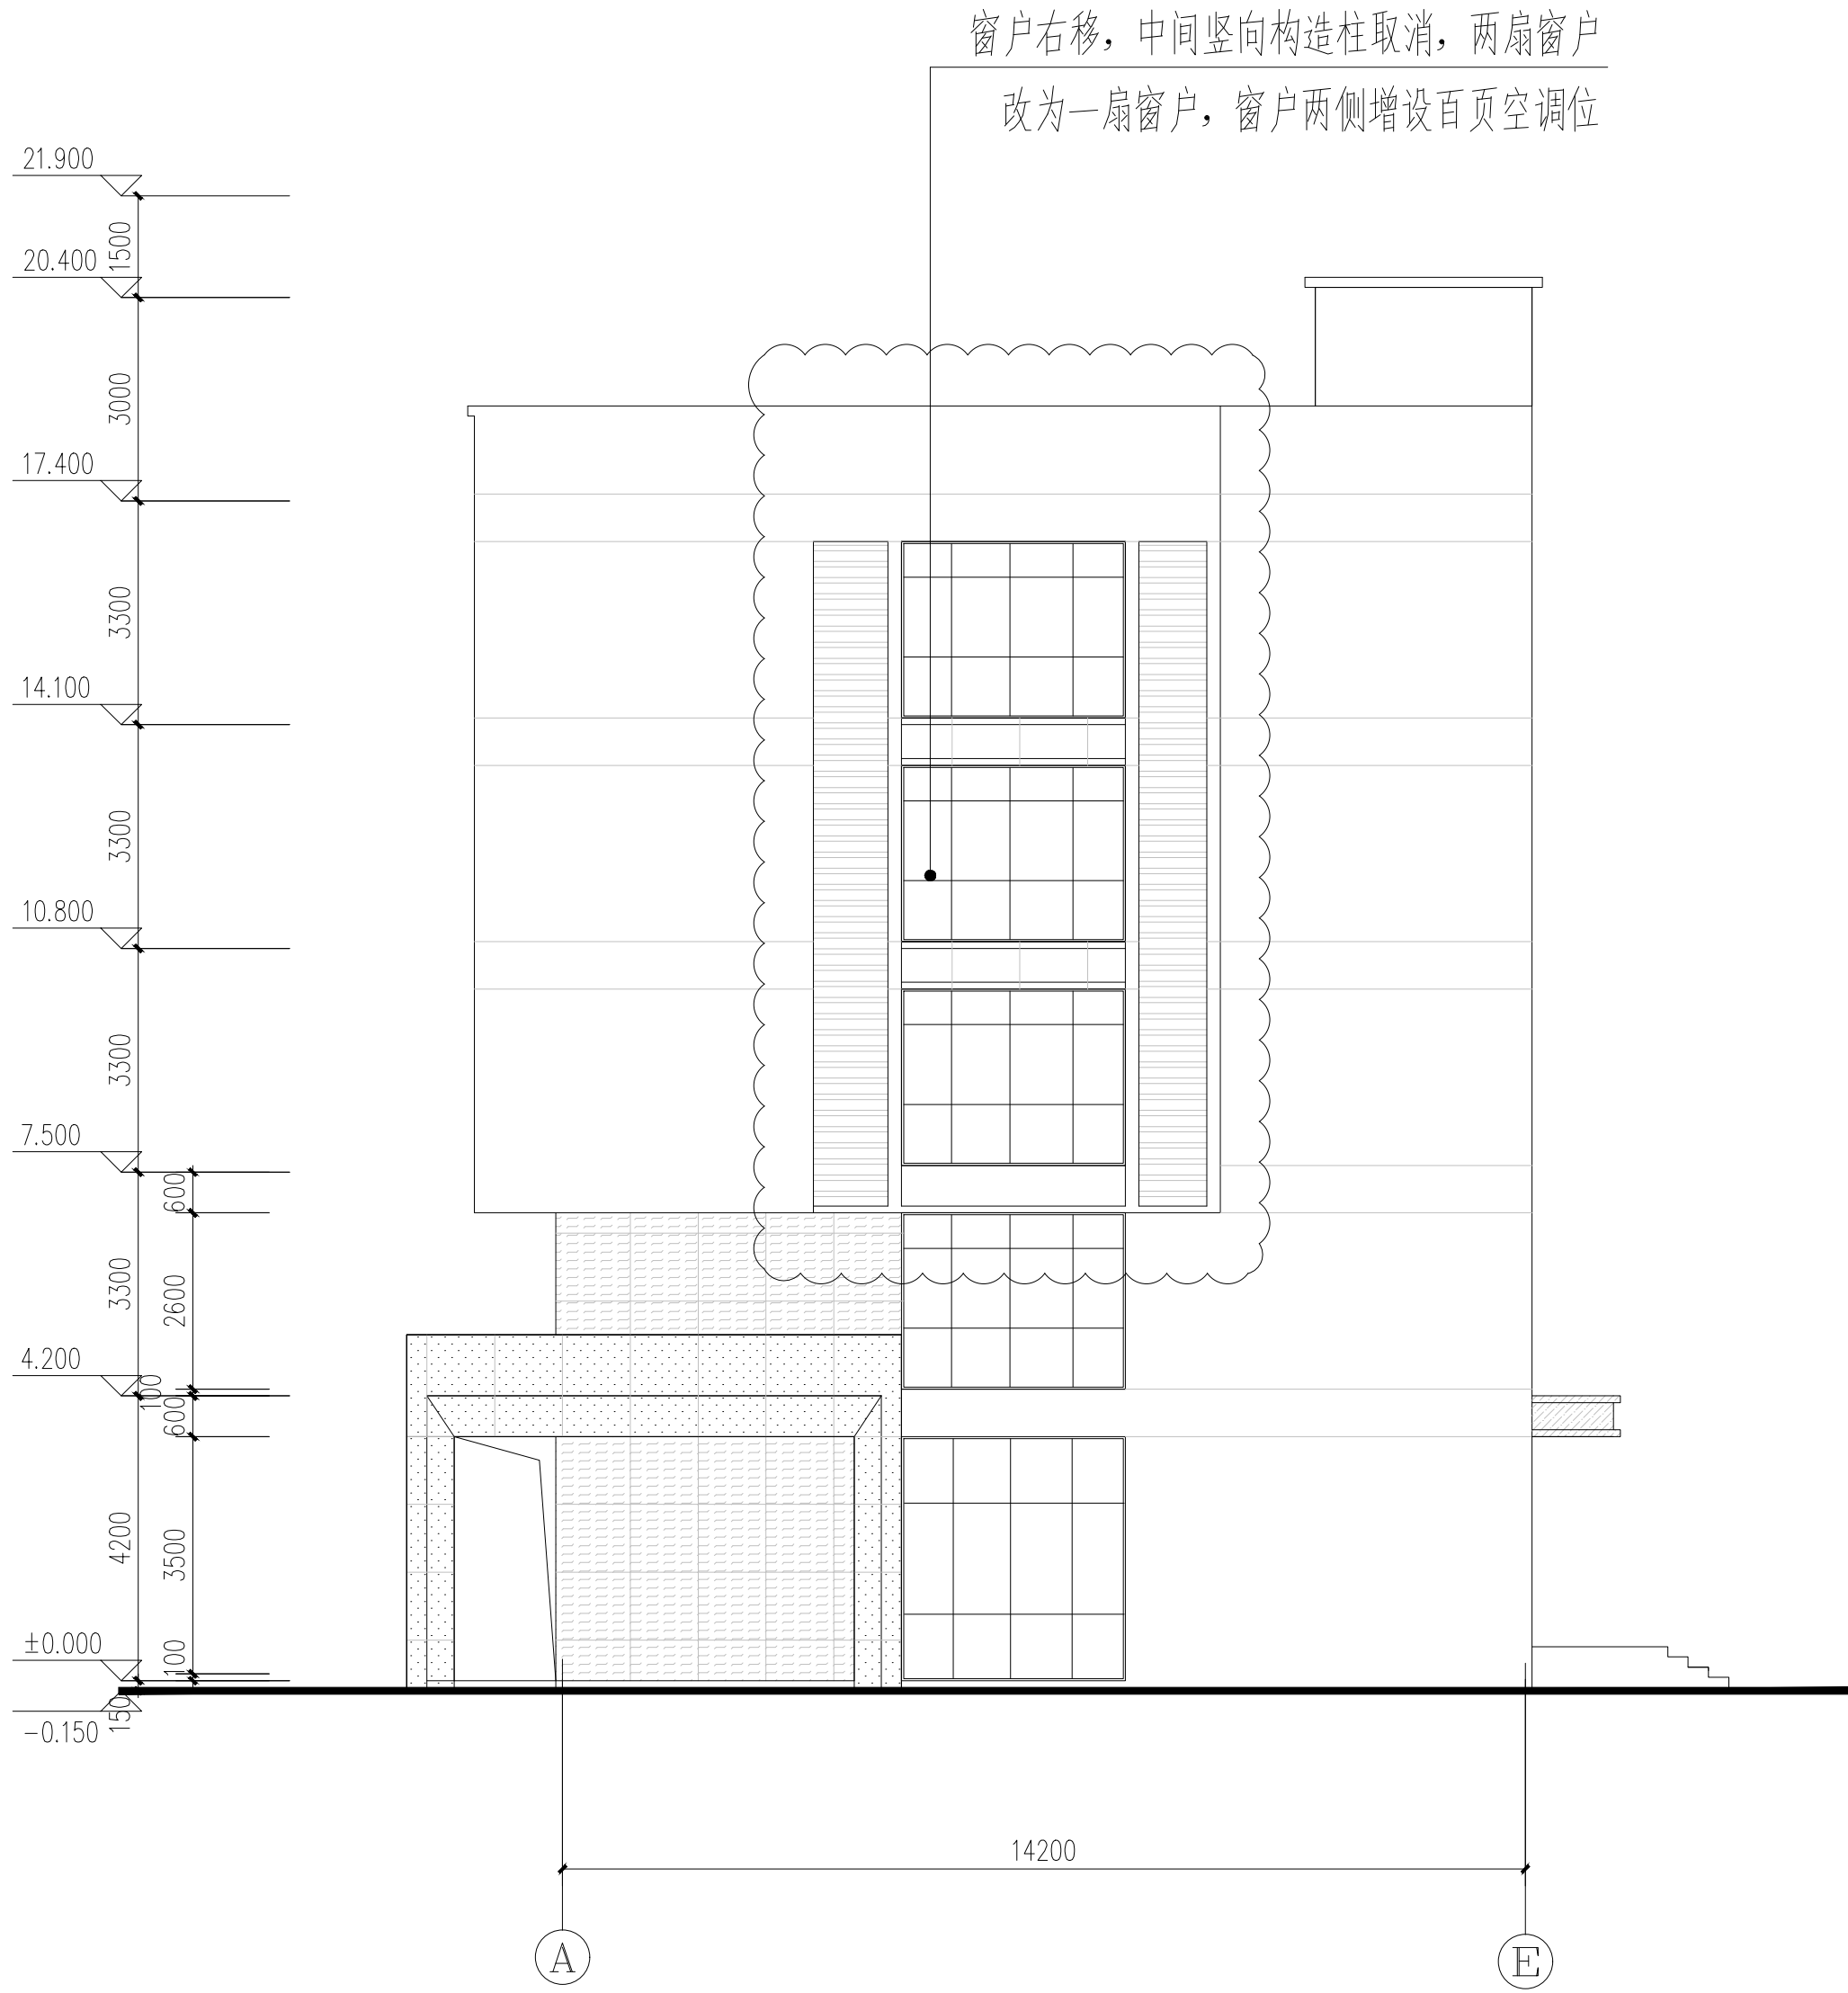

侧立面图 1:100

审 定	张 善 军	张善军
工程负责人	郑功农	郑功农
专业负责人	郑功农	郑功农
审 核	张 绳 景	张绳景
校 对	张 善 军	张善军
设 计	徐 恩 辉	徐恩辉
制 图	徐 恩 辉	徐恩辉

工程编号	2022-05
图 别	建 施
图 号	03
日 期	2023.02

总平面图 变更前

单位名称:

福建境景
建筑设计有限公司

建模乙级: A235005080

备注:

施工图审查单位:

施工图审查合格书编号:

图纸专用章:

注册建筑师执业章:

注册结构师执业章:

工程名称:

沙县如意苑商务中心


建设单位: 三明市沙县区虬江街道金泉村
股份经济合作社

审 定	张 善 军	
工程负责人	郑功农	
专业负责人	郑功农	
审 核	张 绳 景	
校 对	张 善 军	
设 计	徐 恩 辉	
制 图	徐 恩 辉	

图名:


总平面图

工程编号	2022-05
图 别	建 施
图 号	14
日 期	2022.07

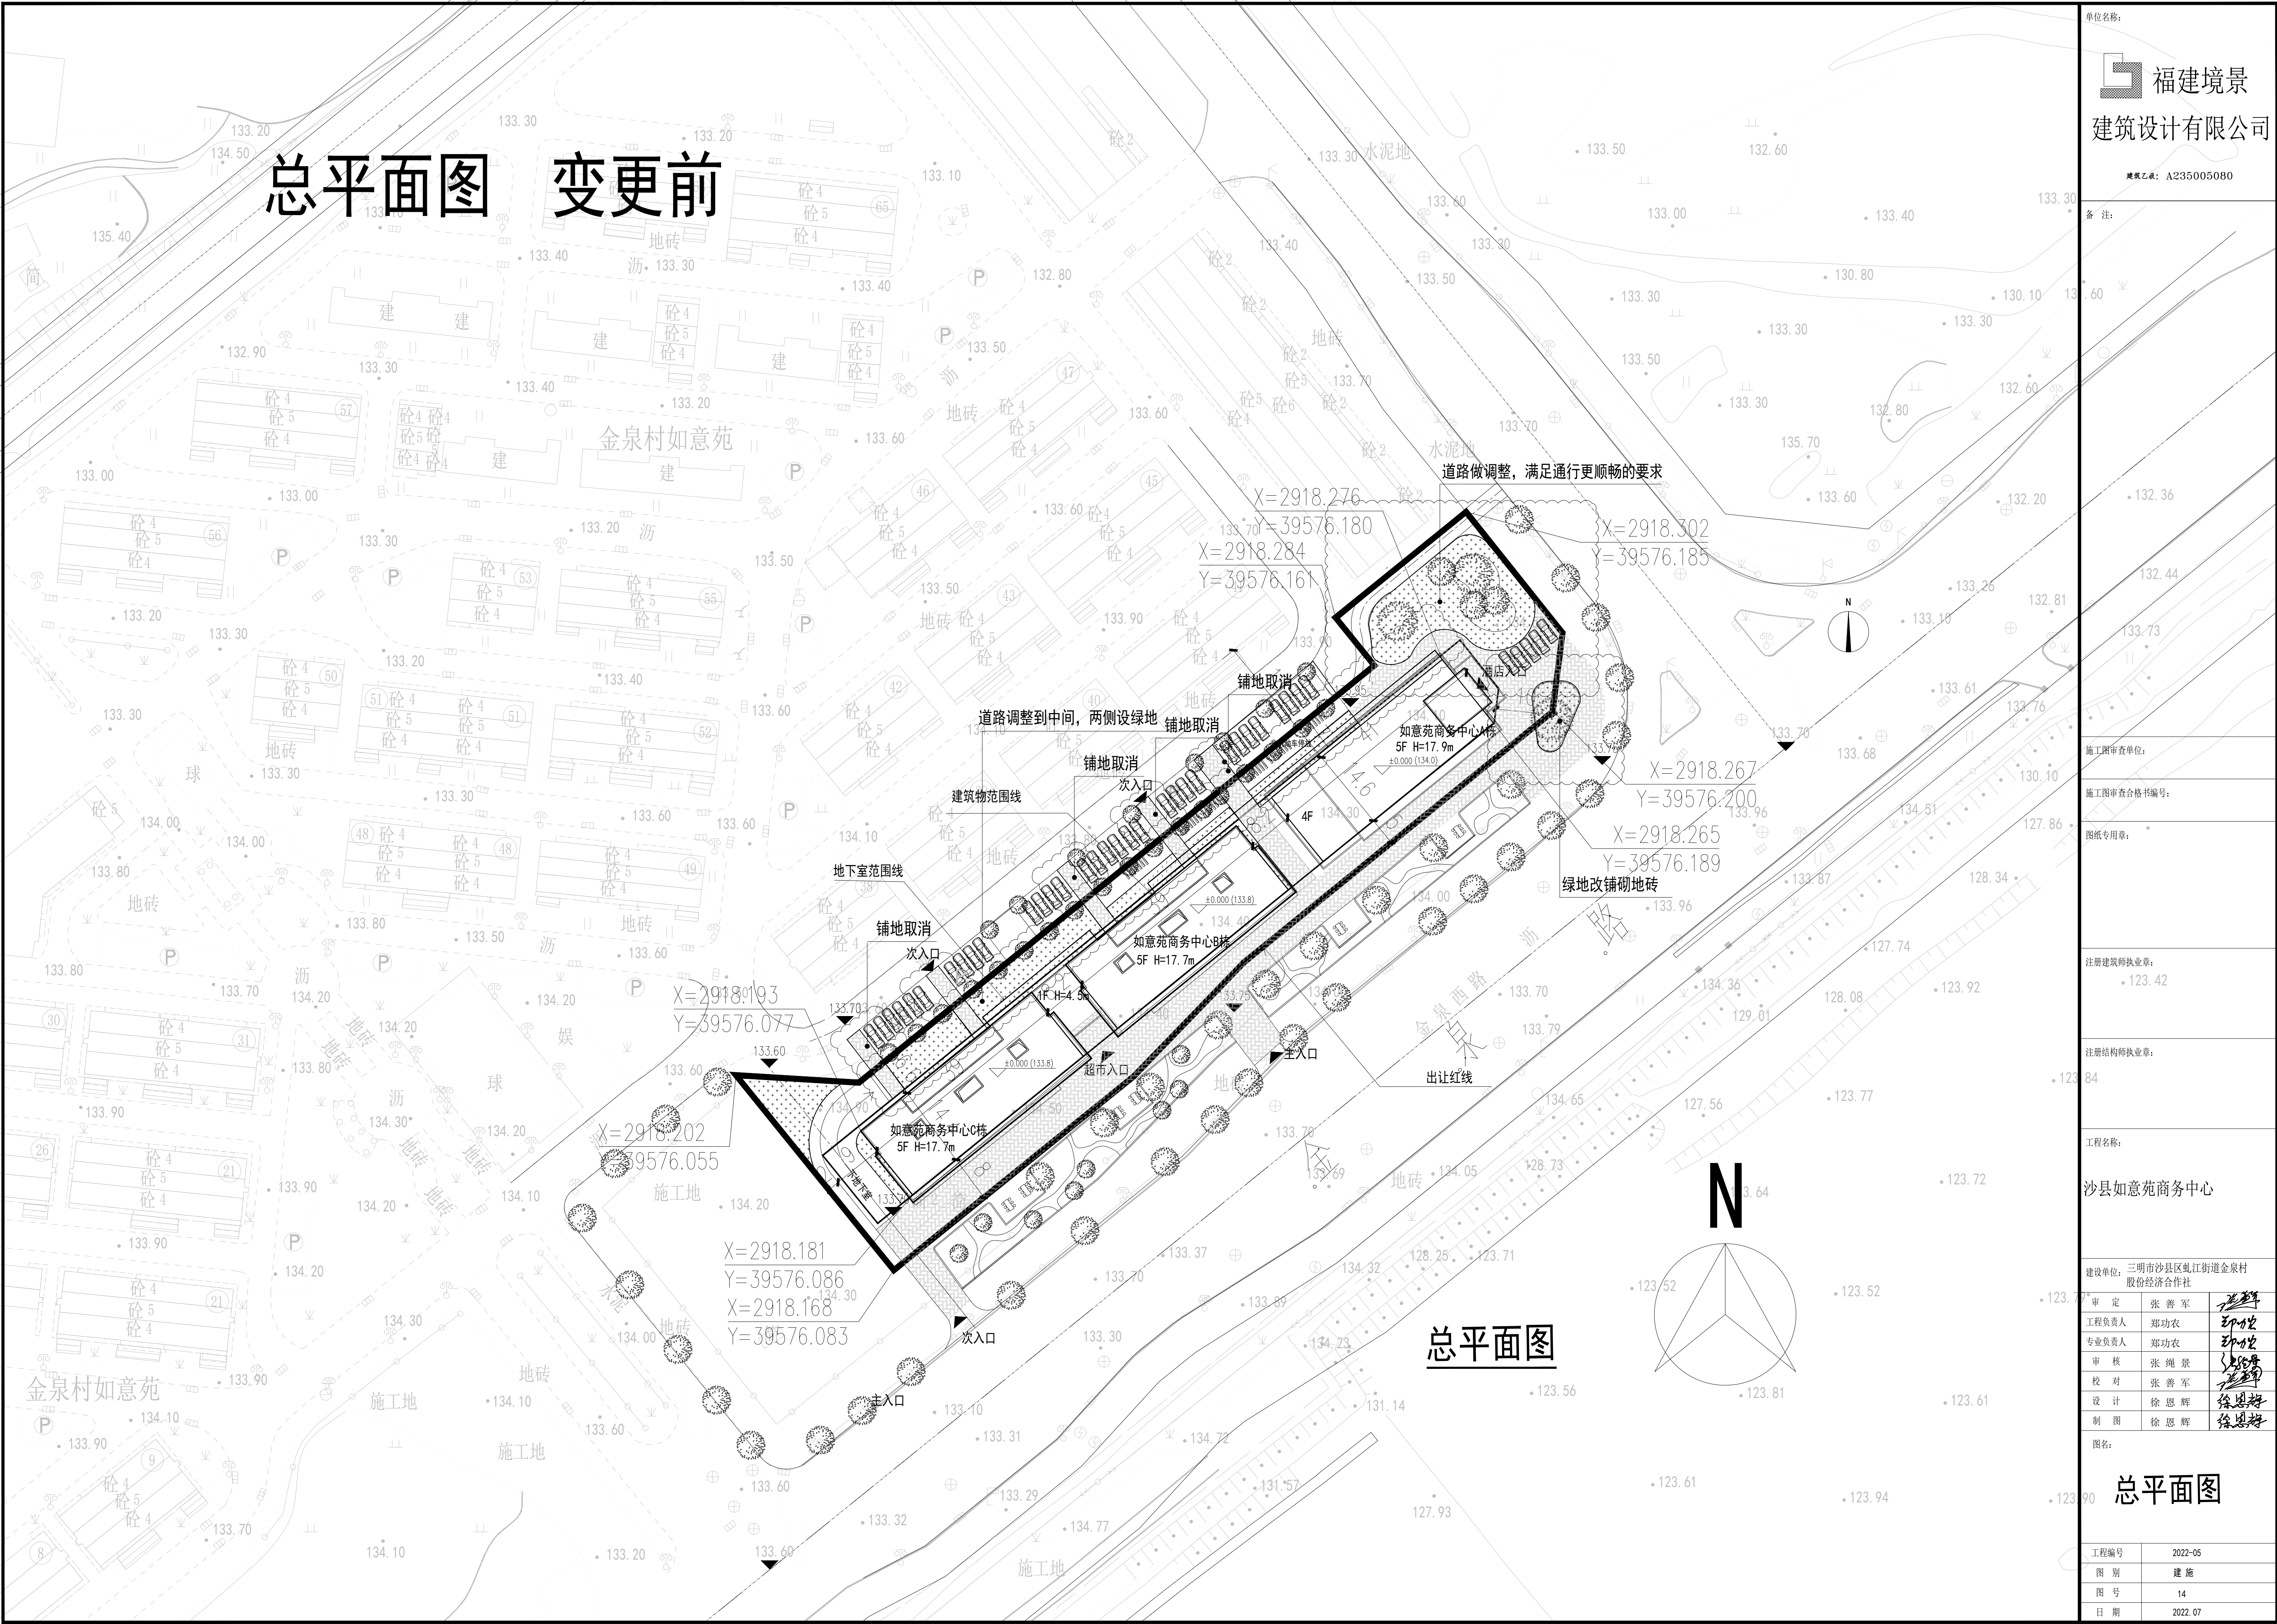

图名	总平面图
图号	01
比例	1:500
日期	2022.05
设计	徐恩辉
审核	张善军
专业负责人	郑功农
审定	张善军
制图	徐恩辉
校核	张善军
设计	徐恩辉
工程负责人	郑功农
专业负责人	郑功农
审核	张善军
校核	张善军
设计	徐恩辉
制图	徐恩辉

总平面图 变更后

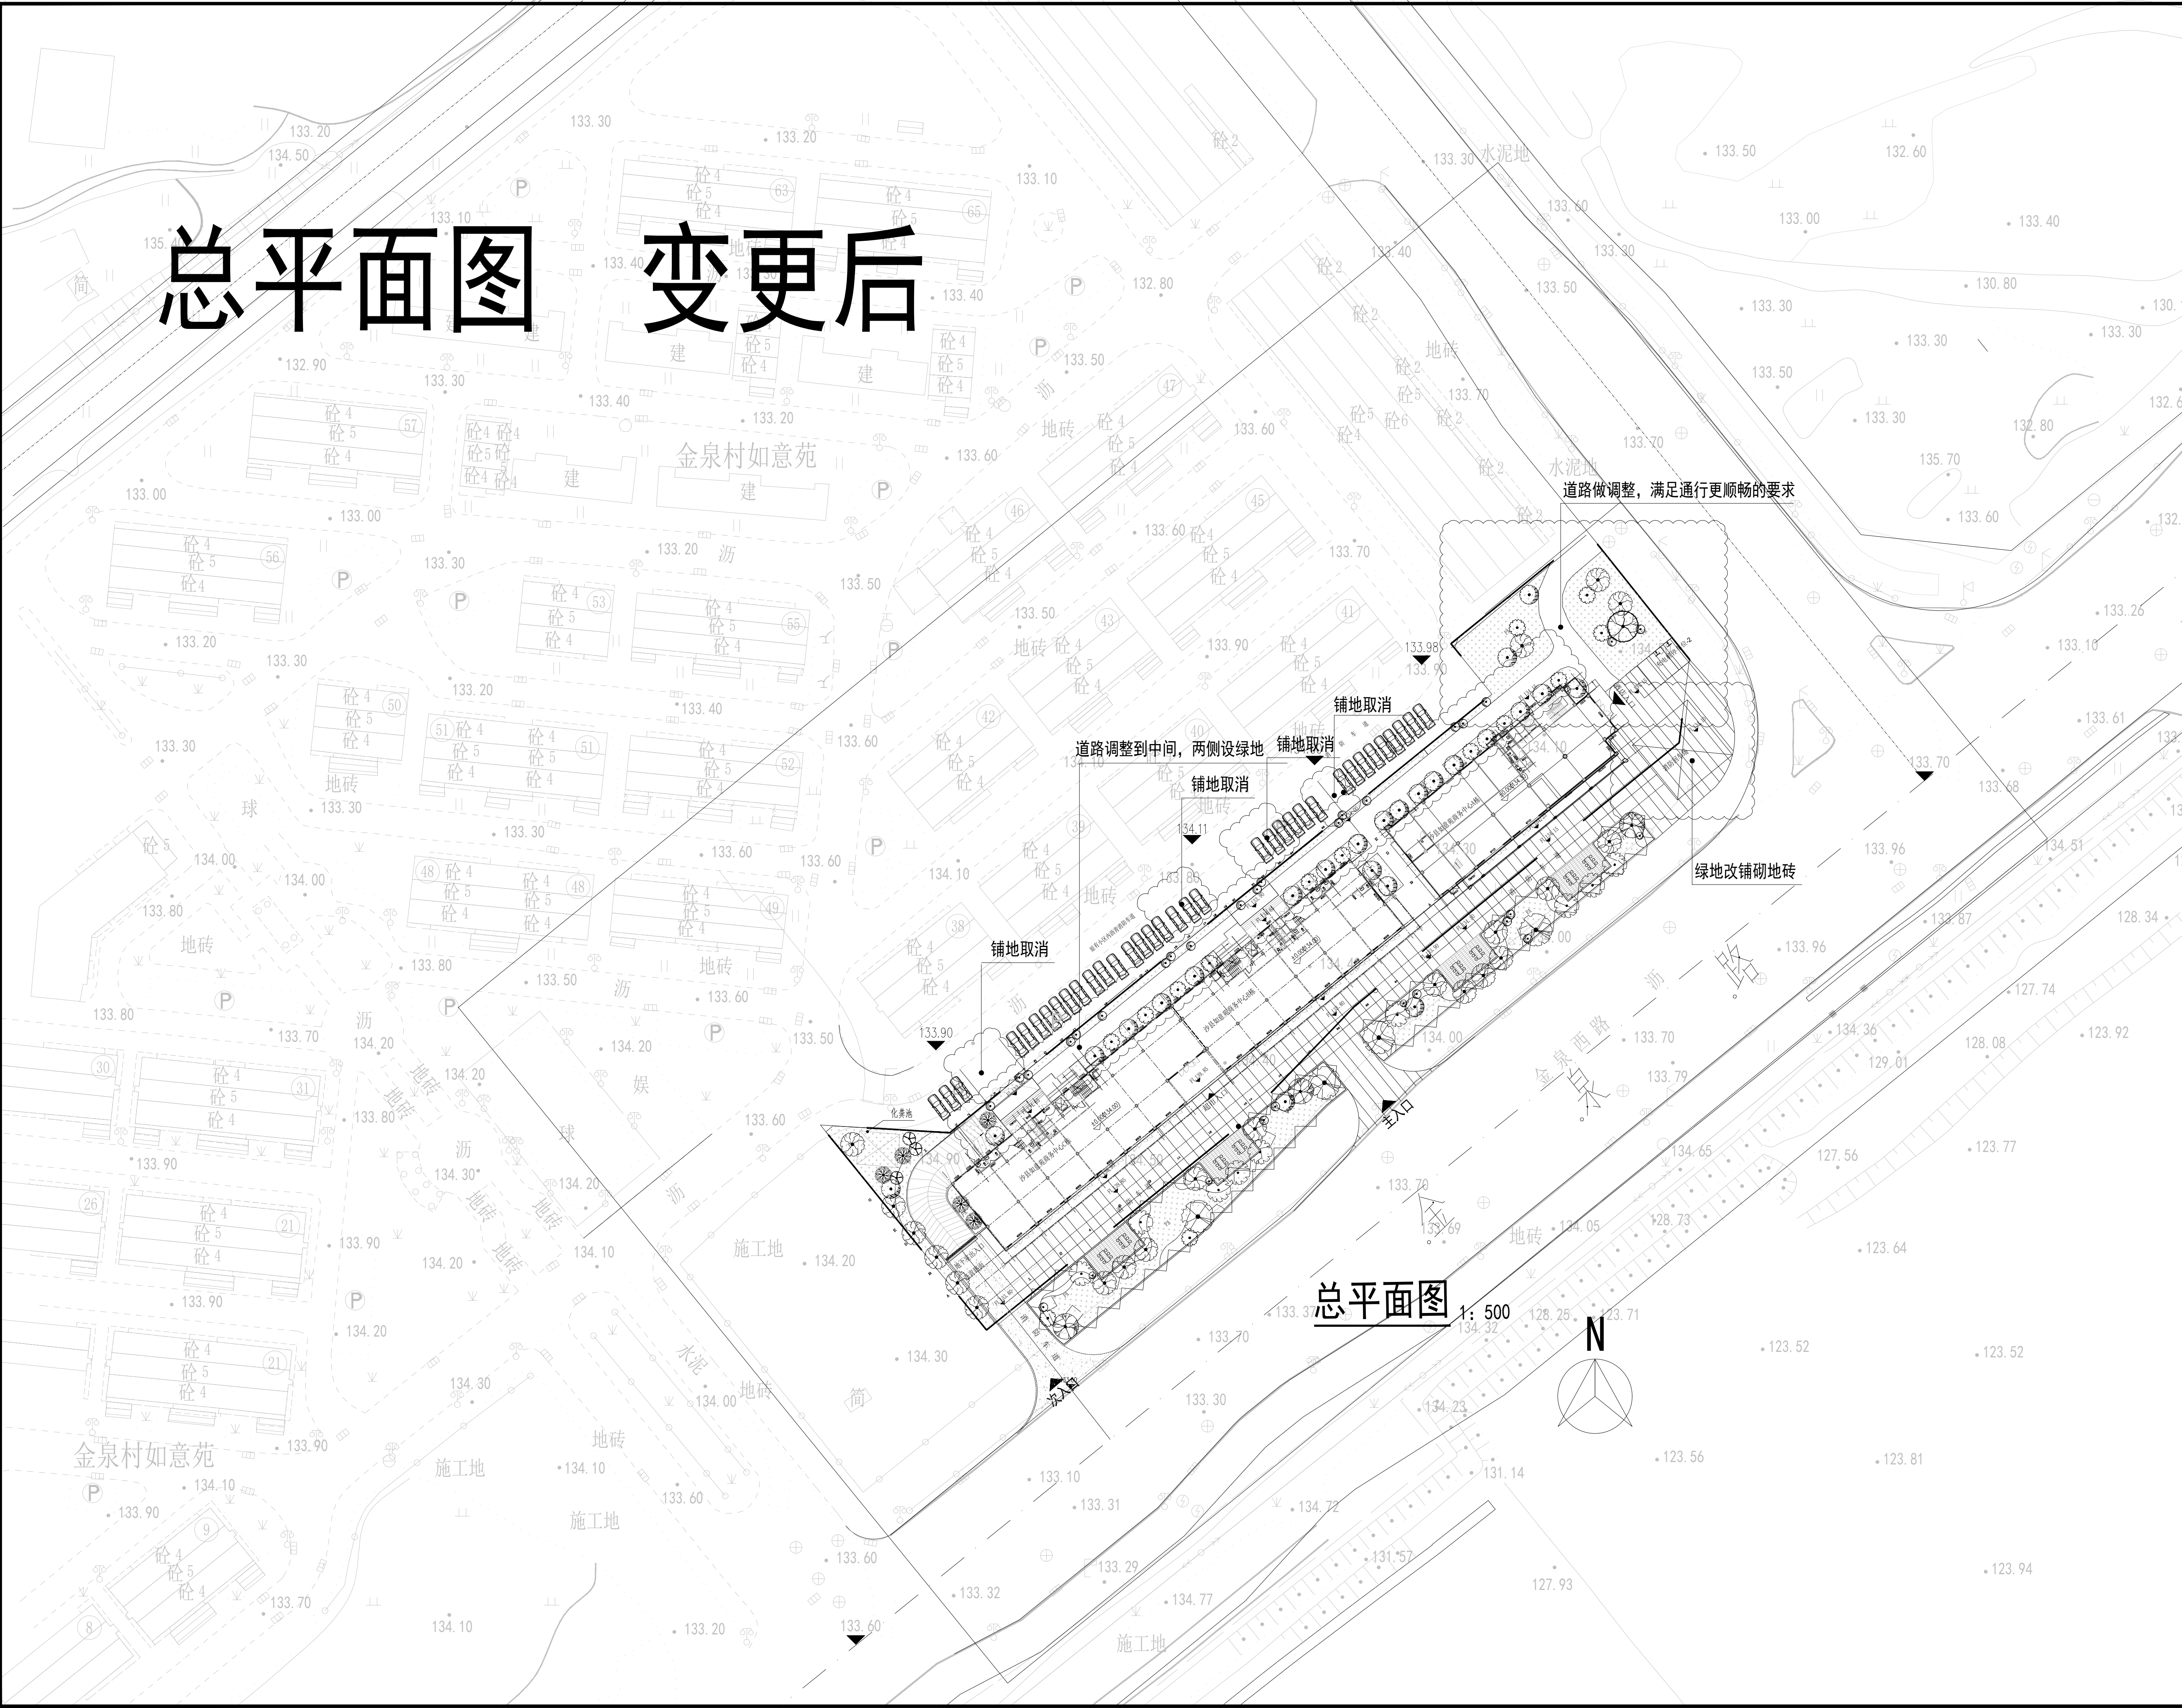

总平面图 1: 500

单位名称:	
福建境景 建筑设计有限公司	
建模乙级: A235005080	
备注:	
施工图审查单位:	
施工图审查合格书编号:	
图纸专用章:	
注册建筑师执业章:	
注册结构师执业章:	
工程名称:	
沙县如意苑商务中心	
建设单位: 三明市沙县区虬江街道金泉村 股份经济合作社	
审定	张善军
工程负责人	郑功农
专业负责人	郑功农
审核	张善军
校核	张善军
设计	徐恩辉
制图	徐恩辉
图名:	
总平面图	
工程编号	2022-05
图别	建施
图号	15
日期	2022.07