


变更平面

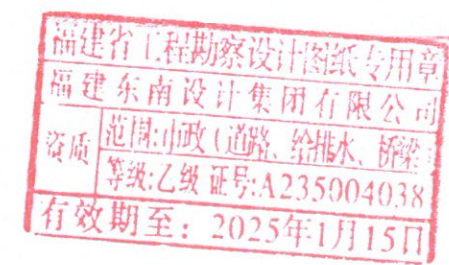

设计变更(补充)说明																			
建设单位		海翼瑞都(福建)房地产开发有限公司			主送单位		建设单位												
工程名称		三元区棚户区改造马道山-新田巷片区道路工程			抄送单位		各有关单位												
工程编号		SZ2018-27			发文日期		2024 年 05 月												
更改理由	☐ 1. 原设计计算的更正。									☐ 4. 建设单位要求更改。									
	☐ 2. 原构造设计的改进或完善。									☐ 5. 施工单位要求更改。									
	☐ 3. 地质条件与原资料有出入造成的修改。									☐ 6. 施工图审查意见。									
更改说明	1. 本更改应先经甲方确认后方可报批。																		
	2. 本更改应经有关单位审批审查通过后方可作为施工依据。																		
	3. 与本更改有关的图纸应在施工前相应修改。																		
	4. 本次变更与原设计图中图号相同的图纸, 原设计图纸作废, 以本次变更图纸为准。																		
变更内容	1、根据现场实际情况及业主要求, 对道路(桩号K0+64.311-K0+212.674)路线平面及竖向进行变更设计, 具体变更设计内容详附图。																		
	2、因主路形成破坏原3.5m道路, 现对3.5m道路改线, 接入主路桩号K0+140。																		
	3、未变更部分图纸按原设计图纸施工。																		
福建东南设计集团有限公司		审核	陈少魁	项目负责	陈少魁	设计	任玉昆	专业	道路										
			任玉昆	专业负责	任玉昆	校对	陈少魁	编号	01										


本变更单盖章方可生效


领单人:

领单日期:

第 1 页, 共 1 页

变
更
内
容

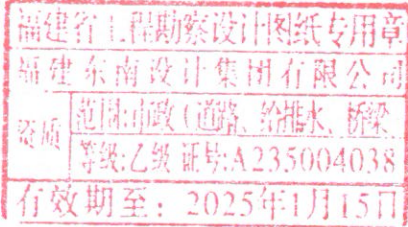

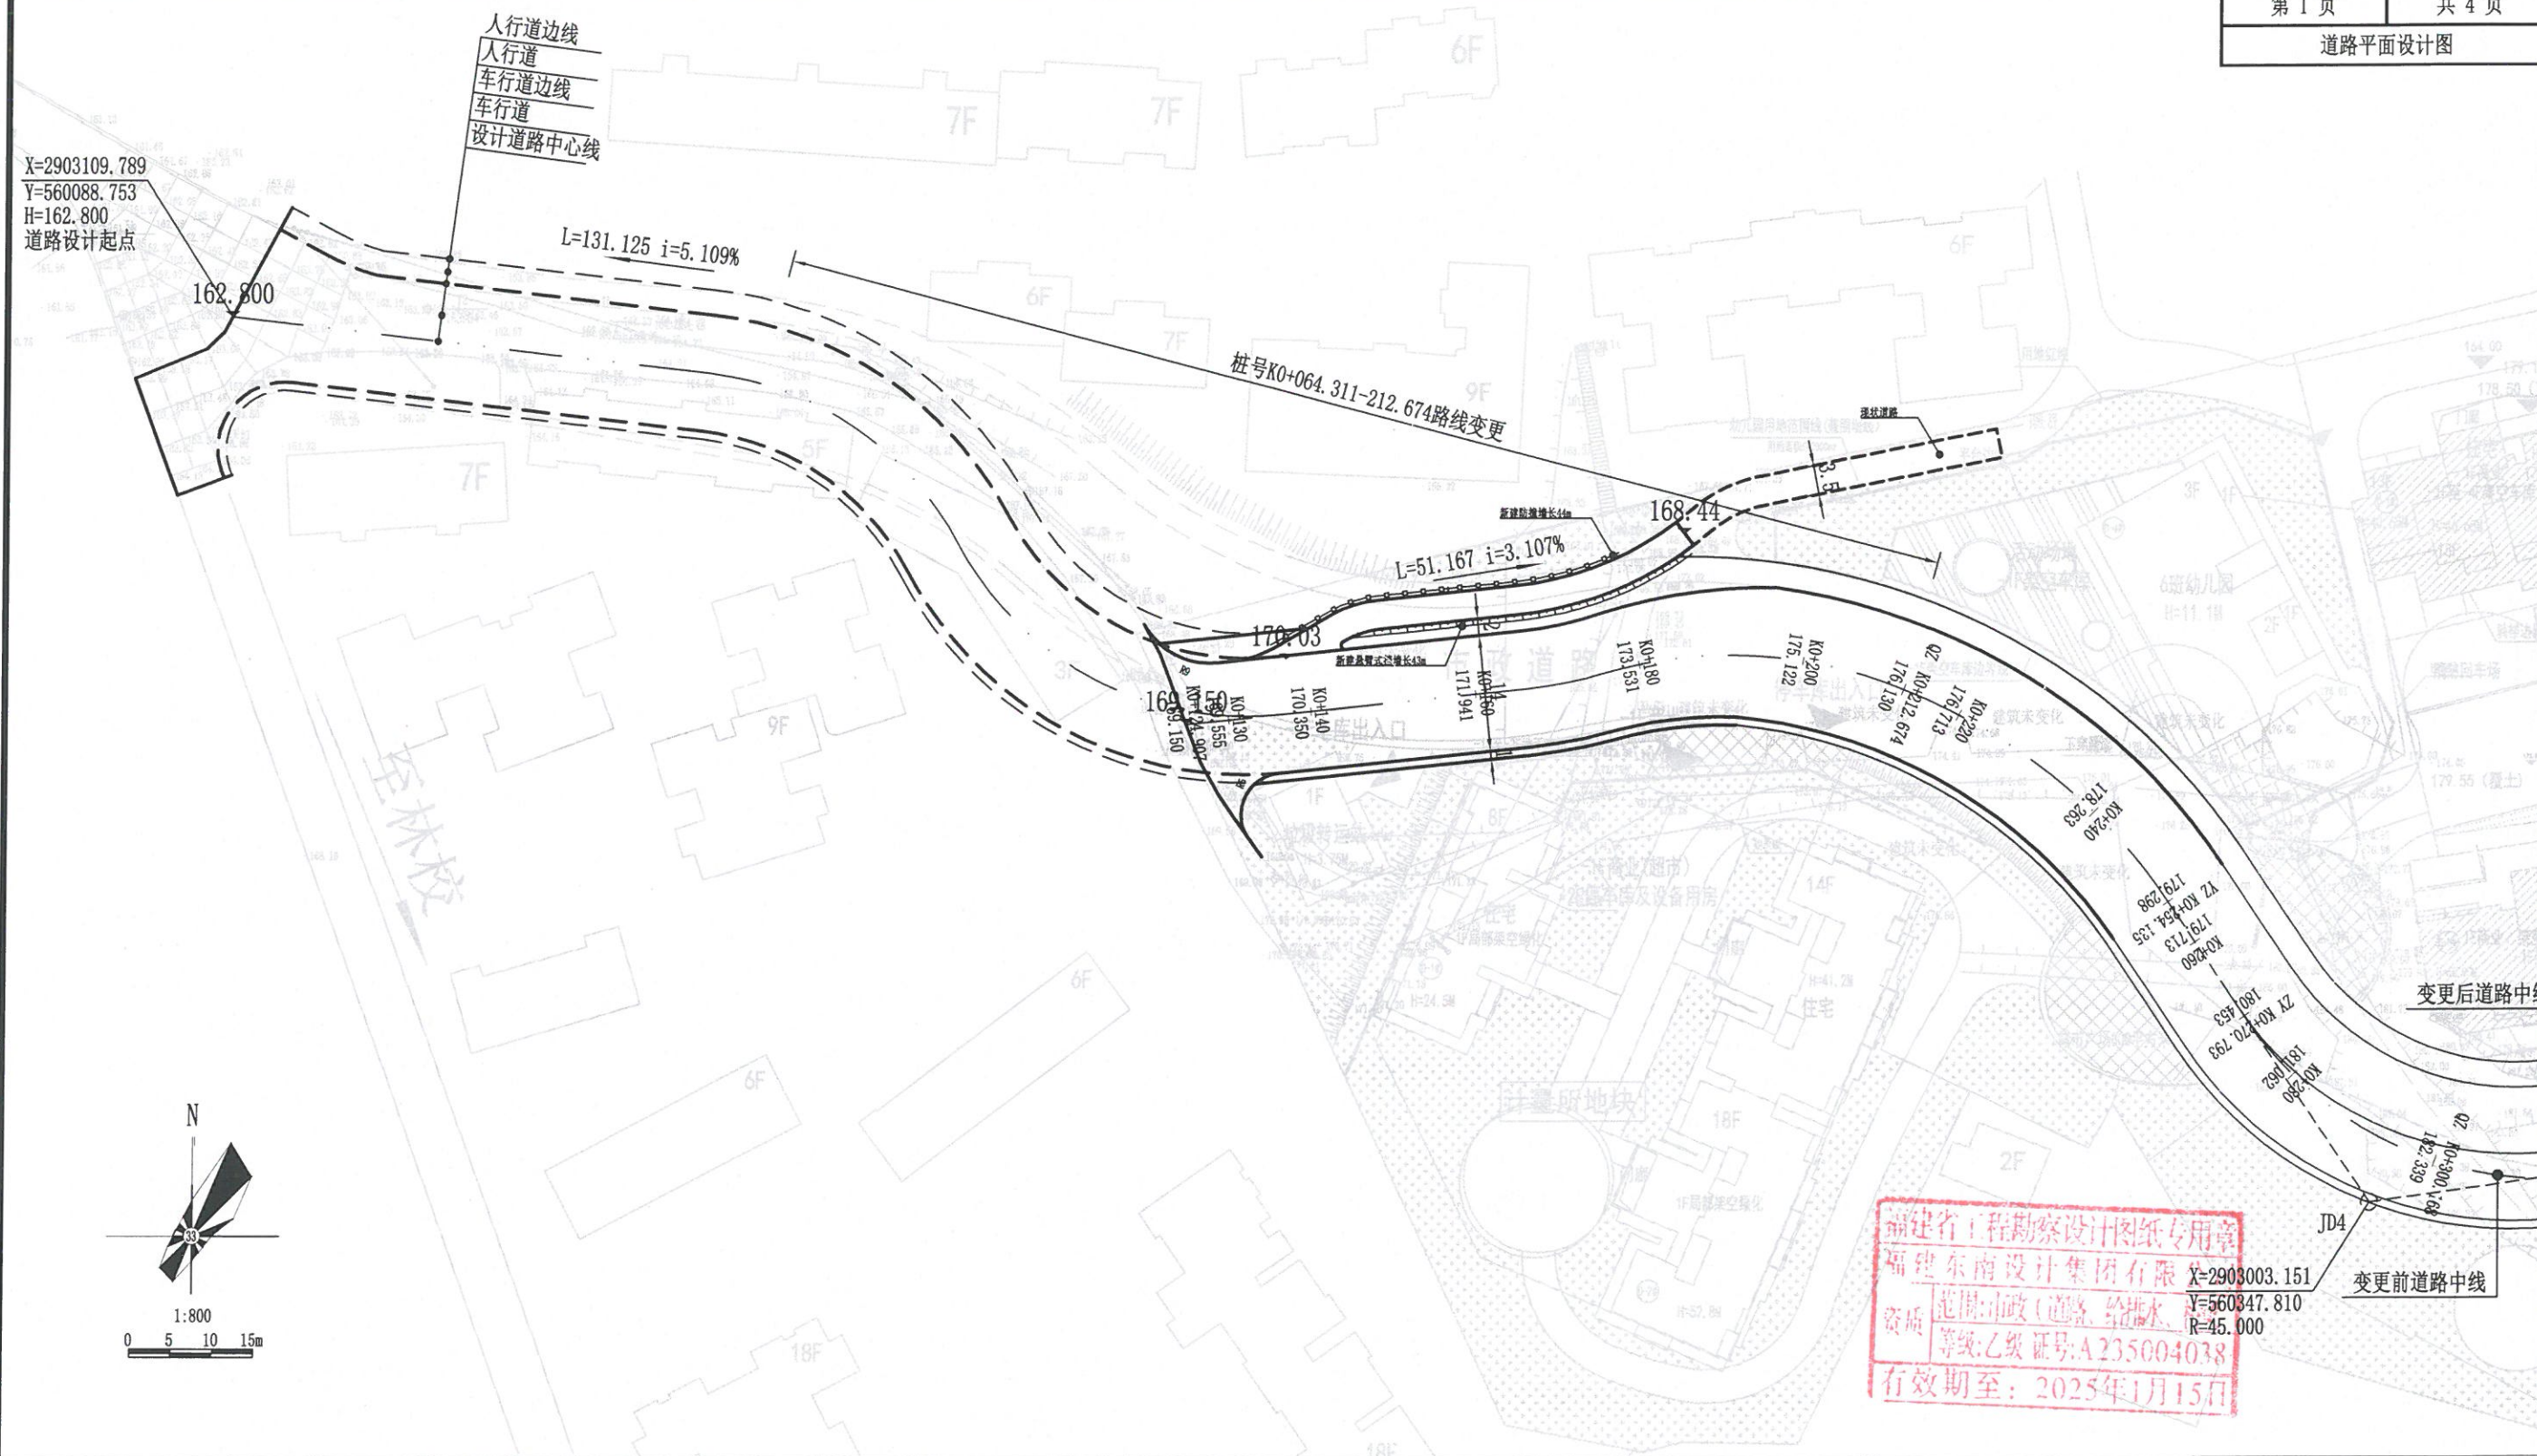

图例:

- 施工边界
—— 无障碍缘石坡道
□ —— 树池

道路平面设计图

说明:

- 1、本图坐标系为1980西安坐标系,中央子午线117°。
- 2、本图高程基准为1985国家高程基准,等高距为0.5米。
- 3、本图出图比例1:1000。



福建东南设计集团有限公司
福建省建设厅乙级证书第 A235004038

建设单位
工程名称

海翼瑞都(福建)房地产开发有限公司
三元区棚户区改造马道山-新田巷片区道路工程

图纸名称
工程编号

道路平面设计图
SZ2018-27 分项名称 道路工程

审核
项目负责人

陈少鑫

专业负责
校核

任玉昆

设计
绘图

任玉昆

日期
图号

2024年05月
道路平面-1/4

X=2903109.789
Y=560088.753
H=162.800
道路设计起点



图例:

- J—

—Y—

—W—

—DL—
- 新建给水管

—新建雨水管

—新建污水管

—新建强电管
- TX—


—RQ—
- 新建弱电管

—新建燃气管

管线综合平面设计图


说明:


- 1、本图坐标系为2000国家大地坐标系，中央子午线117°。
- 2、本图高程基准为1985国家高程基准，等高距为1.0米。
- 3、本图出图比例1:800。

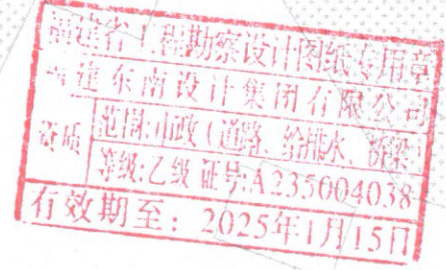

福建东南设计集团有限公司 SEADI 福建省建设厅乙级证书第 A235004038	建设单位	海翼瑞都（福建）房地产开发有限公司	图纸名称	管线综合平面设计图			审核	陈少智	专业负责	陈少智	设计	陈少智	日期	2024年05月
	工程名称	三元区棚户区改造马道山-新田巷片区道路工程	工程编号	SZ2018-27	分项名称	给排水工程	项目负责人	陈少智	校核	陈少智	绘图	陈少智	图号	PS-02-1

原平面

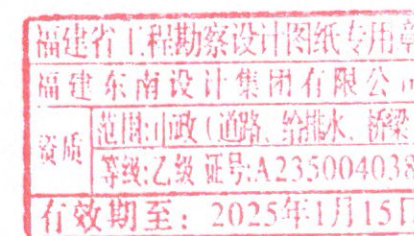

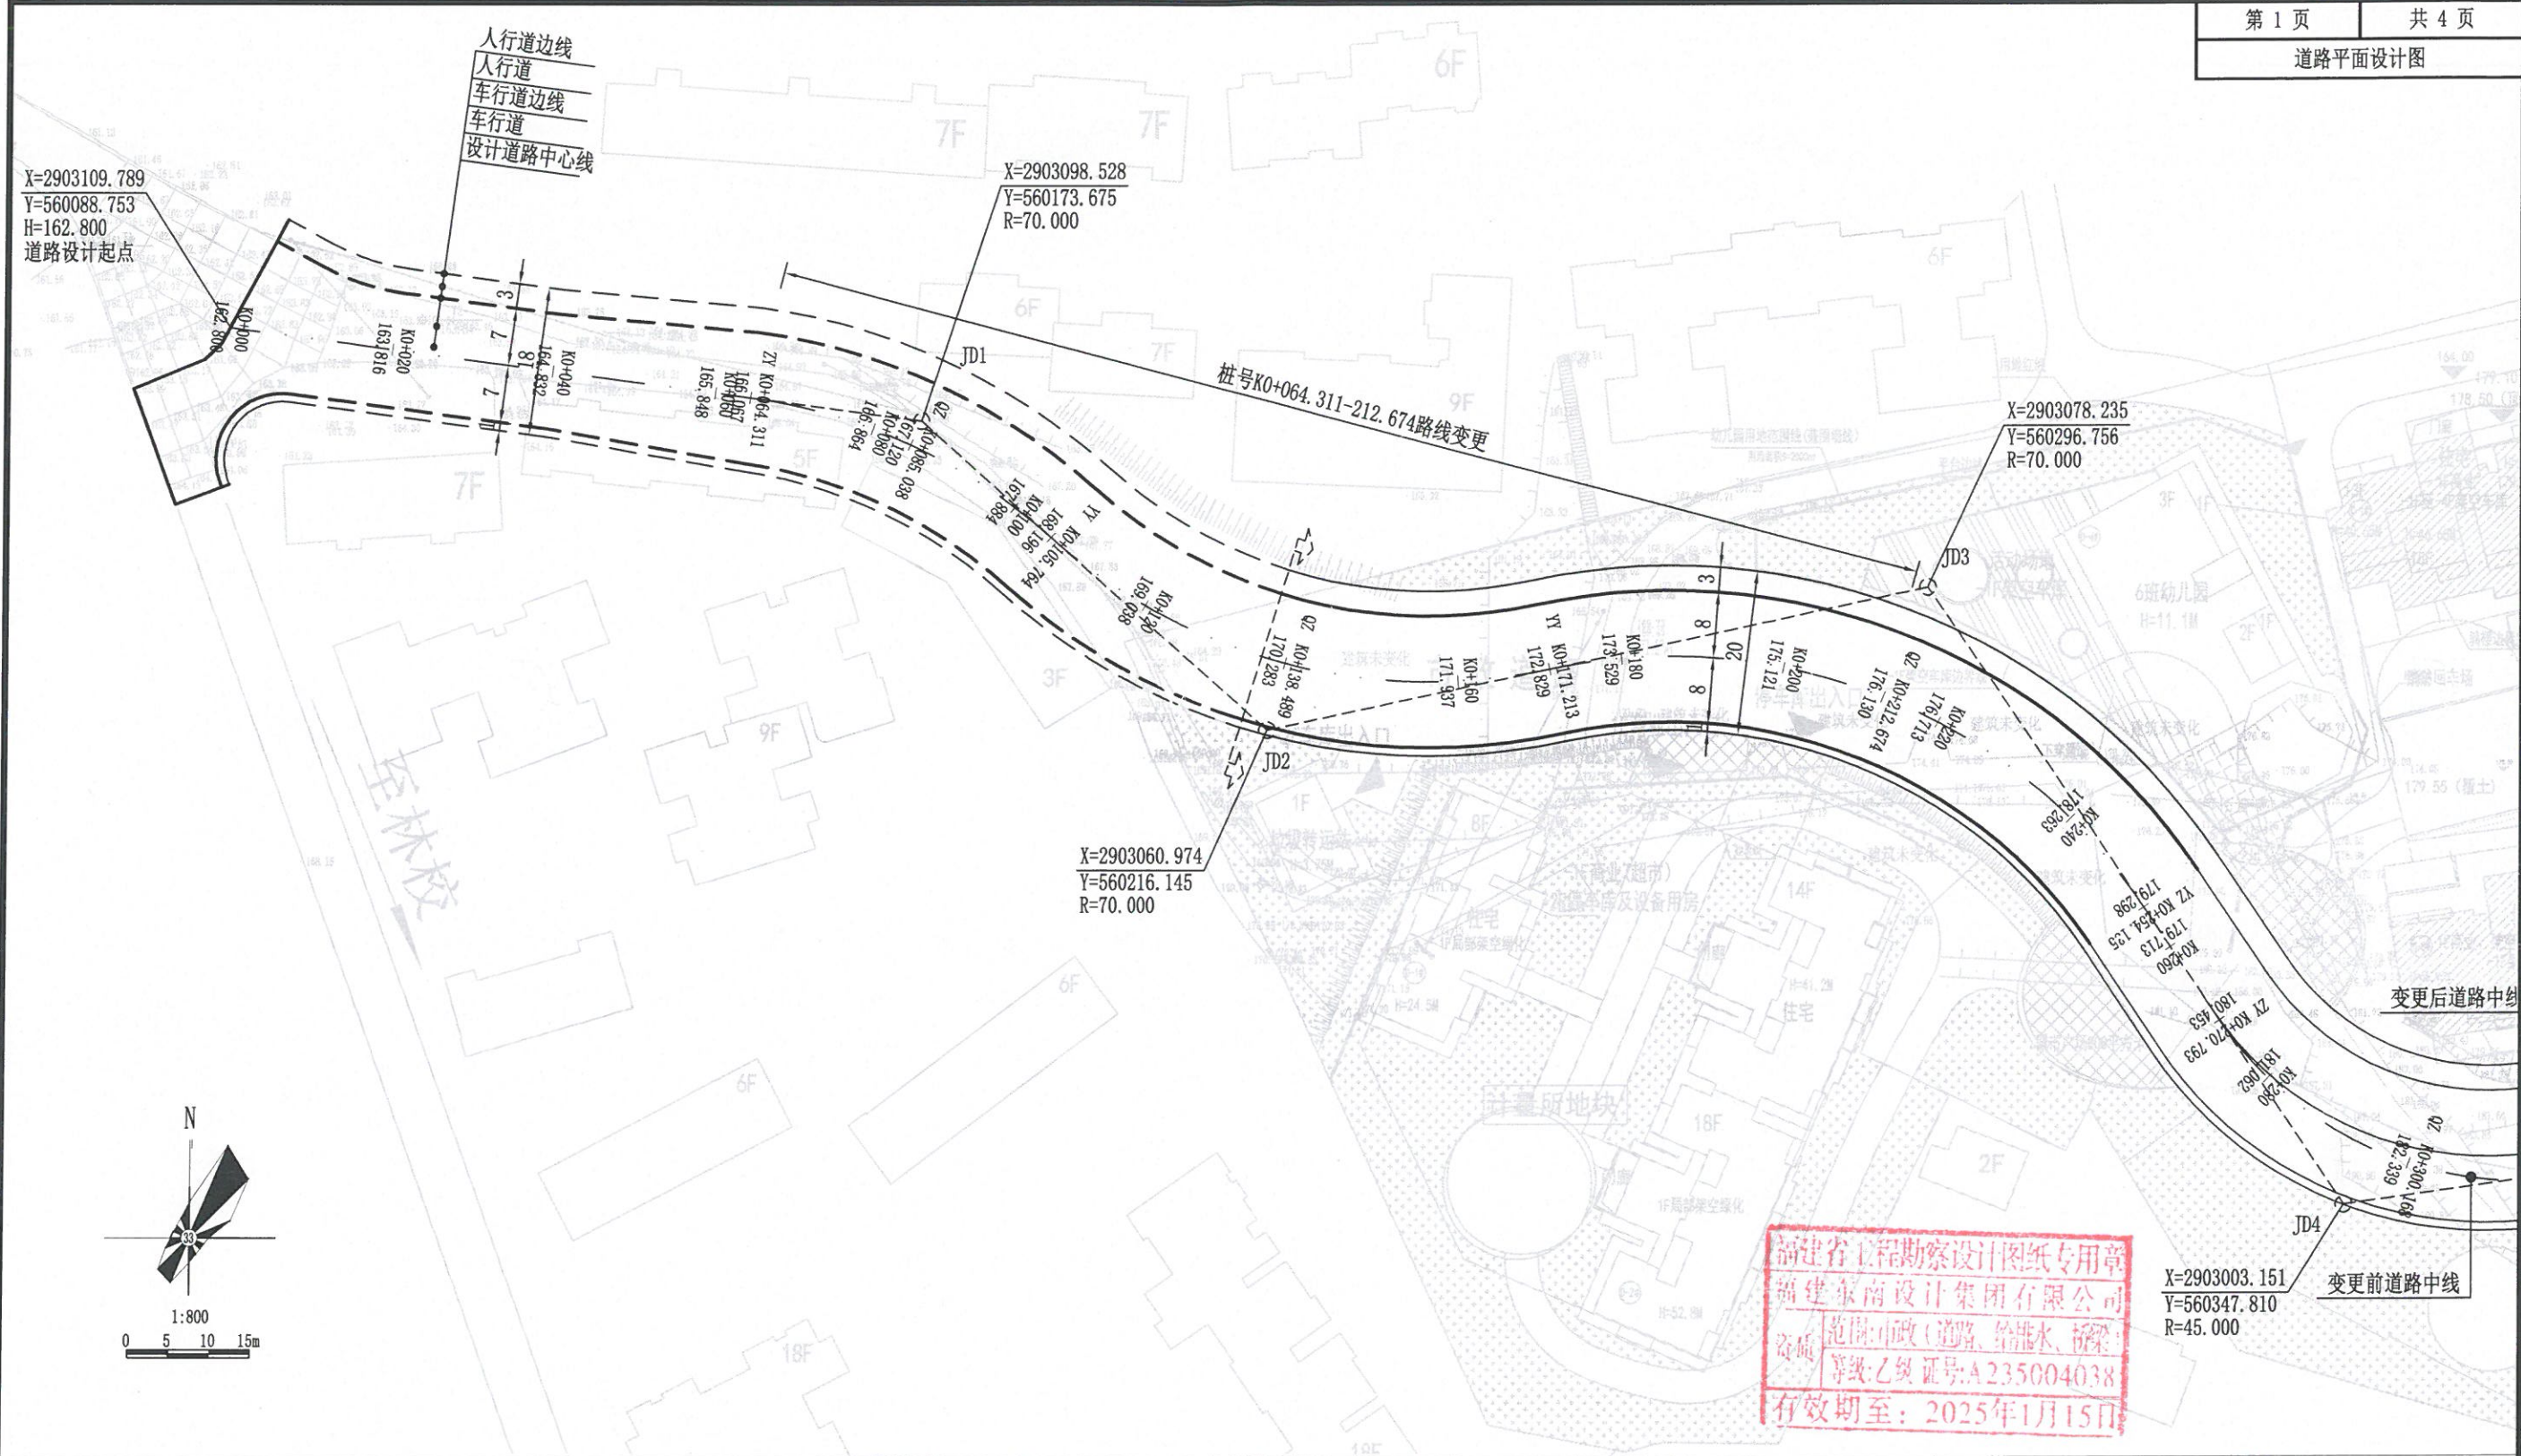

图例:


- 施工边界
- 无障碍缘石坡道
- — 树池

道路平面设计图

说明:

- 1、本图坐标系为1980西安坐标系,中央子午线117°。
- 2、本图高程基准为1985国家高程基准,等高距为0.5米。
- 3、本图出图比例1:1000。

 福建东南设计集团有限公司 SEADI 福建省建设厅乙级证书第 A235004038	建设单位	海翼瑞都（福建）房地产开发有限公司	图纸名称	道路平面设计图			审核		专业负责	任玉昆	设计	任玉昆	日期	2022年07月
	工程名称	三元区棚户区改造马道山-新田巷片区道路工程	工程编号	SZ2018-27	分项名称	道路工程	项目负责		校核	陈少鑫	绘图	任玉昆	图号	道路平面-1/4

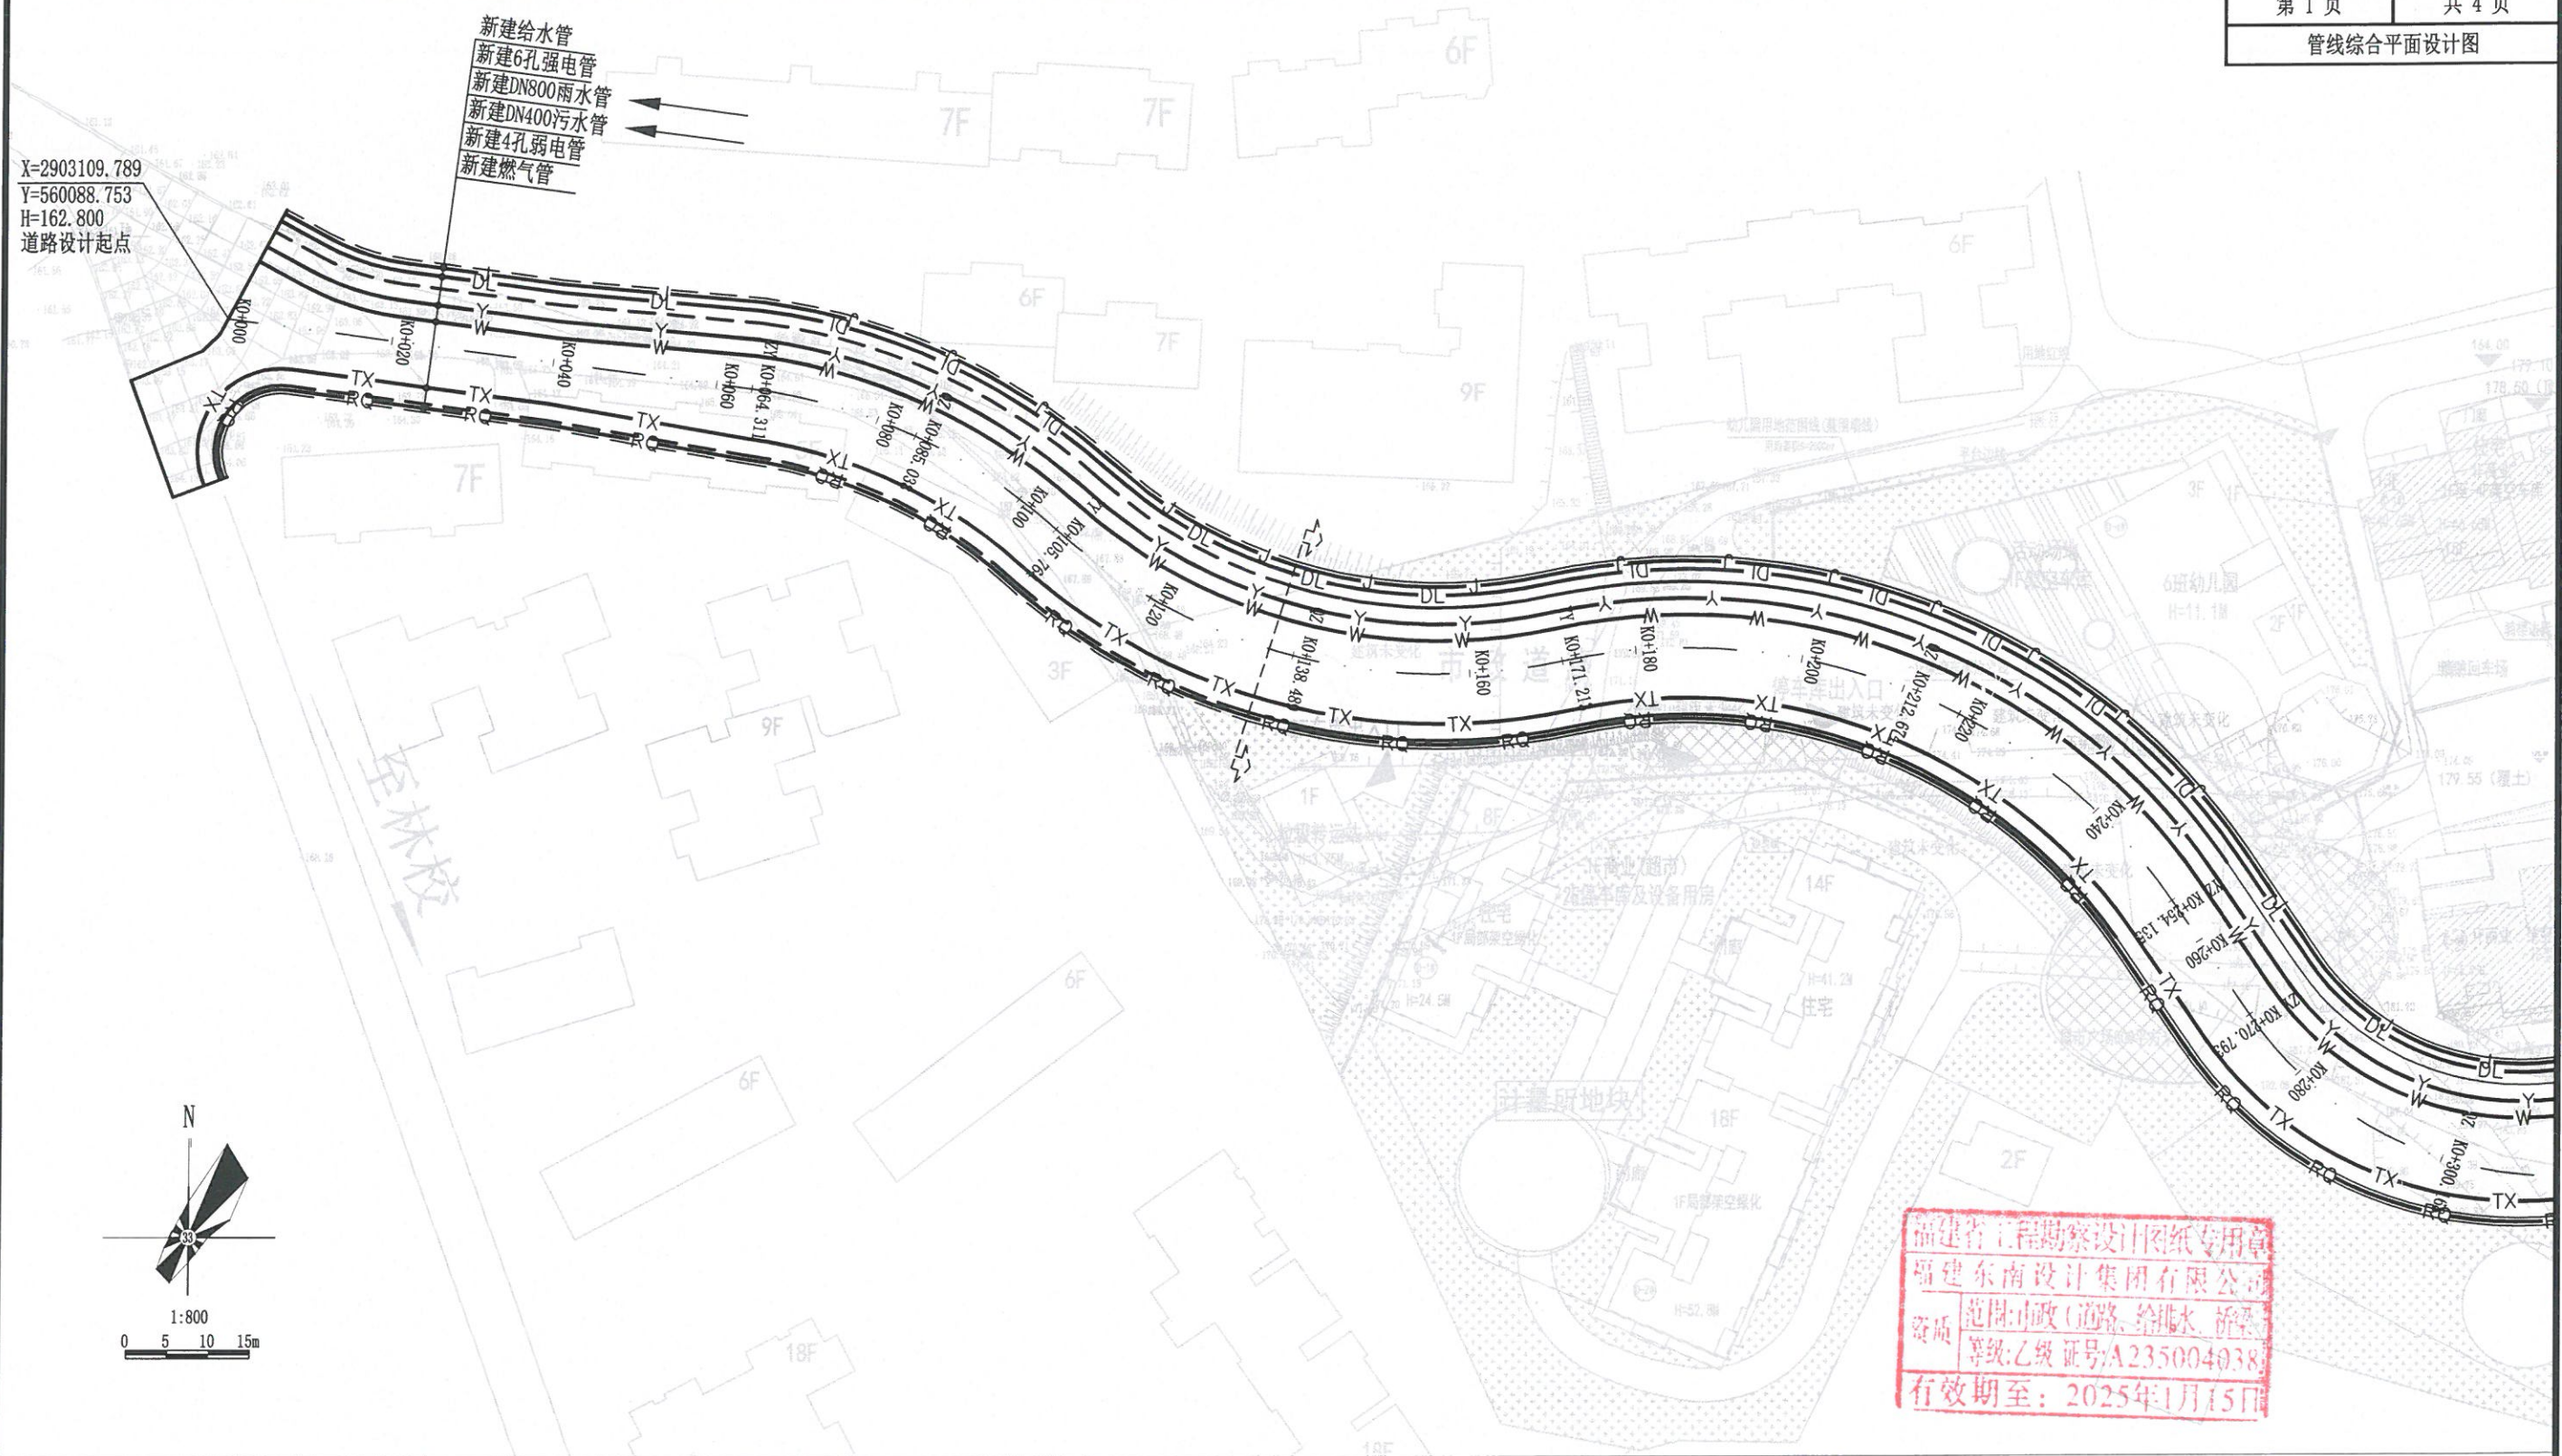

管线综合平面设计图

 福建东南设计集团有限公司 SEADI 福建省建设厅乙级证书第 A235004038	建设单位	海翼瑞都（福建）房地产开发有限公司	图纸名称	管线综合平面设计图			审 核		专业负责		设 计		日 期	2022年07月
	工程名称	三元区棚户区改造马道山-新田巷片区道路工程	工程编号	SZ2018-27	分项名称	给排水工程	项目负责		校 核		绘 图		图 号	PS-02-1