



福建一建金麟郡

规划及建筑方案设计（变更）

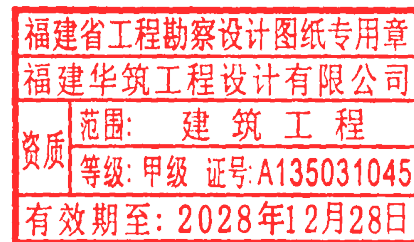

福建华筑工程设计有限公司
2024 年 6 月

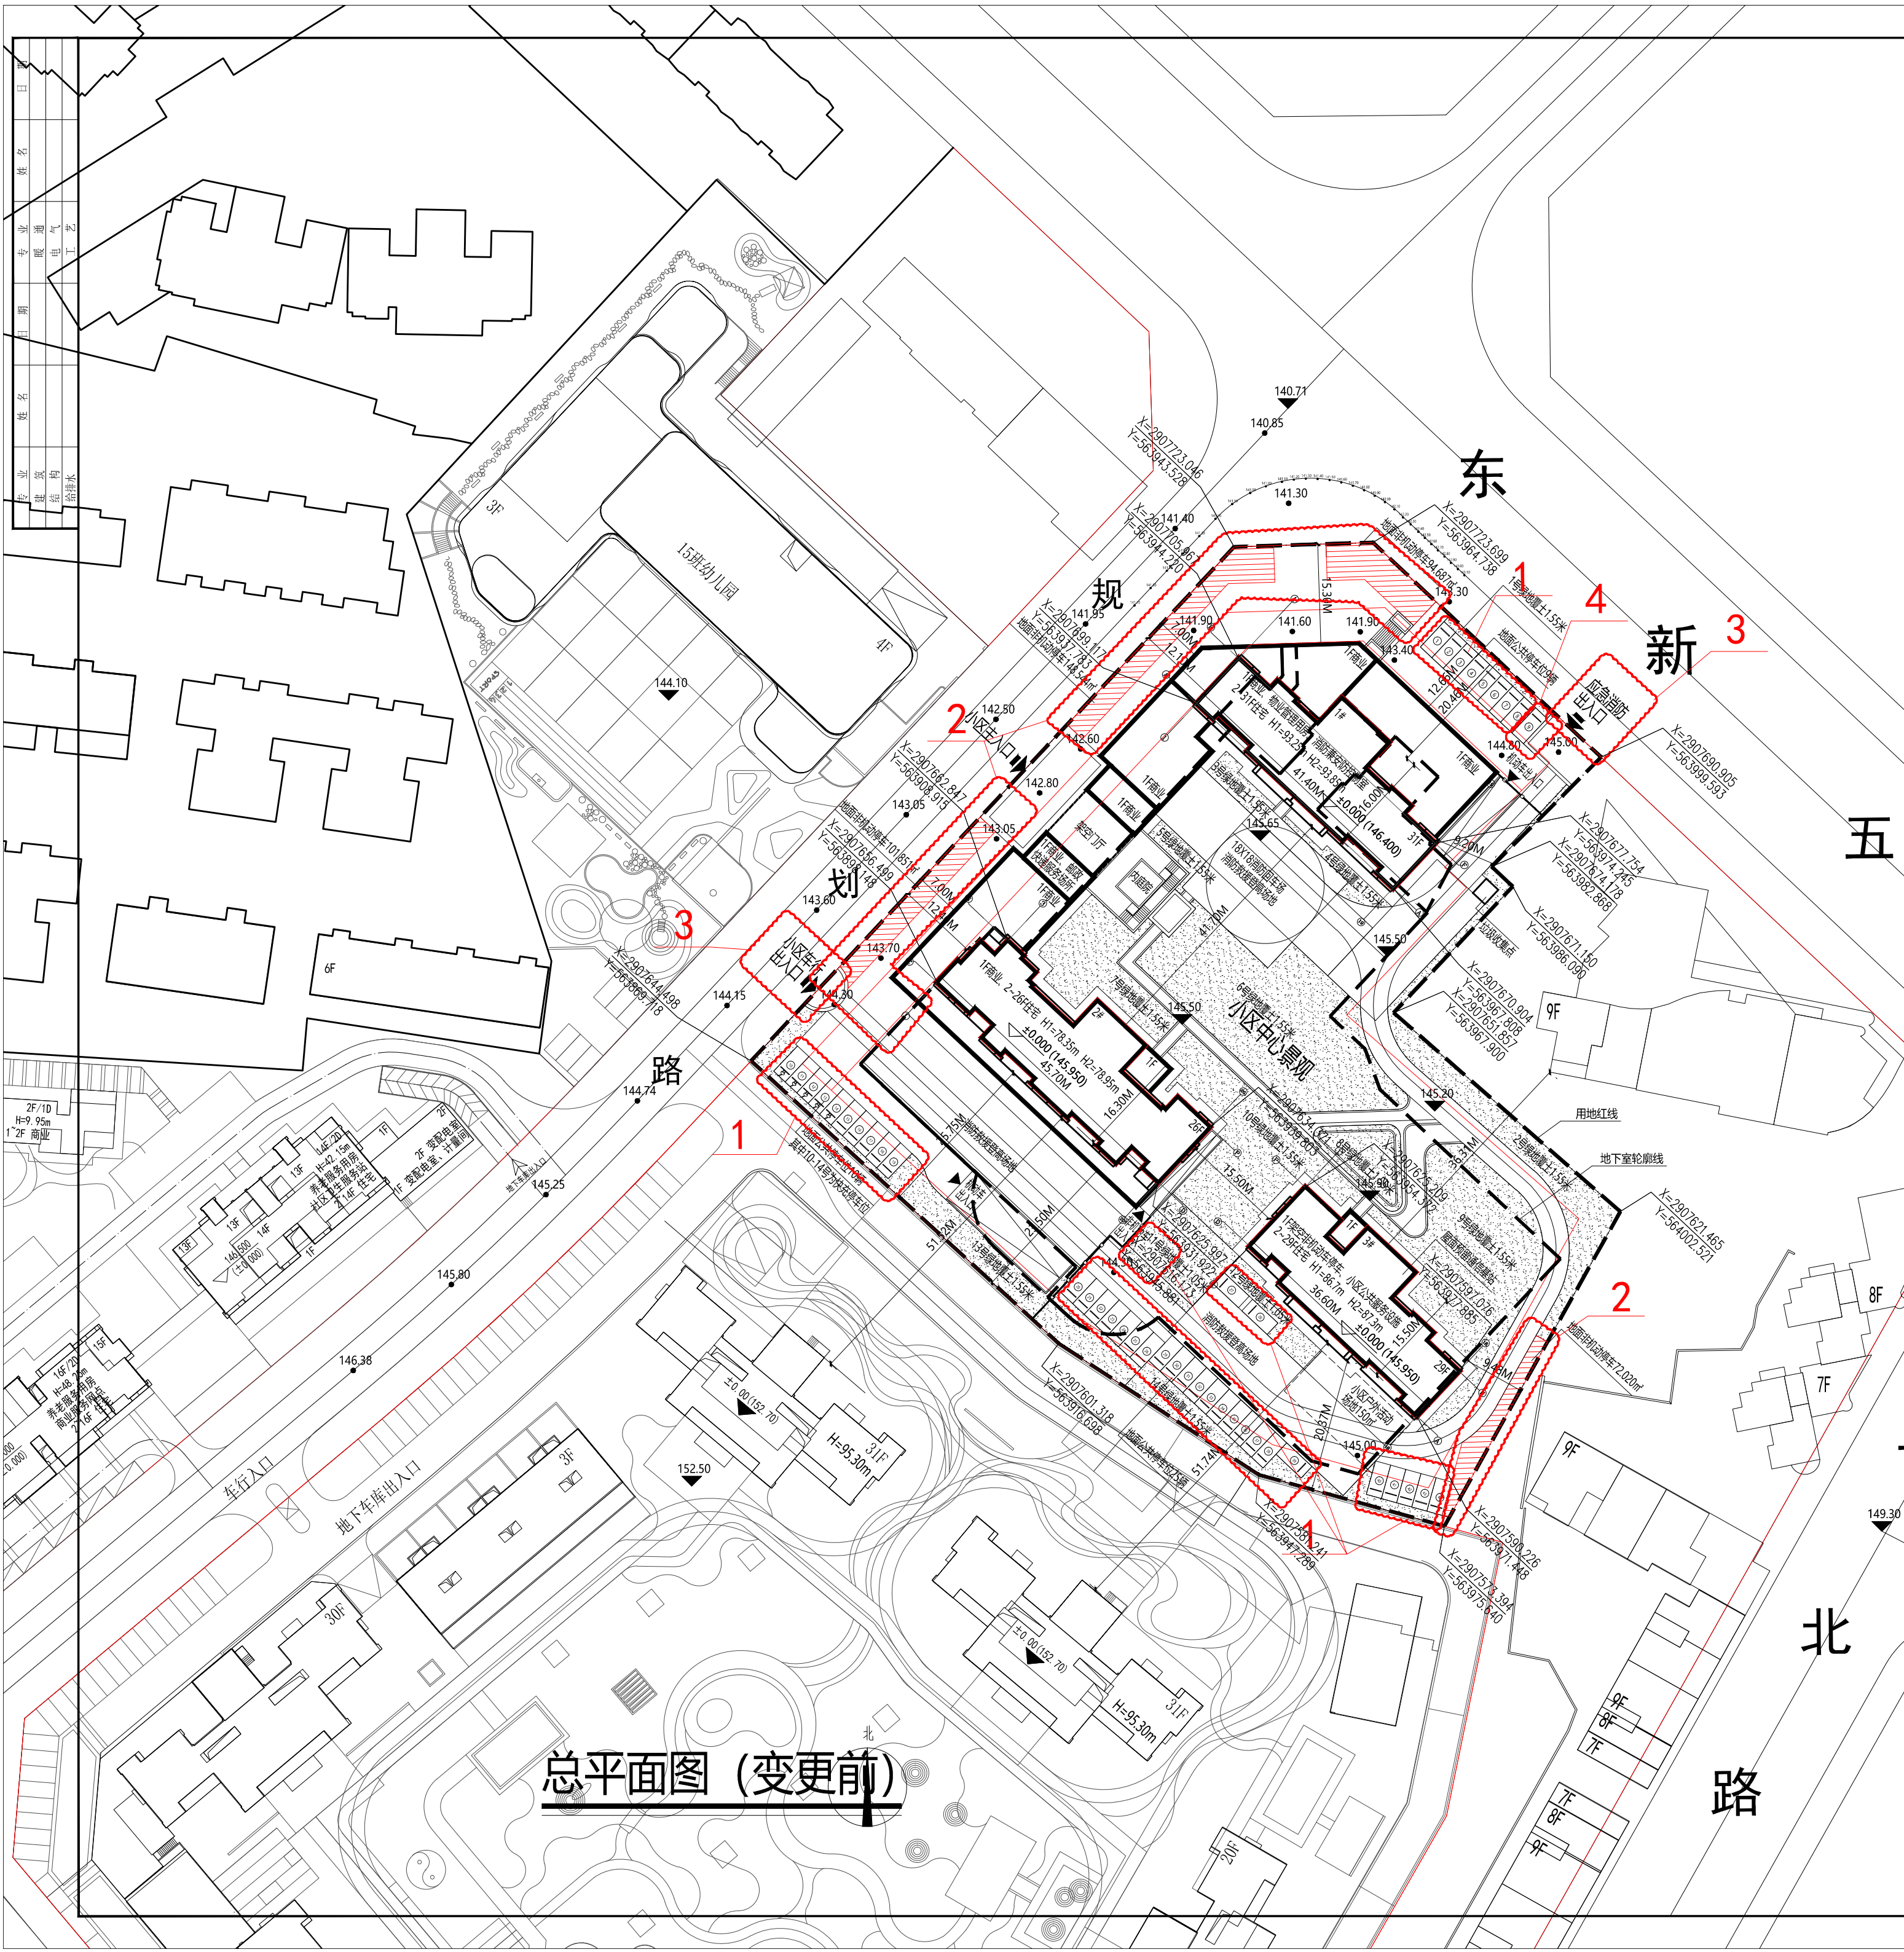

地块经济技术指标				建筑设计单位	
项目名称		单位	数值		
1	建设用地面积		m ²		11446.80
2	总建筑面积		m ²		53320.183
	其中	地上建筑面积	m ²	40496.579	
		地下建筑面积	m ²	12823.604	
3	计容建筑面积		m ²	40040.654	
	其中	住宅	m ²	37705.789	
		商业	m ²	2000.302	
		配套公建建筑面积	m ²	331.693	
		其中	物业管理用房（套内）	m ²	100.350
			小区公共服务设施（套内）	m ²	150.413
			快递服务场所（套内）	m ²	30.380
			消防兼安防控制室（套内）	m ²	50.550
		其他计容	m ²	2.870	
		烟囱	m ²	0.800	
	送风井	m ²	2.070		
不计容建筑面积		m ²	13279.529		
4	其中	地下室	m ²	12595.576	
		洗车场	m ²	212.639	
		架空、架空通道	m ²	196.260	
		架空非机动车停车	m ²	155.105	
		架空休闲	m ²	104.560	
		1#配电站通道	m ²	15.389	
5	容积率	-	3.498		
6	建筑密度	%	24.979%		
7	建筑占地面积	m ²	2859.273		
8	绿地率	%	25.00%		
9	绿化面积	m ²	2861.70		
10	总户数	户	331		
	其中	安置户数	户	226	
		商品房户数	户	105	
11	居住人口	人	1059		
12	机动车停车位		辆	441	
	其中	地上停车位	辆	44	
		地下停车位	辆	397	
13	非机动车停车面积		m ²	802.008	
	其中	地上非机动车停车面积	m ²	572.208	
		地下非机动车停车面积	m ²	229.800	



福建华筑工程设计有限公司
HuaZhu Architecture Design
工程设计证书编号: 甲级A135031045号

备注:


图纸专用章

图纸专用章

福建省工程勘察设计图纸专用章
福建华筑工程设计有限公司
范围: 建筑工程
资质等级: 甲级 证号: A135031045
有效期至: 2028年12月28日

备注:
1.机动车位计算方式为计容面积/100*1.1辆:
40040.654/100*1.1=441辆
2.非机动车位计算方式为计容面积/100*2㎡:
40040.654/100*2=800.813㎡

总平面图 (变更前)

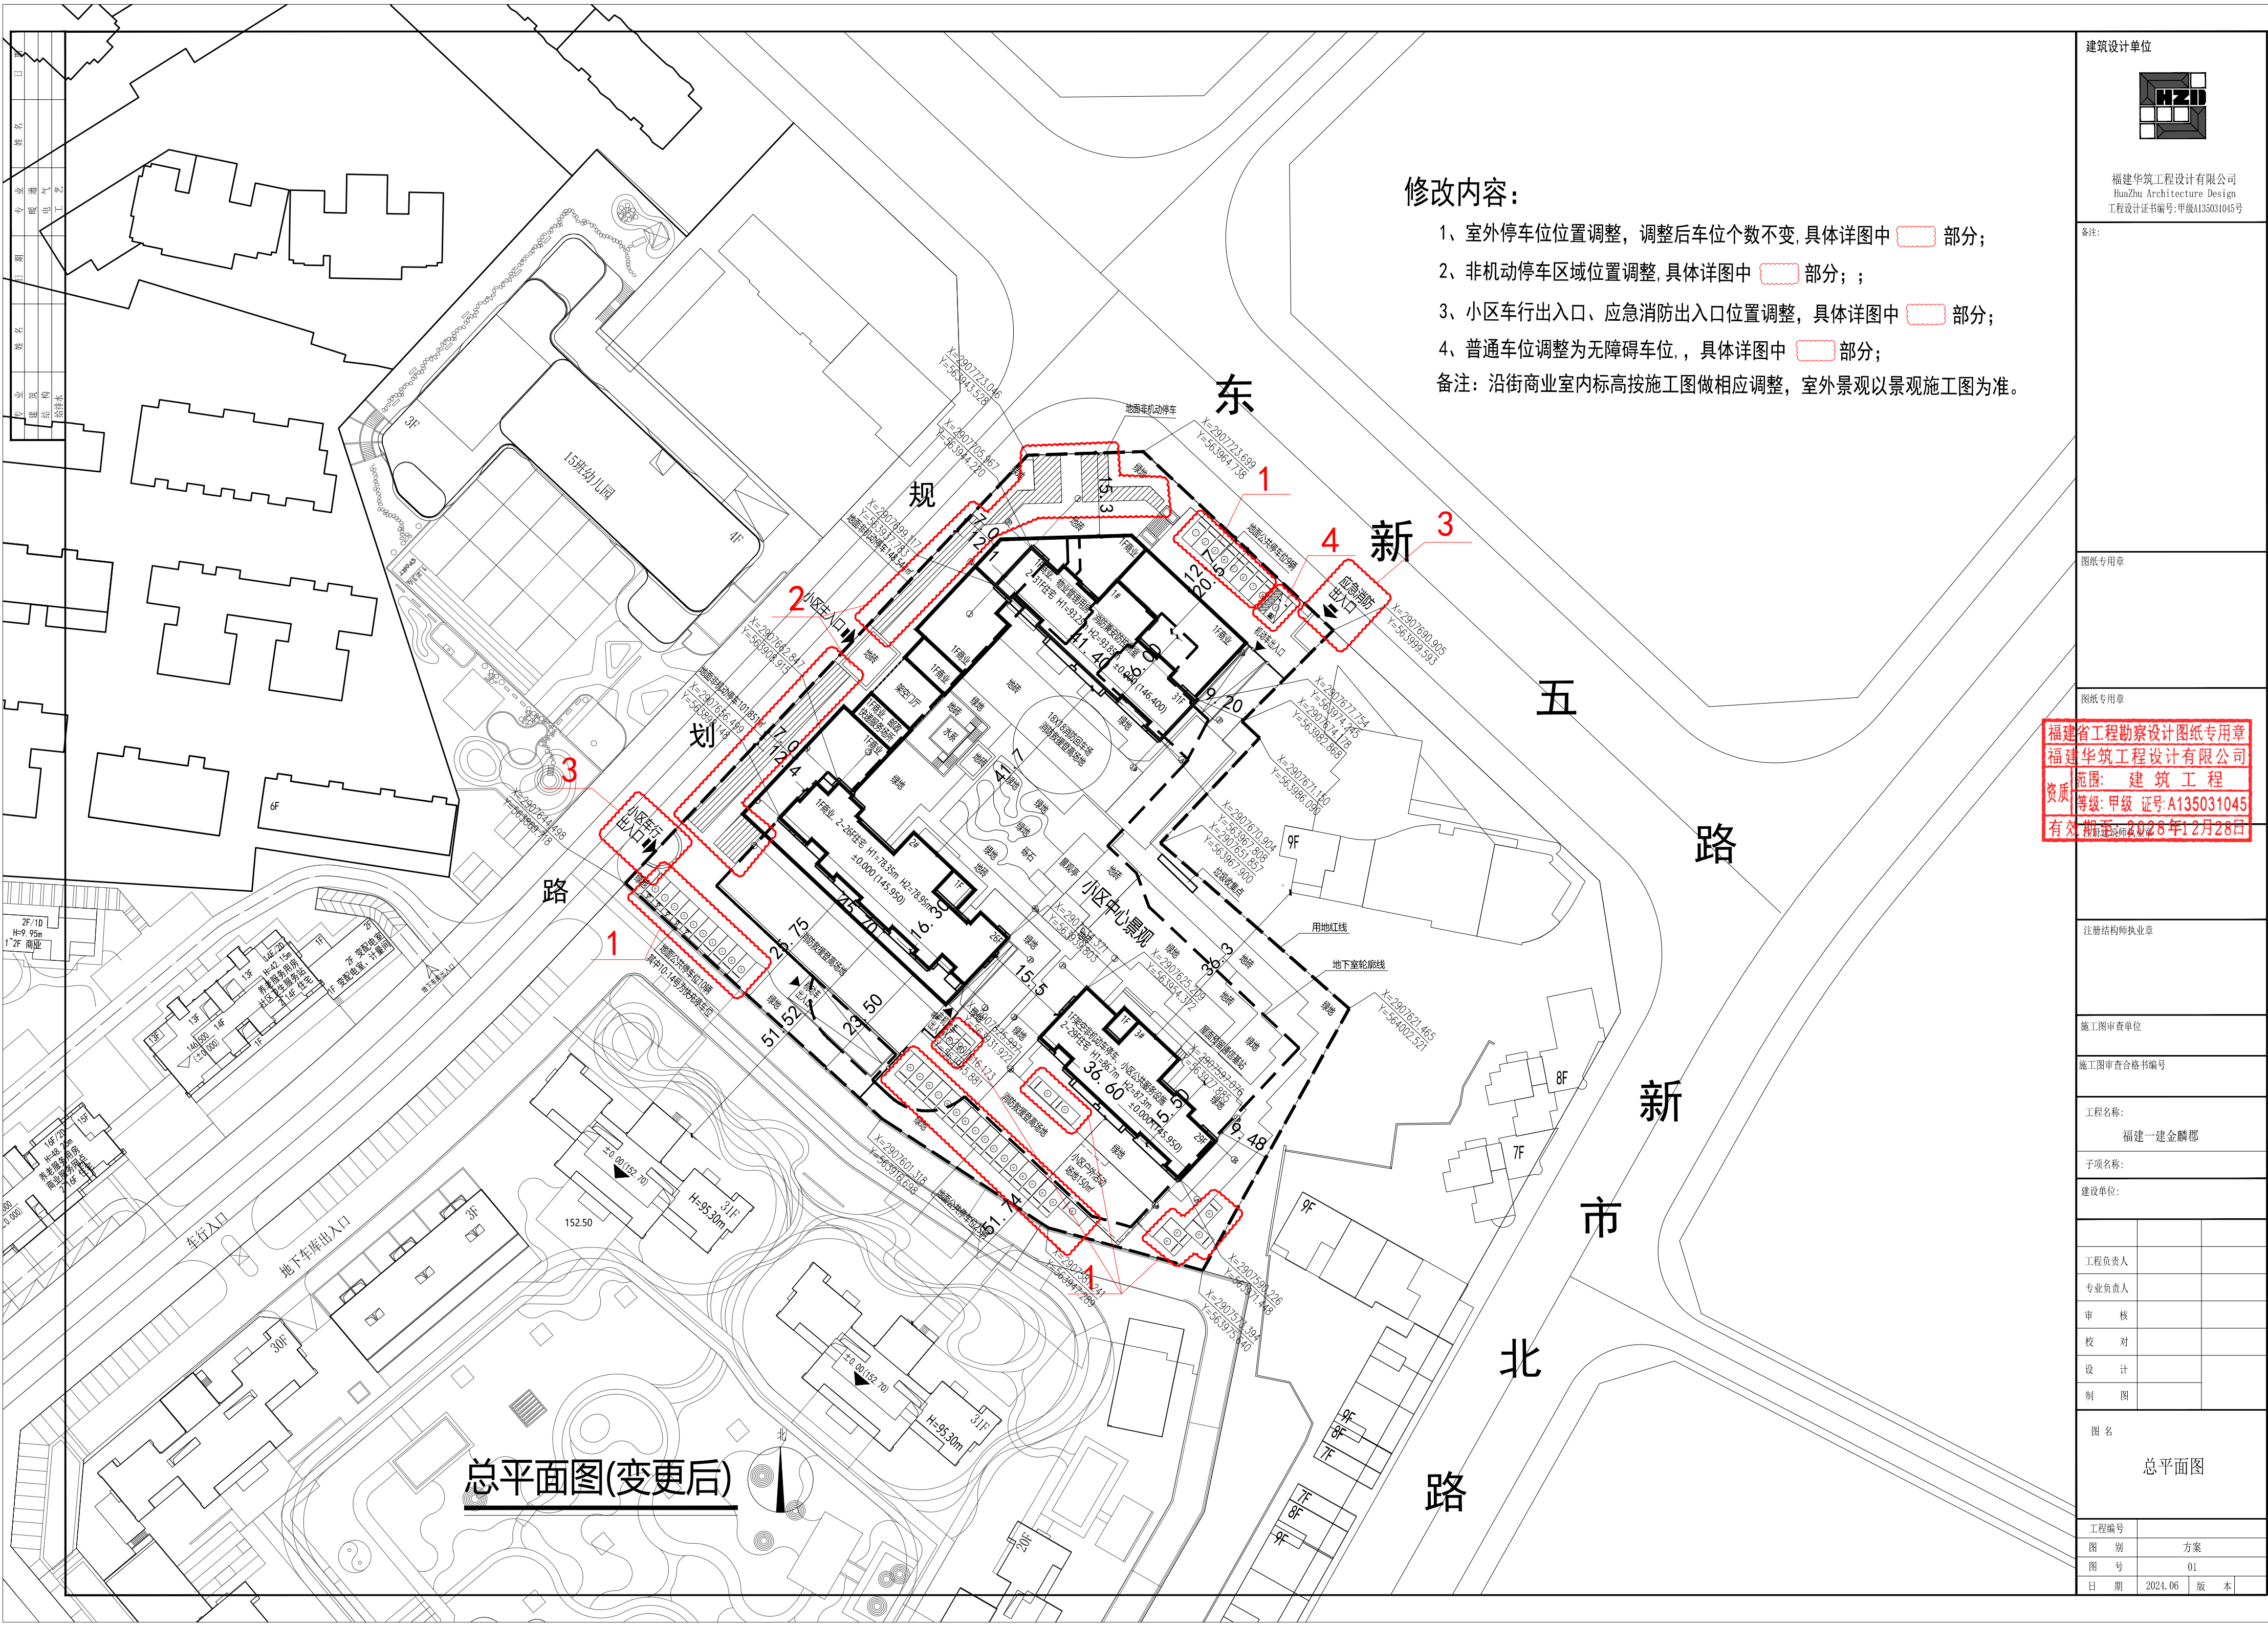

修改内容:

- 1、室外停车位位置调整, 调整后车位个数不变, 具体详图中 部分;
 - 2、非机动车停车区域位置调整, 具体详图中 部分; ;
 - 3、小区车行出入口、应急消防出入口位置调整, 具体详图中 部分;
 - 4、普通车位调整为无障碍车位, , 具体详图中 部分;
- 备注: 沿街商业室内标高按施工图做相应调整, 室外景观以景观施工图为准。

建筑设计单位



福建华筑工程设计有限公司
HuaZhu Architecture Design
工程设计证书编号: 甲级A135031045号

备注:

图纸专用章

图纸专用章

福建省工程勘察设计图纸专用章
福建华筑工程设计有限公司
范围: 建筑工程
资质等级: 甲级 证号: A135031045
有效期至: 2028年12月28日

注册结构师执业章

施工图审查单位

施工图审查合格书编号

工程名称:

福建一建金麟郡

子项名称:

建设单位:

工程负责人

专业负责人

审核

校对

设计

制图

图名

总平面图

工程编号

图别


方案

图号


01

日期

2024.06 版本

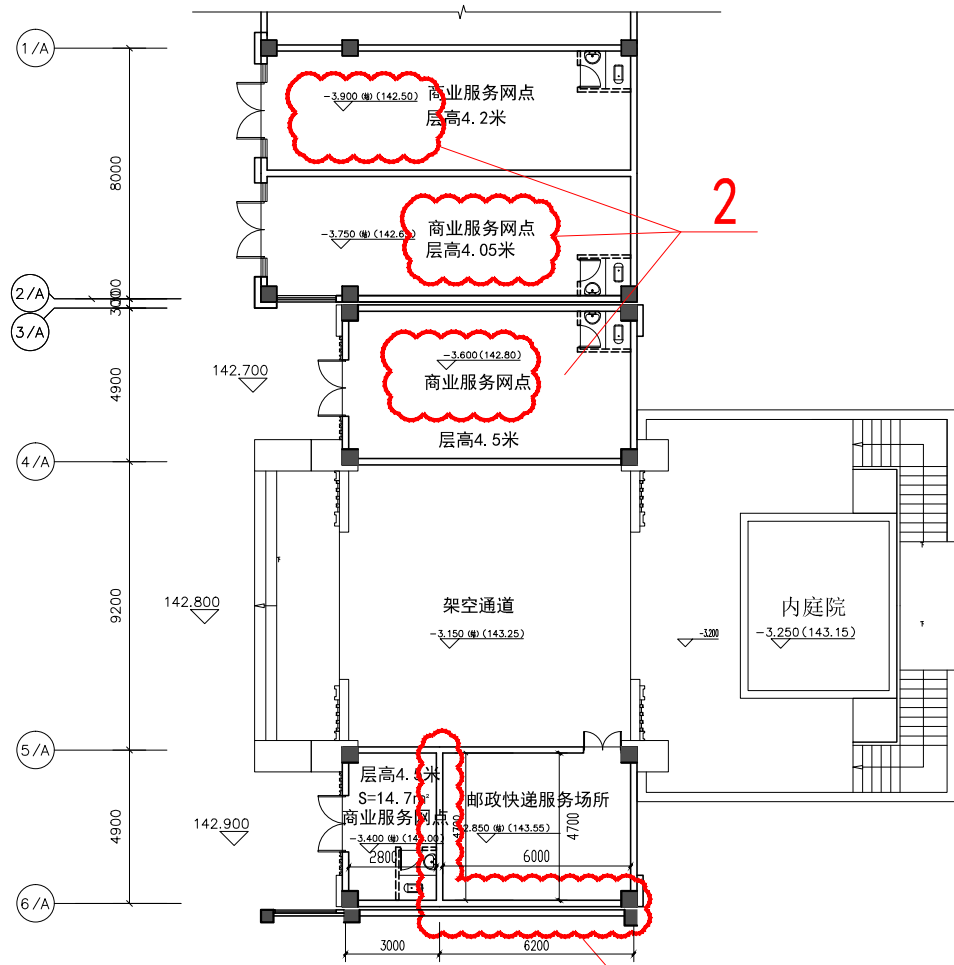

1#楼一层局部平面图（变更前）

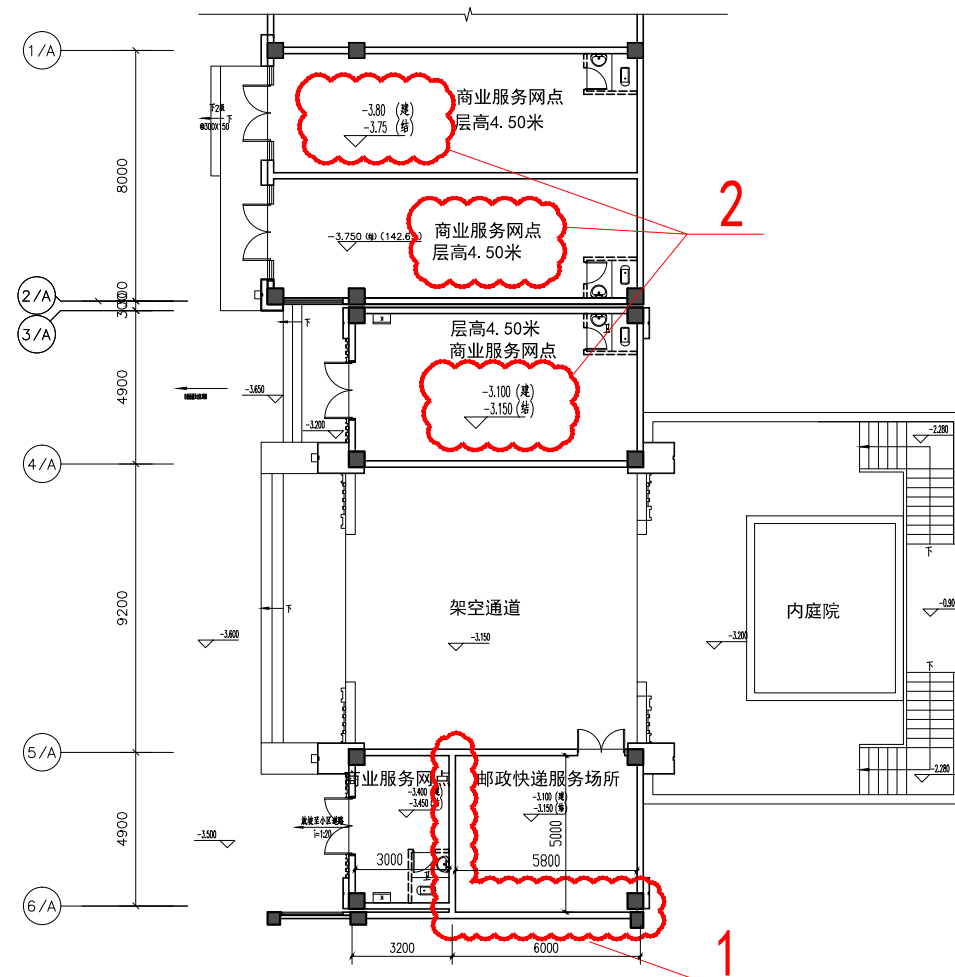


1#楼一层局部平面图（变更后）


- 1、S-A轴~S-B轴店铺与邮政快递墙体调整，邮政快递服务场所6/A轴墙体取消；
- 2、沿街商业标高调整；

福建省工程勘察设计图纸专用章
福建华筑工程设计有限公司
范围：建筑工程
资质等级：甲级 证号：A135031045
有效期至：2028年12月28日

福建华筑工程设计有限公司						证书编号	A135031045	审查批准号		工程号	2022058	项目号
						建设单位	福建一建集团三明（绿岩）盛建置业有限公司			阶段	方案	
审定			校对			项目名称	福建一建金麟郡			专业	建筑	
审核			设计			比例				图号		版本号
项目负责			专业负责				1#楼一层局部平面图			日期	2024.06	

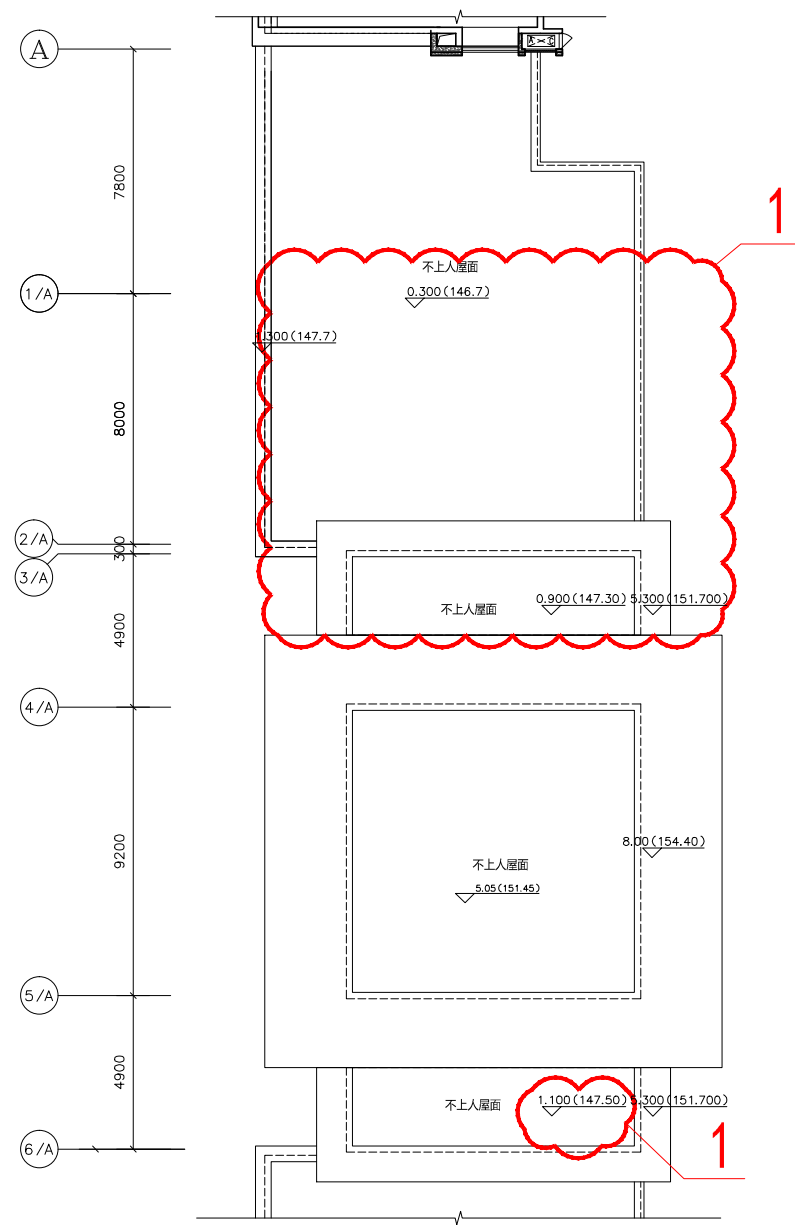

1#楼二层局部平面图（变更前）

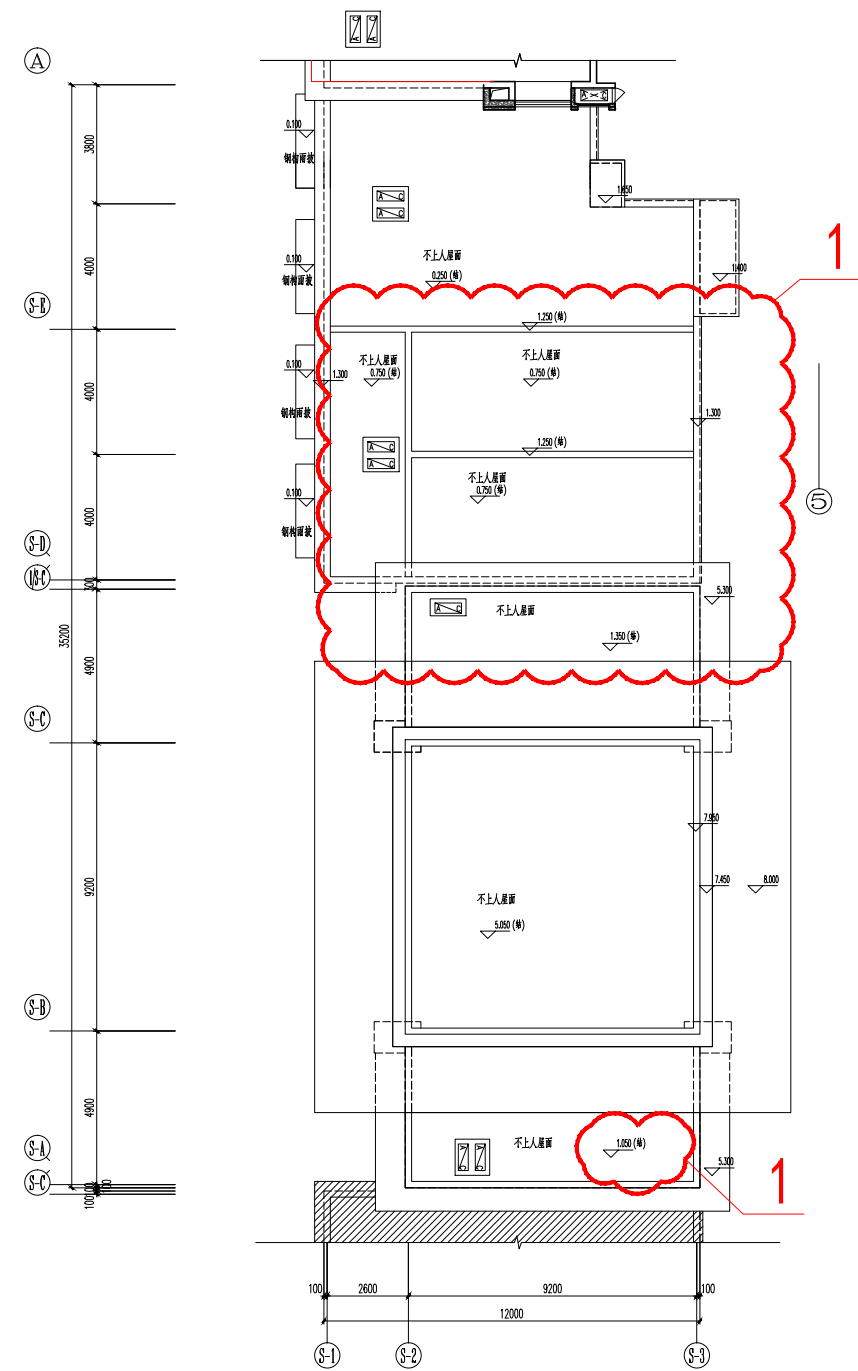


1#楼二层局部平面图（变更后）


1、商业及邮政快递服务场所屋面结构标高调整；造型外立面调整；

福建省工程勘察设计图纸专用章
福建华筑工程设计有限公司
范围：建筑工程
资质等级：甲级 证号：A135031045
有效期至：2028年12月28日

福建华筑工程设计有限公司						证书编号	A135031045	审查批准号		工程号	2022058	项目号
						建设单位	福建一建集团三明（绿岩）盛建置业有限公司			阶段	方案	
审定			校对			项目名称	福建一建金麟郡			专业	建筑	
审核			设计			比例				图号		版本号
项目负责			专业负责				1#楼二层局部平面图			日期	2024.06	

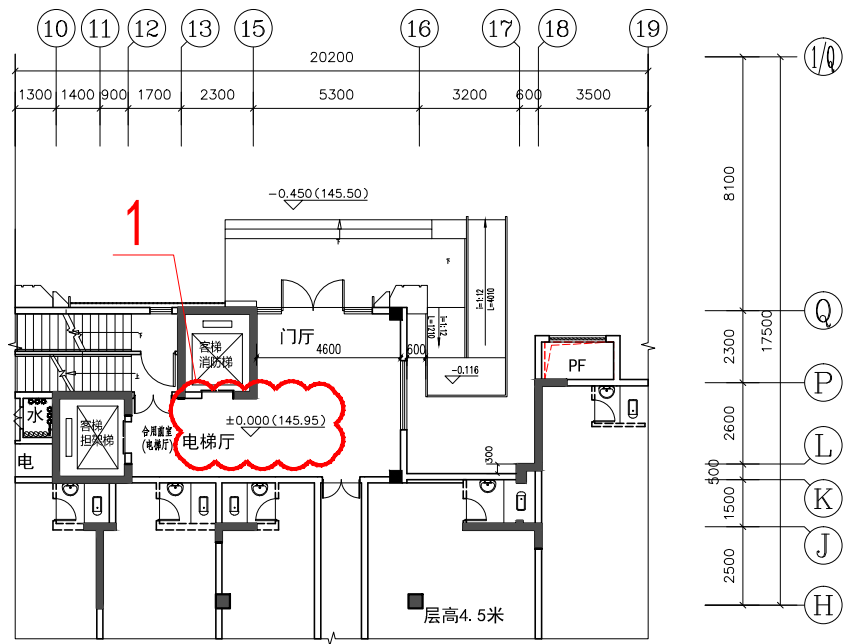

2#楼一层局部平面图（变更前）

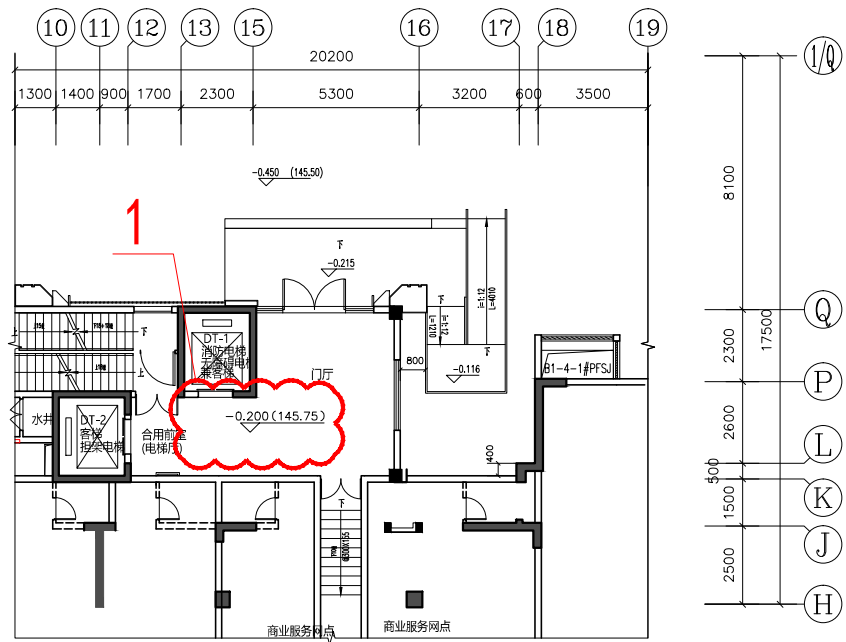


2#楼一层局部平面图（变更后）

1、一层门厅室内标高降低0.2m;


福建省工程勘察设计图纸专用章
福建华筑工程设计有限公司
范围: 建筑工程
资质等级: 甲级 证号: A135031045
有效期至: 2028年12月28日

福建华筑工程设计有限公司						证书编号	A135031045	审查批准号		工程号	2022058	项目号
						建设单位	福建一建集团三明（绿岩）盛建置业有限公司			阶段	方案	
审定			校对			项目名称	福建一建金麟郡			专业	建筑	版本号
审核			设计			比例				图号		
项目负责			专业负责				2#楼一层局部平面图			日期	2024.06	

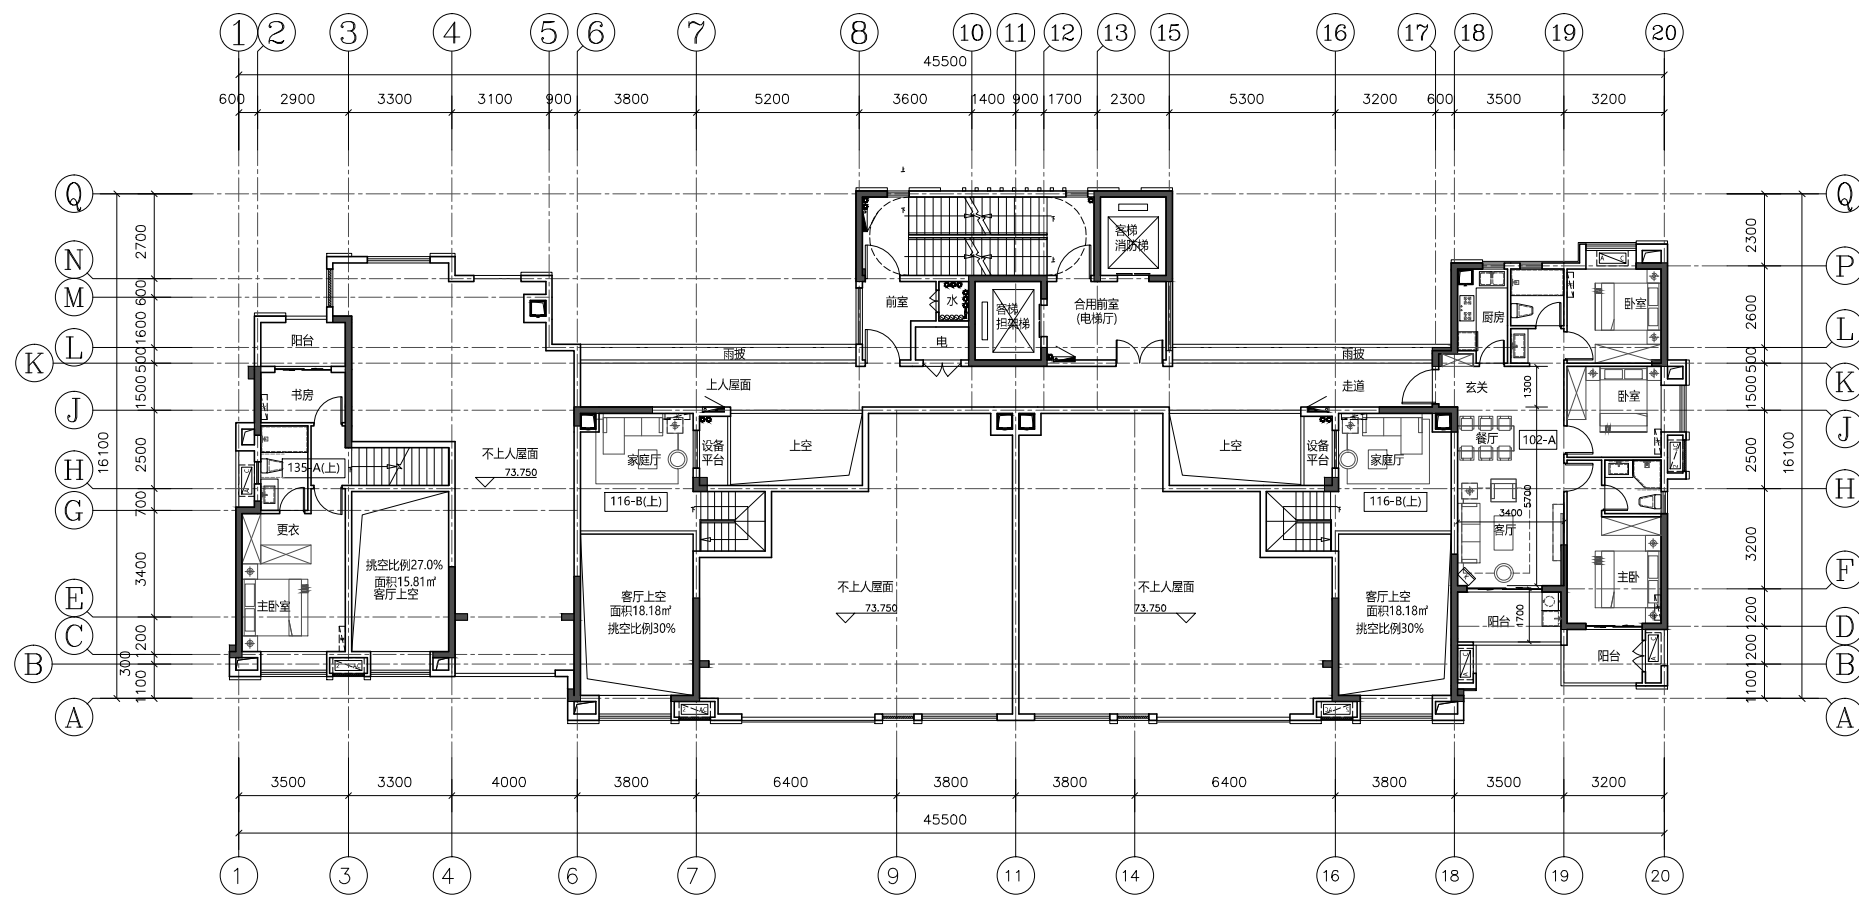

2#楼二十六层平面图（变更前）


福建省工程勘察设计图纸专用章
福建华筑工程设计有限公司
范围：建筑工程
资质等级：甲级 证号：A135031045
有效期至：2028年12月28日

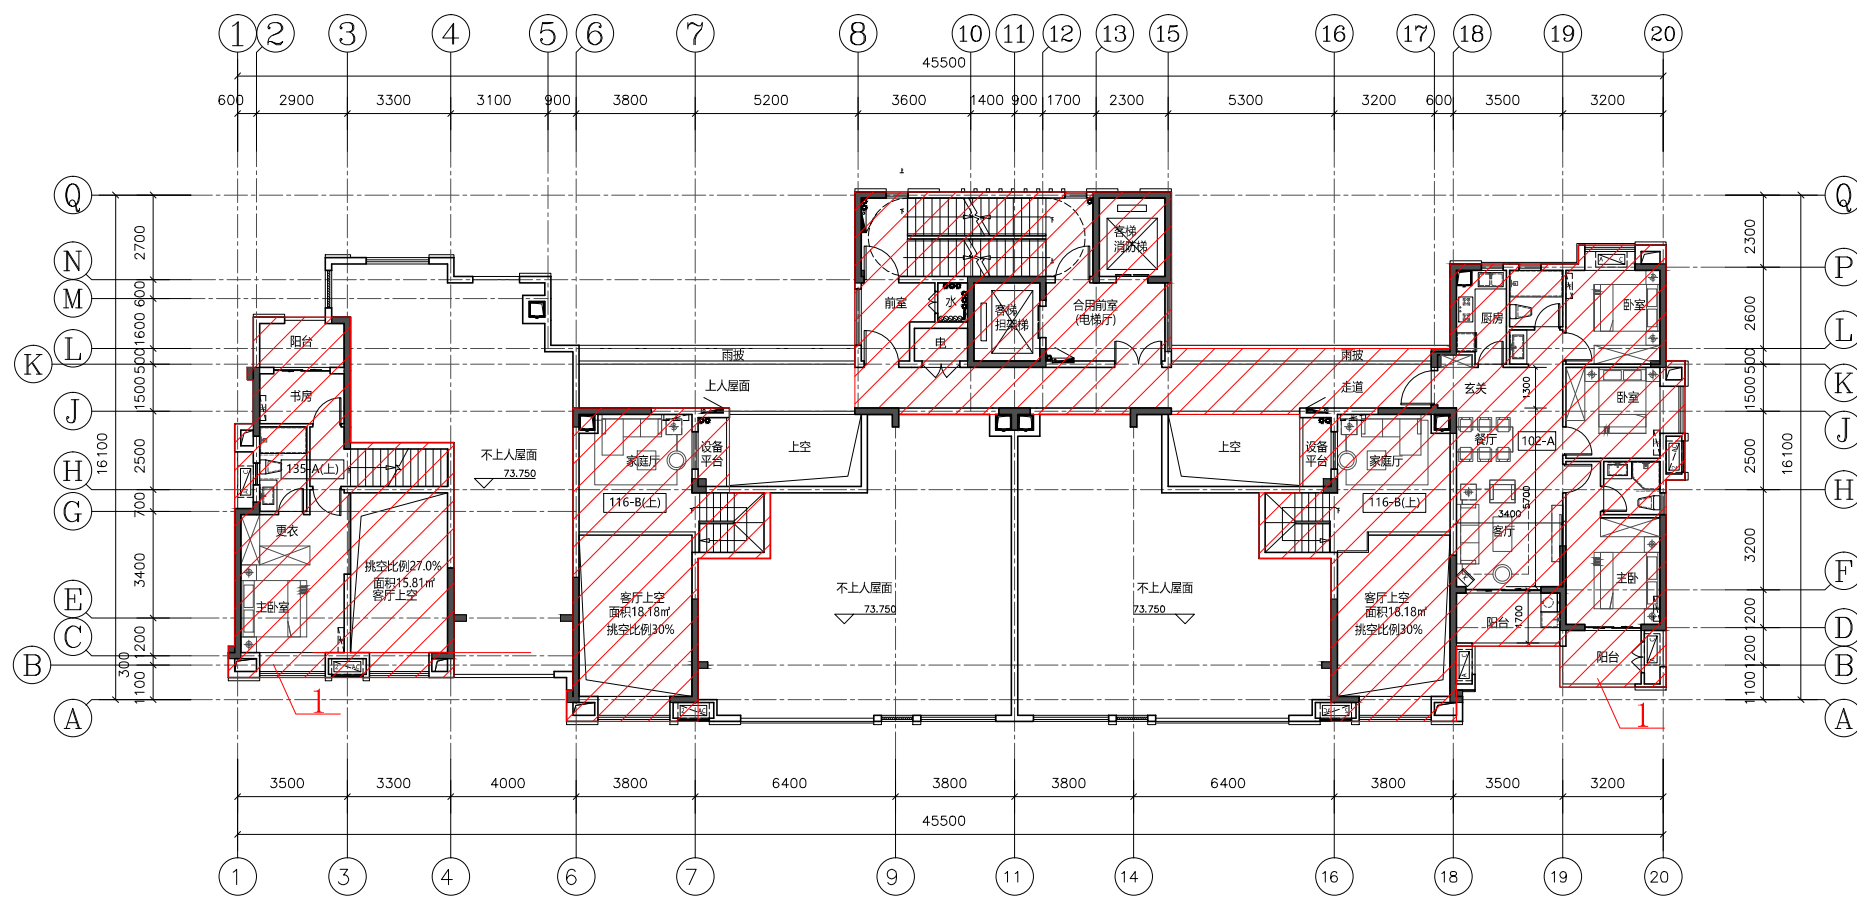


2#楼二十六层平面图（变更后）

1、阴影区楼面标高升高0.15m;

福建华筑工程设计有限公司					证书编号	A135031045	审查批准号		工程号	2022058	项目号	
					建设单位	福建一建集团三明（绿岩）盛建置业有限公司				阶 段	方案	
审 定			校 对		项目名称	福建一建金麟郡				专 业	建筑	版本号
审 核			设 计		比例	2#楼二十六层局部平面图				图 号		
项目负责			专业负责									

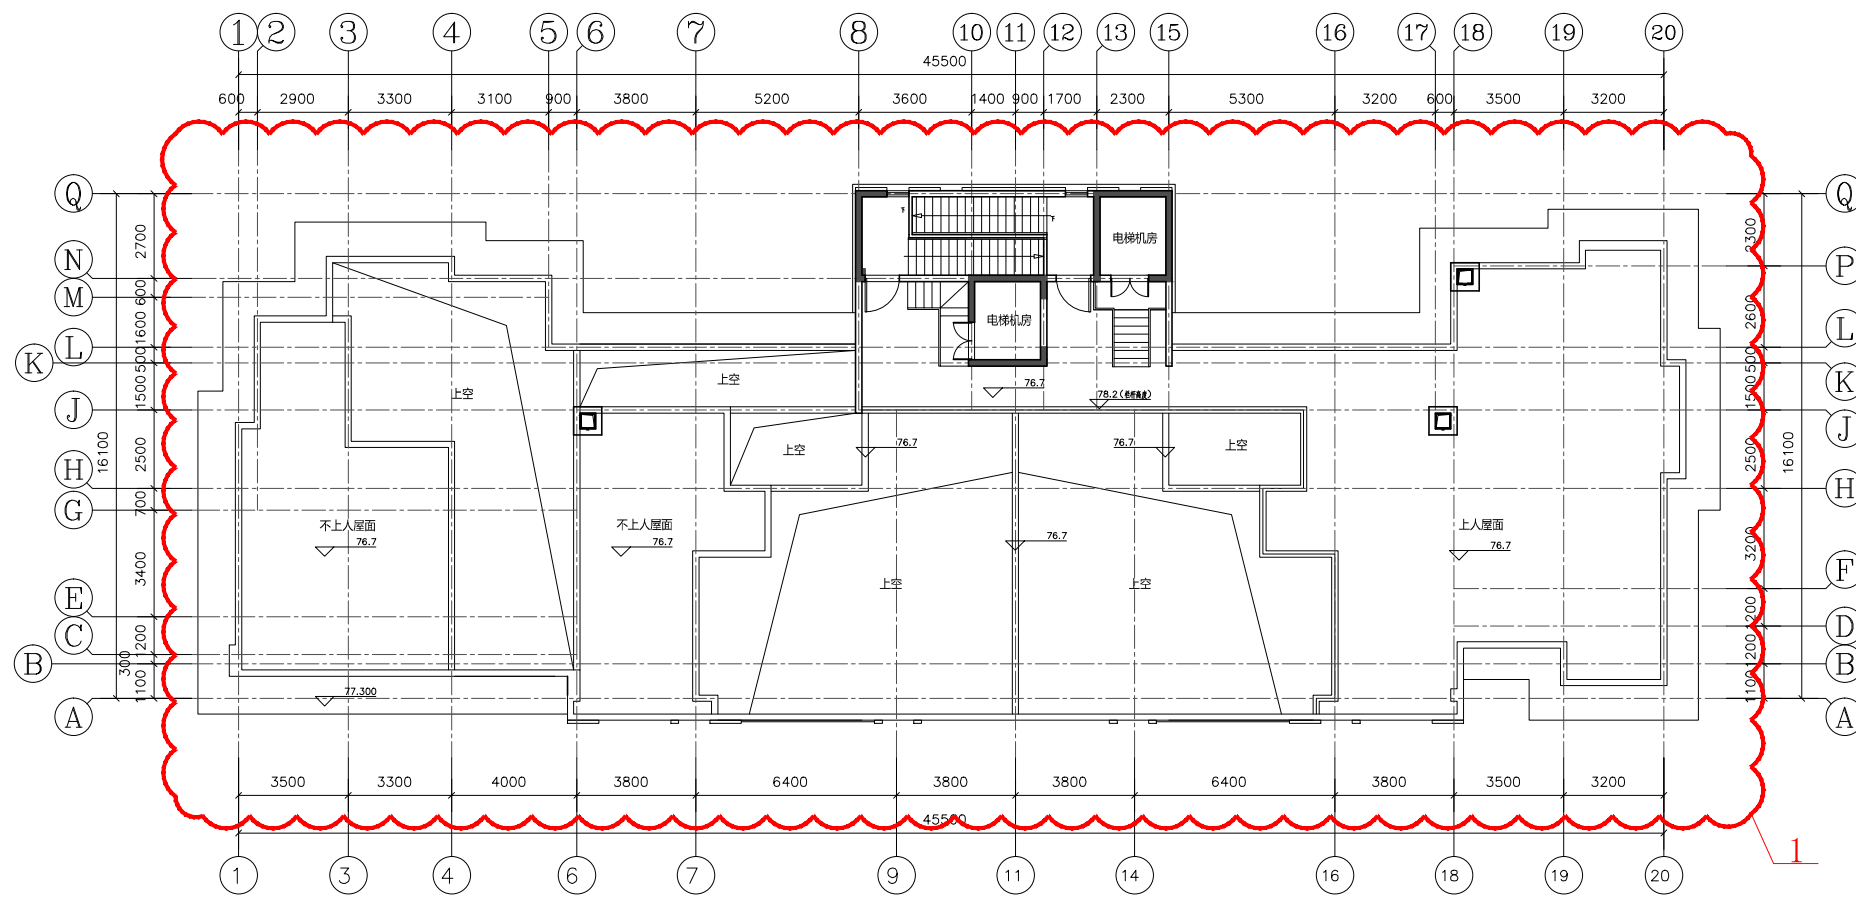

2#楼屋面层平面图（变更前）

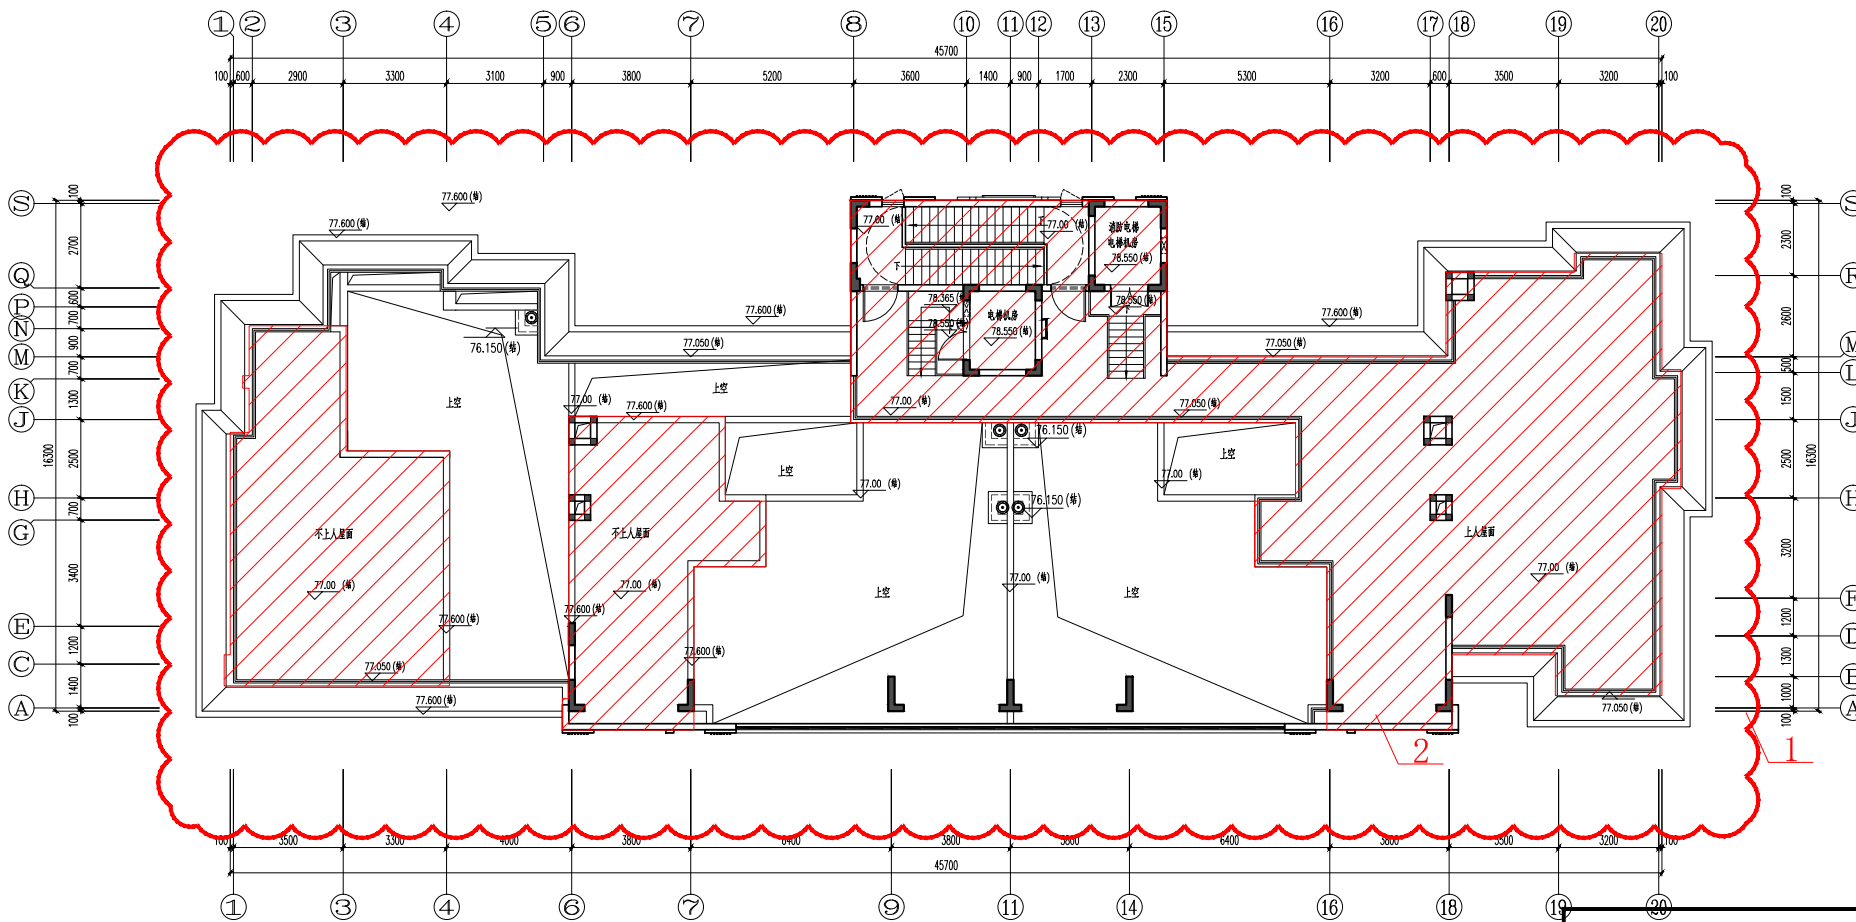


2#楼屋面层平面图（变更后）


福建省工程勘察设计图纸专用章
福建华筑工程设计有限公司
范围: 建筑工程
资质等级: 甲级 证号: A135031045
有效期至: 2028年12月28日

- 1、施工图优化，屋面柱子、造型及烟囱调整；
- 2、阴影部分楼面标高升高0.30m；

福建华筑工程设计有限公司				证书编号	A135031045	审查批准号		工程号	2022058	项目号
				建设单位	福建一建集团三明（绿岩）盛建置业有限公司			阶段	方案	
				项目名称	福建一建金麟郡			专业	建筑	版本号
				比例				图号		
				项目负责	2#楼屋面层平面图			日期	2024.06	

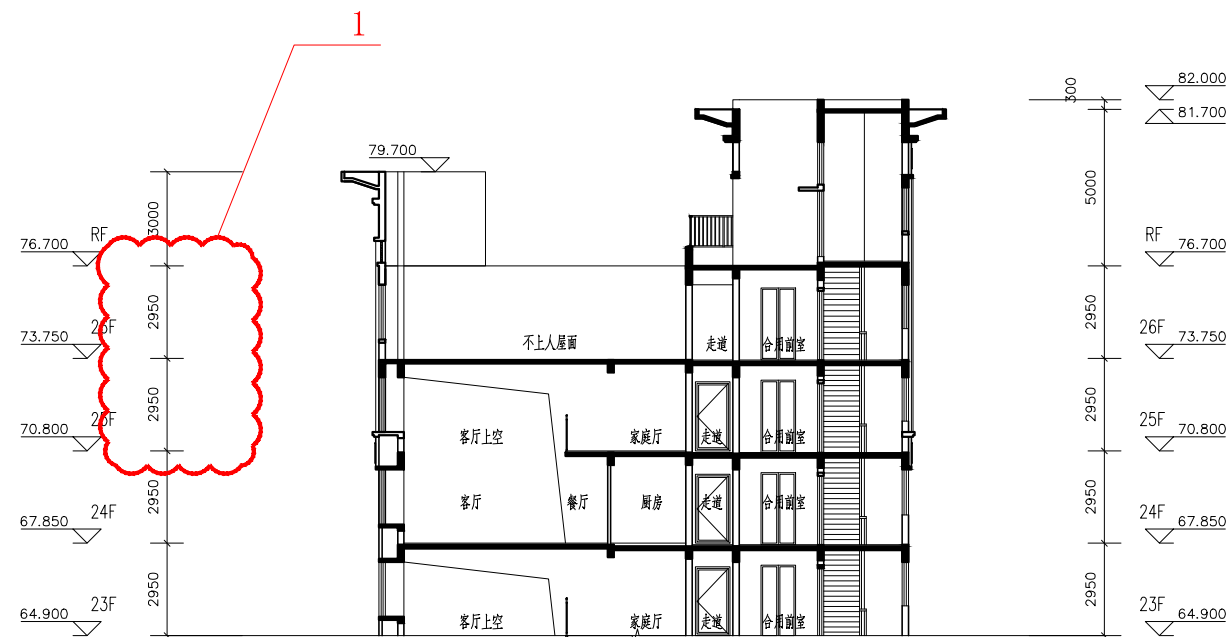

2#1-1剖面局部立面图（变更前）

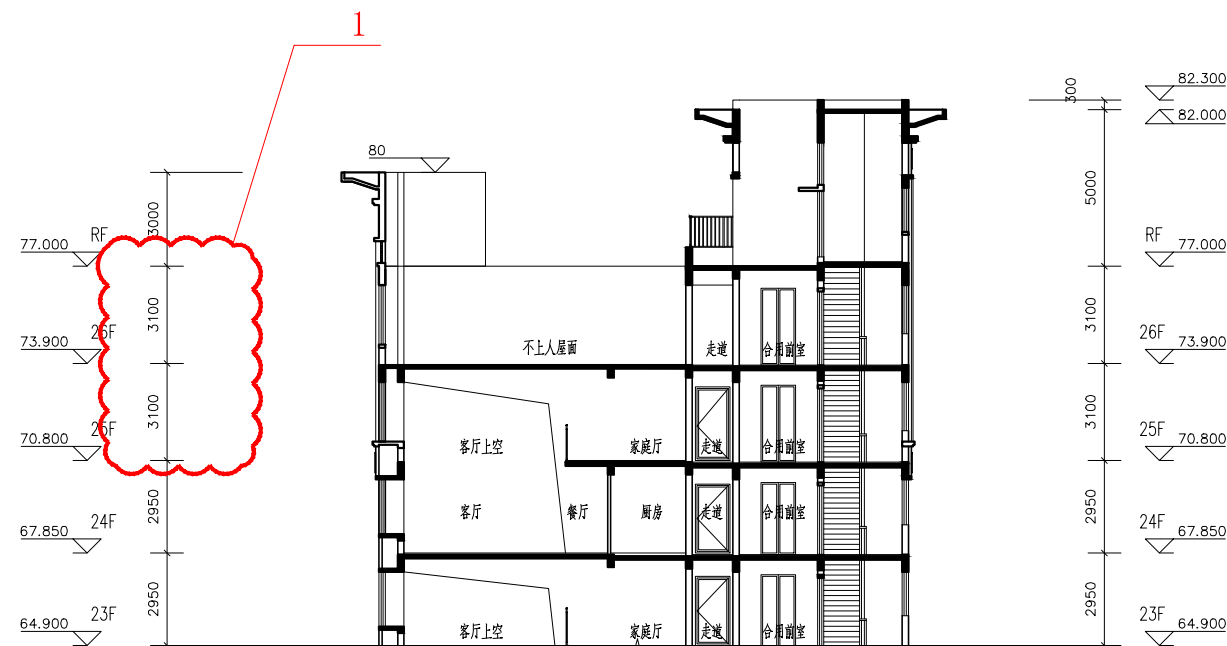

2#1-1剖面局部立面图（变更后）

1、25层，26层层高加高150mm，标高相应变化。

福建省工程勘察设计图纸专用章
福建华筑工程设计有限公司
范围：建筑工程
资质等级：甲级 证号：A135031045
有效期至：2028年12月28日

福建华筑工程设计有限公司						证书编号	A135031045	审查批准号		工程号	2022058	项目号
						建设单位	福建一建集团三明（绿岩）盛建置业有限公司			阶段	方案	
审定			校对			项目名称	福建一建金麟郡			专业	建筑	版本号
审核			设计			比例				图号		
项目负责人			专业负责				2#1-1剖面局部立面图			日期	2024.06	



2#南立面局部立面图（变更前）




2#南立面局部立面图（变更后）

1、25层，26层层高加高150mm，标高相应变化。


福建省工程勘察设计图纸专用章
福建华筑工程设计有限公司
范围：建筑工程
资质等级：甲级 证号：A135031045
有效期至：2028年12月28日

福建华筑工程设计有限公司						证书编号	A135031045	审查批准号		工程号	2022058	项目号
						建设单位	福建一建集团三明（绿岩）盛建置业有限公司			阶段	方案	
审定			校对			项目名称	福建一建金麟郡			专业	建筑	版本号
审核			设计			比例				图号		
项目负责			专业负责				2#南立面局部立面图			日期	2024.06	

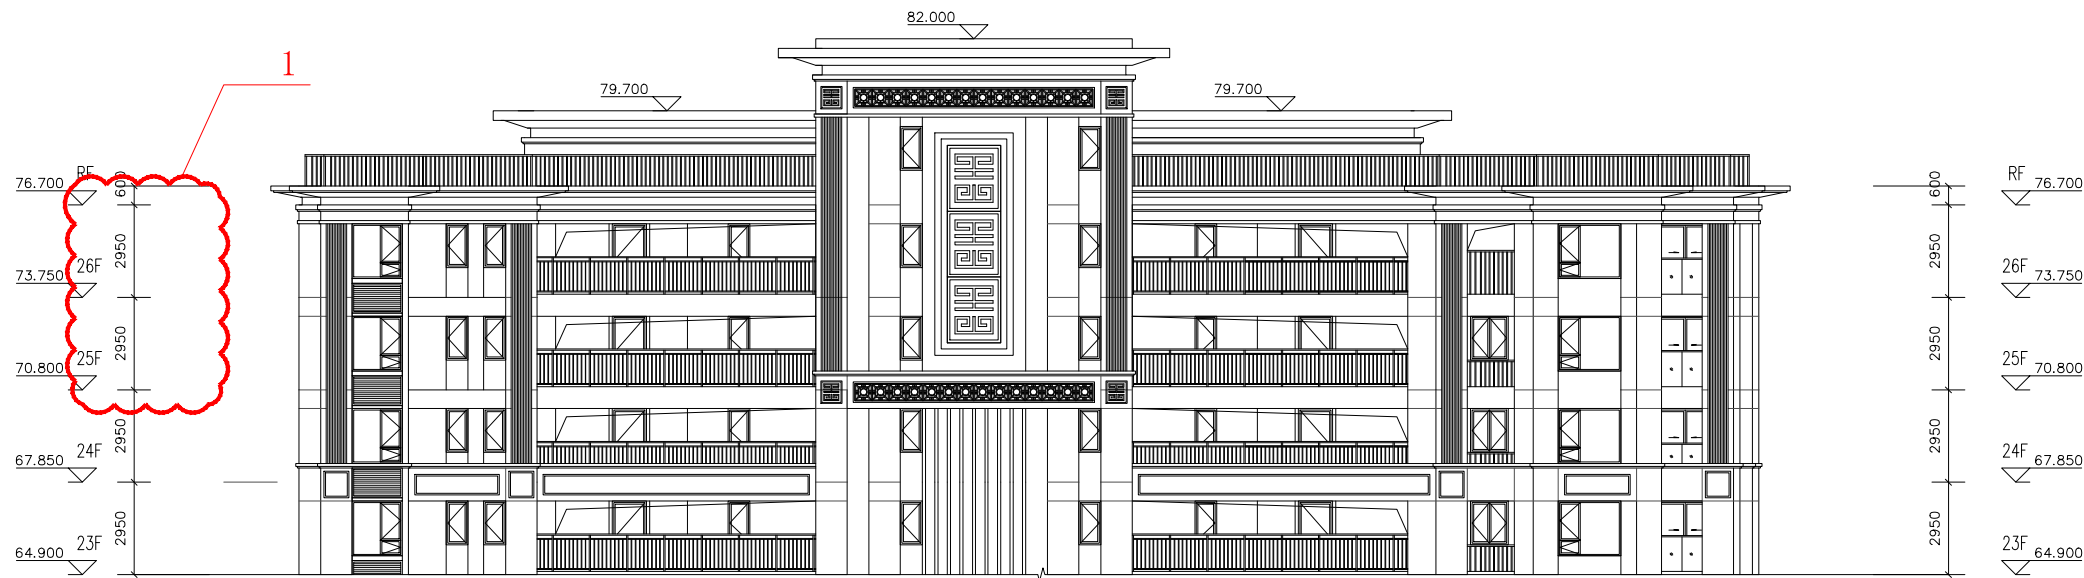

福建省工程勘察设计图纸专用章
福建华筑工程设计有限公司
范围: 建筑工程
资质等级: 甲级 证号: A135031045
有效期至: 2028年12月28日


2#北立面局部立面图（变更前）

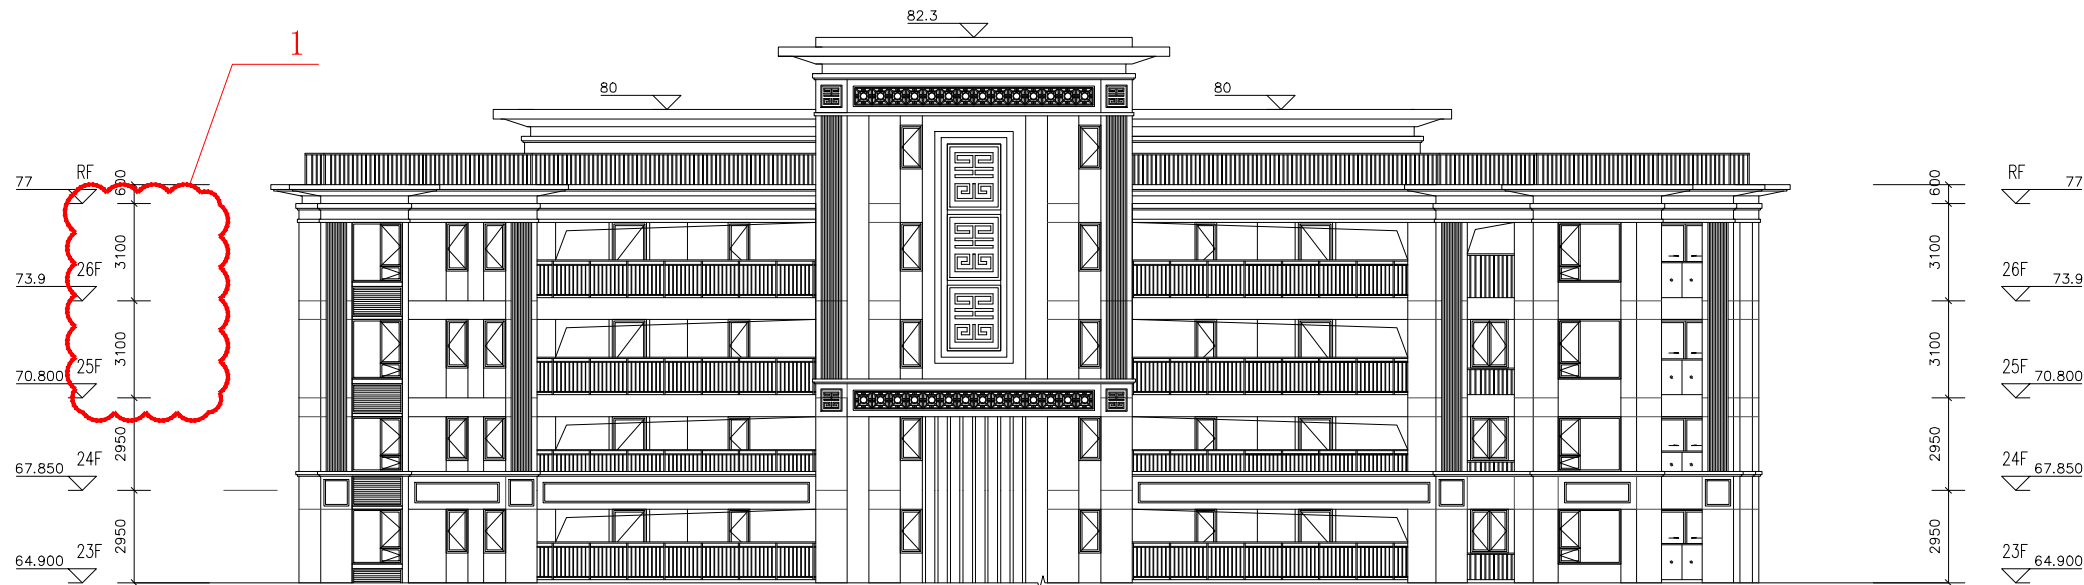


2#北立面局部立面图（变更后）

1、25层，26层层高加高150mm，标高相应变化。


福建华筑工程设计有限公司						证书编号	A135031045	审查批准号		工程号	2022058	项目号
						建设单位	福建一建集团三明（绿岩）盛建置业有限公司			阶段	方案	
审定			校对			项目名称	福建一建金麟郡			专业	建筑	版本号
审核			设计			比例				图号		
项目负责			专业负责				2#北立面局部立面图			日期	2024.06	

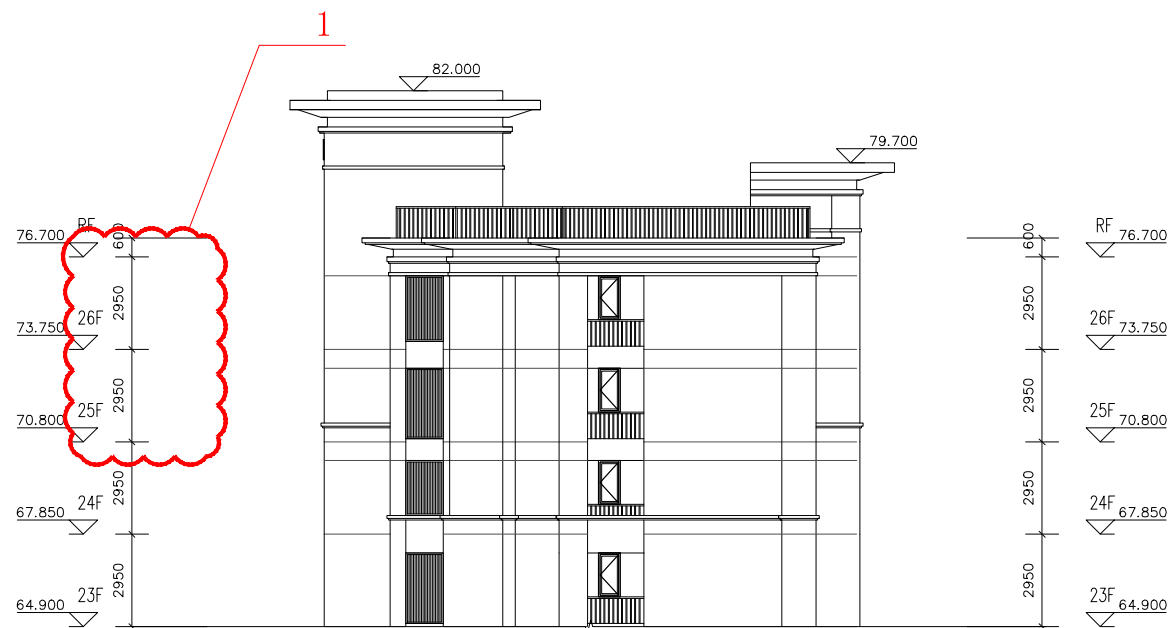


2#西立面局部立面图（变更前）

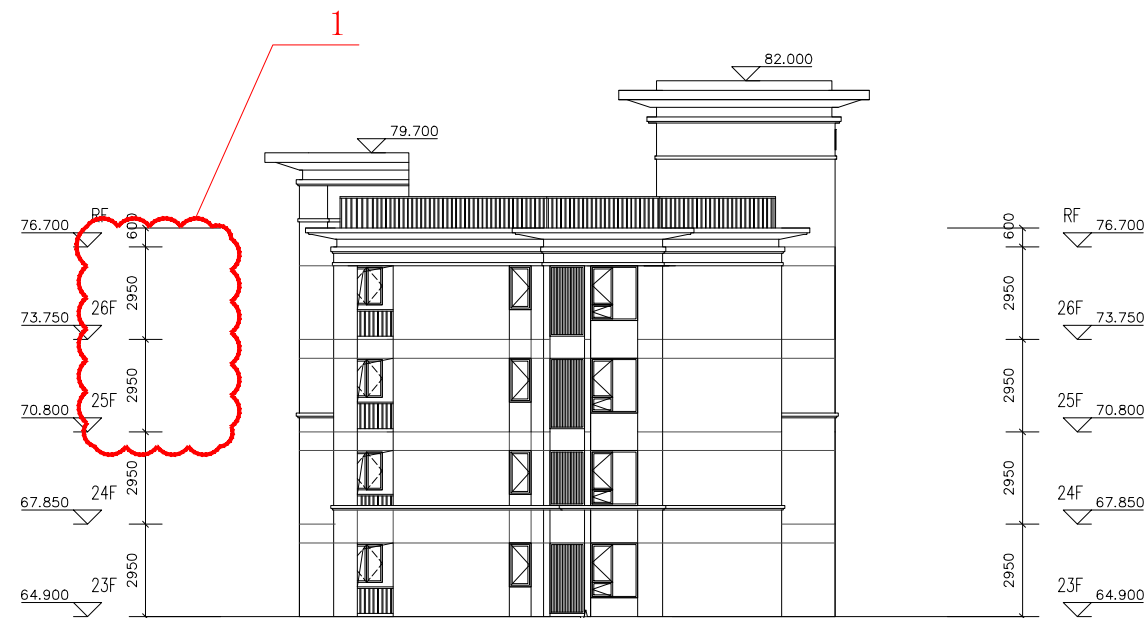

2#东立面局部立面图（变更前）

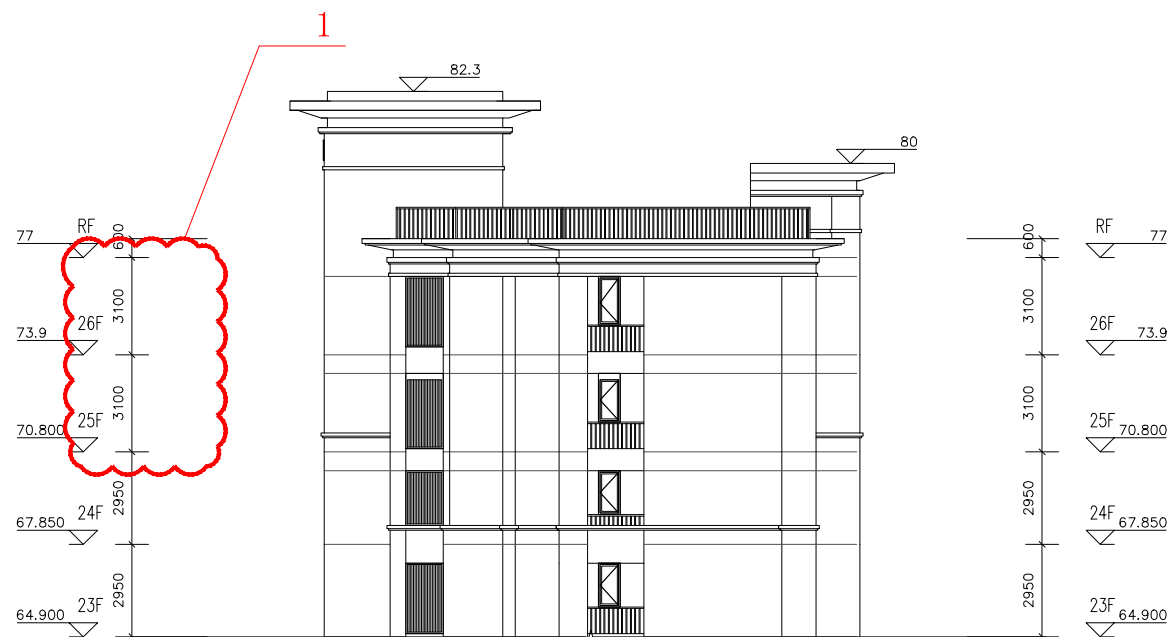

2#西立面局部立面图（变更后）

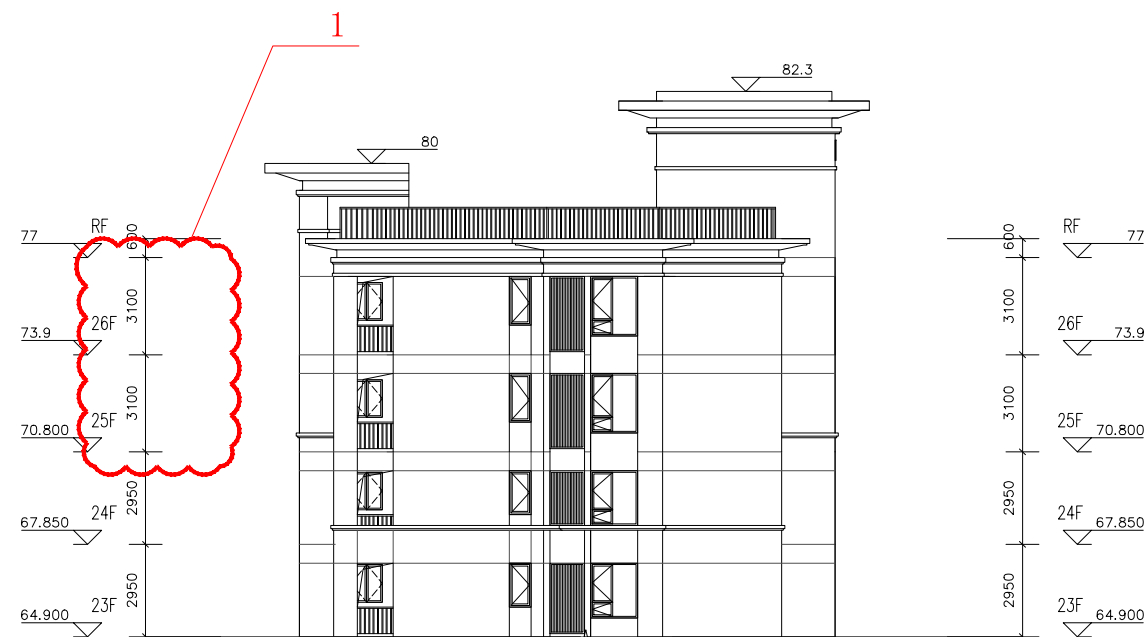

2#东立面局部立面图（变更后）


1、25层，26层层高加高150mm，标高相应变化。

1、25层，26层层高加高150mm，标高相应变化。


福建省工程勘察设计图纸专用章
福建华筑工程设计有限公司
范围：建筑工程
资质等级：甲级 证号：A135031045
有效期至：2028年12月28日

福建华筑工程设计有限公司				证书编号	A135031045	审查批准号		工程号	2022058	项目号
				建设单位	福建一建集团三明（绿岩）盛建置业有限公司			阶段	方案	
审定			校对		项目名称	福建一建金麟郡		专业	建筑	版本号
审核			设计		比例			图号		
项目负责人			专业负责			2#西立面局部立面图 2#东立面局部立面图		日期	2024.06	

变更内容:
1、施工图结构深化, 车位尺寸及位置相应调整, 调整后车位减少1个。

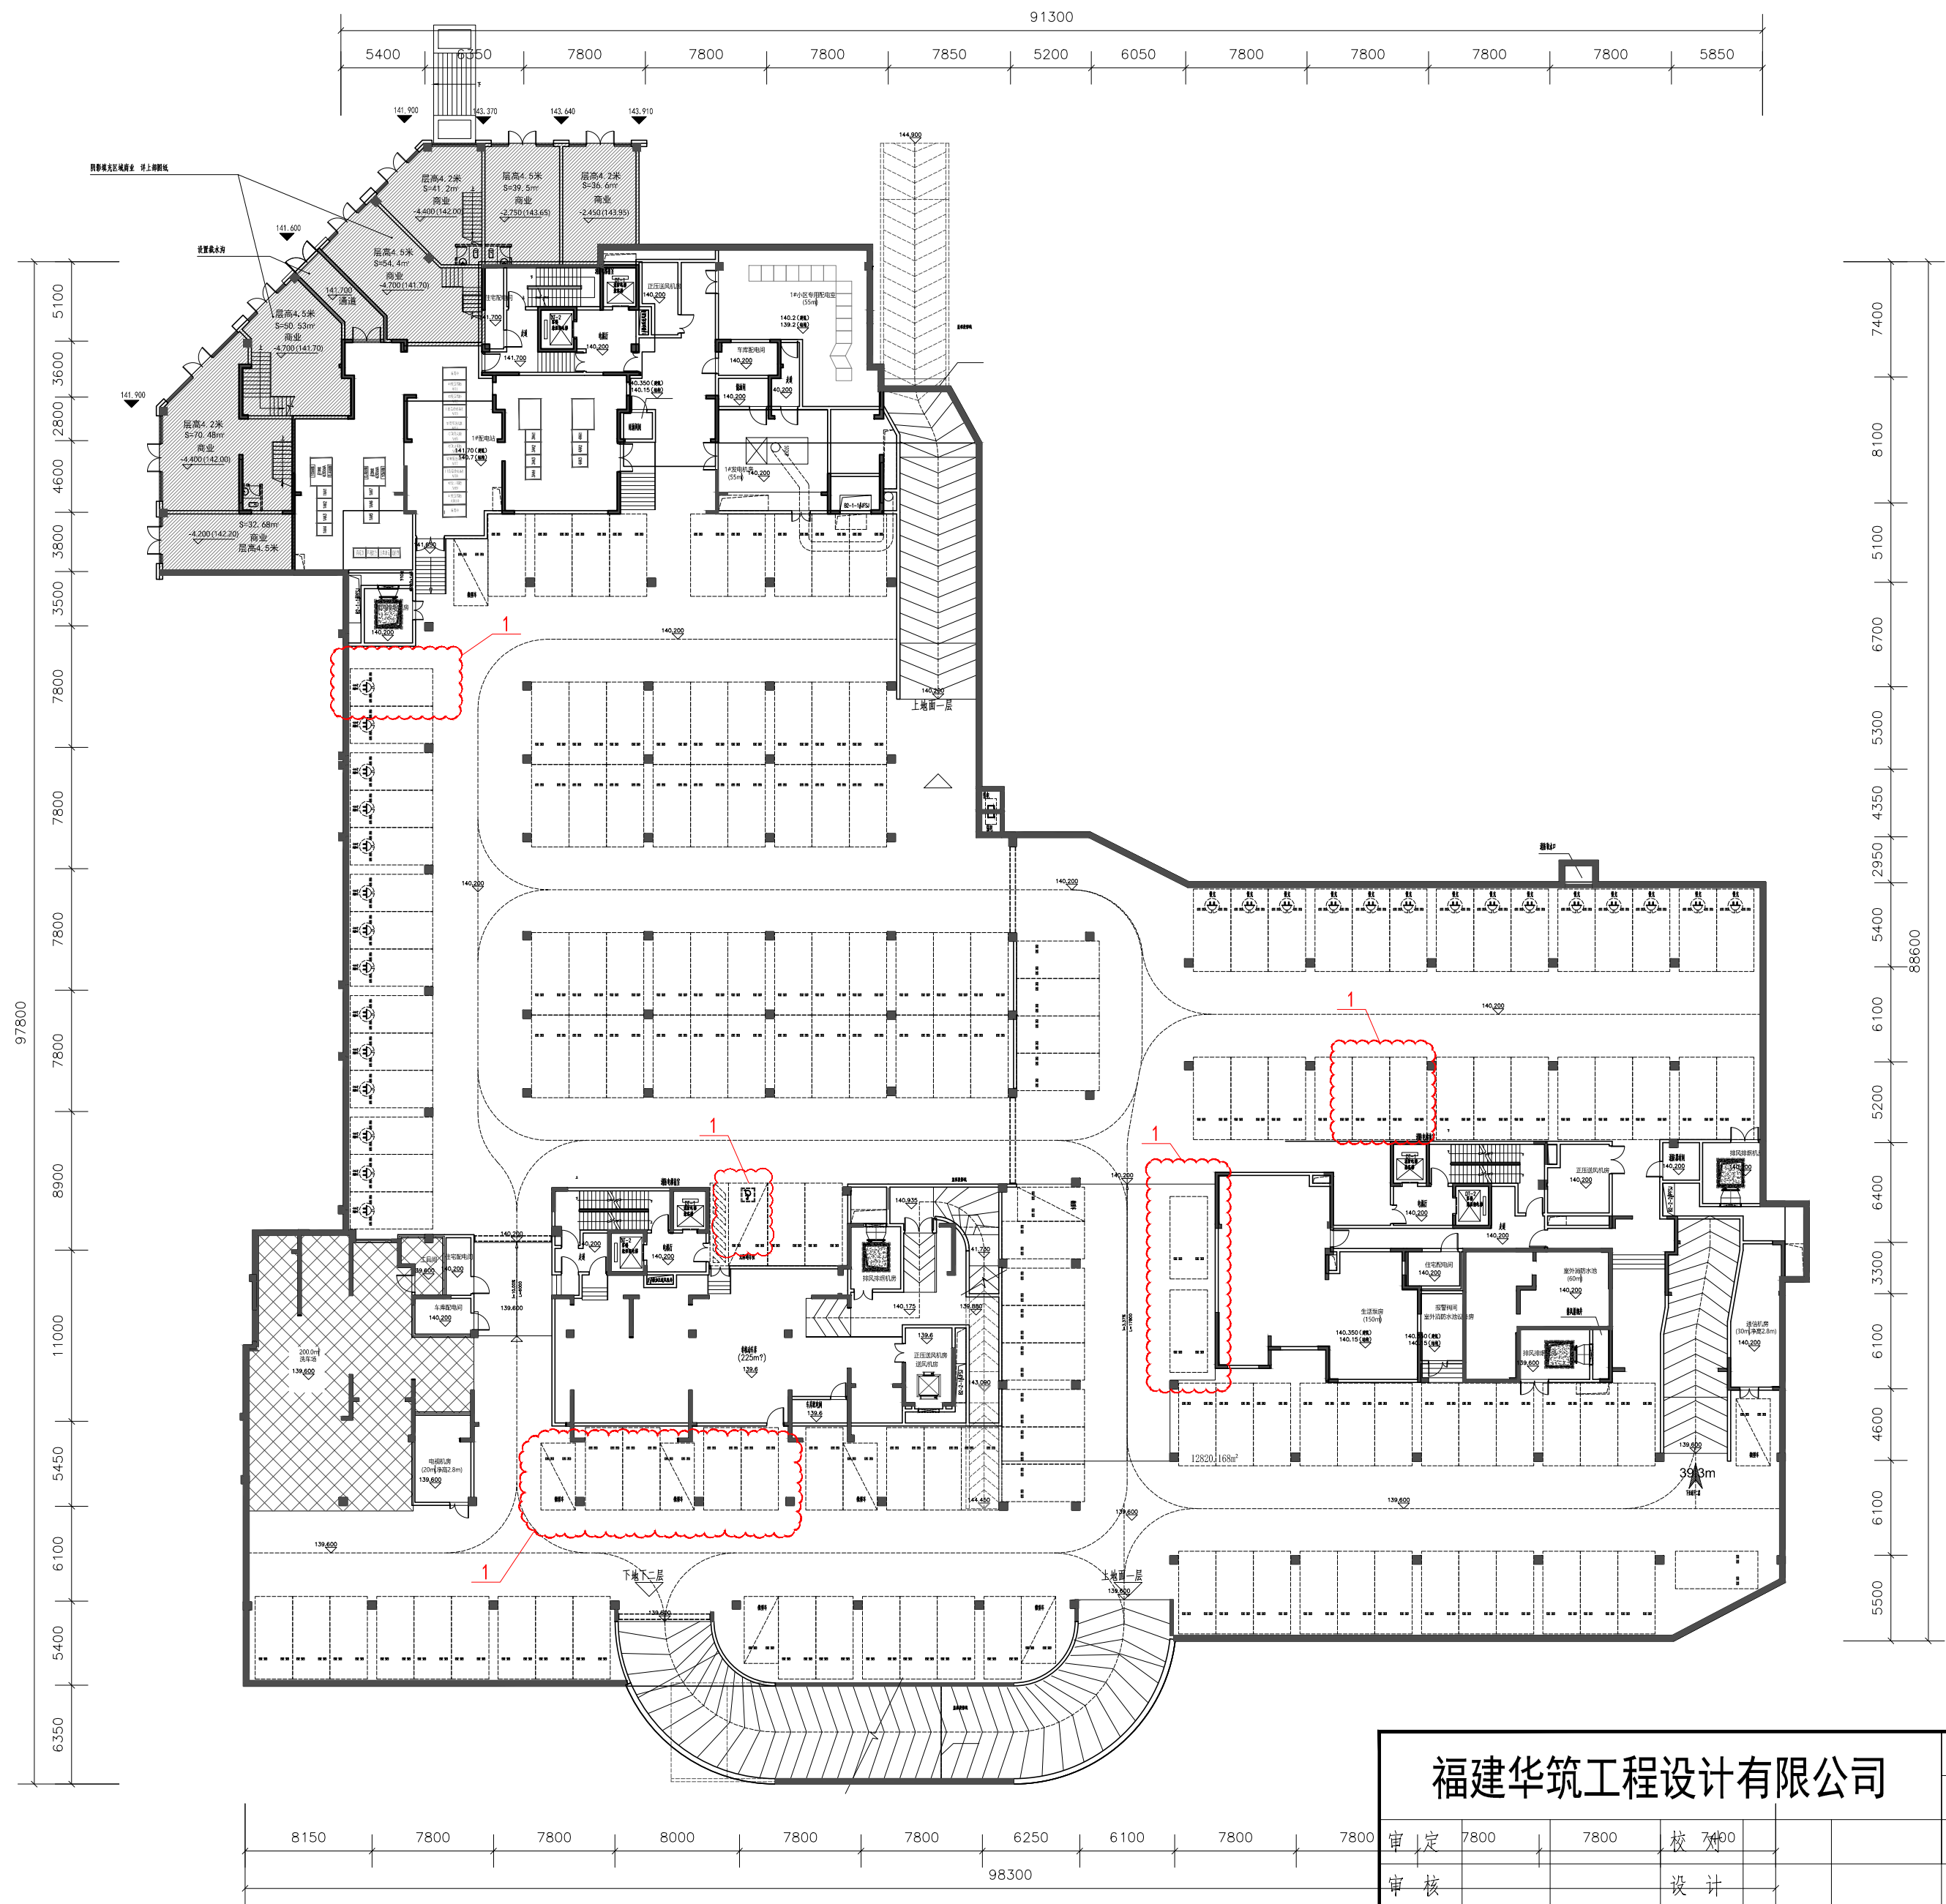


福建省工程勘察设计图纸专用章
福建华筑工程设计有限公司
范围: 建筑工程
资质: 等级: 甲级 证号: A135031045
有效期至: 2028年12月28日

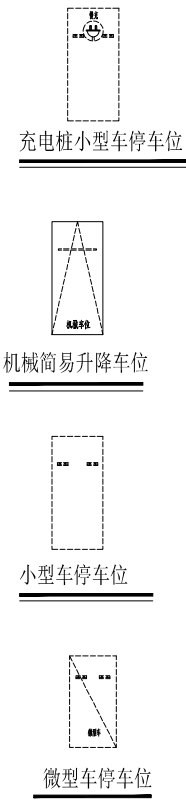

地下室一层平面图 (变更前)
注: 1. 地下室总建筑面积: 12823.604m²
2. 地下室一层建筑面积: 6637.136m²
3. 地下室二层建筑面积: 6186.468m²
4. 本项目总停车数为441辆, 其中地面停车位为44辆
地下室总停车数为403辆, 其中小型车位262辆,
微型车位19辆, 机械车位122辆, 折算完19x0.7+262+122=397
机械车位占比122/441=27.67%

福建华筑工程设计有限公司						证书编号	A135031045	审查批准号		工程号	2022058	项目号
						建设单位	福建一建集团三明（绿岩）盛建置业有限公司				阶 段	
审 定	7800		7800	校 核		项目名称	福建一建金麟郡			专 业	建筑	版本号
审 核				设 计			比 例				图 号	
项目负责				专业负责		地下室一层平面图(变更前)			日 期	2024.06		


变更内容:
1、施工图结构深化, 车位尺寸及位置相应调整, 调整后车位减少1个。

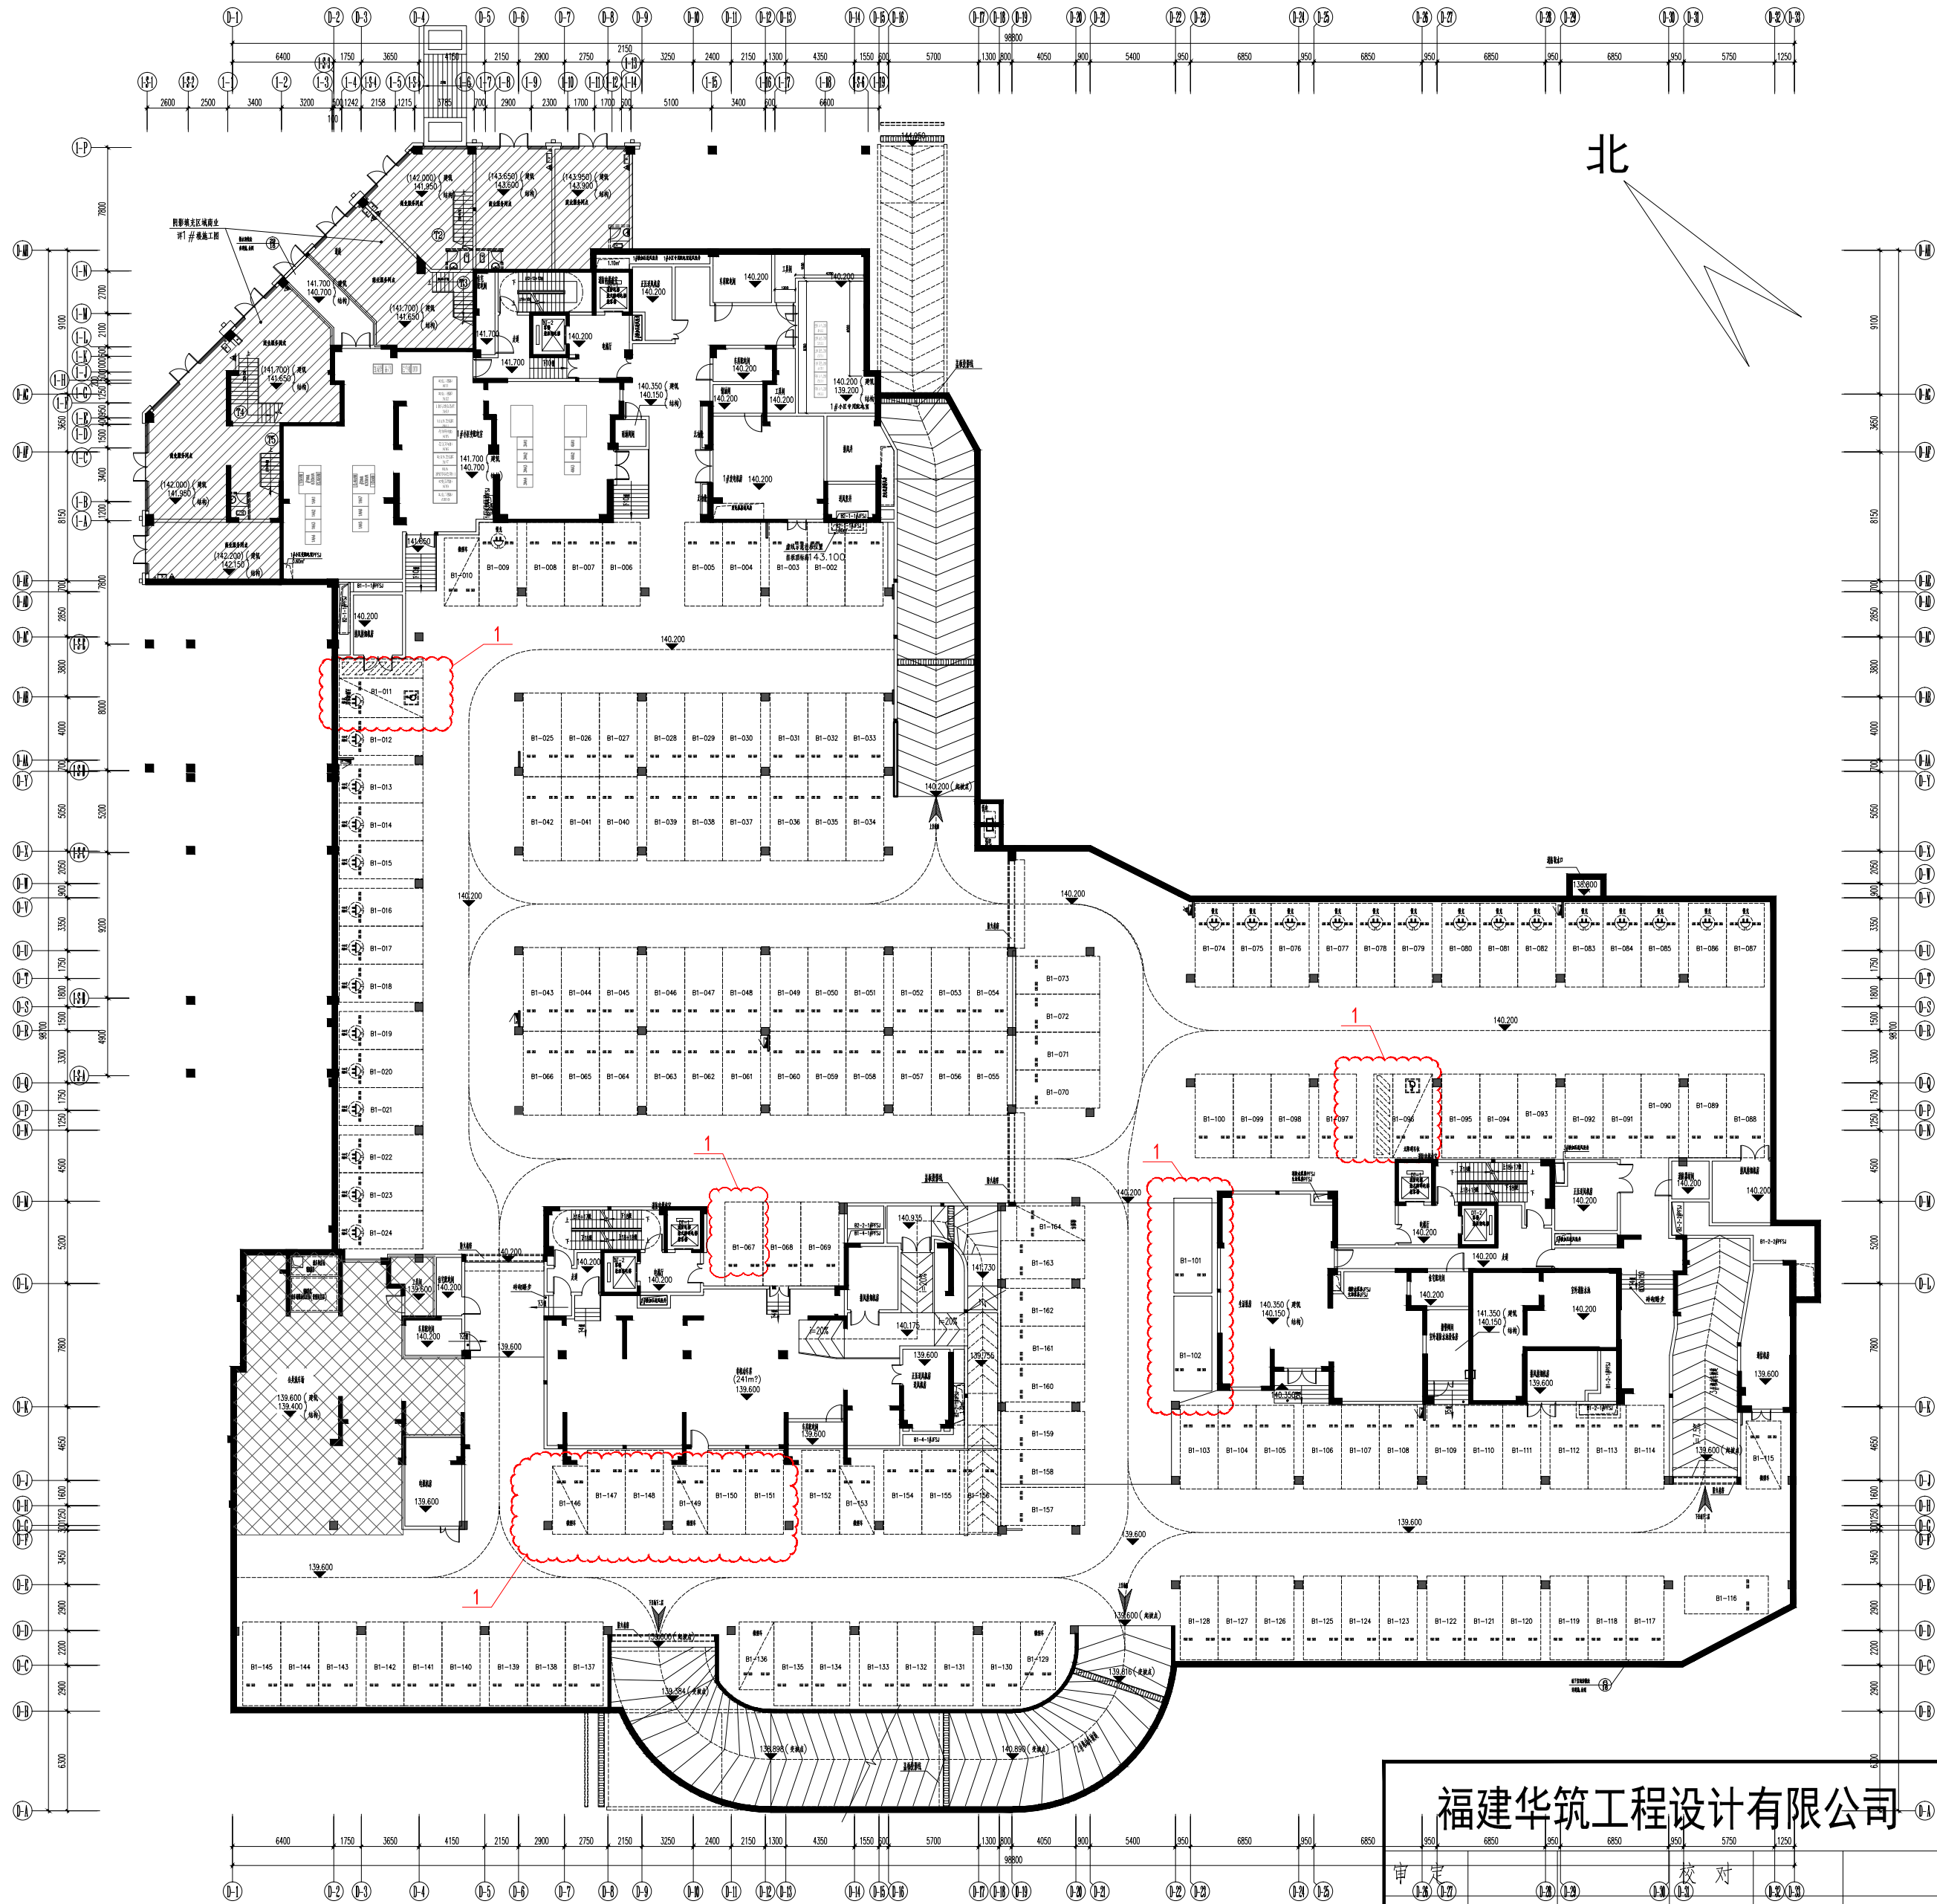



地下室一层平面图(变更后)
注:1.地下室总建筑面积: 12823.604m²
2.地下室一层建筑面积: 6637.136m²
3.地下室二层建筑面积: 6186.468m²
4.本项目总停车数为441辆, 其中地面停车位为44辆。
地下室总停车数为403辆, 其中小型车259辆, 无障碍车位2辆,
微型车位20辆, 机械车位122辆, 折算完20x0.7+259+2+122=397
机械车位占比122/441=27.67%

福建华筑工程设计有限公司		证书编号	A135031045	审查批准号		工程号	2022058	项目号	
		建设单位	福建一建集团三明(绿岩)盛建置业有限公司			阶段	方案		
		项目名称	福建一建金麟郡			专业	建筑		
		比例				图号		版本号	
		项目负责人				日期	2024.06		

变更内容：
1、施工图结构深化，车位位置调整并且增设一个微型车位。

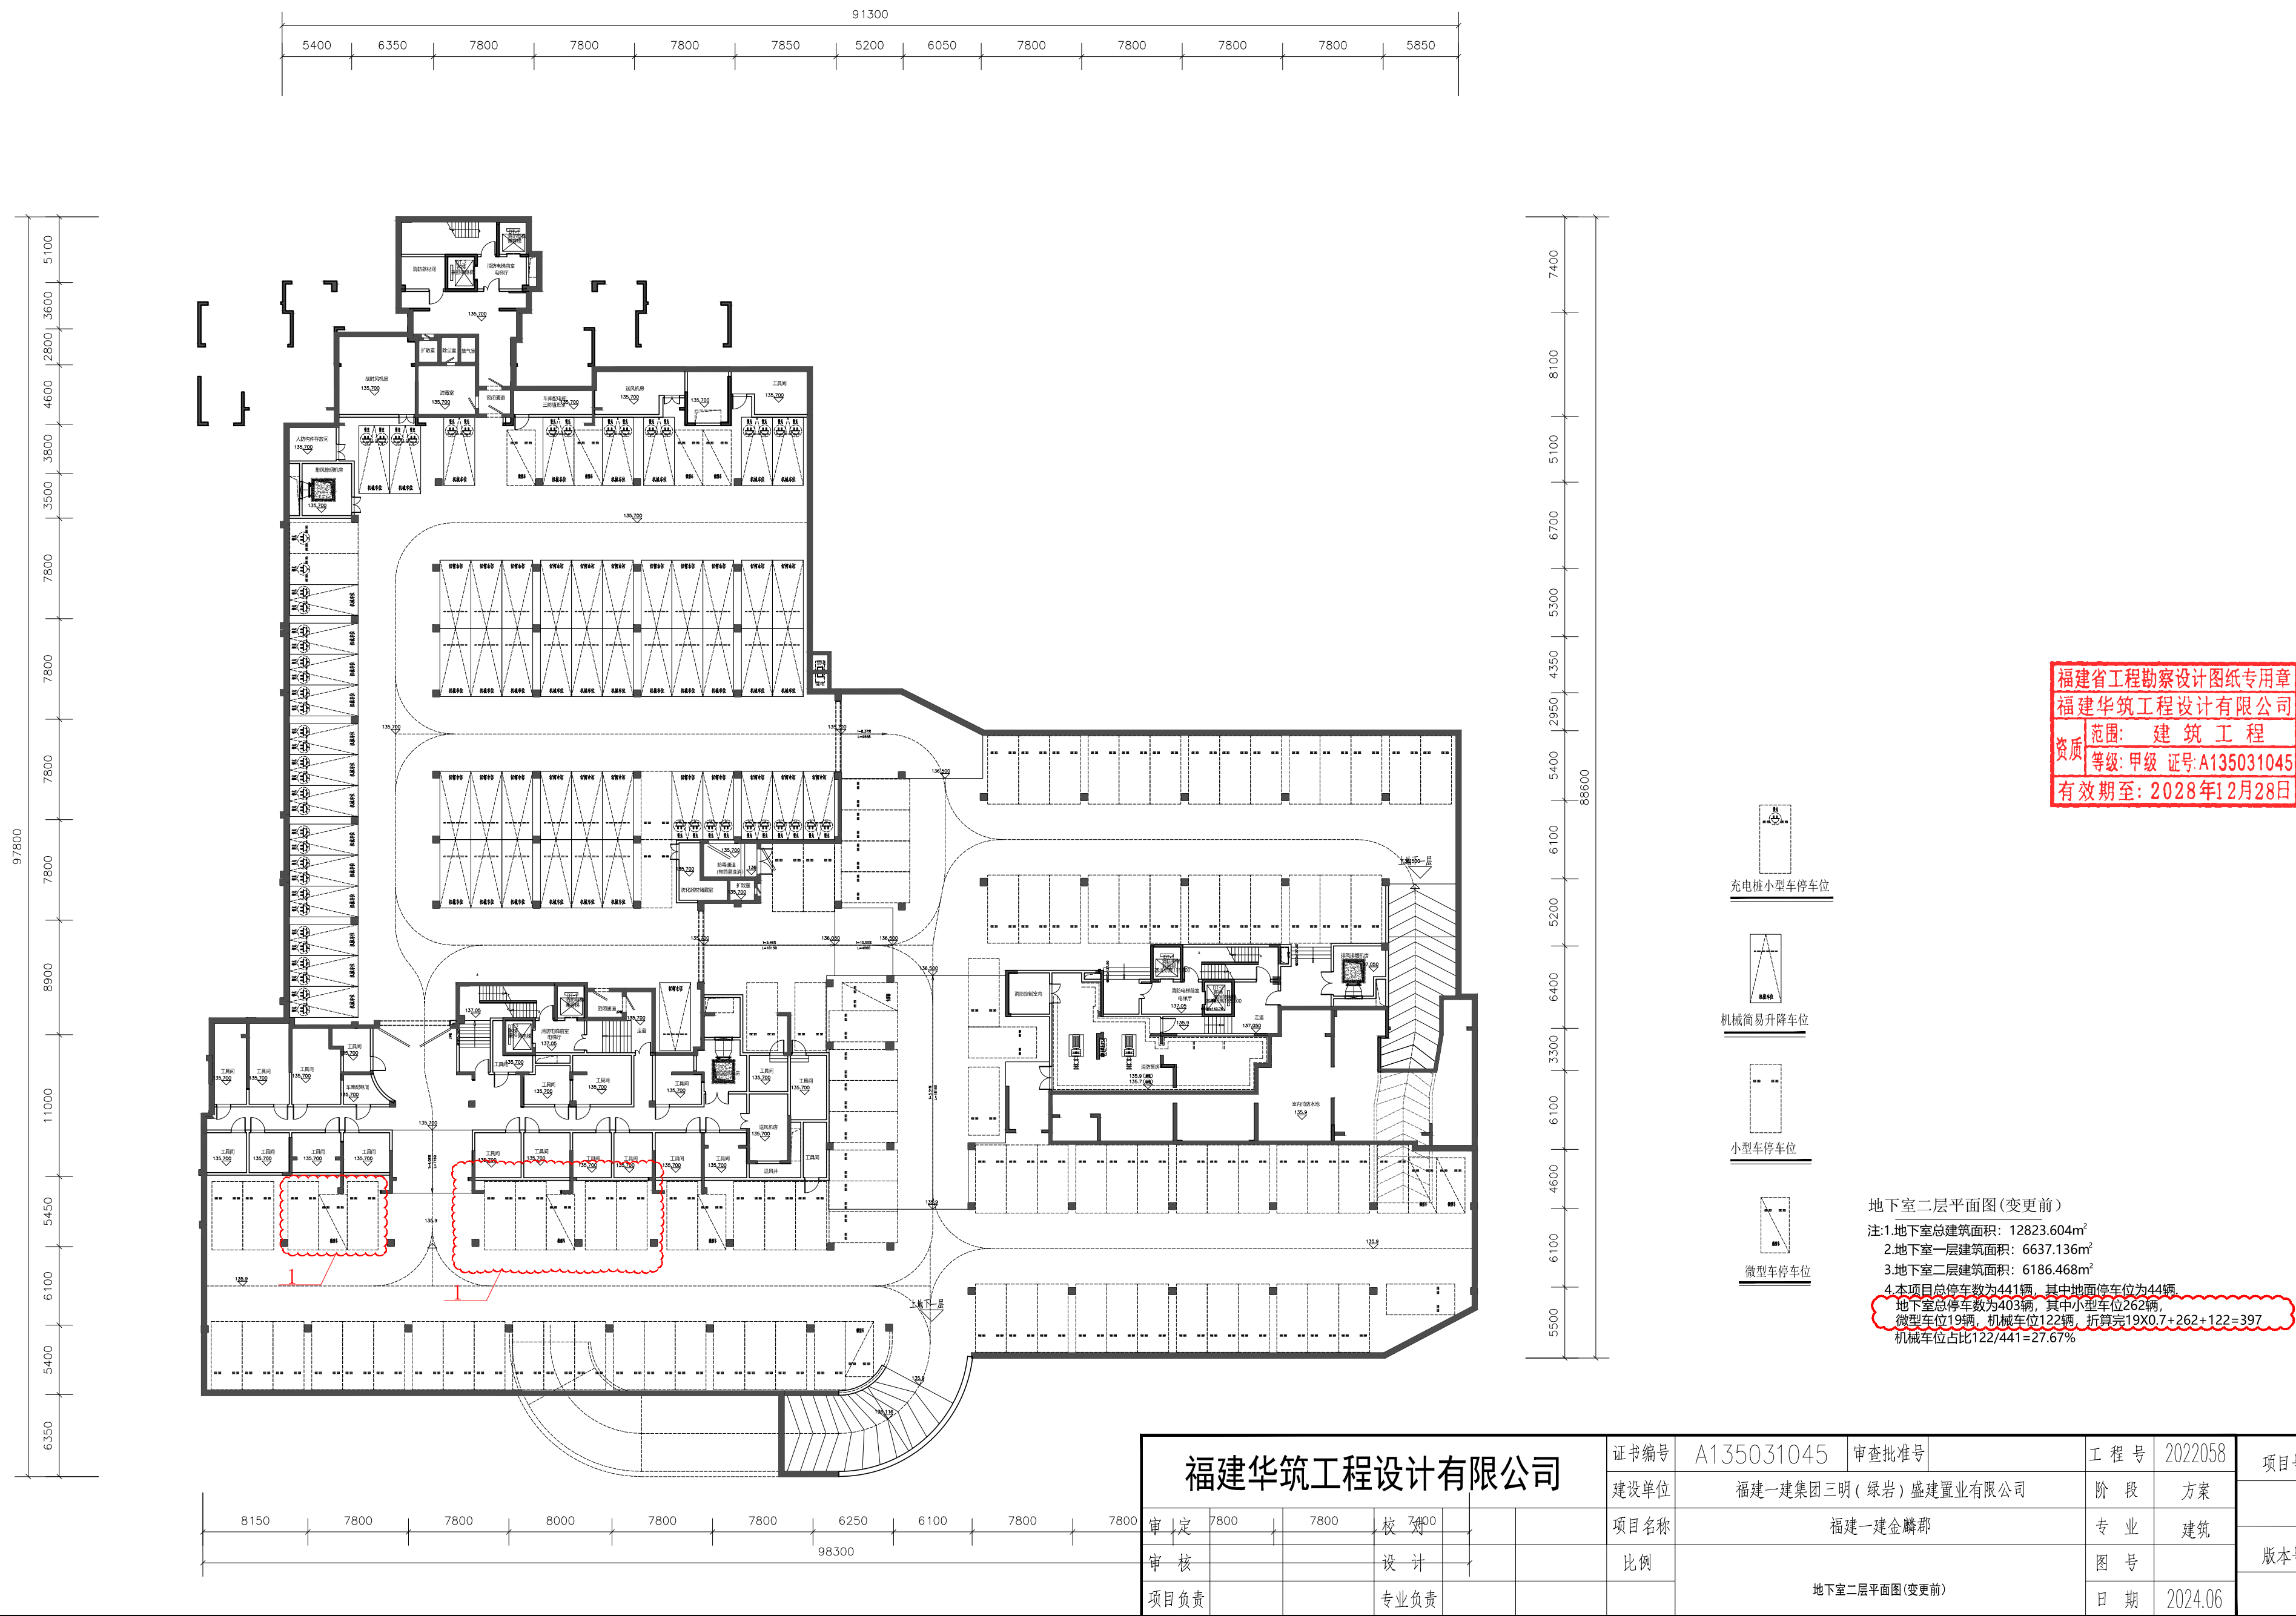

变更内容：
1、施工图结构深化，车位位置调整并且增设一个微型车位。

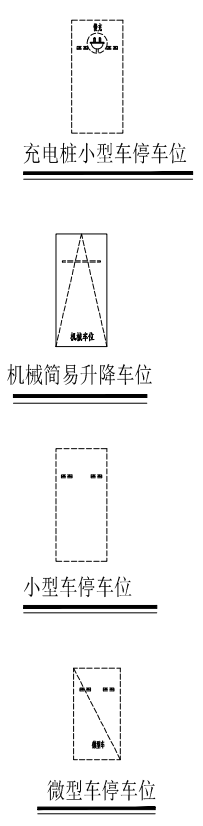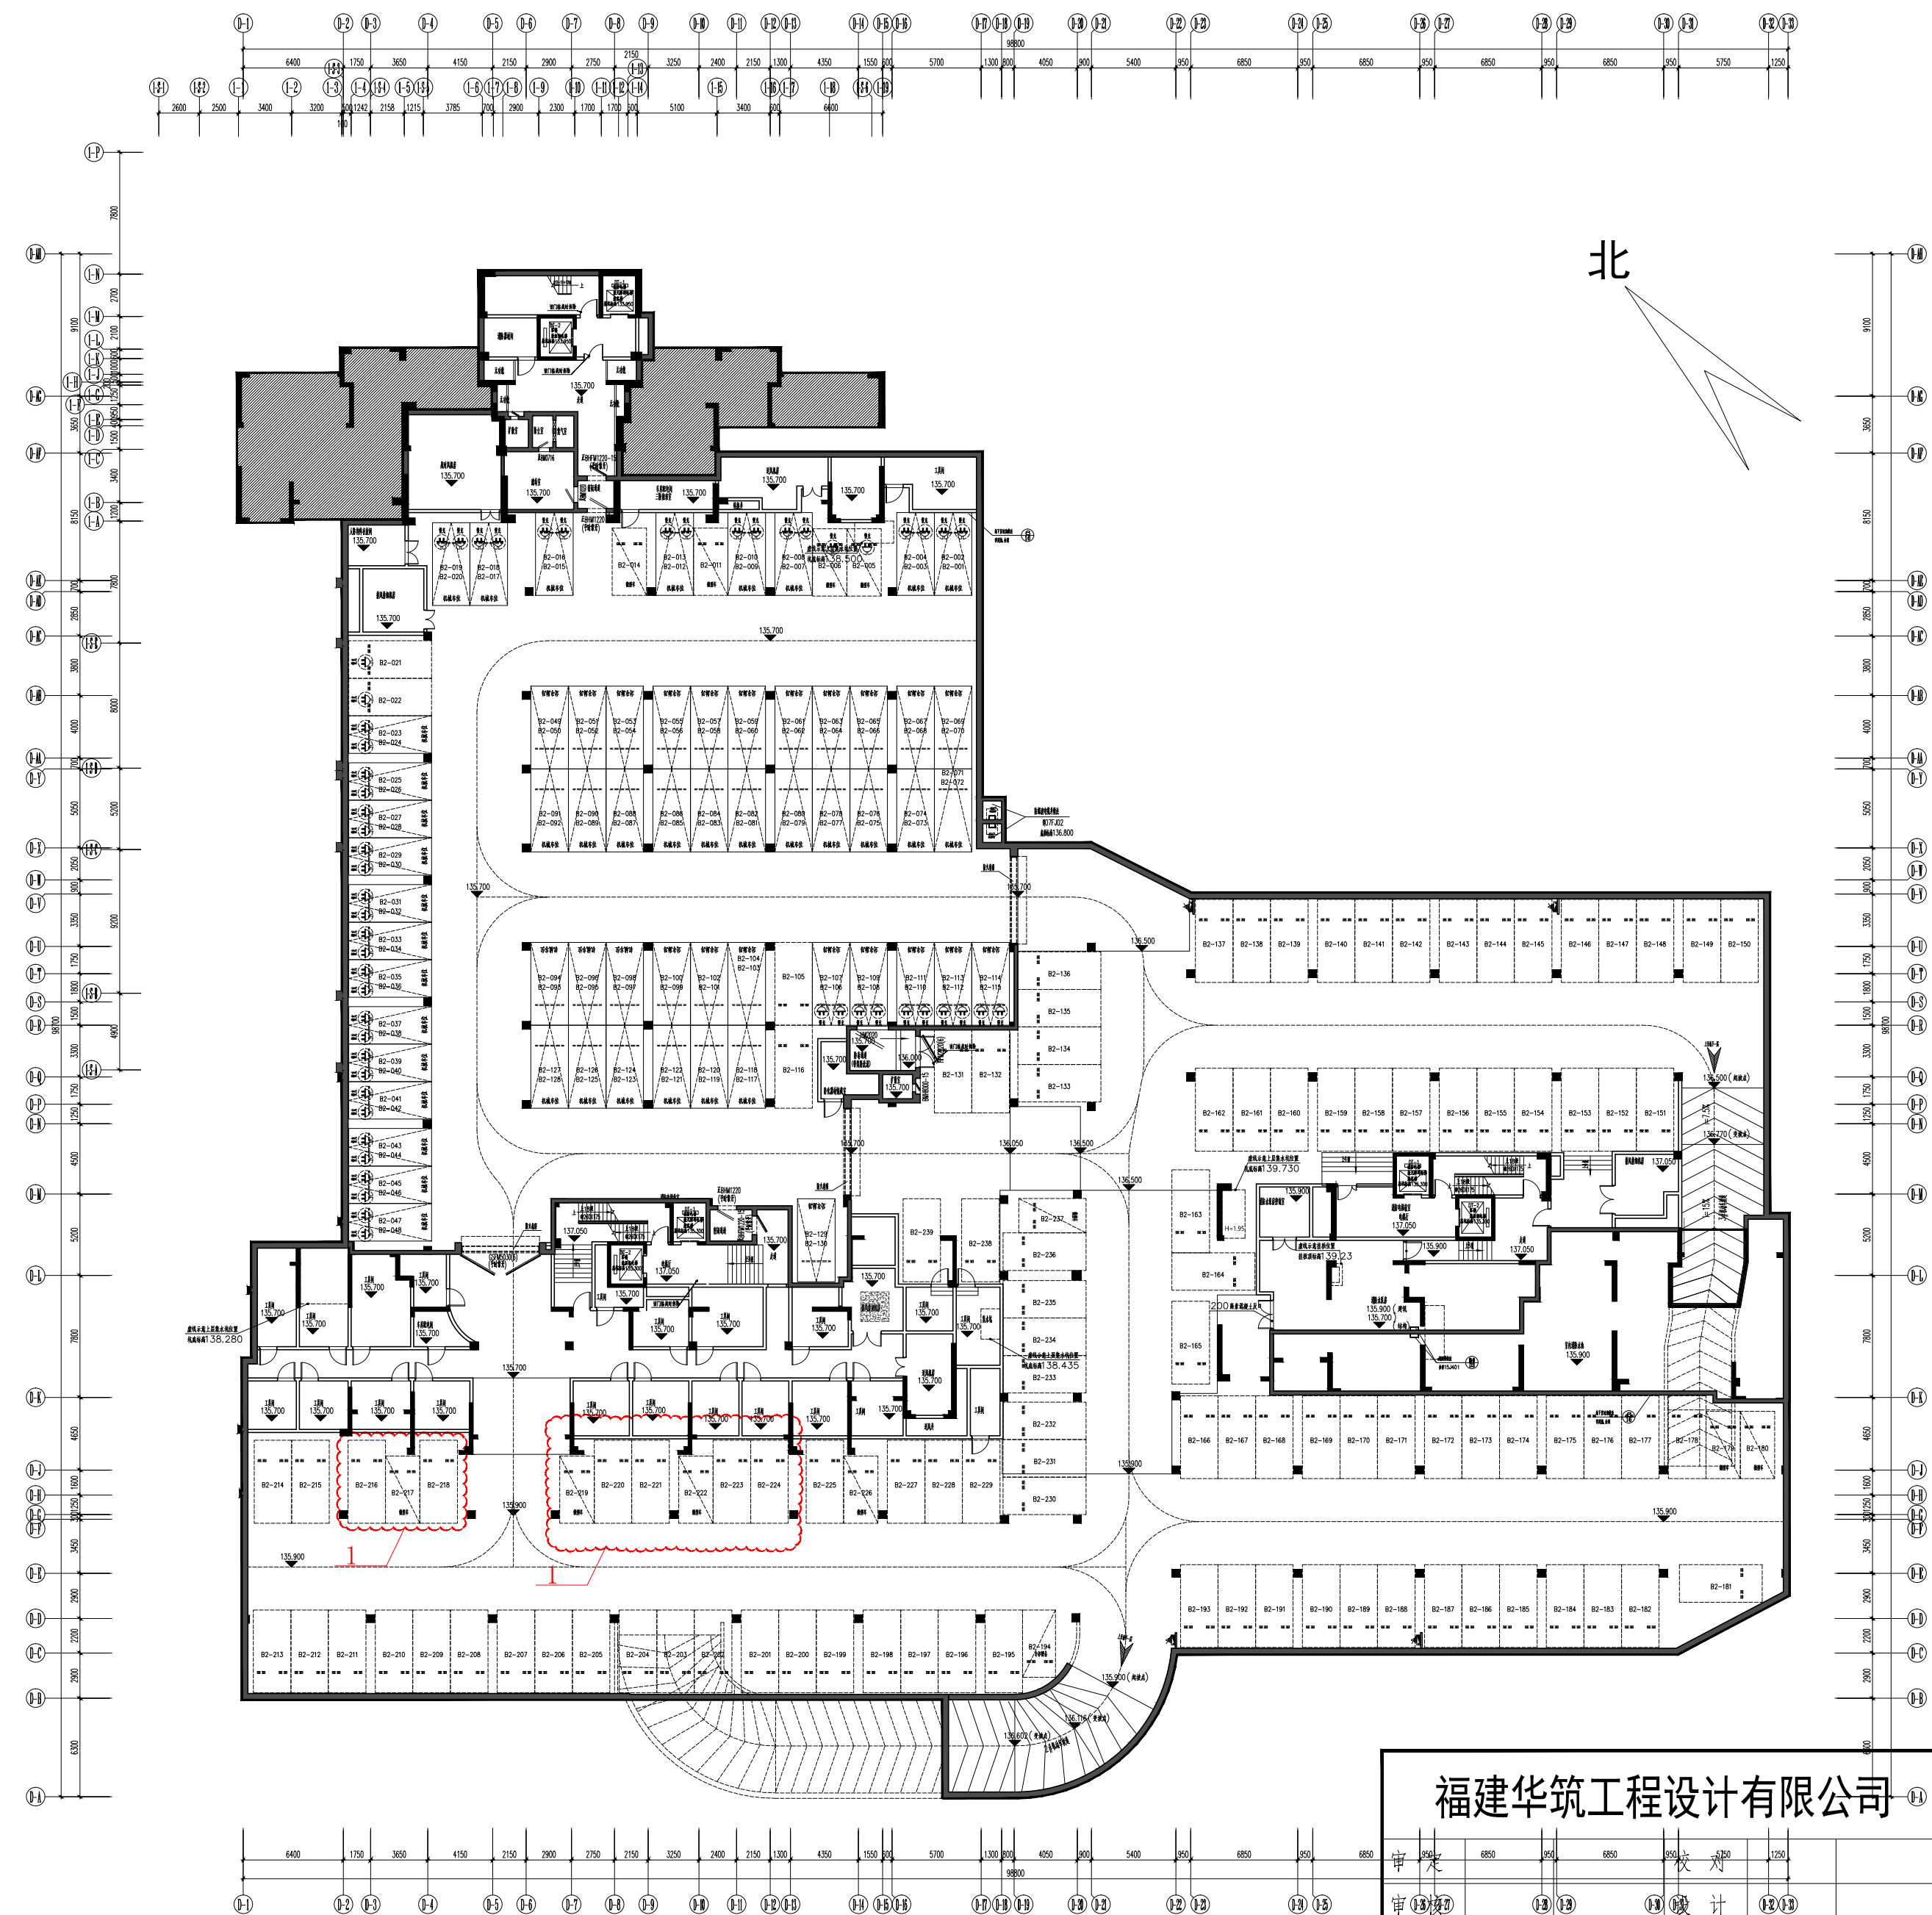

地下室二层平面图(变更后)

注:1.地下室总建筑面积: 12823.604m²
2.地下室一层建筑面积: 6637.136m²
3.地下室二层建筑面积: 6186.468m²
4.本项目总停车数为441辆,其中地面停车位为44辆
地下室总停车数为403辆,其中小型车位259辆,无障碍车位2辆,
微型车位20辆,机械车位122辆,折算完20X0.7+259+2+122=397
机械车位占比122/441=27.67%

福建华筑工程设计有限公司				证书编号	A135031045	审查批准号		工程号	2022058	项目号
				建设单位	福建一建集团三明（绿岩）盛建置业有限公司			阶段	方案	
				项目名称	福建一建金麟郡			专业	建筑	版本号
				比例				图号		
								日期	2024.06	
项目负责				专业负责			地下室二层平面图(变更后)			