



桂
75.32

0、恒古恆正伴恆動

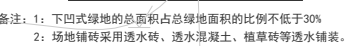

注：本图纸未经施工图审查和政府各职能部门审查不得用于施工。

专业
建筑
结构
给排水

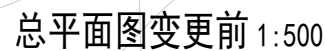

备注：1：下凹式绿地的总面积占总绿地面积的比例不低于30%
2：场地铺装采用透水砖、透水混凝土、植草砖等透水铺装。

福建清华建筑设计院有限公司


设计号 PROJECT NO.		22-03-02	
审定 AUTHORIZED BY			
项目负责人 PROJECT CHIEF MANAGER		周 宇	
专业负责人 DISCIPLINE RESPONSIBLE BY		周 宇	
审核 VERIFIED BY		周 宇	
校 对 CHECKED BY		曹文财	
设 计 DESIGNED BY		张艳滨	
制 图 DRAWN BY		张艳滨	
比 例 SCALE	1:500	图 别 PHASE	总建初
日 期 DATE	2021.10	图 号 NO.	04

注：本图纸未经施工图审查和政府各职能部门审查不得用于施工。

一层平面变更

变更内容:

- 1、重新确定0标高位置；
- 2、首层楼梯间加装门窗；
- 3、增设架空层。

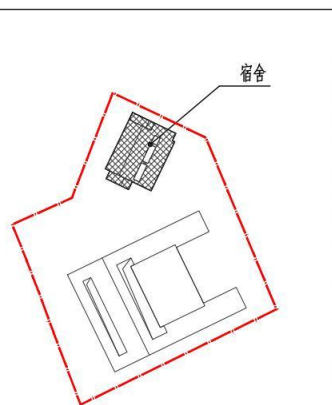

一层平面图变更后 1:100

注：1.本楼总建筑面积1274.35m²，
其中计容建筑面积为954.37m²，
不计容建筑面积为319.98m²，
占地面积为372.40m²。
2.本层计容建筑面积为52.42m²。

福建清华建筑设计院有限公司



FUJIAN QINGHUA
ARCHITECTURE DESIGN INSTITUTE Co, Ltd

备注:
NOTES

施工图审查单位：
CONSTRUCTION DRAWING CENSORED BY

三明市建筑工程施工图设计文件审查中心

施工图审查合格书编号：
CONSTRUCTION DRAWING CERTIFICATE NO.

图纸专用章:
DRAWING STAMP

注册建筑师执业章:
REGISTERED ARCHITECT'S STAMP

注册结构师执业章:
REGISTERED ENGINEER'S STAMP

版别 VERSION	序号 NO.	日期 DATE

建设单位
CLIENT

工程名称	PROJECT NAME
------	--------------

项目工程 ITEM NAME	数量 QUANTITY	单位 UNIT	材料名称 MATERIAL NAME	规格 SPECIFICATION	品牌 BRAND	产地 ORIGIN	备注 REMARKS
1. 基础工程	1	m³	混凝土	C30	海螺	中国	
2. 主体结构	1	m³	钢筋混凝土	C30	海螺	中国	
3. 屋面工程	1	m²	防水卷材	SBS	东方雨虹	中国	
4. 装饰装修	1	m²	乳胶漆	立邦	立邦	中国	
5. 安装工程	1	m	电线电缆	国标	正泰	中国	
6. 给排水工程	1	m	PPR管	20mm	伟星	中国	
7. 暖通工程	1	m	散热器	铜铝复合	金鹿	中国	
8. 电气工程	1	m	配电箱	200A	正泰	中国	
9. 弱电工程	1	m	网络线	六类	超五类	中国	
10. 其他工程	1	m	其他材料				

图 名
SHEET NAME

一层平面图变更后

设计号
PROJECT NO.

審定
AUTHORIZED BY

AUTHORIZED BY
项目负责人
PROJECT CHIEF

DISCIPLINE RESPONSIBLE BY

DISCIPLINE R
审核
VERIFIED BY

CHECKED BY

DESIGNED BY

DESTINGED
制 图
DRAWN BY

比例
SCALE

日期
DATE

注:本图纸未经施工图审查和政府各职能部门审查不得用于施工。

注:本图纸未经施工图审查和政府各职能部门审查不得用于施工。




注: 1.本楼总建筑面积952.32m²,
其中计容建筑面积为952.32m²,
占地面积为372.40m².
2.本层计容建筑面积为372.40m².

日期	
姓名	
姓名	
专业	电气
日期	
姓名	
姓名	
专业	建筑
专业	结构
专业	给排水

二层平面变更

变更内容:

- 1、因增设架空层，本层房间功能更改；
- 2、因增设架空层，部分门改窗；
- 3、因增设架空层，删除部分门窗；
- 4、因增设架空层，增设矮墙；
- 5、本层楼层标高由0.000修改为3.880。

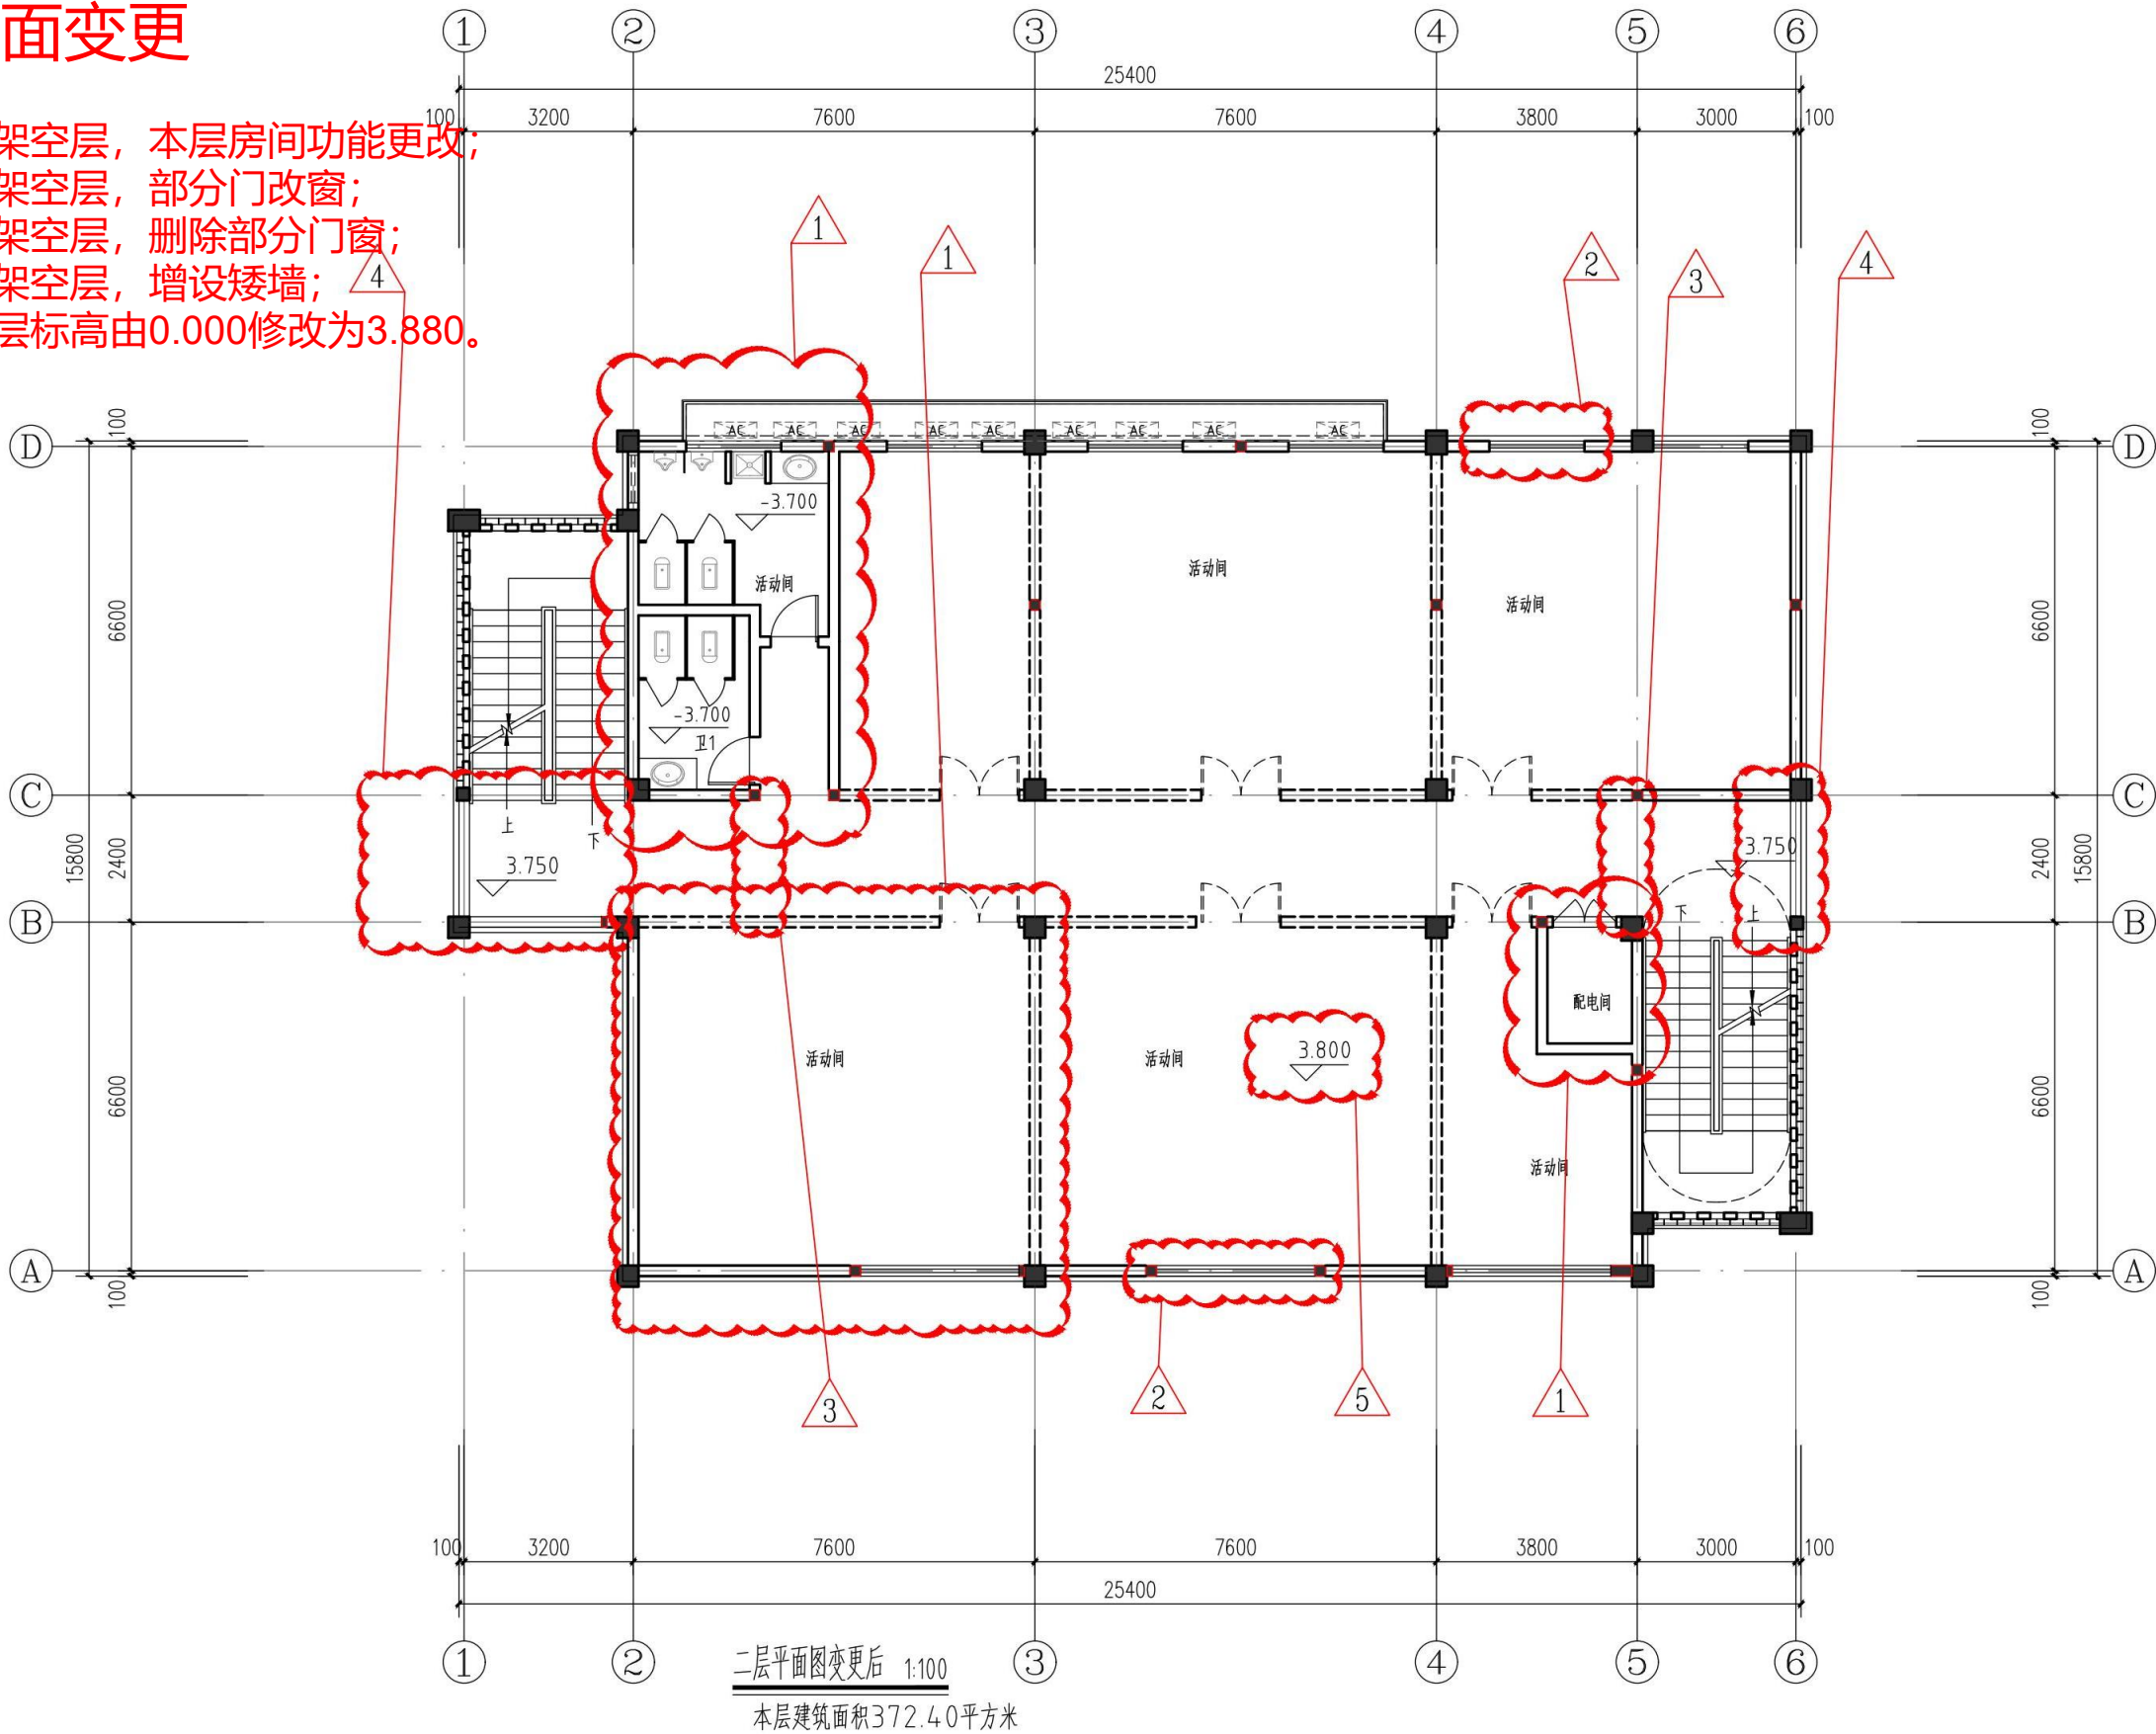

福建清华建筑设计院有限公司



FUJIAN QINGHUA
ARCHITECTURE DESIGN INSTITUTE Co., Ltd

备注:

NOTES

施工图审查单位:
CONSTRUCTION DRAWING CENSORED BY

三明市建筑工程施工图设计文件审查中心

施工图审查合格书编号:
CONSTRUCTION DRAWING CERTIFICATE NO.

图纸专用章:
DRAWING STAMP

注册建筑师执业章:
REGISTERED ARCHITECT'S STAMP

注册结构师执业章:
REGISTERED ENGINEER'S STAMP

版别 VERSION 序号 NO. 日期 DATE

建设单位
CLIENT

工程名称
PROJECT NAME

项目工程
ITEM NAME

图名
SHEET NAME

一层平面图变更后

设计号

PROJECT NO.

审定

AUTHORIZED BY

项目负责人

PROJECT CHIEF MANAGER

专业负责人

DISCIPLINE RESPONSIBLE BY

审核

VERIFIED BY

校对

CHECKED BY

设计

DESIGNED BY

制图

DRAWN BY

比例

SCALE

日期

DATE

图别


PHASE

图号

NO.

注: 本图纸未经施工图审查和政府各职能部门审查不得用于施工。

日期	
姓名	
姓名	
专业	电气
日期	
姓名	
姓名	
专业	建筑
专业	结构
专业	给排水

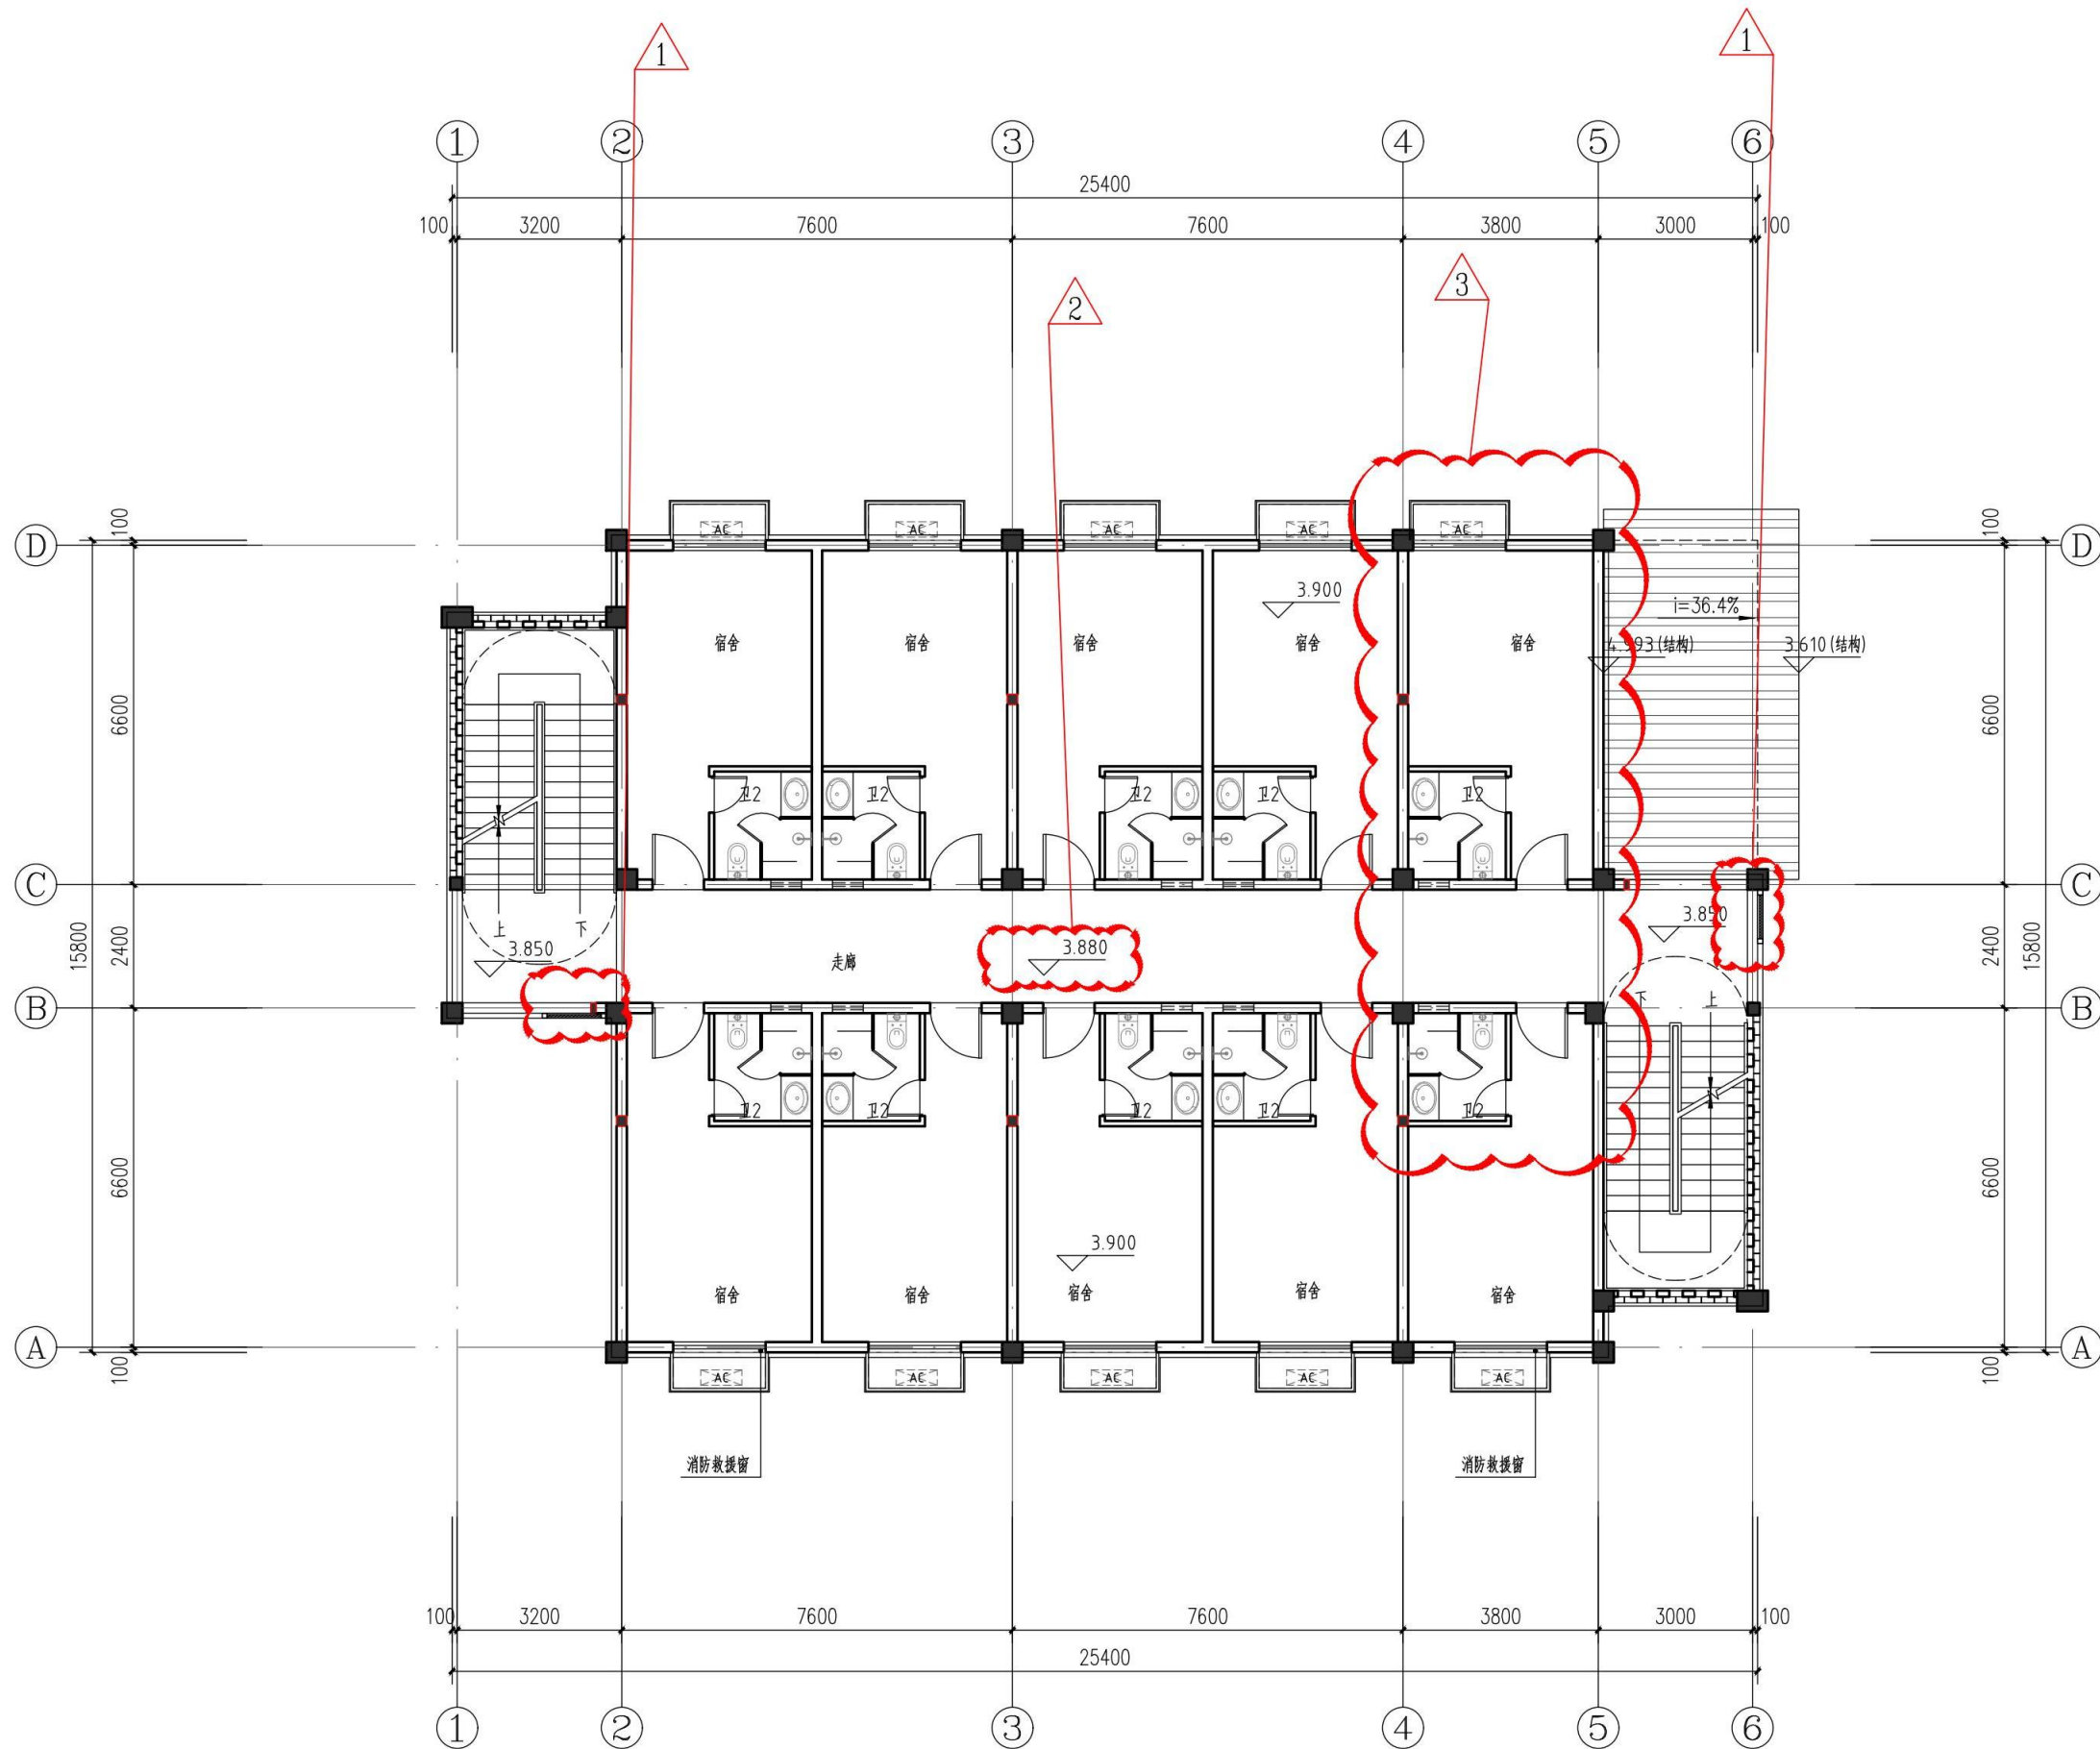

二层平面图变更前 1:100
本层建筑面积353.32平方米

福建清华建筑设计院有限公司



FUJIAN QINGHUA
ARCHITECTURE DESIGN INSTITUTE Co., Ltd

备注:
NOTES

施工图审查单位:
CONSTRUCTION DRAWING CENSORED BY

三明市建筑工程施工图设计文件审查中心

施工图审查合格书编号:
CONSTRUCTION DRAWING CERTIFICATE NO.

图纸专用章:
DRAWING STAMP

注册建筑师执业章:
REGISTERED ARCHITECT'S STAMP

注册结构师执业章:
REGISTERED ENGINEER'S STAMP

版别 VERSION	序号 NO.	日期 DATE
------------	--------	---------

建设单位 CLIENT	
----------------	--

工程名称 PROJECT NAME	
----------------------	--

项目工程 ITEM NAME	
-------------------	--

图名 SHEET NAME	二层平面图变更前
------------------	----------

设计号 PROJECT NO.	
--------------------	--

审定 AUTHORIZED BY	
---------------------	--

项目负责人 PROJECT CHIEF MANAGER	
--------------------------------	--

专业负责人 DISCIPLINE RESPONSIBLE BY	
------------------------------------	--

审核 VERIFIED BY	
-------------------	--

校对 CHECKED BY	
------------------	--

设计 DESIGNED BY	
-------------------	--

制图 DRAWN BY	
----------------	--

比例 SCALE	
-------------	--

图别 PHASE	
-------------	--

日期 DATE	
------------	--

图号 NO.	
-----------	--


注:本图纸未经施工图审查和政府各职能部门审查不得用于施工。

日期	
姓名	
姓名	
专业	电气
暖通	
日期	
姓名	
姓名	
专业	建筑
结构	
给排水	

三层平面变更

变更内容:

- 1、删除部分百叶窗;
- 2、本层楼层标高由3.880修改为7.680;
- 3、卫生间位置及空调板位置修改。

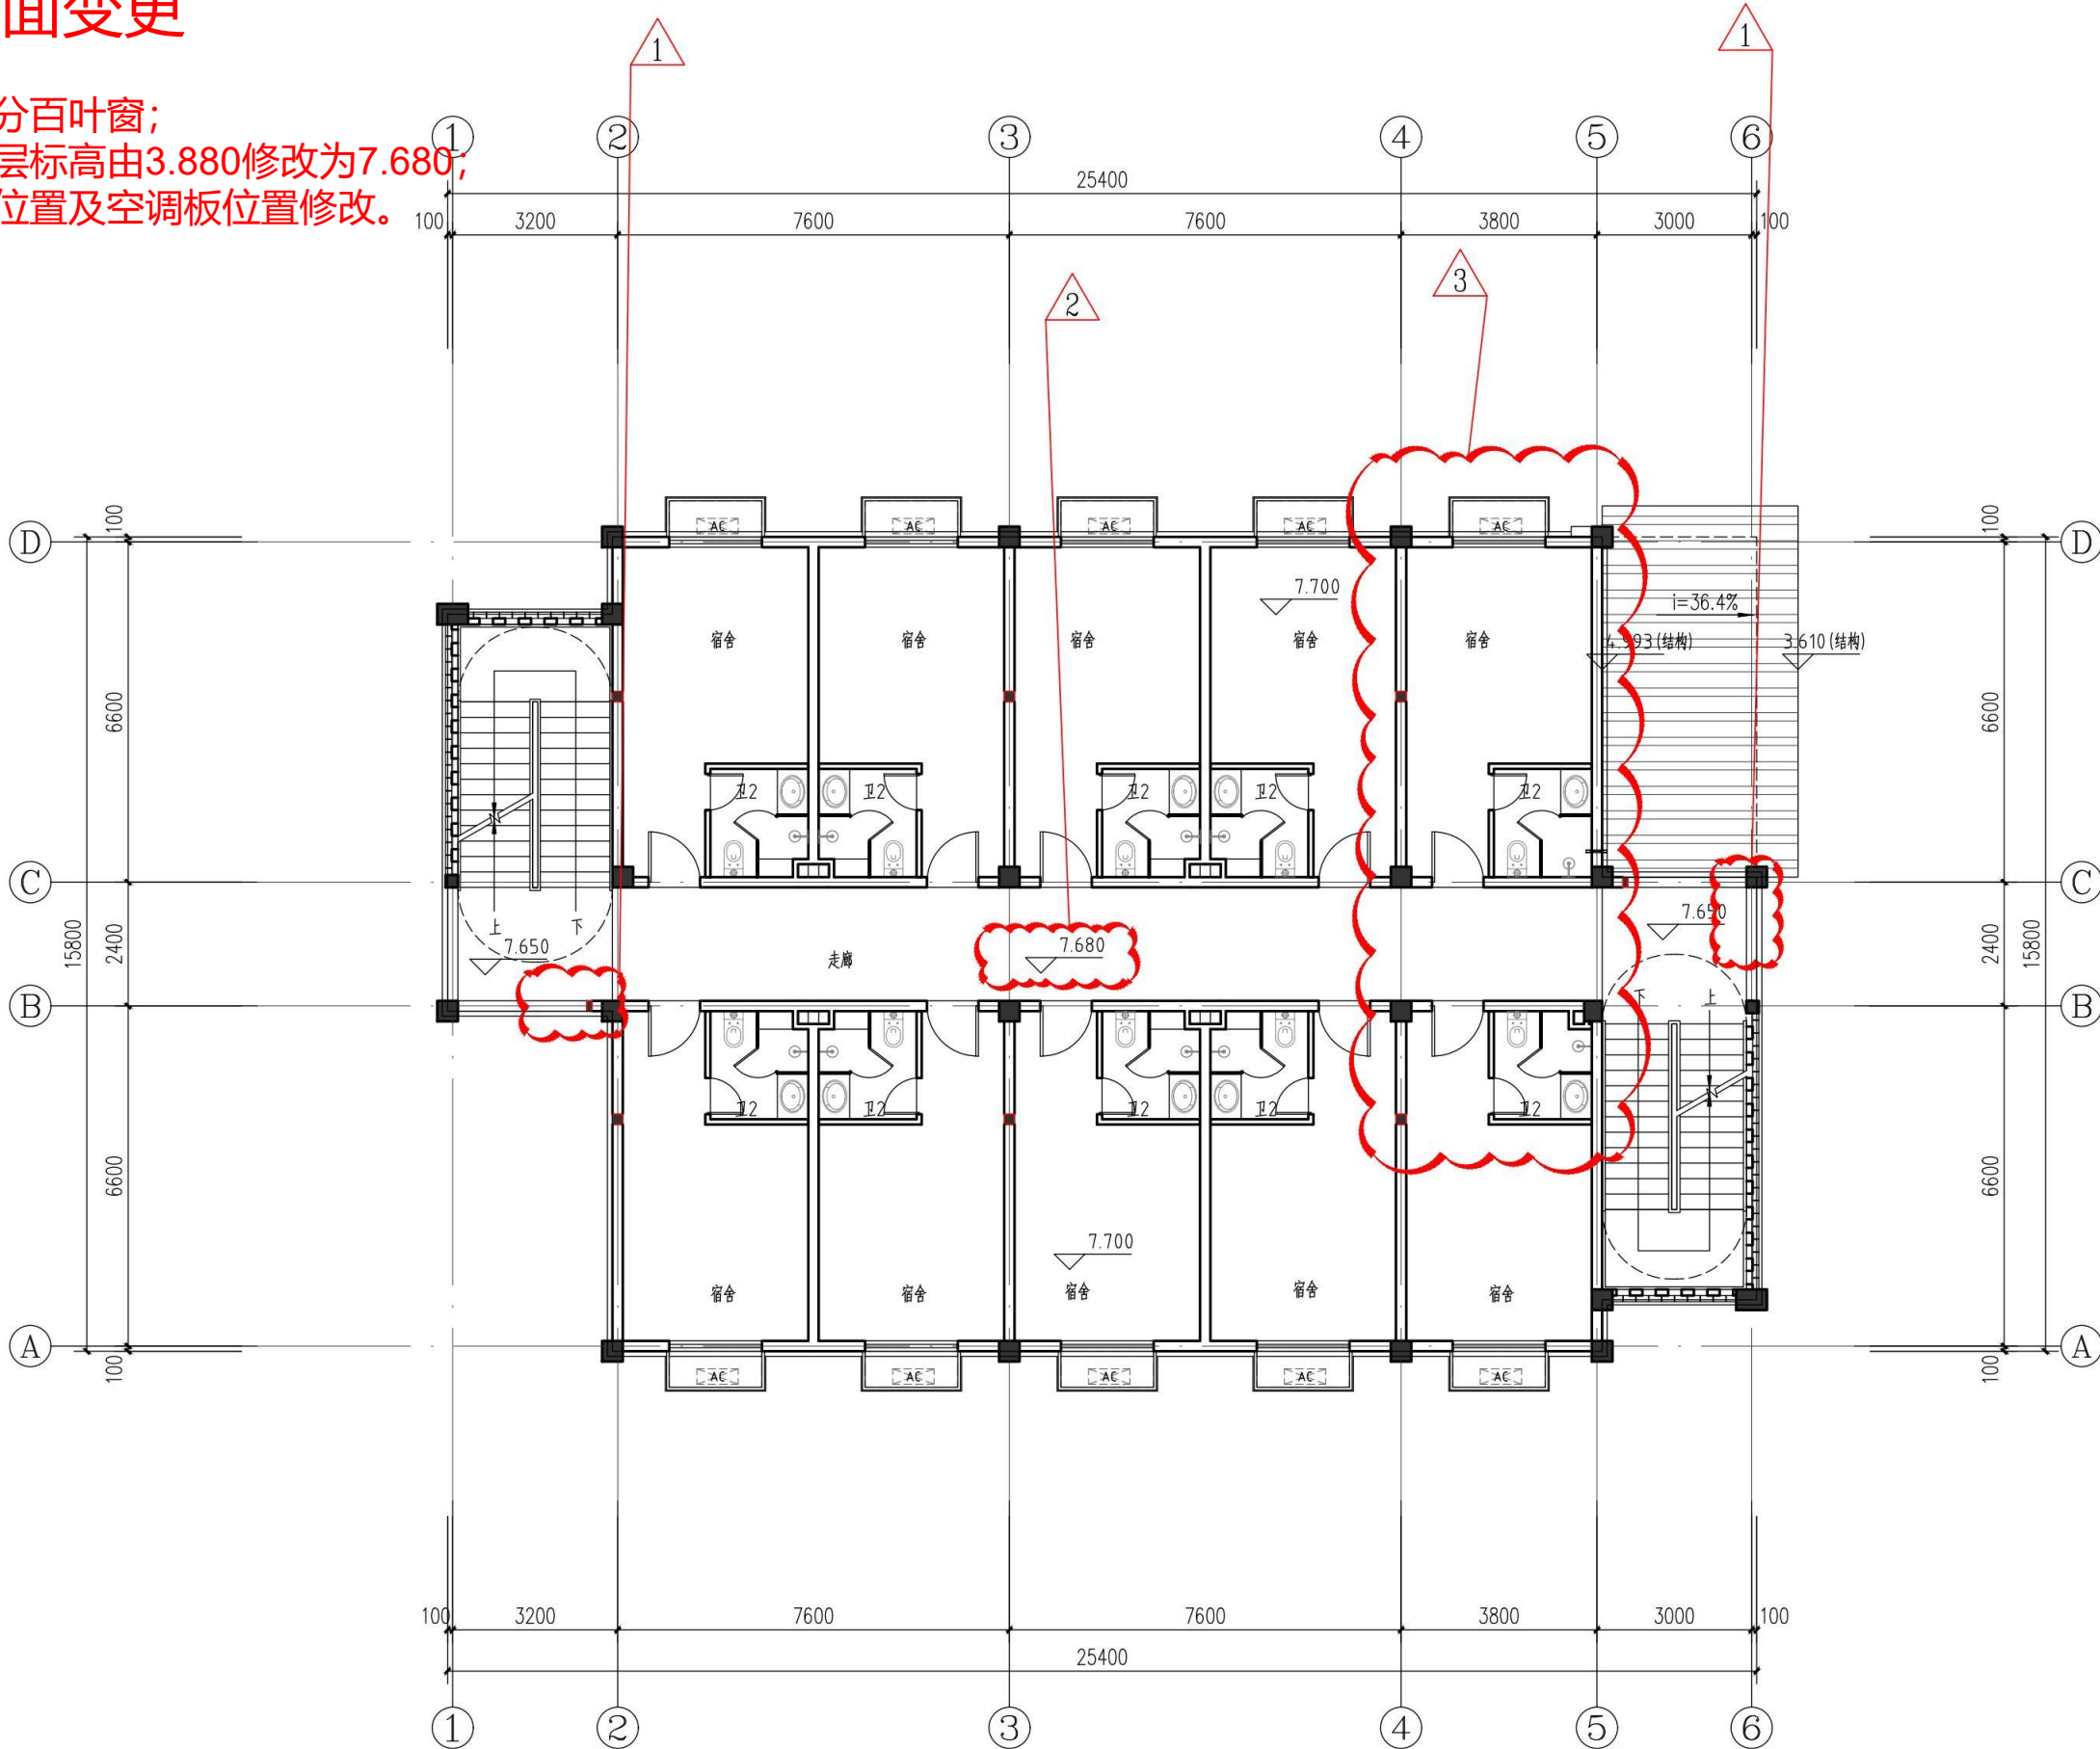

三层平面图变更后 1:100

本层建筑面积352.6平方米

福建清华建筑设计院有限公司



FUJIAN QINGHUA
ARCHITECTURE DESIGN INSTITUTE Co., Ltd

备注:

NOTES

施工图审查单位:
CONSTRUCTION DRAWING CENSORED BY

三明市建筑工程施工图设计文件审查中心

施工图审查合格书编号:
CONSTRUCTION DRAWING CERTIFICATE NO.

图纸专用章:
DRAWING STAMP

注册建筑师执业章:
REGISTERED ARCHITECT'S STAMP

注册结构师执业章:
REGISTERED ENGINEER'S STAMP

版别 VERSION	序号 NO.	日期 DATE
------------	--------	---------

建设单位
CLIENT

工程名称
PROJECT NAME

项目工程
ITEM NAME

图名
SHEET NAME

三层平面图变更后

设计号
PROJECT NO.

审定
AUTHORIZED BY

项目负责人
PROJECT CHIEF MANAGER

专业负责人
DISCIPLINE RESPONSIBLE BY

审核
VERIFIED BY

校对
CHECKED BY

设计
DESIGNED BY

制图
DRAWN BY

比例
SCALE


日期
DATE

图别
PHASE

图号
NO.

注: 本图纸未经施工图审查和政府各职能部门审查不得用于施工。

专业	日期	姓名	专业	日期	姓名
建筑			电气		
结构			暖通		
给排水					

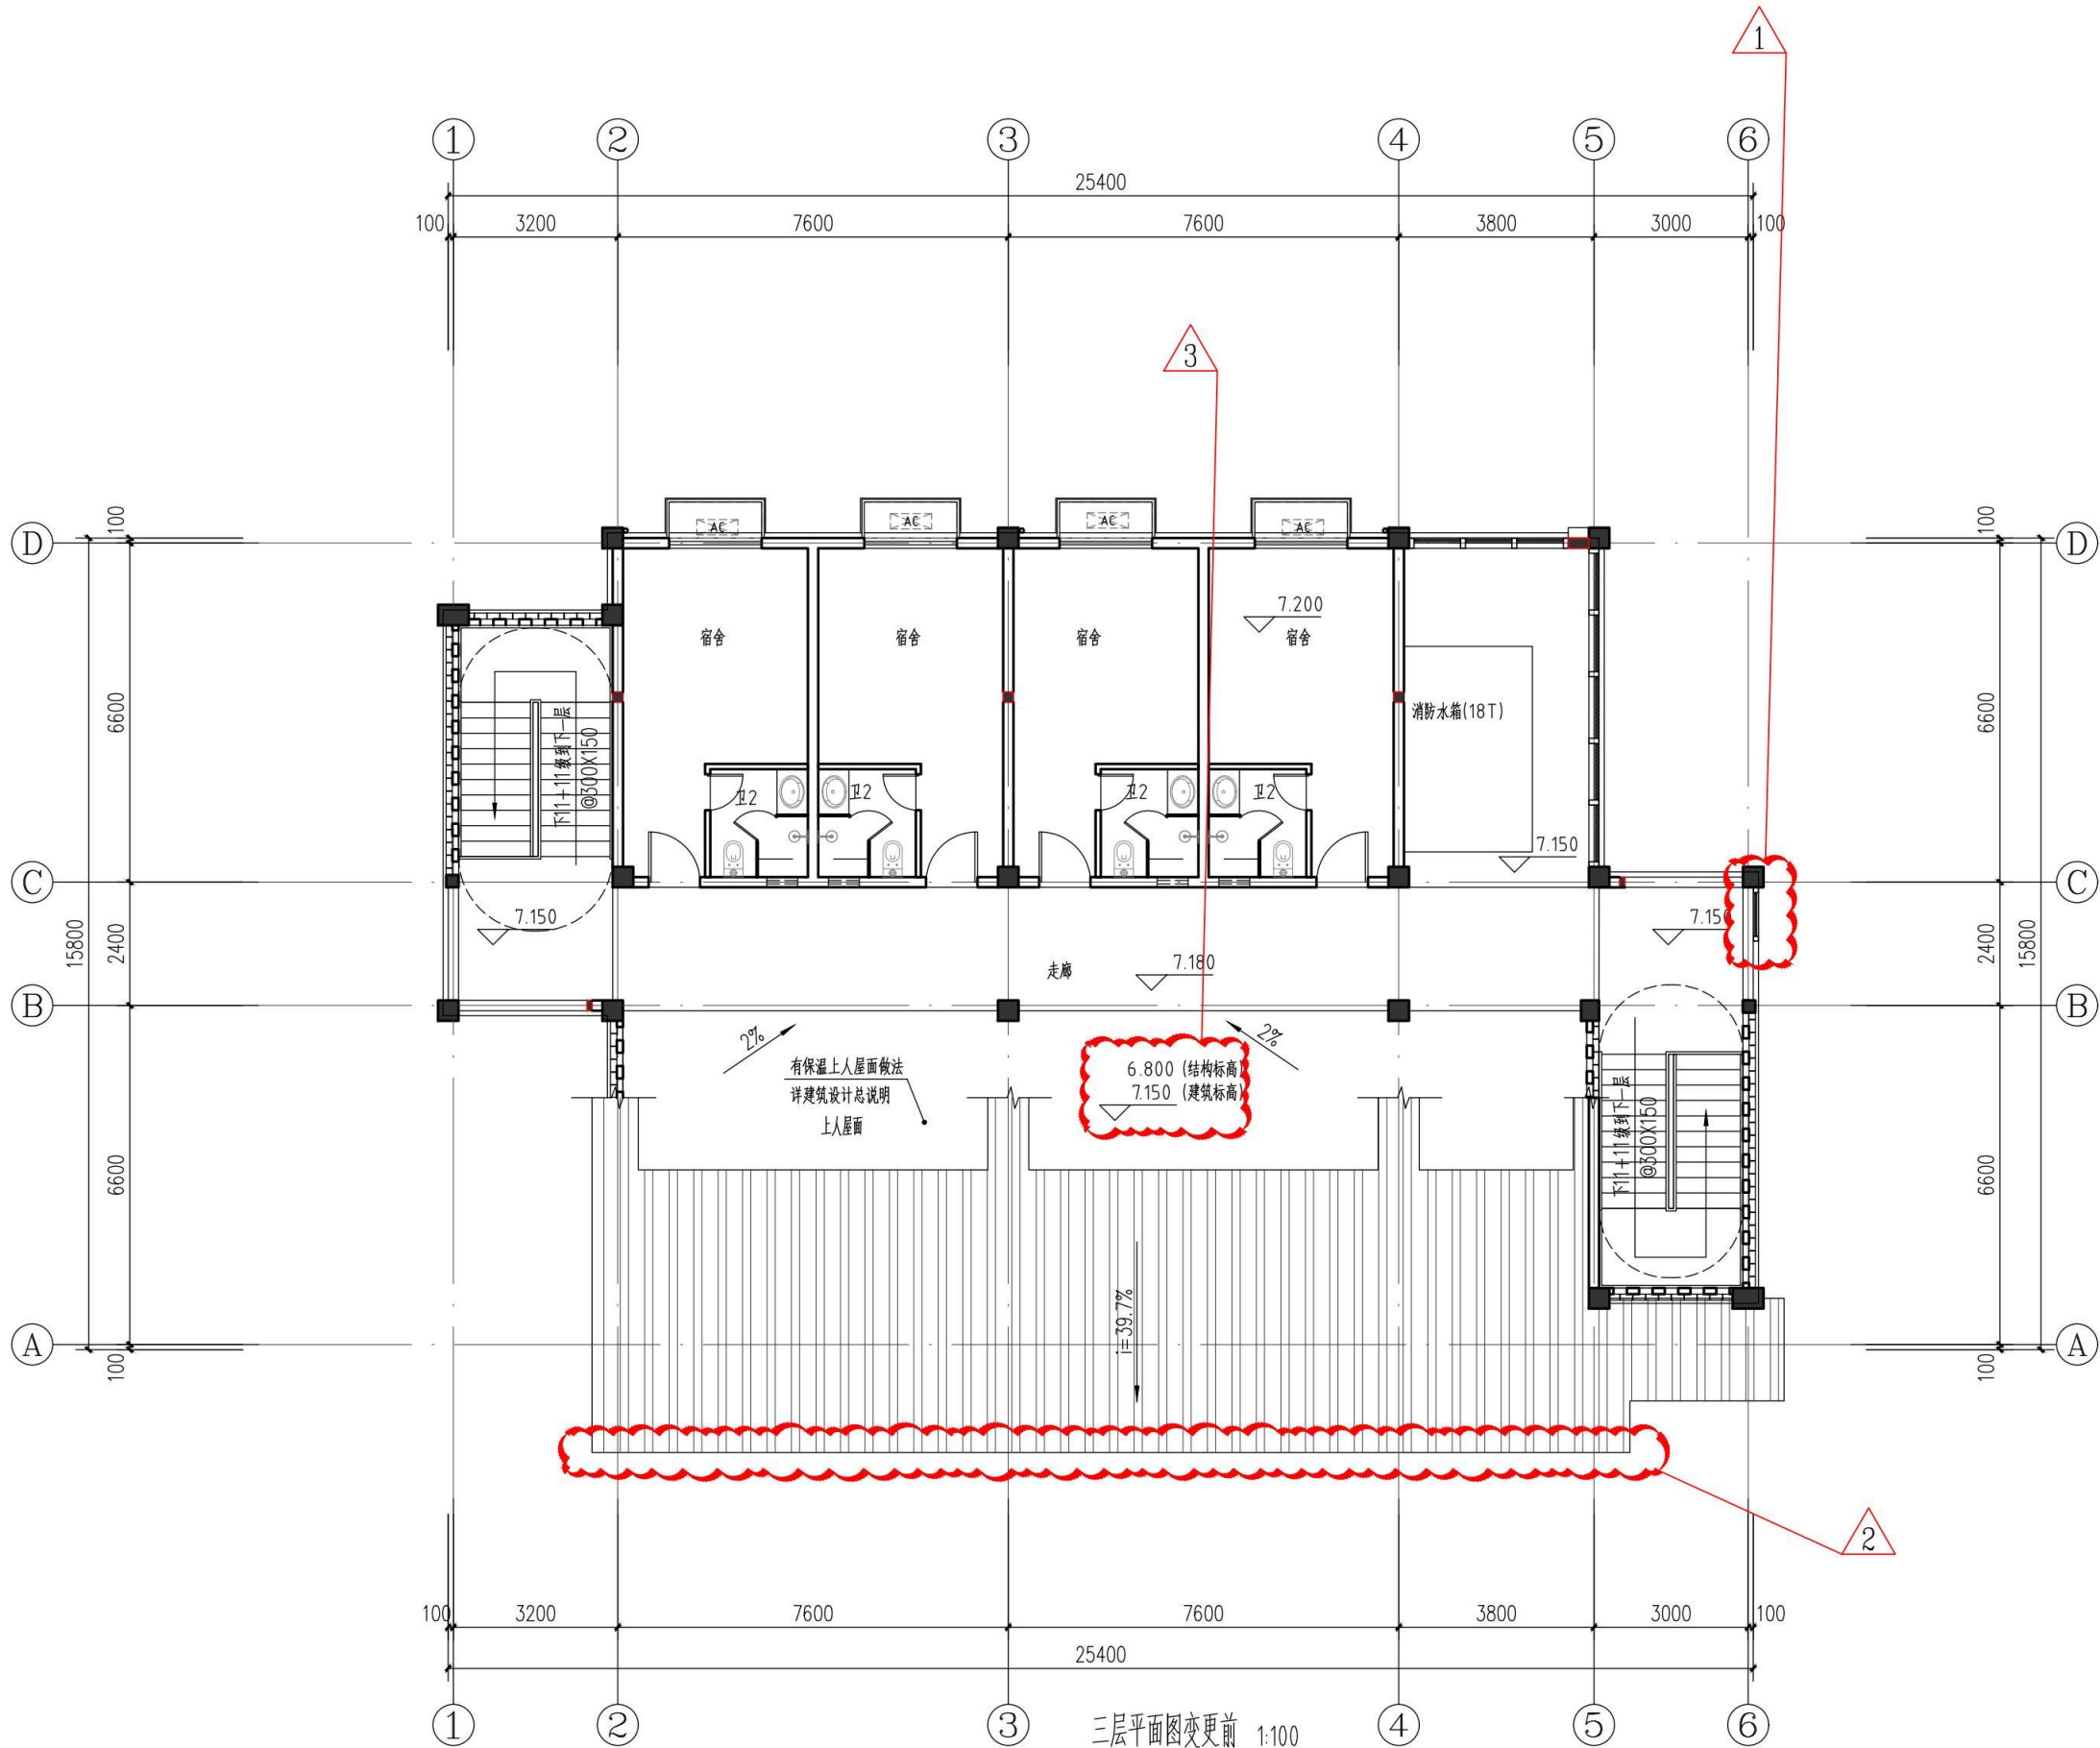

三层平面图变更前 1:100
注：1、本层建筑面积226.60平方米。

福建清华建筑设计院有限公司



FUJIAN QINGHUA
ARCHITECTURE DESIGN INSTITUTE Co., Ltd

备注：
NOTES

施工图审查单位：
CONSTRUCTION DRAWING CENSORED BY

三明市建筑工程施工图设计文件审查中心

施工图审查合格书编号：
CONSTRUCTION DRAWING CERTIFICATE NO.

图纸专用章：
DRAWING STAMP

注册建筑师执业章：
REGISTERED ARCHITECT'S STAMP

注册结构师执业章：
REGISTERED ENGINEER'S STAMP

版别 VERSION 序号 NO. 日期 DATE

建设单位
CLIENT

工程名称
PROJECT NAME


项目工程
ITEM NAME

图名
SHEET NAME 三层平面图变更前

设计号 PROJECT NO.		
审定 AUTHORIZED BY		
项目负责人 PROJECT CHIEF MANAGER		
专业负责人 DISCIPLINE RESPONSIBLE BY		
审核 VERIFIED BY		
校对 CHECKED BY		
设计 DESIGNED BY		
制图 DRAWN BY		
比例 SCALE		图别 PHASE
日期 DATE		图号 NO.

注：本图纸未经施工图审查和政府各职能部门审查不得用于施工。

专业	日期	姓名	专业	日期	姓名
建筑			电气		
结构			暖通		
给排水					

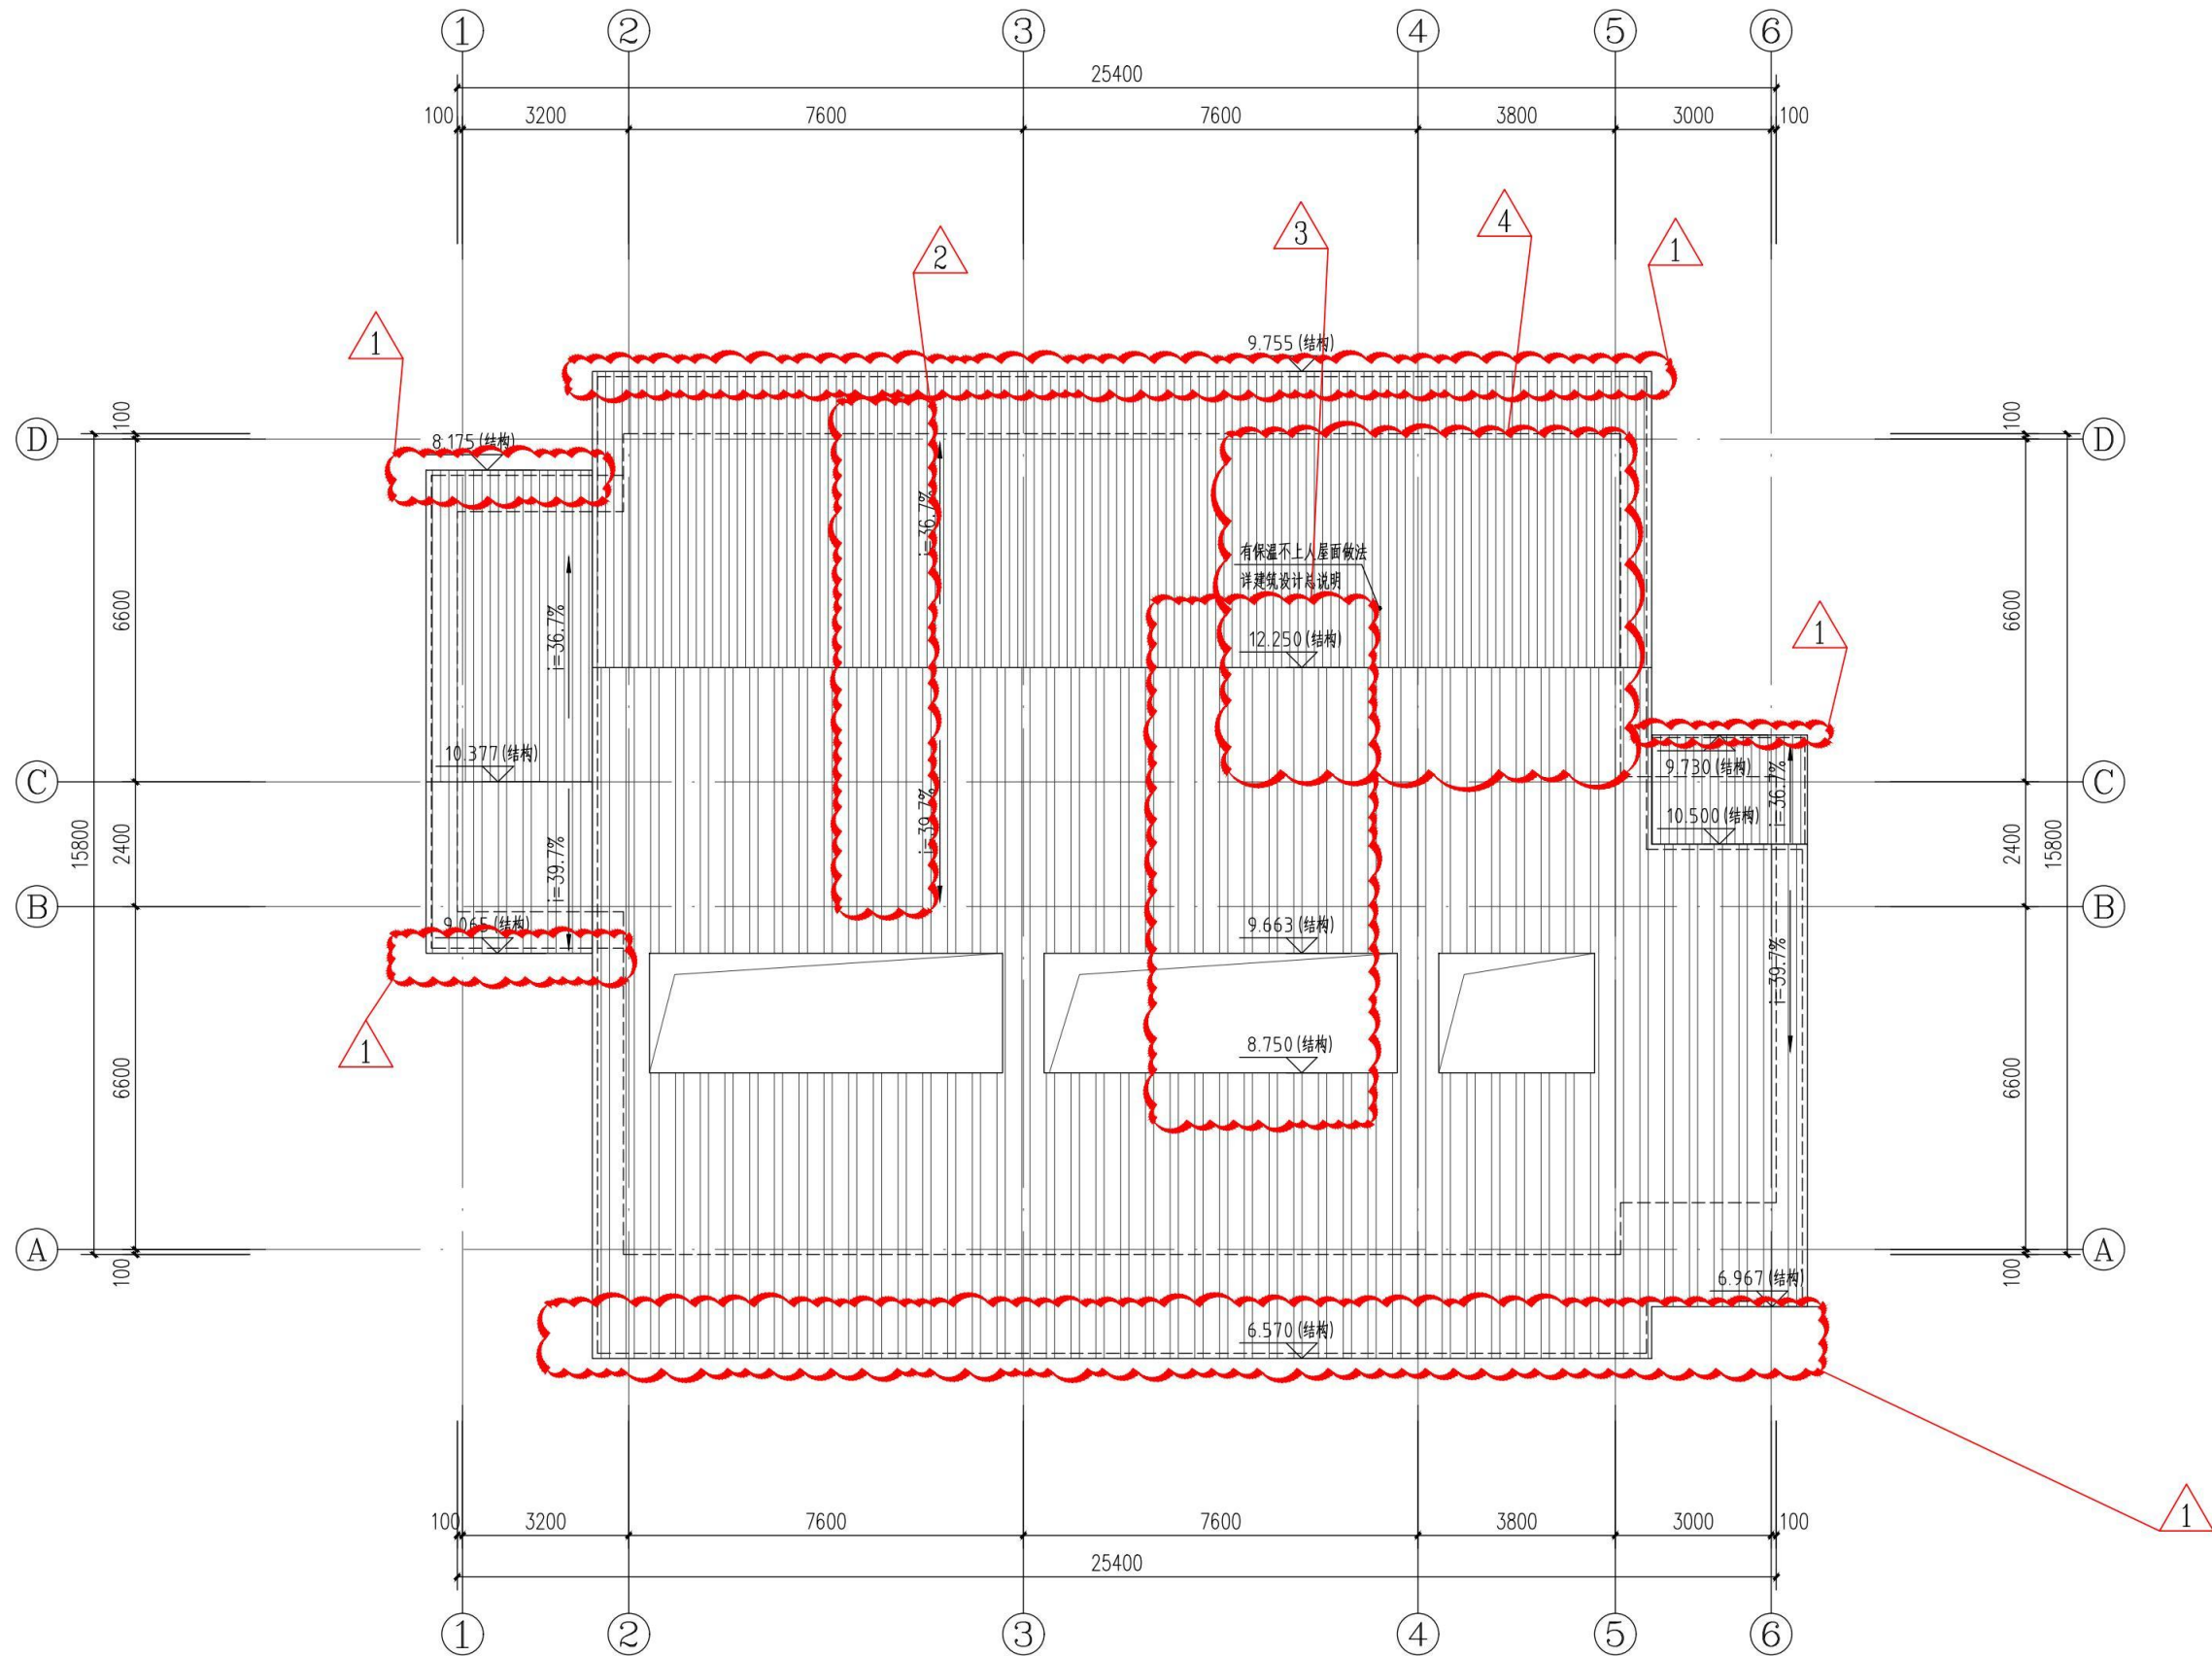

福建清华建筑设计院有限公司



FUJIAN QINGHUA
ARCHITECTURE DESIGN INSTITUTE Co., Ltd

备注:
NOTES

施工图审查单位:
CONSTRUCTION DRAWING CENSORED BY

三明市建设工程施工图设计文件审查中心

施工图审查合格书编号:
CONSTRUCTION DRAWING CERTIFICATE NO.

图纸专用章:
DRAWING STAMP

注册建筑师执业章:
REGISTERED ARCHITECT'S STAMP

注册结构师执业章:
REGISTERED ENGINEER'S STAMP

版别	VERSION	序号	NO.	日期	DATE
----	---------	----	-----	----	------

建设单位	CLIENT
------	--------

工程名称	PROJECT NAME
------	--------------

项目工程	ITEM NAME
------	-----------


图名	SHEET NAME	屋顶平面图变更前
----	------------	----------

设计号	PROJECT NO.	
审定	AUTHORIZED BY	
项目负责人	PROJECT CHIEF MANAGER	
专业负责人	DISCIPLINE RESPONSIBLE BY	
审核	VERIFIED BY	
校对	CHECKED BY	
设计	DESIGNED BY	
制图	DRAWN BY	
比例	SCALE	图别
日期	DATE	图号
		NO.

注: 本图纸未经施工图审查和政府各职能部门审查不得用于施工。

专业	实名	签名	日期	专业	实名	签名	日期
建筑				电气			
结构				暖通			
给排水							


变更内容:

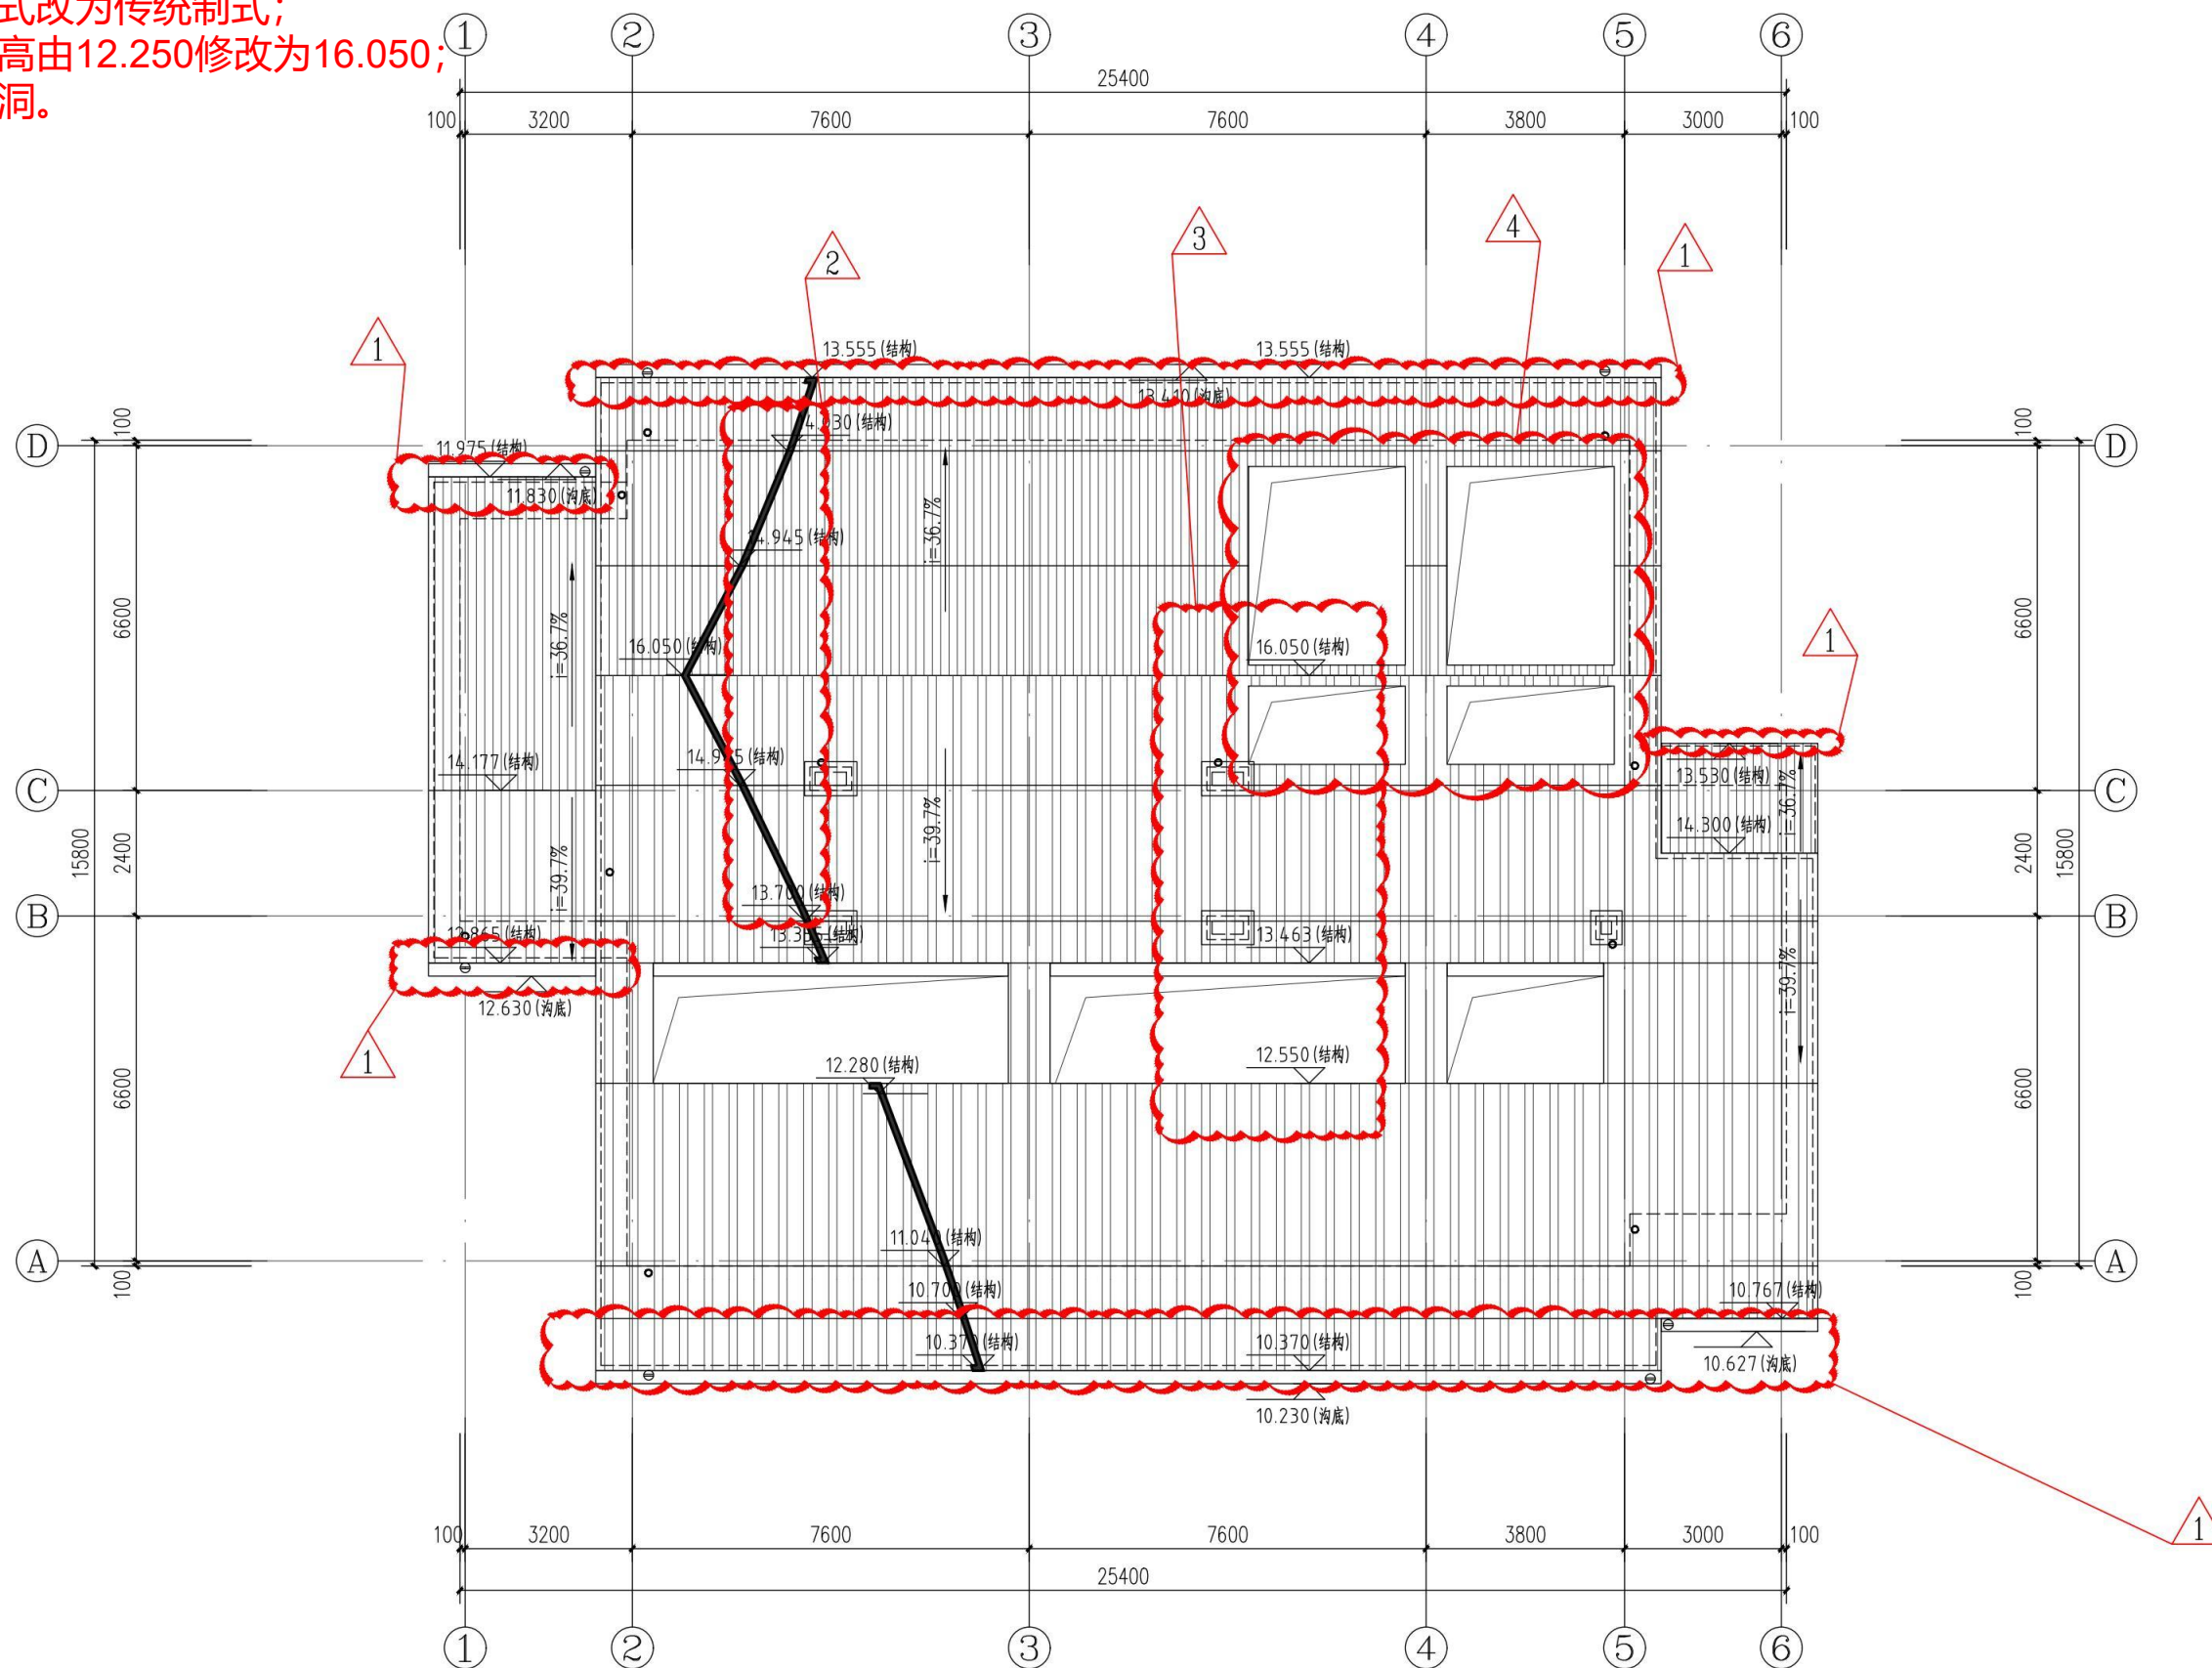

福建清华建筑设计院有限公司

FUJIAN QINGHUA
ARCHITECTURE DESIGN INSTITUTE Co, Ltd

专业	实名	签名	日期	专业	实名	签名	日期
建筑				电气			
结构				暖通			
给排水							

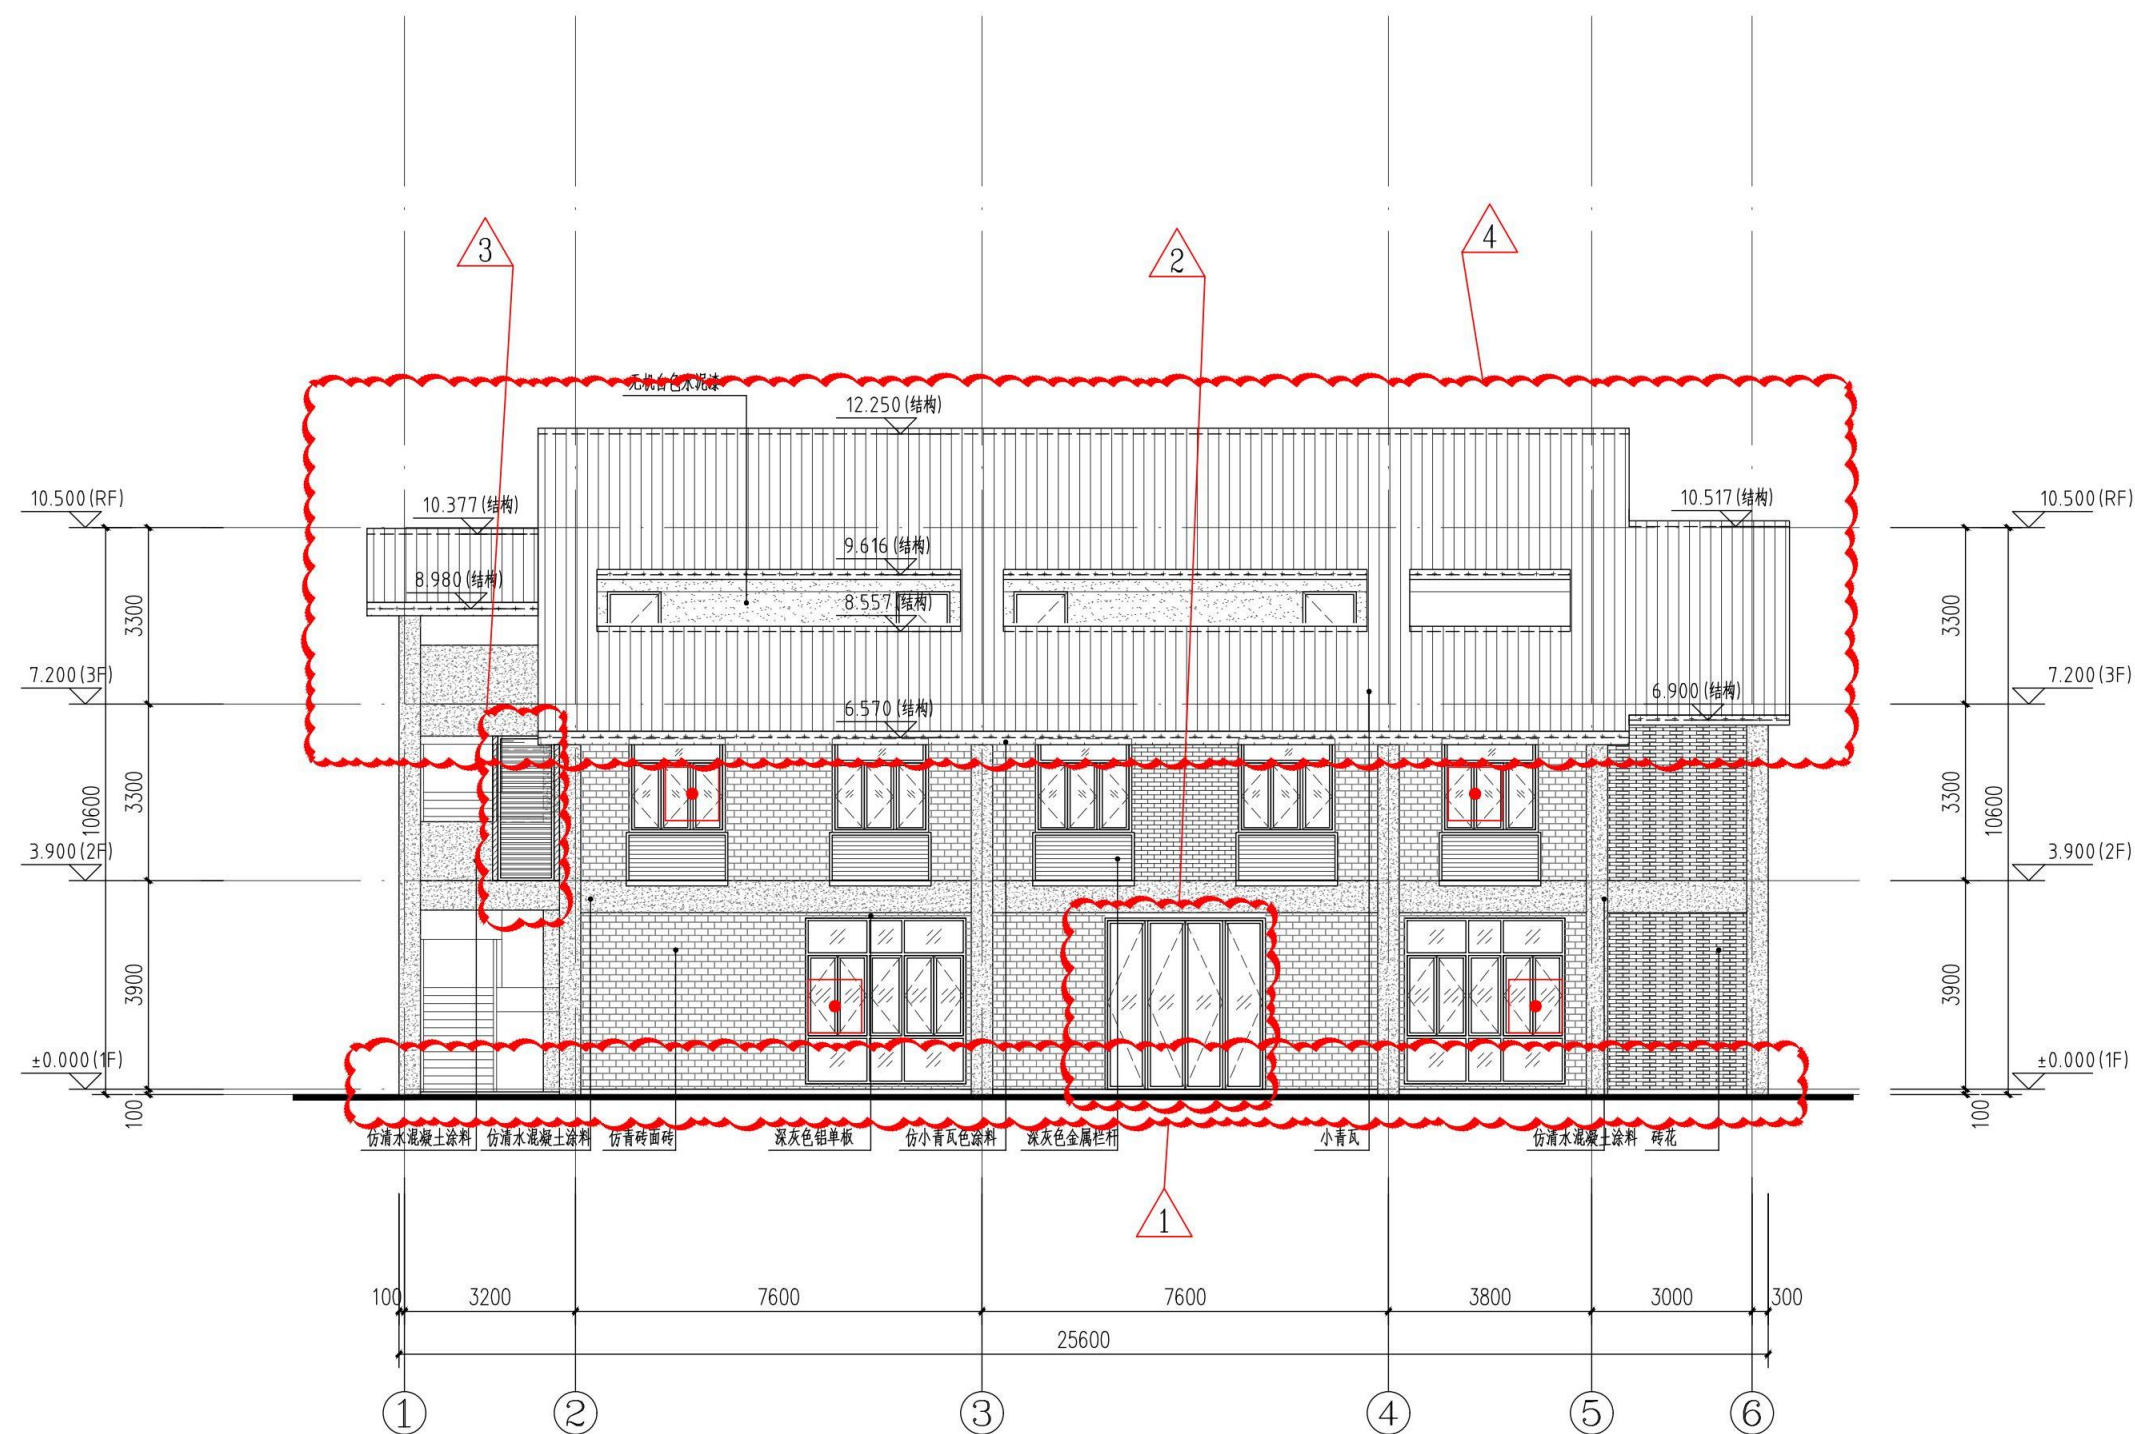

①-⑥轴立面图变更前 1:100

福建清华建筑设计院有限公司



FUJIAN QINGHUA
ARCHITECTURE DESIGN INSTITUTE Co., Ltd

备注:
NOTES

施工图审查单位：
CONSTRUCTION DRAWING CENSORED BY

三明市建筑工程施工图设计文件审查中心

施工图审查合格书编号：
CONSTRUCTION DRAWING CERTIFICATE NO.

图纸专用章:
DRAWING STAMP

注册建筑师执业章:
REGISTERED ARCHITECT'S STAMP

注册结构师执业章:
REGISTERED ENGINEER'S STAMP

版別 VERSION	序号 NO.	日期 DATE

建设单位 CLIENT	
----------------	--

工程名称 PROJECT NAME	
----------------------	--

项目工程 ITEM NAME	
-------------------	--

图 名
SHEET NAME

①-⑥轴立面图变更前


设计号			
PROJECT NO.			
审定			
AUTHORIZED BY			
项目负责人			
PROJECT CHIEF MANAGER			
专业负责人			
DISCIPLINE RESPONSIBLE BY			
审核			
VERIFIED BY			
校对			
CHECKED BY			
设计			
DESIGNED BY			
制图			
DRAWN BY			
比例		图别	
SCALE		PHASE	
日期		图号	
DATE		NO.	

注:本图纸未经施工图审查和政府各职能部门审查不得用于施工。

1-6轴立面变更

变更内容:

- 1、增设架空层;
- 2、部分门改窗;
- 3、删除部分百叶窗
- 4、根据屋顶平面图调整立面相应修改。

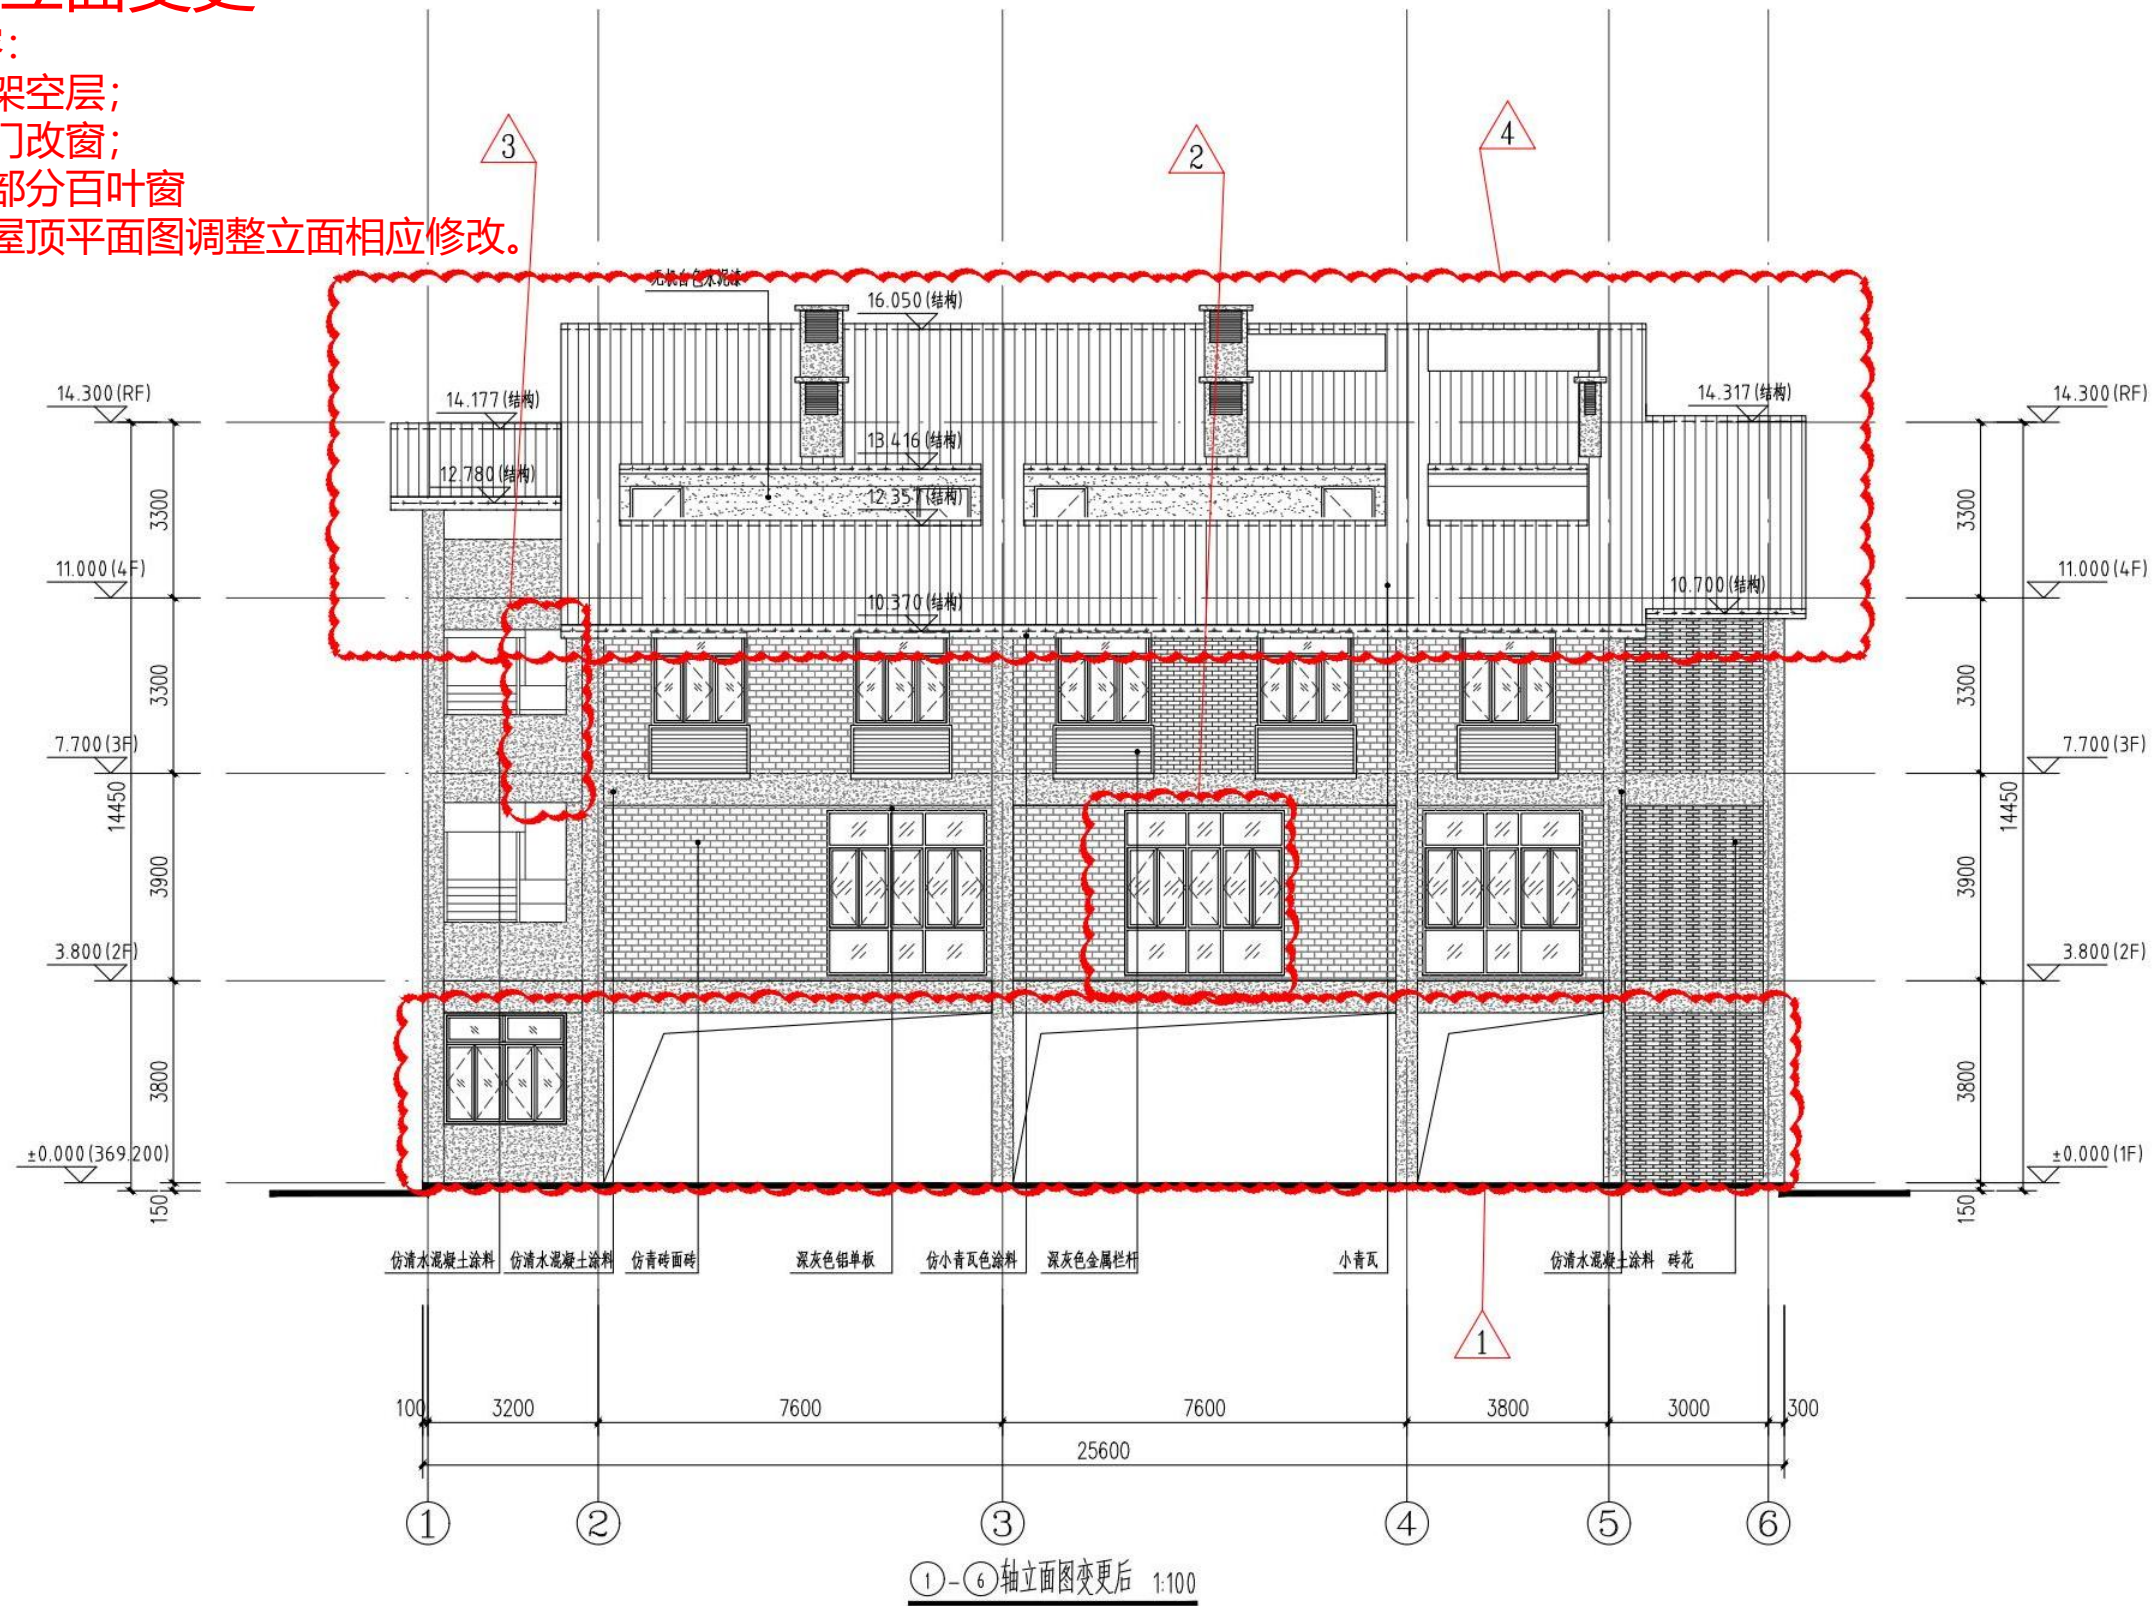

福建清华建筑设计院有限公司



FUJIAN QINGHUA
ARCHITECTURE DESIGN INSTITUTE Co., Ltd

备注:
NOTES

施工图审查单位：
CONSTRUCTION DRAWING CENSORED BY

三明市建筑工程施工图设计文件审查中心

施工图审查合格书编号：
CONSTRUCTION DRAWING CERTIFICATE NO.

图纸专用章:
DRAWING STAMP

注册建筑师执业章:
REGISTERED ARCHITECT'S STAMP

注册结构师执业章:
REGISTERED ENGINEER'S STAMP

版别 VERSION	序号 NO.	日期 DATE

建设单位
CLIENT

工程名称
PROJECT NAME

项目工程
ITEM NAME

图 名
SHEET NAME

①-⑥轴立面图变更后

设计号
PROJECT NO.

審定

AUTHORIZED BY _____

项目负责人

PROJECT CHIEF MA

专业负责人

DISCIPLINE RES

VERIFIED BY

校 对

CHECKED BY

设计

DESIGNED BY

制 图

DRAIN BY _____

比例	
----	--

SCALE

日期

DATE: _____

注:本图纸未经施工图审查和政府各职能部门审查不得用于施工。

© 2006 The Authors

日期	
姓名	
姓名	
专业	电气
日期	
姓名	
姓名	
专业	建筑
姓名	结构
姓名	给排水



⑥-①轴立面图变更前 1:100

福建清华建筑设计院有限公司



FUJIAN QINGHUA
ARCHITECTURE DESIGN INSTITUTE Co., Ltd

备注:
NOTES

施工图审查单位:
CONSTRUCTION DRAWING CENSORED BY

三明市建筑工程施工图设计文件审查中心

施工图审查合格书编号:
CONSTRUCTION DRAWING CERTIFICATE NO.

图纸专用章:
DRAWING STAMP

注册建筑师执业章:
REGISTERED ARCHITECT'S STAMP

注册结构师执业章:
REGISTERED ENGINEER'S STAMP

版别 VERSION 序号 NO. 日期 DATE

建设单位
CLIENT

工程名称
PROJECT NAME

项目工程
ITEM NAME

图名
SHEET NAME

⑥-①轴立面图变更前

设计号
PROJECT NO.

审定
AUTHORIZED BY

项目负责人
PROJECT CHIEF MANAGER

专业负责人
DISCIPLINE RESPONSIBLE BY

审核
VERIFIED BY

校对
CHECKED BY

设计
DESIGNED BY

制图
DRAWN BY

比例
SCALE

日期
DATE


图别
PHASE

图号
NO.

注: 本图纸未经施工图审查和政府各职能部门审查不得用于施工。

专业	实名	签名	日期	专业	实名	签名	日期
建筑				电气			
结构				暖通			
给排水							

日期	
姓名	
姓名	
专业	电气
日期	
姓名	
姓名	
专业	建筑
专业	结构
专业	给排水

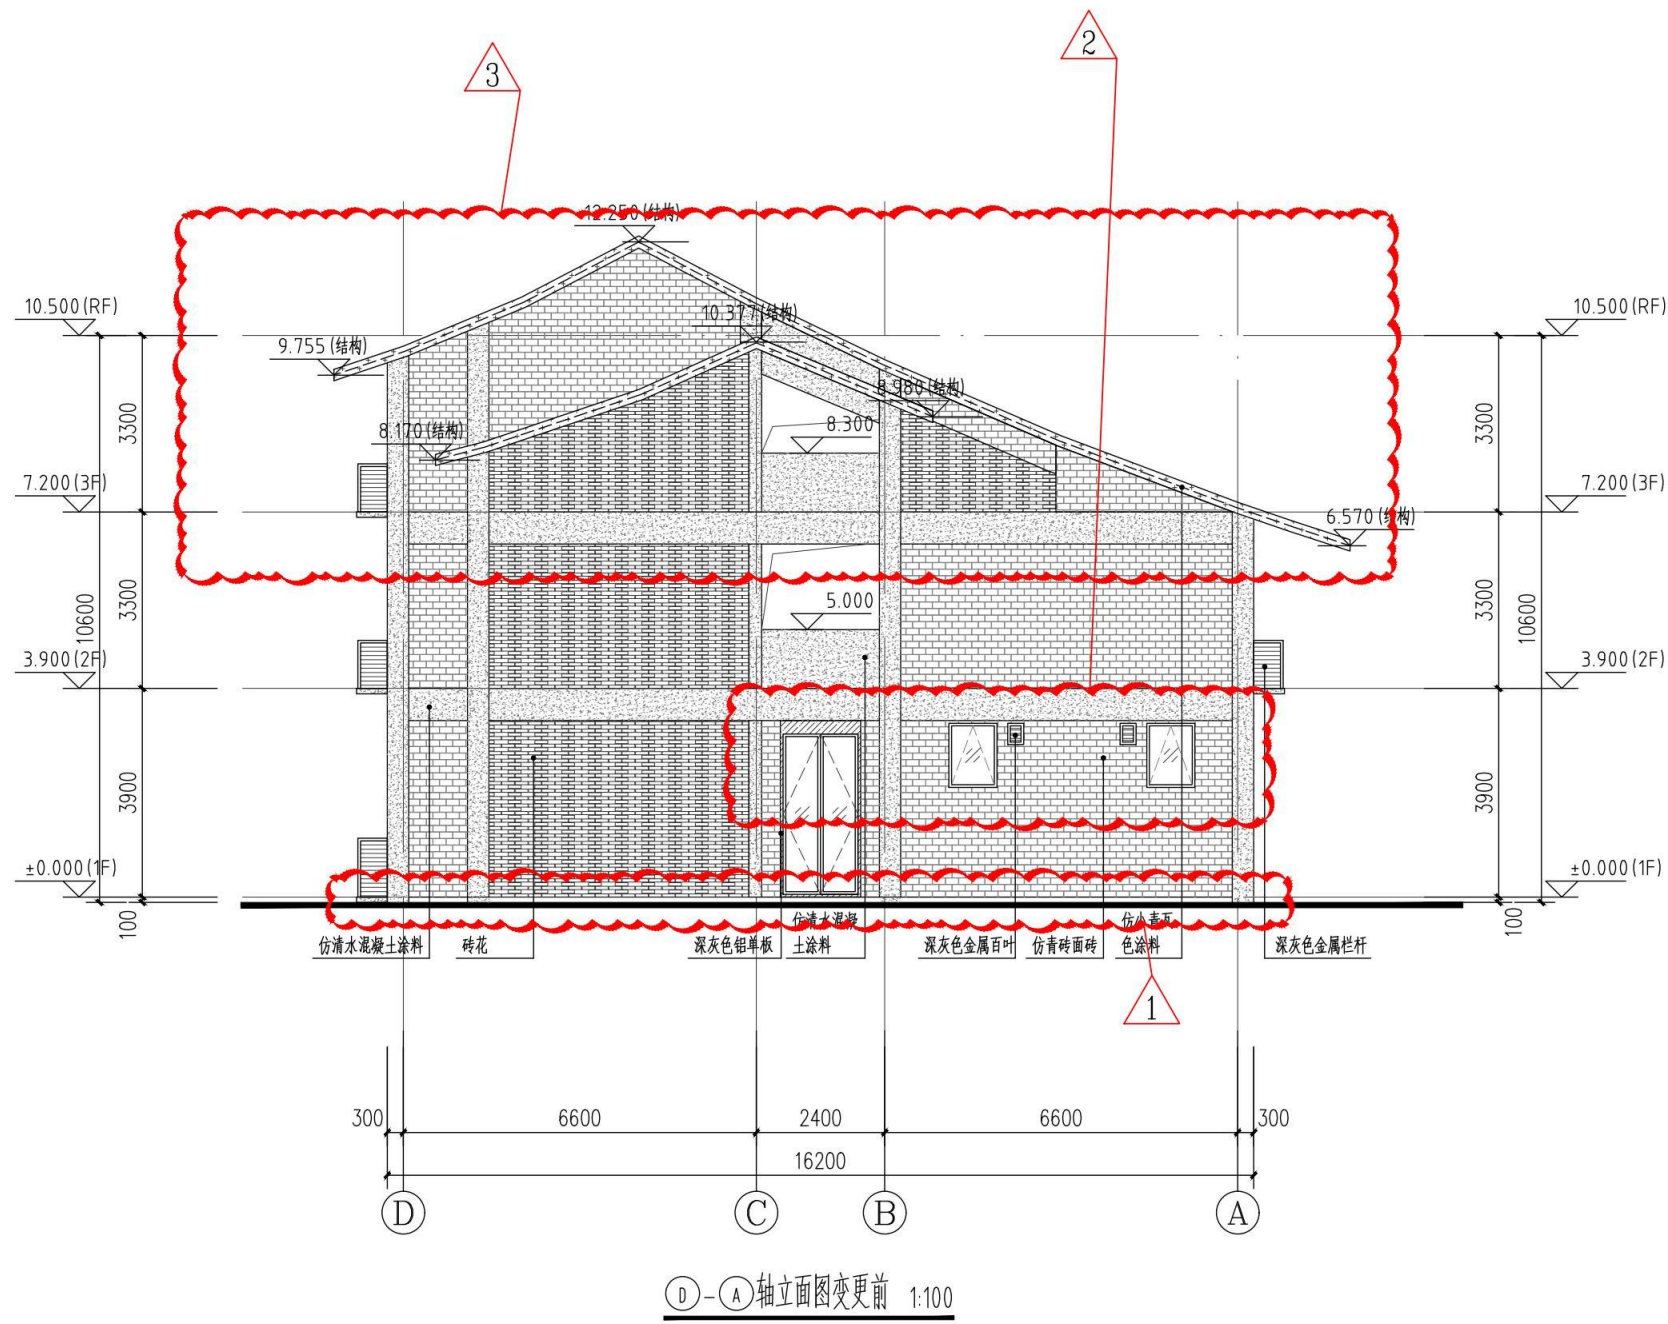

福建清华建筑设计院有限公司



FUJIAN QINGHUA
ARCHITECTURE DESIGN INSTITUTE Co., Ltd

备注:
NOTES

施工图审查单位:
CONSTRUCTION DRAWING CENSORED BY

三明市建筑工程施工图设计文件审查中心

施工图审查合格书编号:
CONSTRUCTION DRAWING CERTIFICATE NO.

图纸专用章:
DRAWING STAMP

注册建筑师执业章:
REGISTERED ARCHITECT'S STAMP

注册结构师执业章:
REGISTERED ENGINEER'S STAMP

版别 VERSION 序号 NO. 日期 DATE

建设单位
CLIENT

工程名称
PROJECT NAME

项目工程
ITEM NAME

图名
SHEET NAME

③-④轴立面图变更前

设计号
PROJECT NO.

审定
AUTHORIZED BY

项目负责人
PROJECT CHIEF MANAGER

专业负责人
DISCIPLINE RESPONSIBLE BY

审核
VERIFIED BY

校对
CHECKED BY

设计
DESIGNED BY

制图
DRAWN BY

比例
SCALE

日期
DATE

图别
PHASE

图号
NO.


注: 本图纸未经施工图审查和政府各职能部门审查不得用于施工。

日期	
姓名	
姓名	
专业	电气
日期	
姓名	
姓名	
专业	建筑
姓名	给排水

D-A轴立面变更

变更内容:

- 1、增设架空层;
- 2、根据二层平面图调整立面相应修改;
- 3、根据屋顶平面图调整立面相应修改。

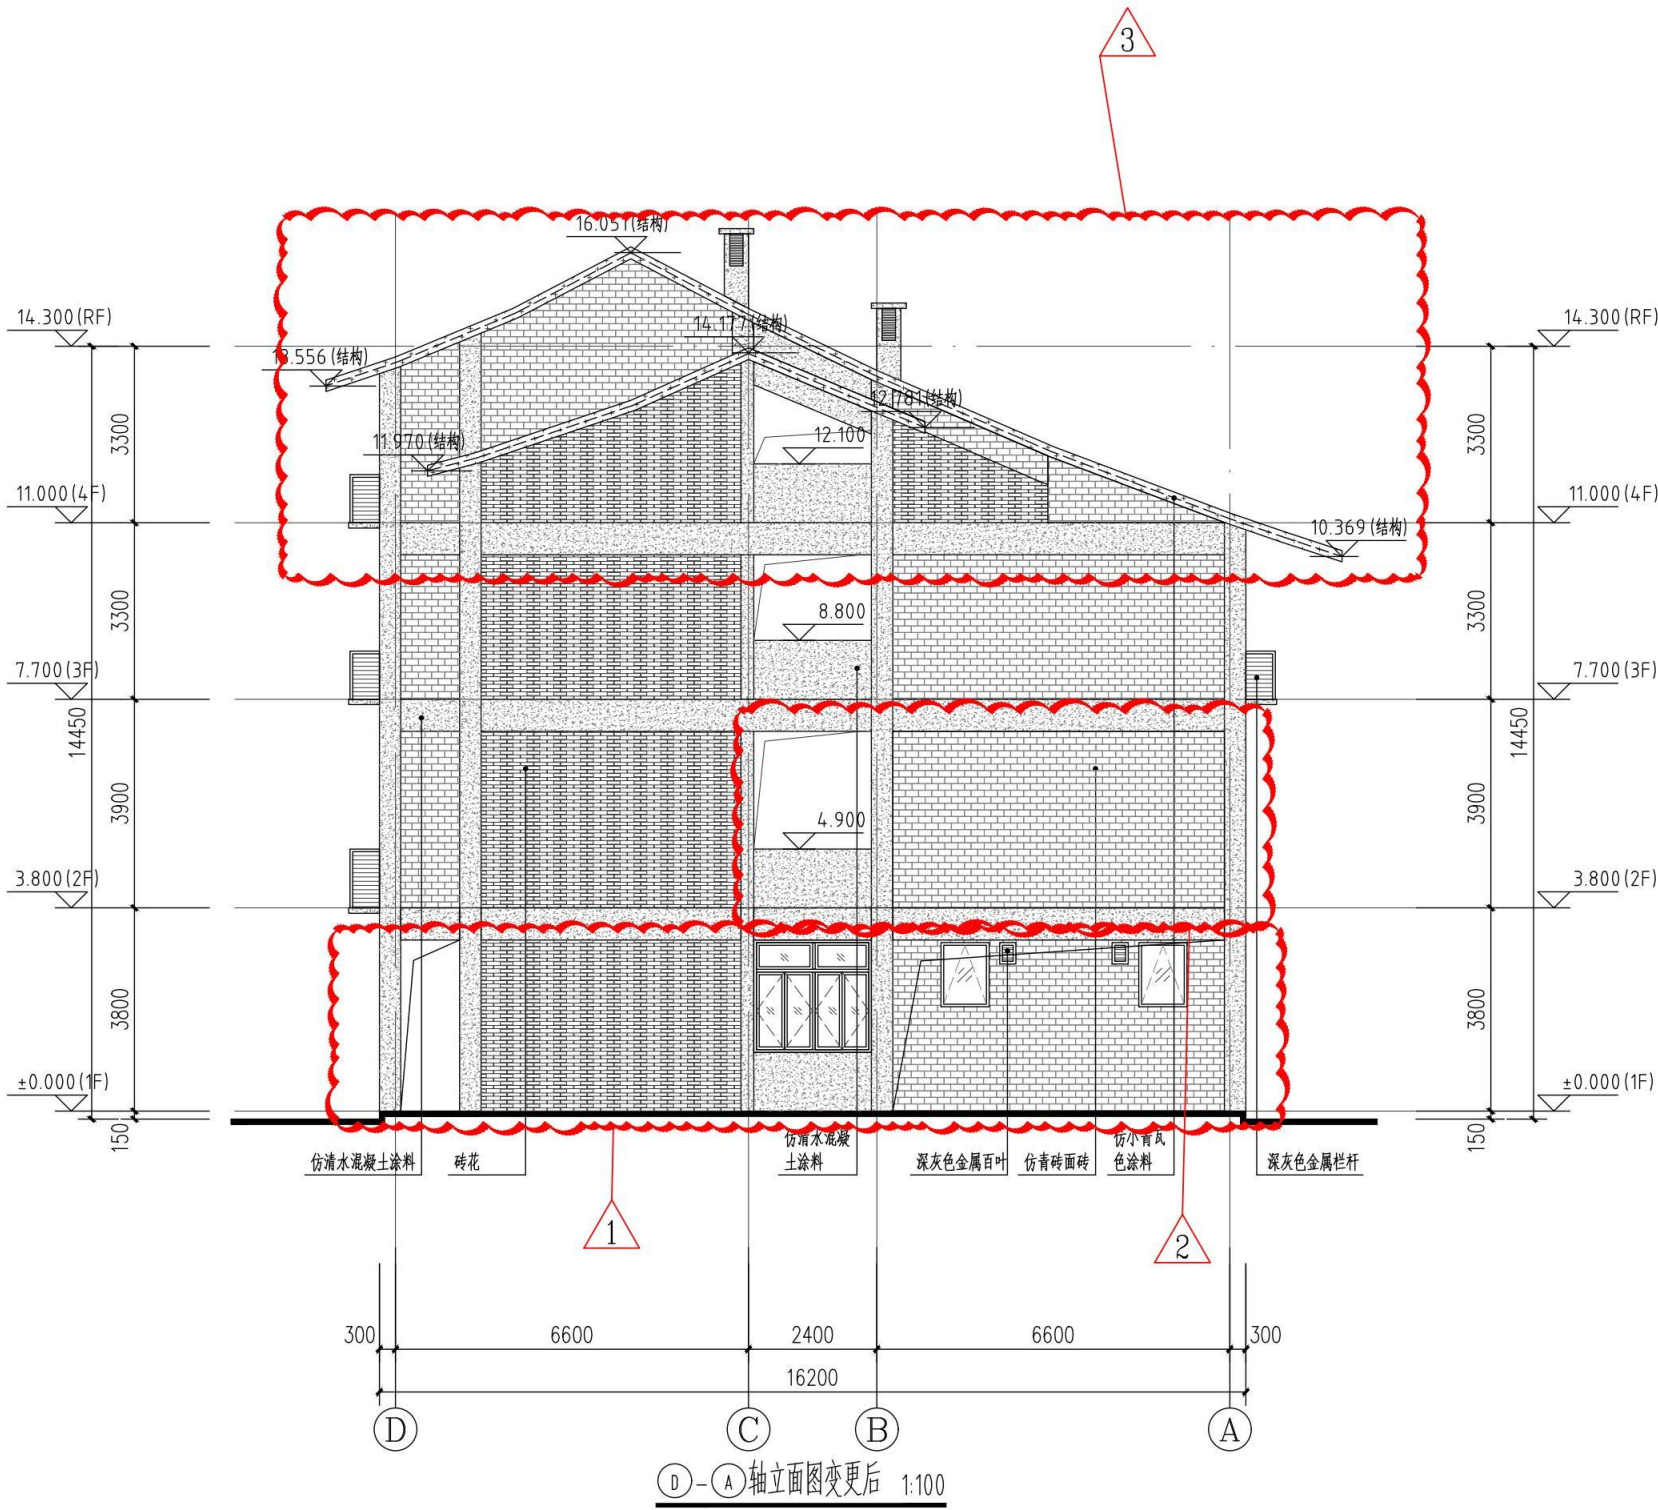

福建清华建筑设计院有限公司



FUJIAN QINGHUA
ARCHITECTURE DESIGN INSTITUTE Co., Ltd

备注:
NOTES

施工图审查单位:
CONSTRUCTION DRAWING CENSORED BY

三明市建筑工程施工图设计文件审查中心

施工图审查合格书编号:
CONSTRUCTION DRAWING CERTIFICATE NO.

图纸专用章:
DRAWING STAMP

注册建筑师执业章:
REGISTERED ARCHITECT'S STAMP

注册结构师执业章:
REGISTERED ENGINEER'S STAMP

版别 VERSION 序号 NO. 日期 DATE

建设单位
CLIENT

工程名称
PROJECT NAME

项目工程
ITEM NAME

图名
SHEET NAME
③-④轴立面图变更后

设计号
PROJECT NO.
审定
AUTHORIZED BY
项目负责人
PROJECT CHIEF MANAGER
专业负责人
DISCIPLINE RESPONSIBLE BY
审核
VERIFIED BY
校对
CHECKED BY
设计
DESIGNED BY
制图
DRAWN BY
比例
SCALE
图别
PHASE
日期
DATE
图号
NO.

注:本图纸未经施工图审查和政府各职能部门审查不得用于施工。

专业	实名	签名	日期	专业	实名	签名	日期
建筑				电气			
结构				暖通			
给排水							

福建清华建筑设计院有限公司

FUJIAN QINGHUA
ARCHITECTURE DESIGN INSTITUTE Co., Ltd

备注:
NOTES

施工图审查单位：
CONSTRUCTION DRAWING CENSORED BY

三明市建筑工程施工图设计文件审查中心

施工图审查合格书编号：
CONSTRUCTION DRAWING CERTIFICATE NO.

图纸专用章:
DRAWING STAMP

注册建筑师执业章:
REGISTERED ARCHITECT'S STAMP

注册结构师执业章:
REGISTERED ENGINEER'S STAMP

版别 VERSION	序号 NO.	日期 DATE

建设单位
CLIENT

工程名称	PROJECT NAME
------	--------------

项目工程
ITEM NAME

图 名

SHEET NAME

①—A 轴立面图变更前

设计号
PROJECT NO.

审 定
AUTHORIZED BY
项目各事人

项目负责人
PROJECT CHIEF MANAGER

专业负责人	
DISCIPLINE RESPONSIBLE BY	
审 核	

校 对

CHECKED BY
设计
DESIGNED BY

DESIGNED BY
制 图
DRAWN BY


比 例 SCALE	
--------------	--

日期	
DATE	

图 别	
PHASE	

图 号	
NO.	

注：本图纸未经施工图审查和政府各职能部门审查不得用于施工。

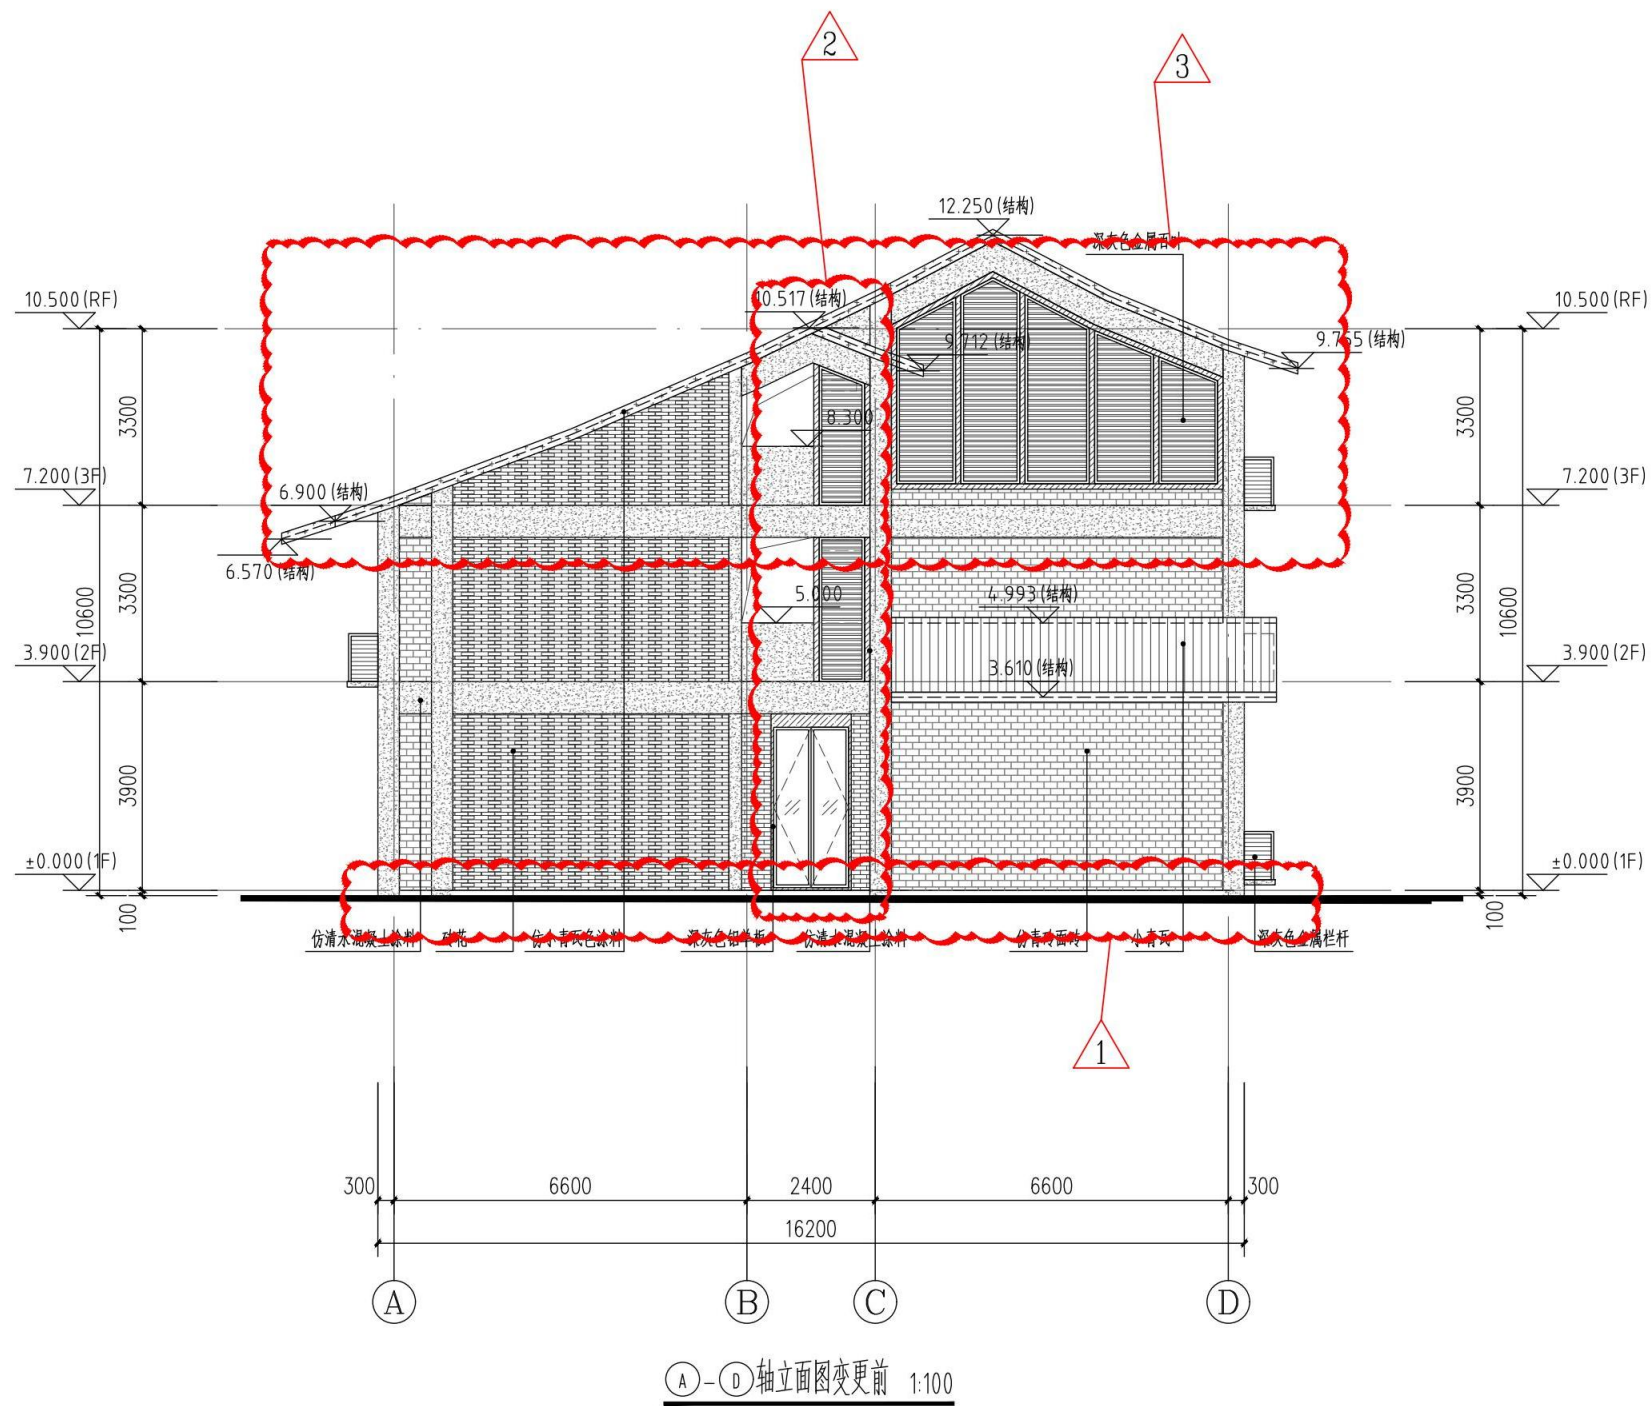


日期	
姓名	
姓名	
专业	电气
日期	
姓名	
姓名	
专业	建筑
专业	结构
专业	给排水

A-D轴立面变更

变更内容:

- 1、增设架空层;
- 2、删除部分百叶窗;
- 3、根据屋顶平面图调整立面相应修改。

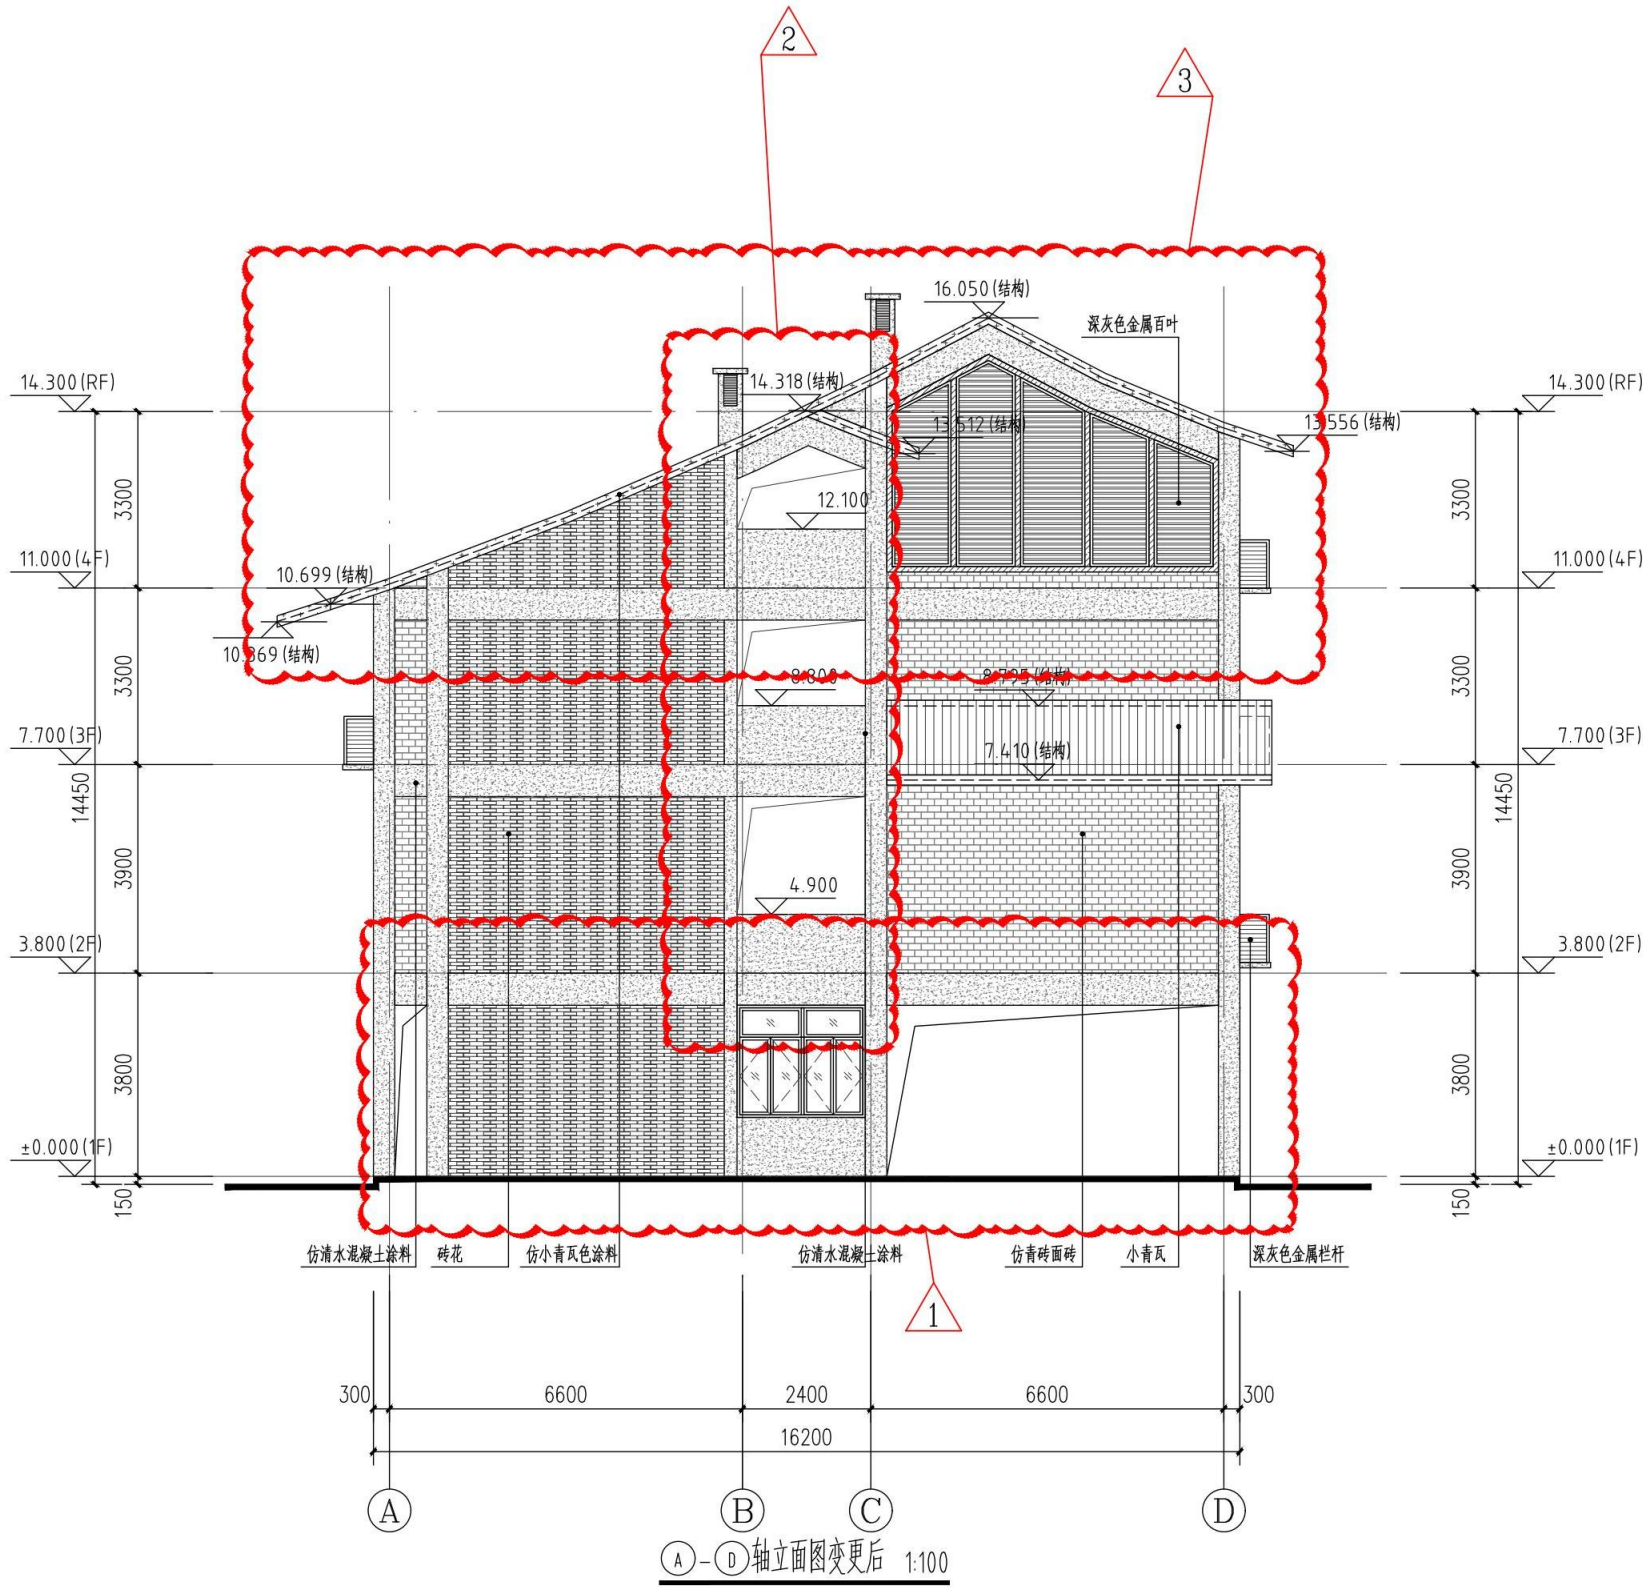

福建清华建筑设计院有限公司



FUJIAN QINGHUA
ARCHITECTURE DESIGN INSTITUTE Co., Ltd

备注:

NOTES

施工图审查单位:
CONSTRUCTION DRAWING CENSORED BY

三明市建筑工程施工图设计文件审查中心

施工图审查合格书编号:
CONSTRUCTION DRAWING CERTIFICATE NO.

图纸专用章:
DRAWING STAMP

注册建筑师执业章:
REGISTERED ARCHITECT'S STAMP

注册结构师执业章:
REGISTERED ENGINEER'S STAMP

版别 VERSION	序号 NO.	日期 DATE
------------	--------	---------

建设单位
CLIENT

工程名称
PROJECT NAME

项目工程
ITEM NAME

图名
SHEET NAME

①-④轴立面图变更后

设计号
PROJECT NO.

审定
AUTHORIZED BY

项目负责人
PROJECT CHIEF MANAGER

专业负责人
DISCIPLINE RESPONSIBLE BY

审核
VERIFIED BY

校对
CHECKED BY

设计
DESIGNED BY

制图
DRAWN BY

比例
SCALE

日期
DATE

图别
PHASE

图号
NO.


注: 本图纸未经施工图审查和政府各职能部门审查不得用于施工。

日期	
姓名	
姓名	
专业	电气
日期	
姓名	
姓名	
专业	建筑
专业	结构
专业	给排水

1-1剖面变更

变更内容:

- 1、增设架空层;
- 2、根据屋顶平面图调整立面相应修改。

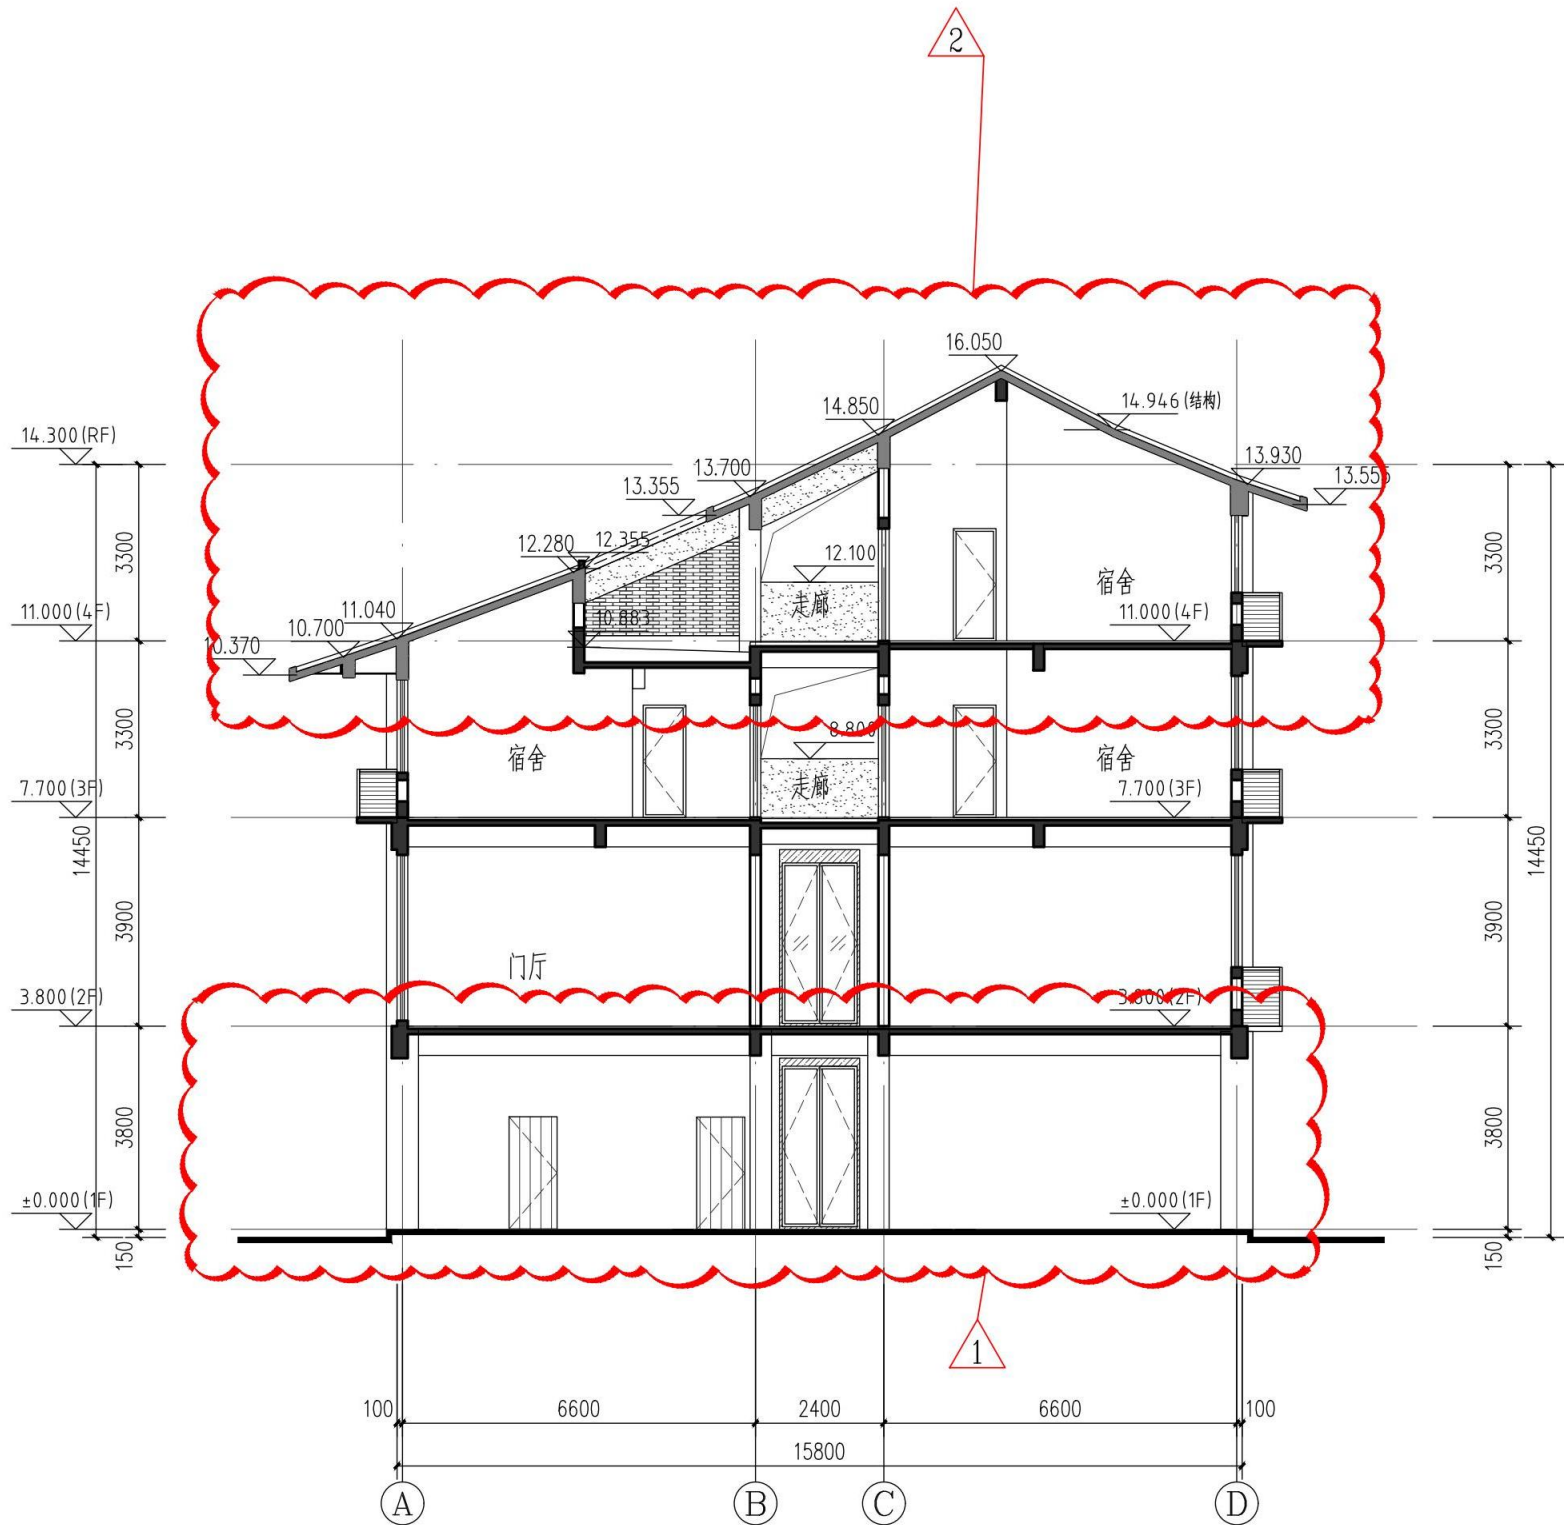

1-1剖面图变更后 1:100

福建清华建筑设计院有限公司



FUJIAN QINGHUA
ARCHITECTURE DESIGN INSTITUTE Co., Ltd

备注:
NOTES

施工图审查单位:
CONSTRUCTION DRAWING CENSORED BY

三明市建筑工程施工图设计文件审查中心

施工图审查合格书编号:
CONSTRUCTION DRAWING CERTIFICATE NO.

图纸专用章:
DRAWING STAMP

注册建筑师执业章:
REGISTERED ARCHITECT'S STAMP

注册结构师执业章:
REGISTERED ENGINEER'S STAMP

版别 VERSION	序号 NO.	日期 DATE
------------	--------	---------

建设单位
CLIENT

工程名称
PROJECT NAME

项目工程
ITEM NAME

图名
SHEET NAME

1-1剖面图变更后

设计号
PROJECT NO.

审定
AUTHORIZED BY

项目负责人
PROJECT CHIEF MANAGER

专业负责人
DISCIPLINE RESPONSIBLE BY

审核
VERIFIED BY

校对
CHECKED BY

设计
DESIGNED BY

制图
DRAWN BY

比例
SCALE

日期
DATE

图别
PHASE

图号
NO.

日期
DATE

图号
NO.

注: 本图纸未经施工图审查和政府各职能部门审查不得用于施工。