

设计修改通知单


建设单位	沙县绿欧房地产开发有限公司	工程编号	2014-33 (20)	主送单位	
工程名称	金洲公寓	发文日期	2024. 10	抄送单位	
更改理由	1. 原设计图纸错、漏、碰、缺的更正; 2. 原构造设计的改进或完善; 3. 配合其它专业进行的修改; 4. 建设单位要求修改; 5. 施工条件变化造成的修改; 6. 施工质量问题补强或修改; 7. (其它)				

一、新增一栋配电房, 建筑面积增加160m2, 占地建筑面积增加160m2, 计容建筑面积增加160m2.

二、1#楼一层店面 1-aH~1-bA 轴交 1-b1~1-b3 轴间局部店面取消, 建筑面积减少 332.17 m2, 占地建筑面积减少332.17 m2. 计容建筑面积减少332.17m2.

三、总平停车位布置修改, 小区北侧停车位改为绿化, 小区西侧及南侧沿街商铺装硬地改为停车位, 总停车位保持不变。

西侧1#楼沿街商业部分硬地改绿化, 幼儿园周边北侧及西侧绿化改为活动场地, 小区总体绿化面积保持不变。

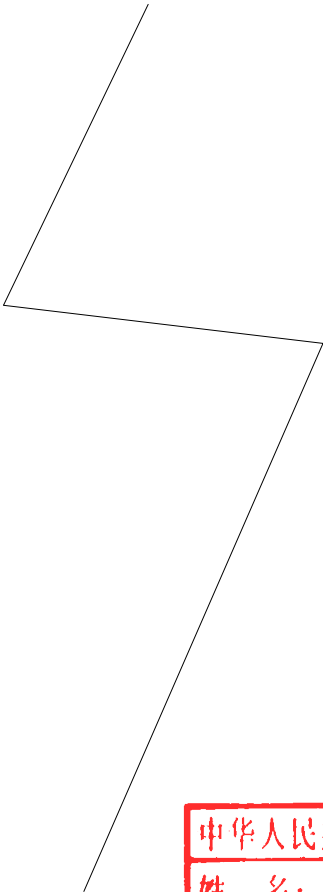

福建省工程勘察设计图纸专用章
福建省机电沿海建筑设计研究院有限公司
资质 范围: 建筑工程
等级: 甲级 证号: A135003677
有效期至: 2025年03月02日


中华人民共和国一级注册建筑师
姓 名: 彭晓辉
注册号: 3500367-003
有效期: 至2024年11月15日

项目负责人	设计	审 核	制图	福建省机电沿海建筑设计研究院有限公司			
专业负责人	设计	校 对	制图				
会 总 图		结 构	电 气	图 名	总平布局修改通知单1	专 业	建筑
签 建 筑		给排水	暖 通			图 号	01


注: 1. 需要图审(含重大变更)的图纸不得采用本通知单。 2. 凡可能影响其它专业的修改, 必须通知相关专业, 且出图前须经过图纸会签。

[illegible]

修改记录:

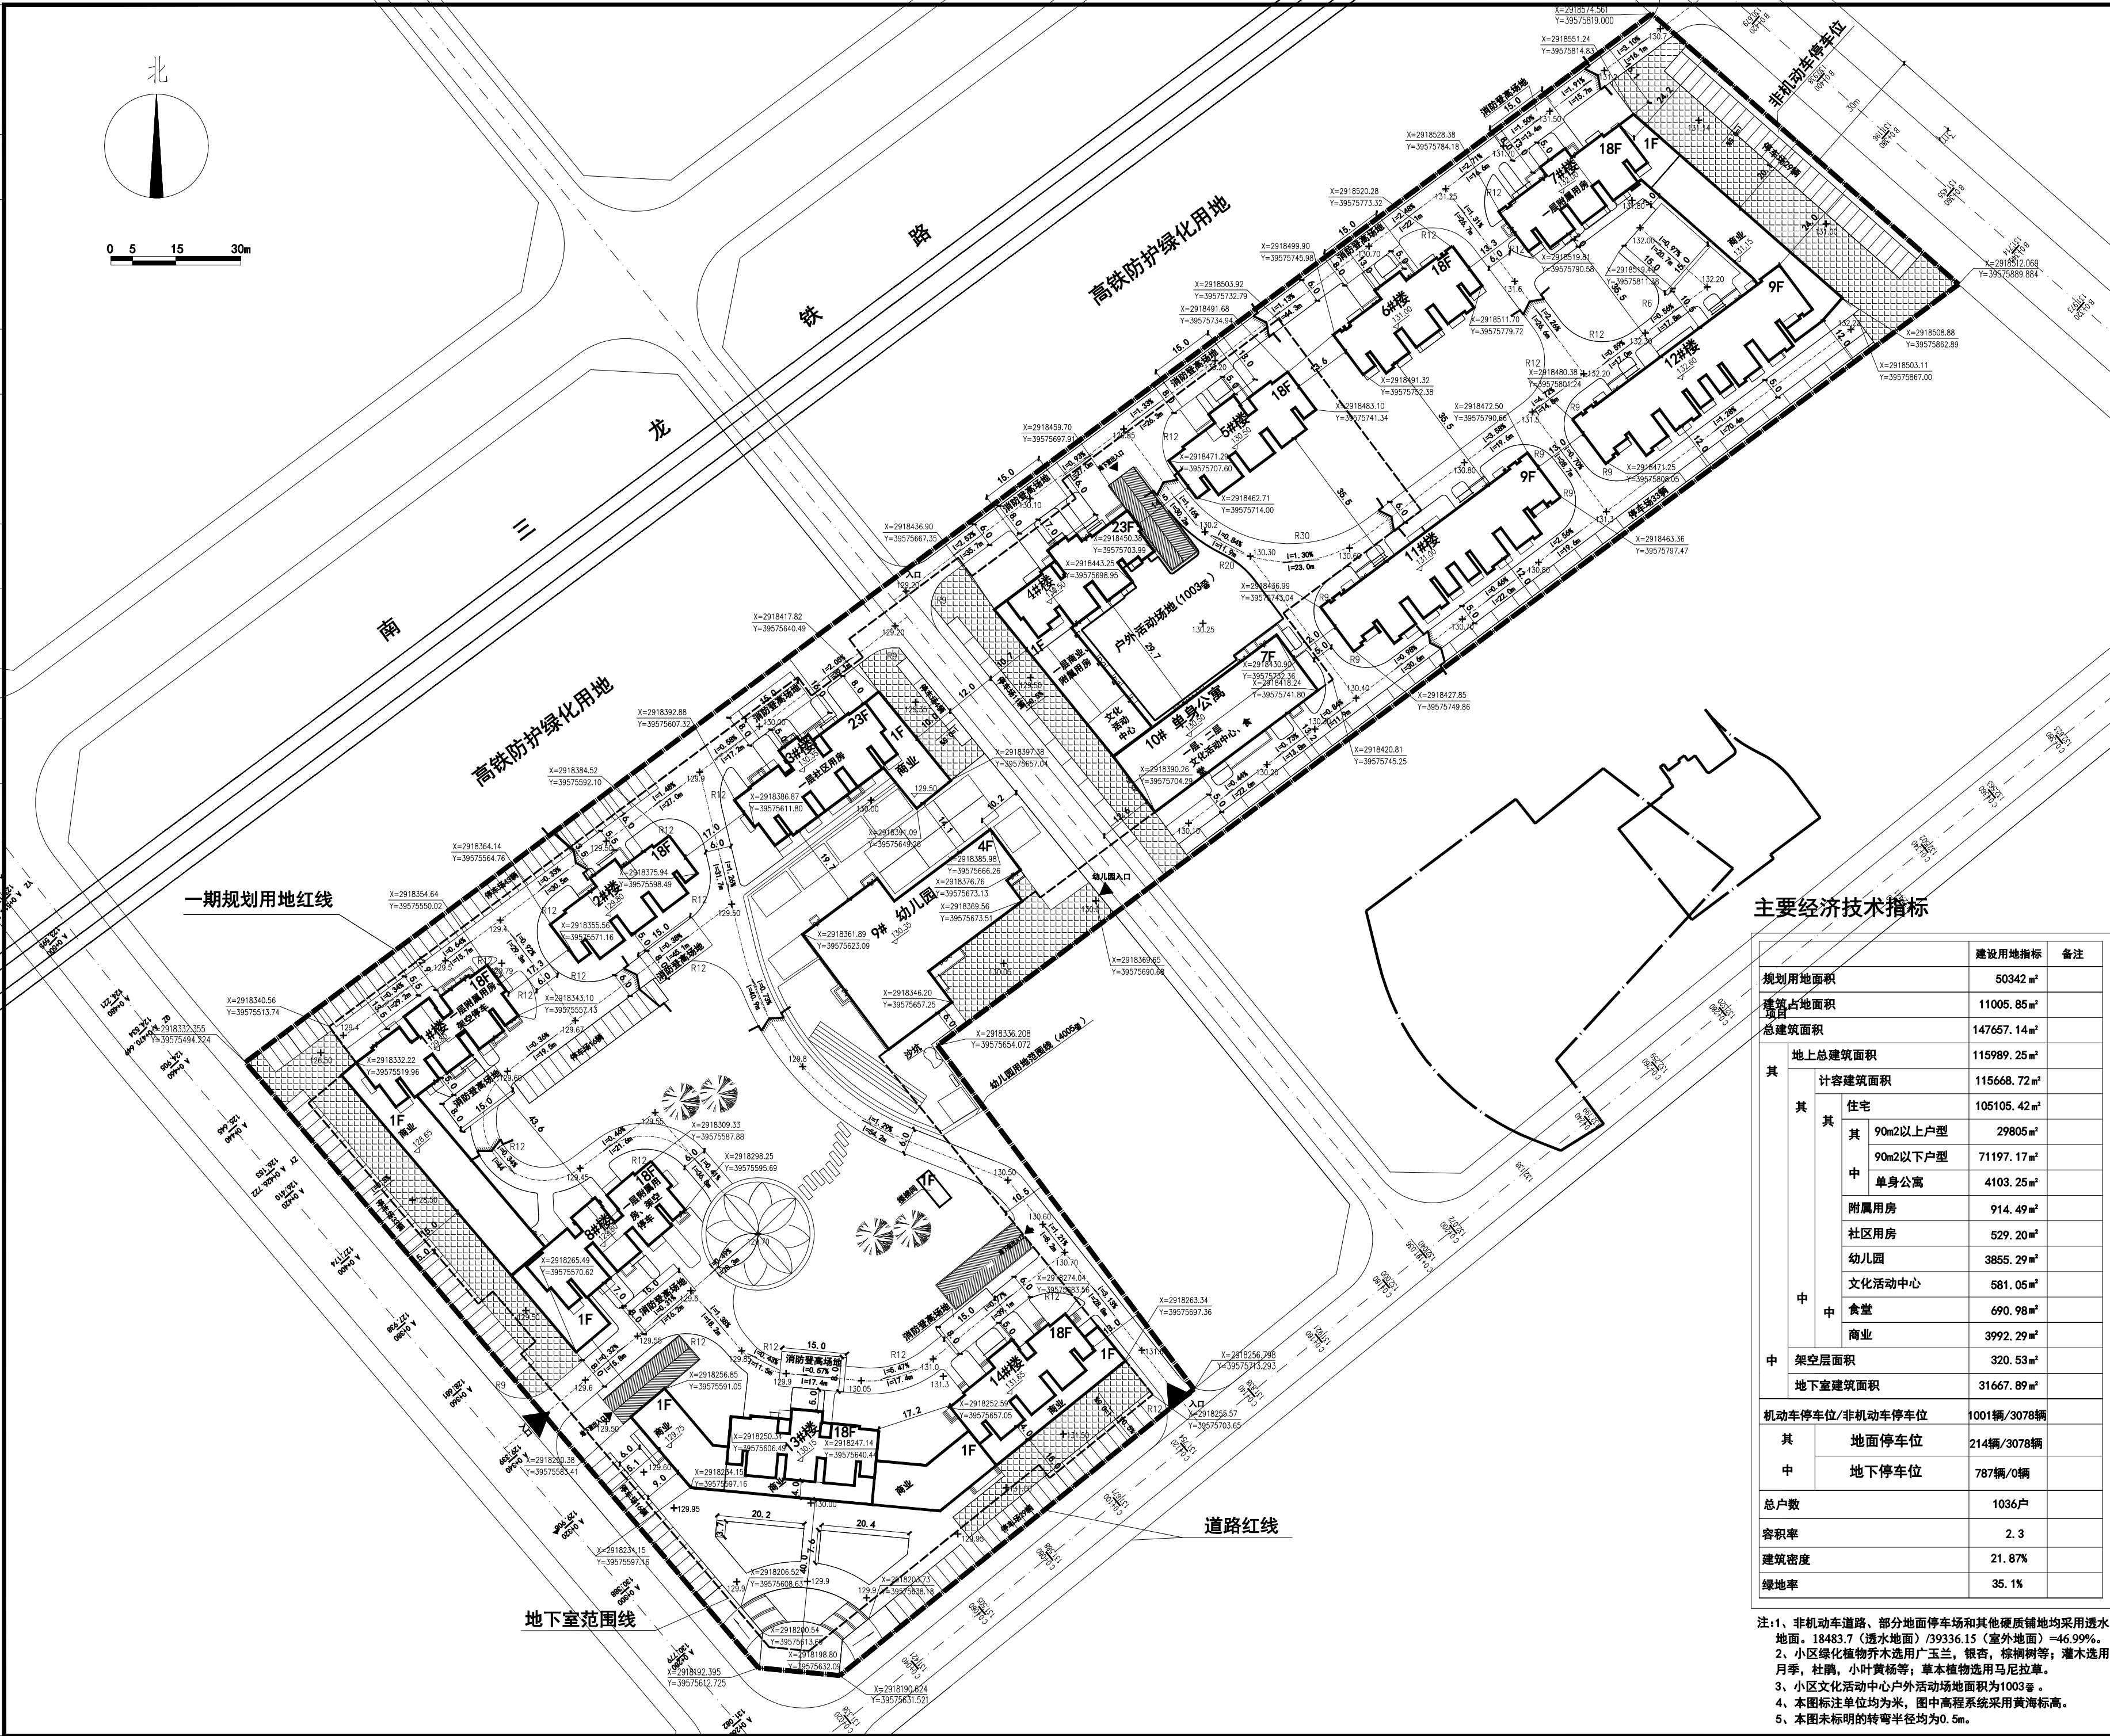


福建省机电建沿海 建筑设计研究院有限公司 证书编号: A135003677 A235003674 资质范围: 建筑工程甲级 机械行业甲级 电子工程甲级 轻钢结构甲级 工程咨询甲级 市政工程乙级 城乡规划丙级 变电工程丙级			
施工图审查批准单位:			
施工图审查批准证书号:			
图纸专用章 福建省工程勘察设计院图纸专用章 福建省机电建沿海建筑设计研究院有限公司 范围: 建筑工程 资质等级: 甲级 证号: A135003677 有效期至: 2025年03月02日			
注册执业章 中华人民共和国一级注册建筑师 姓名: 彭晓辉 注册号: 3500367-003 有效期至: 至2026年10月10日			
注册执业章			
建设单位: 沙县绿欧房地产 开发有限公司			
工程名称: 金洲公寓			
职 责	姓 名	签 名	
审 定			
项目负责人	彭晓辉		
项目经理	彭晓辉		
专业负责人	彭晓辉		
审 核	张玉林		
校 对	林伟		
设 计	袁泉		
图名: 总平面布置图(变更前)			
工程编号	2014-33	版 别	1.00
图 别	总施	图 号	01
日 期	2014年12月23日		

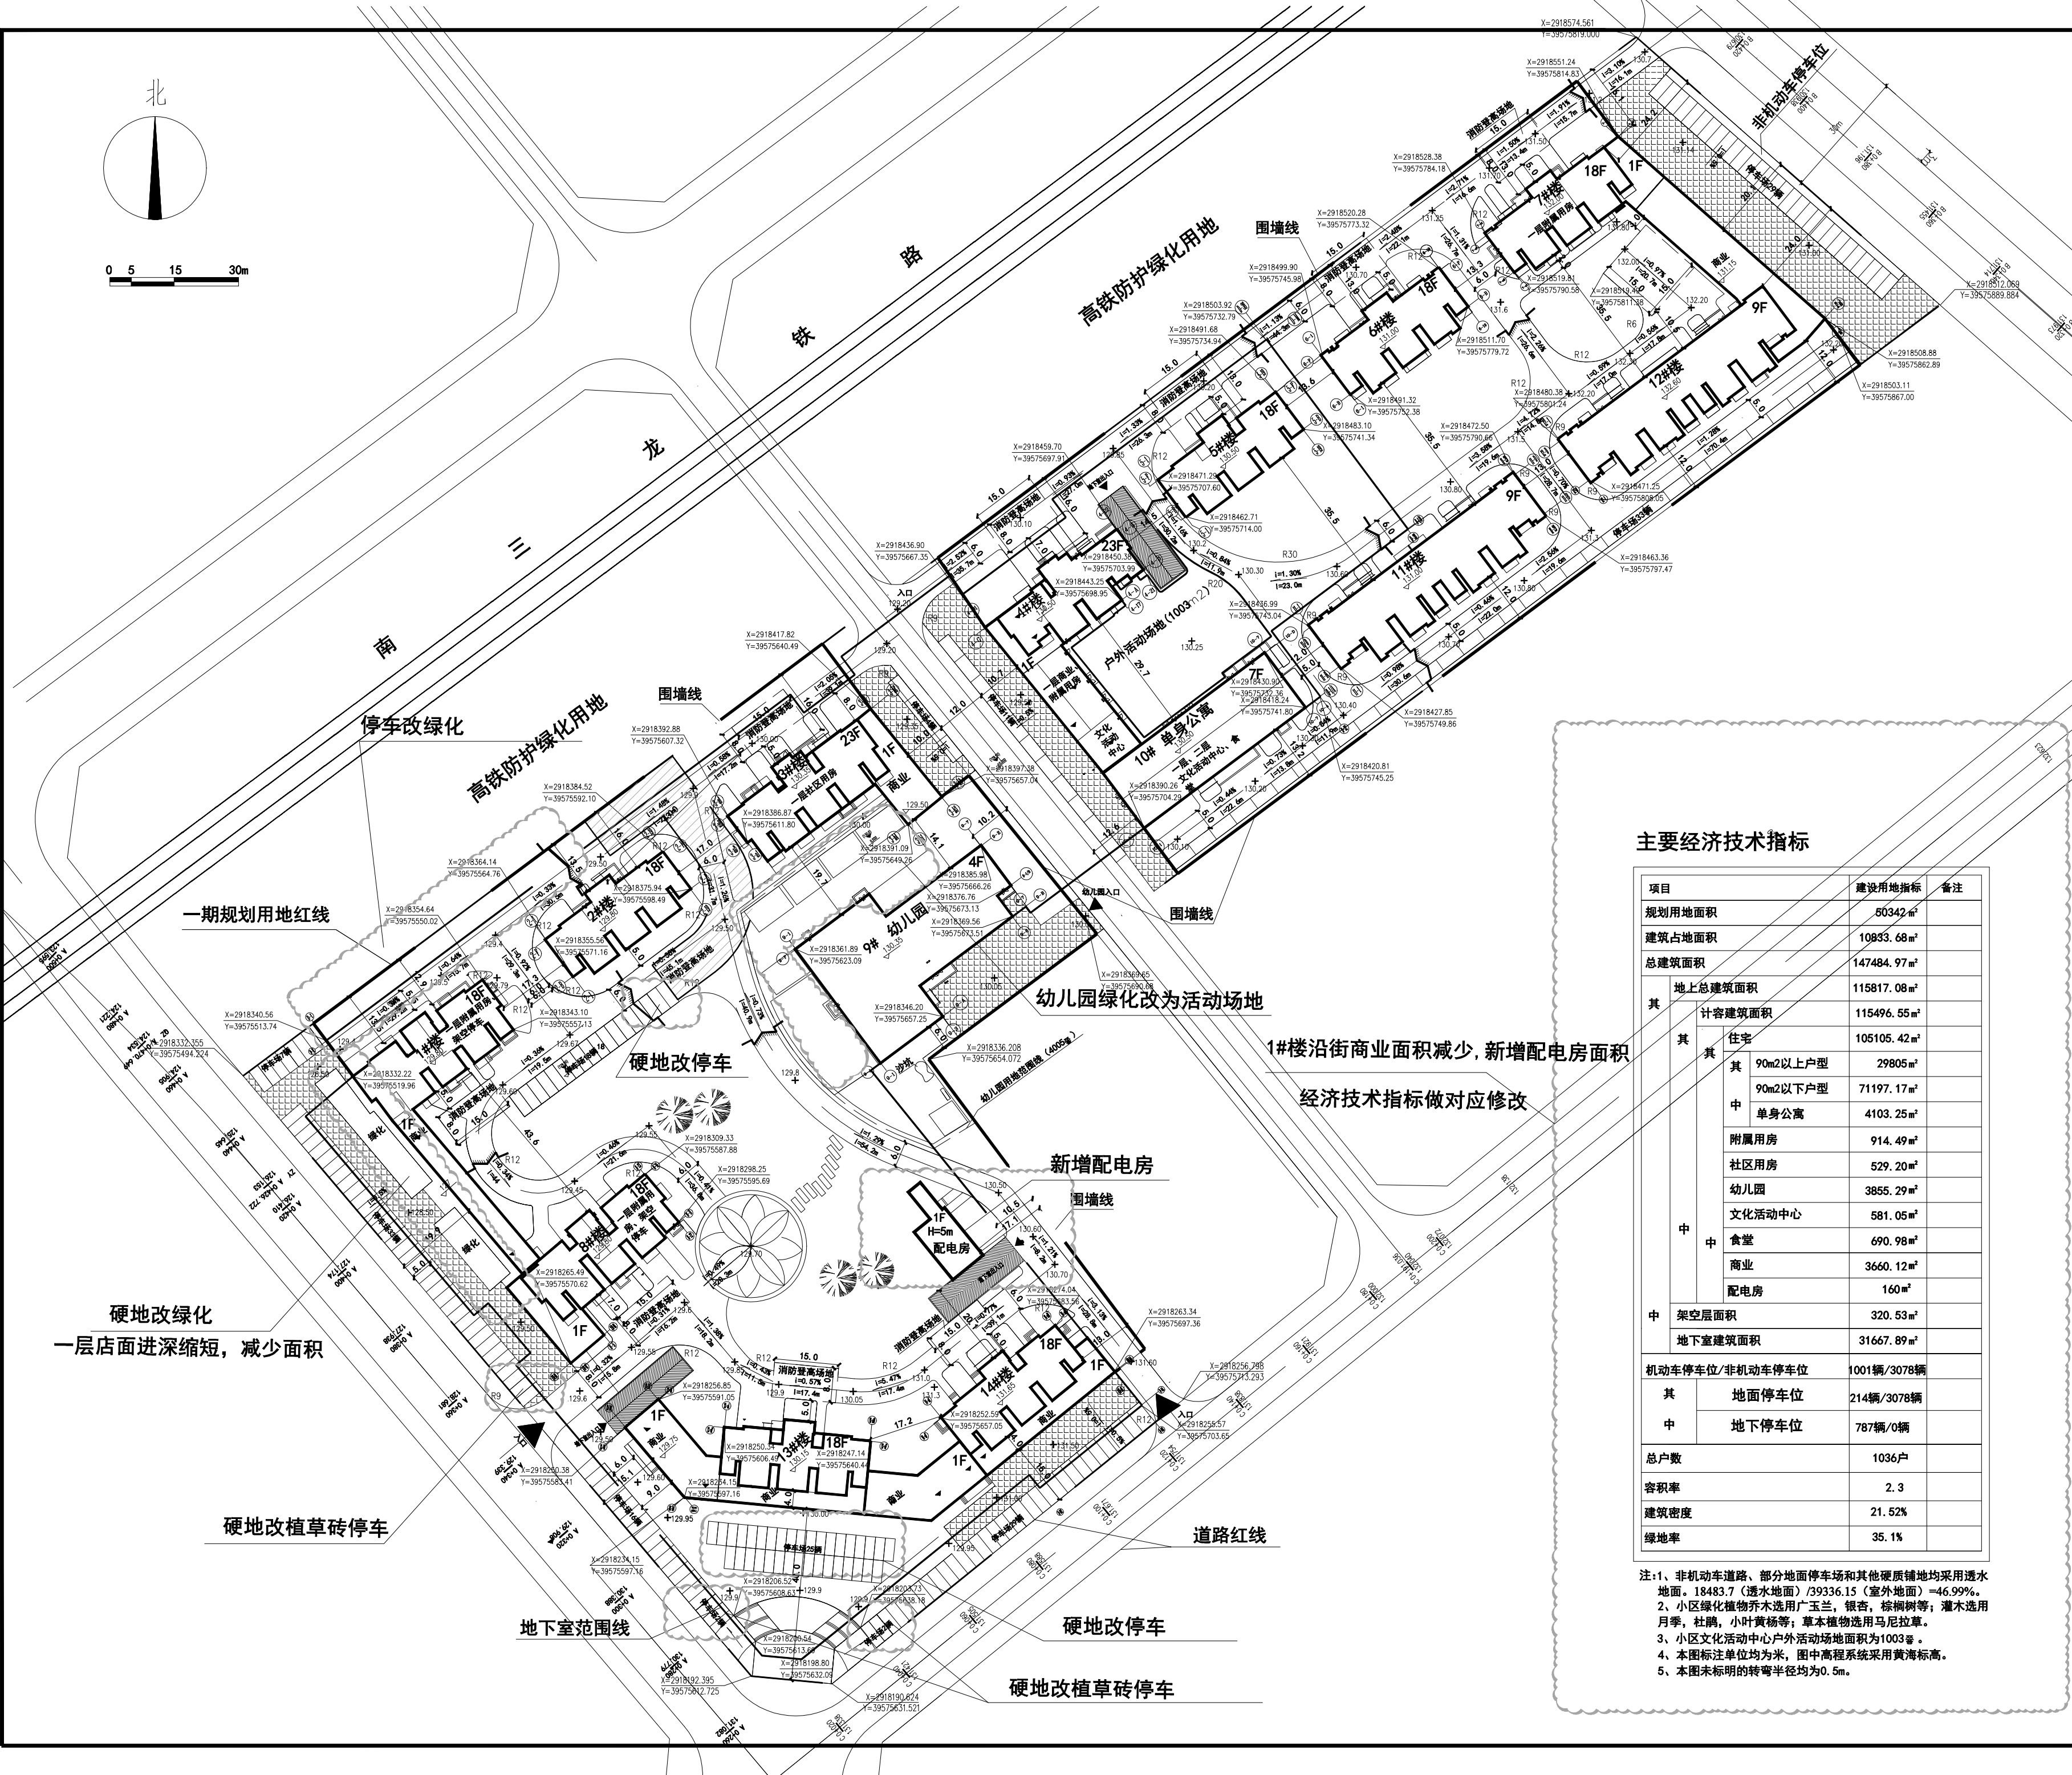

工程编号	2014-33	版 别	1.00
图 别	总施	图 号	01
日 期	2024年10月24日		

注:1、非机动车道路、部分地面停车场和其他硬质铺地均采用透水地面。18483.7(透水地面)/293636.15(室外地面)=46.99%。
2、小区绿化选乔木选用广玉兰,银杏,棕榈树等;灌木选用月季,杜鹃,小叶黄杨等;草本植物选用马尼拉草。
3、小区文化活动中中心户外活动场地面积为1003㎡。
4、本图标注单位均为米,图中高程系统采用黄海标高。
5、本图标明的转弯半径均为0.5m。

修改记录:

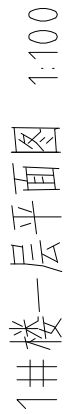

说明:

- 1、进道及折回层面采用防滑卷杆，台阶处设防滑台0/A4，坡道做法参10J930
- 2、进道及折回10J930 2/J25。
- 3、上翻靠柱安装，不侧闪，图中未标注时均取100。外墙窗户单位为200，卫生间内墙为100。
3. 本层共有排烟风3个，又双器共38(A型)共MF /ABC3具具体量详见平面图

4、地面有地漏或出水口的楼面均做0.5%坡度按向地漏或出水口。

地漏位置详水施

5. 本层101UPVC雨水管竖井有20根



其中：屋面排水面积为1055.69平方米，建筑面积为055.69平方米

其中：架空面积366.62平方米，住宅面积为33.96平方米，爬立面面积748.47平方米，裙用房面积86.74平方米。

7. 凡需用墙面及柱面涂料者：

7.1 凡需用墙面及柱面涂料者用传统纸浆火胶粉拌灰甲乙类物品。

图例	说明
==	200厚砌体 (具体材料详见说明)
==	100厚现浇空心砌块
==	住宅防隔墙 (用户自理, 二次装修砌块不得出梁上)
	灭火器 消火栓
	空调立管 (排水处)
---	过水孔100×100 (宽), 孔洞同楼面。
。	ø110U PVC雨水管
	雨水管不能水落真
。	坡漏 (做法详水施)。

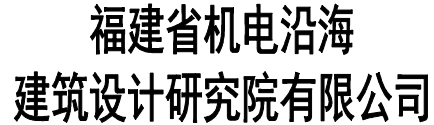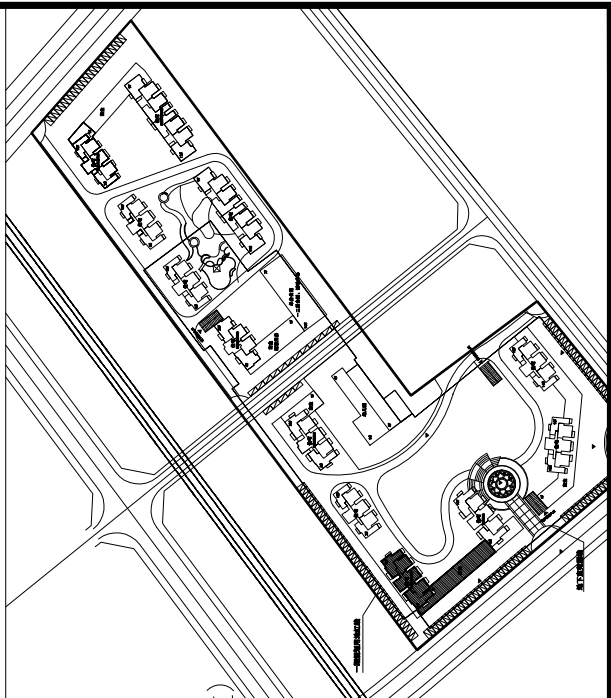

证书编号: A135003677 A235003674

资质范围: 建筑工程甲级 机械行业甲级
电子工程甲级 轻钢结构甲级
工程咨询甲级 市政工程乙级
城乡规划丙级 变电工程丙级

施工图审查批准单位:

施工图审查批准书证号:

图纸专用章

福建省机电沿海建筑设计研究院有限公司
范围: 建筑工程
等级: 甲级 证号: A135003677
有效期至: 2025年03月02日

注册执业章

中华人民共和国一级注册建筑师
姓名： 彭晓辉
注册号： 3500367-003
有效期： 至2026年10月10日

注册执业章

建设单位:

沙县绿欧房地产开发有限公司

工程名称:

金洲公寓

职 责	姓 名	签 名
审 定		
项目负责人	彭晓辉	彭晓辉
项目经理	彭晓辉	彭晓辉
专业负责人	彭晓辉	彭晓辉
审 核	张玉林	张玉林
校 对	王建平	王建平
设 计	魏洪	魏洪


图名:

1#楼一层平面图(变更前)

工程编号	2014-33	版 别	1.00
------	---------	-----	------

图 别	建施	图 号	4-2
-----	----	-----	-----

日 期 2014年 11月 23 日

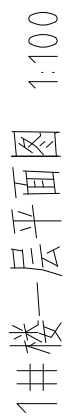



修改注明:
一、1#楼一层店面 1-aH~1-bA 轴交 1-b1~1-b3 轴间局部店面取消, 建筑面积减少 332.17 m²。

说明:


1. 本图及台面板层采用清水砼,台阶处浇筑1:0.30 台/0.4;坡面处浇筑1:0.30 坡/0.45,坡脚处手抹1:0.30 2/25。
2. 1/2圈管柱内嵌设 不锈钢门框,图中未标注的门框均为100 外墙及分户墙均为200,卫生间内墙为100。
3. 本图共有错台13个,尺寸共38个(型号墙/ABC3)具体位置详见平面。
4. 凡墙上有地漏或出水口的矮墙,均做0.5%的坡度指向地漏或出水口。
5. 本图(0.110UPVC)水管管径为200mm。
6. 凡剪力墙暗梁以柱梁为准。
7. 墙顶面厨房商业店面一律做防水,防水等级为Ⅱ类,其他部品。

图例	说明
==	200厚砌体(具体材料详见说明)
==	100厚现浇空心砌块
==	住宅内隔墙(用户自理,二次装修时不得随意拆除)
	灭火器 消火栓
—	空调立管(冷水流)
—	过水孔100×100(宽、高),孔距同楼面。
。	Ø110U PVC雨水管
	雨水管(接水落管)
◎	地漏(按设计水施)

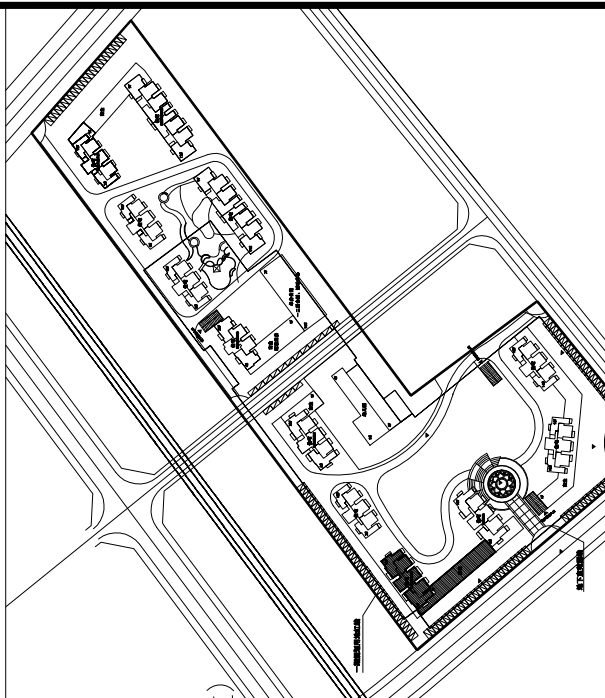


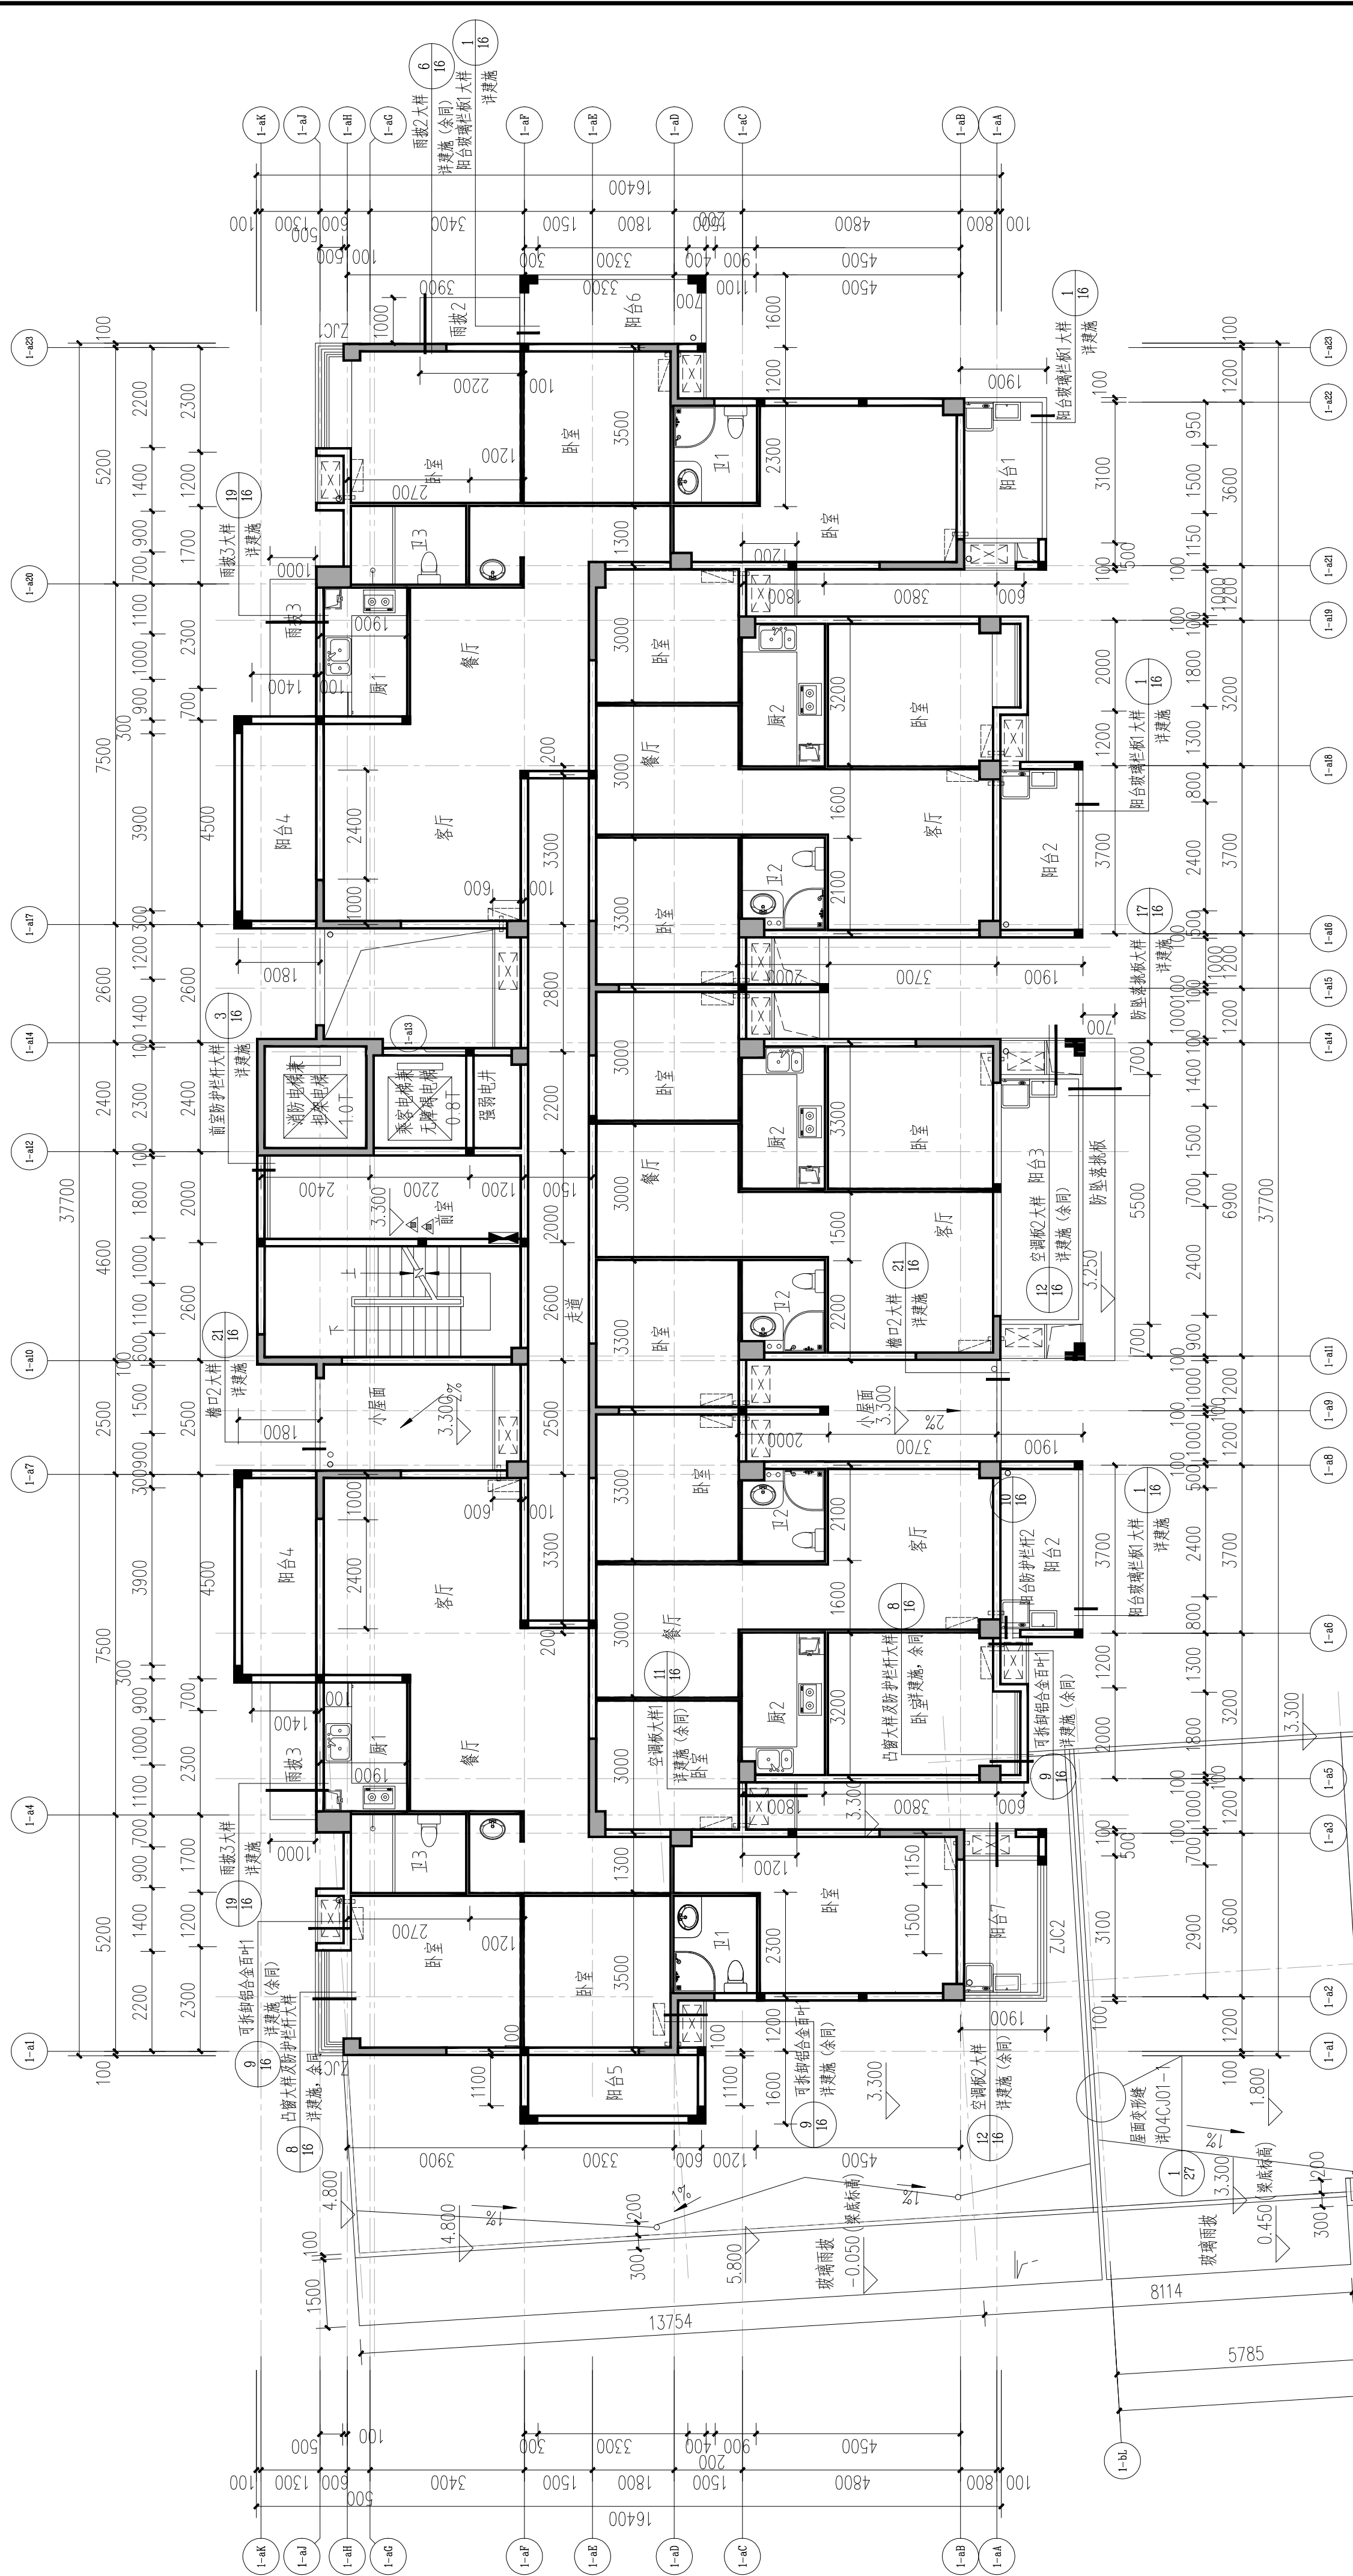[illegible]

1#楼二层平面图 1:100

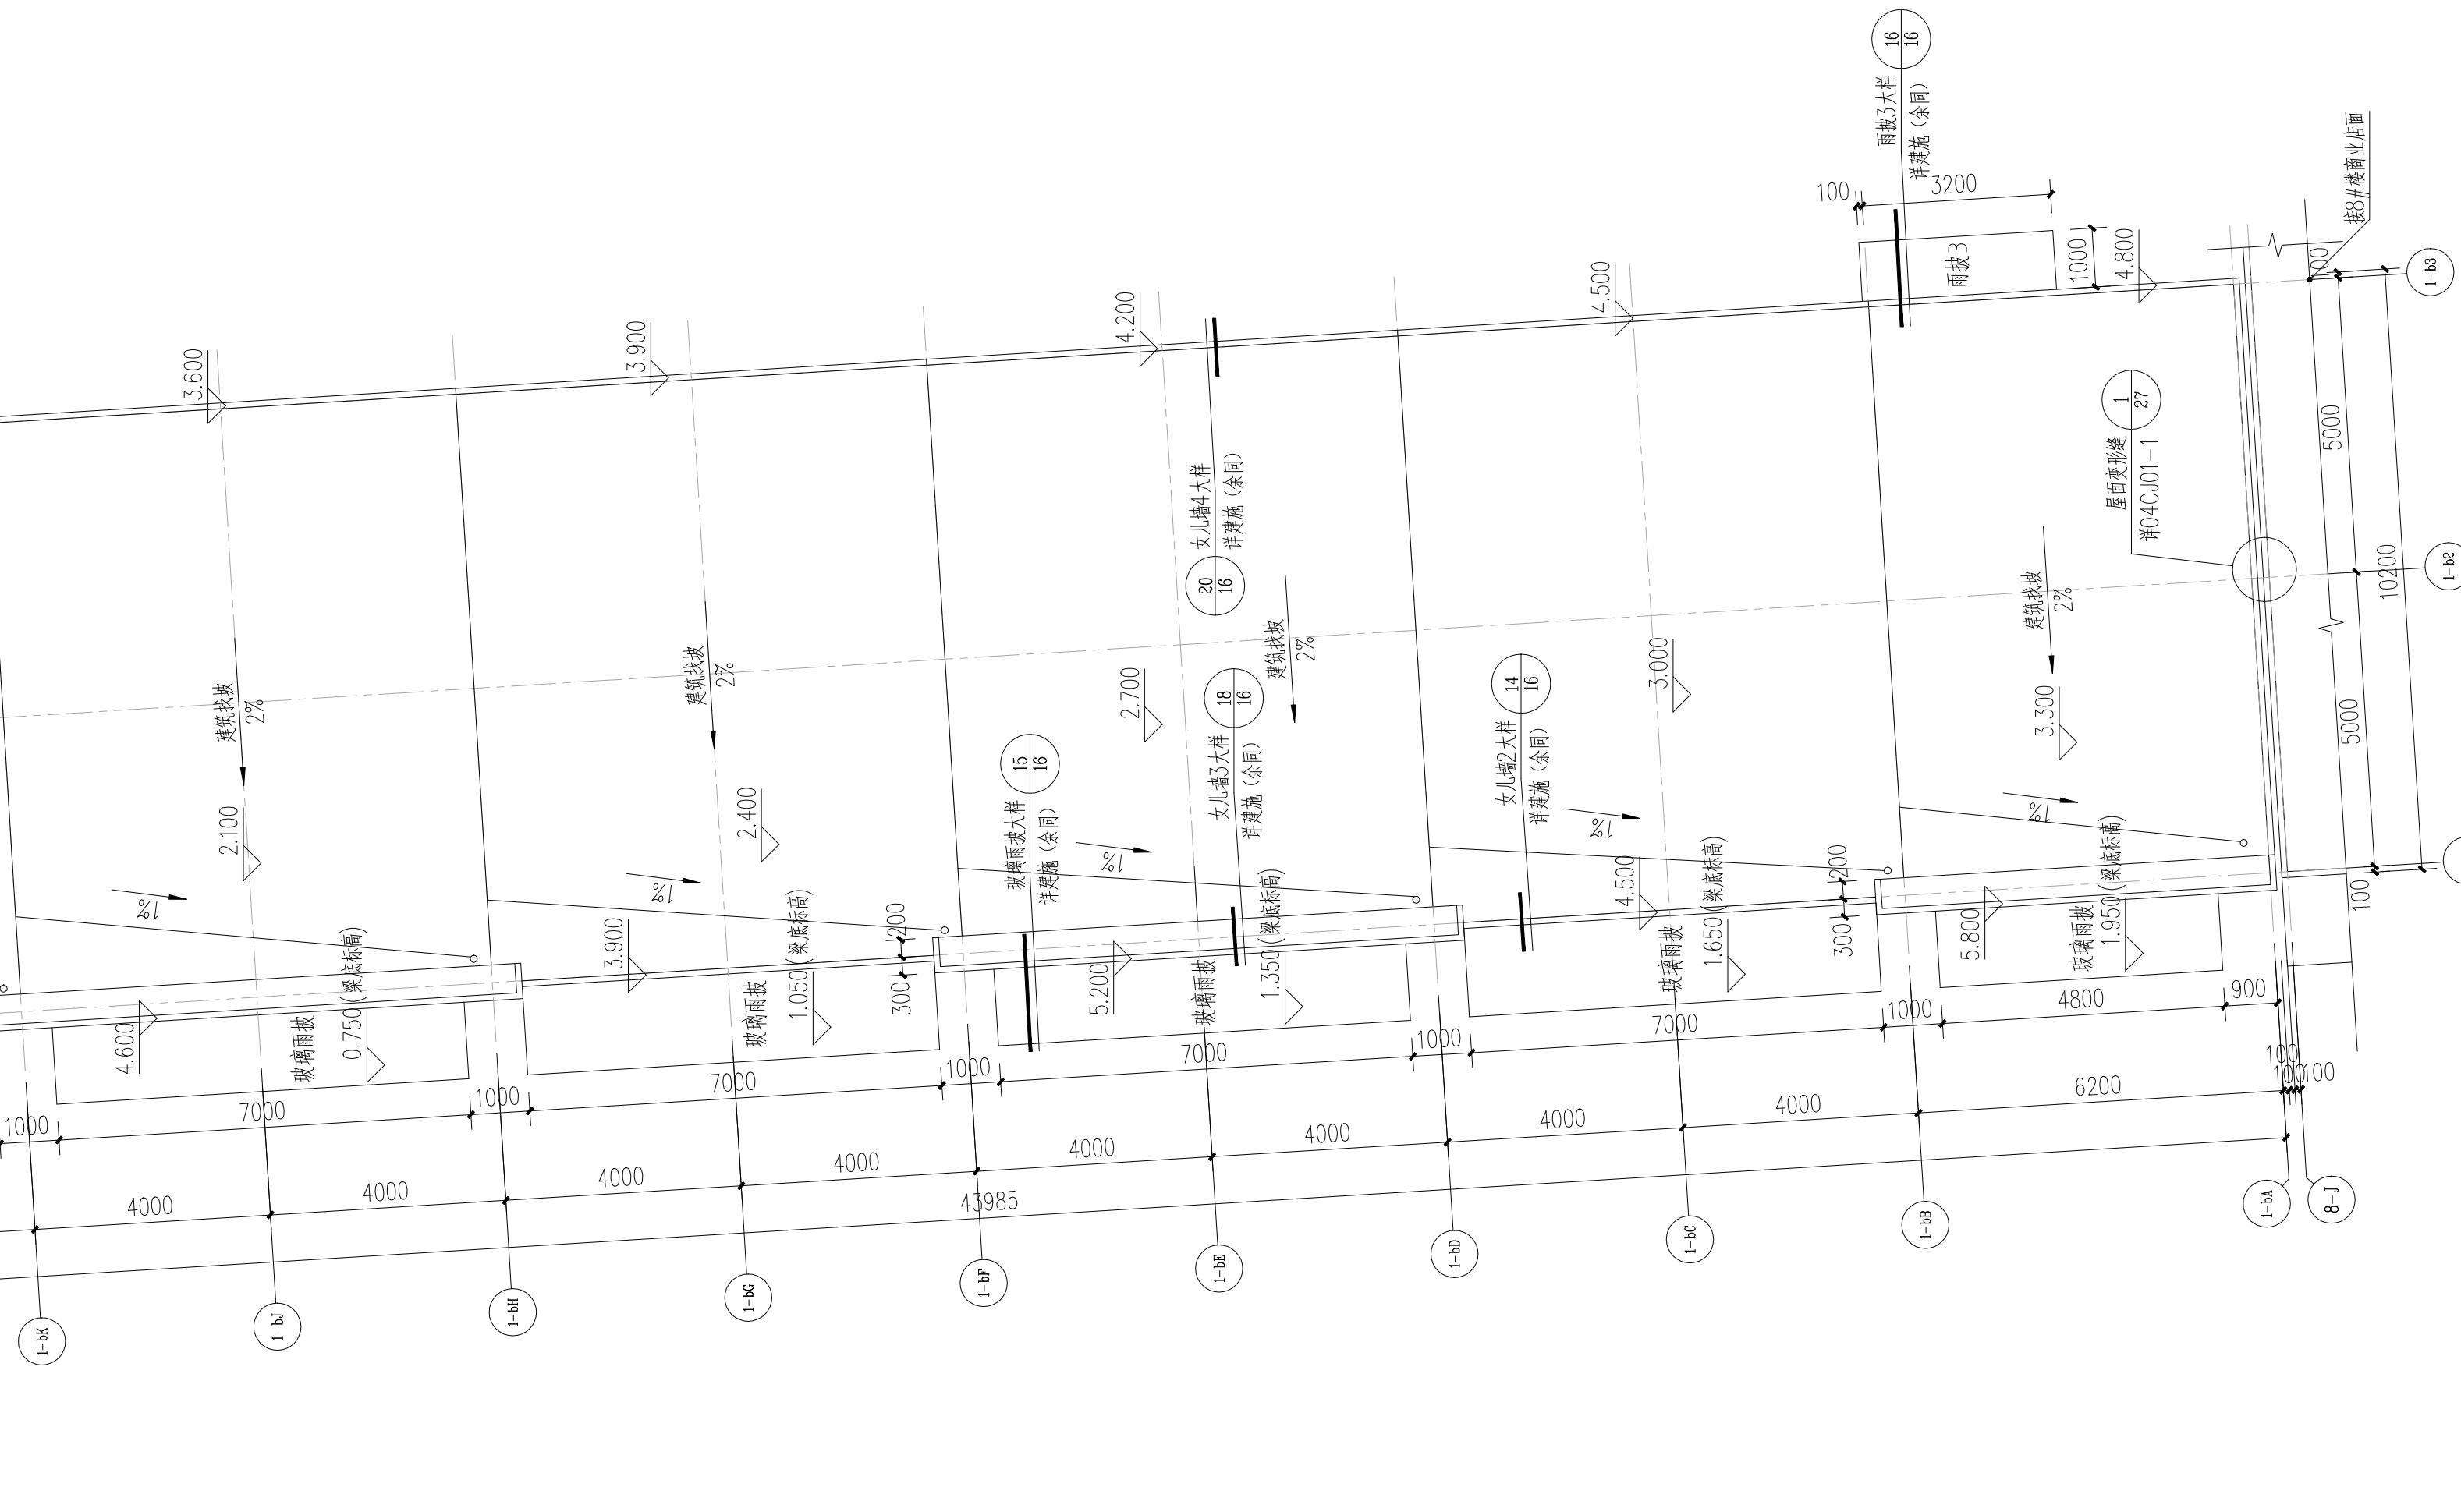

图例	说明	图例	说明
==	200厚砌体 (具体材料详见说明)	◦	地漏 (做法详大施)
==	100厚混凝土空心砌块	洗衣机	洗衣机 (由用户自理)
==	住宅内墙墙垛 (用户自理)	厨房, 卫生间排气管道 (成品)	
	灭火器 消火栓	燃气灶	燃气灶 (由用户自理)
	空调室外机	洗手盆	洗手盆 (由用户自理)
	空调室内机	座便器	座便器 (由用户自理)
	空调预留洞	淋浴盆	淋浴盆 (由用户自理)
≡	进水和100×100 (英寸) 孔底同楼面板		
◦	Ø110U PVC排水管	◦	空调立管 (详大施)

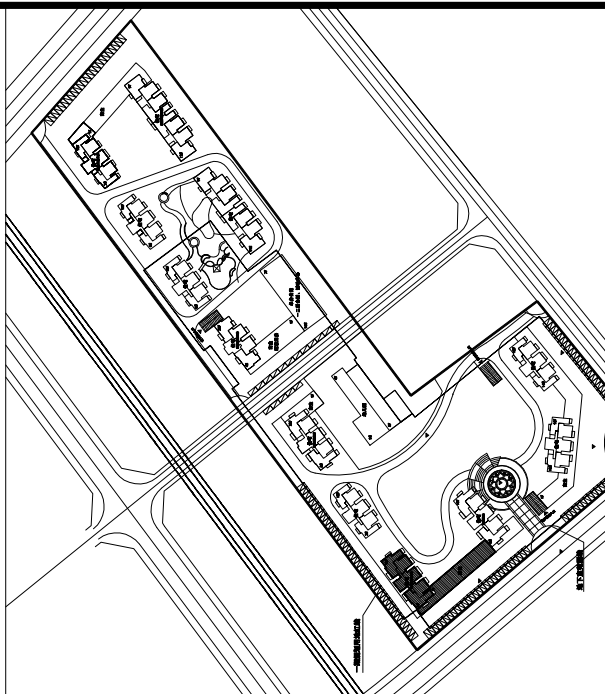

福建省机电沿海
建筑设计研究院有限公司


证书编号: A135003677 A235003674

资质范围: 建筑工程甲级 机械行业甲级
电子工程甲级 轻钢结构甲级
工程咨询甲级 市政工程乙级
城乡规划丙级 变电工程丙级

施工图审查批准单位:

施工图审查批准书证号:

图纸专用章

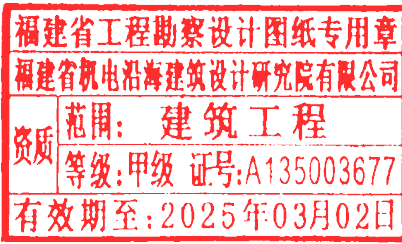

注册执业章

中华人民共和国一级注册建筑师

姓名：彭晓辉
注册号：3500367-003
有效期：至2026年10月10日

注册执业章

建设单位:

沙县绿欧房地产开发有限公司

工程名称:

金洲公寓

1#楼

职 责	姓 名	签 名
审 定		
项目负责人	彭晓辉	彭晓辉
项目经理	彭晓辉	彭晓辉
专业负责人	彭晓辉	彭晓辉
审 核	张玉林	张玉林
校 对	王建平	王建平
设 计	魏洪	魏洪


图名:

1#楼二层平面图 (变更前)

工程编号	2014-33	版 别	1.00
------	---------	-----	------


图 别	建施	图 号	5
-----	----	-----	---

日 期	2014年 11月 23 日
-----	----------------

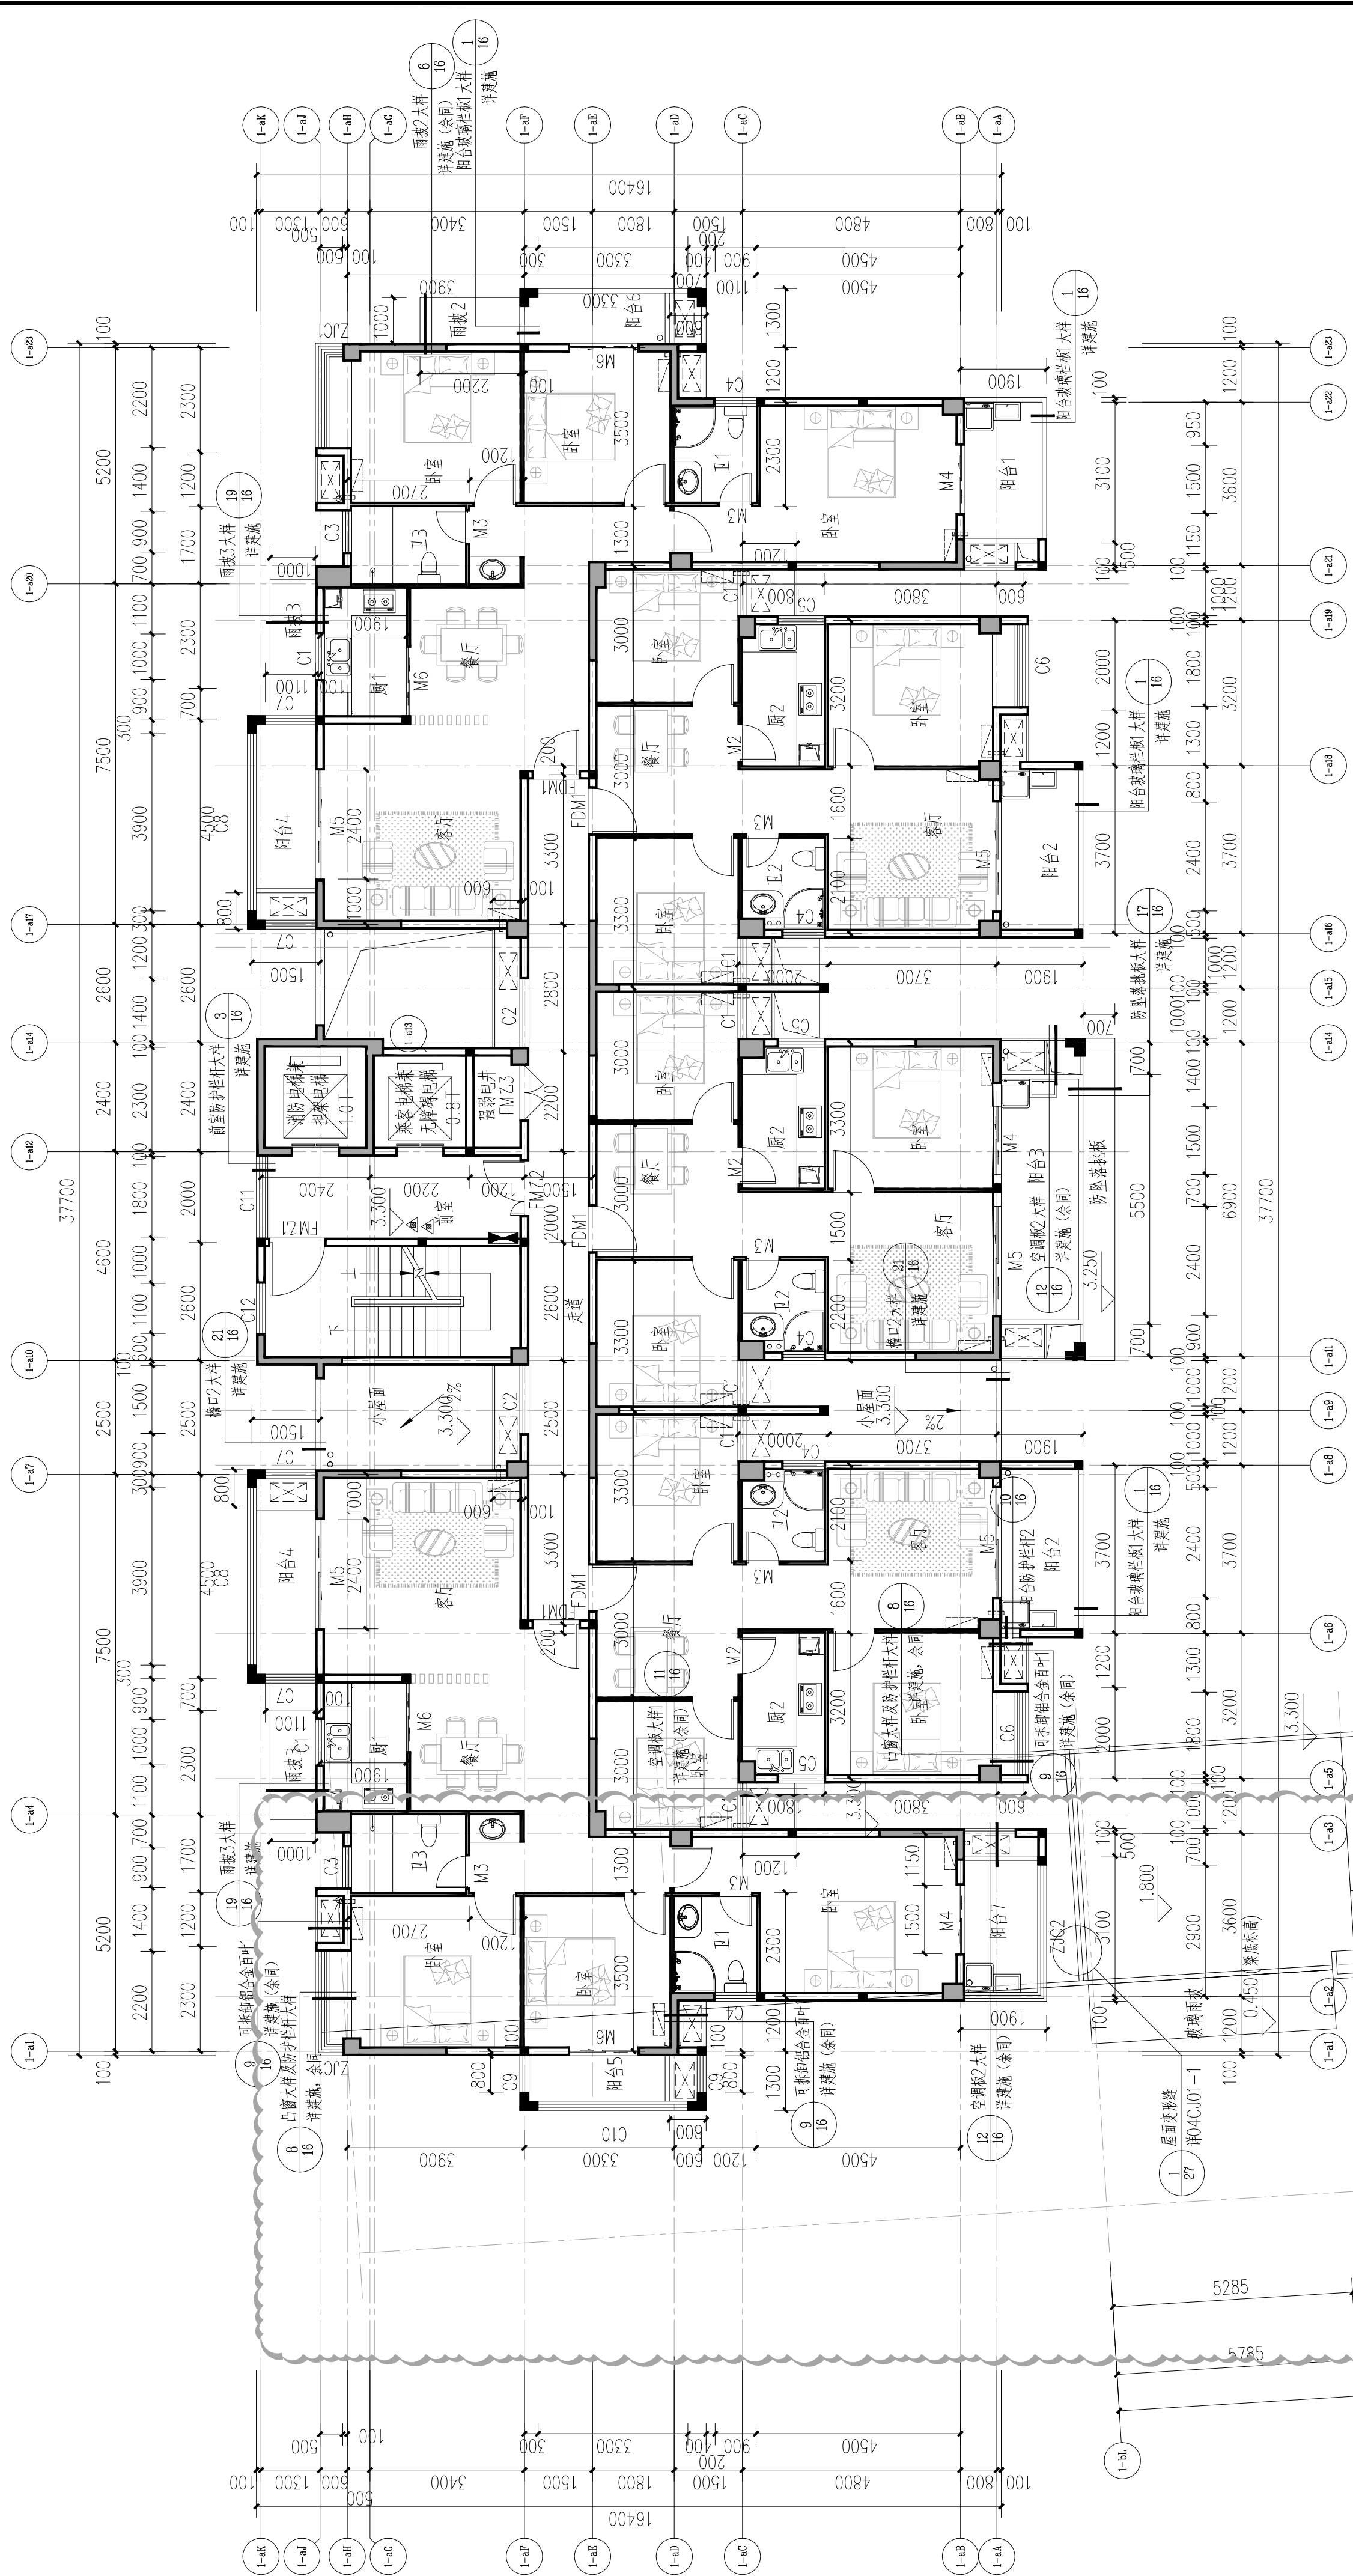


修改注明:


一、1#楼一层店面 1-aH~1-bA 轴交 1-b1~1-b3 轴间局部店面取消, 建筑面积减少 332.17 m²。

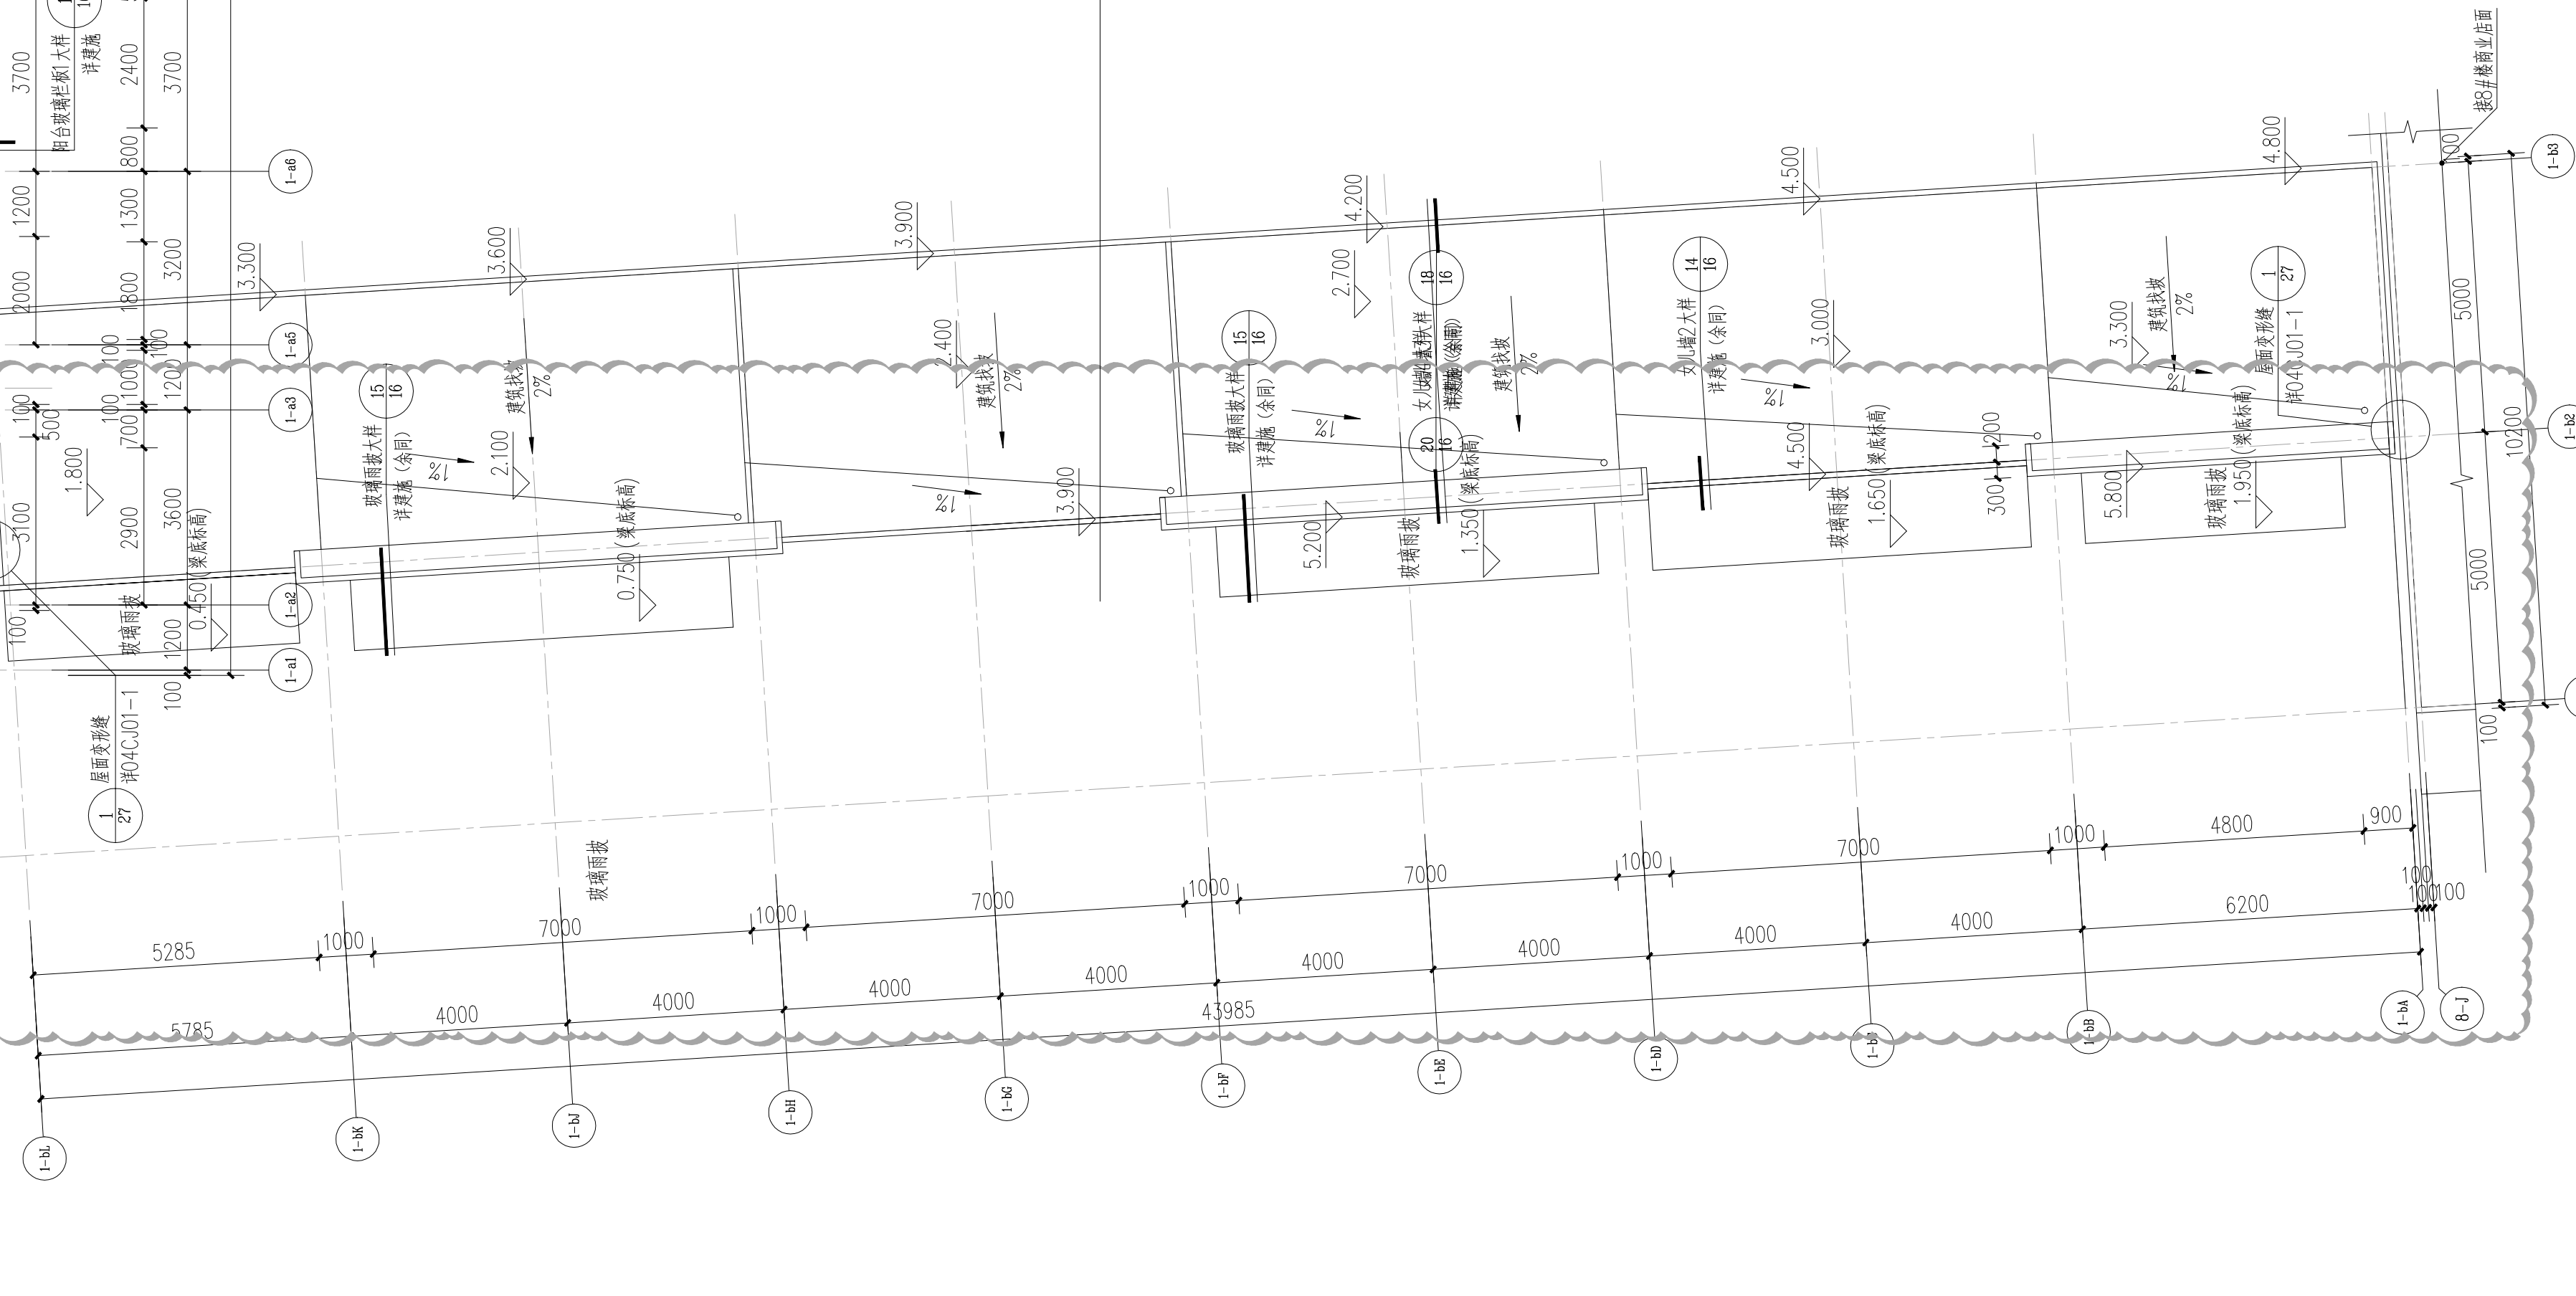

图例	说明	图例	说明
==	200厚墙体 (具体材料详见说明)	○	地漏 (做防水处)
==	100厚现浇空心楼块	洗衣机	洗衣机 (由用户自理)
==	住宅厨房隔墙 (用户自理, 二次装修时不得做出变化)	厨房, 卫生间接水道 (成品)	
	灭火器	热水器	热水器 (由用户自理)
	空调室外机	空调室内机	空调室内机 (由用户自理)
	空调预留洞	座便器	座便器 (由用户自理)
	过水孔100×100 (做防水), 孔底同楼面	淋浴盆	淋浴盆 (由用户自理)
○	Ø110U PVC雨水管	空调立管 (防水处)	

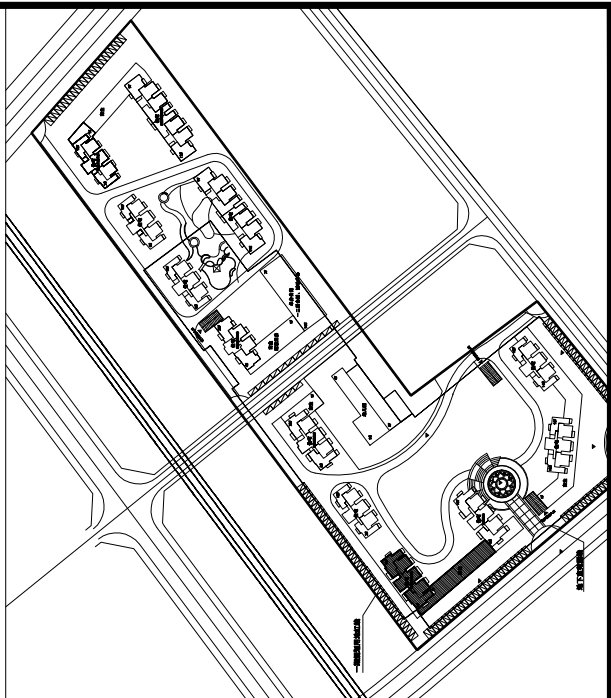

专业名称：建筑、给排水、电气、暖通、动力、结构、专业名称：建筑、给排水、电气、暖通、动力、结构、专业名称：建筑、给排水、电气、暖通、动力、结构、

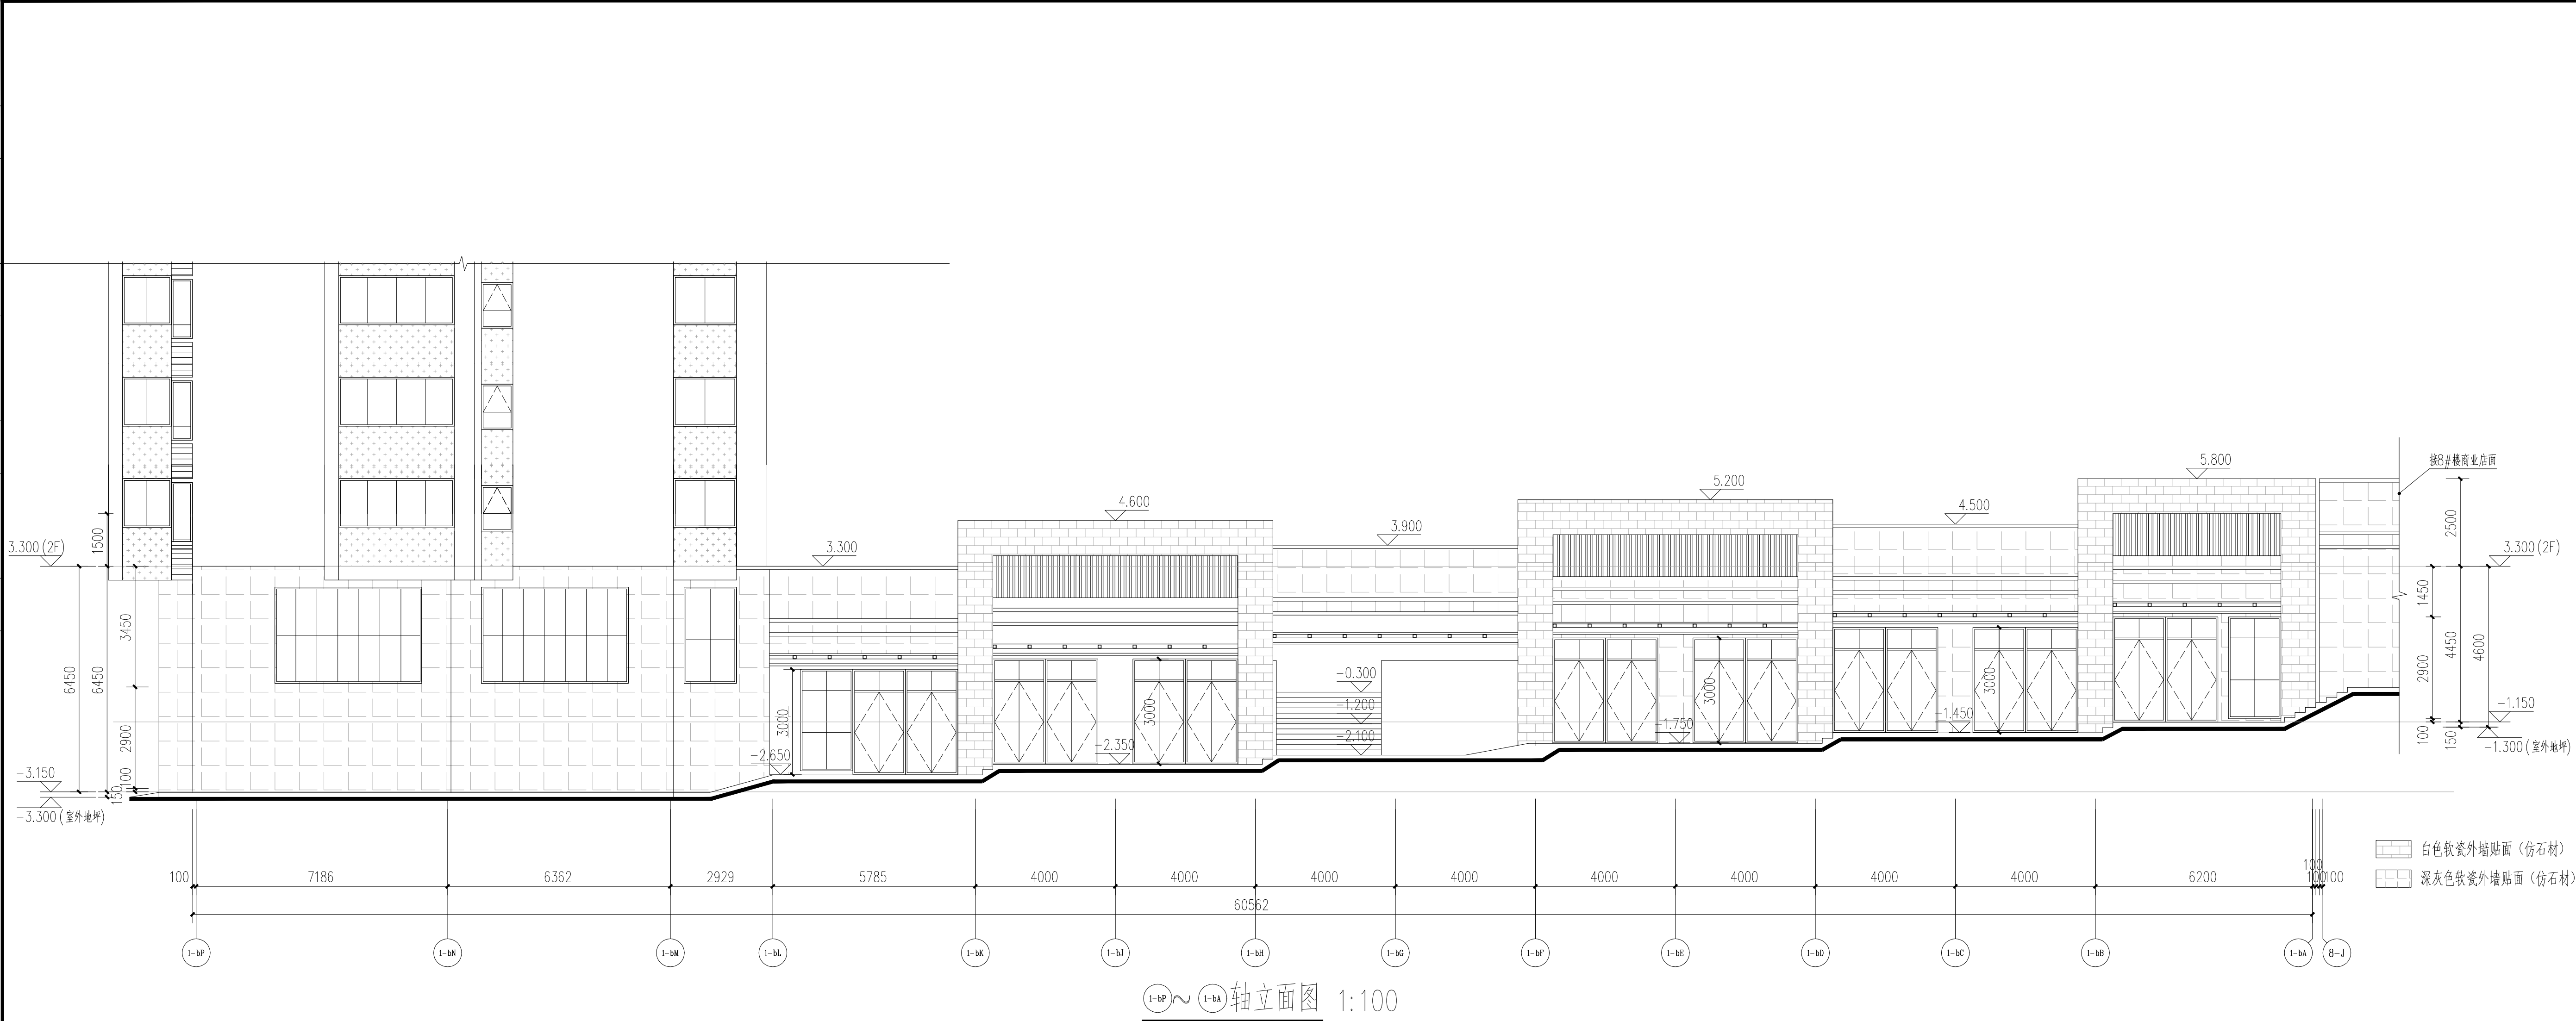



福建省机电沿海
建筑设计研究院有限公司

证书编号: A135003677 A235003674
资质范围: 建筑工程甲级 机械行业甲级
电子工程甲级 轻钢结构甲级
工程咨询甲级 市政工程乙级
城乡规划丙级 变电工程丙级

施工图审查批准单位:

施工图审查批准书证号:

图纸专用章

福建省工程勘察设计图纸专用章
福建省机电沿海建筑设计研究院有限公司
范围: 建筑工程
资质等级: 甲级 证号: A135003677
有效期至: 2025年03月02日

注册执业章

中华人民共和国一级注册建筑师
姓名: 彭晓辉
注册号: 3500367-003
有效期: 至2024年11月15日

注册执业章

建设单位:

沙县绿欧房地产开发有限公司

工程名称:

金洲公寓
1#楼


职 责	姓 名	签 名
审 定		
项目负责人	彭晓辉	
项目经理	彭晓辉	
专业负责人	彭晓辉	
审 核	张玉林	
校 对	王建平	
设 计	魏洪	

图名:

沿街立面修改


工程编号	2014-33	版 别	1.00
图 别	建施	图 号	修4
日 期	2021年 4月 16日		

专业	建筑	结构	专业	给排水	电气	专业	暖通	动力	专业	总图	工艺	专业	暖通	动力	专业	总图	工艺
姓名			姓名			姓名			姓名			姓名			姓名		

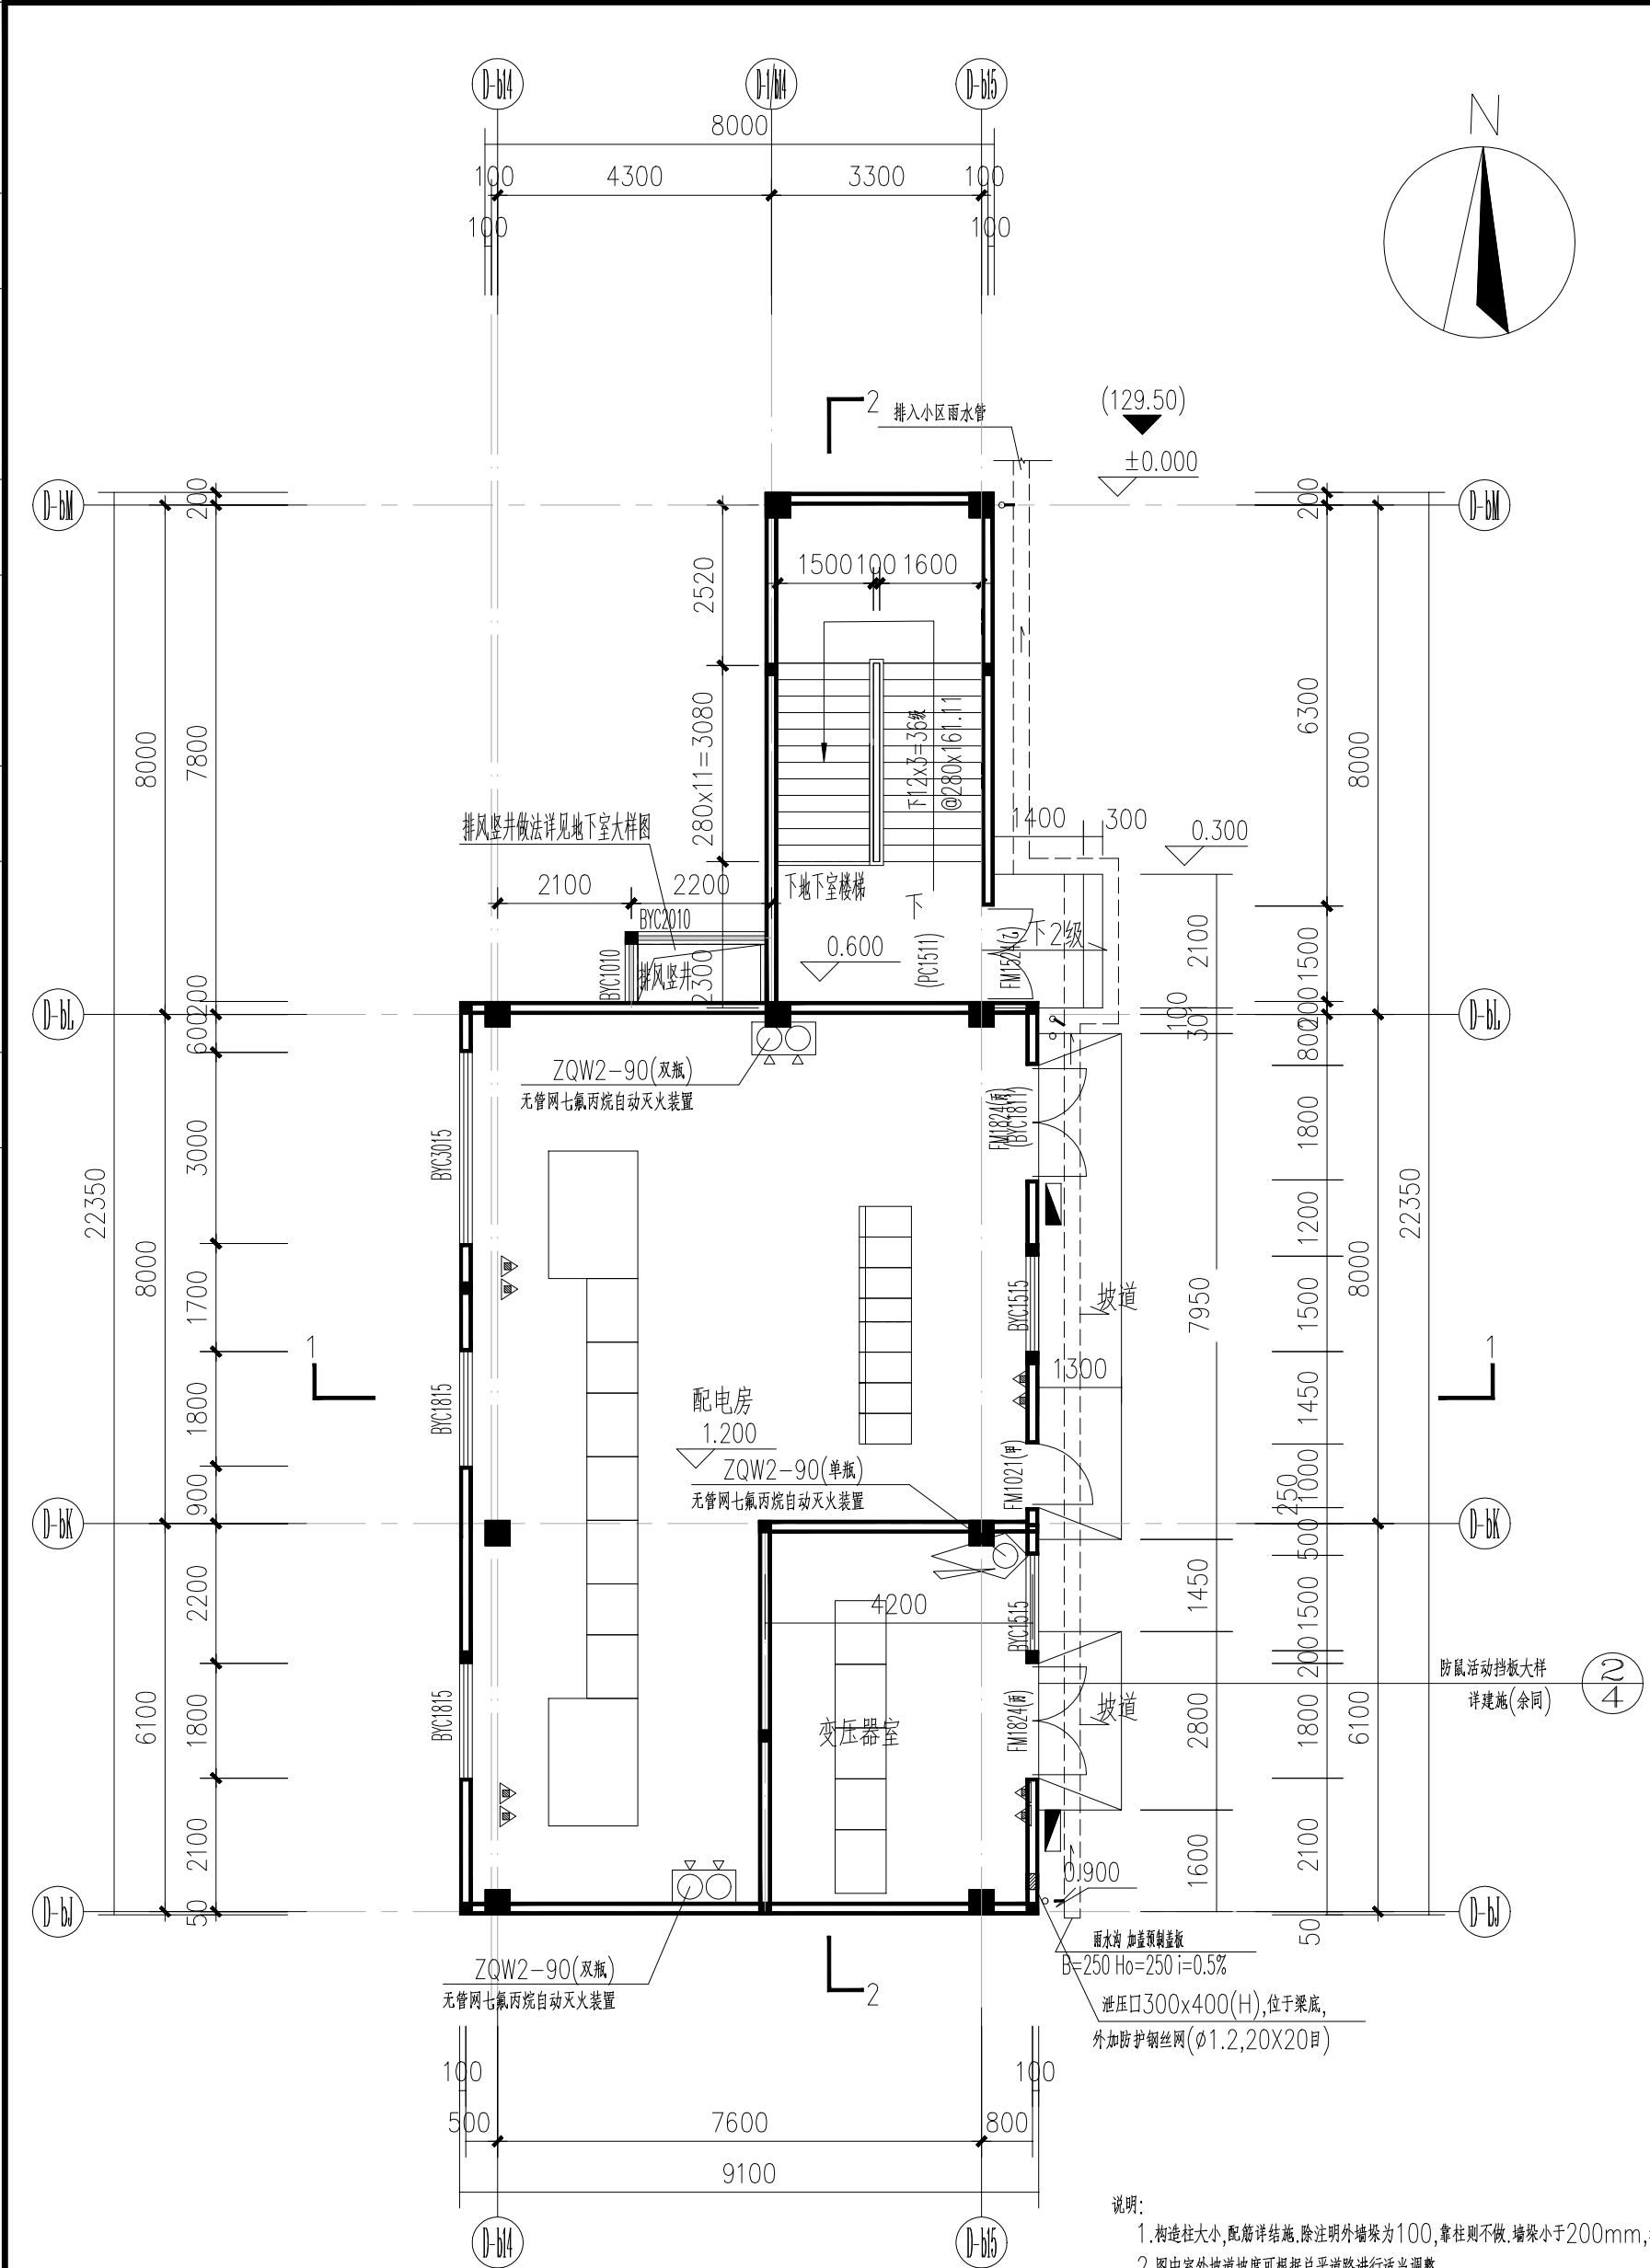

一层平面图 1:100

- 说明:
- 构造柱大小,配筋详结构,除注明外墙为100,靠柱则不做,墙垛小于200mm,均用C20素混凝土浇筑。
 - 图中室外坡道坡度可根据总平面图进行适当调整。
 - 本层 $\phi 100$ UPVC雨水管共有3根,具体位置详见水施图。
 - 本层共有消火栓共2个,灭火器共8个(手提式磷酸铵盐干粉灭火器型号为MF/ABC5),管网七氟丙烷自动灭火装置共5瓶,体位置详见水施图。
 - 本层建筑面积为160平方米,最大人数3人。
 - 配电房室内电缆沟,待专业电力设计公司提供资料实施。
 - 本工程位于地下室顶板上,室外覆土1米,结构板标高详见地下室图纸。

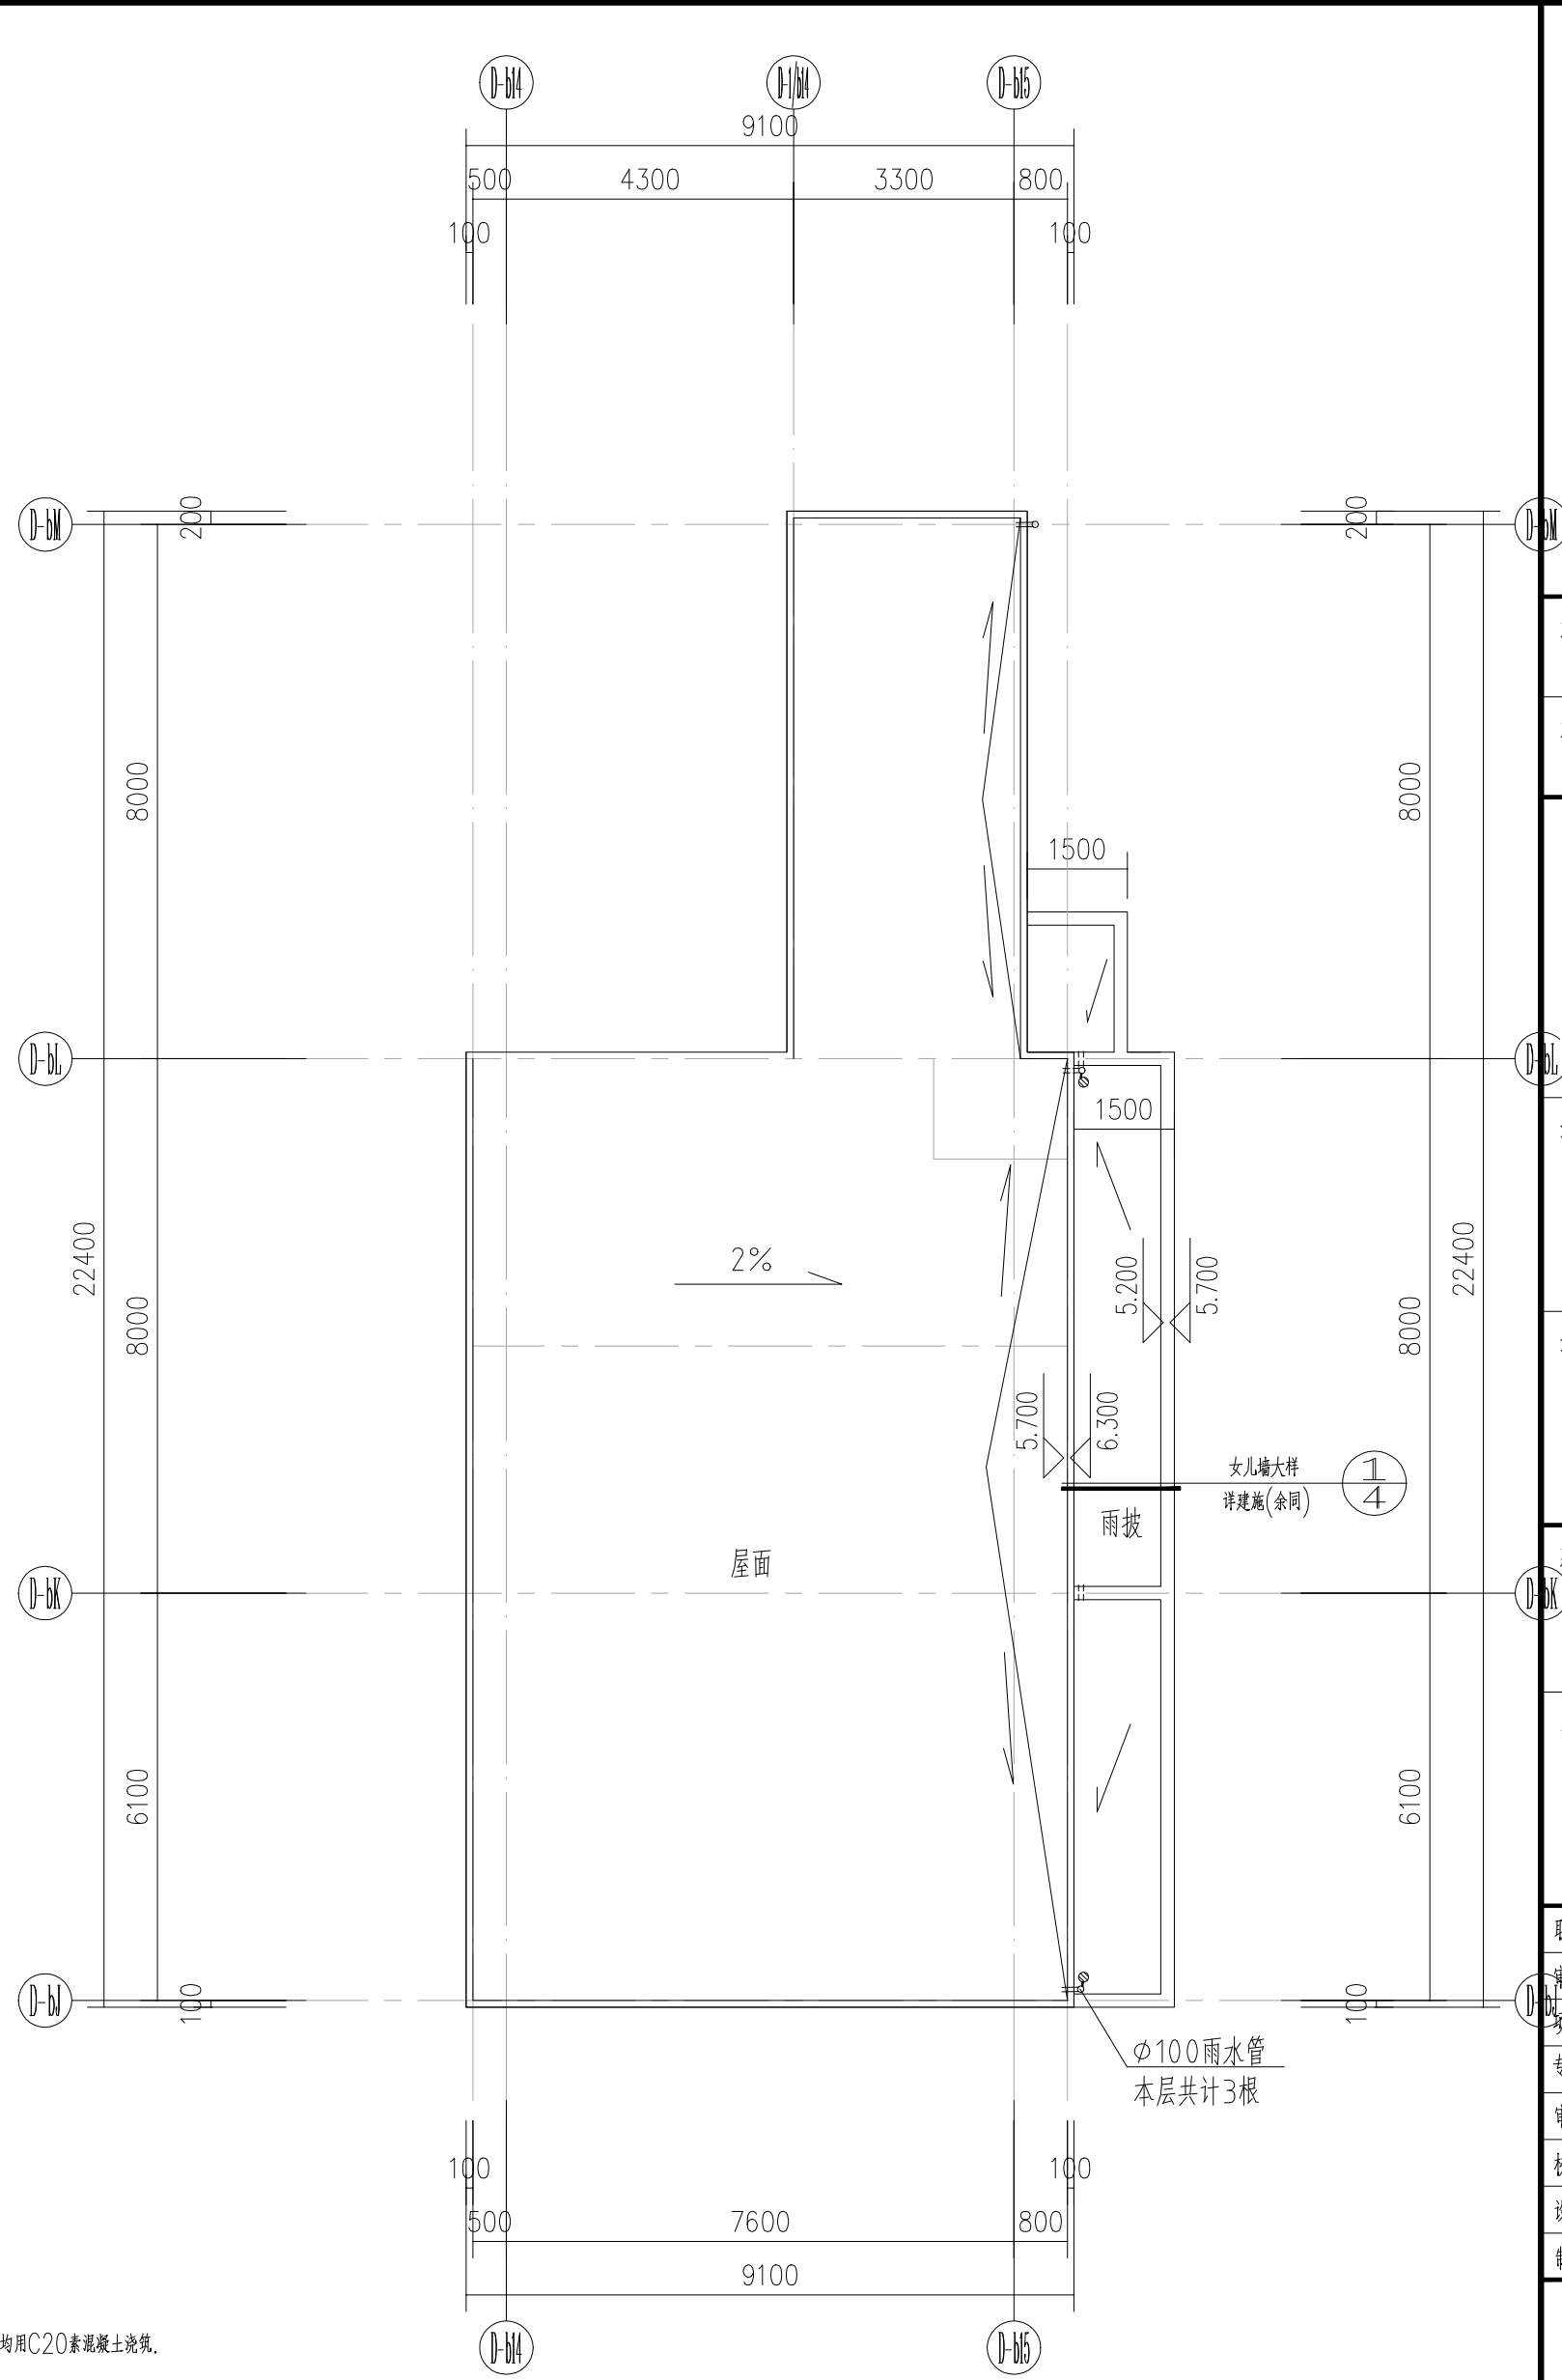

屋顶平面图 1:100



福建省机电建筑设计研究院

证书编号: A135003677·A235003674
(130126-Sj, 130126-Sy)

资质范围: 建筑工程甲级, 机械行业甲级
电子工程甲级, 轻钢结构甲级
工程咨询甲级, 岩土勘察乙级
市政工程乙级, 变电工程丙级

施工图审查批准单位:

施工图审查批准书证号:






图框主图章
福建省工程勘察设计图纸专用章
福建省机电建筑设计研究院有限公司
范围: 建筑工程
资质等级: 甲级 证号: A135003677
有效期至: 2025年03月02日

注册执业章
中华人民共和国一级注册建筑师
姓名: 彭晓辉
注册号: 3500367-003
有效期: 至2024年11月15日

注册执业章

建设单位:
沙县绿欧房地产开发有限公司

工程名称:
金洲公寓一配电房

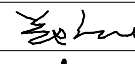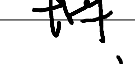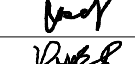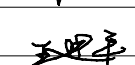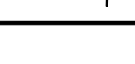职 责	姓 名	签 名
审 定	郑庆日	
项目负责人	彭晓辉	
专业负责人	彭晓辉	
审 核	张玉林	
校 对	许晓燕	
设 计	王建平	
制 图	王建平	

图名:
一层平面图
屋顶平面图

工程编号	2014-33	版 别	
图 别	建 施	图 号	2
日 期	2019年3月21日		