




一建·沁园春

XIA YANG SHENG YI JIAN PENG HU QU GAI ZAO C&D DI KUAI

(下洋省一建棚户区改造A地块)变更项目二期工程



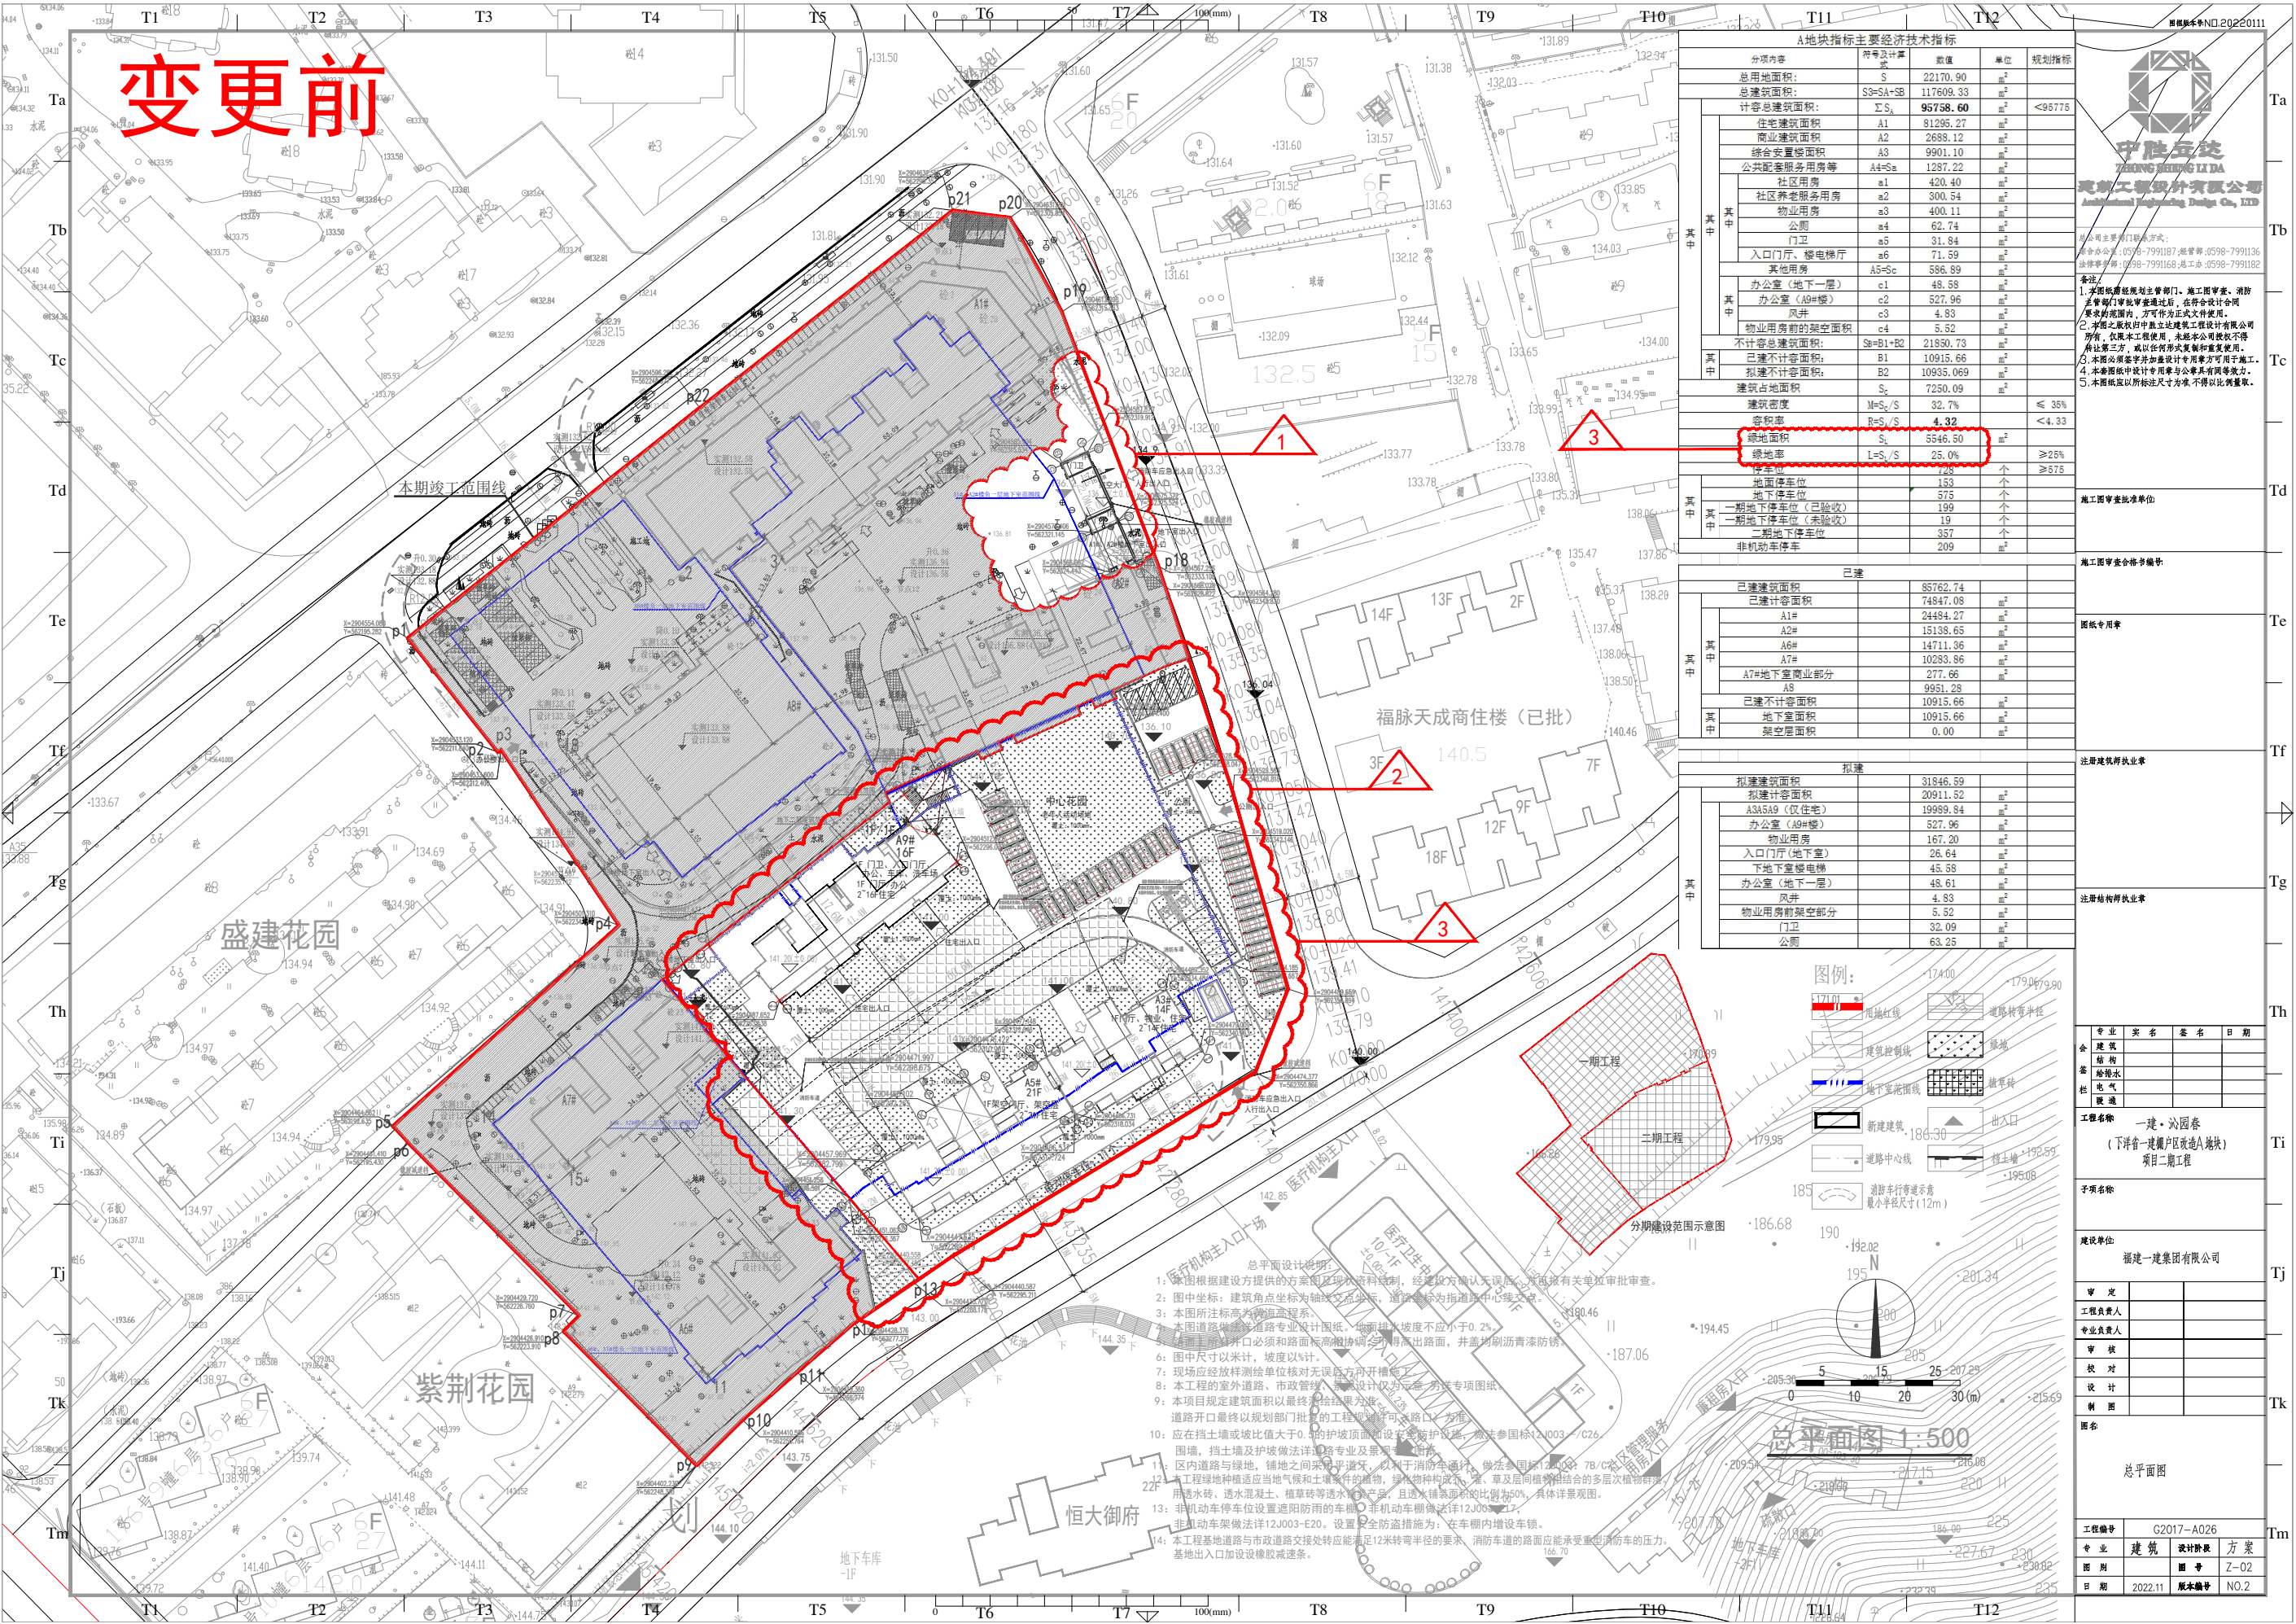

变更前

A地块指标主要经济技术指标				
分项内容	符号及计算	数量	单位	规划指标
总用地面积	S	22170.90	m ²	
总建筑面积	S ₀ =S _A +S _B	117609.33	m ²	
计容总建筑面积	ΣS _i	96758.60	m ²	<98778
住宅建筑面积	A1	81295.27	m ²	
商业建筑面积	A2	2688.12	m ²	
综合配套建筑面积	A3	9901.10	m ²	
公共配套服务用房等	A4+S _a	1287.22	m ²	
社区用房	a1	420.40	m ²	
社区养老服务用房	a2	300.54	m ²	
物业用房	a3	400.11	m ²	
公厕	a4	62.74	m ²	
门卫	a5	31.84	m ²	
入口门厅、楼梯电梯	a6	71.59	m ²	
其他用房	A5+S _c	586.89	m ²	
办公室(地下一层)	c1	49.58	m ²	
办公室(A9#楼)	c2	527.96	m ²	
风井	c3	4.83	m ²	
物业用房前的架空面积	c4	5.52	m ²	
不计容总建筑面积	S _B =B1+B2	21850.73	m ²	
已建不计容面积	B1	10915.66	m ²	
拟建不计容面积	B2	10935.069	m ²	
建筑占地面积	S _c	7250.09	m ²	
建筑密度	M=S _c /S	32.7%		≤35%
容积率	R=S ₀ /S	4.32		<4.33
绿地面积	S _g	5546.50	m ²	
绿地率	L=S _g /S	25.0%		≥25%
停车位		128	个	≥875
地面停车位		153	个	
地下停车位(已验收)		373	个	
一期地下停车位(未验收)		199	个	
二期地下停车位		19	个	
非机动车停车位		337	个	
		209	m ²	

已建		已建	
已建建筑面积		85762.74	m ²
已建计容面积		74847.08	m ²
A1#		24484.27	m ²
A2#		15138.65	m ²
A6#		14711.36	m ²
A7#		10283.86	m ²
A7#地下室商业部分		277.66	m ²
A3		9951.23	m ²
已建不计容面积		10915.66	m ²
地下室面积		10915.66	m ²
架空层面积		0.00	m ²

拟建		拟建	
拟建建筑面积		31846.59	m ²
拟建计容面积		20911.52	m ²
A3A5A9(仅住宅)		19989.84	m ²
办公室(A9#楼)		527.96	m ²
物业用房		167.20	m ²
入口门厅(地下室)		26.64	m ²
地下室楼梯电梯		45.88	m ²
办公室(地下一层)		48.61	m ²
风井		4.83	m ²
物业用房前架空部分		5.52	m ²
门卫		32.09	m ²
公厕		63.25	m ²

图例:

用地红线

建筑控制线

地下室范围线

新建建筑

道路中心线

消防车道

最小半径尺寸(12m)

道路转弯半径

绿地

坡面线

出入口

挡土墙

总平面图 1:500

0 5 10 15 20 25 30(m)

分期建设范围示意图

一期工程

二期工程

总平面设计说明

1. 本项目根据建设方提供的方案图及地质资料编制, 经建设方确认无误, 并经有关部门审批审查。

2. 图中坐标: 建筑角点坐标为轴线坐标系, 道路坐标为指道路中心线坐标。

3. 本图所注标高为黄海高程。

4. 本图道路横断面设计图, 路面坡度不应小于0.2%。

5. 路面材料必须和路面材料相协调, 并高出路面, 并应刷沥青漆防腐。

6. 图中尺寸以米计, 坡度以‰计。

7. 现场应放样测绘给地核对无误后方可开槽施工。

8. 本工程的室外道路、市政管线、景观设计仅为示意, 另设专项图纸。

9. 本项目规定建筑面积最终以最终测绘结果为准。

10. 道路开口最终以规划部门批准的工程规划许可为准。

11. 应在挡土墙或坡比值大于0.5的护坡顶部设置受保护设施, 做法参照国标《GB 5003-2003》C26。

12. 区内道路与绿地、铺地之间设置平交道, 以利于消防车通行, 做法参照国标《GB 5003-2003》C26。

13. 本工程绿地种植应当当地气候和土壤条件的植物, 植物种类构成, 乔、灌、草及层间植物相结合的多层次植物群落。

14. 用透水砖、透水混凝土、植草砖等透水铺装, 且透水铺装面积的比例为50%, 具体详景观图。

15. 非机动车停车位设置遮阳防雨的车棚, 非机动车棚做法详《12J003-2》。

16. 非机动车架做法详《12J003-E20》。设置安全防护措施为: 在车棚内增设车锁。

17. 本工程基地道路与市政道路交接处应能满足12米转弯半径的要求, 消防车道路面应能承受消防车的压力。

18. 基地出入口加设防撞设施。

专业 姓名 盖章 日期

建筑 结构 给排水 电气 暖通

工程名称 福建·沁园春 (下洋第一建户区改造A地块) 项目二期工程

子项目名称

建设单位 福建一建集团有限公司

审定 工程负责人 专业负责人 审核 校对 设计 制图

工程编号 G2017-A026

专业 建筑 设计阶段 方案

图例 图号 Z-02

日期 2022.11 版本号 NO.2

变更内容:

1. 东北侧门卫重新设计, 室外道路标高由134.91变更为134.33, 东北侧出入口由道路变更为台阶, 增设无障碍坡道, 东北侧原有消防应急出入口同步取消。

A1#与A2#之间增加消防回车场。满足消防规范要求。

2、地面机动车停车位布局调整，沿围墙及建筑布置，对应车道同步调整。

变更前地面机动车停车位：153个。（其中一期已建24个。）

其中普通机动车停车位：77个；双层机械机动车停车位：76个

变更后地面机动车停车位：153个。（其中一期已建24个。）

其中普通机动车停车位: 87个; 微型车停车位: $2 \times 0.7 = 1$ 个。

单层机械机动车停车位:15个。

三层机械机动车停车位:50个。

3、绿地景观布局优化,

A3#楼南侧道路取消。

变更前:绿地面积: 5546.50m²


(包含一期绿化面积3573.874m²。)

绿地率: 25.0%


变更后:绿地面积: 6380.145m²

(包含一期绿化面积3573.874m².)

绿地率: 28.78%

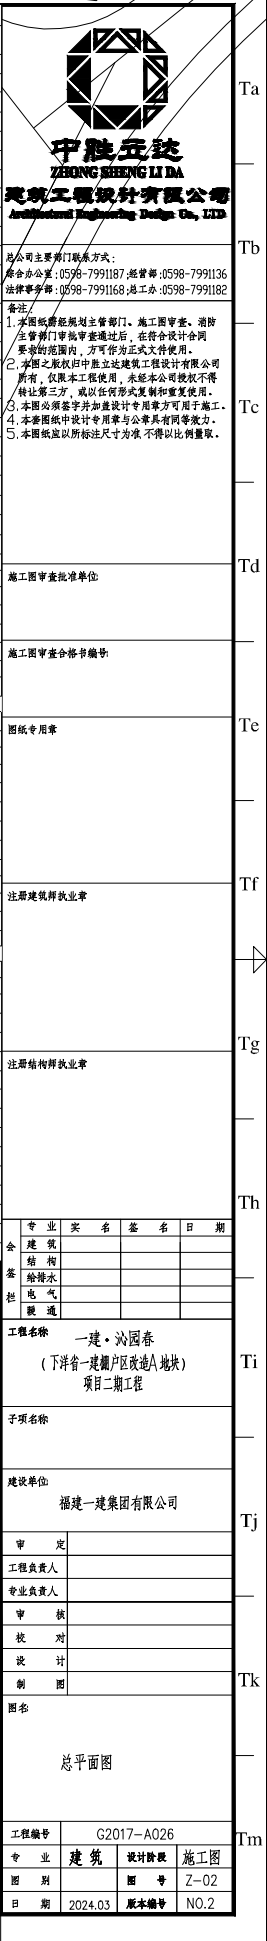


变更前

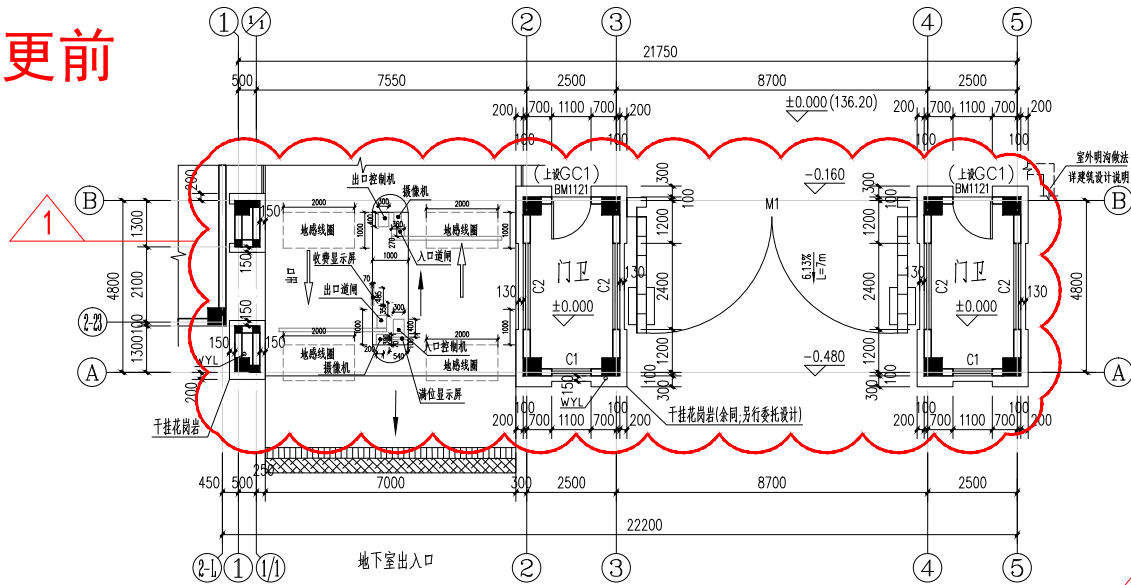


一层平面图 1:100


- 本工程主体结构为框架结构，高度为6.18米，门卫建筑面积27m²，占地面积为28.82m²。
- 未注明构造柱为GZ·b×h=200×200。
- 图中车库自动道闸参17J927-1 DZB-1030W为参考，具体做法由业主自理。
- 建筑设计施工说明做法详主楼建筑设计说明。
- 未尽事宜详见国家现行的有关施工验收规范。

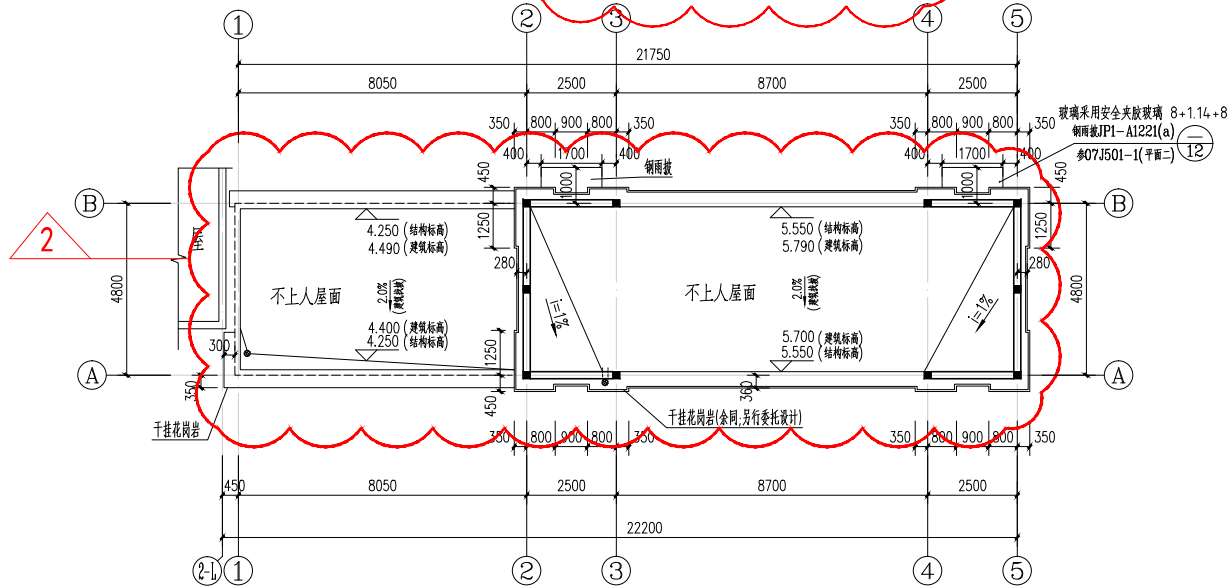


屋面平面图 1:100

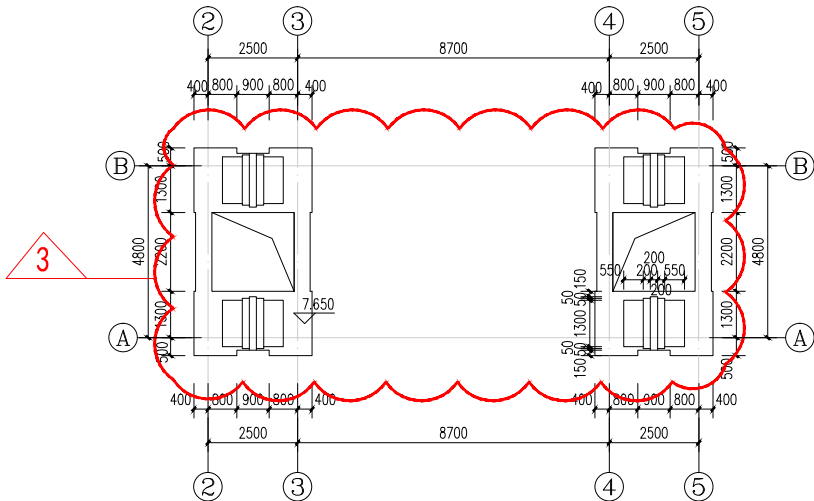

造型屋顶平面图 1:100

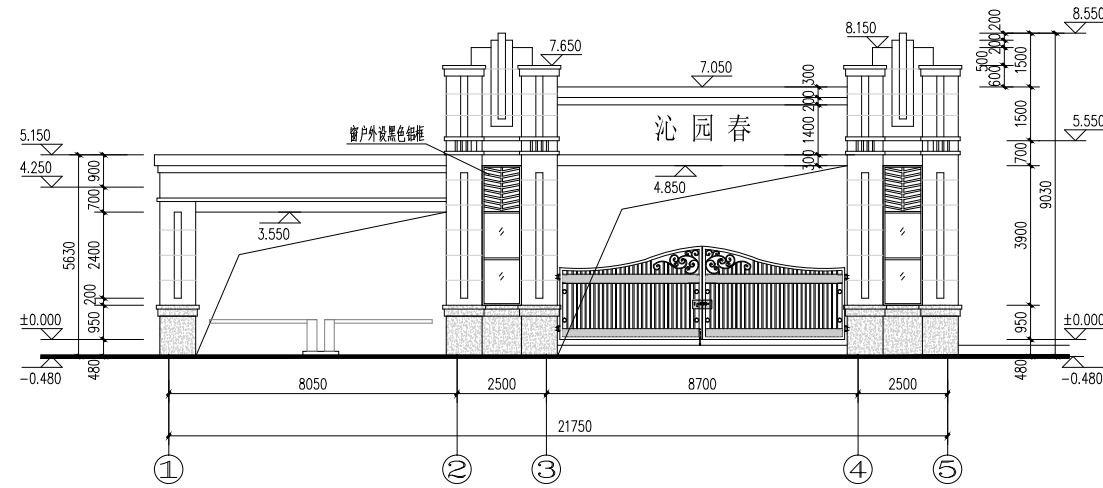


①~⑤轴立面图 1:100

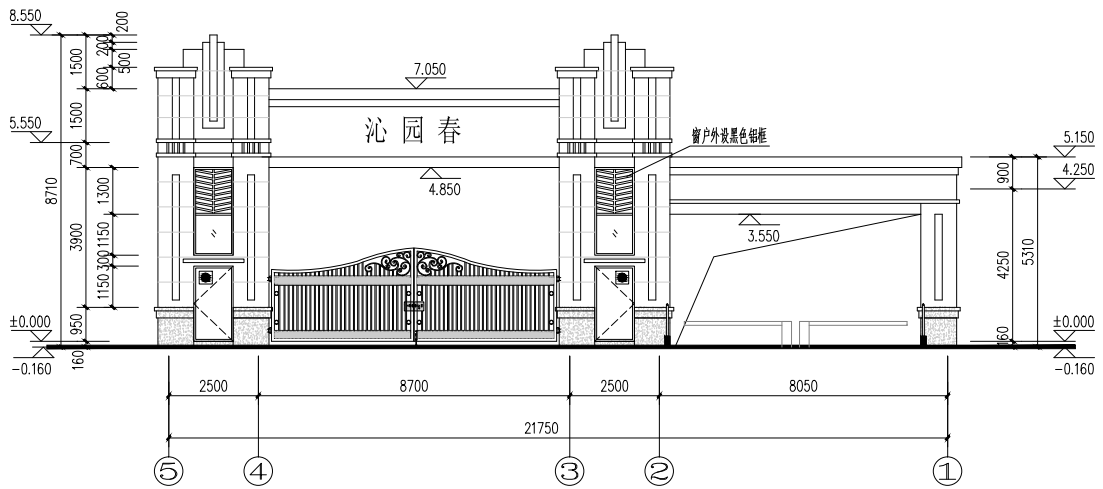

⑤~①轴立面图 1:100

消防救援窗口，净高度和净宽度均不小于1.0m，安全易碎玻璃，下沿距室内地面不大于1.2m

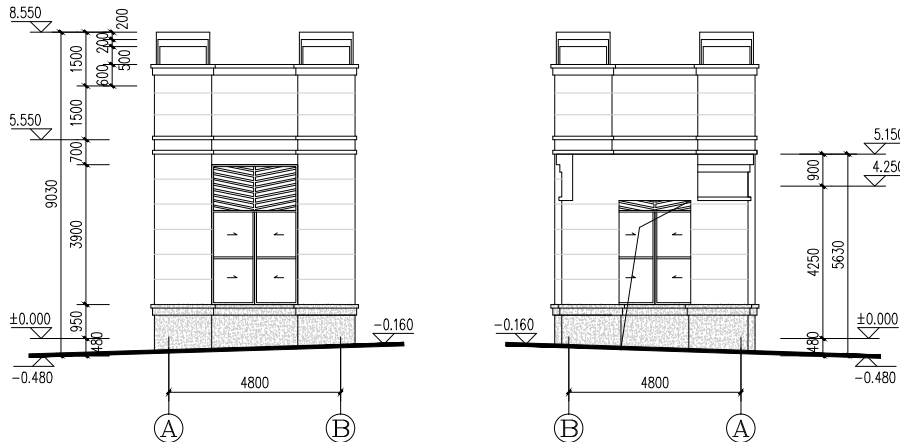

A~B轴立面图 1:100

B~A轴立面图 1:100

外装饰材料表

代号	填充	名称	构造做法	备注
外饰1		英国棕色干挂花岗岩	另行委托设计	色板由设计人员现场定
外饰2		米黄色干挂花岗岩	同上	同上

注：立面颜色与效果图颜色相差较大时，参见效果图



总公司地址：0598-7991187, 经营地址：0598-7991136, 法律事务部：0598-7991168, 施工部：0598-7991182

- 备注：
- 本图仅供建设单位、主管部门、施工图审查、消防、主管部门审批审查通过后，在符合设计合同要求的范围内，方可作为正式文件使用。
 - 本图之版权归中胜立达建筑设计有限公司所有，仅限本工程使用，未经本公司授权不得转让第三方，或以任何形式复制或重发使用。
 - 本图必须加盖专业注册章并加盖设计专用章方可用于施工。
 - 本图图幅中设计专用章与公章具有同等效力。
 - 本图版数应以所标注尺寸为准，不得以比例量取。

施工图审查批准单位：

施工图审查合格书编号：

图框专用章

注册建筑师执业章

注册结构师执业章

专业	姓名	签名	日期
建筑			
结构			
给排水			
电气			
暖通			

工程名称 一建·沁园春
(下洋省一建棚户区改造A地块)项目二期工程

子项名称 门卫










建设单位 福建一建集团有限公司

审定		
工程负责人		
专业负责人		
审核		
校对		
设计		
制图		

图名

一层平面图 屋面层平面图
立面图

工程编号	专业	建筑	设计阶段	方案
图例	图号	02		
日期	2023.11.	版本号	NO.1	

 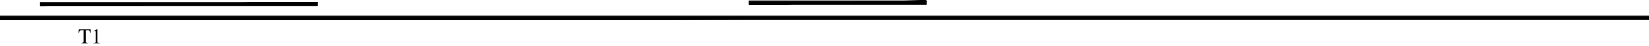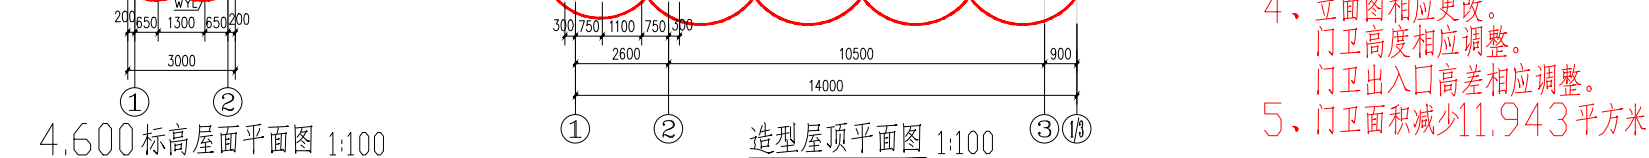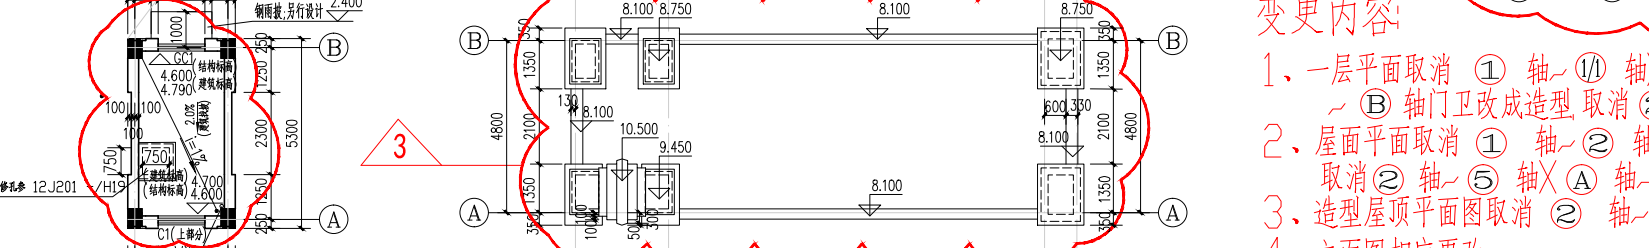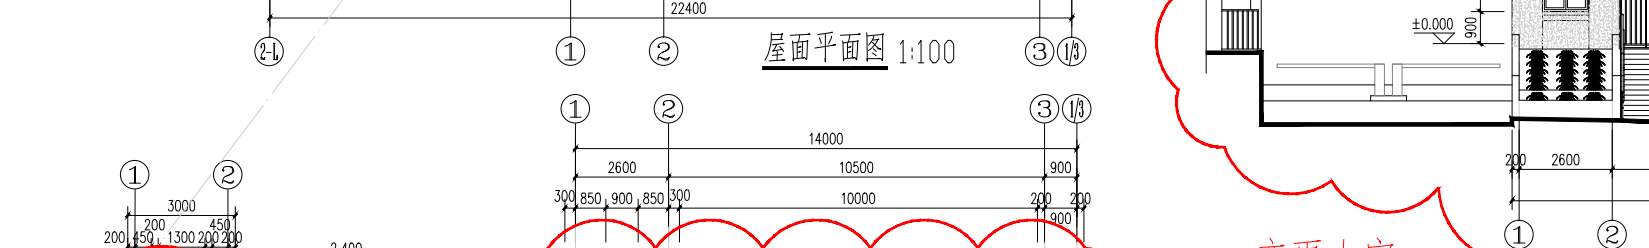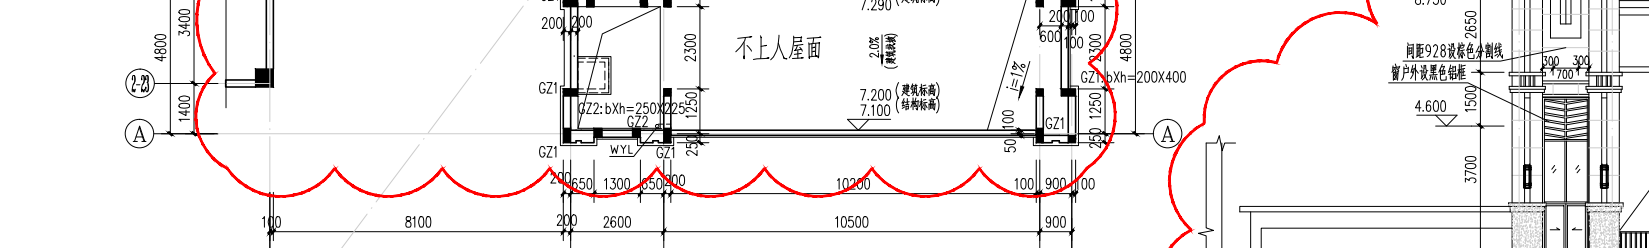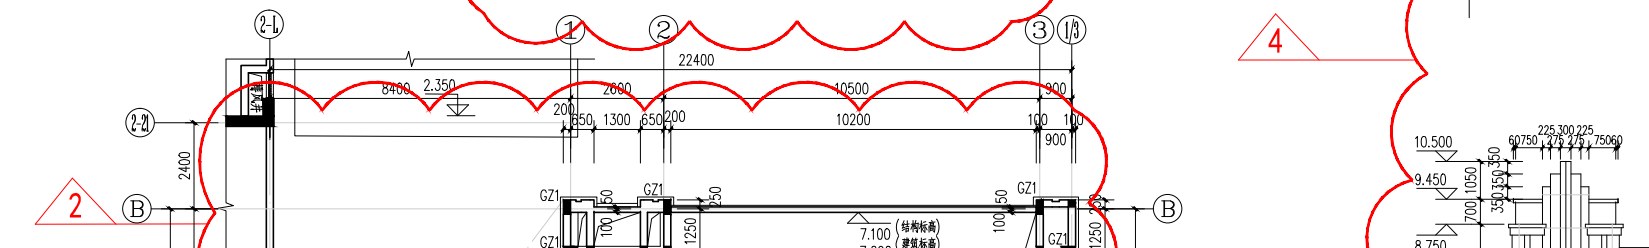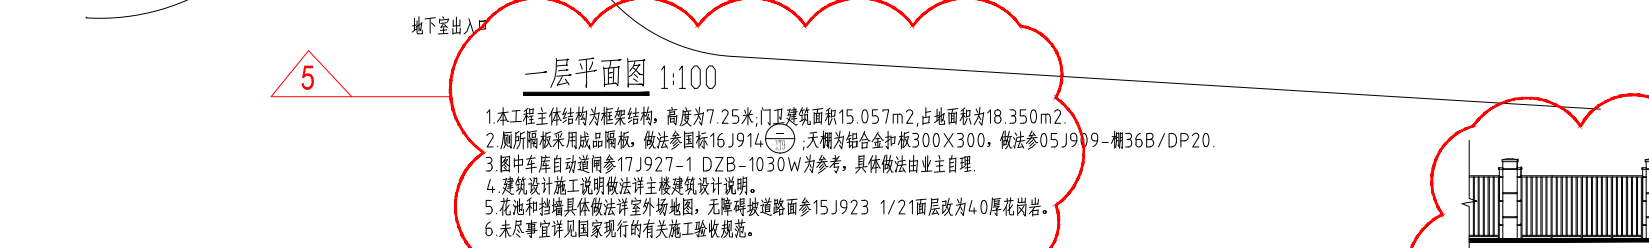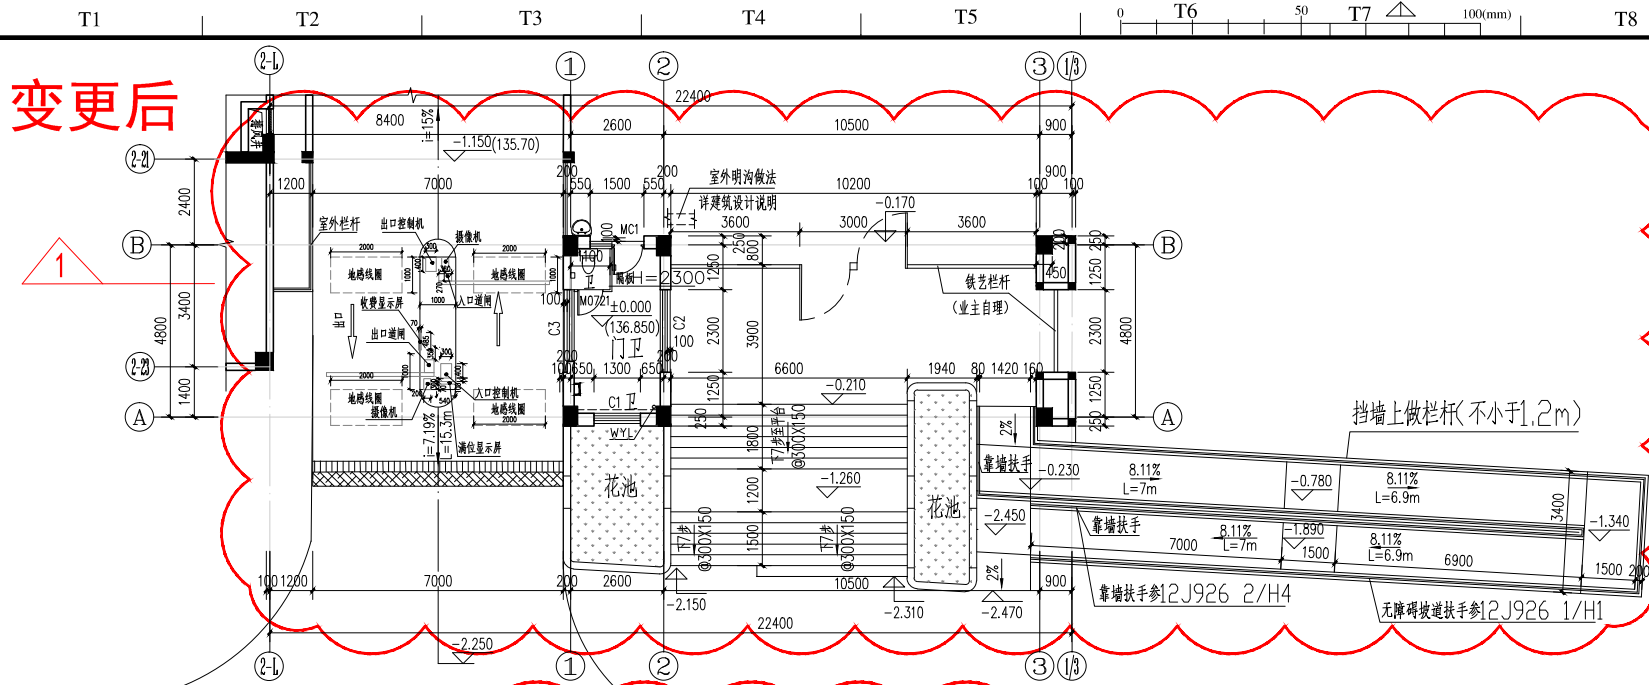


变更后

一层平面图 1:100

- 本工程主体结构为框架结构，高度为7.25米，门卫建筑面积15.057m²，占地面积为18.350m²。
- 厕所隔间采用成品隔间，做法参照国标16J914-1；天棚为铝合金扣板300X300，做法参照05J909-1-36B/DP20。
- 图中车库自动道闸参照17J927-1 DZB-1030W为参考，具体做法由业主自理。
- 建筑设计施工说明做法详建筑说明。
- 花池和挡墙具体做法详室外场地图，无障碍坡道路面参照15J923 1/21面层改为40厚花岗岩。
- 未尽事宜详见国家现行的有关施工验收规范。


屋面平面图 1:100

造型屋顶平面图 1:100

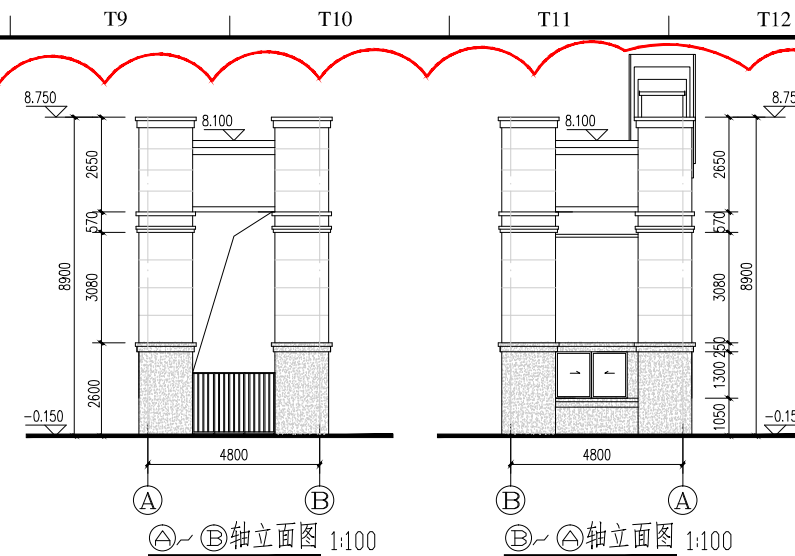


A~B轴立面图 1:100

B~A轴立面图 1:100

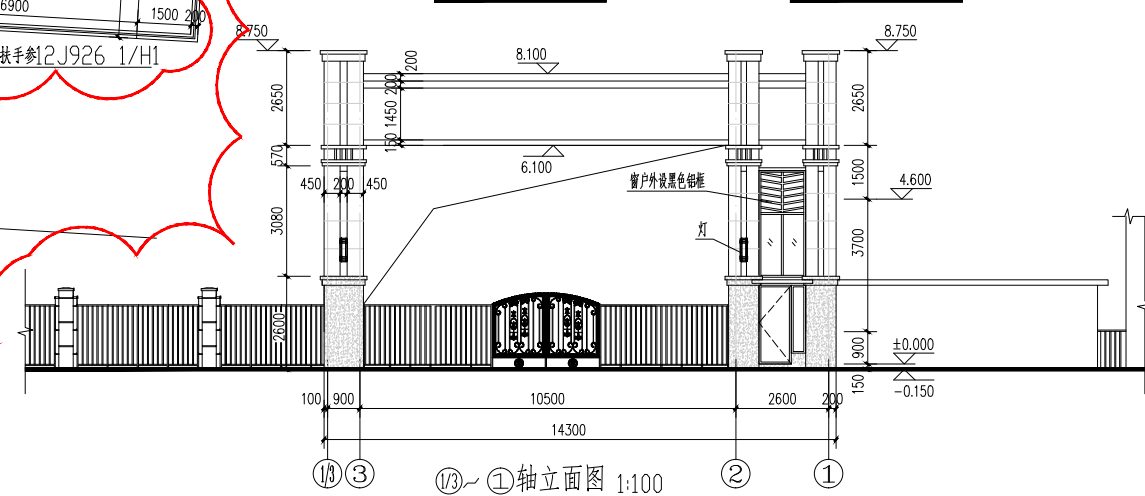

1/3~1轴立面图 1:100

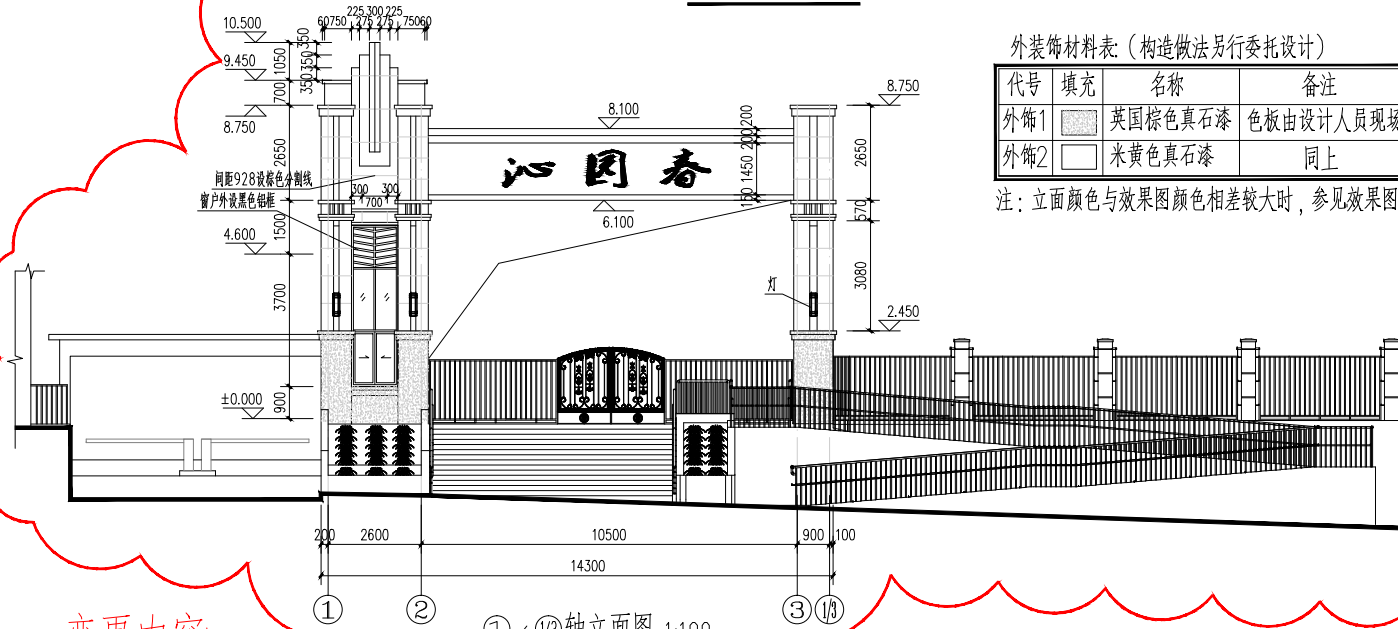

1~1/3轴立面图 1:100

外装饰材料表 (构造做法另行委托设计)

代号	填充	名称	备注
外饰1		英国棕色真石漆	色板由设计人员现场定
外饰2		米黄色真石漆	同上

注：立面颜色与效果图颜色相差较大时，参见效果图。

变更内容：

- 一层平面取消 ① 轴~①/① 轴×A 轴~B 轴造型，取消 ④ 轴~⑤ 轴×A 轴~B 轴门卫改成造型，取消 ② 轴~⑤ 轴×A 轴~B 轴干挂花岗岩线条。
- 屋面平面取消 ① 轴~② 轴×A 轴~B 轴屋面板，取消 ② 轴~⑤ 轴×A 轴~B 轴干挂花岗岩线条。
- 造型屋顶平面图取消 ② 轴~⑤ 轴×A 轴~B 轴干挂花岗岩线条。
- 立面图相应更改。
门卫高度相应调整。
门卫出入口高差相应调整。
- 门卫面积减少11.943平方米。

中胜云达
ZHONGSHENG YUNDA
建筑工程施工设计有限公司
Architectural Engineering Design Co., Ltd.

公司主要部门联系方式：
综合办公室：0598-7991187 经营部：0598-7991136
法律事务部：0598-7991168 竣工部：0598-7991182

备注：
1. 本图经设计主管部门、施工图审查、消防、人防等部门审批通过后，在符合设计合同要求的范围内，方可作为正式文件使用。
2. 本图之版权归中胜云达建筑工程设计有限公司所有，仅限本工程使用，未经本公司授权不得转借第三方，或以任何形式复制或重复使用。
3. 本图必须加盖专业注册章方可用于施工。
4. 本图须经设计主管部门审批后方可用于施工。
5. 本图应以所标注尺寸为准，不得以比例量取。

施工图审查批准单位

施工图审查合格书编号

图例专用章

注册建筑师执业章

注册结构师执业章

专业	姓名	签名	日期
建筑			
结构			
给排水			
电气			
暖通			

工程名称 一建·沁园春
下洋省一建棚户区改造(地块)项目二期工程

子项目名称 门卫

建设单位 福建一建集团有限公司

审定	
工程负责人	
专业负责人	
审核	
校对	
设计	
制图	

一层平面图 屋面层平面图
立面图

工程编号	
专业	建筑
图例	设计阶段 方案
日期	2024.03
版本号	NO.1

一建·沁园春

XIA YANG SHENG YI JIAN PENG HU QU GAI ZAO DAO DI KUAI